


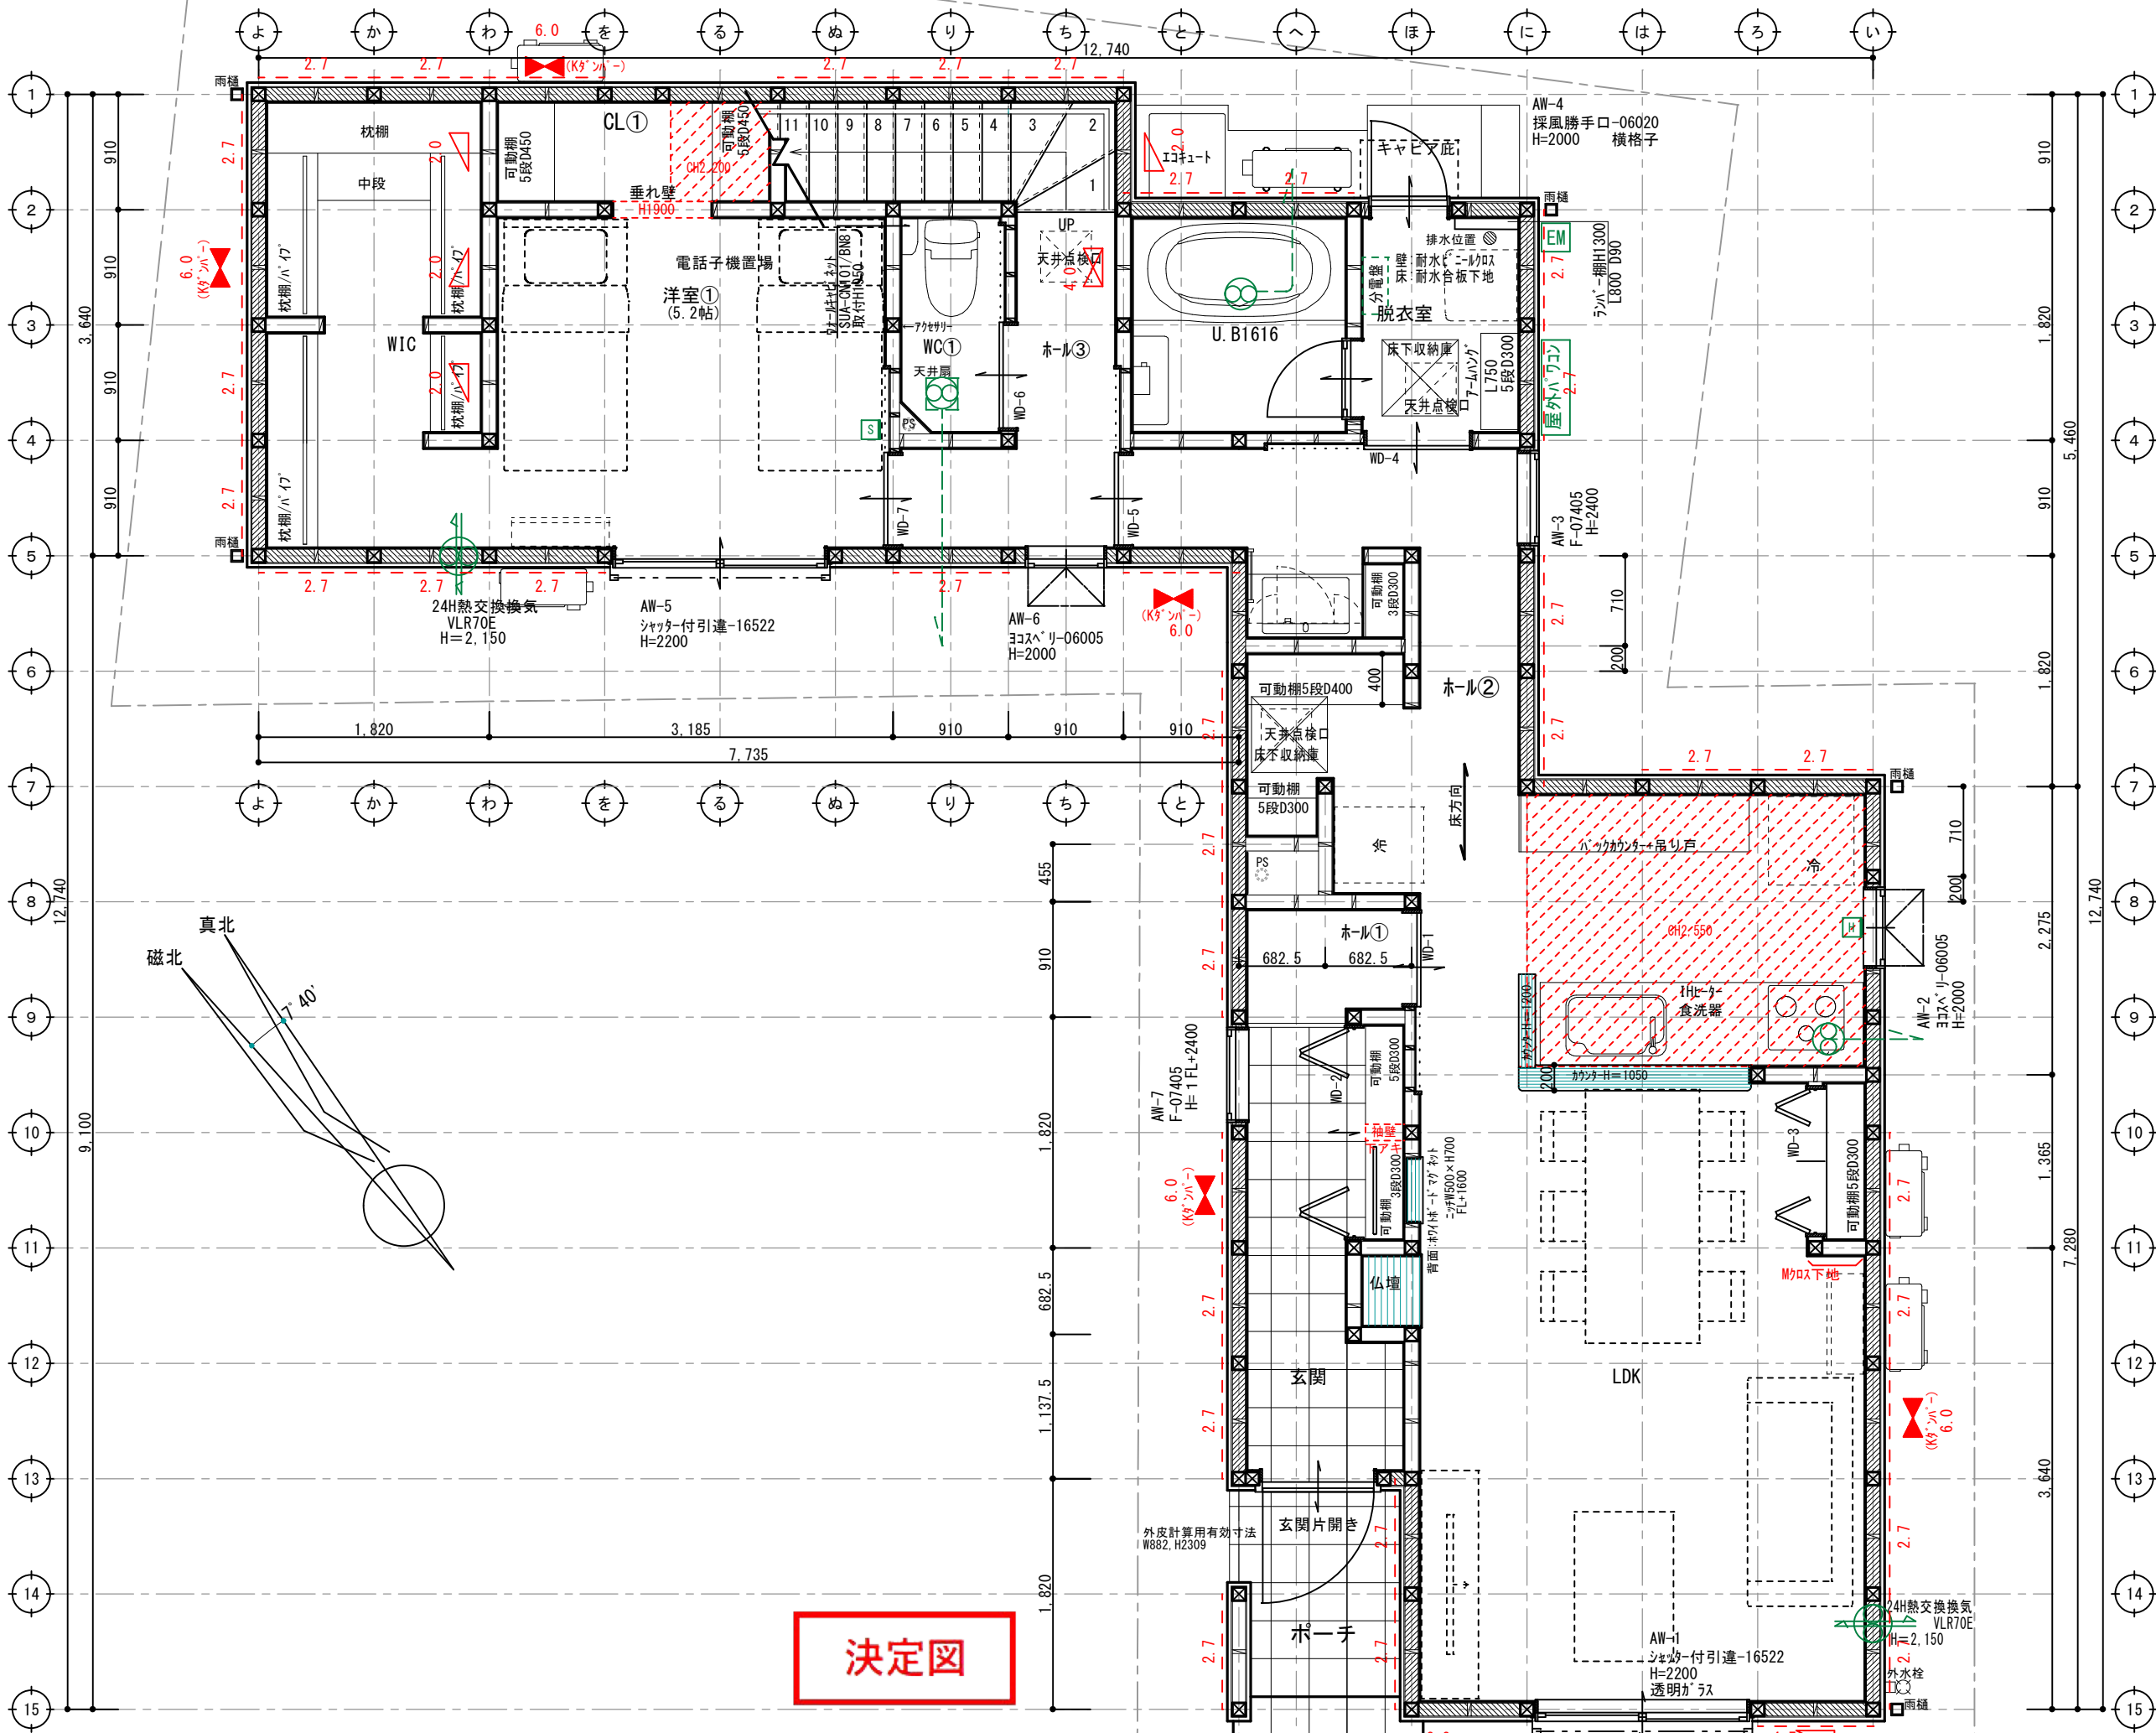

準防火地域

壁付け 住宅用火災報知器	数量
熱感知	電池式(単独型)
熱感知	露出型
1	

壁付け 住宅用火災報知器	数量
煙感知	電池式(単独型)
煙感知	露出型
1	

※ 煙感知器は壁・梁より600mm以上離す壁に取付け可能な場合、天井から150mm以上500mm以内離す換気扇・エアコン吹出口から1500mm以上離す

※ 全室LED照明とする。

※ 標準天井高さ2,400

※ 表記なきガラスは型ガラス

- * 凡例
- 管柱 (105×105)
 - K9'ンバー (3.30倍 FRM-0641)
 - 片筋違い (2.00倍 45×90) (例 左:柱脚 右:柱頭)
 - たすき掛筋違い (4.00倍 45×90)
 - 構造用合板 (2.70倍) (t=9 タイガ-EXHバー)
 - 床点検口
 - 天井点検口
 - 換気扇
 - 熱交換換気扇VLR-70

内装仕上: ホルムアルデヒド発散等級F☆☆☆☆等級相当
天井裏等: ホルムアルデヒド発散等級F☆☆☆☆等級相当

アドバンスシリーズ スマートデザイン (外部)	
凡例	
1	コンセント 1ヶ所
2	コンセント 2ヶ所
3	コンセント 3ヶ所
1ET	コンセント1ヶ所接地ターミナル付
2ET	コンセント2ヶ所接地ターミナル付
WP	コンセント 防水型
	エアコン用コンセント
	200V用コンセント
WP	防雨入線プレート
	スイッチ
3	3路スイッチ
4	4路スイッチ
	直結電源
TV	テレビ取出口
TEL	電話取出口 (テレホンガイド)
LAN	LAN取出口 (テレホンガイド)
	壁照明
	リモコン (給湯関係・ルフロ)
	メーター
	分電盤
	チャイム

※ACコンセント天井付け
※TVアンテナ工事
※スイッチはFL+1100、コンセントはFL+200

決定図