


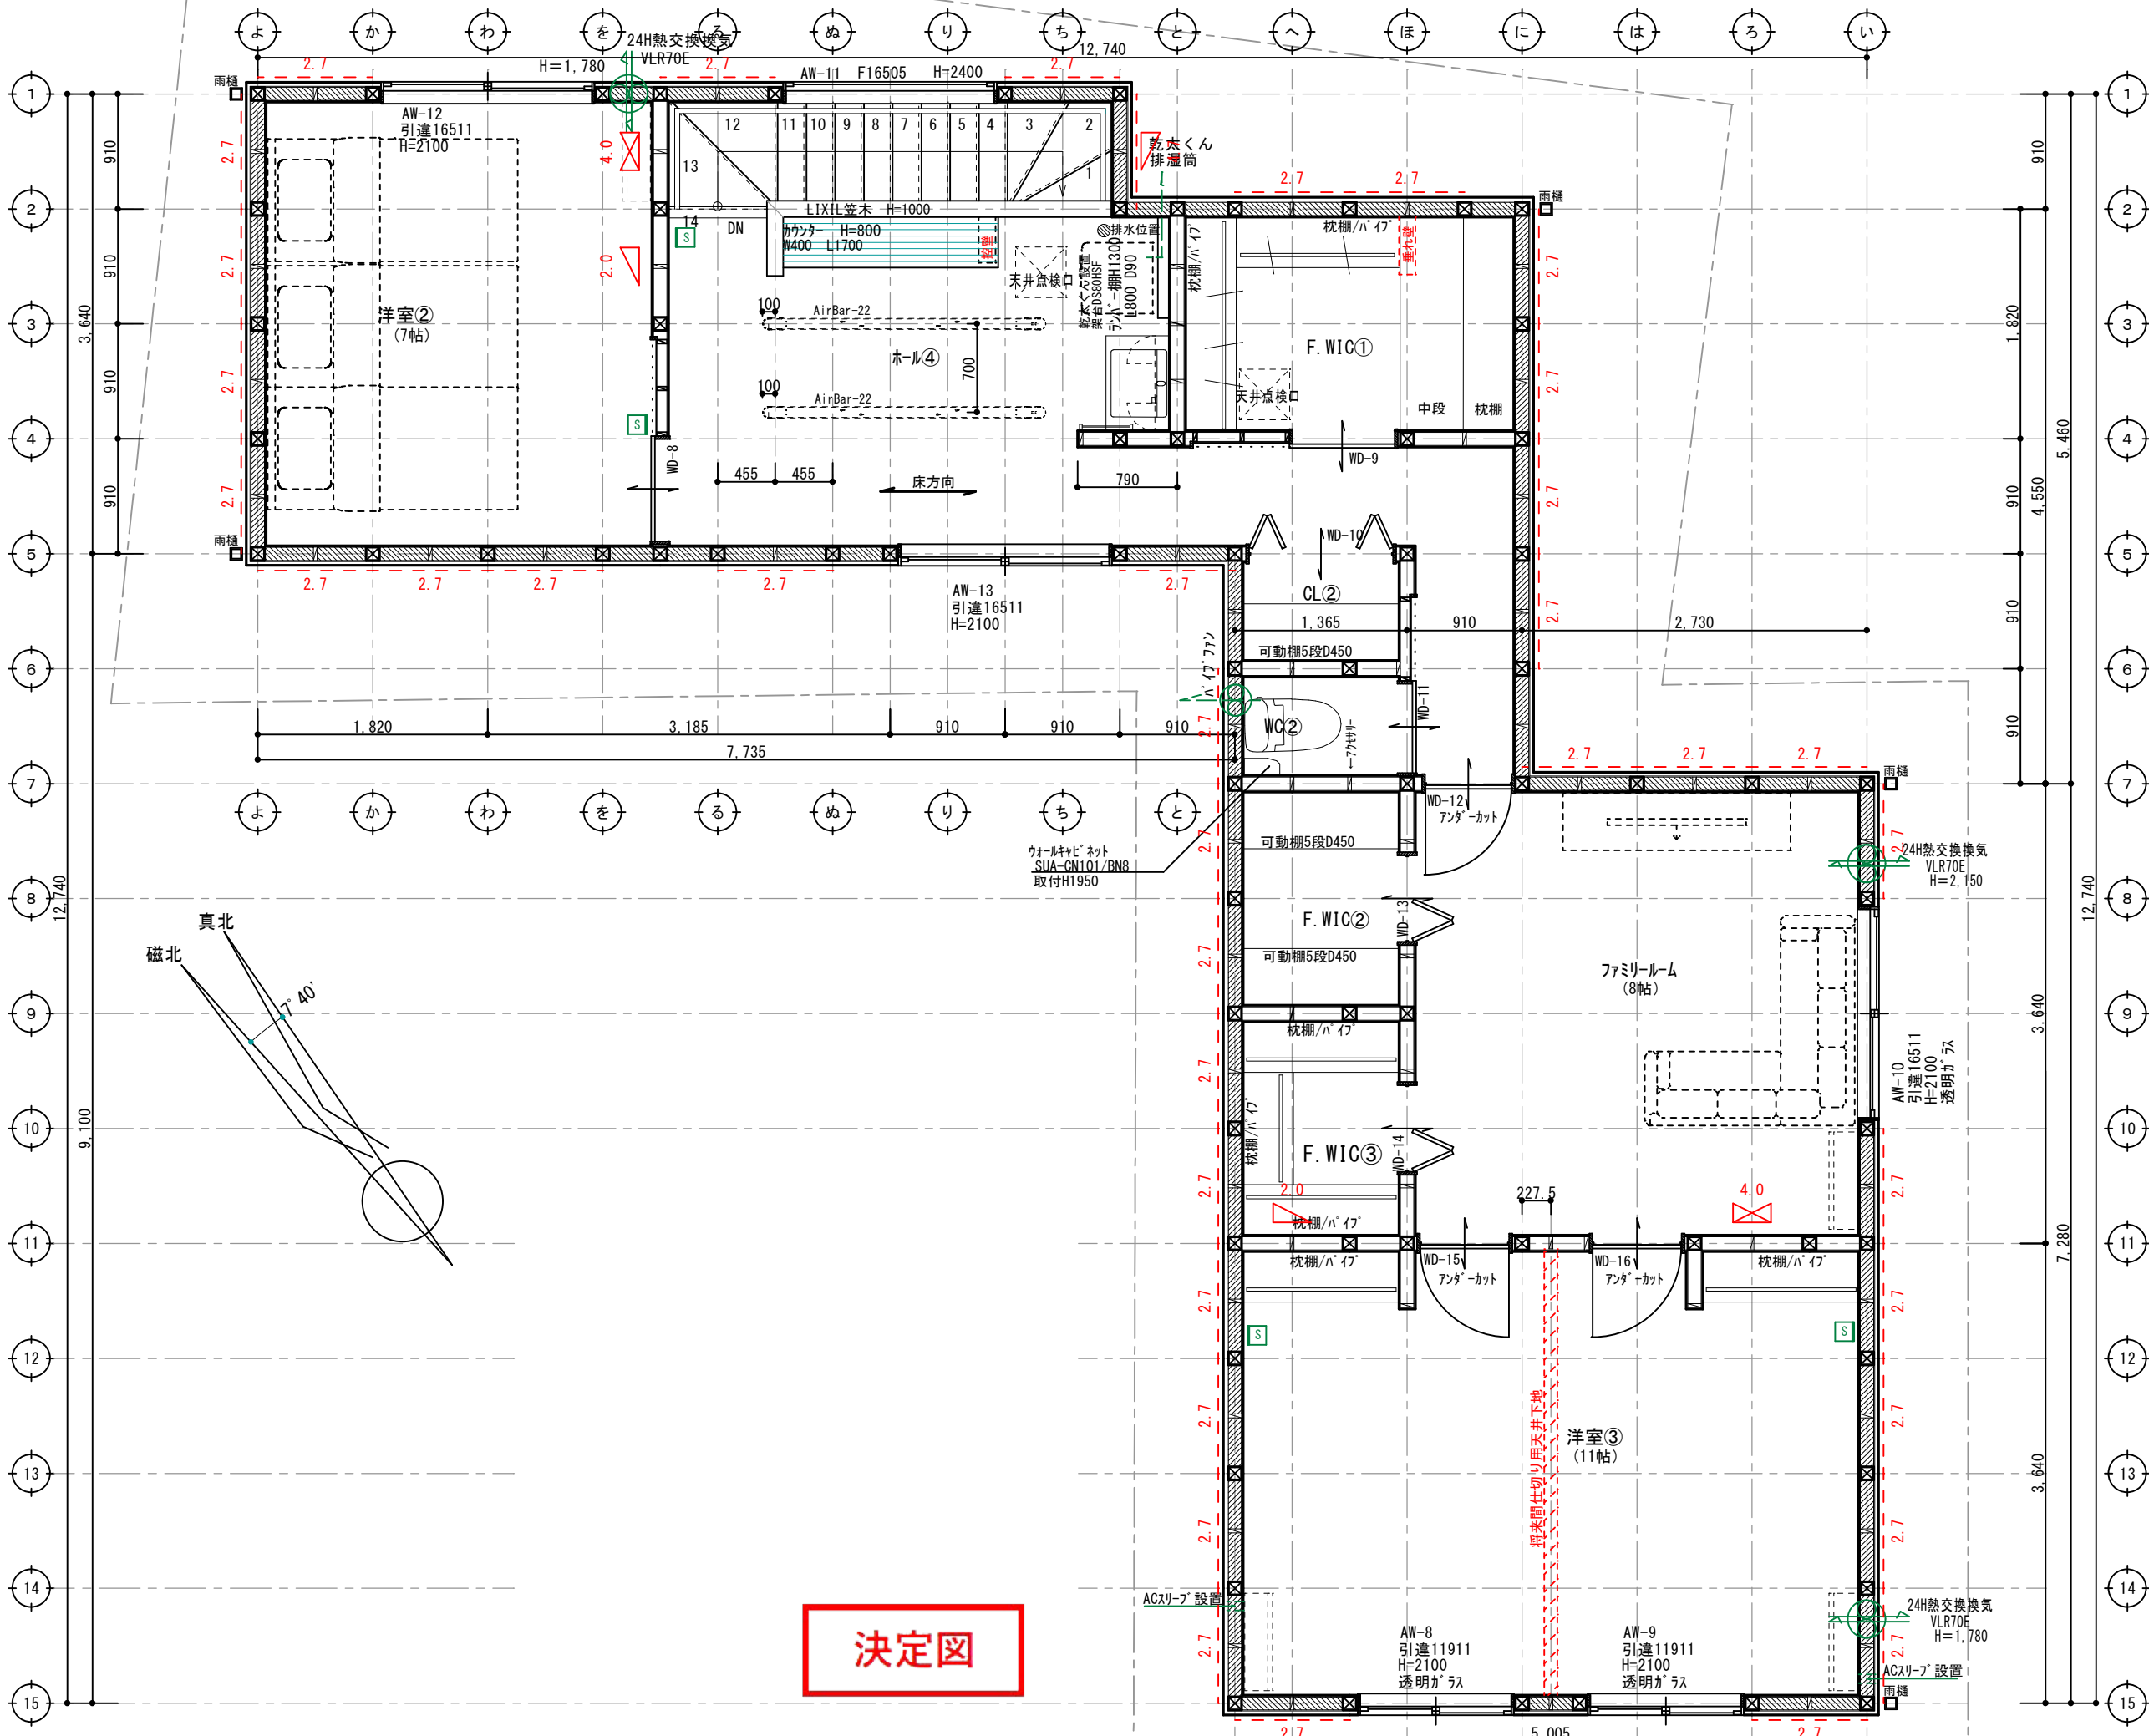

準防火地域

壁付け		数量
H	熱感知器	電池式(単独型)
	熱感知器	露出型
壁付け 住宅用火災報知器		数量
S	煙感知器	電池式(単独型)
	煙感知器	露出型

- ※ 煙感知器は壁・梁より600mm以上離す壁に取付ける場合、天井から150mm以上500mm以内離す換気扇・エアコン吹出口から1500mm以上離す
- ※ 全室LED照明とする。
- ※ 標準天井高さ2,400
- ※ 表記なきガラスは型ガラス

* 凡例

- 管柱 (105×105)
- Kタ'ンバー (3.30倍 FRM-0641)
- 片筋違 (2.00倍 45×90) (例 左:柱脚 右:柱頭)
- たすき掛筋違 (4.00倍 45×90)
- 構造用合板 (2.70倍) (t=9 タイガ・EXハイパー)
- 床点検口
- 天井点検口
- 換気扇
- 熱交換換気扇VLR-70

内装仕上: ホルムアルデヒド発散等級F☆☆☆☆等級相当
天井裏等: ホルムアルデヒド発散等級F☆☆☆☆等級相当

アドバンスシリーズ		スマートデザイン (外部)
凡例	1	コンセント 1ヶ所
	2	コンセント 2ヶ所
	3	コンセント 3ヶ所
	1ET	コンセント1ヶ所接地ターミナル付
	2ET	コンセント2ヶ所接地ターミナル付
WP		コンセント 防水型
		エアコン用コンセント
		200V用コンセント
WP		防雨入線プレート
		スイッチ
	3	3路スイッチ
	4	4路スイッチ
		直結電源
TV		テレビ取出口
TEL		電話取出口 (テレホンガイド)
LAN		LAN取出口 (テレホンガイド)
		壁照明
		リモコン (給湯関係・ルフロ)
		メーター
		分電盤
		チャイム

- ※ACコンセント天井付け
- ※TVアンテナ工事
- ※スイッチはFL+1100、コンセントはFL+200