


準防火地域



南側立面図 S=1/100

東側立面図 S=1/100

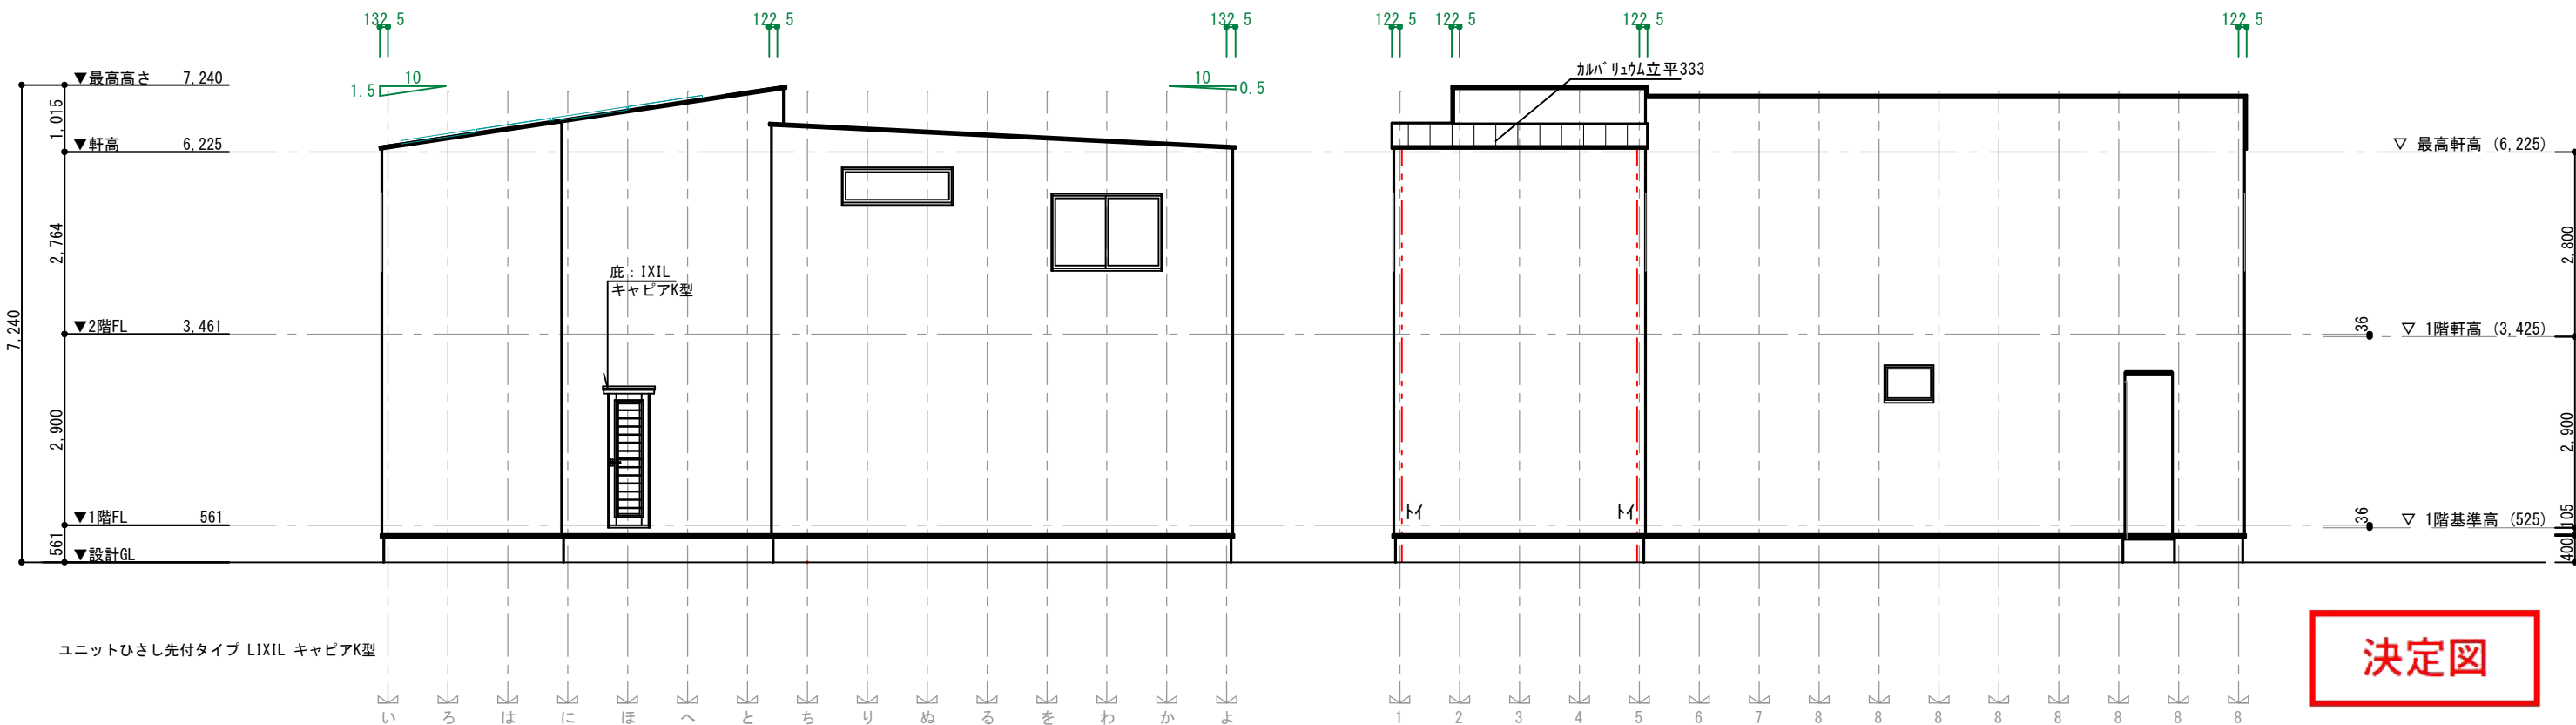

北側立面図 S=1/100

西側立面図 S=1/100

決定図

外壁開口部は全て防火戸（全て延焼線内）

|    |                                                                       |          |   |                                 |                               |  |          |    |          |         |
|----|-----------------------------------------------------------------------|----------|---|---------------------------------|-------------------------------|--|----------|----|----------|---------|
| 訂正 | 浜岡一級総合設計事務所<br>一級建築士事務所 静岡県知事登録第(10)2441号<br>一級建築士 大臣登録第 365879号 西原利昌 | PG HOUSE | 株式会社 LIFEFUND InDesign office 一級建築士事務所<br>事務所登録(2)第7595号 一級建築士登録 第179770号 鈴木 達男<br>〒432-8023 静岡県浜松市中央区鴨江3丁目70番23号 | 年月日<br>2025.4.20<br>縮尺<br>1/100 | 件名<br>外山裕也様 新築工事<br>図名<br>立面図 |  | 設計<br>倉田 | IC | 工事<br>青島 | 図番<br>4 |
|----|-----------------------------------------------------------------------|----------|---|---------------------------------|-------------------------------|--|----------|----|----------|---------|