




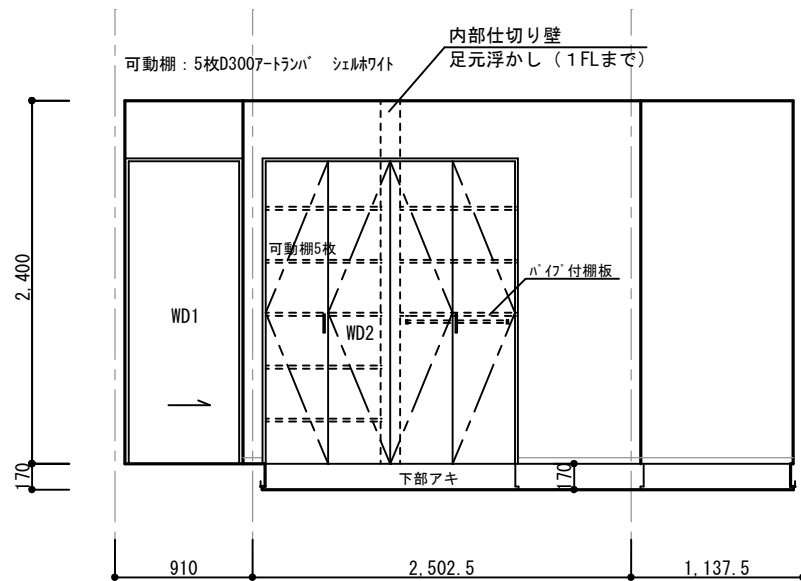


玄関 東面

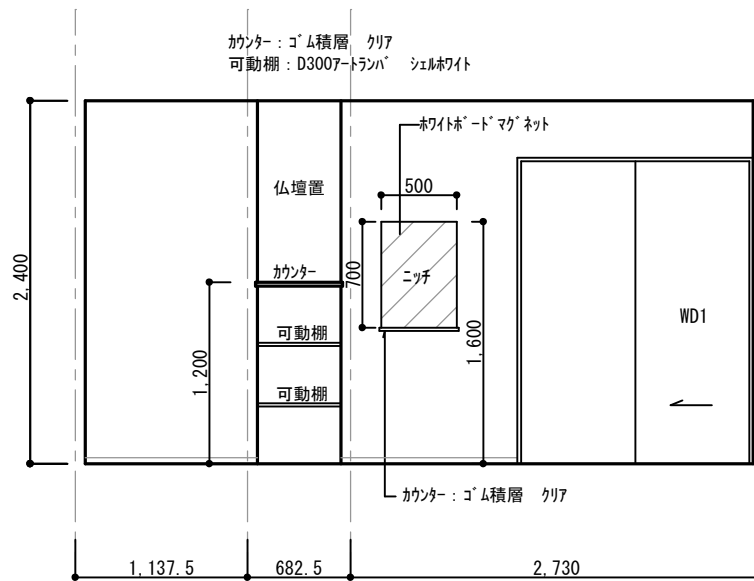

LDK 西面

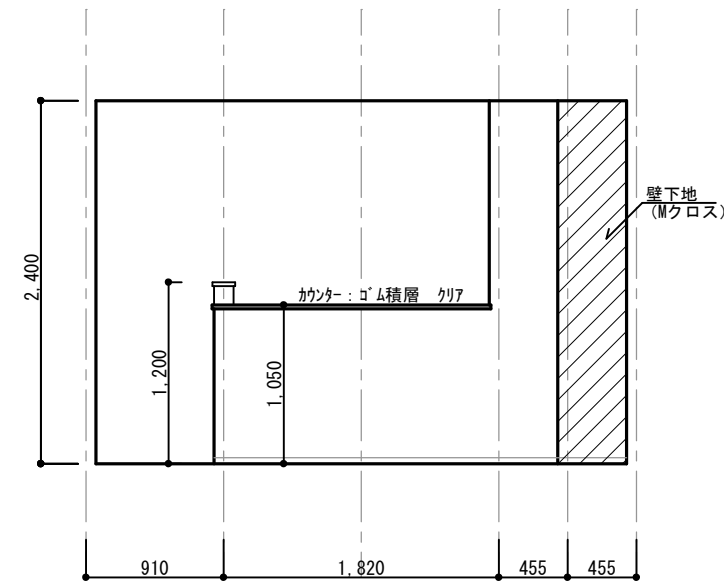


LDK 北面

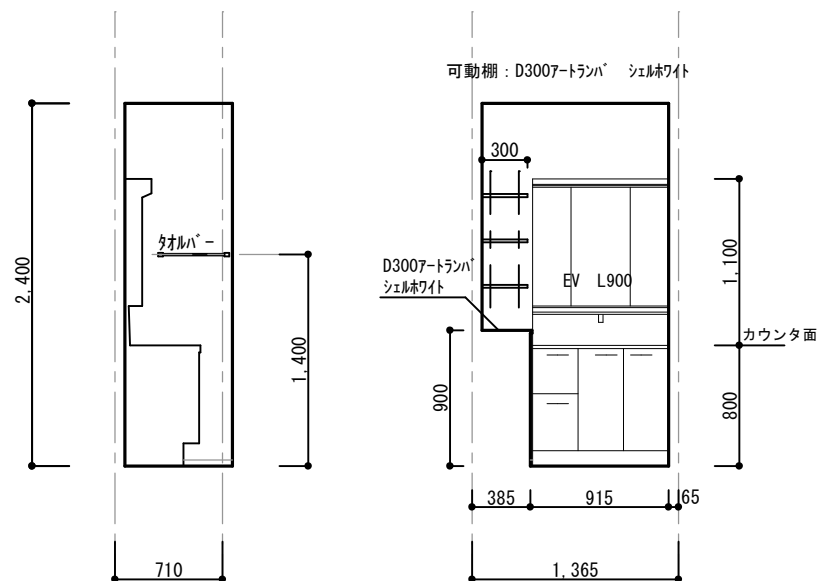


1階洗面 西面


1階洗面 南面

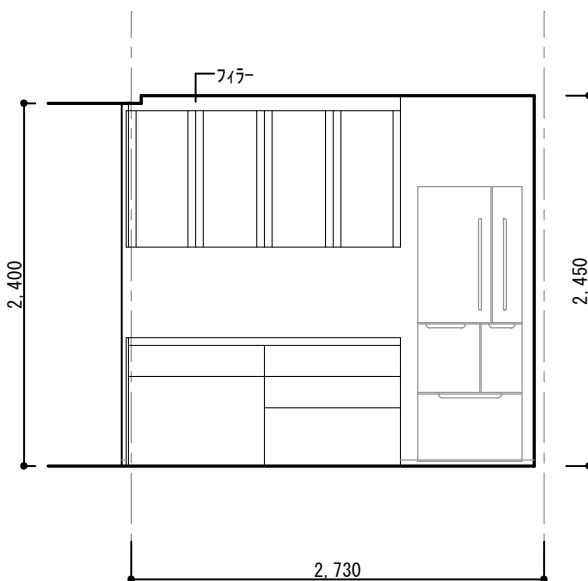


キッチン 北面

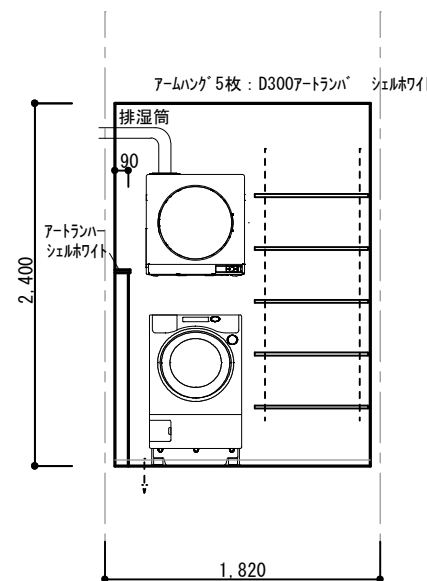

脱衣室 東面

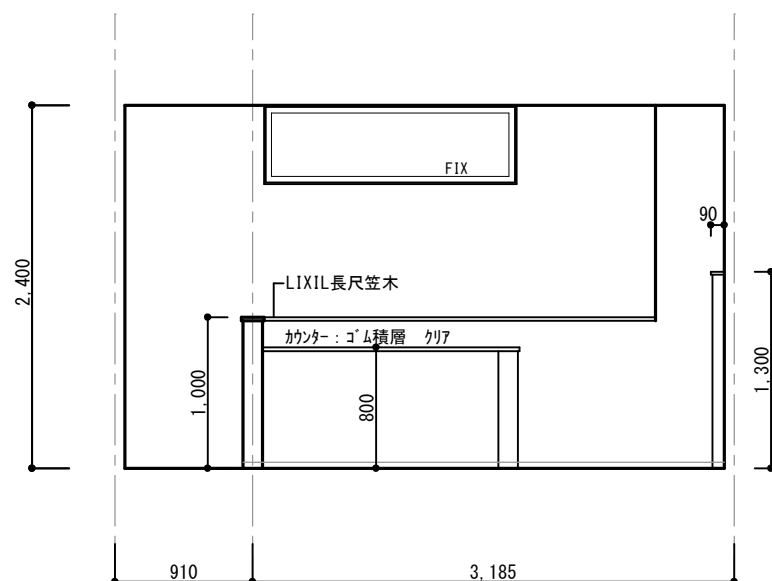


ホール④ 北面

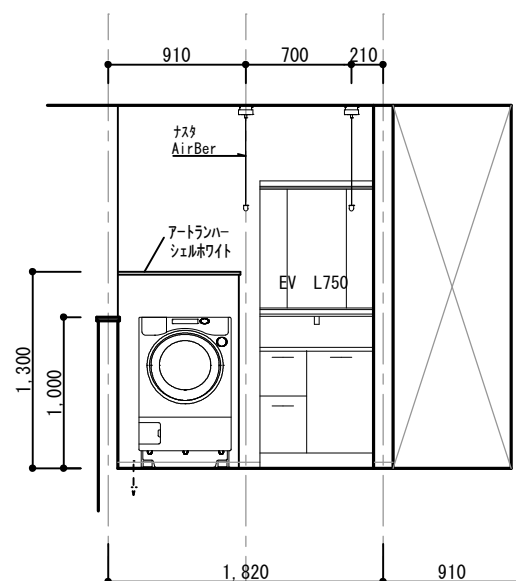

ホール④ 東面

決定図

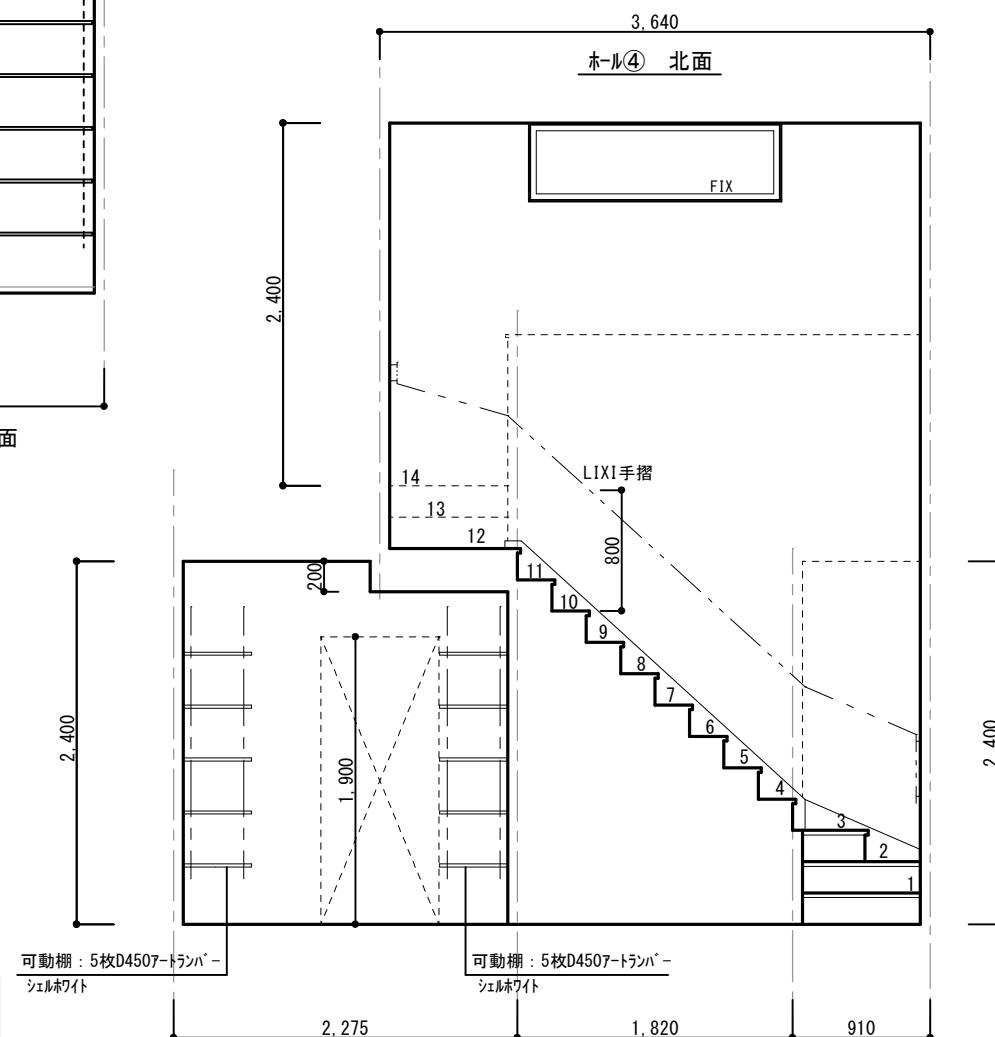

ホール③ 北面

ホール④ 北面

訂正	浜岡一級総合設計事務所 一級建築士事務所 静岡県知事登録第 (10)2441 号 一級建築士 大臣登録第 365879 号 西原利昌	LIFEFUND PG HOUSE	株式会社 LIFEFUND InDesign office 一級建築士事務所 事務所登録 (2) 第7595号 一級建築士登録 第179770号 鈴木 達男 〒432-8023 静岡県浜松市中央区鶴江3丁目70番23号	年月日 2025.4.20	件名 外山裕也様 邸新築工事	設計 倉田	IC	工事 青島	図番 6-1
縮尺 1/50	図名 展開図								