


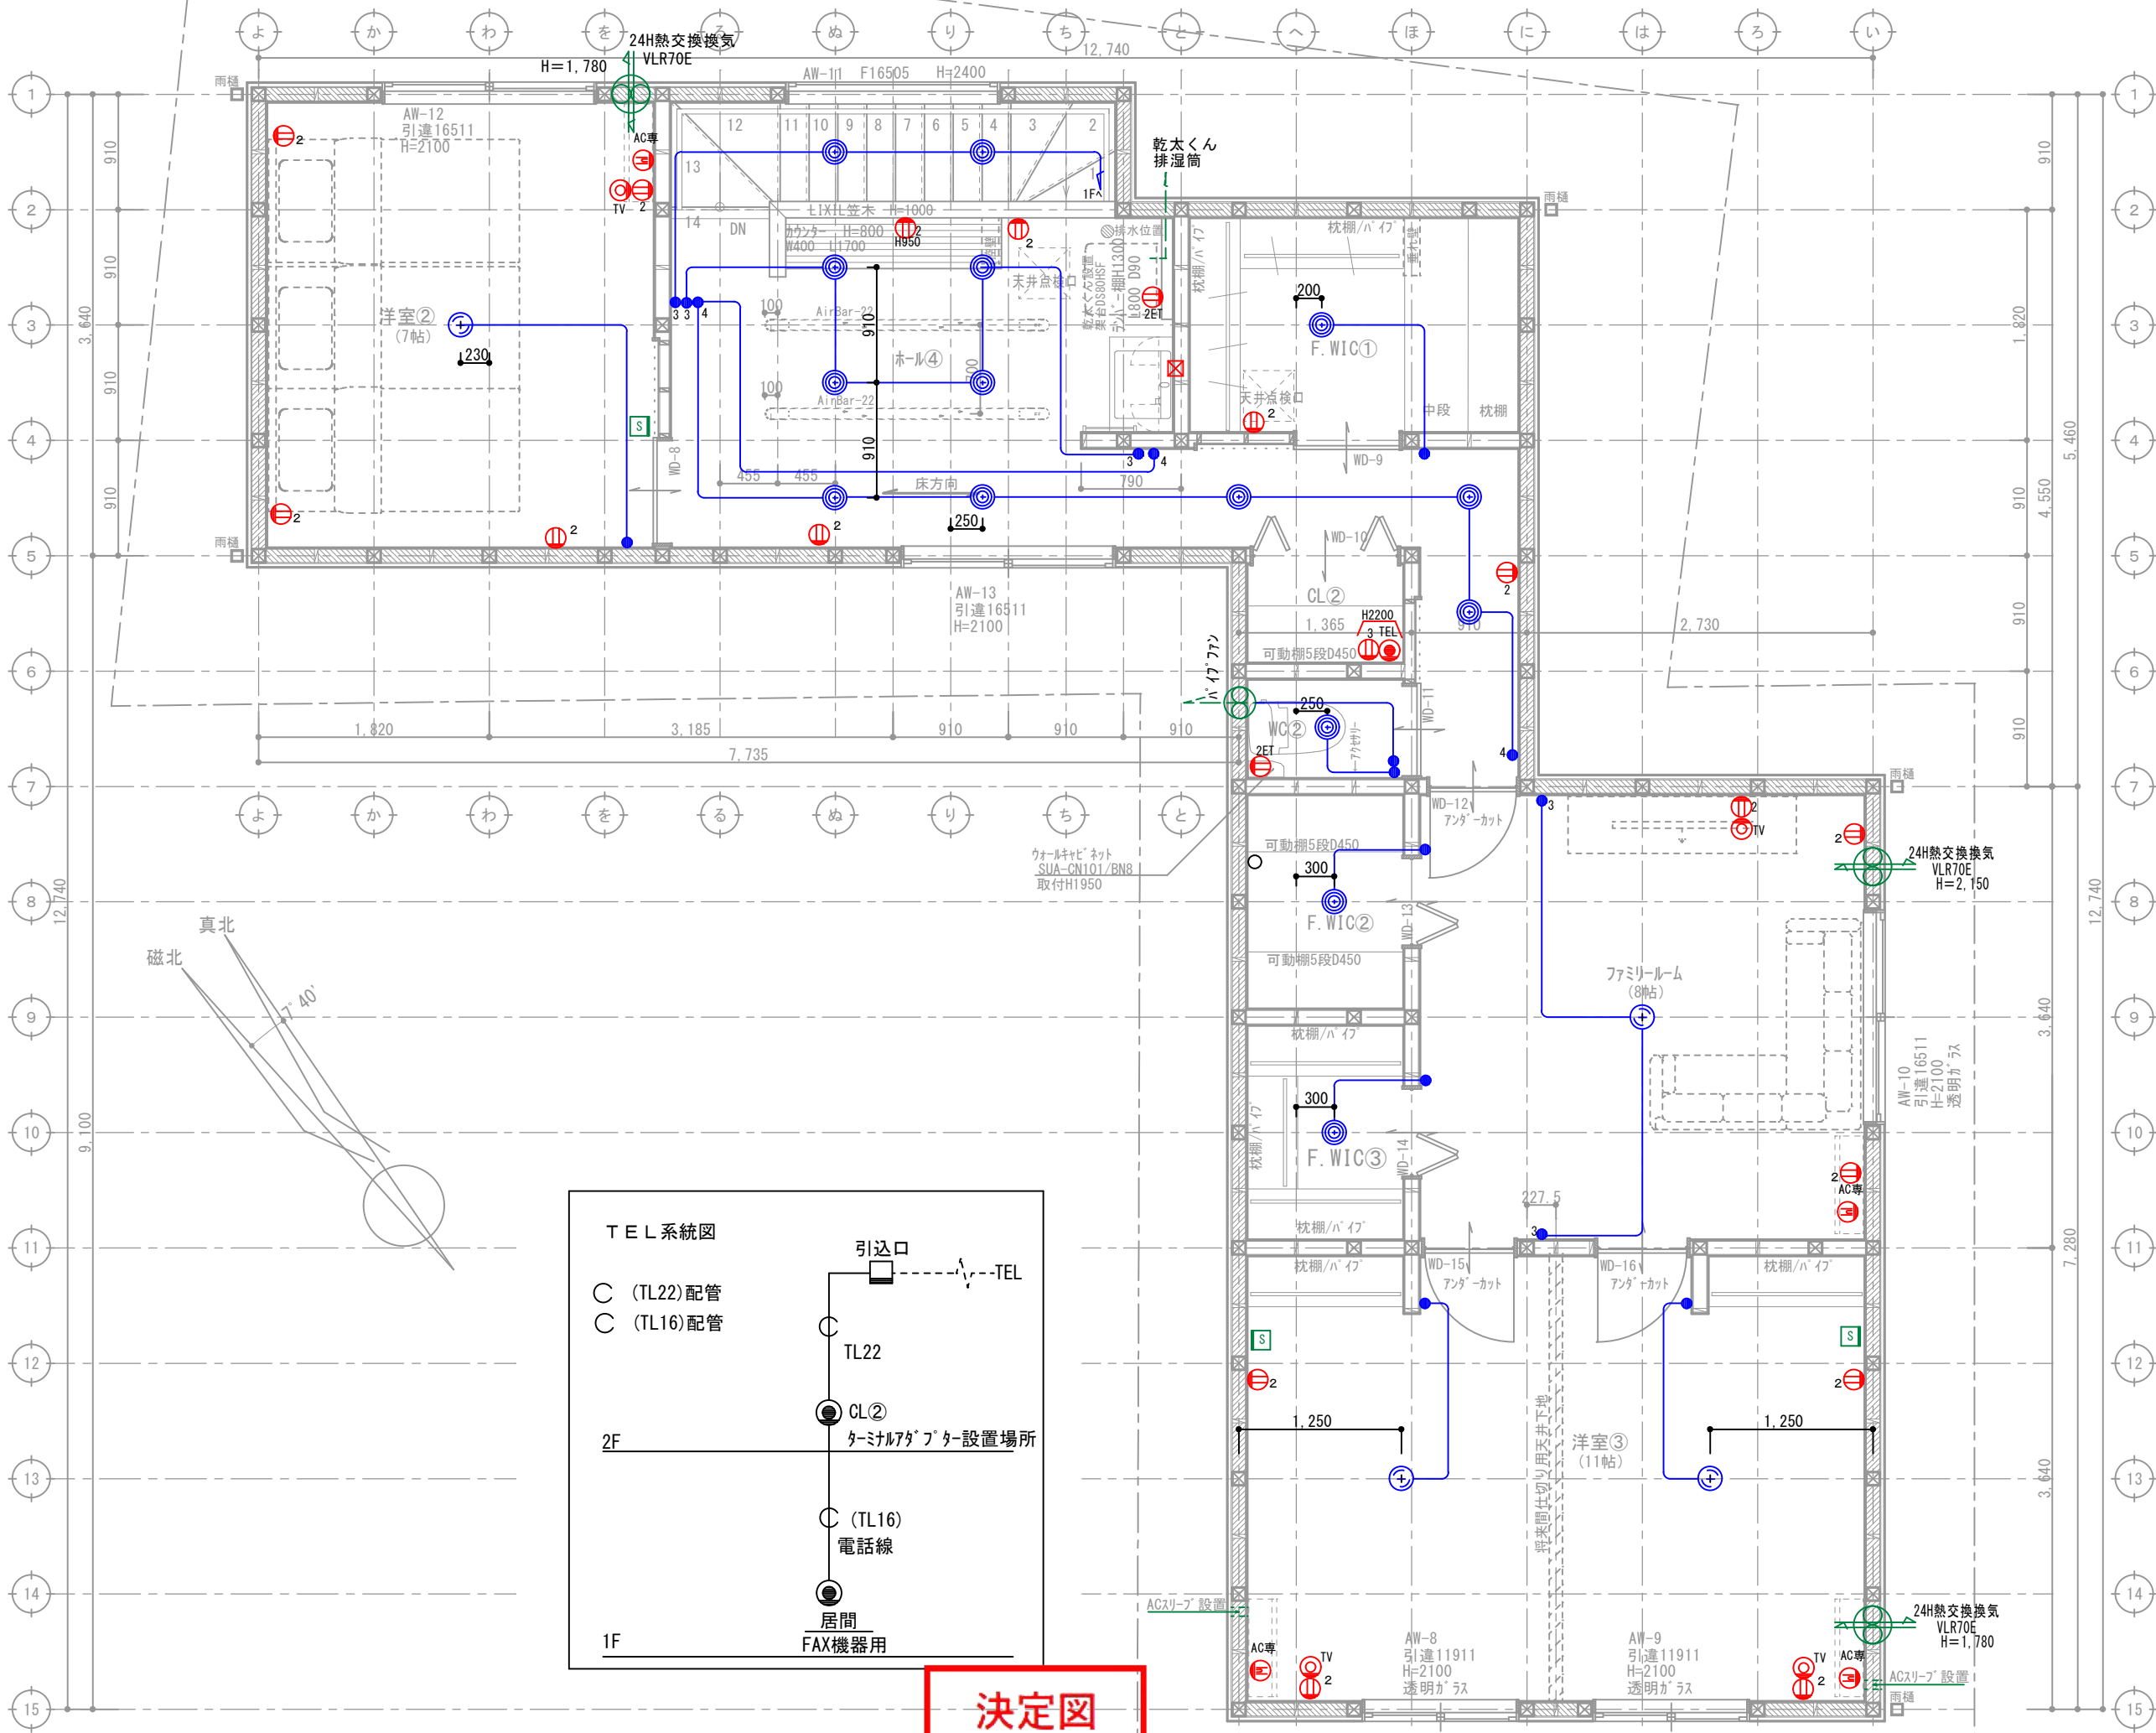

準防火地域


壁付け		数量
H 熱感知	電池式(単独型)	
	露出型	
壁付け 住宅用火災報知器		数量
S 煙感知	電池式(単独型)	
	露出型	

- ※ 煙感知器は壁・梁より600mm以上離す
壁に取付ける場合、
天井から150mm以上500mm以内離す
換気扇・エアコン吹出口から1500mm以上離す
- ※ 全室LED照明とする。
- ※ 標準天井高さ2,400
- ※ 表記なきガラスは型ガラス

* 凡例

- 管柱 (105×105)
- Kタ'ン' (3.30倍 FRM-0641)
- 片筋違い (2.00倍 45×90)
(例 左:柱脚 右:柱頭)
- たすき筋違い (4.00倍 45×90)
- 構造用合板 (2.70倍)
(t=9 タイガ'EXハ'ー)
- 床点検口
- 天井点検口
- 換気扇
- 熱交換換気扇VLR-70

内装仕上: ホルムアルデヒド発散等級F☆☆☆☆等級相当
天井裏等: ホルムアルデヒド発散等級F☆☆☆☆等級相当

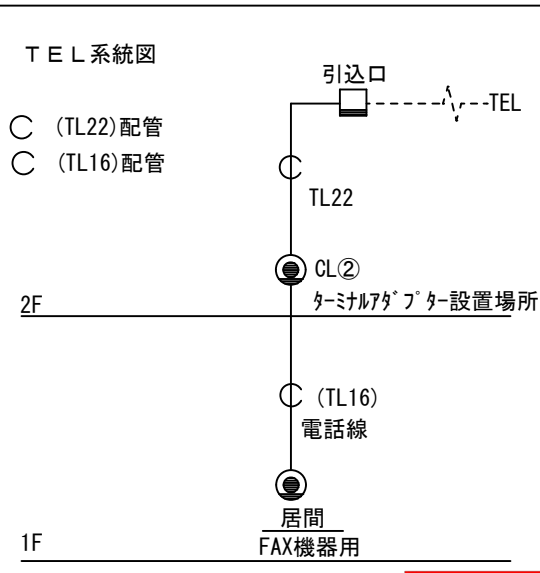

決定図

アドバンスシリーズ スマートデザイン (外部)	
凡例	
1	コンセント 1ヶ所
2	コンセント 2ヶ所
3	コンセント 3ヶ所
1ET	コンセント1ヶ所接地ターミナル付
2ET	コンセント2ヶ所接地ターミナル付
WP	コンセント 防水型
	エアコン用コンセント
	200V用コンセント
WP	防雨入線プレート
	スイッチ
3	3路スイッチ
4	4路スイッチ
	直結電源
TV	テレビ取出口
TEL	電話取出口 (テレホンガイド)
LAN	LAN取出口 (テレホンガイド)
	壁照明
	リモコン (給湯関係・ルフロ)
	メーター
	分電盤
	チャイム

- ※ACコンセント天井付け
- ※TVアンテナ工事
- ※スイッチはFL+1100、コンセントはFL+200