


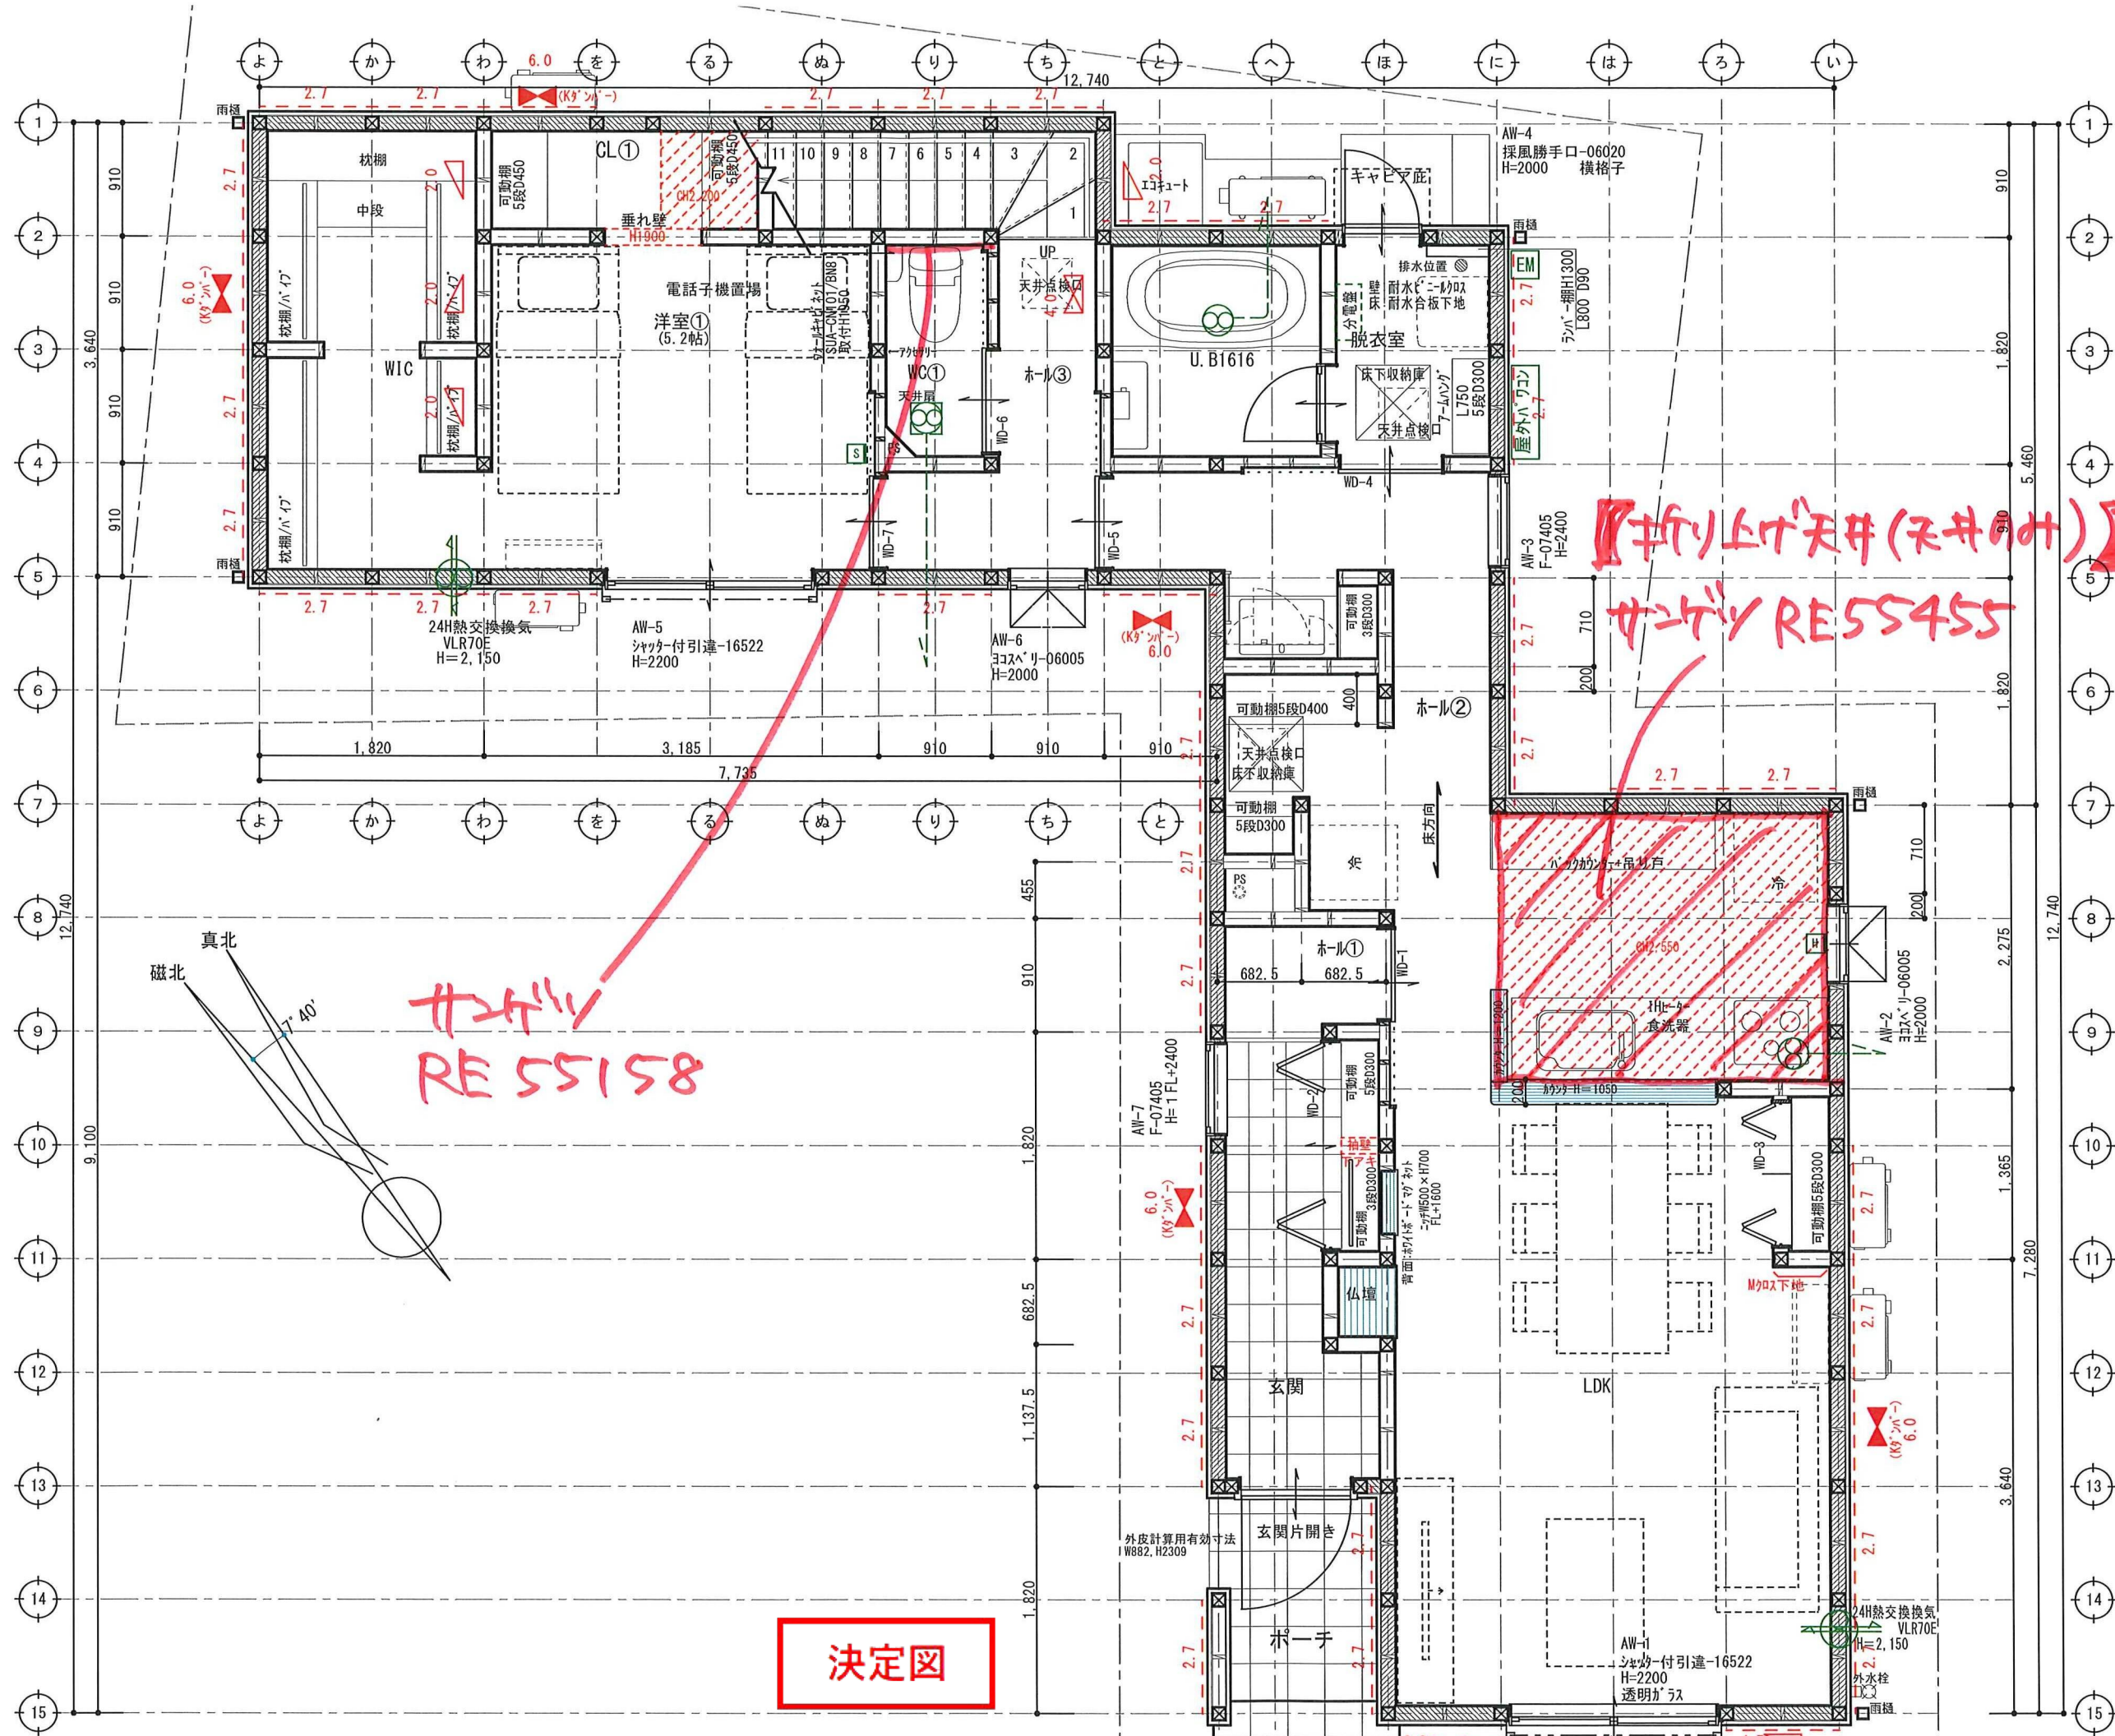

準防火地域

| 壁付け 住宅用火災報知器 |      |          | 数量 |
|--------------|------|----------|----|
| H            | 熱感知器 | 電池式(単独型) | 1  |
|              | 熱感知器 | 露出型      |    |
| 壁付け 住宅用火災報知器 |      |          | 数量 |
| S            | 煙感知器 | 電池式(単独型) | 1  |
|              | 煙感知器 | 露出型      |    |

※ 煙感知器は壁・梁より600mm以上離す  
壁に取付ける場合、  
天井から150mm以上500mm以内離す  
換気扇・エアコン吹出口から1500mm以上離す  
※ 全室LED照明とする。  
※ 標準天井高さ2,400  
※ 表記なきガラスは型ガラス

\* 凡例


- 管柱 (105×105)
- K9' ユニ (3.30倍 FRM-0641)
- 片筋違い (2.00倍 45×90)  
(例 左:柱脚 右:柱頭)
- たすき掛筋違い (4.00倍 45×90)
- 構造用合板 (2.70倍)  
(t=9 タイガ-EXNIN-)
- 床点検口
- 天井点検口
- 換気扇
- 熱交換換気扇VLR-70

内装仕上: ホルムアルデヒド発散等級F☆☆☆☆等級相当  
天井裏等: ホルムアルデヒド発散等級F☆☆☆☆等級相当

| アドバンスシリーズ<br>スマートデザイン (外部) |                  |
|----------------------------|------------------|
| 凡例                         |                  |
| 1                          | コンセント 1ヶ口        |
| 2                          | コンセント 2ヶ口        |
| 3                          | コンセント 3ヶ口        |
| 1ET                        | コンセント1ヶ口接地ターミナル付 |
| 2ET                        | コンセント2ヶ口接地ターミナル付 |
| WP                         | コンセント 防水型        |
| EA                         | エアコン用コンセント       |
| 200V                       | 200V用コンセント       |
| WP                         | 防雨入線プレート         |
| スイッチ                       | スイッチ             |
| 3                          | 3路スイッチ           |
| 4                          | 4路スイッチ           |
| 直結電源                       | 直結電源             |
| TV                         | テレビ取出口           |
| TEL                        | 電話取出口 (テレホンガイド)  |
| LAN                        | LAN取出口 (テレホンガイド) |
| 照明                         | 照明               |
| リモコン                       | リモコン (結露関係・ルフロ)  |
| メーター                       | メーター             |
| 分電盤                        | 分電盤              |
| チャイム                       | チャイム             |

※ACコンセント天井付け  
※TVアンテナ工事  
※スイッチはFL+1100、コンセントはFL+200



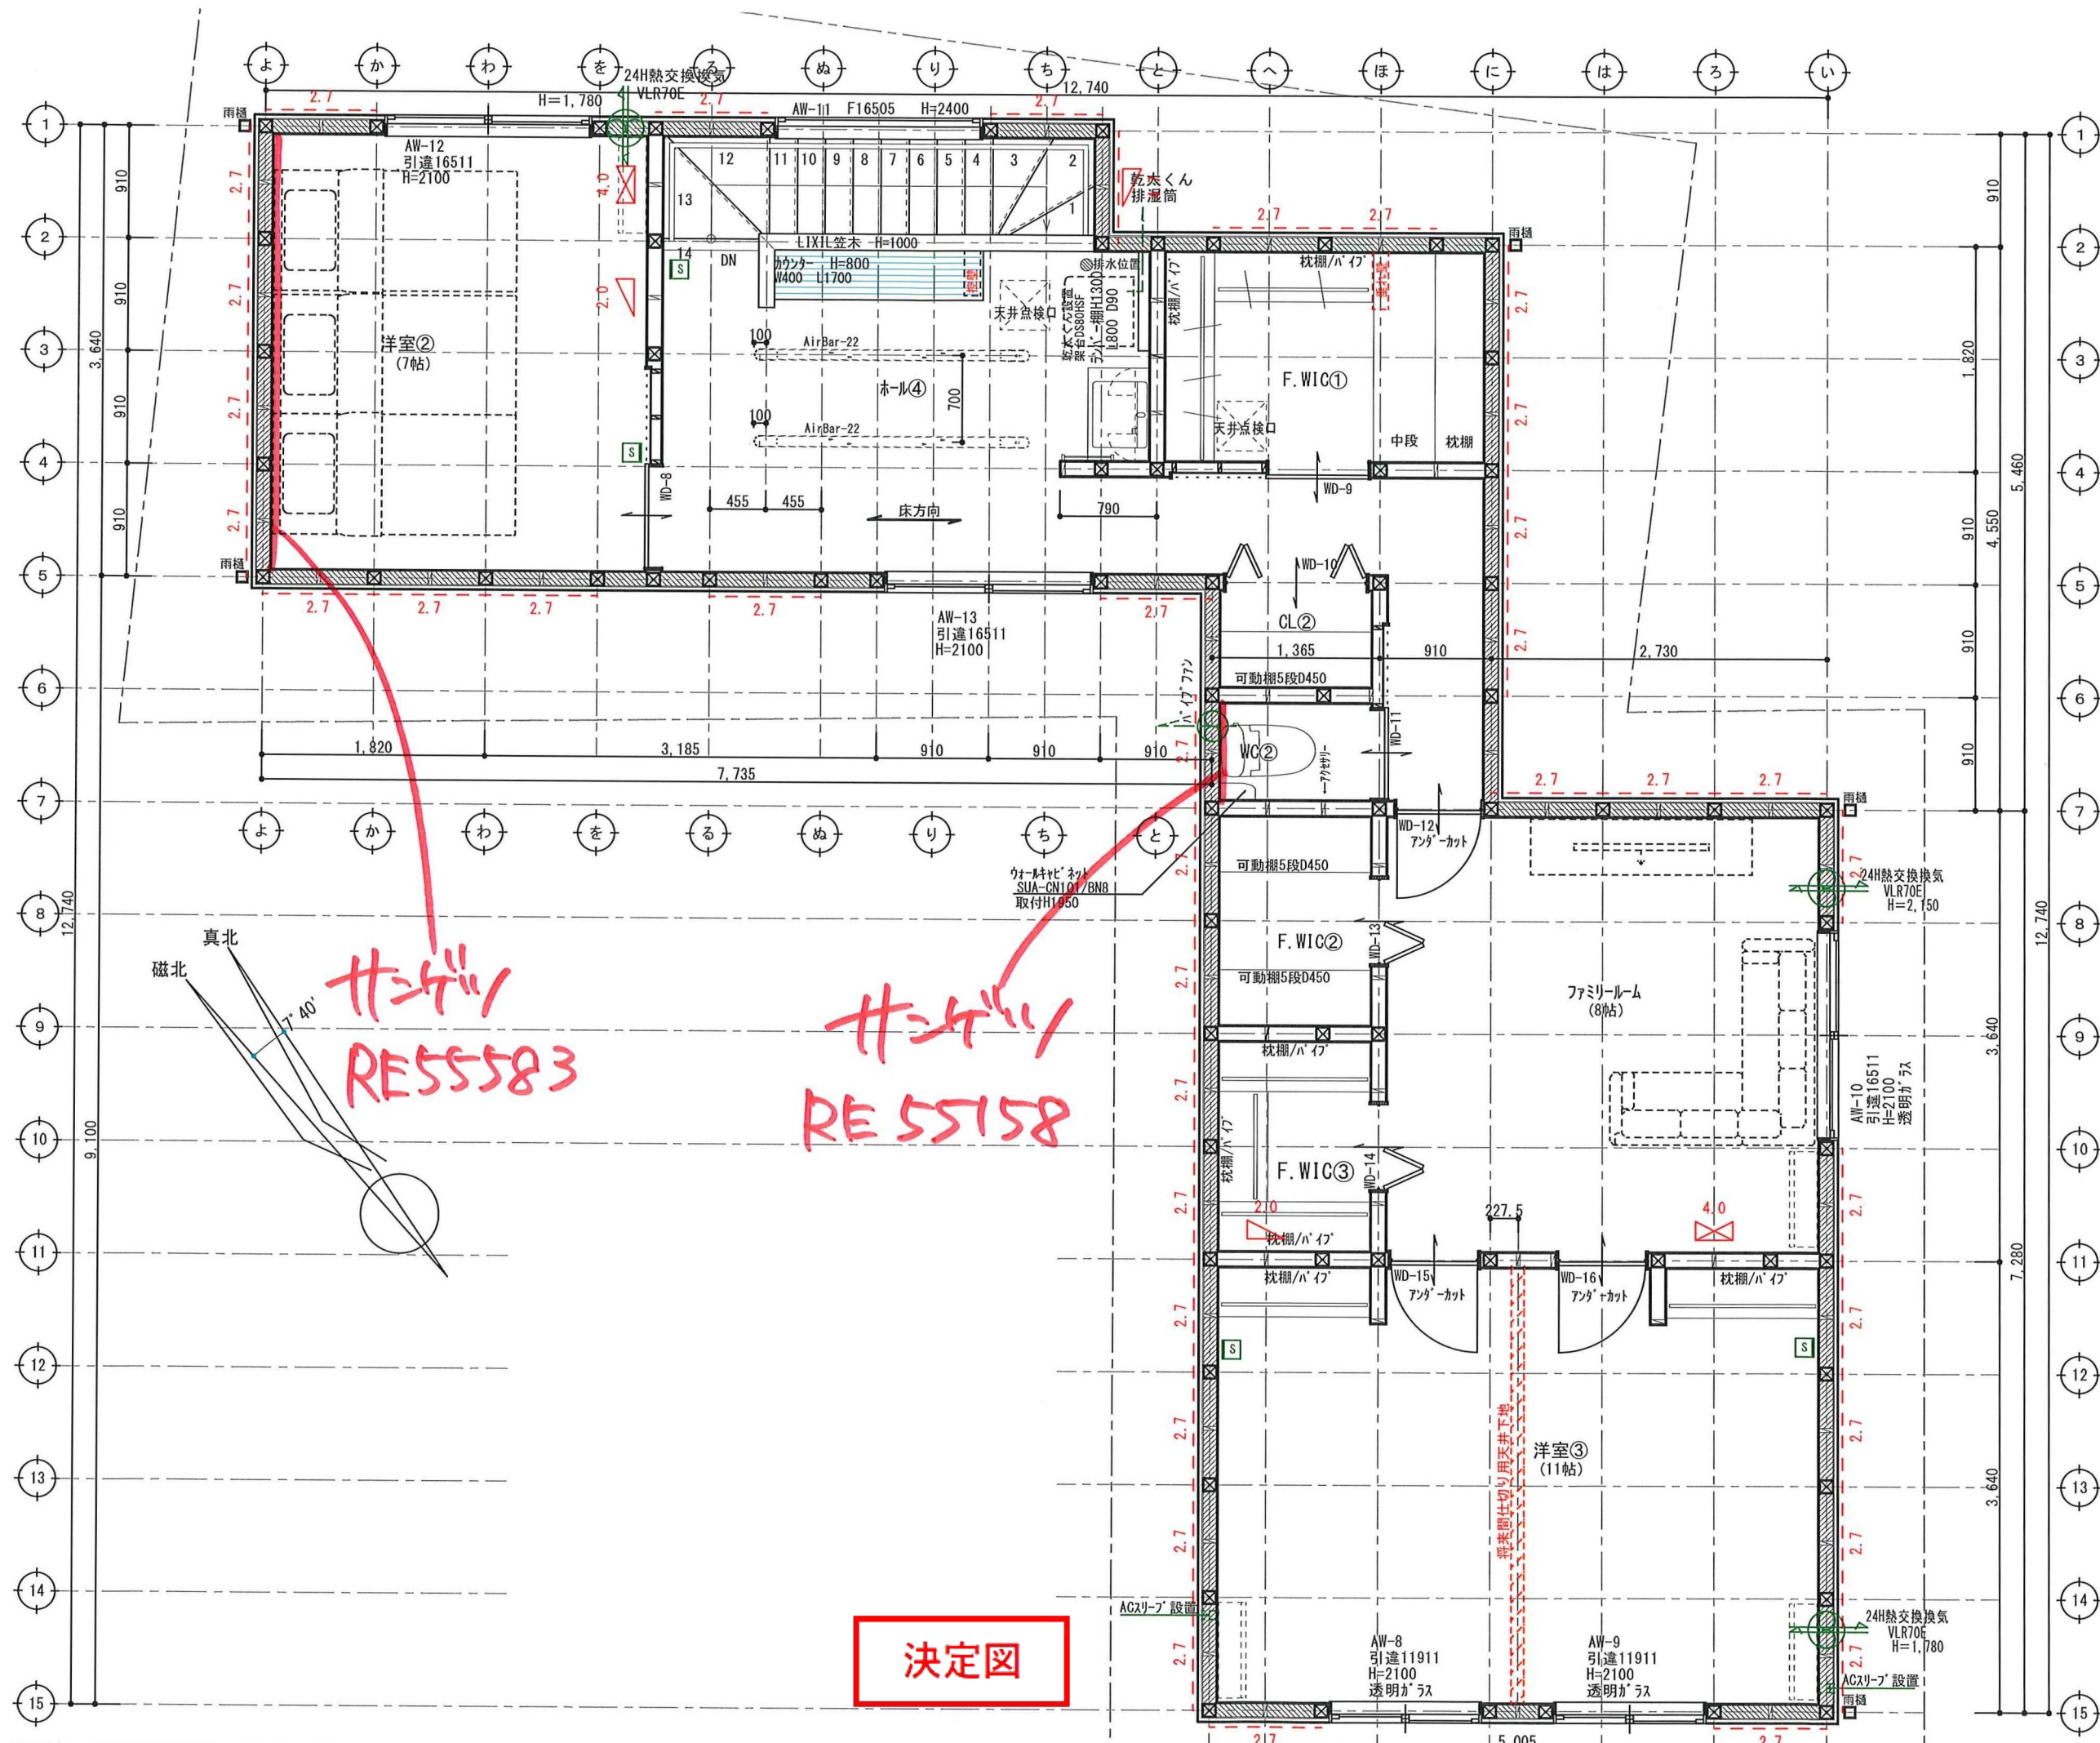

準防火地域

| 壁付け          |          | 数量 |
|--------------|----------|----|
| 熱感知          | 電池式(単独型) | 4  |
|              | 露出型      |    |
| 壁付け 住宅用火災報知器 |          | 数量 |
| 煙感知          | 電池式(単独型) | 4  |
|              | 露出型      |    |

- ※ 煙感知器は壁・梁より600mm以上離す  
壁に取付ける場合、  
天井から150mm以上500mm以内離す  
換気扇・エアコン吹出口から1500mm以上離す
- ※ 全室LED照明とする。
- ※ 標準天井高さ2,400
- ※ 表記なきガラスは型ガラス

\* 凡例

- ☒ 管柱 (105×105)
- △ K9' ユニ (3.30倍 FRM-0641)
- △ 片筋違 (2.00倍 45×90)  
(例 左:柱脚 右:柱頭)
- △ たすき掛筋違 (4.00倍 45×90)
- △ 構造用合板 (2.70倍)  
(t=9 タイプ-EXH(n-))
- △ 床点検口
- △ 天井点検口
- ⊕ 換気扇
- ⊕ 熱交換換気扇VLR-70

内装仕上: ホルムアルデヒド発散等級F☆☆☆☆等級相当  
天井裏等: ホルムアルデヒド発散等級F☆☆☆☆等級相当

| アドバンスシリーズ<br>スマートデザイン (外部) |                  |
|----------------------------|------------------|
| 凡例                         |                  |
| 1                          | コンセント 1ヶ所        |
| 2                          | コンセント 2ヶ所        |
| 3                          | コンセント 3ヶ所        |
| 1ET                        | コンセント1ヶ所接地ターミナル付 |
| 2ET                        | コンセント2ヶ所接地ターミナル付 |
| WP                         | コンセント 防水型        |
| WP                         | エアコン用コンセント       |
| WP                         | 200V用コンセント       |
| WP                         | 防雨入線プレート         |
| 3                          | スイッチ             |
| 4                          | 3路スイッチ           |
| 4                          | 4路スイッチ           |
| TEL                        | 直結電源             |
| TEL                        | テレビ取出口           |
| LAN                        | 電話取出口 (テレホンガイド)  |
| LAN                        | LAN取出口 (テレホンガイド) |
| 照明                         | 壁照明              |
| リモコン                       | リモコン (結露関係・ルフロ)  |
| メーター                       | メーター             |
| 分電盤                        | 分電盤              |
| チャイム                       | チャイム             |

- ※ ACコンセント天井付け
- ※ TVアンテナ工事
- ※ スイッチはFL+1100、コンセントはFL+200