


■ 仕 様			■ HEAT20 G1		
断熱工事		■ 床:カネライトフォーム t65 ■ 土間床等の外周:スタイロフォームAT t25 ■ 壁:アクアフォームLITE吹付 t85 ■ 天井:アクファフォームLITE吹付 t170			
床下換気		■ 基礎パッキン JOTO (玄関・UB周り:気密基礎パッキン)			
防虫防蟻		■ 土壌処理・木部 ガントナーMC			
■ 外 部 仕 上 表			準防火地域		
部位		仕上・仕様・メーカー		色番・品番	
屋根		■ ガルバリウム鋼板(t0.35)UK立平 ニスクカラーPro GH 軒先通気金物 日本住環境株式会社【REV-15】		GHK01 Sブラック	
パラペット笠木		■ なし			
破風・鼻隠		■ なし			
雨樋	(軒樋)	■ Panasonic サーフeskエアFS-I型		モダンベージュ	
	(縦樋)	■ Panasonic S30角樋		モダンベージュ	
軒天	屋根軒	■			
	ポーチ軒	■ 神島化学 t= 12mm 軒天ボード エンボス※準防火地域		Wミルトアイポリー	
	バルコニー軒	■			
		■			
外壁	通気金物(15mm)	■メイン	ニチハ エモンエクセラード16 Vシリーズ シャルムロックV		コンティMGアッシュ
	※下地面材:タイガーEXハイパー	■アクセントA	なし		
	防火認定 PC030BE-4028	■アクセントB	なし		
玄関ポーチ		■ 床 LIXILパセオ300/PSO-BR 2		-	
基礎		■ 立上り巾木: モルタル刷毛引き		-	
基礎水切り金物		■ JOTO鋼板製 防鼠材付き水切り JOTO:WMF-N35		シルバー	
バルコニー	床・内壁	■ なし		-	
	笠木	■ なし			
外部建具 ※準防火仕様		■ LIXIL防火戸FG-H(アルゴンガス高遮熱LowE複層 グリーン) ・SD、TSで記載がないものは、オペレーターハンドルとする ・オペレーター付サッシは固定網戸とする ・グレモンハンドル式サッシの選択箇所は可動網戸とする		外観 ホワイト 内観 ホワイト ※樹脂パッキン・網戸付	
シャッター		■ 1階の掃き出し窓 手動			
軒天通気金物					
玄関扉 ※準防火仕様=防火戸 ※検討中		■ LIXIL ジエスタ2 K2仕様 LIXILファミロック タグキー×3 (電池式) 防火戸		ドア型: M26 型 ドア色: クリエモカ ハンドル: S型ハンドル 色 ブラック	
アルミ勝手口庇		■ LIXIL キャピア K型		外壁	
外部物干し金物		■			
換気フード		■ 局所換気扇(トイレ 浴室 キッチンフード) ※防火ダンパー(防火処置)必要箇所は平面図による		外気フード: ホワイト	
		■ ダクトレス熱交換換気システム (日本スティーベル株式会社) VLR-70DF(防火仕様品) ※防火ダンパー(防火処置)必要箇所は平面図による		外気フード: W ホワイト 室内パネル ホワイト	

■ 構 造 概 要					
基礎	■ RCベタ基礎コンクリート				
通し柱・管柱	■ 構造用集成材 105×105		間柱	■ 集成材	
土台	■ 桧 105×105	大引き	■ 桧 90*90	筋交い	■ 構造用製材 火打梁 ■ 鋼製火打(当社基準により米松あり)
桁・梁	■ 構造用製材及び集成材		制震装置	■ Kダンパー (株)アイ・エム・エー	
■ 設 備 装 着 品					
住宅設備	部位	メーカー	商品名 ※ 詳細は見積り、プレゼン参照	見積りNo.	(日付)
	キッチン	LIXIL	■ ES I型 扉グレージュスタック 天板ステンレストップ キッチンパネル:フレッシュホワイト 標準食洗器 標準IH、壁付レンジフードASR(シルバー)	見積り番号 : M24126001673-006-2 (日付)	2025/4/28
	バックカウンタ ※オプション	LIXIL	■ ES L1800(W900スライドストッカー+マルチスペース) 吊り戸	見積り番号 : M24126001673-006-3 (日付)	2025/4/28
	浴室	LIXIL	■ AX1616 PGハウス標準仕様 開き戸:ホワイト アクセント壁:チェリー 浴槽:ストレートライン ベージュ 床:ベージュ マグネットシェフ:ホワイト	見積り番号 : M24126001673-006-1 (日付)	2025/4/28
	1Fトイレ	LIXIL	■ ベーシアシャワートイレ 白 ● タオル掛け: タンク手洗 無し ● 紙巻き器: CF-AA22H /WA	見積り番号 : M24126001673-006-6 (日付)	2025/4/28
	2Fトイレ	LIXIL	■ ベーシアシャワートイレ 白 ● タオル掛け: タンク手洗 無し ● 紙巻き器: CF-AA22H /WA	見積り番号 : M24126001673-006-7 (日付)	2025/4/28
	1F洗面台	LIXIL	■ EV W900(D500タイプ) 扉:クリエモカ [引出しタイプ シングルハンドシャワー スタンダードLED三面鏡 その他 ● タオル掛け:KF-AA71D(白)	見積り番号 : M24126001673-006-4 (日付)	2025/4/28
	W900				
	2F洗面台	LIXIL	■ EV W750(D500タイプ) 扉:クリエモカ [引出しタイプ シングルハンドシャワー スタンダードLED三面鏡 その他 ● タオル掛け:KF-AA71D(白)	見積り番号 : M24126001673-006-5 (日付)	2025/4/28
	W750				
給排水設備	給湯器	■ エコキュート370L Panasonic Sシリーズ スタンダードモデル 追い焚きフルオート			
	排水	■ 下水			
	外水栓	■ 1 カ所 (平面図参照)	■ 外部立栓柱: PVC製 水栓柱12型【前澤化成工業】		
	外部ガーデンパン	■ 無し			
	その他	■ 洗濯機用単水栓: 緊急止水弁付 ■ 洗濯機用排水:トラップ金物(標準) ■ 排水さや管(長期優良住宅仕様)			
ガス配管設備		■ あり(都市ガス) (配置図・平面図参照) ■ガス使用器具 乾太くん+ガスコンロ			架台DS-80HSF
電気設備	インターホン	■ パナソニック VL-SZ30KL			
	TVアンテナ	■ UHF + BS・110度CS／CSアンテナ [2K・4K・8K対応] ■ホワイト			
	エアコン	■ 有 設置場所: 図面参照			
	ソーラー	■ あり(Qセルズ) 12 枚 5.28 KW Re.RISE-G3 440 (1722×1134×30)			
	※標準搭載	※メーカーのモデルチェンジ等で後継品に変更される可能性あり ■ 屋外パワコン			
その他					
決定図					

決定図


		浜 岡 一 級 総 合 設 計 事 務 所		 株式会社 LIFEFUND InDesign office 一級建築士事務所		年 月 日	2025/5/1		件名	外山 裕也様			設計	IC	工務	図 番
		一級建築士事務所 静岡県知事登録第 (10)2441 号 一級建築士 大臣登録第 365879 号 西原利昌		事務所登録 (2)第7595号 一級建築士登録 第179770号 鈴木 達男 〒432-8023 静岡県浜松市中央区鴨江3丁目70番23号		縮尺			図面	仕上表 1			倉田		青島	1-1

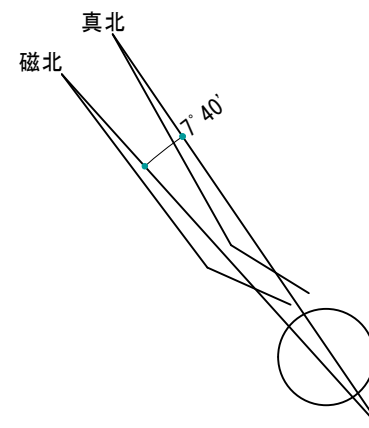

トータル面積表 (㎡)	
敷地面積	155.14
建築面積	74.11
床面積 1階	71.63
2階	74.11
延床面積	145.74
建築率	$(74.11/155.14) \times 100$
容積率	$(145.74/155.14) \times 100$

決定図


訂 正	浜 岡 一 級 総 合 設 計 事 務 所 一級建築士事務所 静岡県知事登録第 (10)2441 号 一級建築士 大臣登録第 365879 号 西原利昌	LIFEFUND PG HOUSE	株式会社 下 LIFEFUND InDesign office 一級建築士事務所 事務所登録 (2) 第7595号 一級建築士登録 第179770号 鈴木 達男 〒432-8023 静岡県浜松市中区鳴江3丁目70番23号	年 月 日	件 名	設計	IC	工事	図 番
				縮 尺	2025. 4. 20 図 名				

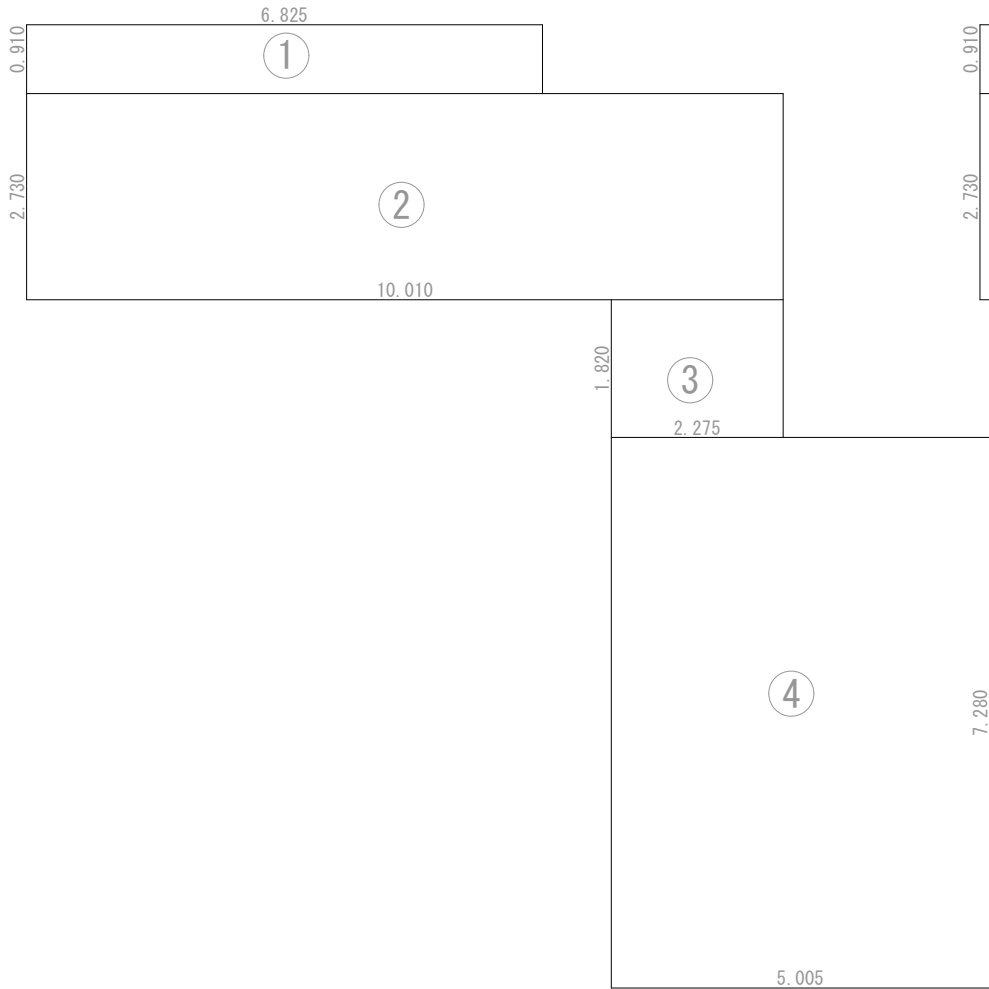

建築面積求積図 S=1/100

建築面積求積表


番号	計算式 (m)	面積 (㎡)
①	6.825 × 0.910	6.21075
②	10.010 × 2.730	27.3273
③	2.275 × 1.820	4.1405
④	5.005 × 7.280	36.4364
合計	≒	74.11495 74.11

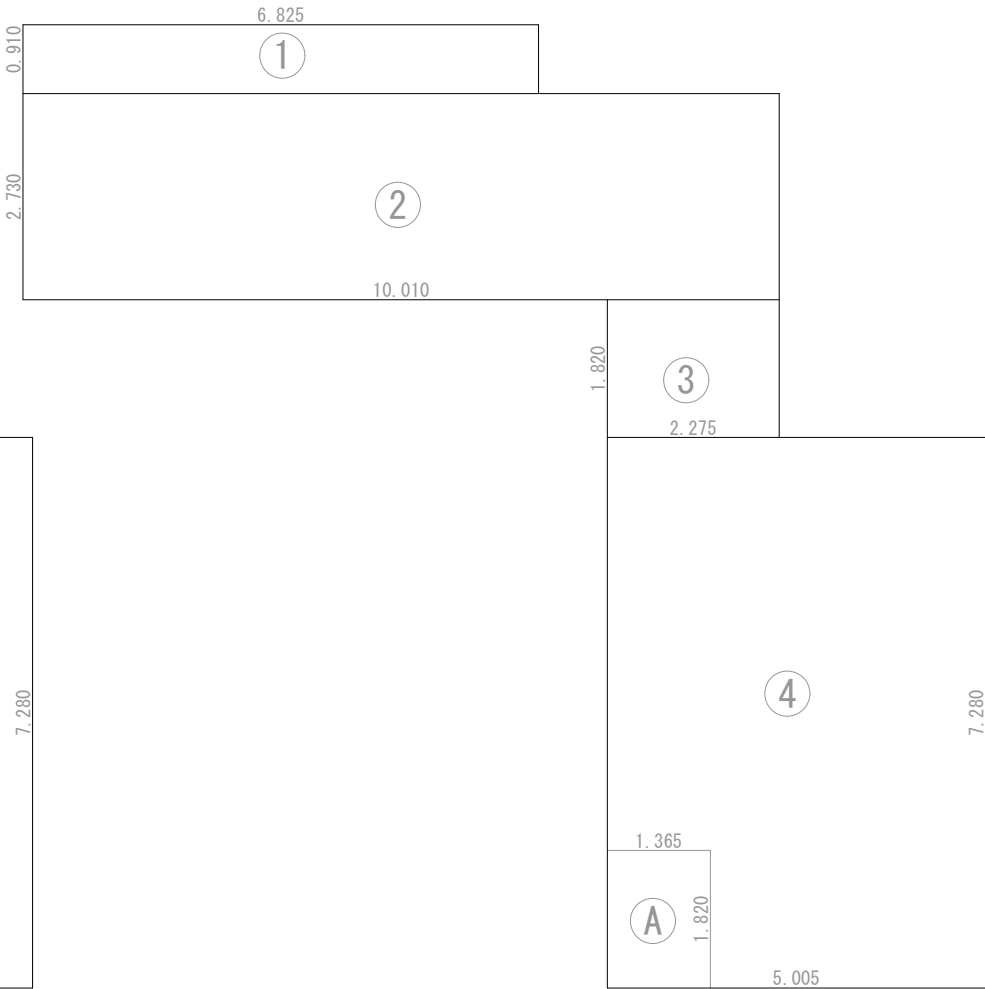

1階床面積図 S=1/100

1階床面積求積表

番号	計算式 (m)	面積 (㎡)
①	6.825 × 0.910	62.1075
②	10.010 × 2.730	27.3273
③	2.275 × 1.820	4.1405
④	5.005 × 7.280	36.4364
A	-1.365 × 1.820	-2.4843
合計	≒	71.63065 71.63

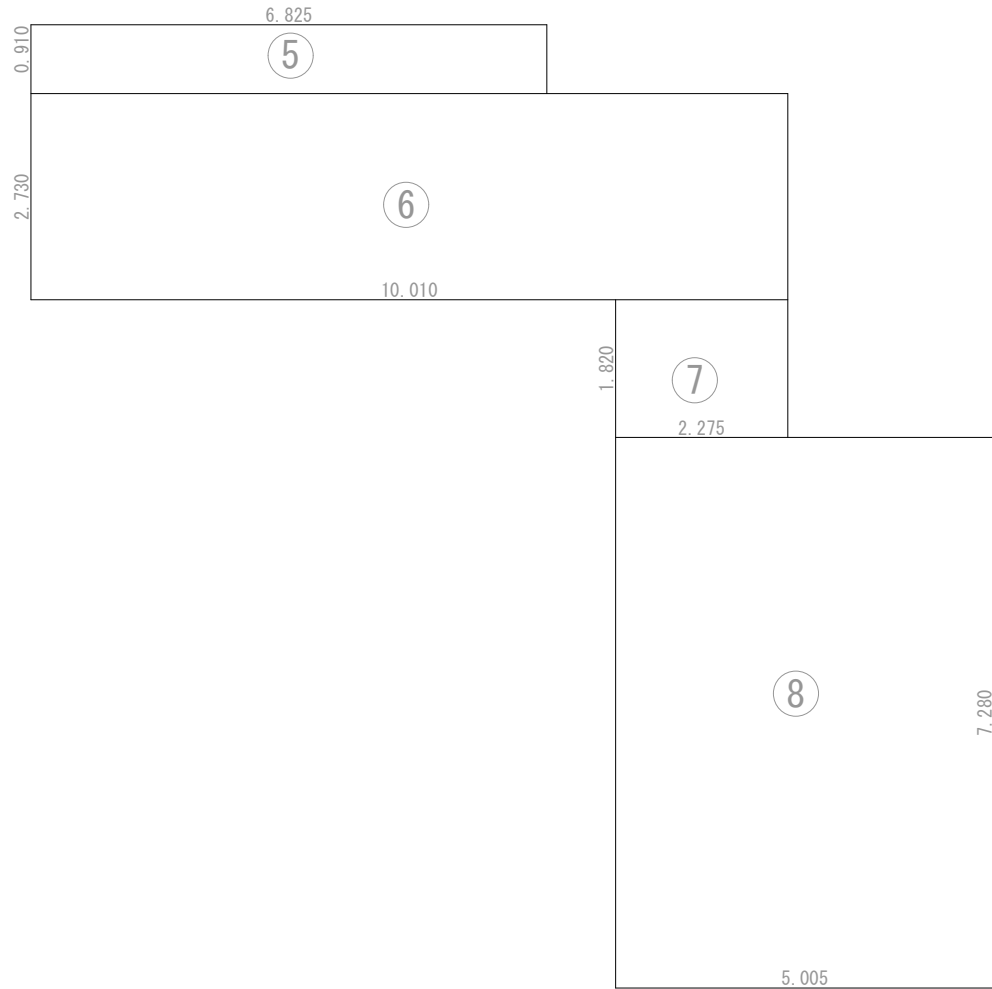

2階床面積図 S=1/100

2階床面積求積表


番号	計算式 (m)	面積 (㎡)
⑤	6.825 × 0.910	6.21075
⑥	10.010 × 2.730	27.3273
⑦	2.275 × 1.820	4.1405
⑧	5.005 × 7.280	36.4364
合計	≒	74.11495 74.11

延べ床面積表

1階床面積 + 2階床面積 71.63 74.11 合計	145.74
------------------------------------	--------

(44.0坪)

決定図

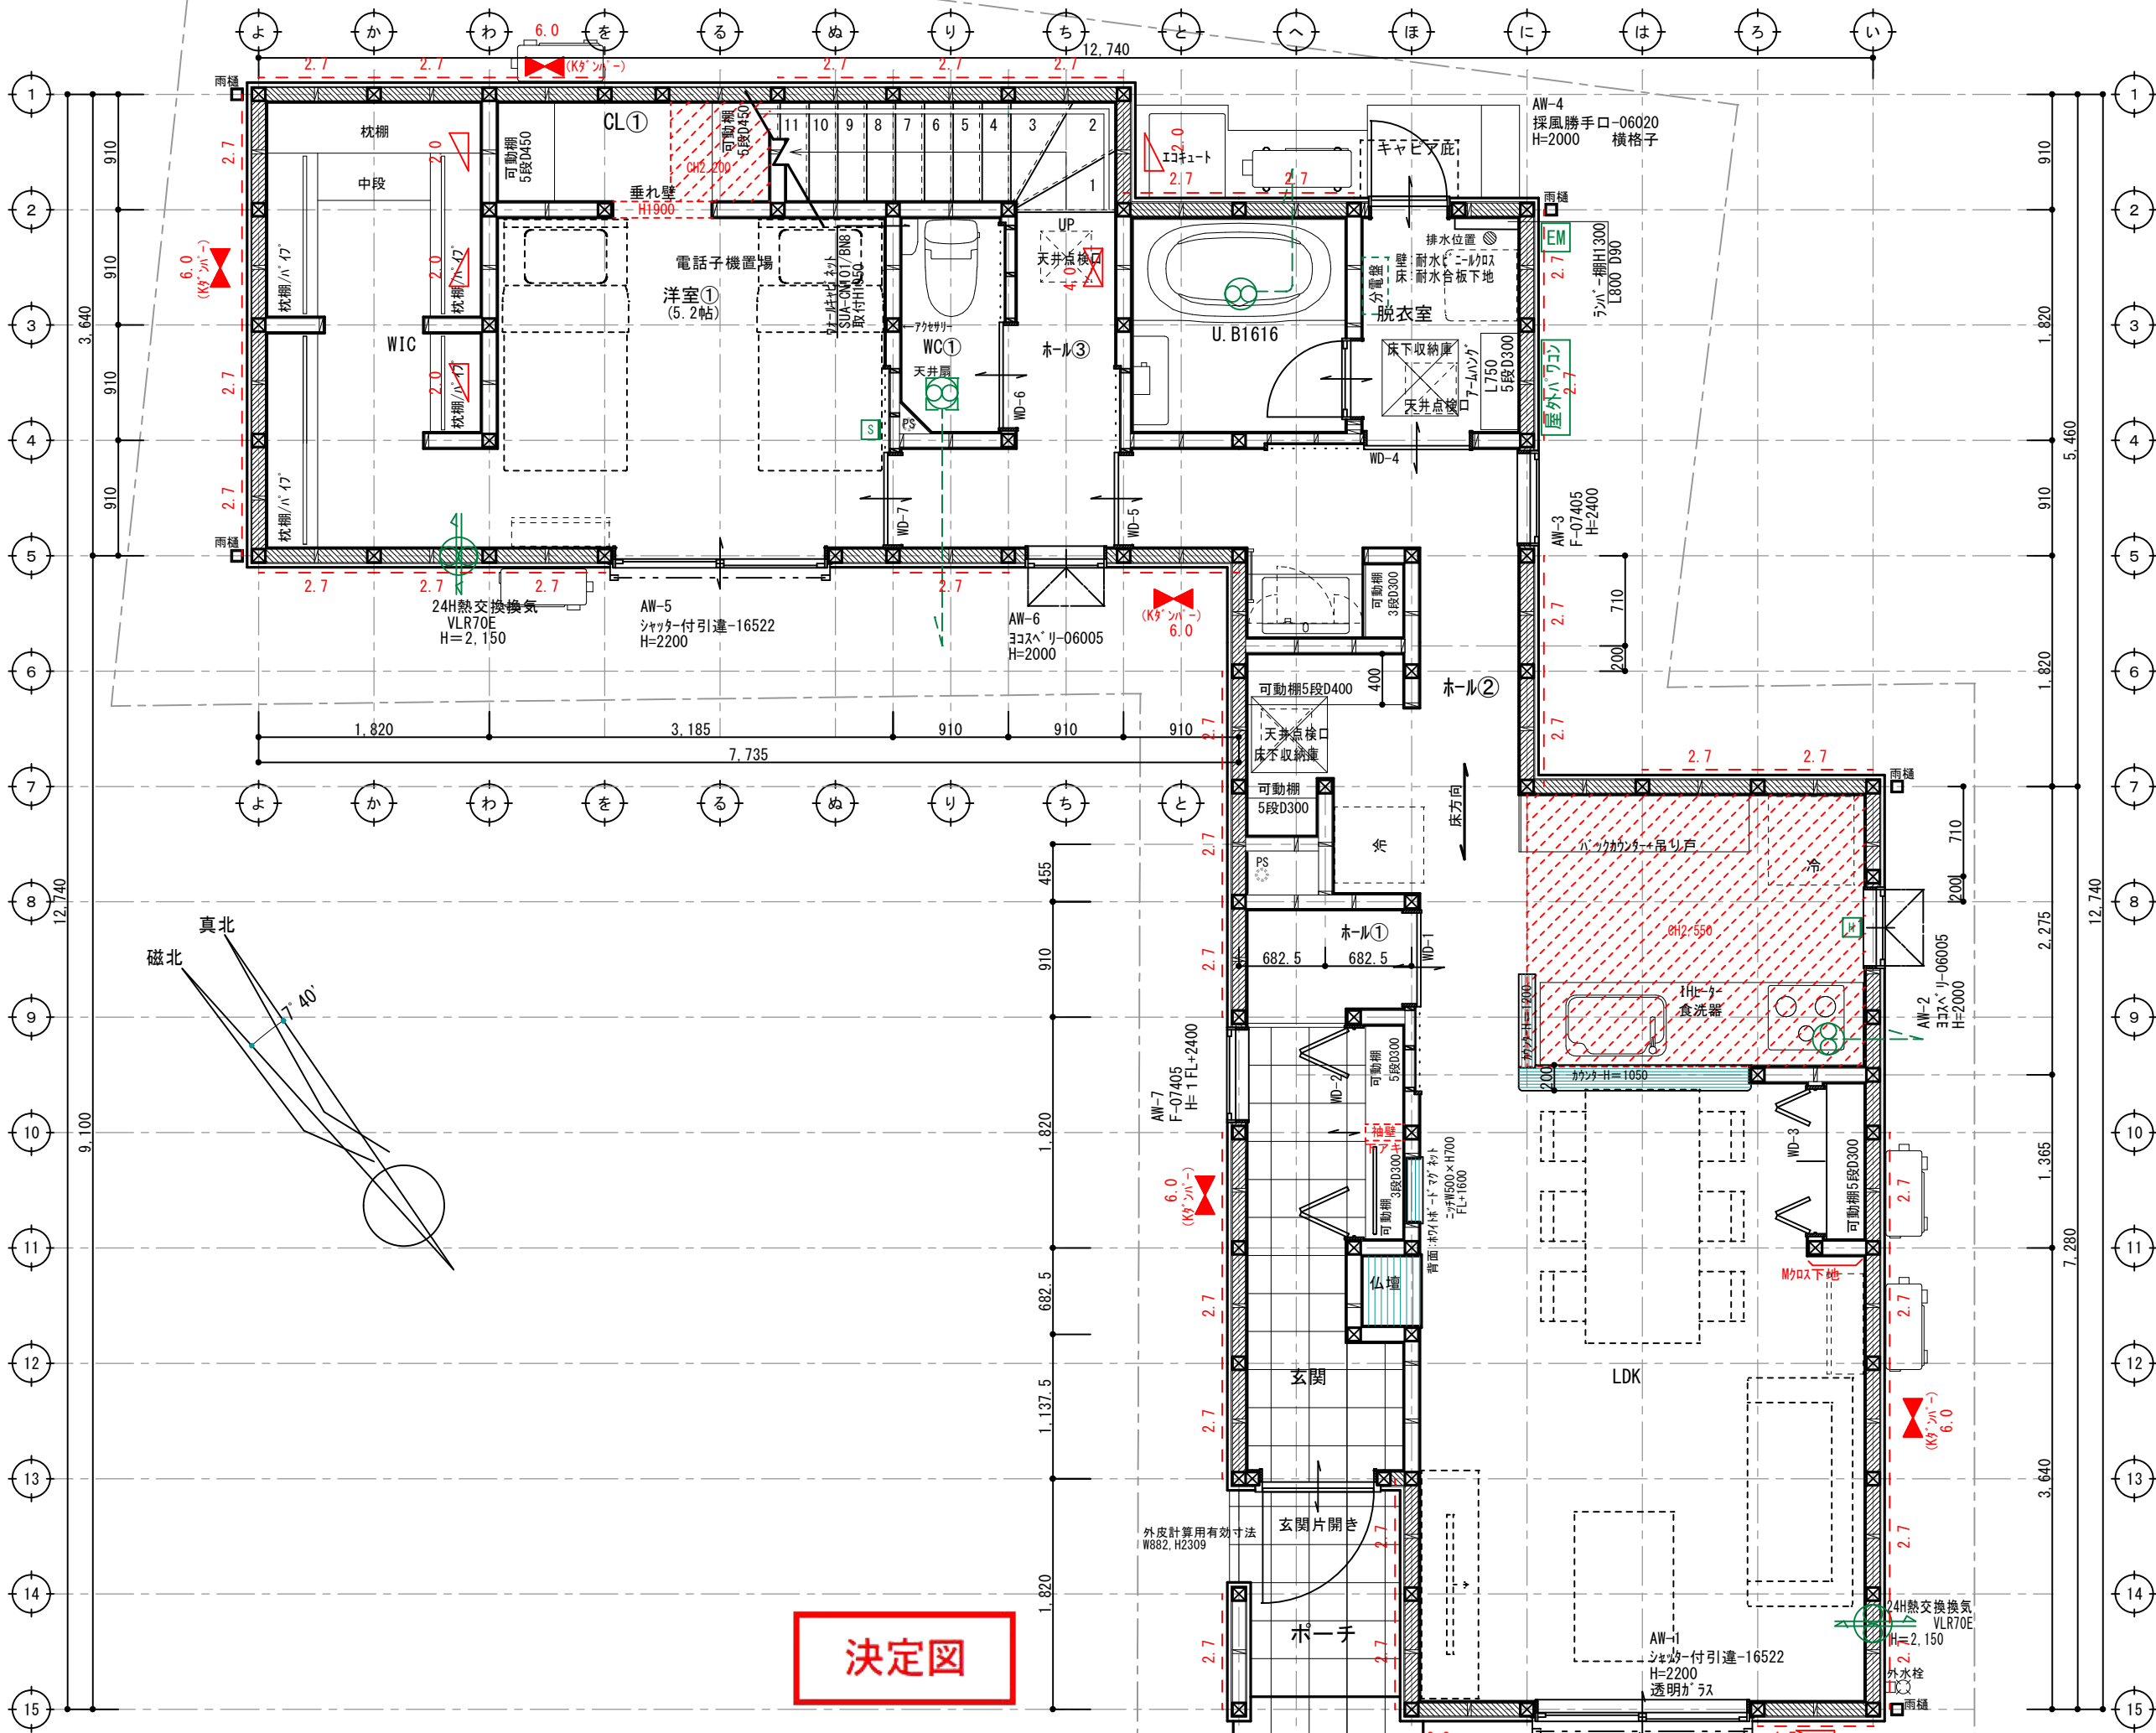

準防火地域

壁付け 住宅用火災報知器	数量
熱感知	1
熱感知	電池式(単独型)
露出型	

壁付け 住宅用火災報知器	数量
煙感知	1
煙感知	電池式(単独型)
露出型	

- ※ 煙感知器は壁・梁より600mm以上離す壁に取付け可能な場合、天井から150mm以上500mm以内離す換気扇・エアコン吹出口から1500mm以上離す
- ※ 全室LED照明とする。
- ※ 標準天井高さ2,400
- ※ 表記なきガラスは型ガラス

* 凡例


- 管柱 (105×105)
- K⁹シャ- (3.30倍 FRM-0641)
- 片筋違い (2.00倍 45×90) (例 左:柱脚 右:柱頭)
- たすき掛筋違い (4.00倍 45×90)
- 構造用合板 (2.70倍) (t=9 タイガ-EXH⁹ハ-)
- 床点検口
- 天井点検口
- 換気扇
- 熱交換換気扇VLR-70

内装仕上: ホルムアルデヒド発散等級F☆☆☆☆等級相当
天井裏等: ホルムアルデヒド発散等級F☆☆☆☆等級相当

アドバンスシリーズ スマートデザイン (外部)	
凡例	
1	コンセント 1ヶ所
2	コンセント 2ヶ所
3	コンセント 3ヶ所
1ET	コンセント1ヶ所接地ターミナル付
2ET	コンセント2ヶ所接地ターミナル付
WP	コンセント 防水型
	エアコン用コンセント
	200V用コンセント
WP	防雨入線プレート
	スイッチ
3	3路スイッチ
4	4路スイッチ
	直結電源
TV	テレビ取出口
TEL	電話取出口 (テレビホンガイド)
LAN	LAN取出口 (テレビホンガイド)
	壁照明
	リモコン (給湯関係・ルフロ)
	メーター
	分電盤
	チャイム

- ※ACコンセント天井付け
- ※TVアンテナ工事
- ※スイッチはFL+1100、コンセントはFL+200

決定図

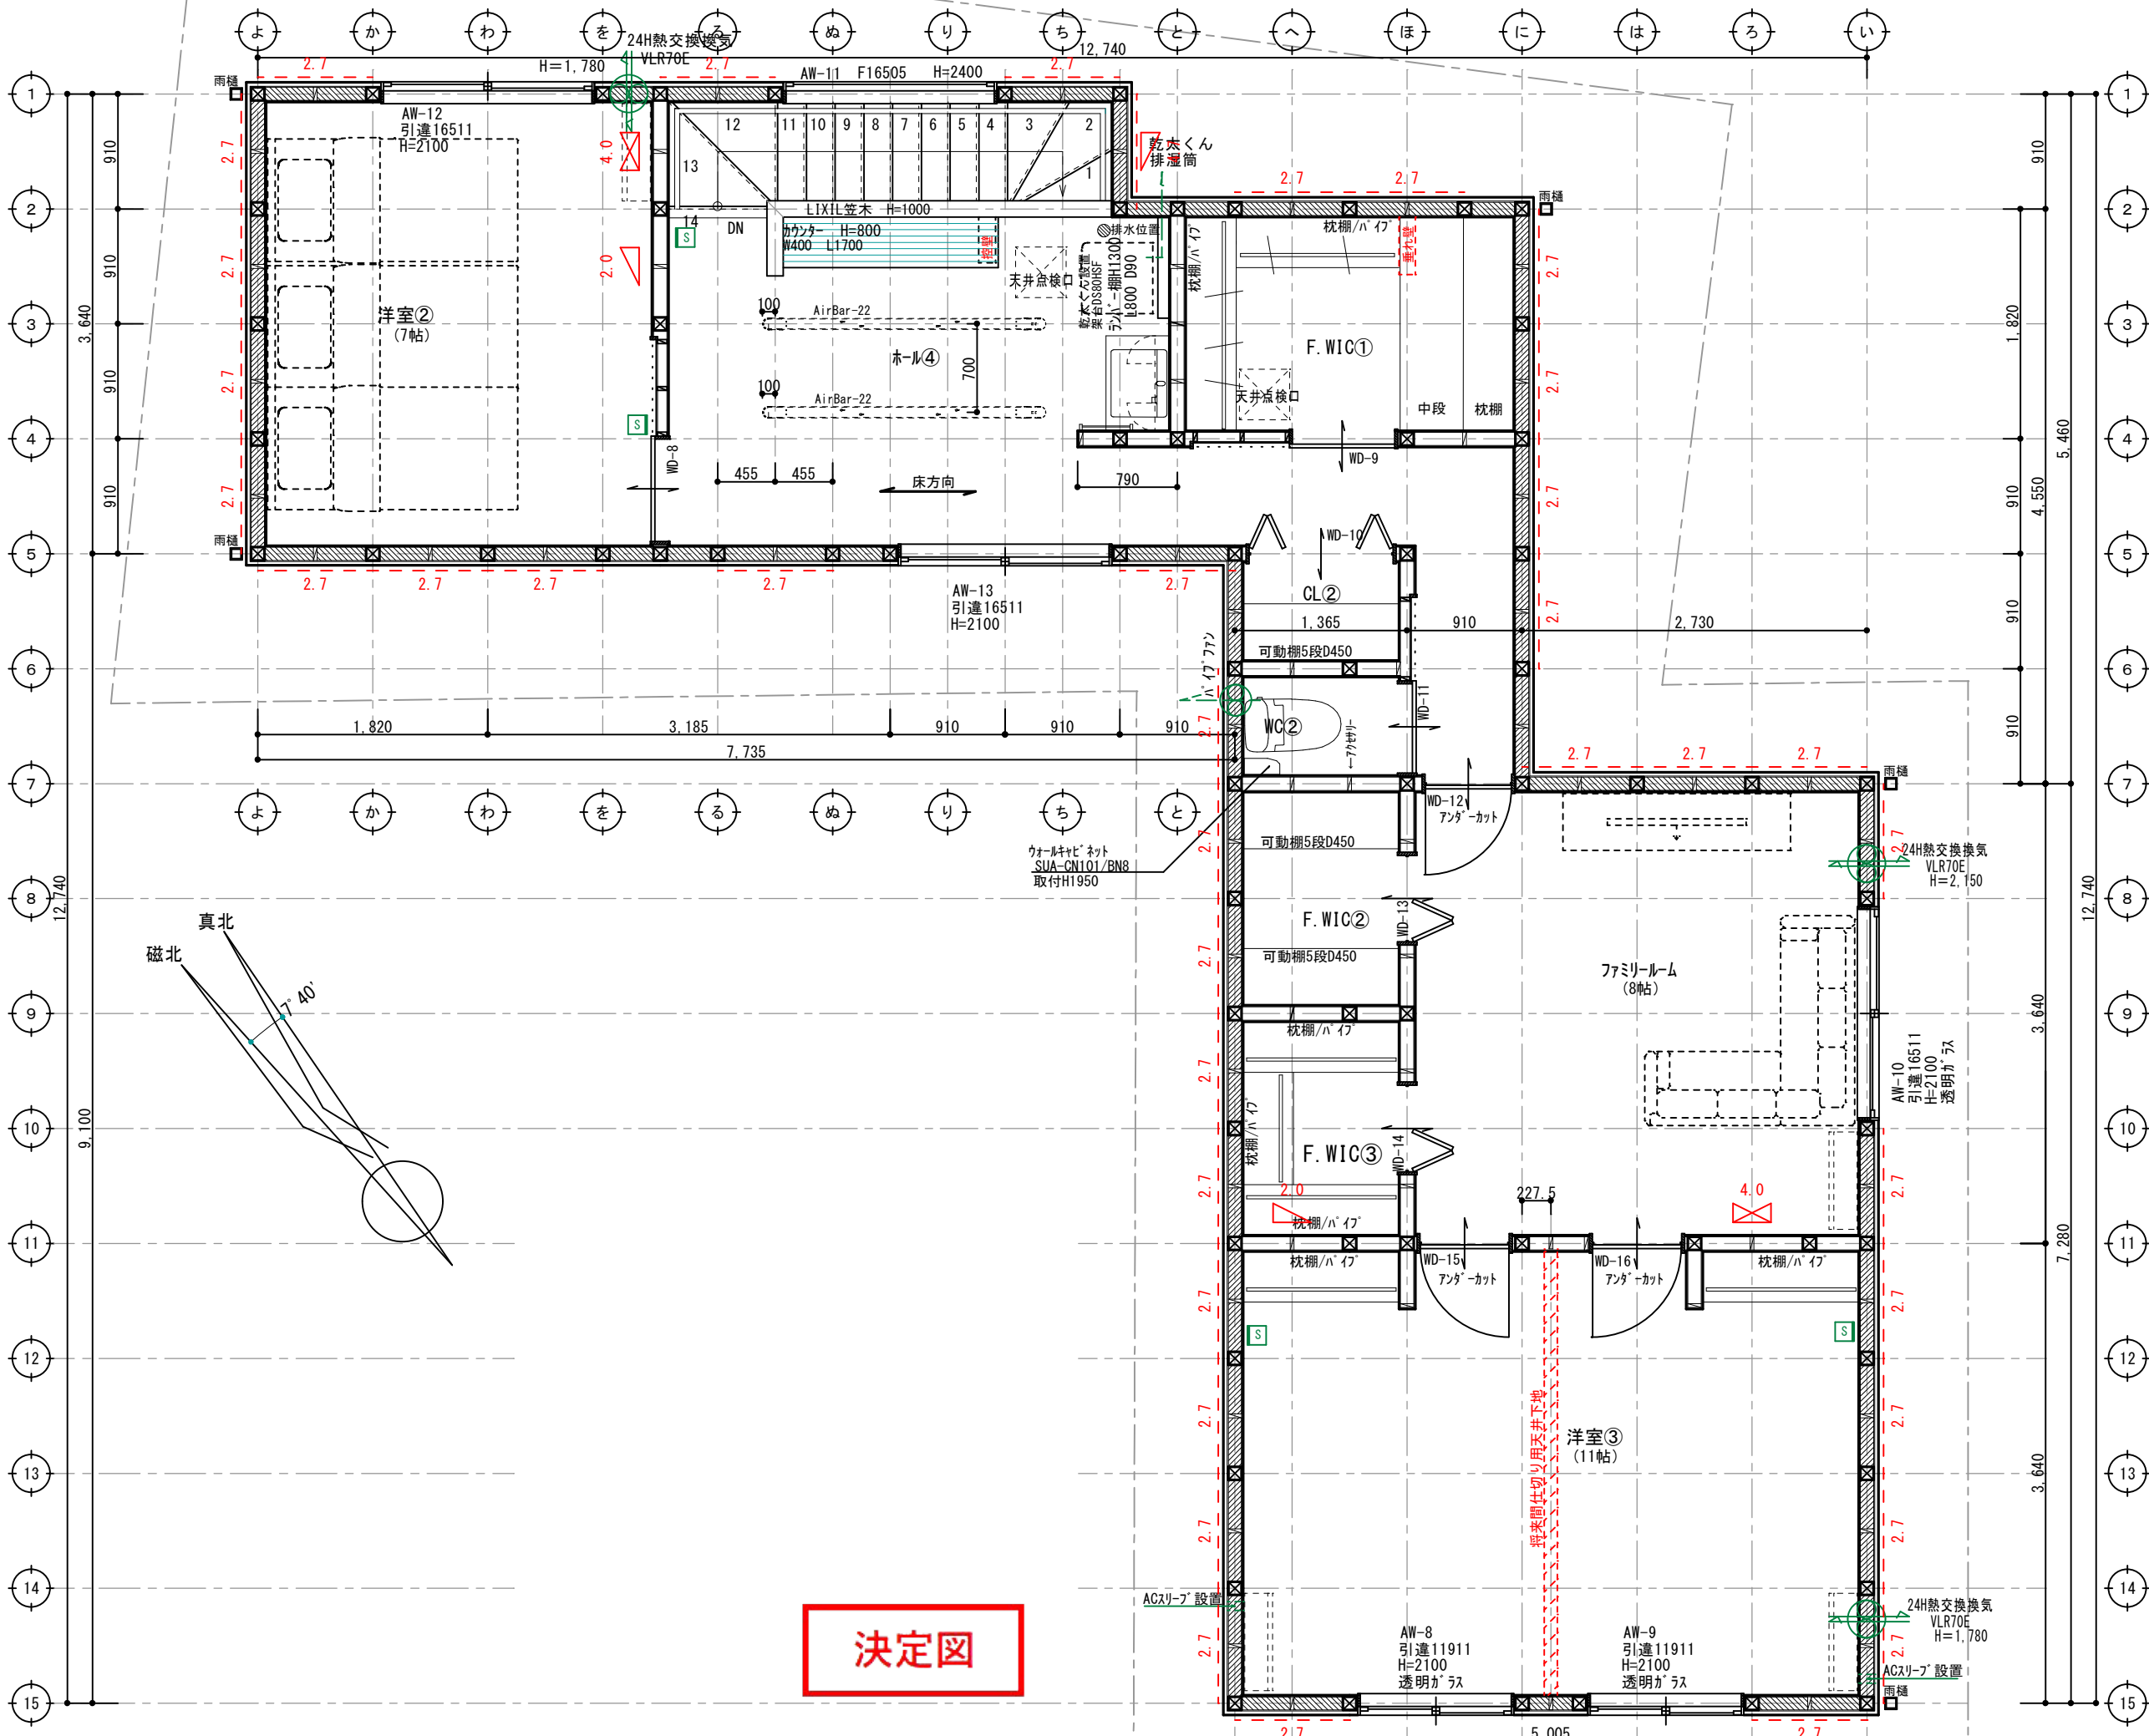

準防火地域

壁付け		数量
H	熱感知器	電池式(単独型)
	熱感知器	露出型
壁付け 住宅用火災報知器		数量
S	煙感知器	電池式(単独型)
	煙感知器	露出型

- ※ 煙感知器は壁・梁より600mm以上離す壁に取付ける場合、天井から150mm以上500mm以内離す換気扇・エアコン吹出口から1500mm以上離す
- ※ 全室LED照明とする。
- ※ 標準天井高さ2,400
- ※ 表記なきガラスは型ガラス


* 凡例

- 管柱 (105×105)
- Kタ'ンバー (3.30倍 FRM-0641)
- 片筋違 (2.00倍 45×90) (例 左:柱脚 右:柱頭)
- たすき掛筋違 (4.00倍 45×90)
- 構造用合板 (2.70倍) (t=9 タイガ-EXハイパー)
- 床点検口
- 天井点検口
- 換気扇
- 熱交換換気扇VLR-70

内装仕上: ホルムアルデヒド発散等級F☆☆☆☆等級相当
天井裏等: ホルムアルデヒド発散等級F☆☆☆☆等級相当

アドバンスシリーズ		スマートデザイン (外部)
凡例	1	コンセント 1ヶ所
	2	コンセント 2ヶ所
	3	コンセント 3ヶ所
	1ET	コンセント1ヶ所接地ターミナル付
	2ET	コンセント2ヶ所接地ターミナル付
WP		コンセント 防水型
		エアコン用コンセント
		200V用コンセント
WP		防雨入線プレート
		スイッチ
	3	3路スイッチ
	4	4路スイッチ
		直結電源
TV		テレビ取出口
TEL		電話取出口 (テレホンガイド)
LAN		LAN取出口 (テレホンガイド)
		壁照明
		リモコン (給湯関係・ルフロ)
		メーター
		分電盤
		チャイム

- ※ACコンセント天井付け
- ※TVアンテナ工事
- ※スイッチはFL+1100、コンセントはFL+200

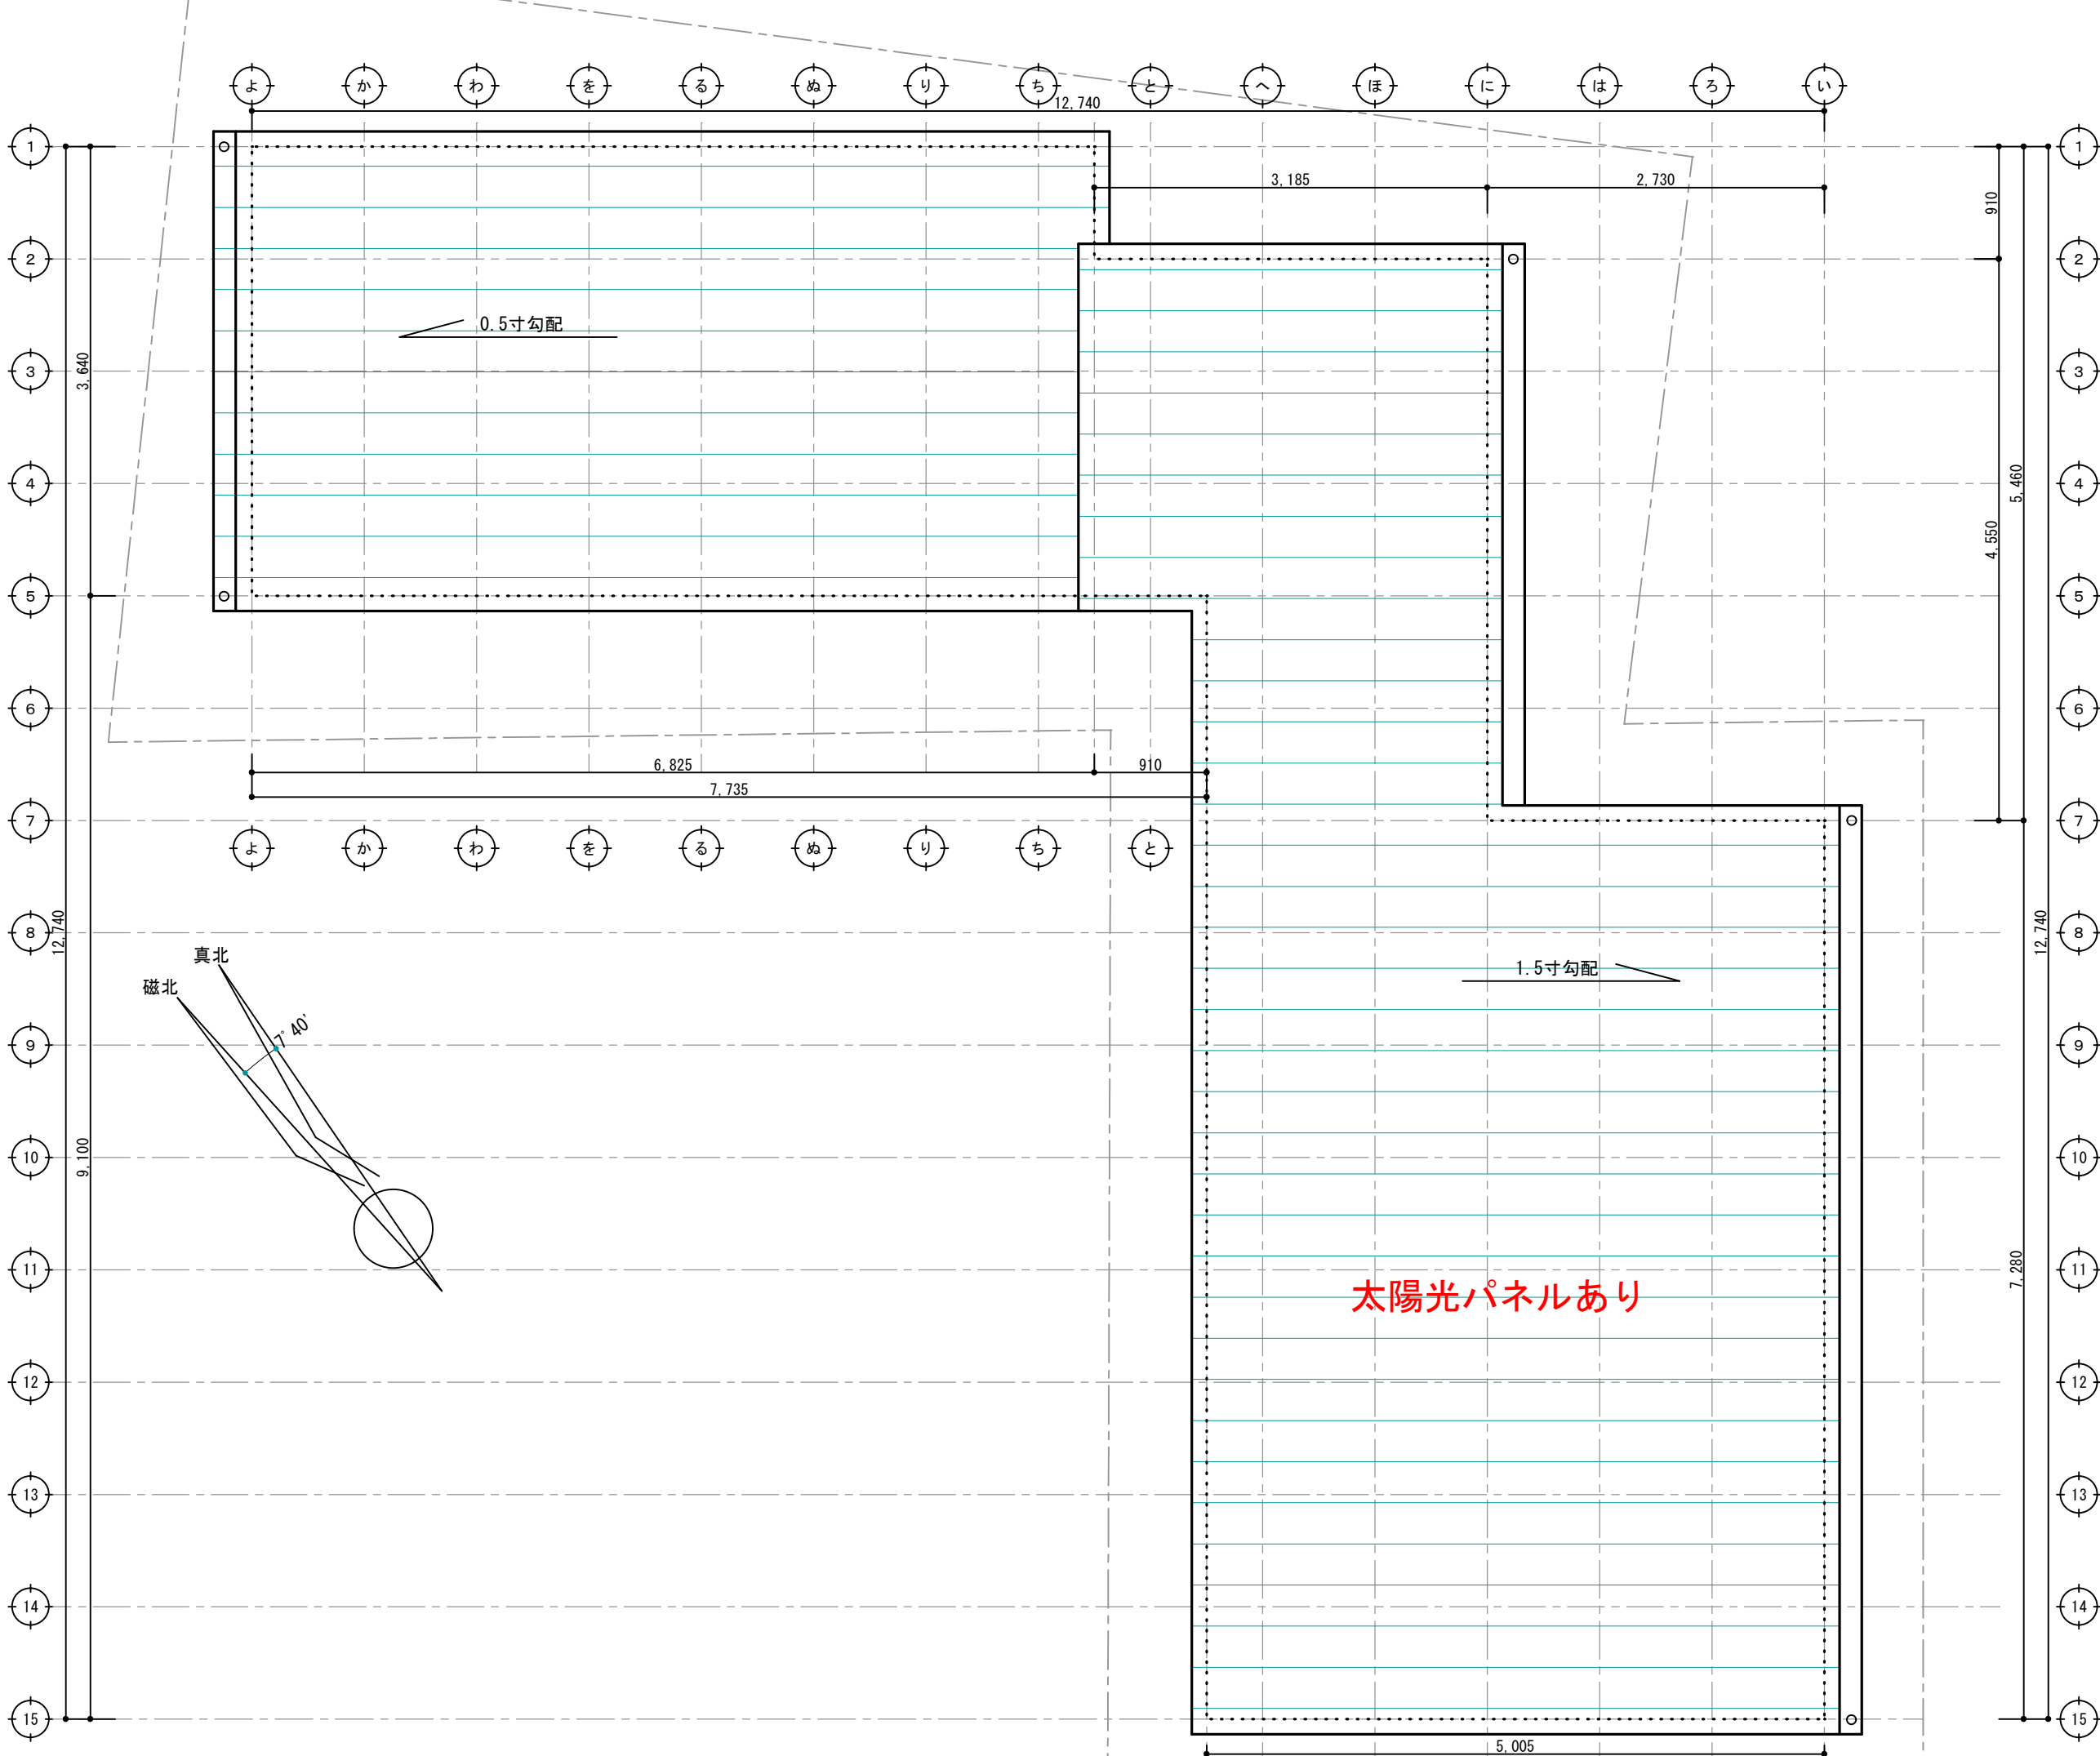

準防火地域

太陽光パネルあり

決定図


訂 正	浜 岡 一 級 総 合 設 計 事 務 所	 PG HOUSE	株式会社 LIFEFUND InDesign office	一級建築士事務所	年 月 日	件 名	外山裕也様 新築工事			設計	IC	工事	図 番
	一級建築士事務所 静岡県知事登録第 (10)2441 号				2025. 4. 20								
	一級建築士 大臣登録第 365879 号 西原利昌				縮 尺 1/50								
			事務所登録 (2) 第7595号	一級建築士登録 第179770号 鈴木 達男						倉田		青島	3-1
			〒432-8023 静岡県浜松市中央区鴨江3丁目70番23号										

準防火地域



南側立面図 S=1/100

東側立面図 S=1/100

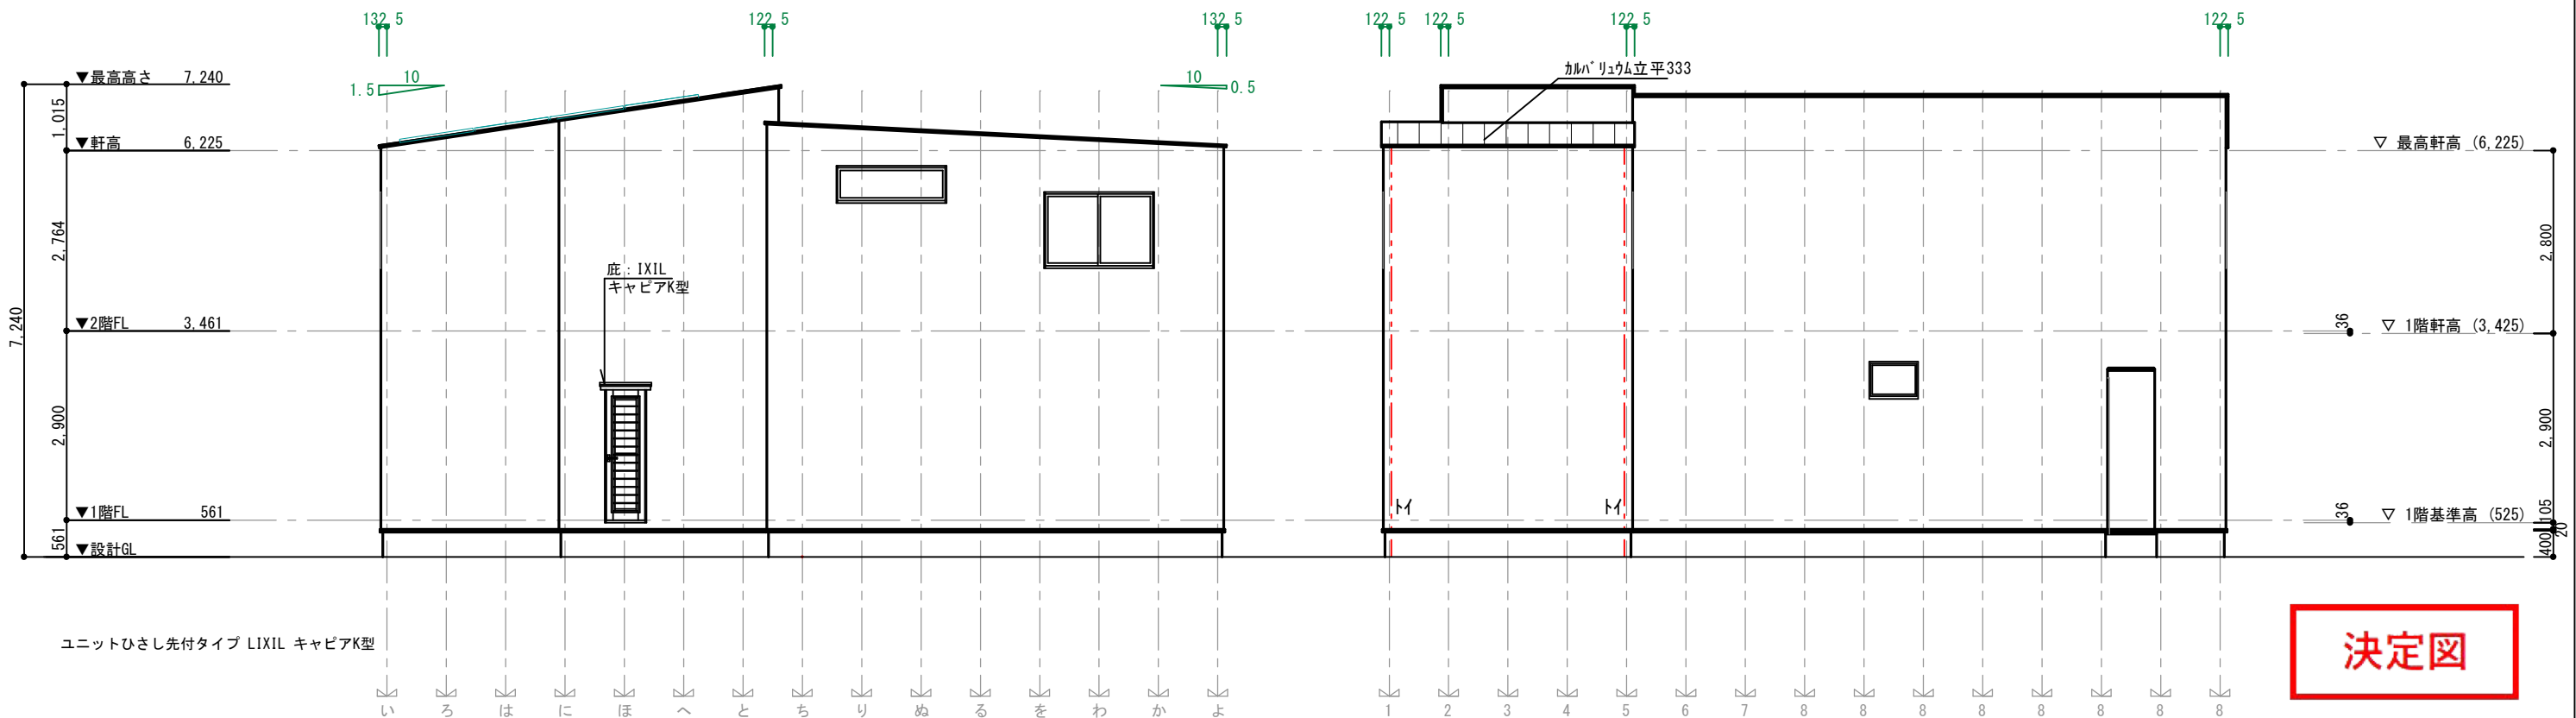

北側立面図 S=1/100

西側立面図 S=1/100

決定図


外壁開口部は全て防火戸（全て延焼線内）

訂正	浜岡一級総合設計事務所 一級建築士事務所 静岡県知事登録第(10)2441号 一級建築士 大臣登録第 365879号 西原利昌	PG HOUSE	株式会社 LIFEFUND InDesign office 一級建築士事務所 事務所登録(2)第7595号 一級建築士登録 第179770号 鈴木 達男 〒432-8023 静岡県浜松市中央区鴨江3丁目70番23号	年月日 2025.4.20 縮尺 1/100	件名 外山裕也様 新築工事 図名 立面図		設計 倉田	IC	工事 青島	図番 4
----	---	----------	---	---------------------------------	-------------------------------	--	----------	----	----------	---------


G 1




訂 正	浜 岡 一 級 総 合 設 計 事 務 所 一級建築士事務所 静岡県知事登録第 (10)2441 号 一級建築士 大臣登録第 365879 号 西原利昌		株式会社 LIFEFUND InDesign office 一級建築士事務所 事務所登録 (2) 第7595号 一級建築士登録 第179770号 鈴木 達男 〒432-8023 静岡県浜松市中央区鴨江3丁目70番23号	年 月 日 2025. 4. 20	件 名 外山裕也様 邸新築工事	設計 倉田	IC 青島	工事 A-5	図 番 A-5
				縮 尺 1/30	図 名 矩計図				

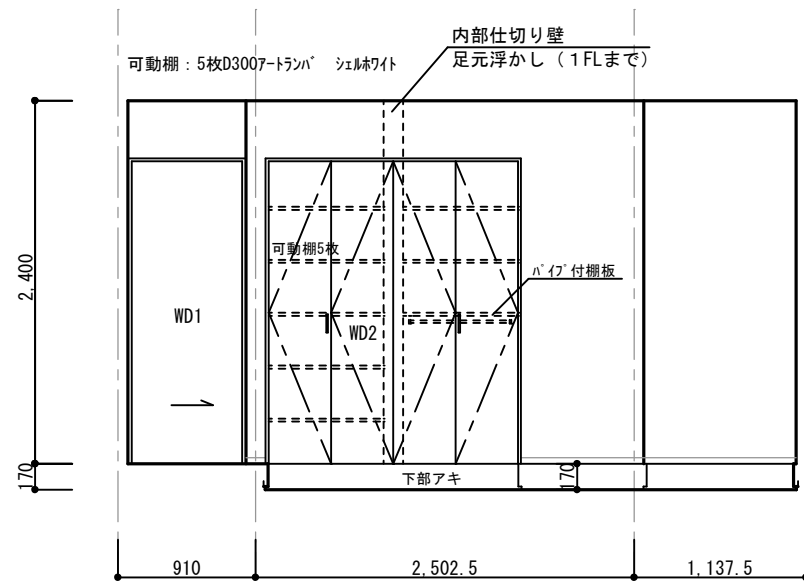


玄関 東面

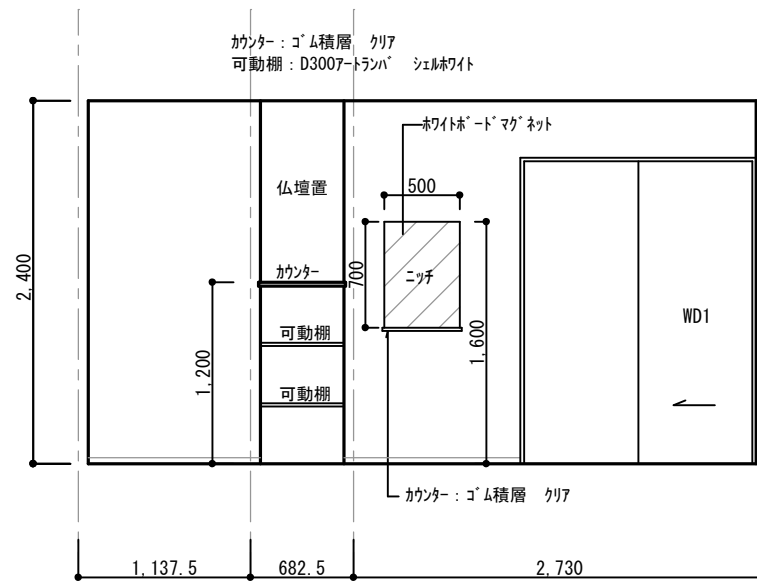

LDK 西面

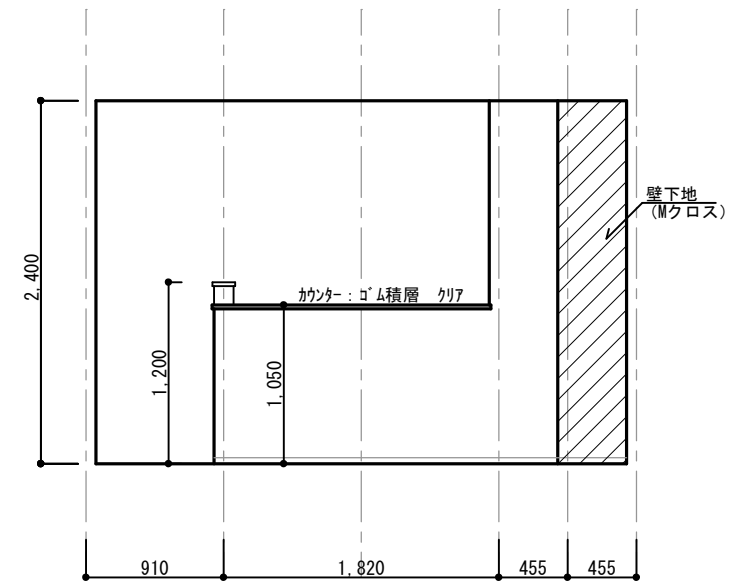


LDK 北面

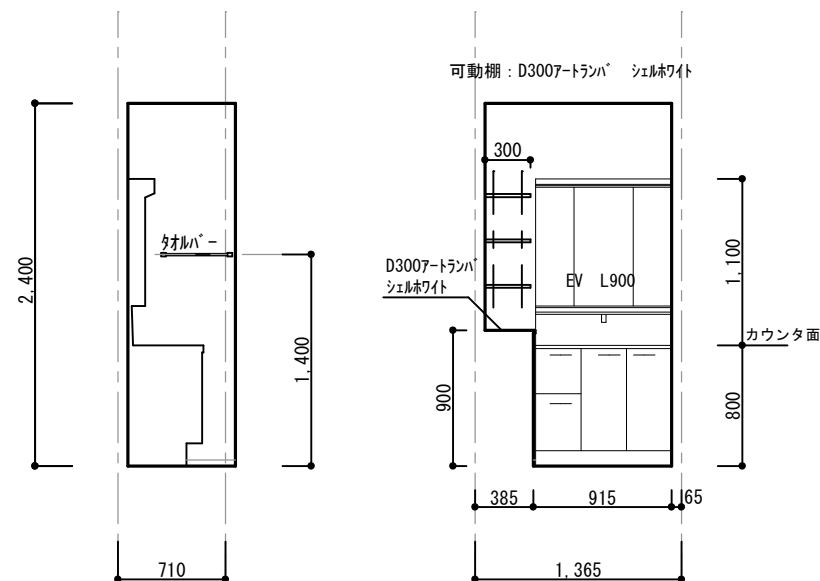


1階洗面 西面


1階洗面 南面

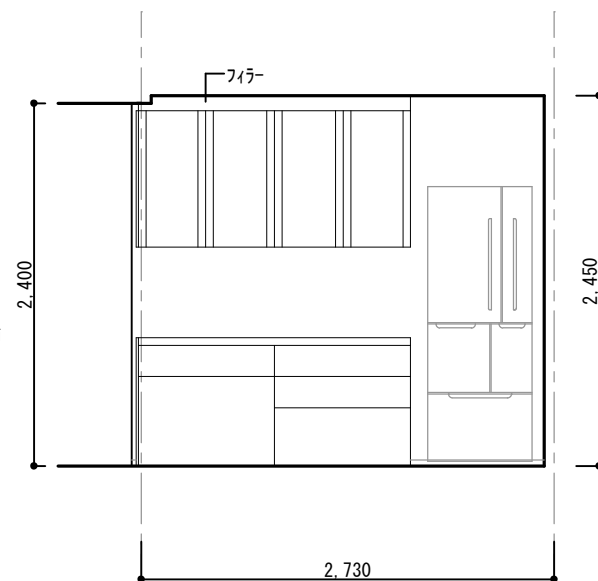


キッチン 北面

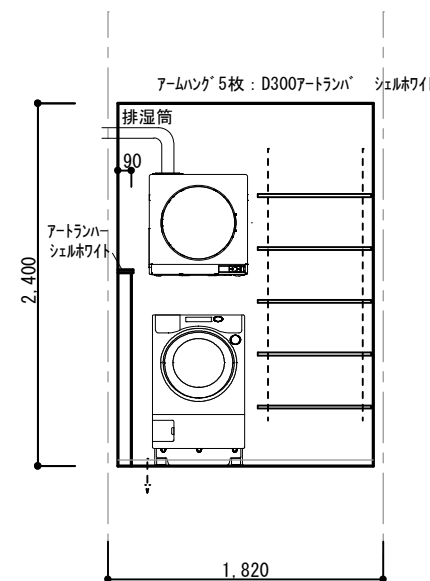

脱衣室 東面

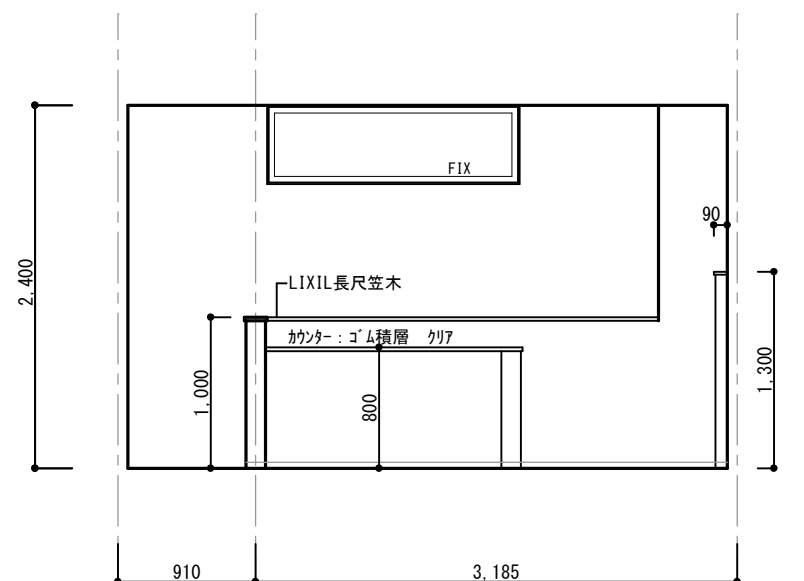


ホール④ 北面

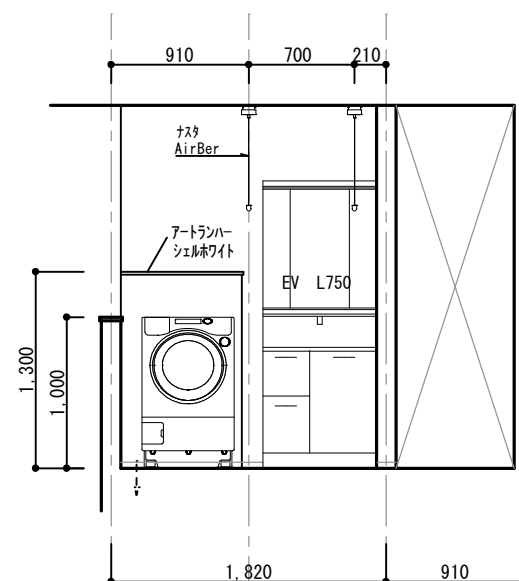

ホール④ 東面


決定図

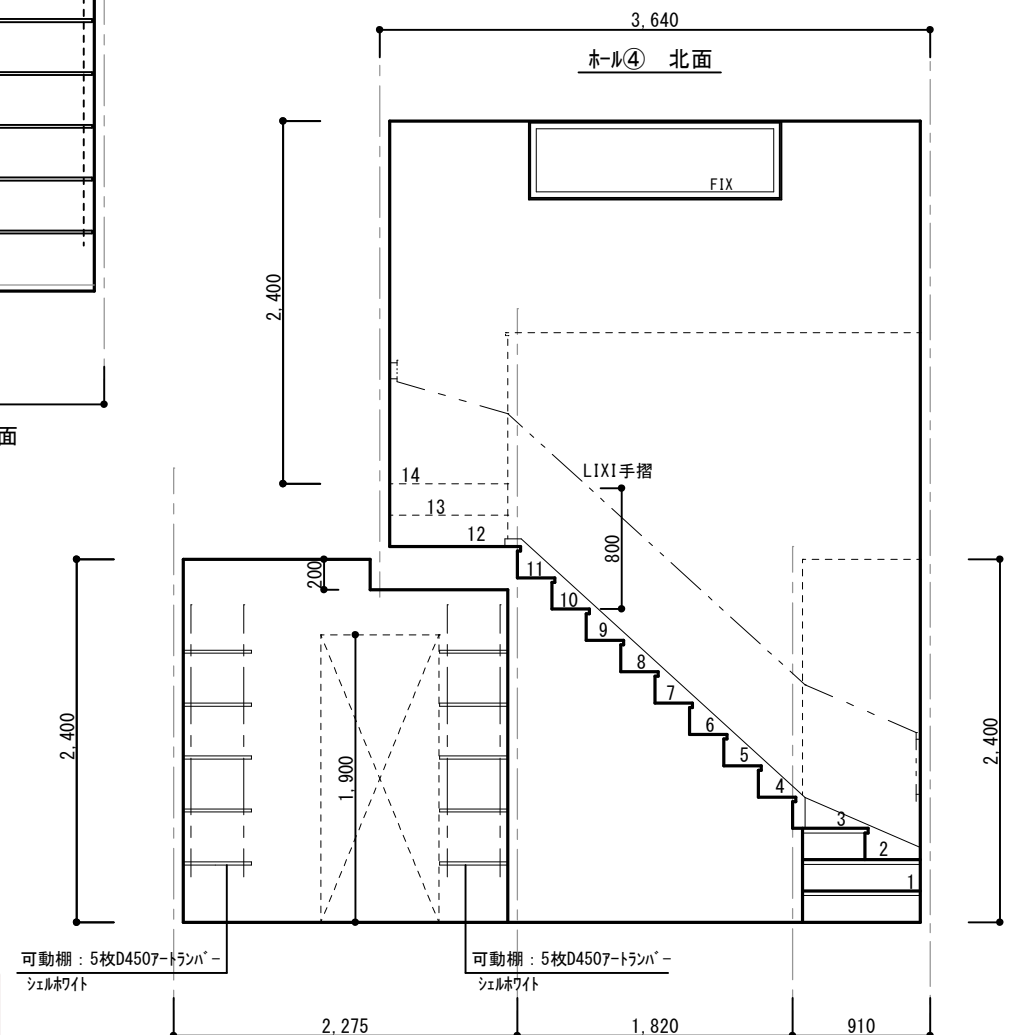

CL① 北面

ホール③ 北面

訂正	浜岡一級総合設計事務所 一級建築士事務所 静岡県知事登録第 (10)2441 号 一級建築士 大臣登録第 365879 号 西原利昌	LIFEFUND PG HOUSE	株式会社 LIFEFUND InDesign office 一級建築士事務所 事務所登録 (2) 第7595号 一級建築士登録 第179770号 鈴木 達男 〒432-8023 静岡県浜松市中央区鶴江3丁目70番23号	年月日 2025.4.20	件名 外山裕也様 邸新築工事	設計 倉田	IC IC	工事 青島	図番 6-1
縮尺 1/50	図名 展開図								

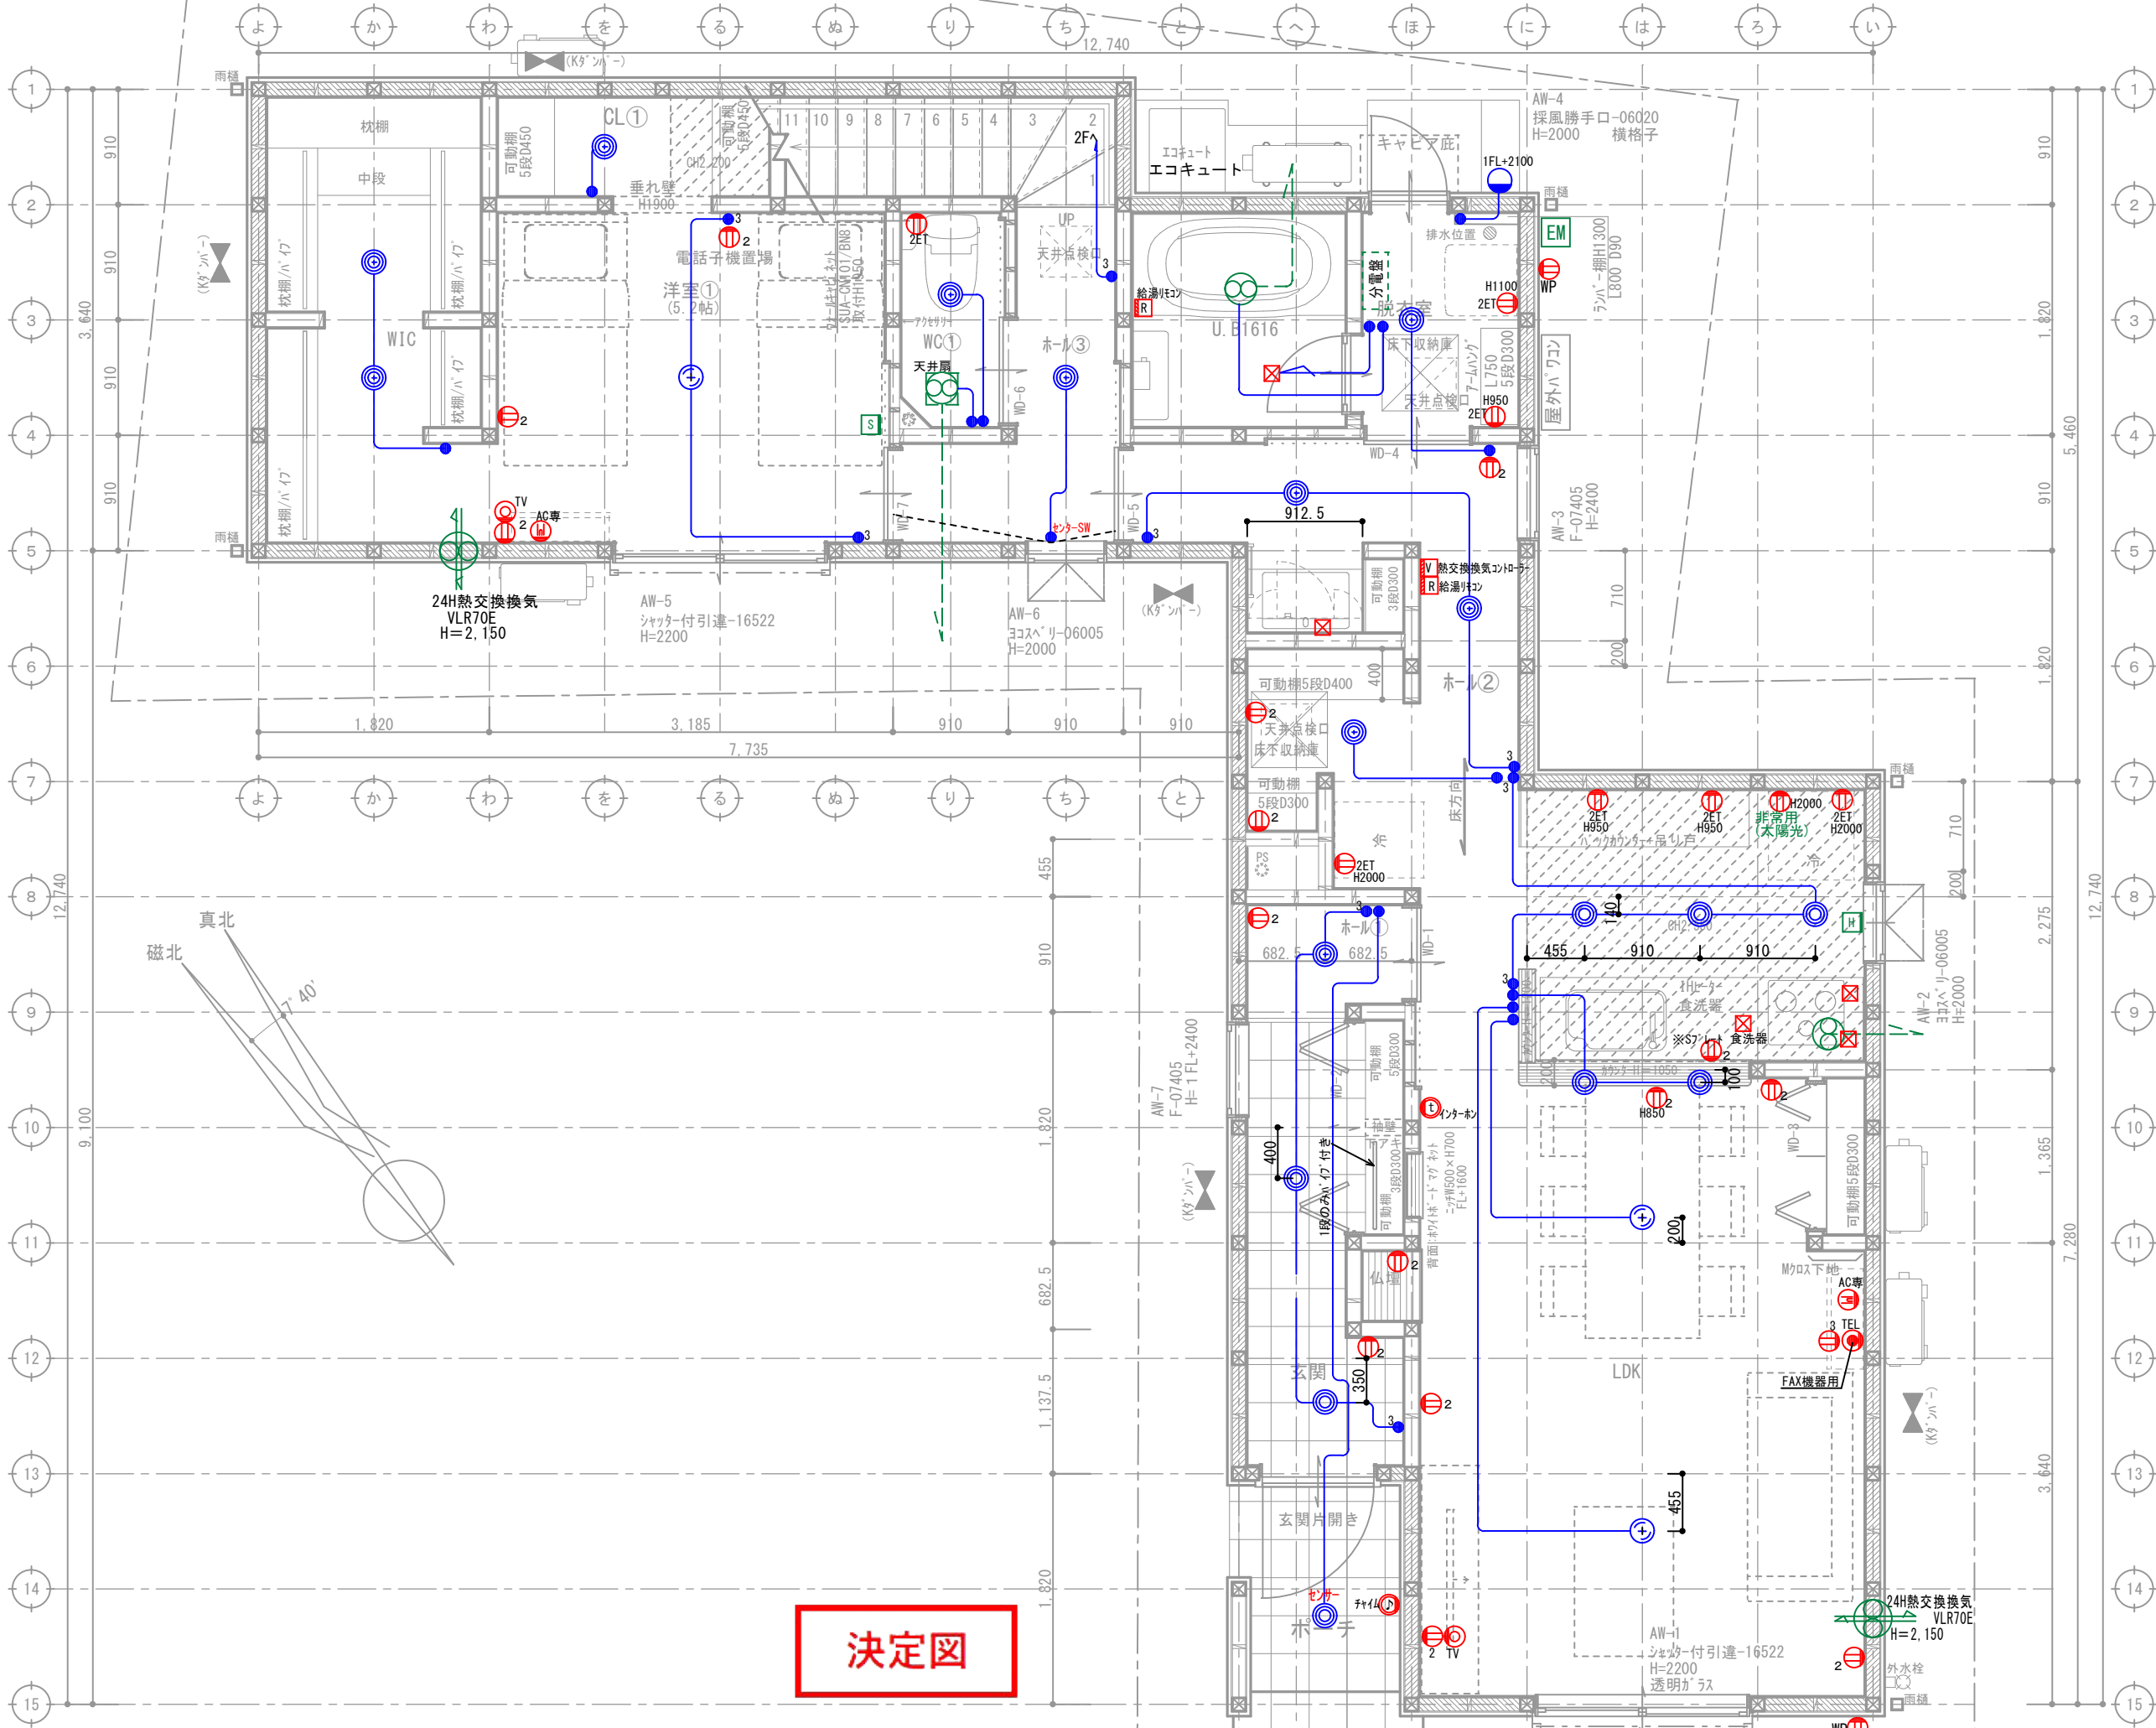

準防火地域

壁付け 住宅用火災報知器	数量
熱感知	電池式(単独型)
煙感知	電池式(単独型)
露出型	

※ 煙感知器は壁・梁より600mm以上離す
壁に取付ける場合、
天井から150mm以上500mm以内離す
換気扇・エアコン吹出口から1500mm以上離す
※ 全室LED照明とする。
※ 標準天井高さ2,400
※ 表記なきガラスは型ガラス

* 凡例


- 管柱 (105×105)
- K⁹シャ- (3.30倍 FRM-0641)
- 片筋違い (2.00倍 45×90)
(例 左:柱脚 右:柱頭)
- たすき掛筋違い (4.00倍 45×90)
- 構造用合板 (2.70倍)
(t=9 タイガ-EXTMハ-)
- 床点検口
- 天井点検口
- 換気扇
- 熱交換換気扇VLR-70

内装仕上: ホルムアルデヒド発散等級F☆☆☆☆等級相当
天井裏等: ホルムアルデヒド発散等級F☆☆☆☆等級相当

アドバンスシリーズ スマートデザイン (外部)	
凡例	
1	コンセント 1ヶ所
2	コンセント 2ヶ所
3	コンセント 3ヶ所
1ET	コンセント1ヶ所接地ターミナル付
2ET	コンセント2ヶ所接地ターミナル付
WP	コンセント 防水型
	エアコン用コンセント
	200V用コンセント
WP	防雨入線プレート
	スイッチ
3	3路スイッチ
4	4路スイッチ
	直結電源
TV	テレビ取出口
TEL	電話取出口 (テレホンガイド)
LAN	LAN取出口 (テレホンガイド)
	壁照明
	リモコン (給湯関係・ルフロ)
	メーター
	分電盤
	チャイム

※ACコンセント天井付け
※TVアンテナ工事
※スイッチはFL+1100、コンセントはFL+200

決定図

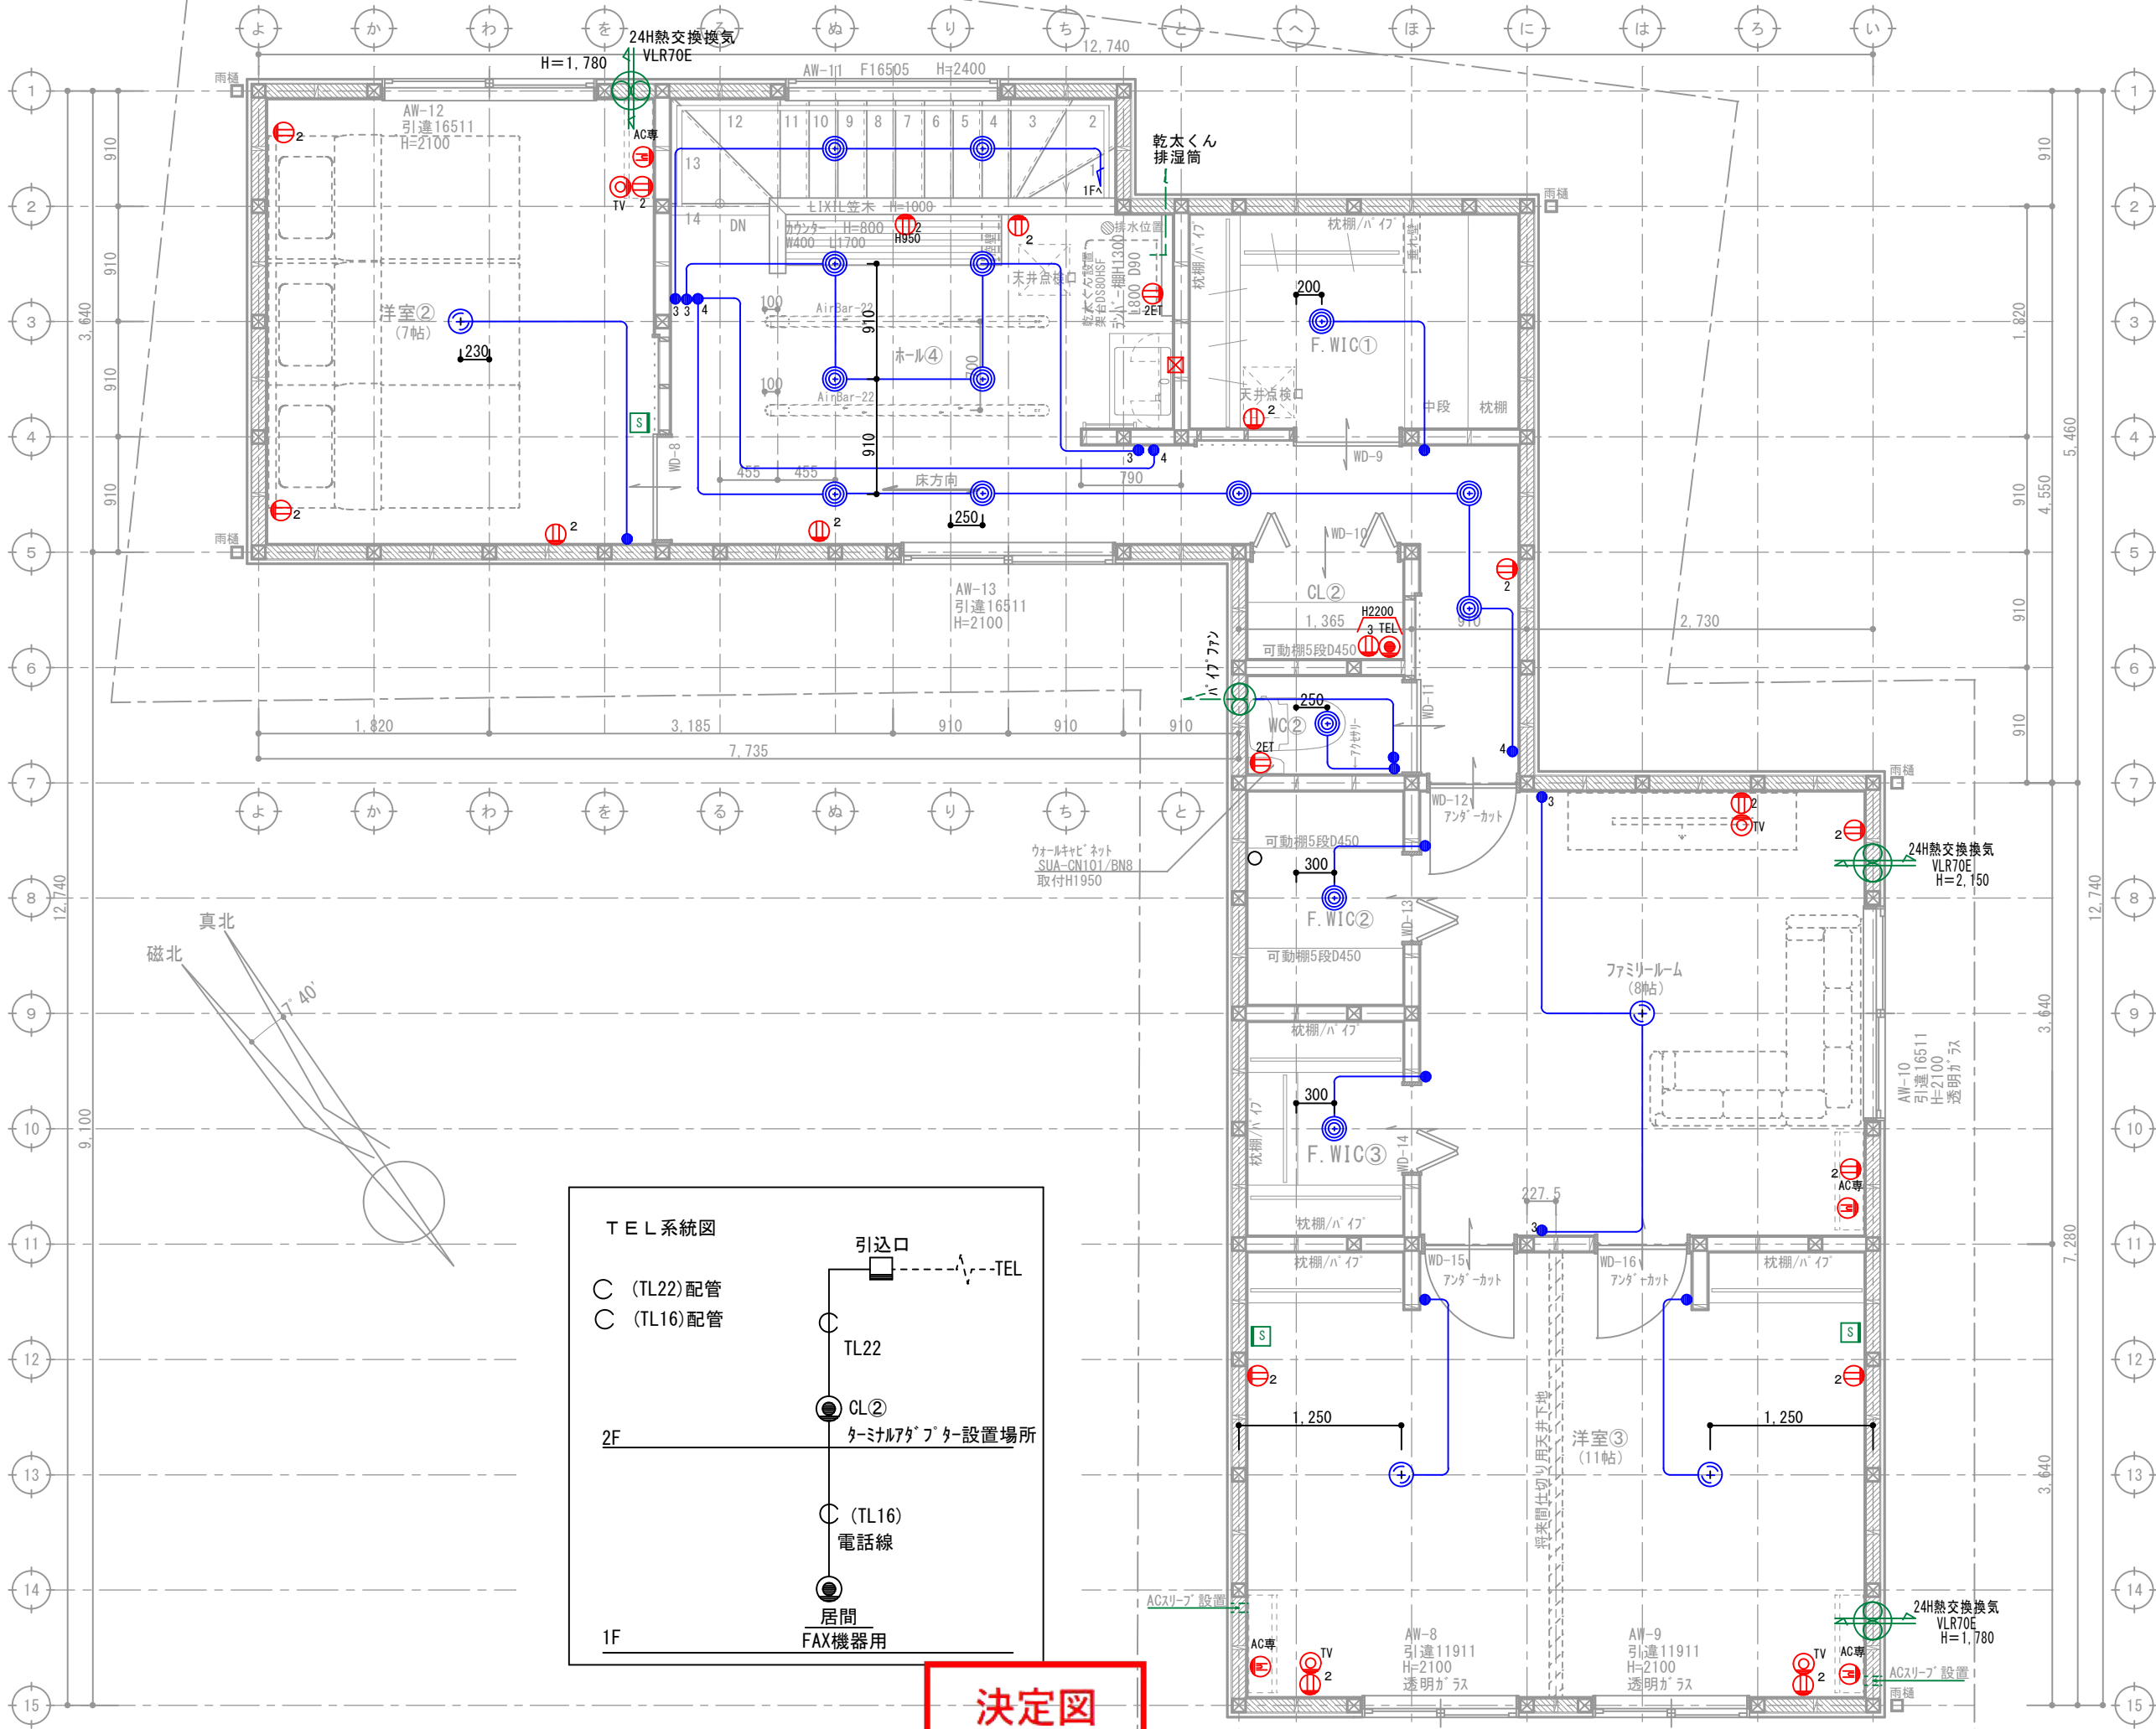

準防火地域

壁付け		数量
H	熱感知器	電池式(単独型)
	熱感知	露出型
壁付け 住宅用火災報知器		数量
S	煙感知器	電池式(単独型)
	煙感知	露出型

- ※ 煙感知器は壁・梁より600mm以上離す壁に取付ける場合、天井から150mm以上500mm以内離す換気扇・エアコン吹出口から1500mm以上離す
- ※ 全室LED照明とする。
- ※ 標準天井高さ2,400
- ※ 表記なきガラスは型ガラス


* 凡例

- 管柱 (105×105)
- Kタノハ (3.30倍 FRM-0641)
- 片筋違い (2.00倍 45×90) (例 左:柱脚 右:柱頭)
- たすき筋違い (4.00倍 45×90)
- 構造用合板 (2.70倍) (t=9 タイガ-EXハイパー)
- 床点検口
- 天井点検口
- 換気扇
- 熱交換換気扇VLR-70

内装仕上: ホルムアルデヒド発散等級F☆☆☆☆等級相当
天井裏等: ホルムアルデヒド発散等級F☆☆☆☆等級相当

アドバンスシリーズ		スマートデザイン (外部)
凡例	1	コンセント 1ヶ所
	2	コンセント 2ヶ所
	3	コンセント 3ヶ所
	1ET	コンセント1ヶ所接地ターミナル付
	2ET	コンセント2ヶ所接地ターミナル付
	WP	コンセント 防水型
		エアコン用コンセント
		200V用コンセント
	WP	防雨入線プレート
		スイッチ
	3	3路スイッチ
	4	4路スイッチ
		直結電源
	TV	テレビ取出口
	TEL	電話取出口 (テレホンガイド)
	LAN	LAN取出口 (テレホンガイド)
		壁照明
		リモコン (給湯関係・ルフロ)
		メーター
		分電盤
		チャーム


- ※ACコンセント天井付け
- ※TVアンテナ工事
- ※スイッチはFL+1100、コンセントはFL+200

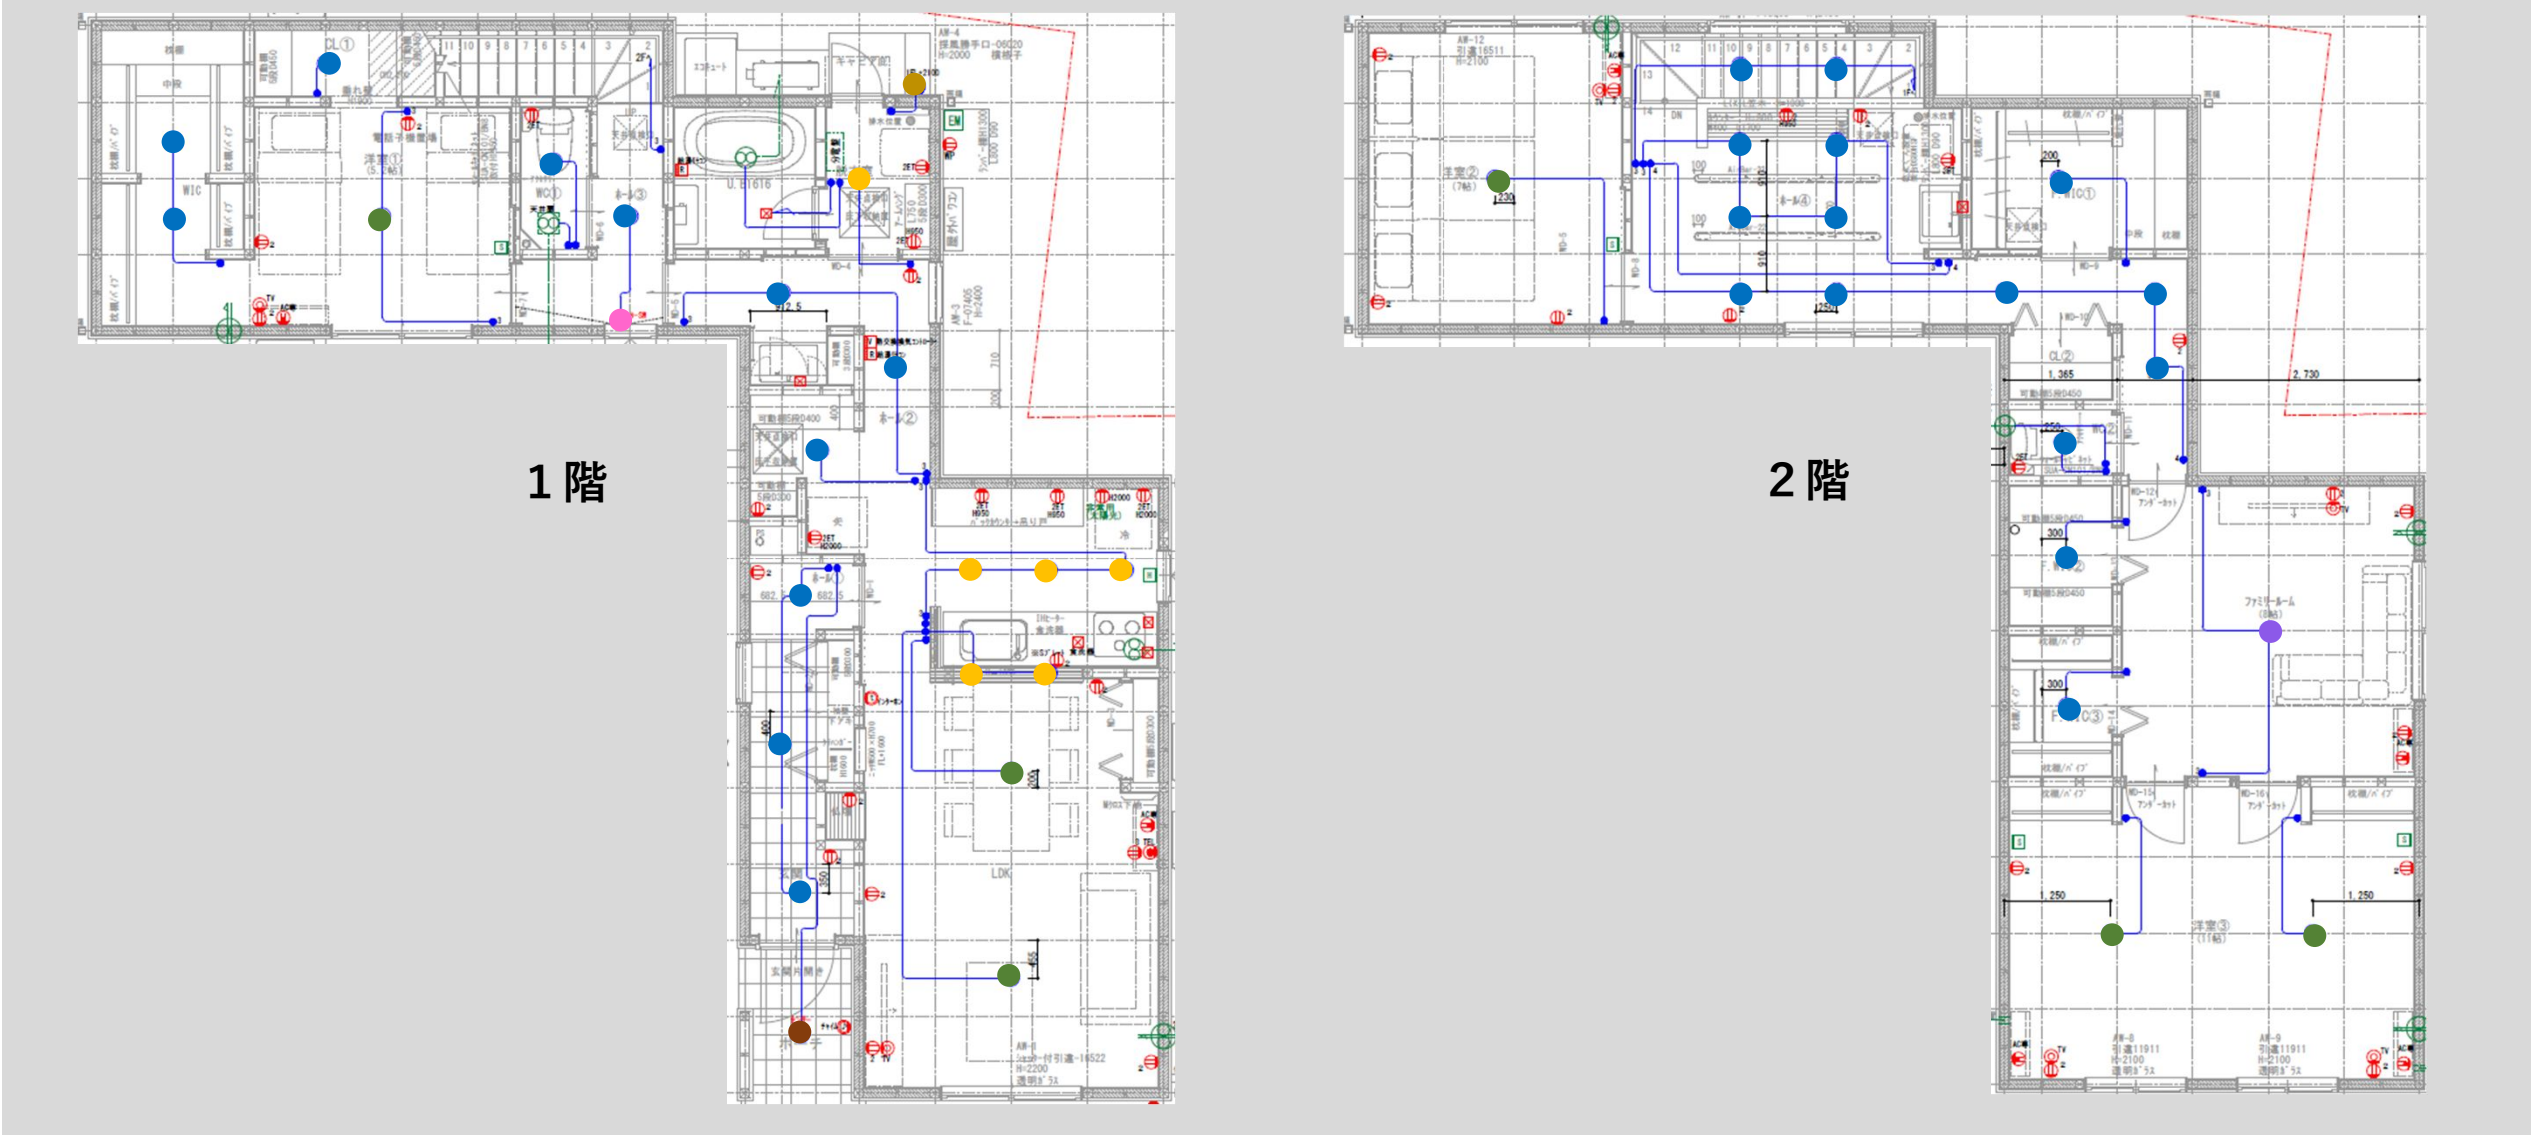

ドアホン：VL-SZ30KL
(Panasonic)



内部SW：アドバンス
シルバー

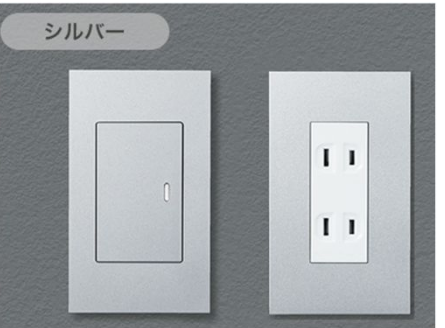

センサースイッチ
● × 1



コンセント：WTA1811CSK
プレート：WTA8101CS

外部：スマデザインシリーズ



2025. 4.20

ポーチ灯
● × 1

DDL-4496YW



高気密Se形 | 人感センサー | 連動マルチタイプ

DDL-4496 YW
電球色 / 2700K・Ra83

定格光束	消費電力	固有エネルギー消費効率
520lm	7.7W	67.5lm/W

¥18,800-(税抜) (LED内蔵)

LED 7.7W 白熱灯60W相当

- アルミダイカスト 白塗装
- アクリル 乳白(マット)
- 径φ111 埋込穴φ100 埋込深80mm 0.5kg
- 14VA
- 点灯照度調節機能付(暗・明・切)
- 点灯保持時間(1分)
- 拡散パネル付
- AC100V
- 光源寿命50,000時間
- 取付可能天井厚5~25mm
- 調光器併用不可

【連動器具について】
LED調光タイプ60VAまで
LED非調光タイプ不可 蛍光灯不可 白熱灯60Wまで

強制ON
ソフトスタート
フェードアウト
埋込穴100
埋込必要高80
LED交換不可
防雨形
温度保護機能付

勝手口灯
● × 1

DWP-40294Y



DWP-40294 Y
電球色 / 2700K・Ra82

定格光束	消費電力	固有エネルギー消費効率
100lm	4.2W	23.8lm/W

¥12,000-(税抜) (ランプ付)

LED電球 4.2W(E17) 白熱灯60W相当

- アクリル 乳白
- プラスチック 黒
- 径φ138 出85mm 0.4kg
- 7VA
- AC100V
- 光源寿命40,000時間
- 取付可能天井厚5~25mm
- 調光器併用不可

カバーはめこみ式

非調光
LED交換可能
防雨形

基本照明ダウンライト
● × 26 (11+15)

DDL6102AW



COBタイプ | 高気密Se形

DDL-6102 AW
温白色 / 3500K・Ra83

定格光束	消費電力	固有エネルギー消費効率
470lm	4.6W	102.1lm/W

¥3,600-(税抜) (LED内蔵)

LED 4.6W 白熱灯60W相当

- 銅板 白塗装
- アクリル 乳白(マット)
- 径φ116 埋込穴φ100 埋込深70mm 0.3kg
- 8VA
- 拡散パネル付
- AC100V
- 光源寿命60,000時間
- 取付可能天井厚5~25mm
- 調光器併用不可

LED交換不可
防雨形
温度保護機能付
埋込穴100
埋込必要高70
傾斜天井55°
準耐火

● × 6

DDL6102WW



COBタイプ | 高気密Se形

DDL-6102 WW
昼白色 / 5000K・Ra83

定格光束	消費電力	固有エネルギー消費効率
480lm	4.6W	104.3lm/W

¥3,600-(税抜) (LED内蔵)

LED 4.6W 白熱灯60W相当

- 銅板 白塗装
- アクリル 乳白(マット)
- 径φ116 埋込穴φ100 埋込深70mm 0.3kg
- 8VA
- 拡散パネル付
- AC100V
- 光源寿命60,000時間
- 取付可能天井厚5~25mm
- 調光器併用不可

LED交換不可
防雨形
温度保護機能付
埋込穴100
埋込必要高70
傾斜天井55°
準耐火

● × 6

DCL40507



タイマー付リモコン・ブルレス | 調色調光タイプ

DCL-40507
昼光色 / 6500K・Ra83 ~ 電球色 / 2700K・Ra83

LED	LED 29.5W	定格光束	消費電力	固有エネルギー消費効率
LED	30VA	3699lm	29.5W	125.3lm/W

¥22,000-(税抜) (LED内蔵)

- アクリル 乳白(マット)
- 径φ510 高128mm 1.6kg
- フルレリースイッチ付(全灯・※点灯・常夜灯)
- ※消灯前の調色調光状態
- 調色機能付(6500K~2700K)
- 調光機能付(5%~100%)
- 常夜灯6段階調光
- AC100V
- 光源寿命40,000時間
- 消費効率昼白色時
- 調光器併用不可
- ※シーンコントロールローラーは使用できません。

クイック取付式
カバー回転式

傾斜天井 55° 図取付パーツ DP-40091 可能 図取付パーツ DP-40638

● × 1

DCL40508



タイマー付リモコン・ブルレス | 調色調光タイプ

DCL-40508
昼光色 / 6500K・Ra83 ~ 電球色 / 2700K・Ra83

LED	LED 34W	定格光束	消費電力	固有エネルギー消費効率
LED	35VA	4299lm	34W	126.4lm/W


¥26,000-(税抜) (LED内蔵)

- アクリル 乳白(マット)
- 径φ510 高128mm 1.6kg
- フルレリースイッチ付(全灯・※点灯・常夜灯)
- ※消灯前の調色調光状態
- 調色機能付(6500K~2700K)
- 調光機能付(5%~100%)
- 常夜灯6段階調光
- AC100V
- 光源寿命40,000時間
- 消費効率昼白色時
- 調光器併用不可
- ※シーンコントロールローラーは使用できません。

クイック取付式
カバー回転式

傾斜天井 55° 図取付パーツ DP-40091 可能 図取付パーツ DP-40638

決定図

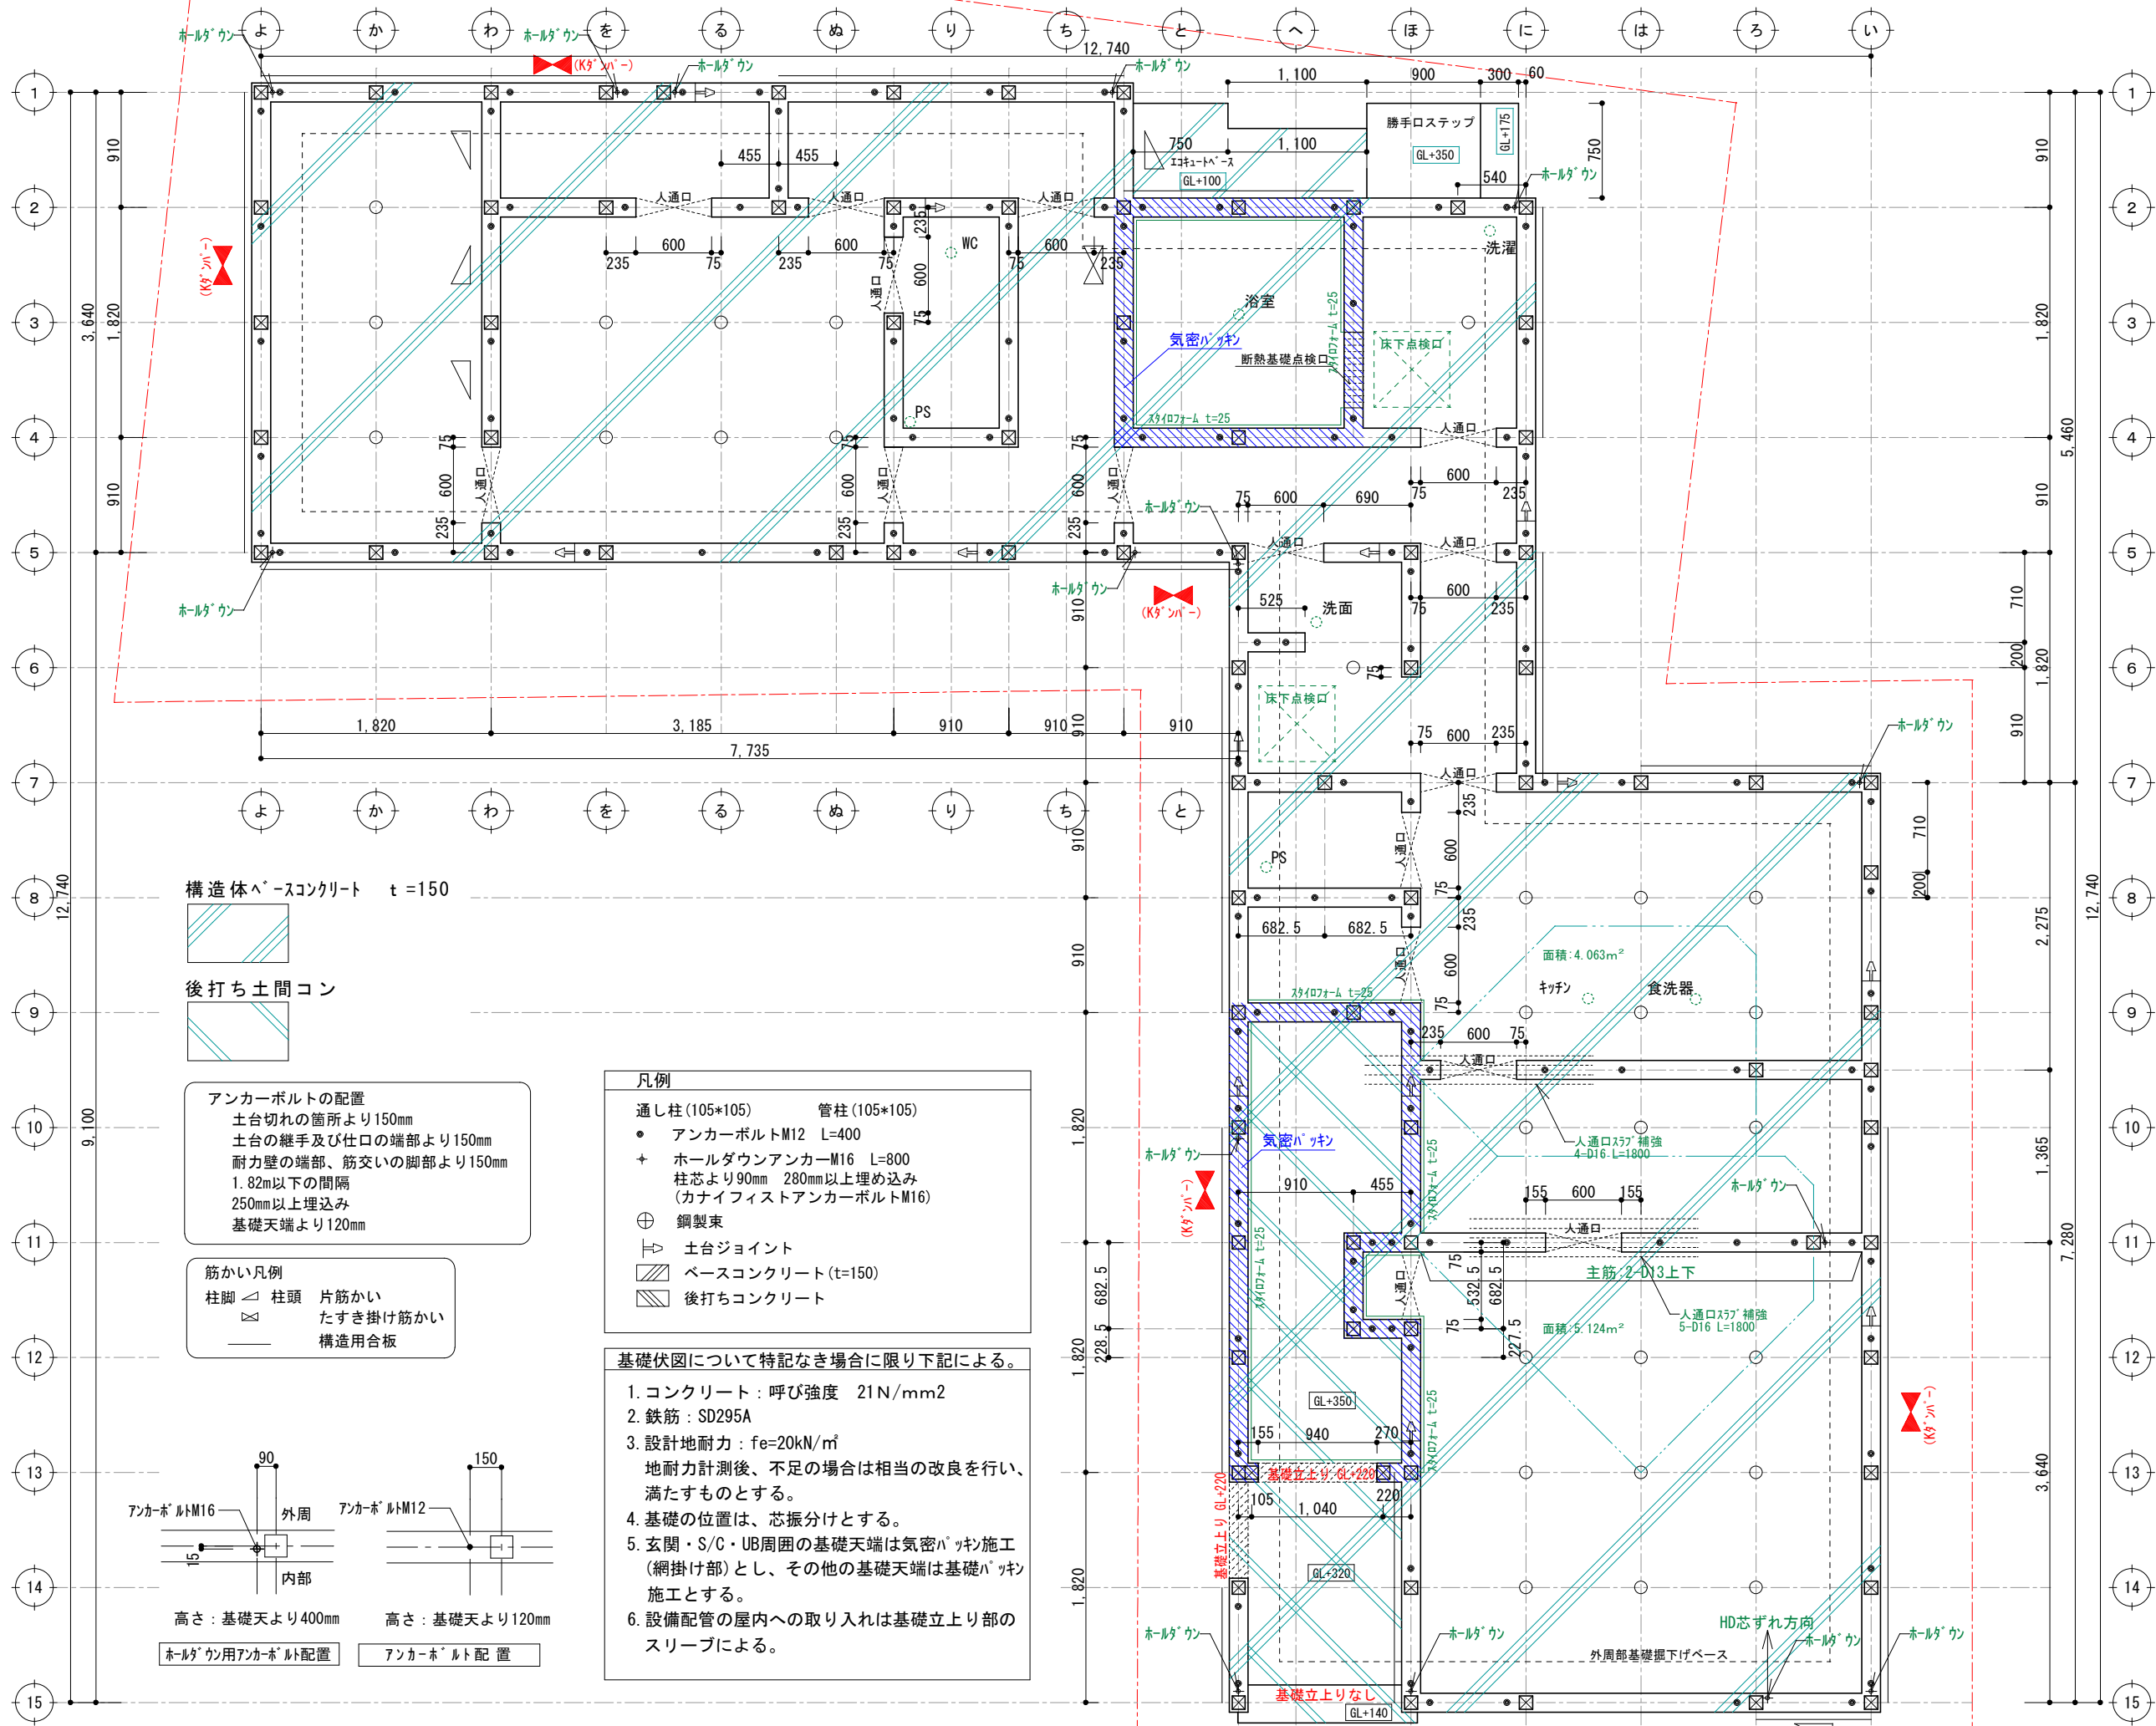

構造体ベースコンクリート t=150

後打ち土間コン

アンカーボルトの配置
土台切れの箇所より150mm
土台の継手及び仕口の端部より150mm
耐力壁の端部、筋交いの脚部より150mm
1.82m以下の間隔
250mm以上埋込み
基礎天端より120mm

筋かい凡例
柱脚 △ 柱頭 片筋かい
たすき掛け筋かい
構造用合板


凡例


通し柱 (105*105) 管柱 (105*105)

- アンカーボルトM12 L=400
- ホールダウンアンカーM16 L=800
柱芯より90mm 280mm以上埋め込み
(カナフィストアンカーボルトM16)
- 鋼製束
- 土台ジョイント
- ベースコンクリート (t=150)
- 後打ちコンクリート


基礎伏図について特記なき場合に限り下記による。

- コンクリート：呼び強度 21N/mm²
- 鉄筋：SD295A
- 設計地耐力：fe=20kN/m²
地耐力計測後、不足の場合は相当の改良を行い、満たすものとする。
- 基礎の位置は、芯振分けとする。
- 玄関・S/C・UB周囲の基礎天端は気密パッキン施工（網掛け部）とし、その他の基礎天端は基礎パッキン施工とする。
- 設備配管の屋内への取り入れは基礎立上り部のスリーブによる。

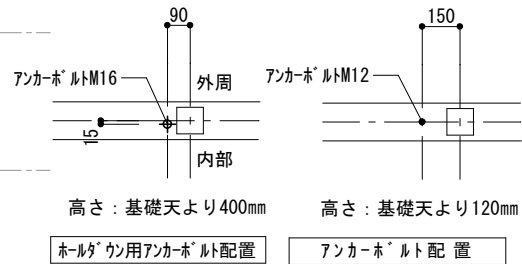


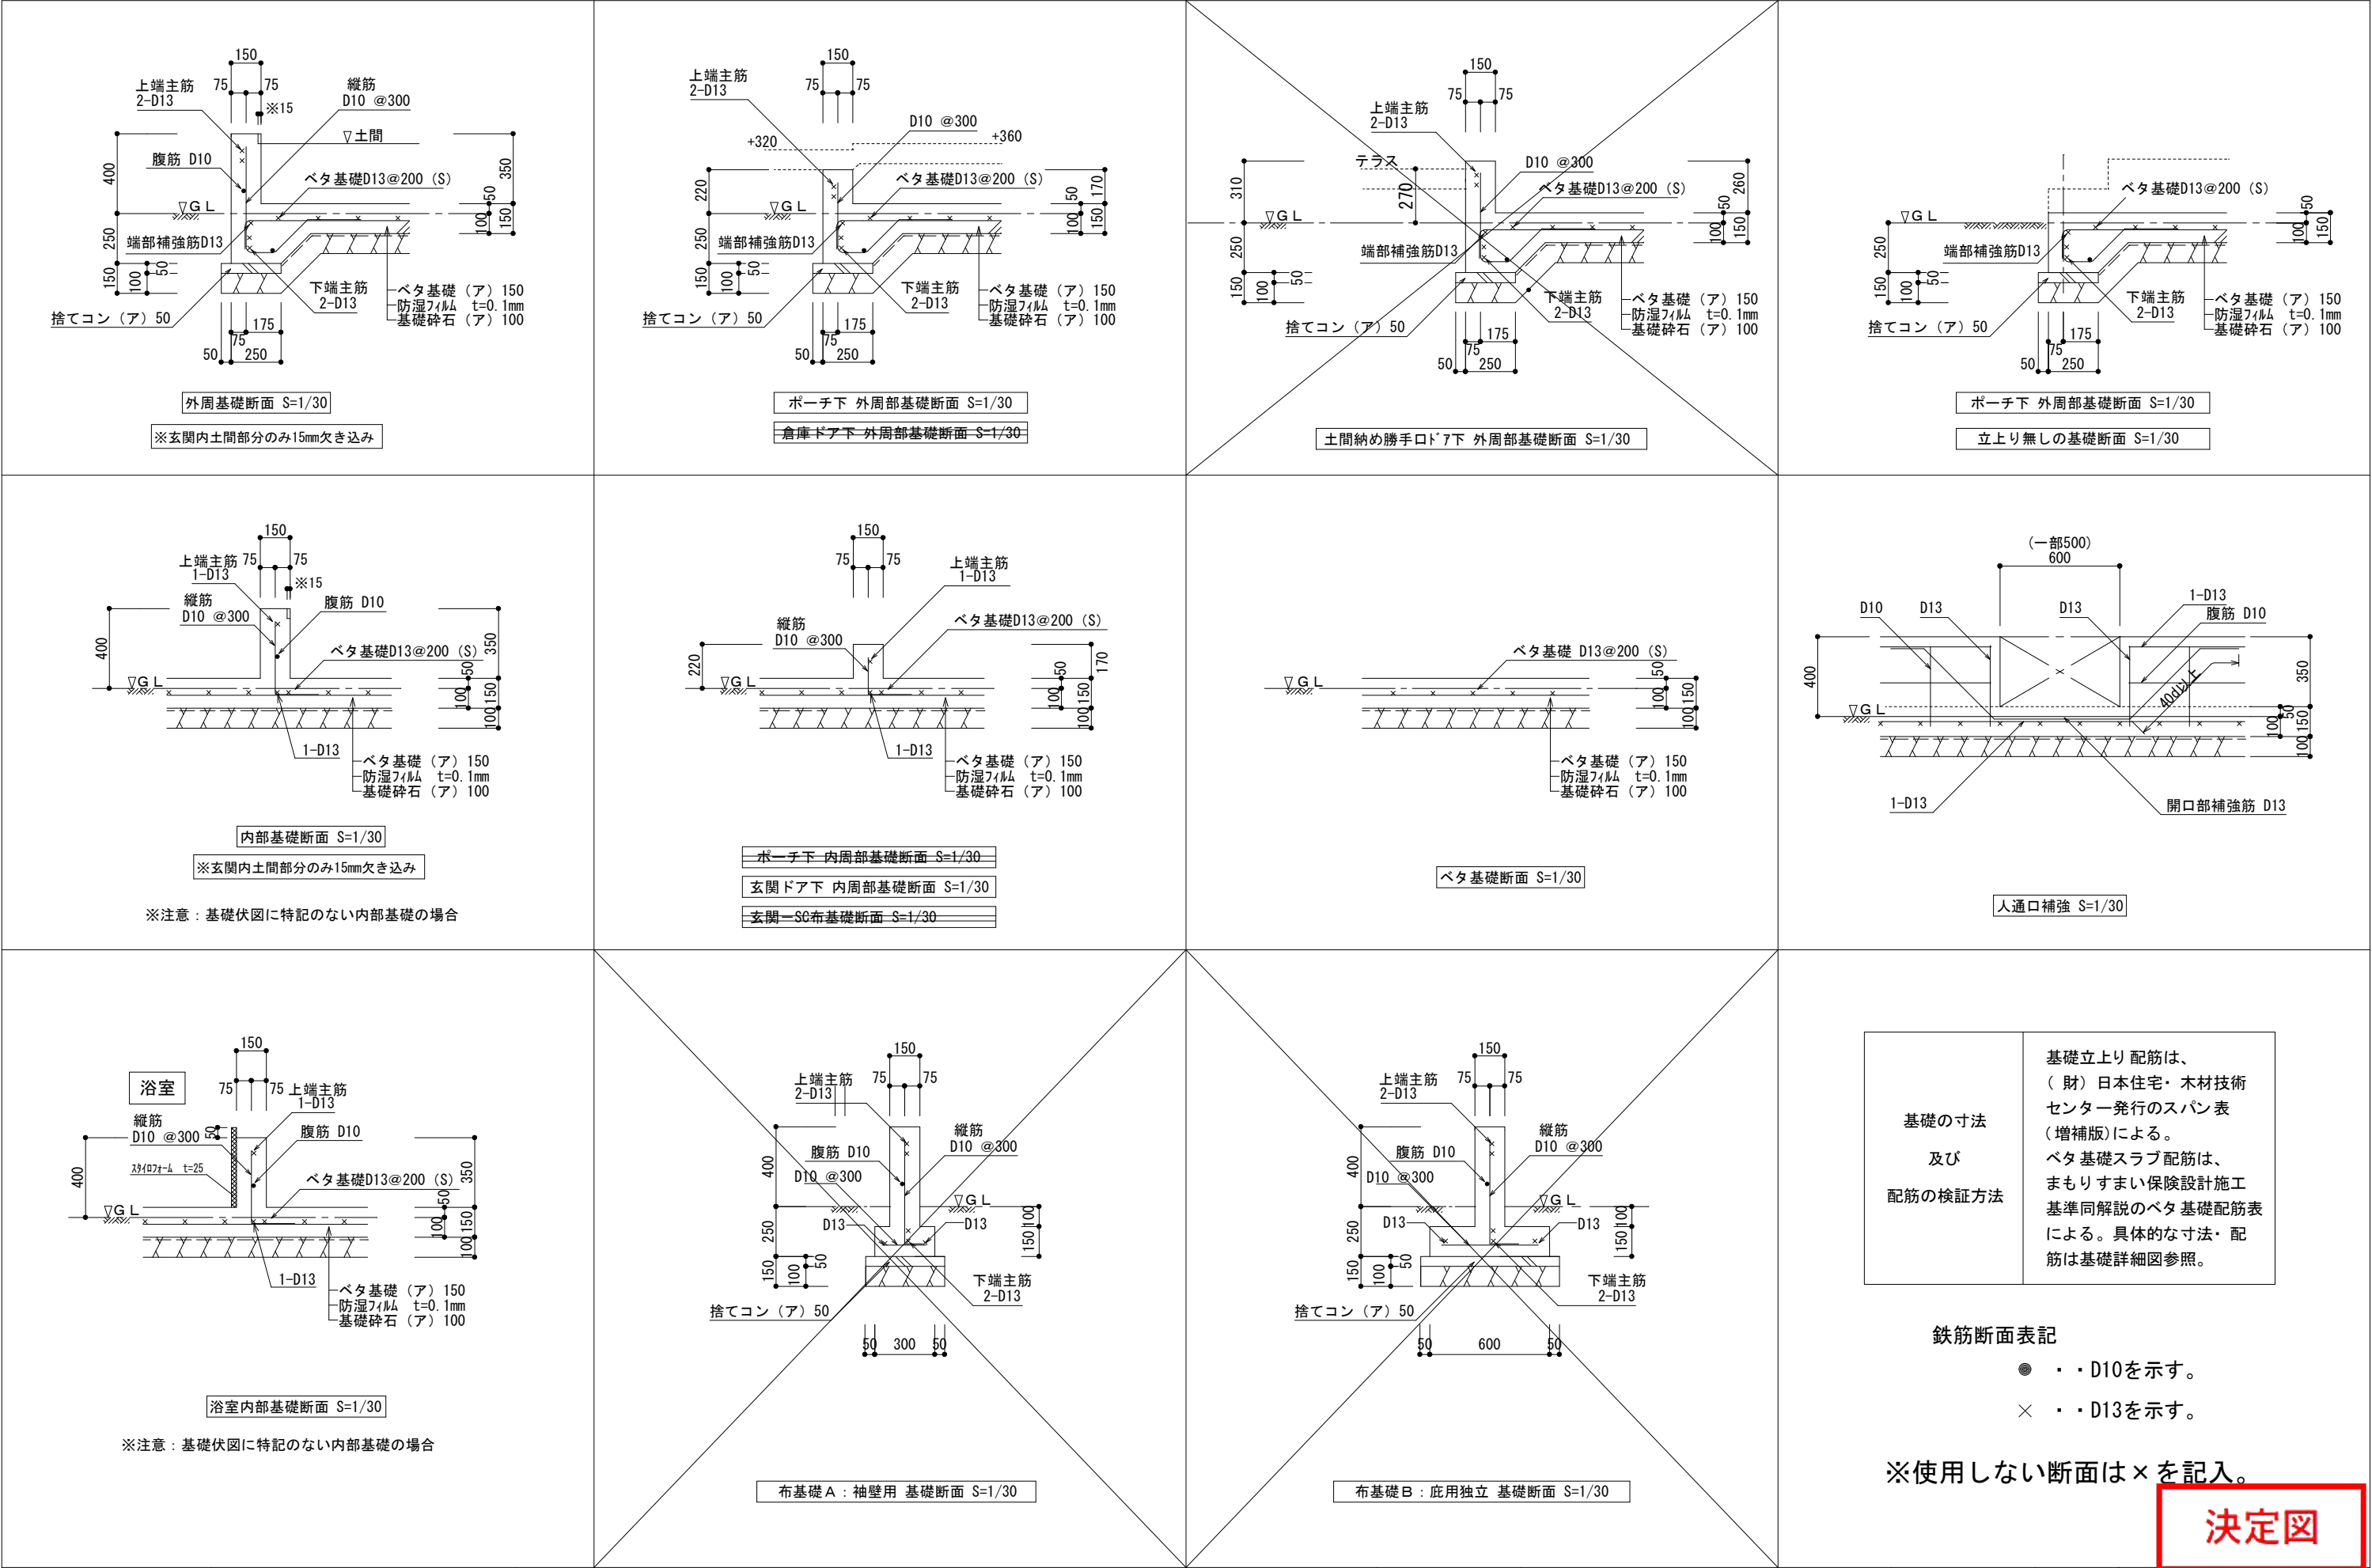

決定図

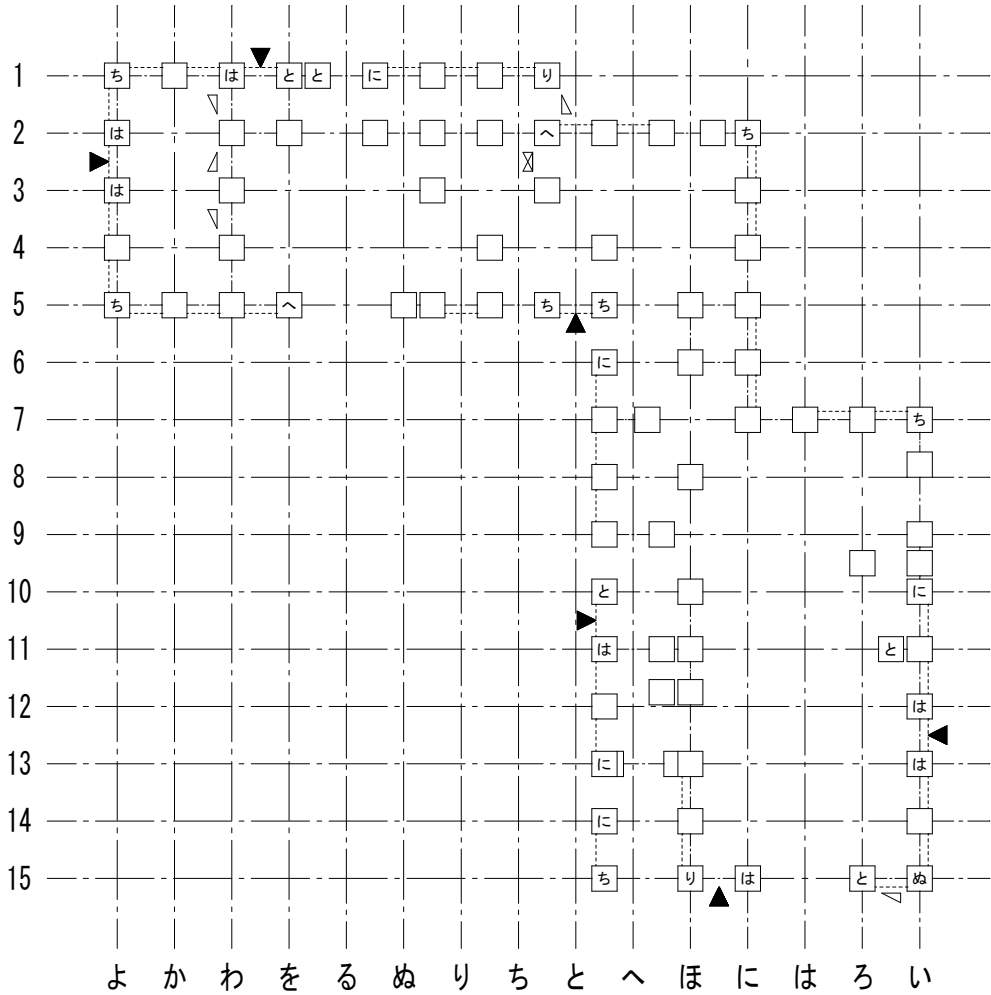

1 階柱壁伏図

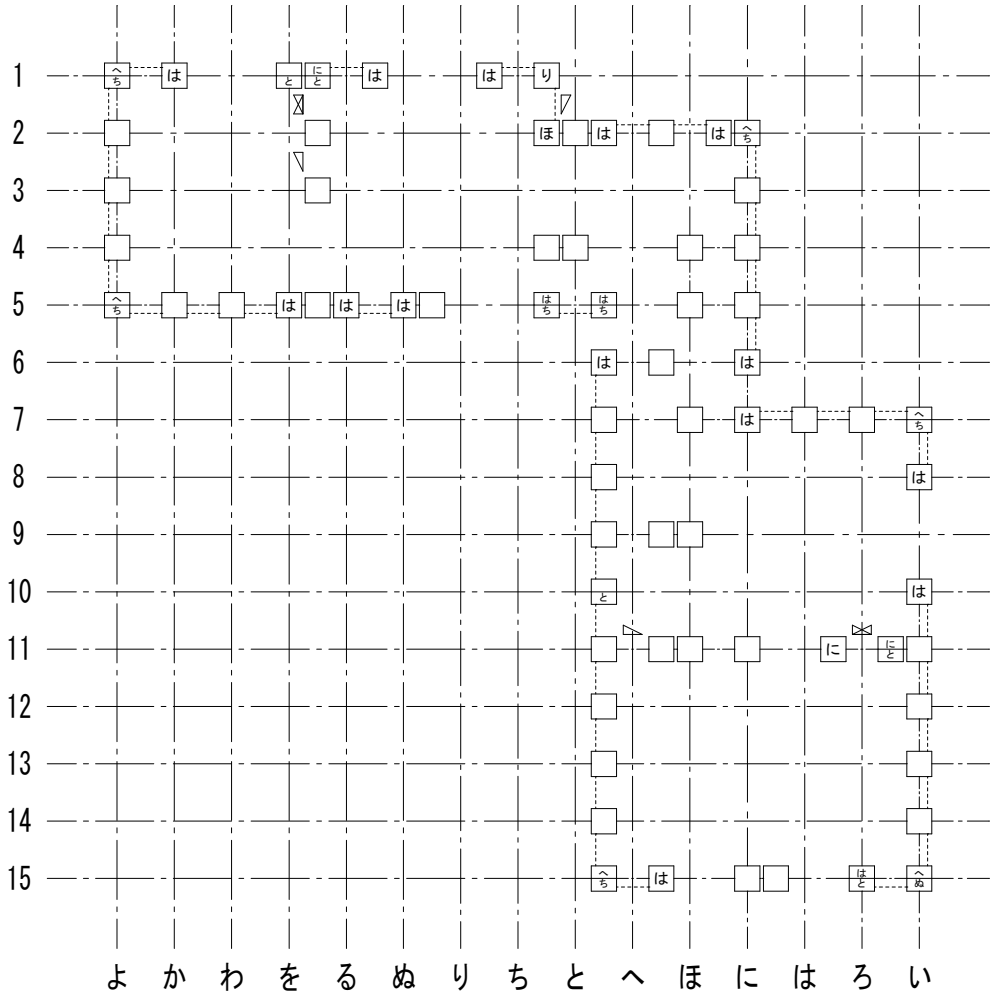

2 階柱壁伏図

接合部凡例			
*接合部凡例はユーザ設定されたものです。			
記号	仕様（カナイ金物）	N	倍率
SBCP	スリムビルドコーナー75, チビクリCK (化粧柱の場合)	0.00	1.00
SBCP	スリムビルドコーナー75, チビクリCK (化粧柱の場合)	0.65	1.00
SBCP	は スリムビルドコーナー75	1.00	1.00
ARCG	に アレントコーナー合板用	1.40	2.20
ARCG	ほ アレントコーナー合板用	1.60	2.20
ARCG	へ アレントコーナー合板用	1.80	2.20
HD15	と ブレイブホールダウン B-HD15	2.80	3.60
HD20	ち ブレイブホールダウン B-HD20	3.70	4.70
HD25	り ブレイブホールダウン B-HD25	4.70	4.80
HD30	ぬ ブレイブホールダウン B-HD30	5.60	7.20
J1	る 腰掛け蟻若しくは大入れ蟻掛け+羽子板 [※] ルト、短冊金物		1.90
J2	を 腰掛け蟻若しくは大入れ蟻掛け+羽子板 [※] ルト、短冊金物×2		3.00

※表示なき金物は「は」とする。

梁継手・仕口用
梁継手・仕口用

接合部凡例			
*接合部凡例はユーザ設定されたものです。			
記号	仕様（タナカ金物）	N	倍率
FCP	フックコーナー, チビクリCK (化粧柱の場合)	0.00	1.00
FCP	フックコーナー, チビクリCK (化粧柱の場合)	0.65	1.00
FCP	は フックコーナー	1.00	1.00
CCP	に シナコーナー	1.40	2.20
CCP	ほ シナコーナー	1.60	2.20
CCP	へ シナコーナー	1.80	2.20
HD15	と ビス止めホールダウンU HD15	2.80	3.60
HD20	ち ビス止めホールダウンU HD20	3.70	4.70
HD25	り ビス止めホールダウンU HD25	4.70	4.80
HD30	ぬ ビス止めホールダウンU HD15×2 (HD35)	5.60	7.20
J1	る 腰掛け蟻若しくは大入れ蟻掛け+羽子板 [※] ルト、短冊金物		1.90
J2	を 腰掛け蟻若しくは大入れ蟻掛け+羽子板 [※] ルト、短冊金物×2		3.00


※表示なき金物は「は」とする。

梁継手・仕口用
梁継手・仕口用

筋かいの種類に応じた筋かいの端部の接合部の仕様		
	筋かいの種類	接合部の仕様（構造方法）
イ	鉄筋φ9	柱又は横架材を貫通し、三角座金を介してナット締め、又は鋼板添え板を用い鋼板を柱及び横架材にCN90, 8本平打ち
ロ	筋かい:15×90	柱・横架材を欠き込み、柱・横架材双方に対してN65, 5本平打ち
ハ	筋かい:30×90	鋼板添え板t=1.6mmを筋かいに対してボルトφ12及びCN65, 3本平打ち、柱に対してCN65, 3本平打ち、横架材に対してCN65, 4本平打ち。筋かいプレートBP同等品
ニ	筋かい:45×90	鋼板添え板t=2.3mmを筋かいに対してボルトφ12及びスクリュー釘φ4.5L50, 7本平打ち、柱及び横架材に対してスクリュー釘φ4.5L50, 5本平打ち。筋かいプレートBP-2同等品
ホ	筋かい:90×90	柱又は横架材にボルトφ12mmを用いて一面剪断接合

胴差と通し柱の接合部の仕様		
	胴差と通し柱の条件	仕口
T1	通し柱の片側に胴差が来る場合	胴差を柱にかたぎ大入れ短ほぞ差しの上、羽子板ボルト、かね折り金物又は同等以上の仕口
T2	通し柱の両側に胴差が来る場合	胴差を柱にかたぎ大入れ短ほぞ差しの上、短冊金物又は、同等以上の仕口で胴差相互を緊結
T3	通し柱と胴差の接合部の近くに90×90以上の筋かいが来る場合（通し柱が建物の出隅にあるか、筋かい壁が外壁と直交して接する場合）	胴差を通し柱に、15KN用引き寄せ金物を水平に用いて緊結

決定図

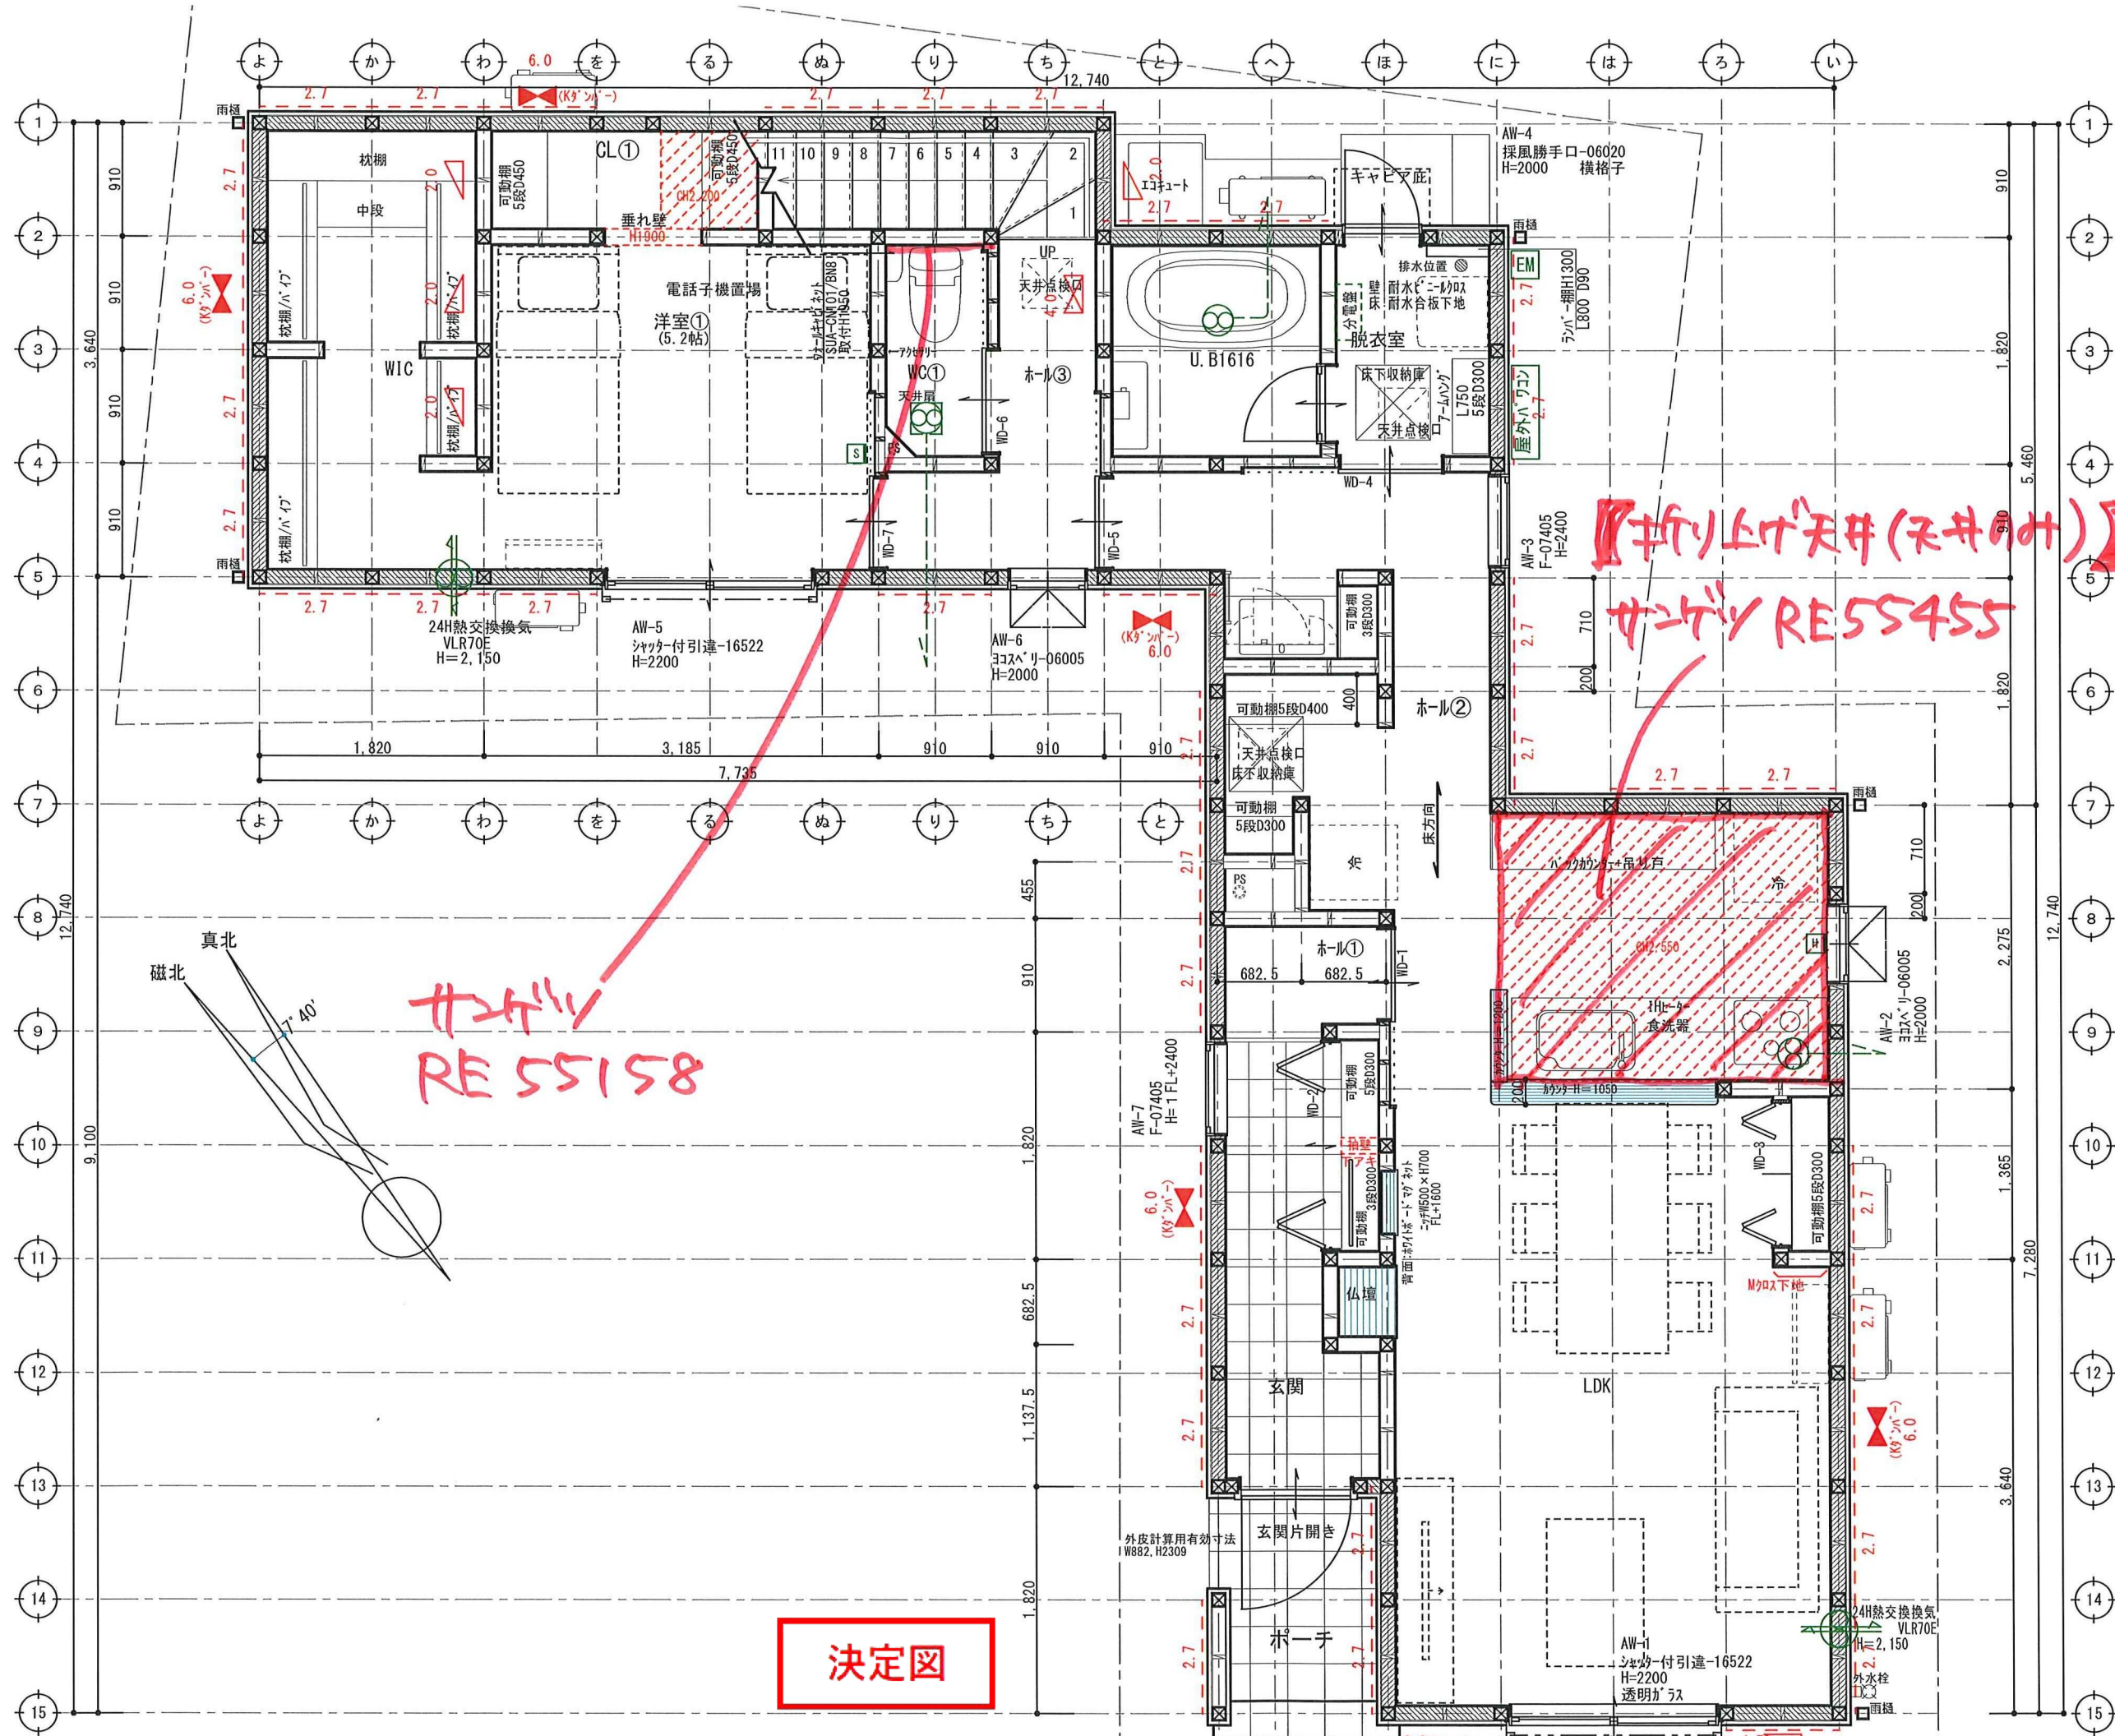

準防火地域

壁付け 住宅用火災報知器			数量
H	熱感知器	電池式(単独型)	1
	熱感知器	露出型	
壁付け 住宅用火災報知器			数量
S	煙感知器	電池式(単独型)	1
	煙感知器	露出型	

※ 煙感知器は壁・梁より600mm以上離す
壁に取付ける場合、
天井から150mm以上500mm以内離す
換気扇・エアコン吹出口から1500mm以上離す
※ 全室LED照明とする。
※ 標準天井高さ2,400
※ 表記なきガラスは型ガラス


* 凡例

- 管柱 (105×105)
- K9' ユニ (3.30倍 FRM-0641)
- 片筋違い (2.00倍 45×90)
(例 左:柱脚 右:柱頭)
- たすき掛筋違い (4.00倍 45×90)
- 構造用合板 (2.70倍)
(t=9 タイガ-EXNIN-)
- 床点検口
- 天井点検口
- 換気扇
- 熱交換換気扇VLR-70

内装仕上: ホルムアルデヒド発散等級F☆☆☆☆等級相当
天井裏等: ホルムアルデヒド発散等級F☆☆☆☆等級相当

アドバンスシリーズ スマートデザイン (外部)	
凡例	
1	コンセント 1ヶ口
2	コンセント 2ヶ口
3	コンセント 3ヶ口
1ET	コンセント1ヶ口接地ターミナル付
2ET	コンセント2ヶ口接地ターミナル付
WP	コンセント 防水型
EA	エアコン用コンセント
200V	200V用コンセント
WP	防雨入線プレート
スイッチ	スイッチ
3	3路スイッチ
4	4路スイッチ
直結電源	直結電源
TV	テレビ取出口
TEL	電話取出口 (テレホンガイド)
LAN	LAN取出口 (テレホンガイド)
照明	照明
リモコン	リモコン (結露関係・ルフロ)
メーター	メーター
分電盤	分電盤
チャイム	チャイム

※ACコンセント天井付け
※TVアンテナ工事
※スイッチはFL+1100、コンセントはFL+200

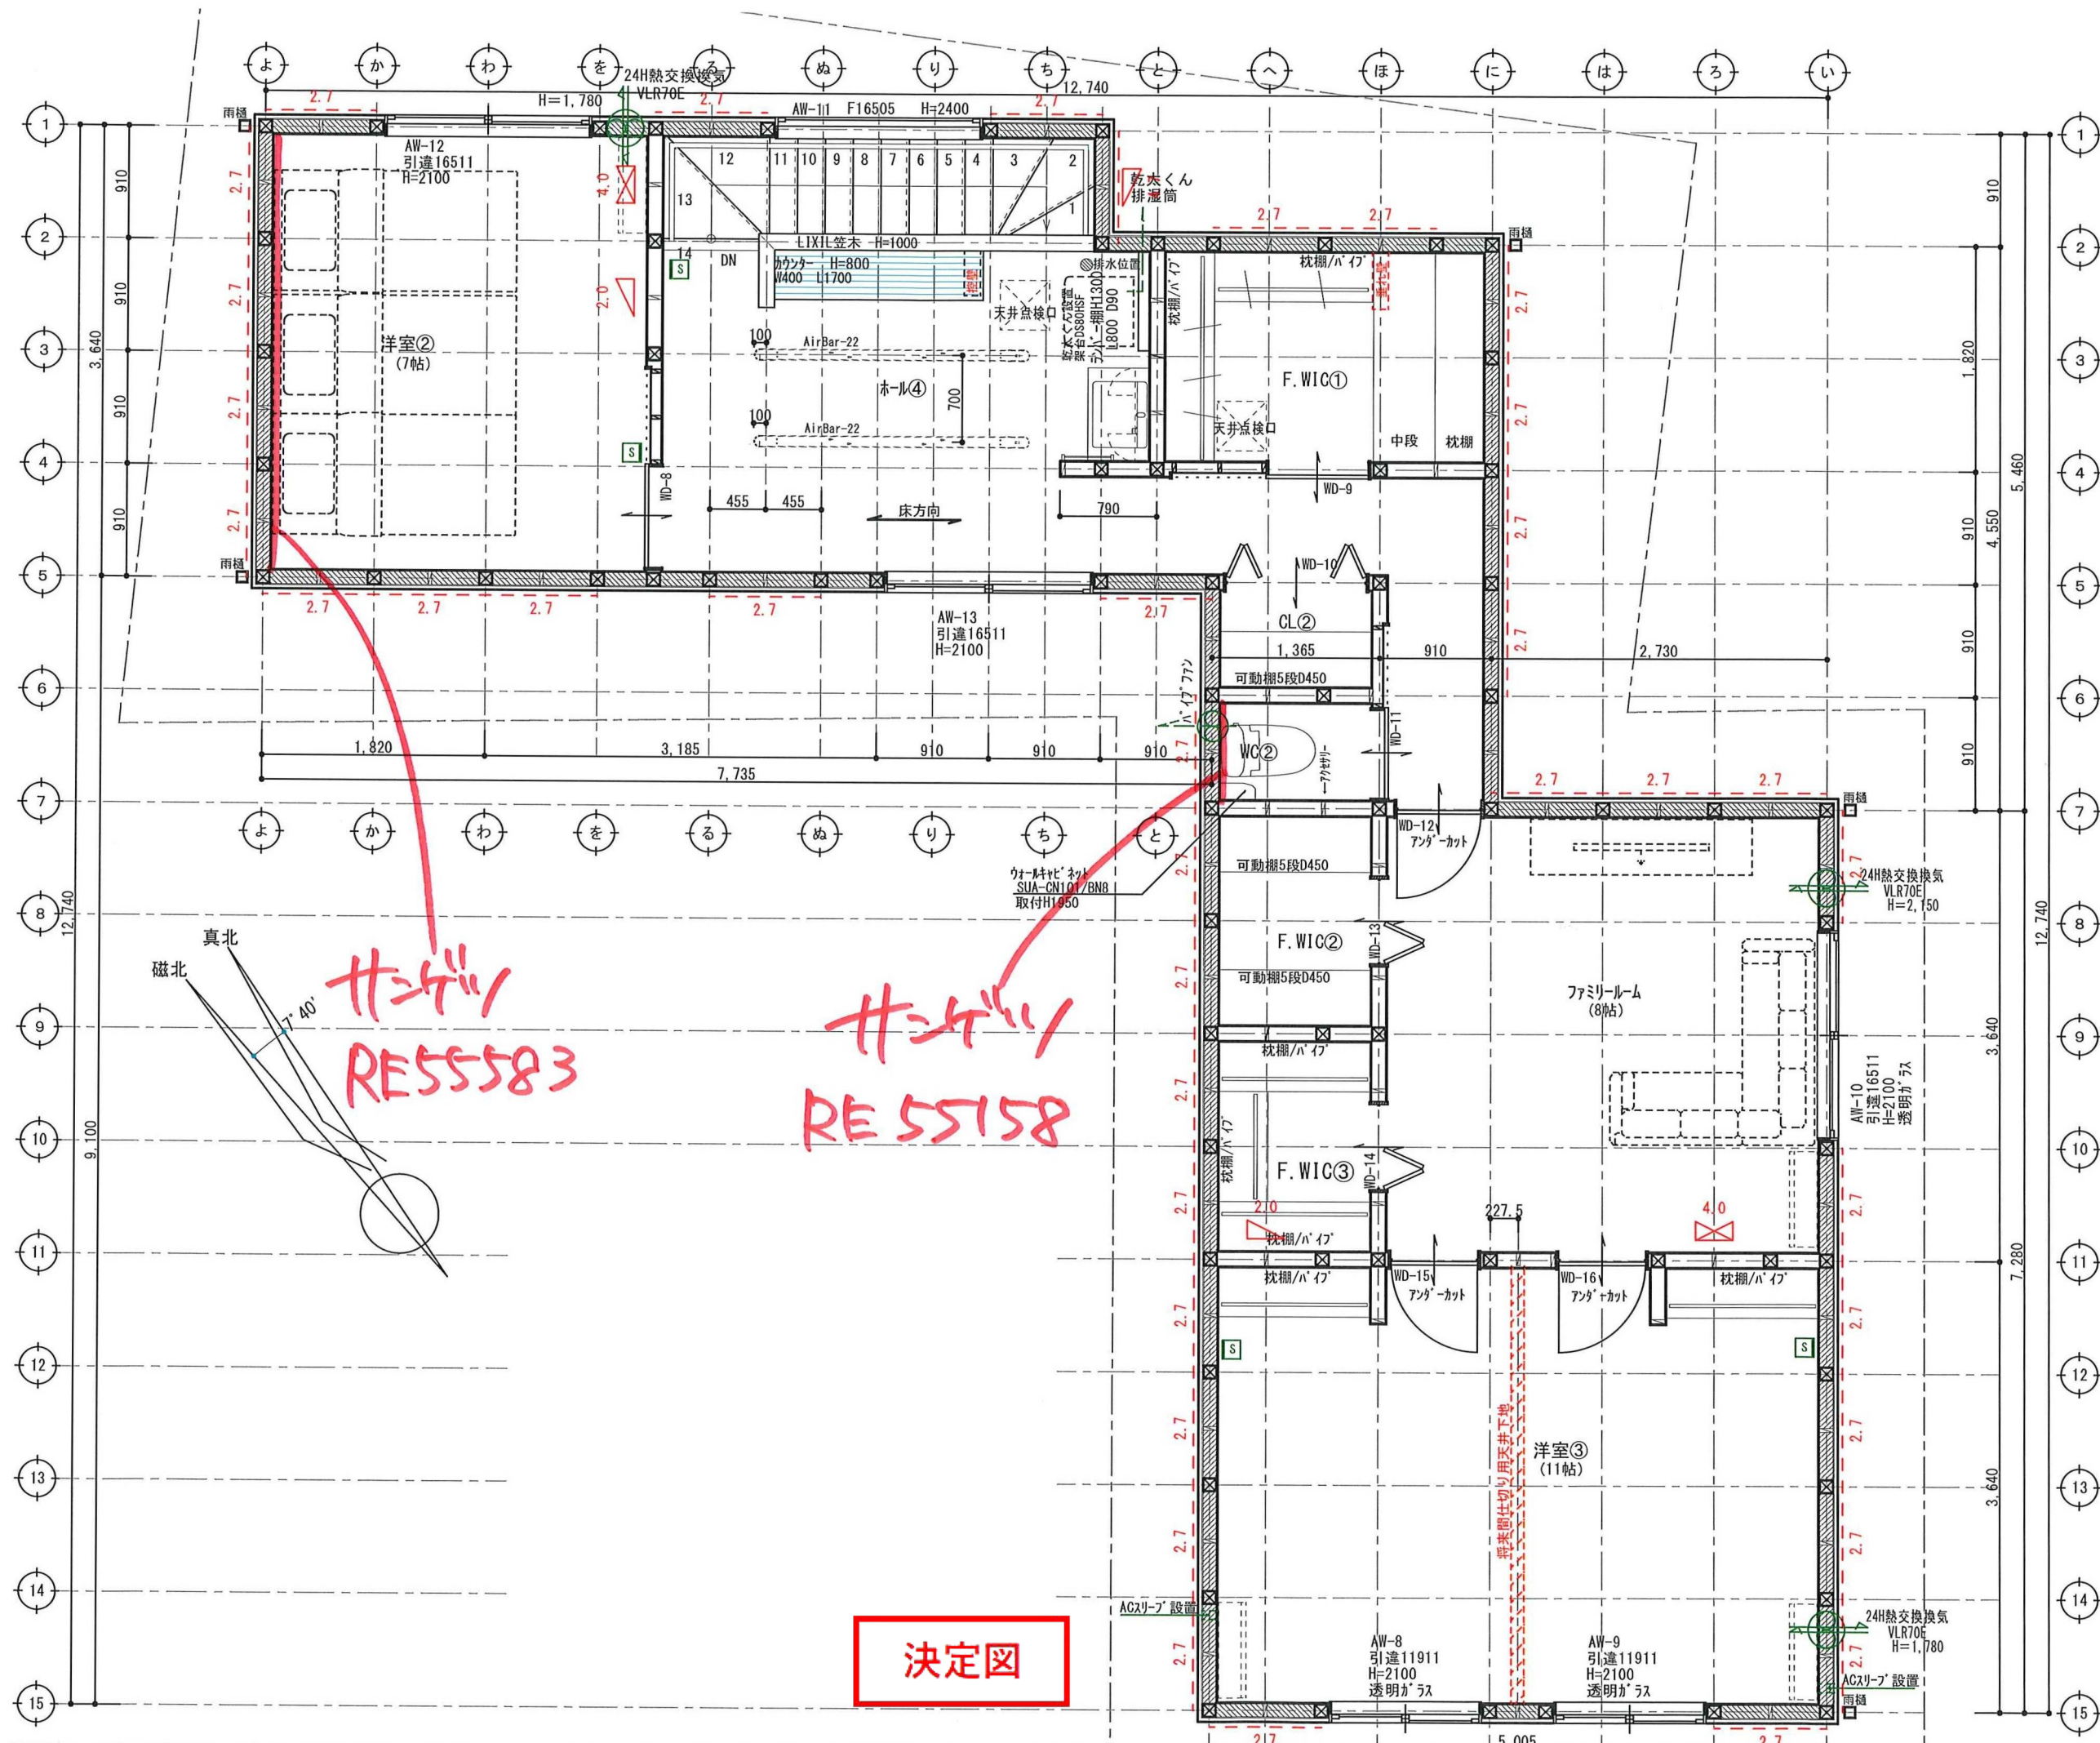

準防火地域

壁付け		数量
H	熱感知器	電池式(単独型)
	露出型	
壁付け 住宅用火災報知器		数量
S	煙感知器	電池式(単独型)
	露出型	4

- ※ 煙感知器は壁・梁より600mm以上離す
壁に取付ける場合、
天井から150mm以上500mm以内離す
換気扇・エアコン吹出口から1500mm以上離す
- ※ 全室LED照明とする。
- ※ 標準天井高さ2,400
- ※ 表記なきガラスは型ガラス

* 凡例

- ☒ 管柱 (105×105)
- △ K9' ユニバーサル (3.30倍 FRM-0641)
- △ 片筋違 (2.00倍 45×90)
(例 左:柱脚 右:柱頭)
- △ たすき掛筋違 (4.00倍 45×90)
- △ 構造用合板 (2.70倍)
(t=9 タイプ EXH(n-))
- △ 床点検口
- △ 天井点検口
- ⊕ 換気扇
- ⊕ 熱交換換気扇VLR-70

内装仕上: ホルムアルデヒド発散等級F☆☆☆☆等級相当
天井裏等: ホルムアルデヒド発散等級F☆☆☆☆等級相当

アドバンスシリーズ スマートデザイン (外部)	
凡例	
1	コンセント 1ヶ所
2	コンセント 2ヶ所
3	コンセント 3ヶ所
1ET	コンセント1ヶ所接地ターミナル付
2ET	コンセント2ヶ所接地ターミナル付
WP	コンセント 防水型
WP	エアコン用コンセント
WP	200V用コンセント
WP	防雨入線プレート
3	スイッチ
4	3路スイッチ
4	4路スイッチ
TEL	直結電源
TEL	テレビ取出口
LAN	電話取出口 (テレホンガイド)
LAN	LAN取出口 (テレホンガイド)
照明	照明
リモコン	リモコン (結露関係・ルフロ)
メーター	メーター
分電盤	分電盤
チャイム	チャイム

- ※ ACコンセント天井付け
- ※ TVアンテナ工事
- ※ スイッチはFL+1100、コンセントはFL+200