


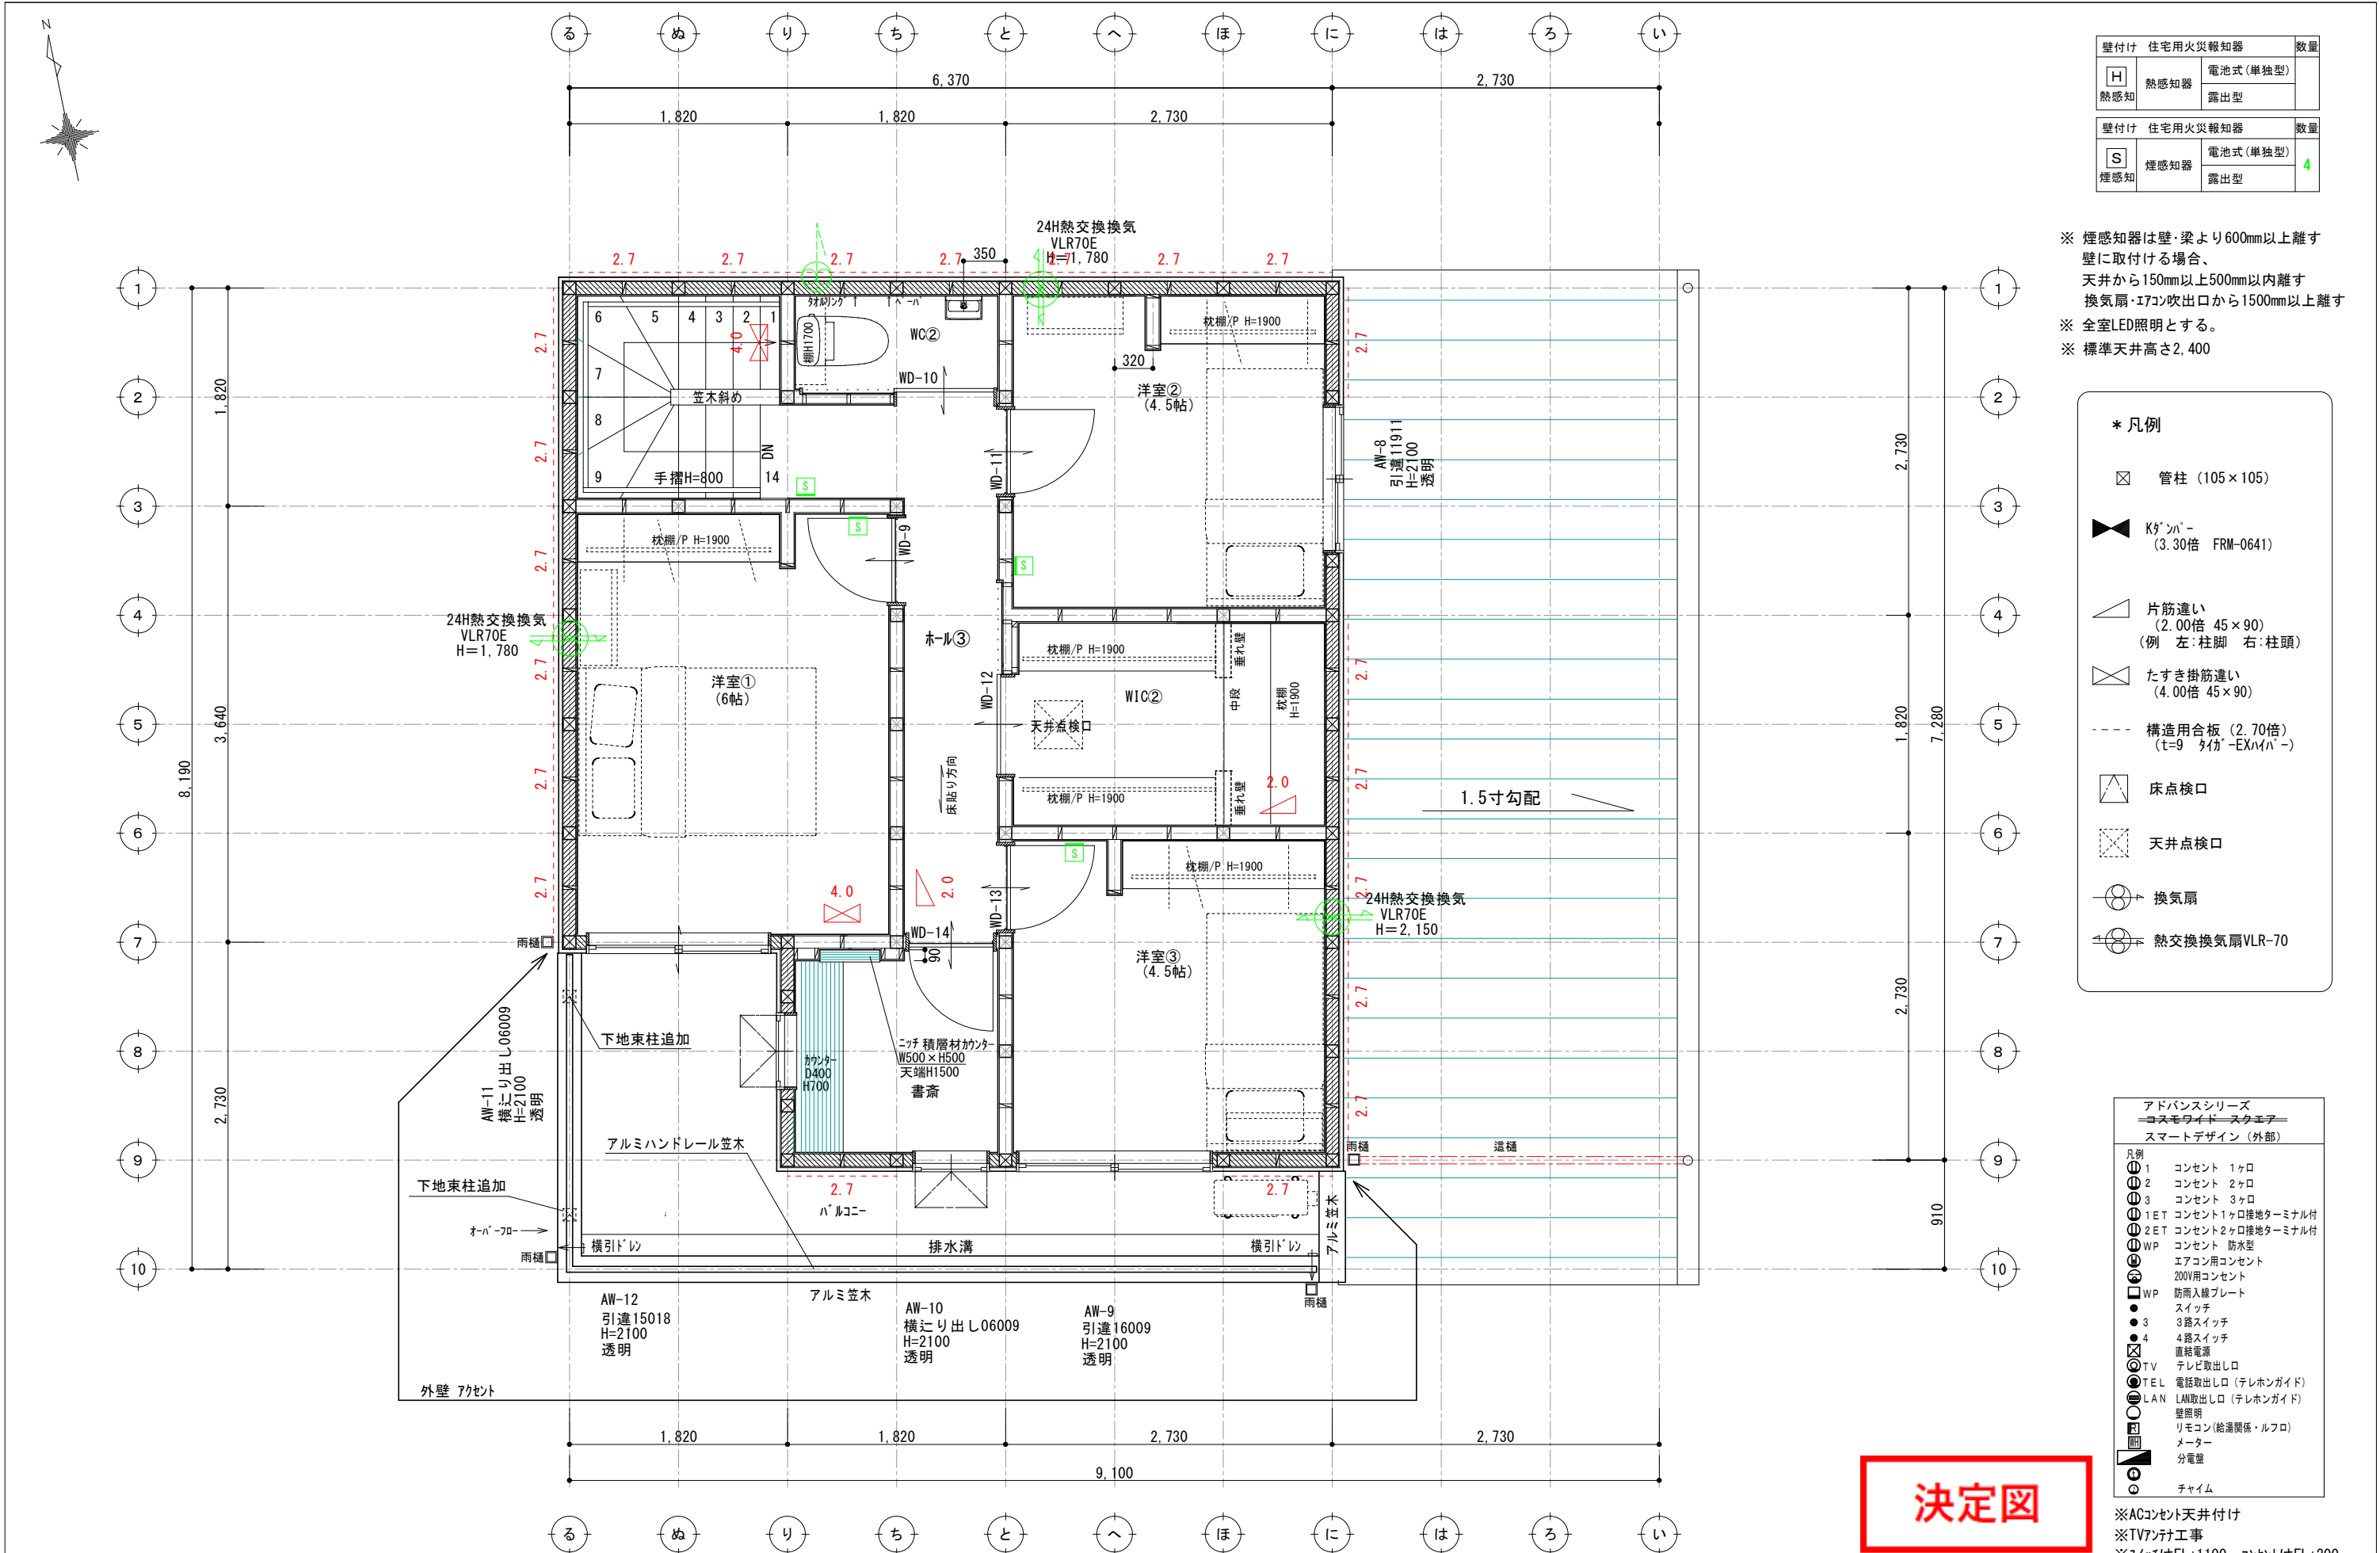

壁付け 住宅用火災報知器			数量
H 熱感知	電池式(単独型)		
	露出型		
壁付け 住宅用火災報知器			数量
S 煙感知	電池式(単独型)		4
	露出型		

※ 煙感知器は壁・梁より600mm以上離す
壁に取付ける場合、
天井から150mm以上500mm以内離す
換気扇・エアコン吹出口から1500mm以上離す
※ 全室LED照明とする。
※ 標準天井高さ2,400

* 凡例

管柱 (105×105)

Kタ'ンパ' (3.30倍 FRM-0641)

片筋違い (2.00倍 45×90)
(例 左:柱脚 右:柱頭)

たすき掛筋違い (4.00倍 45×90)

構造用合板 (2.70倍)
(t=9 3枚付 EXハイバ')

床点検口

天井点検口

換気扇

熱交換換気扇VLR-70

アドバンスシリーズ コスモワイド・ステア スマートデザイン (外部)			
凡例	1	コンセント	1ヶ所
2	コンセント	2ヶ所	
3	コンセント	3ヶ所	
1ET	コンセント1ヶ所接地ターミナル付		
2ET	コンセント2ヶ所接地ターミナル付		
WP	コンセント 防水型		
	エアコン用コンセント		
	200V用コンセント		
WP	防雨入線プレート		
	スイッチ		
●	3	3路スイッチ	
●	4	4路スイッチ	
●	直結電源		
●	テレビ取出口		
●	TEL 電話取出口 (テレホンガイド)		
●	LAN LAN取出口 (テレホンガイド)		
●	壁照明		
●	リモコン (給湯関係・ルフロ)		
●	メーター		
●	分電盤		
●	チャイム		

※ACコンセント天井付け
※TVアンテナ工事
※スイッチはFL+1100、コンセントはFL+200