




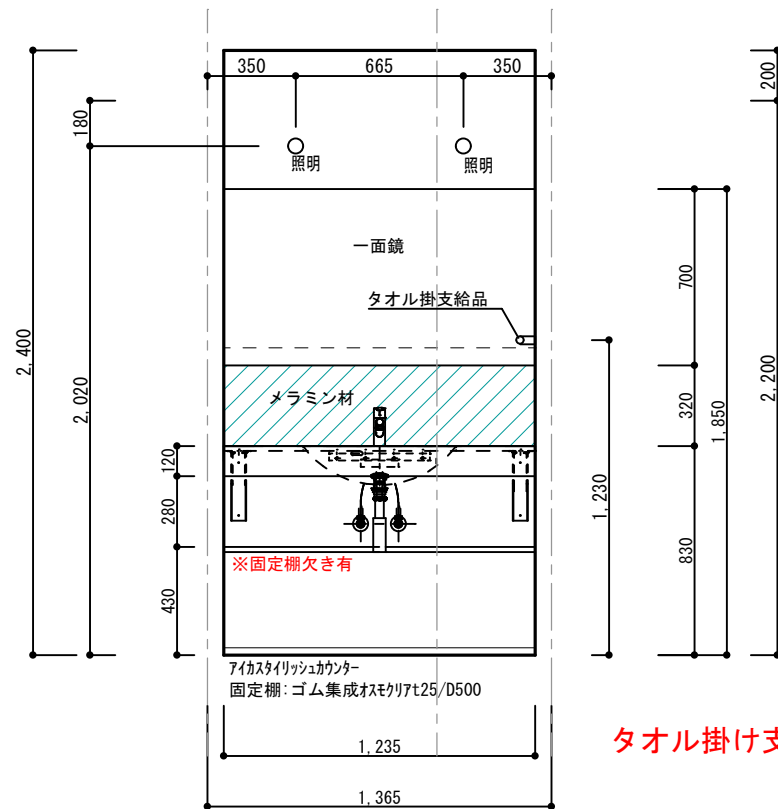


洗面 北

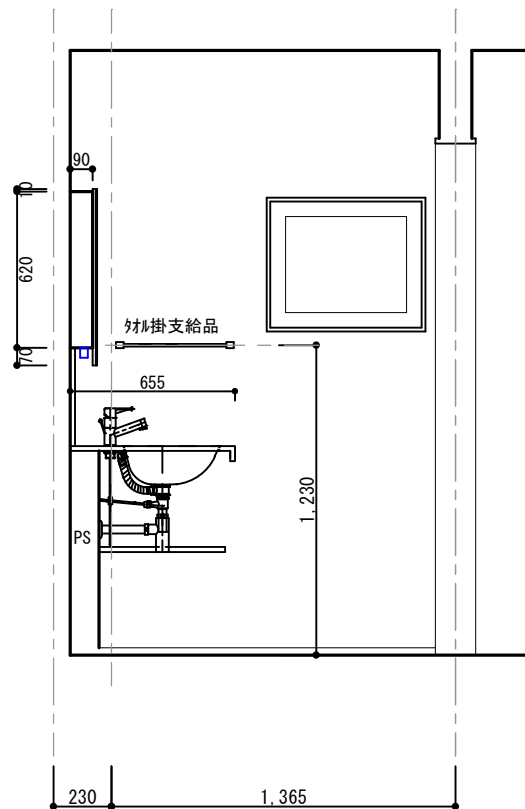


洗面 東

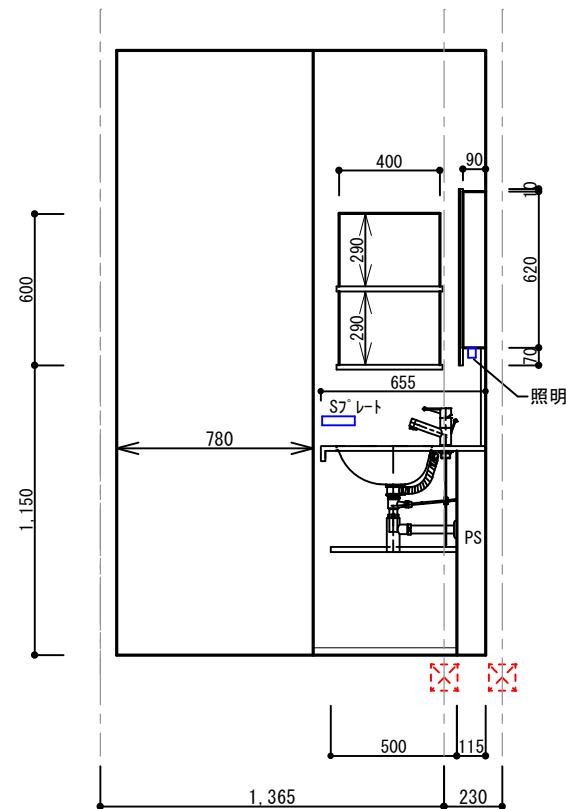


洗面 西

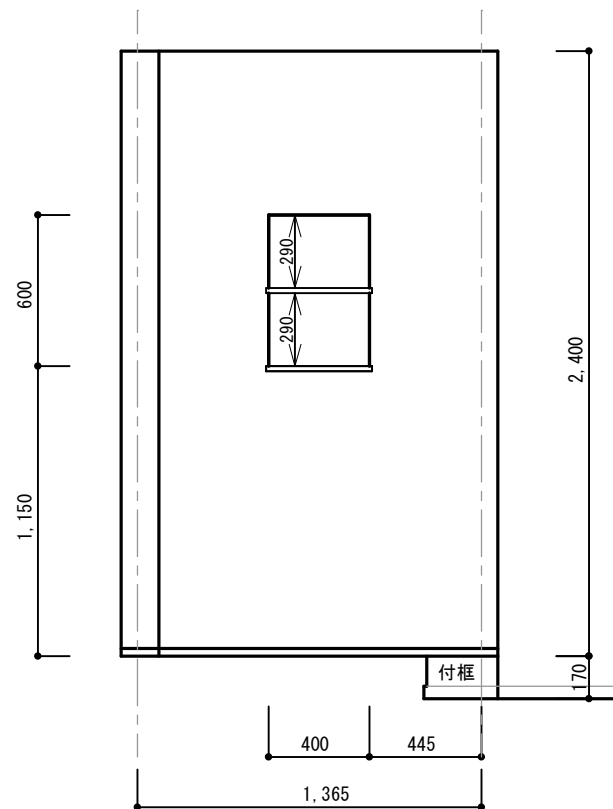

玄関 東

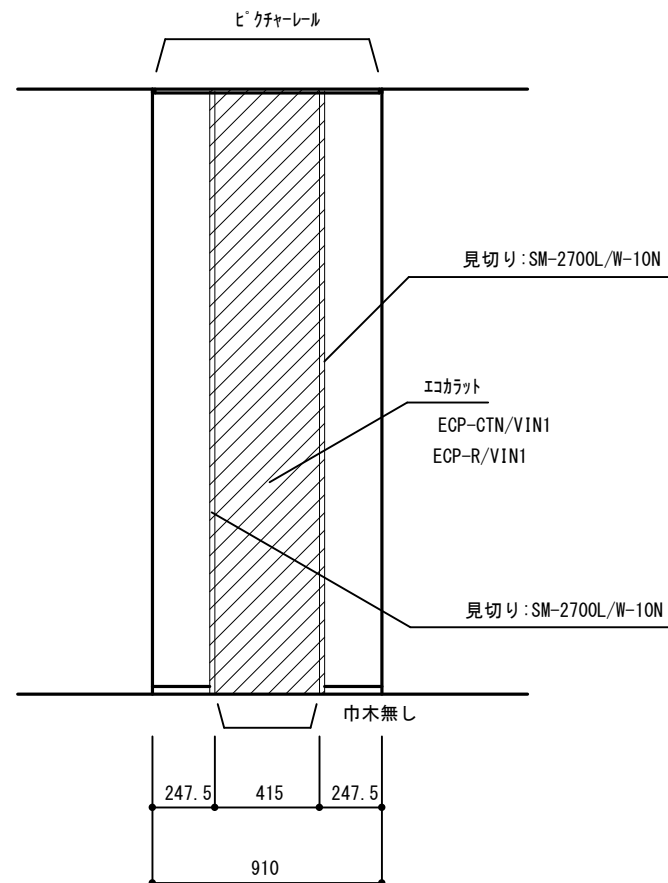

ホ-ル① 南面

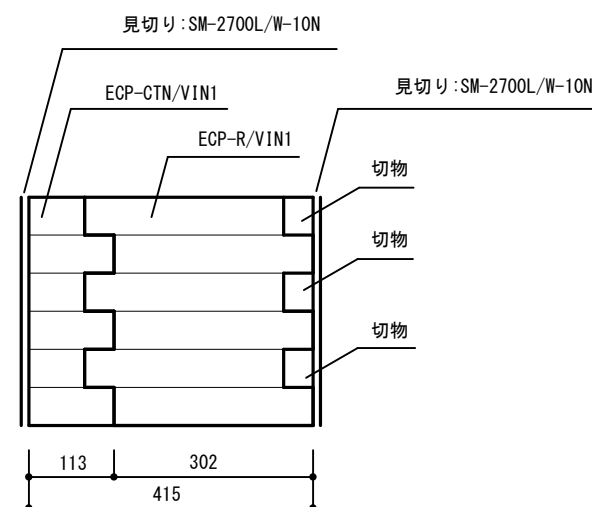

エコラット 納まり

決定図

訂正	浜岡一級総合設計事務所 一級建築士事務所 静岡県知事登録第 (10)2441 号 一級建築士 大臣登録第 365879 号 西原利昌	LIFEFUND PG HOUSE	株式会社 LIFEFUND InDesign office 一級建築士事務所 事務所登録 (2) 第7595号 一級建築士登録 第179770号 鈴木 達男 〒432-8023 静岡県浜松市中央区鴨江3丁目70番23号	年月日 2025.5.25 縮尺 1/50	件名 石原章弘様 邸新築工事 図名 展開図		設計 酒井	IC	工事 青島	図番 6-1
----	--	----------------------	---	--------------------------------	--------------------------------	--	----------	----	----------	-----------