


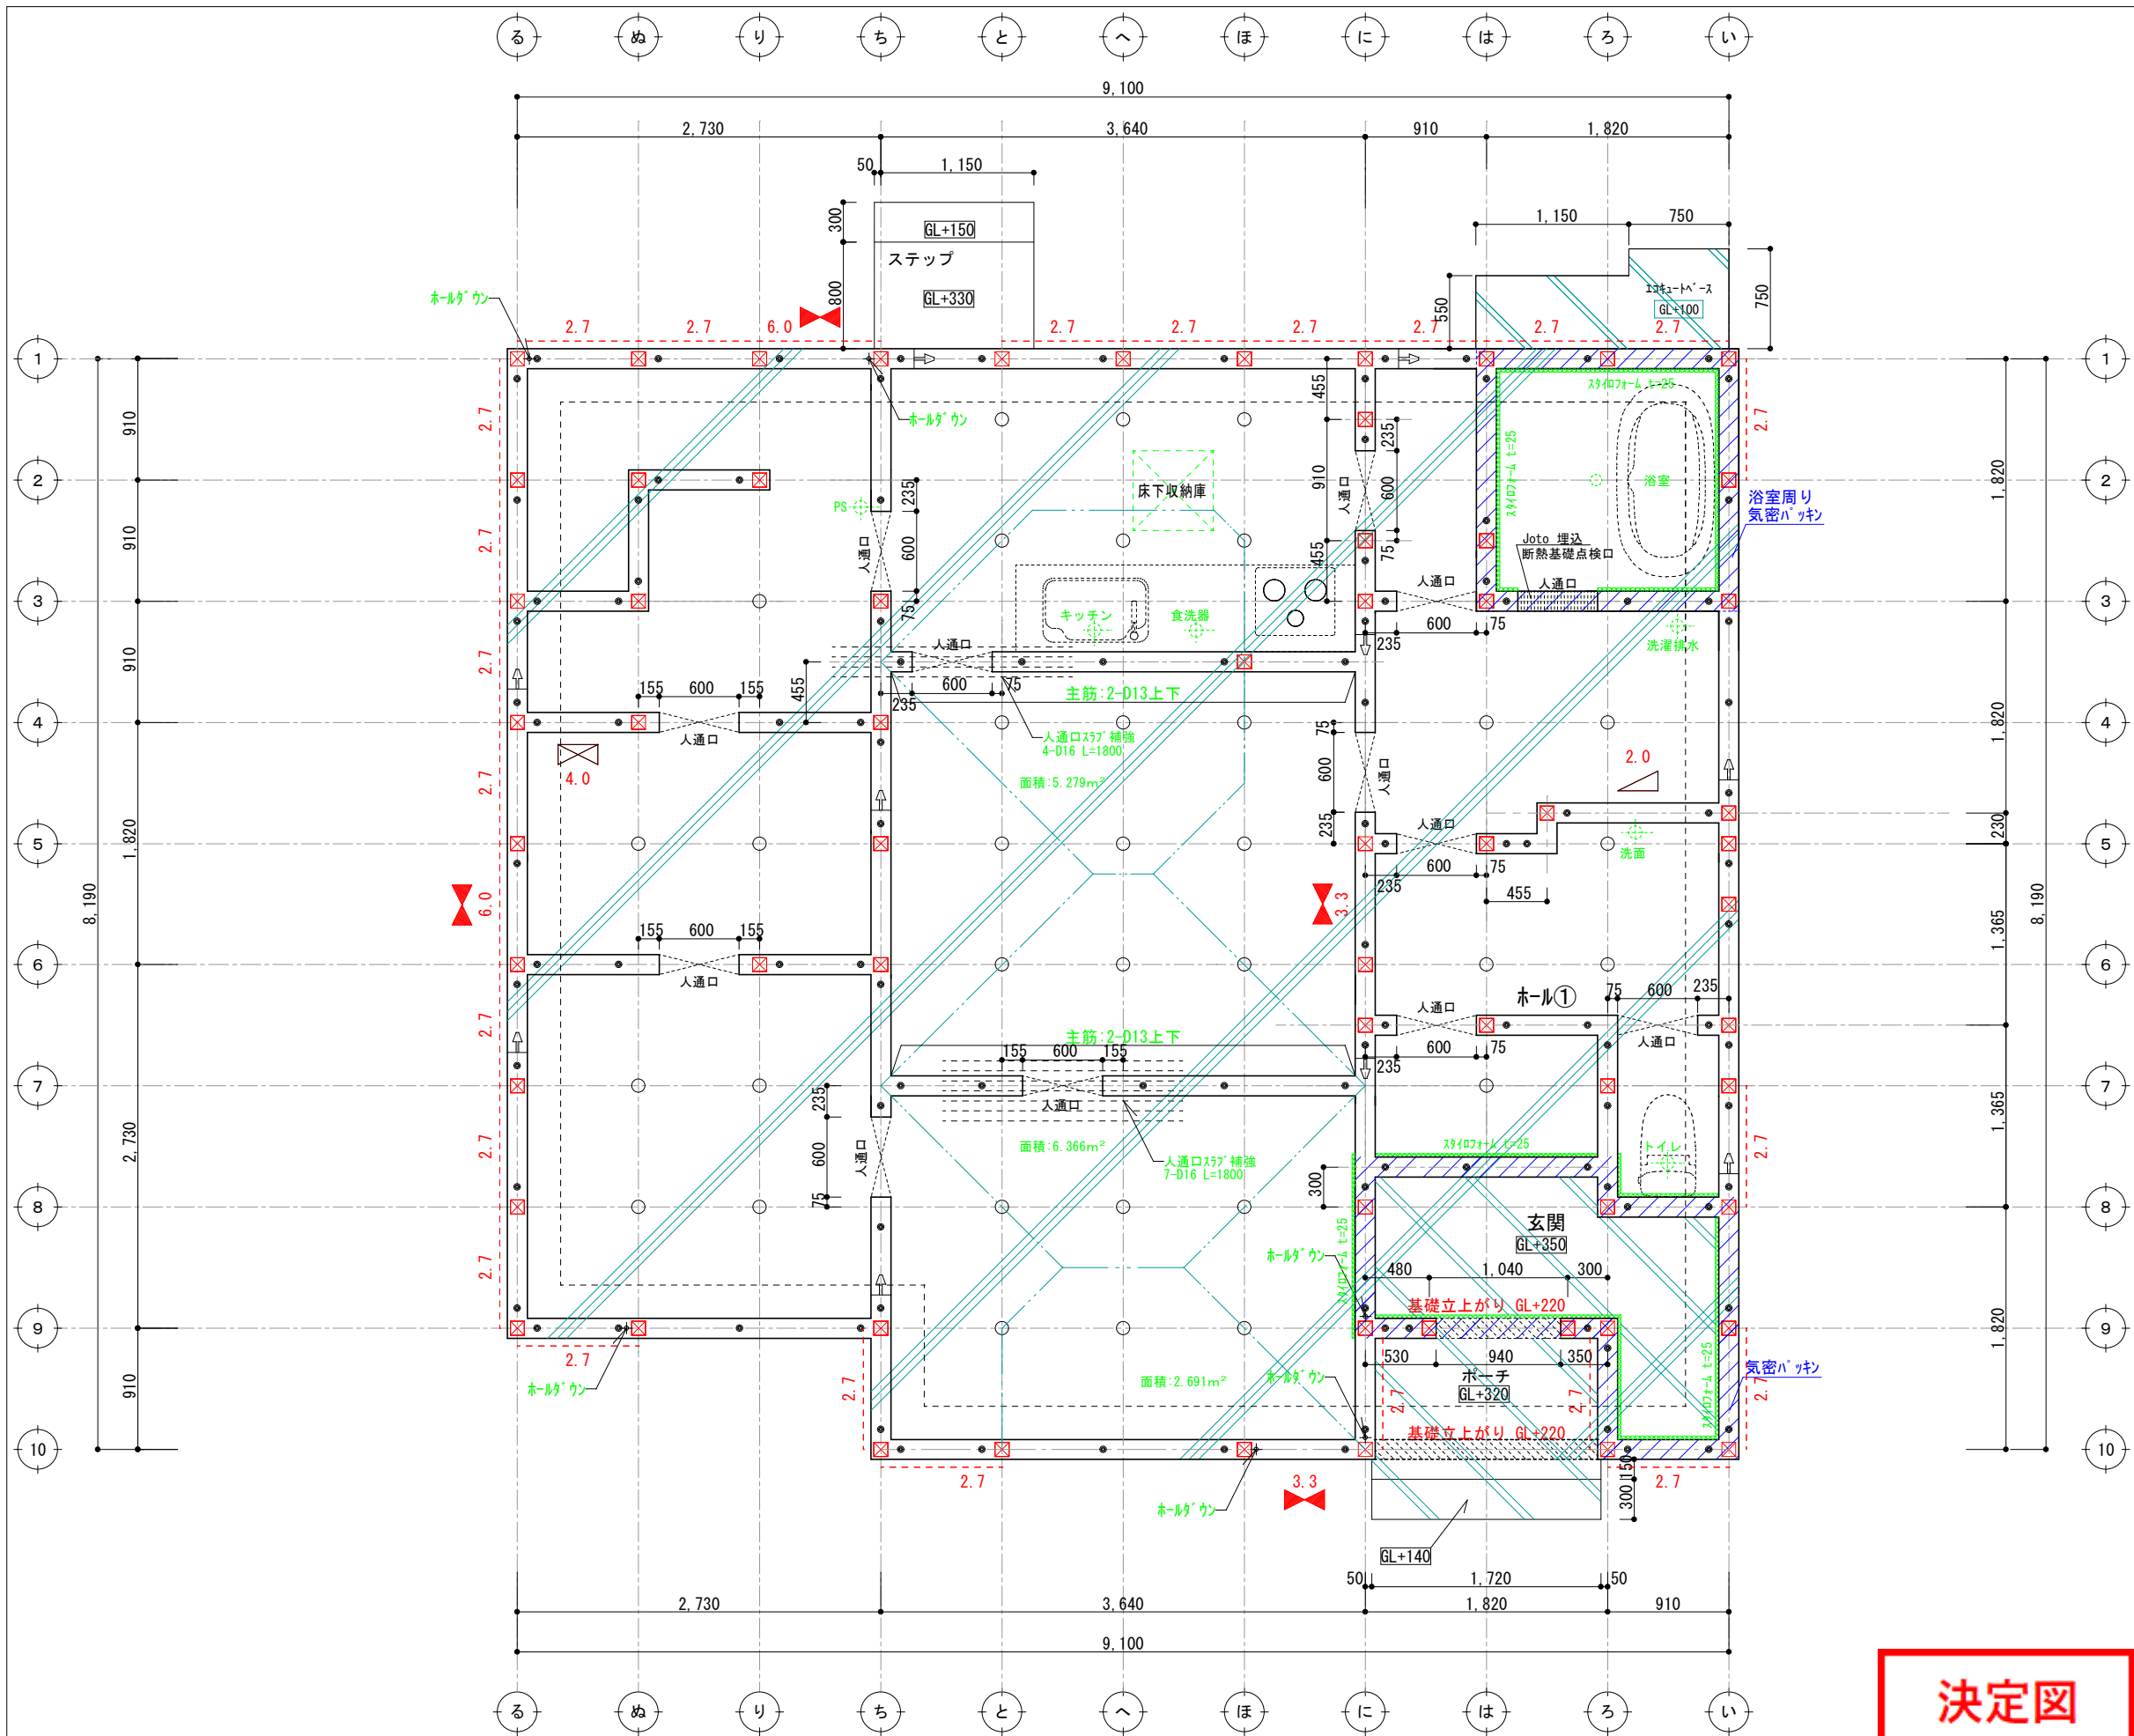

構造体ベースコンクリート t=150


後打ち土間コン

アンカーボルトの配置

- 土台切れの箇所より150mm
- 土台の継手及び仕口の端部より150mm
- 耐力壁の端部、筋交いの脚部より150mm
- 1.82m以下の間隔
- 250mm以上埋込み
- 基礎天端より120mm

筋かい凡例

- 柱脚 柱頭 片筋かい
- たすき掛け筋かい
- 構造用合板

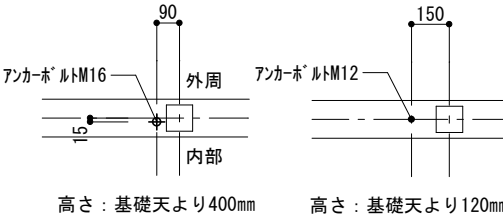

高さ：基礎天より400mm

高さ：基礎天より120mm

ホールダウン用アンカーボルト配置

アンカーボルト配置

凡例

通し柱 (105*105) 管柱 (105*105)

● アンカーボルトM12 L=400

+ ホールダウンアンカーM16 L=800

柱芯より90mm 280mm以上埋め込み

(カナイフリストアンカーボルトM16)

⊕ 鋼製束

土台ジョイント

ベースコンクリート (t=150)

後打ちコンクリート

基礎伏図について特記なき場合に限り下記による。

1. コンクリート：呼び強度 21N/mm²
2. 鉄筋：SD295A
3. 設計地耐力：fe=20kN/m²
地耐力計測後、不足の場合は相当の改良を行い、満たすものとする。
4. 基礎の位置は、芯振分けとする。
5. 玄関・S/C・UB周囲の基礎天端は気密パッキン施工 (網掛け部) とし、その他の基礎天端は基礎パッキン施工とする。
6. 設備配管の屋内への取り入れは基礎立上り部のスリーブによる。

決定図

訂正	浜岡一級総合設計事務所 一級建築士事務所 静岡県知事登録第 (10)2441 号 一級建築士 大臣登録第 365879 号 西原利昌	LIFEFUND PG HOUSE	株式会社 LIFEFUND InDesign office 一級建築士事務所 事務所登録 (2) 第7595号 一級建築士登録 第179770号 鈴木 達男 〒432-8023 静岡県浜松市中央区鴨江3丁目70番23号	年月日 2024.5.25 縮尺 1/50	件名 石原章弘様 邸新築工事 図名 基礎伏図	設計 酒井 IC 工事 青島 図番 B-1
----	--	----------------------	---	--------------------------------	---------------------------------	---