
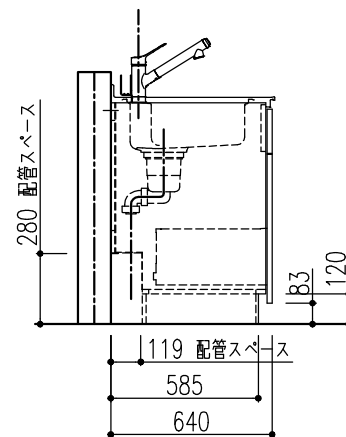
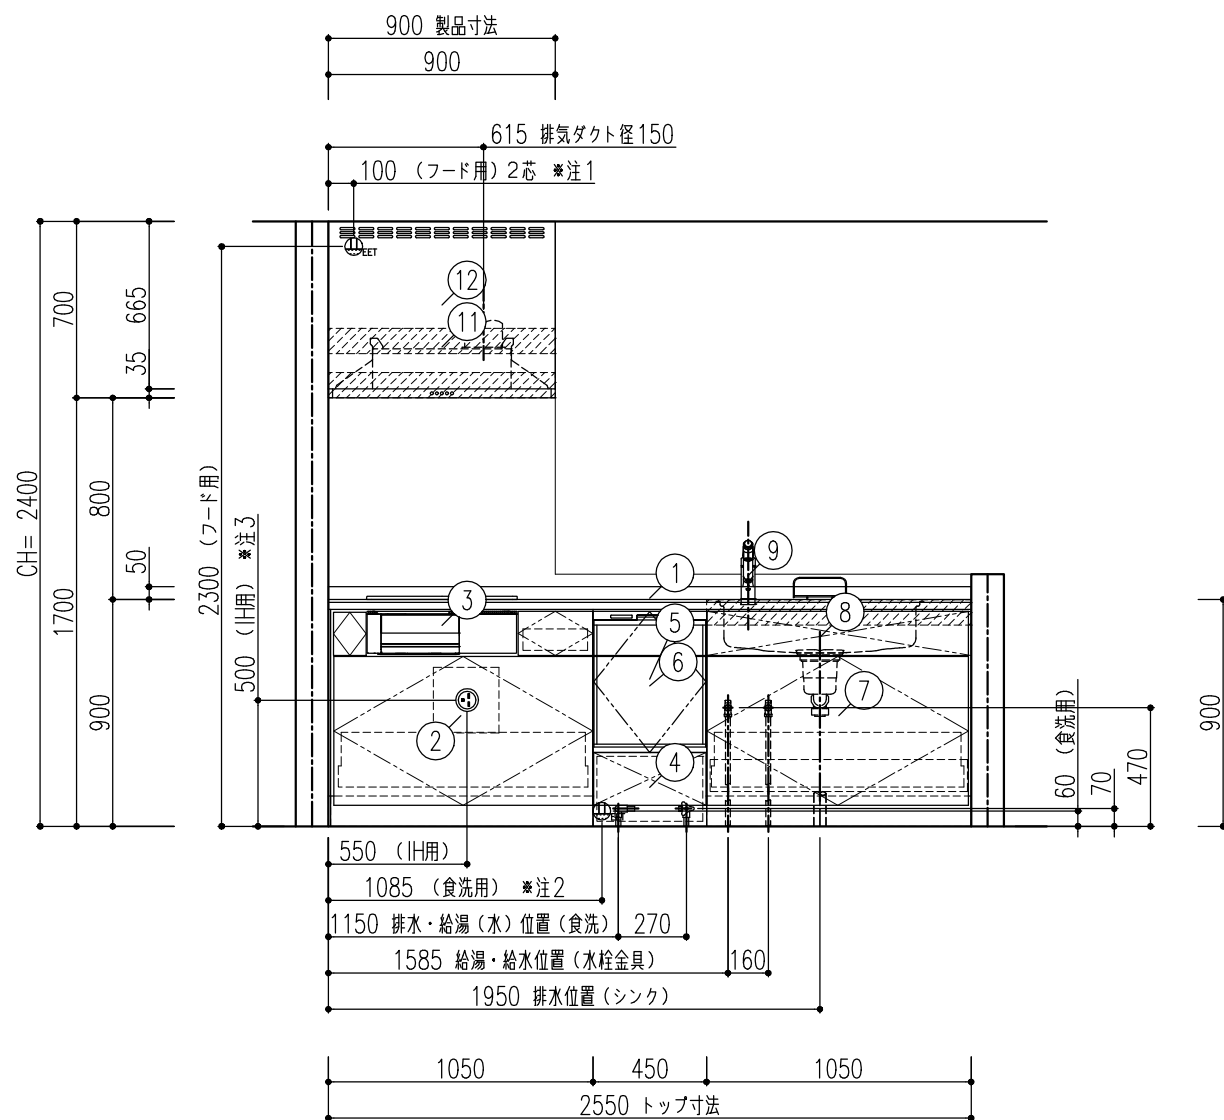


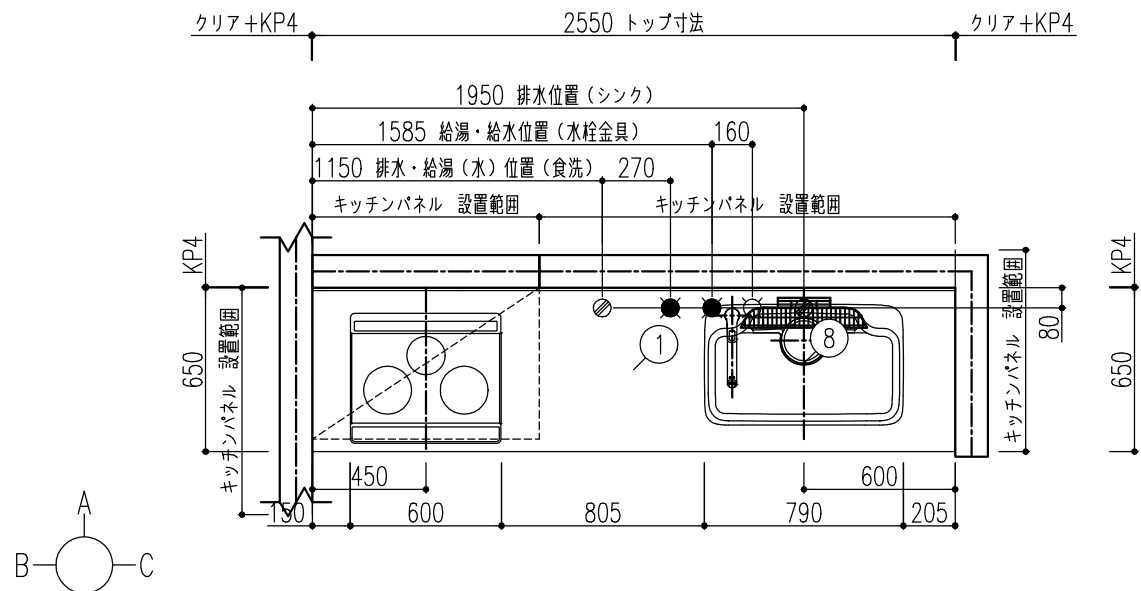

【ご注意】

- 壁面仕上材（キッチンパネル・タイルなど）の貼付下端位置が変わります。〔機能図参照〕
- 記載のキャビネット寸法は扉前面までの呼び寸法です。キャビネット本体の寸法・扉厚み等は商品ガイドの巻末資料をご確認ください。
- 記載のワークトップ、カウンター、エンドパネル、サイドパネルの寸法は呼び寸法です。詳細寸法は商品ガイドの巻末資料をご確認ください。
- レンジフード電源プラグ仕様：2芯電源プラグ（アース工事が必要です。）

[illegible]

注1) 125V・15A 2極接地極付アースターミナル付コンセント 【専用】(フード用)

注2) 125V・15A 2極接地極付アースターミナル付コンセント側板取付【専用】

注3) 250V・30A 2極接地極付コンセント 【専用】

【 ご注意 】

●壁面仕上材（キッチンパネル・タイルなど）の貼付下端位置が変わります。 [機能図参照]

●記載のキャビネット寸法は扉前面までの呼び寸法です。キャビネット本体の寸法・壁厚等は商品ガイドの巻末資料をご確認ください。

●記章のワークトップ、カウンター、エンドパネル、サイドパネルの寸法は呼び寸法です。詳細寸法は商品ガイドの参考資料をご確認ください。

●電気・ガス・給排水・換気等は法令・規定に従って有資格者が行ってください。

●水道工事は排水配管工事となります。

●取付・設置に際し、各製品の取付・設置説明書や図面の機能図を必ずお読み下さい。

●内線規程上、各機器のプラグ仕様に問わず建築側には接地極付コンセントを推奨しています。

●レンジフードにはアース線は同梱されておりません。別途 御用意願います。


●レンジフード電源プラグ仕様：2芯電源プラグ（アース工事がが必要です。）

●食洗機内配管の詳細については必ず別添の機能図をご確認ください。


●食器洗い乾燥機配管は、給水接続か給湯接続かお客様に確認したうえで施工願います。

	特記事項 扉色 VK5:グレージュスタック 取手 [M]スリム取手（ブラック） ワークトップカラー 【DW】ソルティホワイト	物件名	石原章弘 様邸	案件No.	図面名	担当	図面	図番 : 株式会社 LIXIL
				A2502DDD0EEKHS	納まり図	栗野 友仁		
		仕様	ES21	見積No.	縮尺	日付		
				M25026646745-005-2	1/30	2025.04.07		

B面

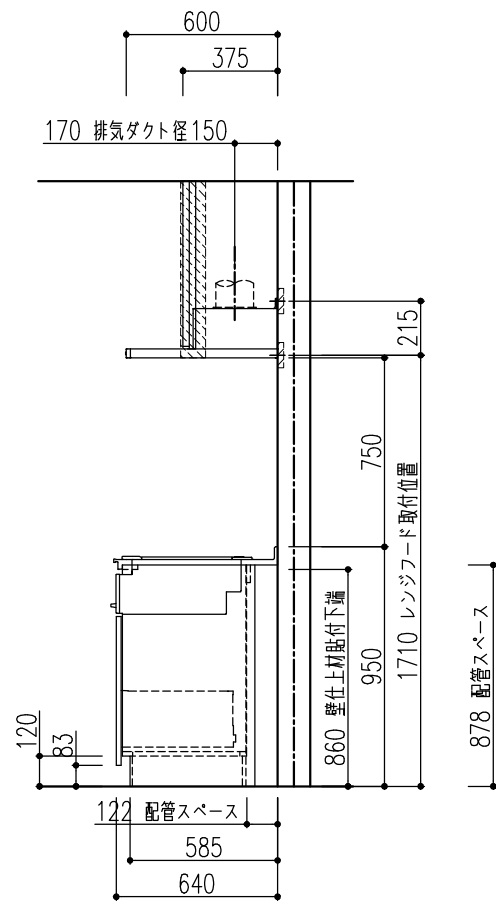

C面

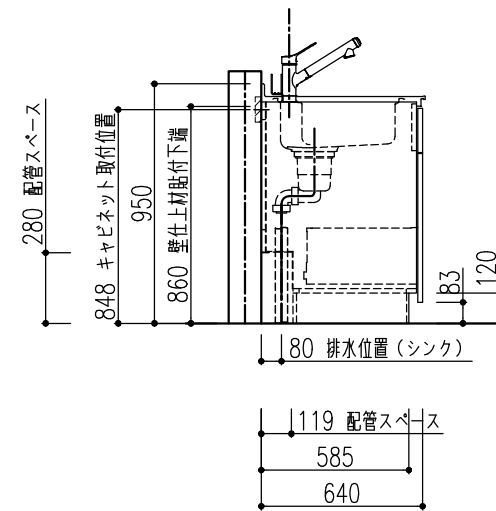


	特記事項 扉色 VK5:グレージュスタック 取手 [M]スリム取手 (ブラック) ワークトップカラー 【DW】 ソルティホワイト	物件名	石原章弘 様邸	案件No.	図面名	担当	図面	図番
				A2502DDD0EEKHS	納まり図	栗野 友仁		株式会社 LIXIL
		仕様	ES21	見積No.	縮尺	日付		
				M25026646745-005-2	1/30	2025.04.07		

■壁面仕上材（キッチンパネル）取付注意事項〔貼付向き〕

●キッチンパネルの貼付向き


キッチンパネルの貼付向きにご注意ください。

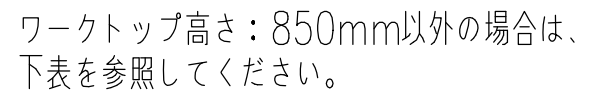

ワークトップ高さ	キッチンパネル 貼付下端位置
900	860
875	835
825	785
800	760

●上表はキッチンパネルの場合です。ステンレスパネルの場合は、キッチンパネルの「取付・設置説明書」を参照してください。

《ワークトップ高さ：850mmの場合》

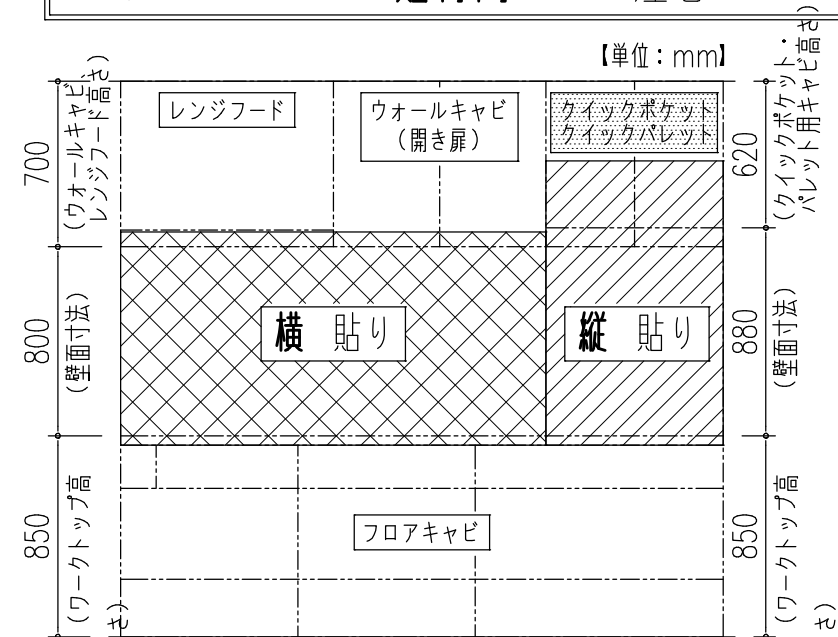

《キッチンパネル 貼付方向》
総高さ：2350mmの場合

	ウォールキャビ		
	開き扉		クイックボケット クイックパレット
	H700	H600 H500	H700 (620) H600 (520)
キッチンパネル 貼付方向	横	縦	

【ご注意】
リシエル以外のクイックパレットは、
キャビネットの背板高さがショート
（-80mm）しておりませんので、
『開き扉』のキッチンパネル貼付方向
に合せてください。


《バックガード：なし、ワークトップ高さ：850mm、ウォールキャビ高さ：700mmの場合》

■レンジフード取付注意事項（壁面取付時）

レンジフードを取付ける場合は下地の桟が厚み30mm以上、幅100mm以上、ビス固定位置が桟の端部から25mm以上であることを確認してください。



また、壁強度などの詳細は「レンジフード設置説明書」を必ず事前に確認してください。

取付位置については、取付設置図を確認してください。

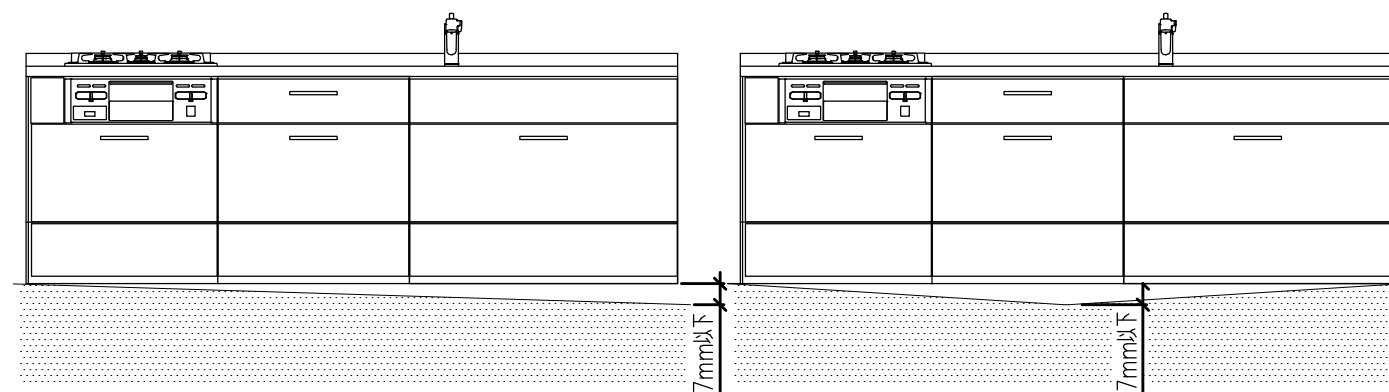


床の不陸は、7 mm 以下に抑えるようにしてください。不陸が大きい場合は、現場責任者に床の修正を依頼してください。

※キャビネット取付時には不陸調整スペーサー等で水平になるように設置してください。

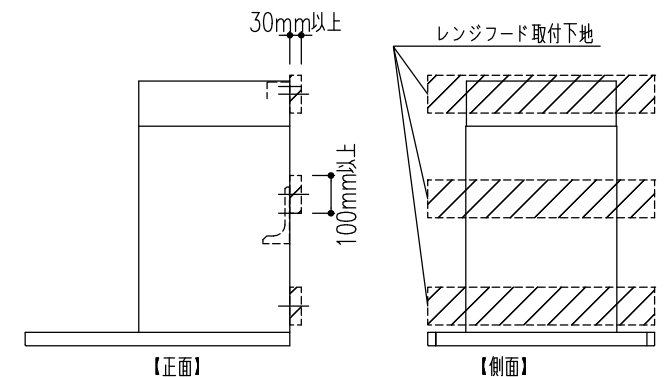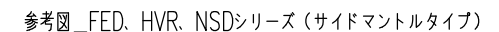


参考図 NBHシリーズ

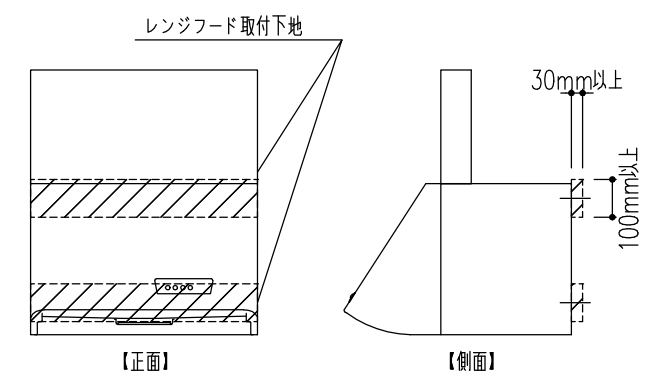

特記事項 扉色 VK5:グレージュスタック 取手 [M]スリム取手 (ブラック) ワークトップカラー 【DW】ソルティホワイト	物件名	石原章弘 様邸	案件No.	図面名	担当	図面	図番 : 株式会社 LIXIL
			A2502DDD0EEKHS	機能図	栗野 友仁		
	仕様	ES21	見積No.	縮尺	日付		
			M25026646745-005-2		2025.04.07		

■ASRフード

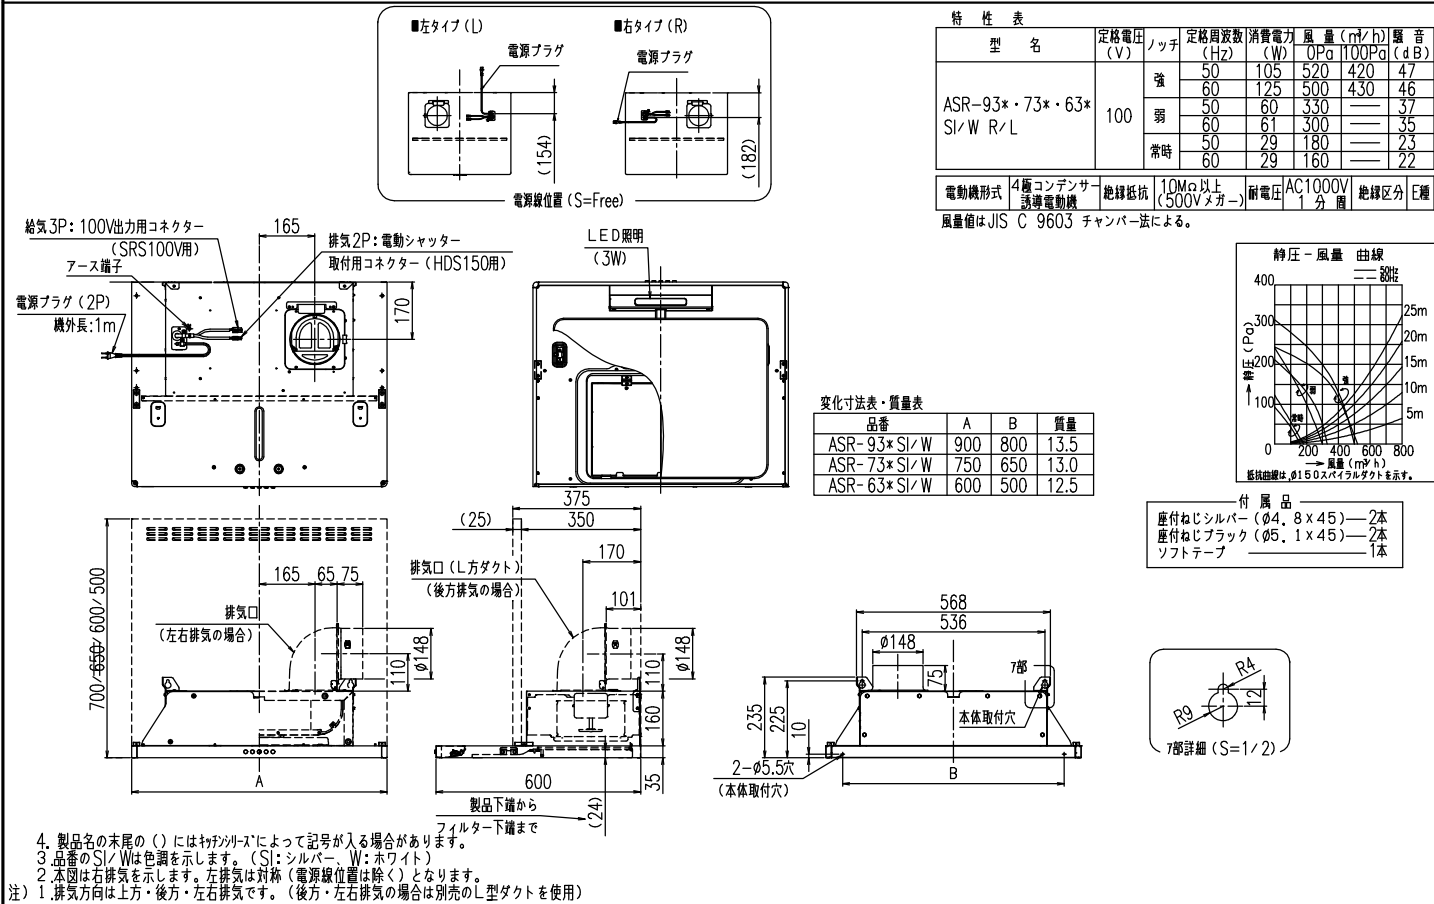


■IHヒーター用コンセント推奨位置図 / 壁付設置の場合

※コンセントや電源プラグが、引き出しおよびIHヒーター用仕切板 (オプション) に接触しないように注意してください。


※木製キャビネットの配管スペース付キャビネットを使用する場合は、点検口裏の配管スペース内にコンセントを設置してください。

キッチン高さ	電源線高さ
800	400
850	450
900	500

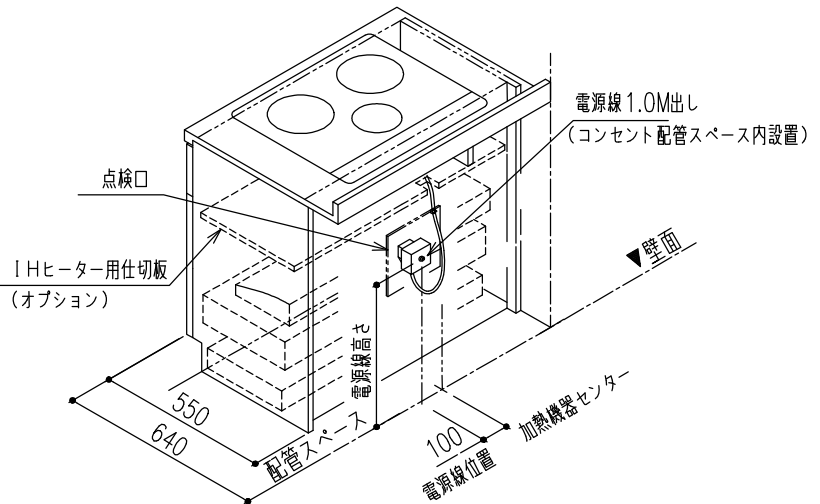

注意: 引き出しおよびIHヒーター用仕切板 (オプション) に接触しないように上記寸法を参照してください。


■食器洗い乾燥機内配管図 床立上げ配管例

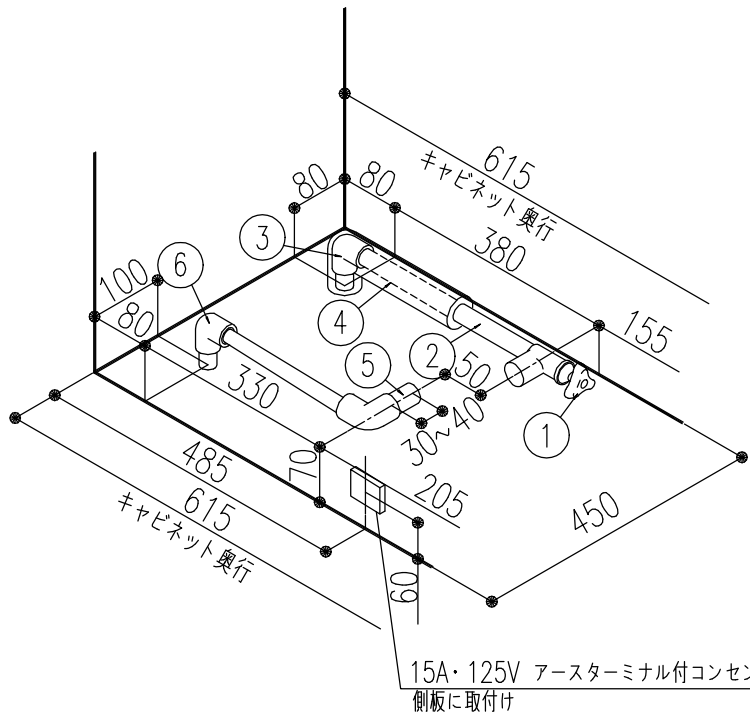

■止水栓図 (床立上げ)


床立上げ配管



配管立ち上げ寸法は、止水栓芯までの高さを示しています。

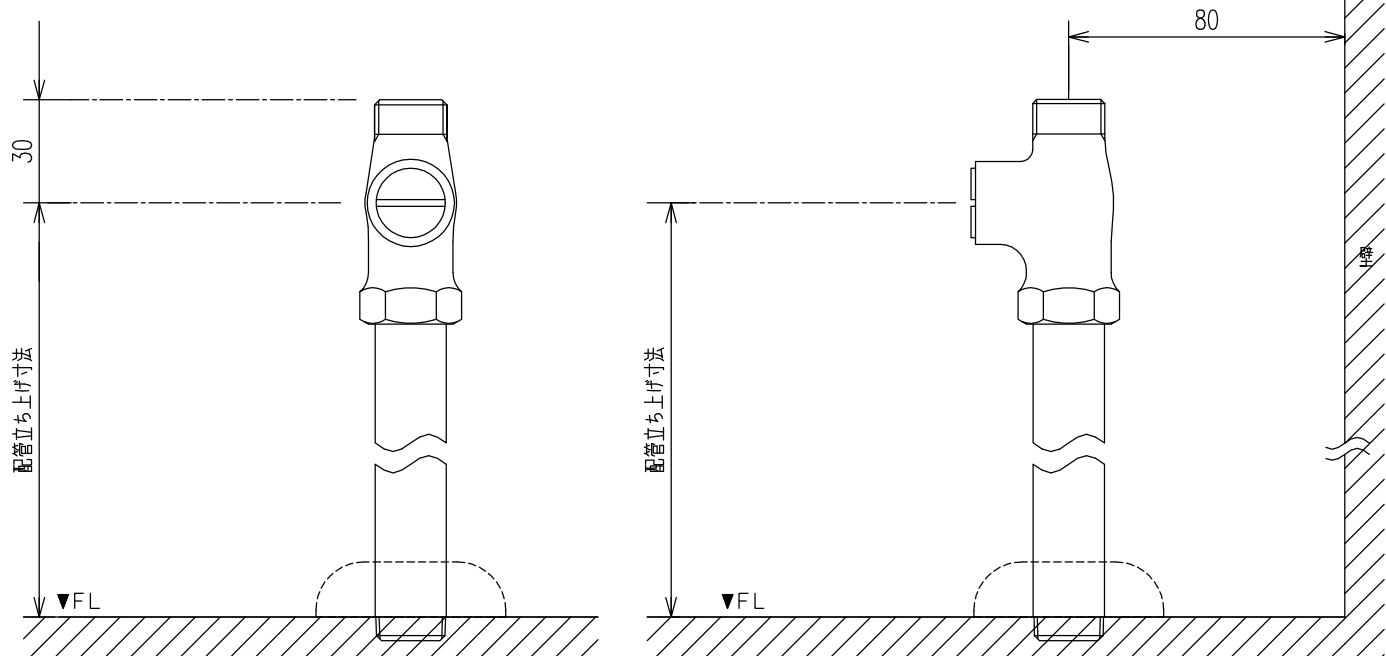

■ キッチン取付者さま向け 動画コンテンツ ■

商品取付けの注意点を2次元コードでご視聴いただけます。
取付日より前に、是非ご確認ください。

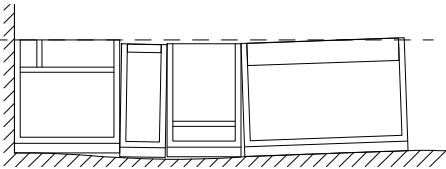荷扱い・搬入	カウンター開梱搬入「養生ツール」	不陸の確認と調整	マグネットキッチンパネル
荷扱い・搬入	カウンター開梱搬入 「養生ツール」のご紹介		マグネット キッチンパネル 「取付・設置」ポイント
作成日：2024年10月01日	作成日：2024年10月01日	作成日：2024年02月07日	作成日：2024年03月06日




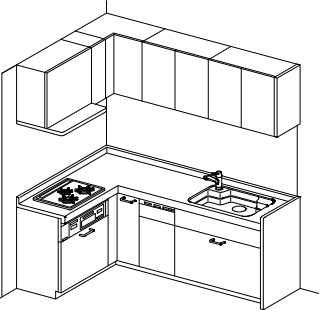
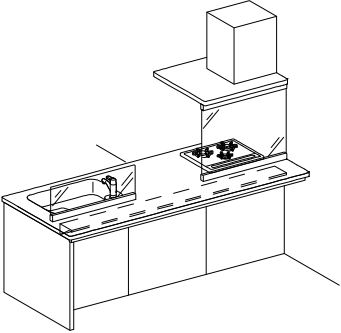
人造大理石カウンターL型キッチン	センターキッチン（ペニンシュラ型）		
			
作成日：2024年02月07日	作成日：2024年02月07日		

--	--	--	--

特記事項 扉色 VK5:グレージュスタック 取手 [M]スリム取手 (ブラック) ワークトップカラー 【DW】ソルティホワイト	物件名	石原章弘 様邸	案件No.	図面名	担当	図面	図番
	仕様	ES21	A2502DDD0EEKHS	機能図	栗野 友仁		株式会社 LIXIL
			見積No.	縮尺	日付		
			M25026646745-005-2		2025.04.07		

■ キッチン取付者さま向け 動画コンテンツ ■

商品取付けの注意点を2次元コードでご視聴いただけます。
取付日より前に、是非ご確認ください。

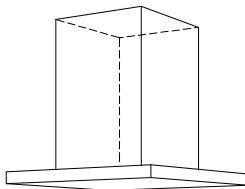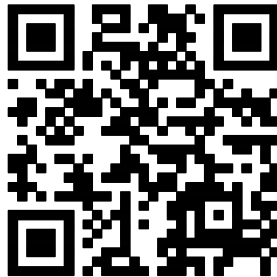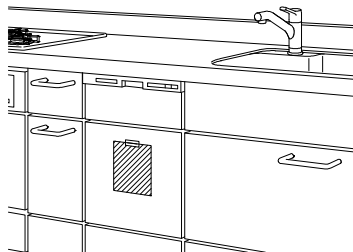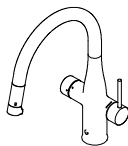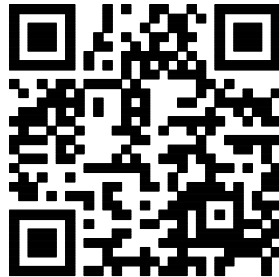センターフード型レンジフード (天吊りフード)  作成日：2024年06月03日 		I H加熱機器関連 I H加熱機器 仕切り板 作成日：2024年02月07日 		食器洗い乾燥機  作成日：2024年02月07日 		ミネラル浄水栓 Greentap  作成日：2024年06月03日 			
	特記事項 扉色 VK5:グレージュスタック 取手 [M]スリム取手 (ブラック) ワークトップカラー 【DW】ソルティホワイト	物件名 ES21 仕様	石原章弘 様邸		案件No.	図面名	担当	図面	図番
					A2502DDD0EEKHS	機能図	栗野 友仁		株式会社 LIXIL
					見積No.	縮尺	日付		
					M25026646745-005-2		2025.04.07		