
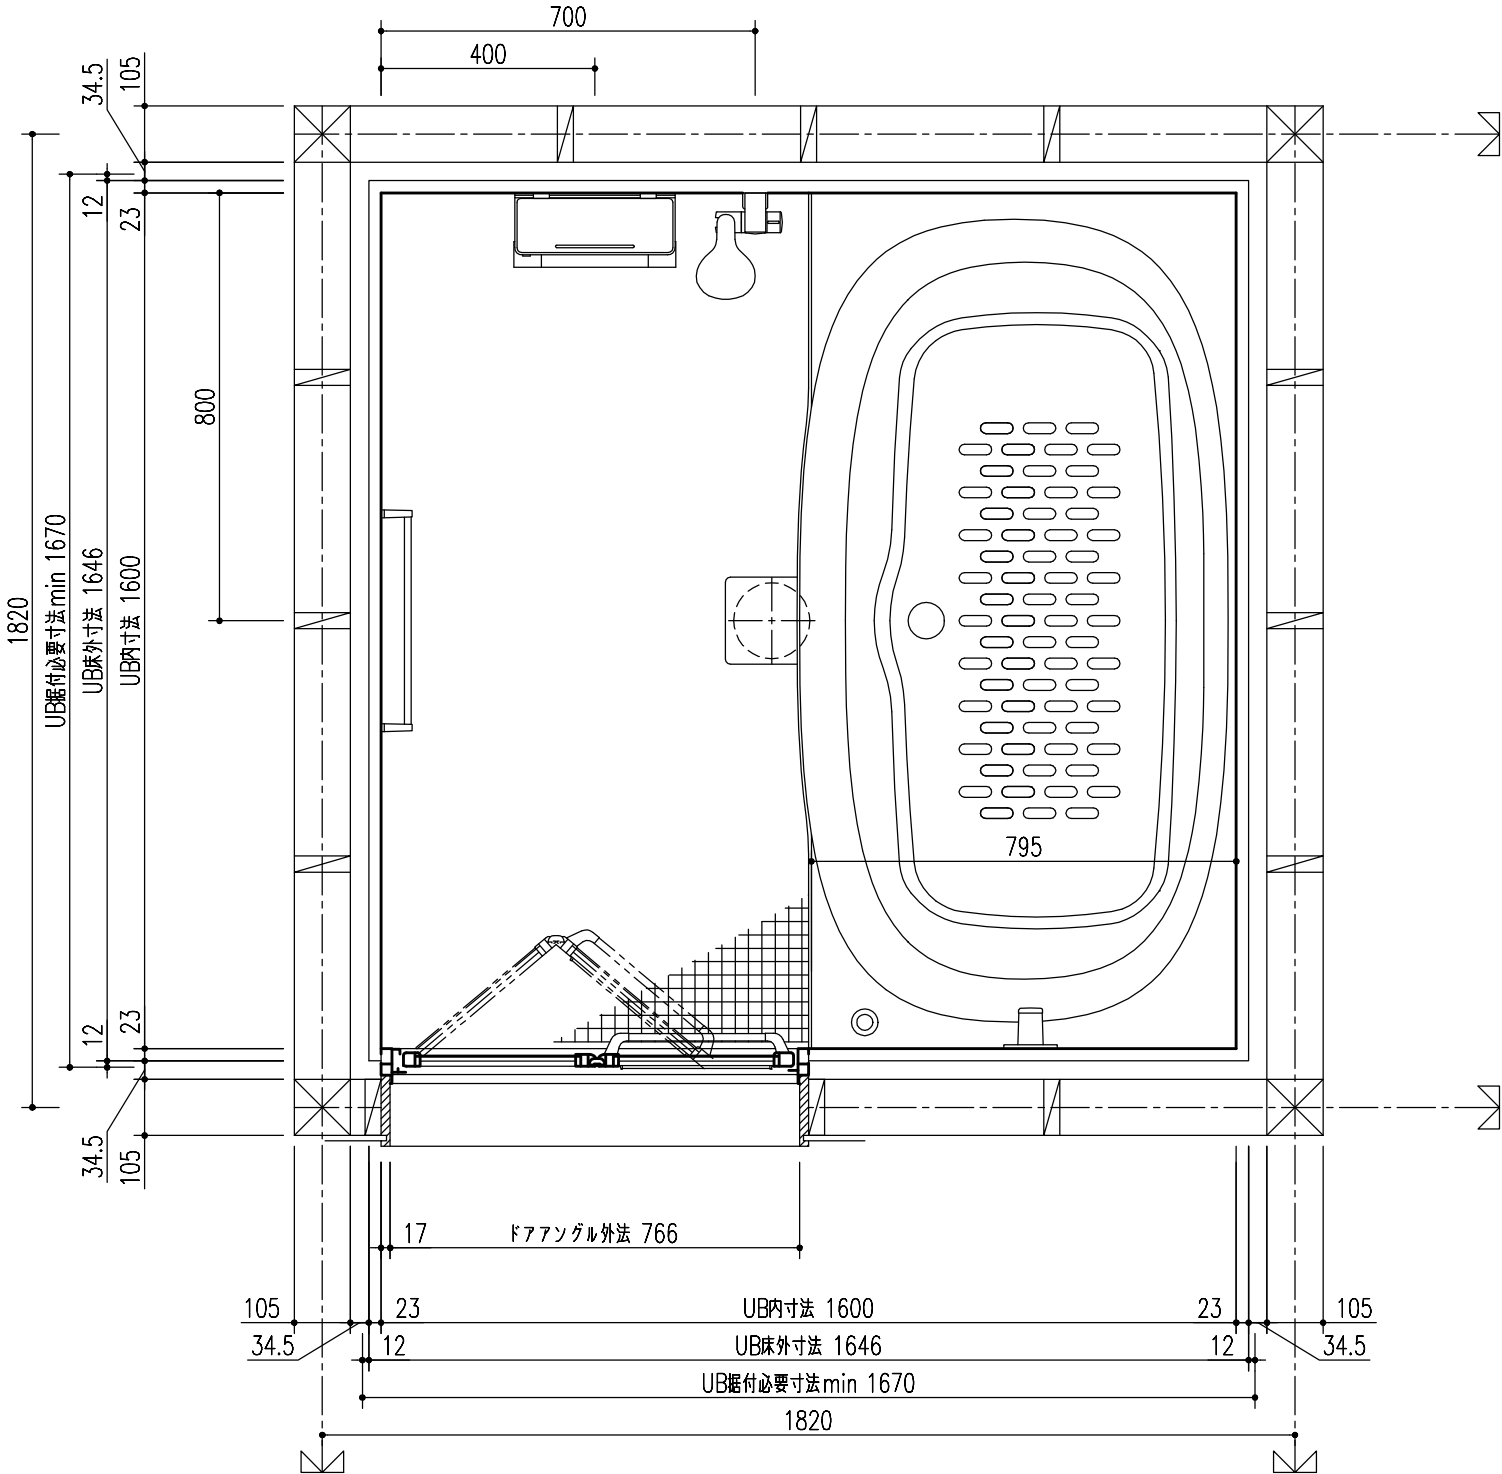


BMUS-1616LBZ-B


部位／項目	仕様（寸法単位：mm）	備考（色柄・品番等）	壁穴加工
床	FRP 単色 バックくるりんボイ排水口	U61	
壁	アクセントパネル(器具面):Lパネル(ハイクラス) ベースパネル:Lパネル(ベーシッククラス)	HN987,LE301	
天井	化粧鋼板複合パネル	UE103	
ドア	折り戸:アルミアルマイト処理(キレイドア) 面 材:型板調樹脂板	VDY-8002006L(81)/WM	
浴槽	FRP ミナモ浴槽(浴槽内法 1501W×802D×480H) プッシュフソウェイ排水栓(メタル調) サーモバスS(浴槽保温材・薄型保温2枚組蓋<ホワイト>) マグネット組蓋フック<ホワイト> エプロン<ホワイト>	NW1	
水栓金具	洗い場側:壁付サーモ水栓(LS)<ホワイト> シャワー:エコアクアシャワー<メタル調-ホワイト> メタル調ホース	BF-BD147TX-J12PU/FW1 BF-SL6BG(1.7)-PU/FW1	
シャワーホースフック	マグネットシャワーホースホルダー<グレー>	SHH-4/N55	
照明	パネルダウンライト(防湿型) 電球色LED 2灯	LE-D1-10A(1.3M)/1L	
タオル掛	アルミパイプ L400 ブラケット:樹脂製	TB-400E-K	現場開口
鏡	防湿型化粧鏡 300W×600H	KGM-3060(1)S	
収納	マグネットシェルフ 300W<ホワイト> ※強度上、ポンプボトルのポンプを棚上で押さないでください。	NT-300A(2)-1S/FW1	
スライドバー	スライドバー<ホワイト> L800	BF-27B(800)-PU3	現場開口
換気扇	天井換気扇 アルミダクトホース付	UF-27A	
給水管	PJ1/2 おねじ止		
給湯管	PJ1/2 おねじ止		
雑排水管	塩ビ管 VU50		
追いだき	浴槽穴加工φ50 水受けトレイ付		
窓	フリーサイズ窓額縁キット 窓開口補強セット	R-1510P-24/W WR-122S	現場開口
保温仕様	洗い場床防水バン保温 床気密材セット トラップ保温 エプロン保温		

天井見上げ図

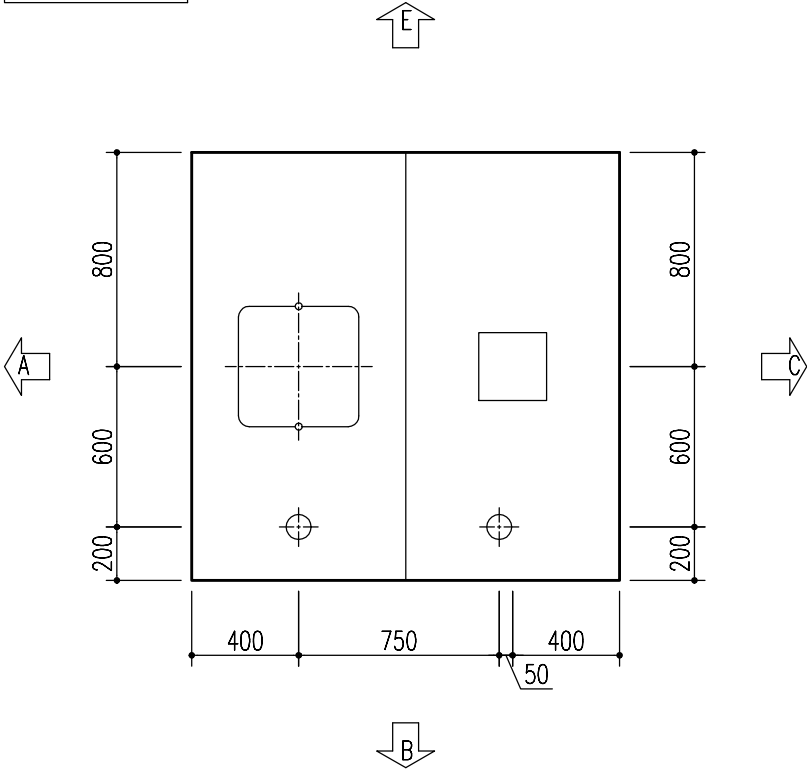

- ※ UB据付必要寸法はドア部の寸法を含みません。ドア部の寸法は詳細図のドア取合をご確認ください。
- ※ 取付ける機器により、UB据付必要寸法は異なります。
- 詳しくは、カタログの「工務店さまへ（取付け前の確認事項）」をご確認ください。
- ※ プラスオプションの追加マグネットアイテムは仕様図には表示されません。

特記事項	受領印	物件名	図面	担当	検図	図番
		石原章弘 様邸		栗野 友仁		日付 2025.04.07
		仕様図	縮尺	株式会社 LIXIL		
		BMUS-1616LBZ-B+H,LR				

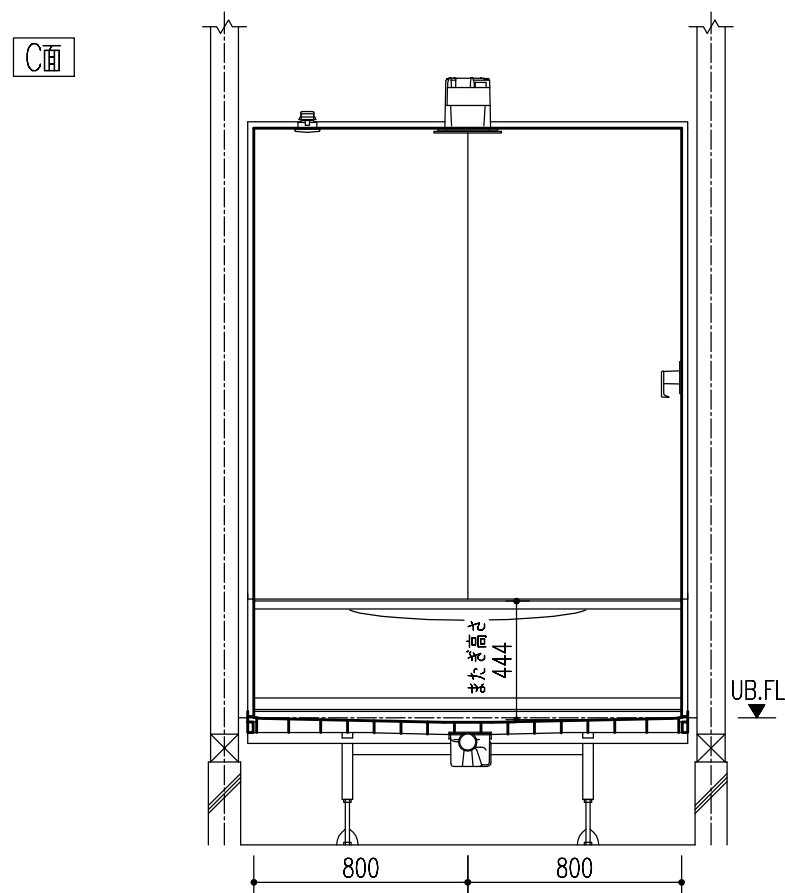

特記事項	受領印	物件名	石原章弘 様邸	図面	担当	検図	図番
		品名	仕様図 BMUS-1616LBZ-B+H,LR		栗野 友仁		日付 2025.04.07
				縮尺	株式会社 LIXIL		

配管接続部詳細図


配管の接続をスムーズに行うためにユニットバス取付前に下記の準備をお願いします。

(1)給水、給湯、排水の一次側は所定の位置に立ち上げておいてください。

(2)排水を脱衣室側(ドア下等)へ抜く場合は、基礎部に開口を設けるか、束構造にして排水管を抜いてください。



シャワーの種類により水栓金具の入口での必要給湯圧力が異なります。詳細はカタログを確認してください。

給水給湯配管立上げ位置 点検口止め

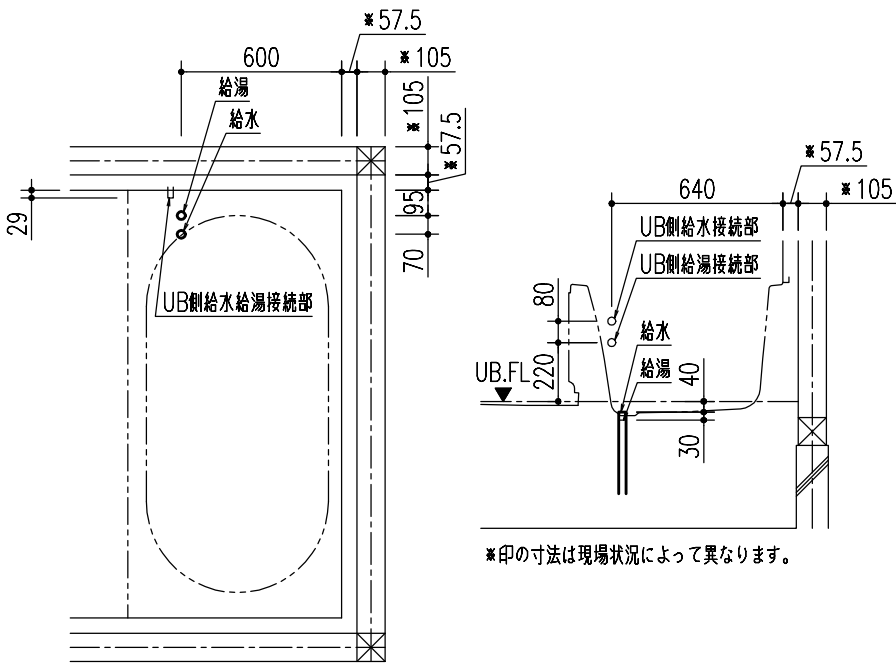

※印の寸法は現場状況によって異なります。

追いだき配管立上位置図

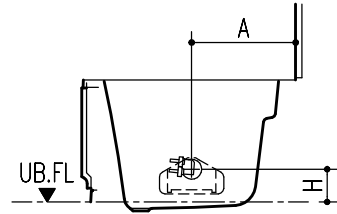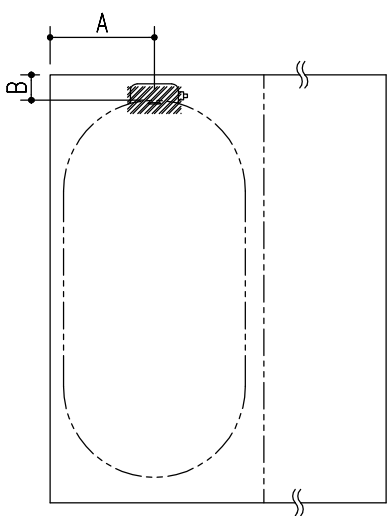



浴槽	A	B	H
ミナモトイド浴槽	506	231	113
1600フイド浴槽	589	247	113
1600ミナモ浴槽	374	231	113
1600エコベンチ浴槽	389	456	103
1600ストレートライン浴槽	369	252	113
1600ロング浴槽	355	194	113
1300ミナモ浴槽	384	132	113
1300ストレートライン浴槽	369	160	113
1200ミナモ浴槽	387	130	113
1150ミナモ浴槽	387	130	113

※図はR勝手の場合です。L勝手の場合は左右反転になります。

※追いだき循環アダプターは現場手配になります。



雑排水管

浴槽側の配管持出し位置・排水管立上位置は専用の配管キット(オプション)を使用した場合の位置です。

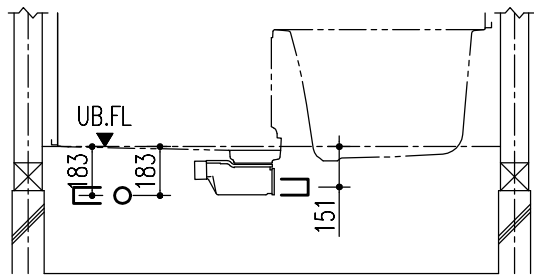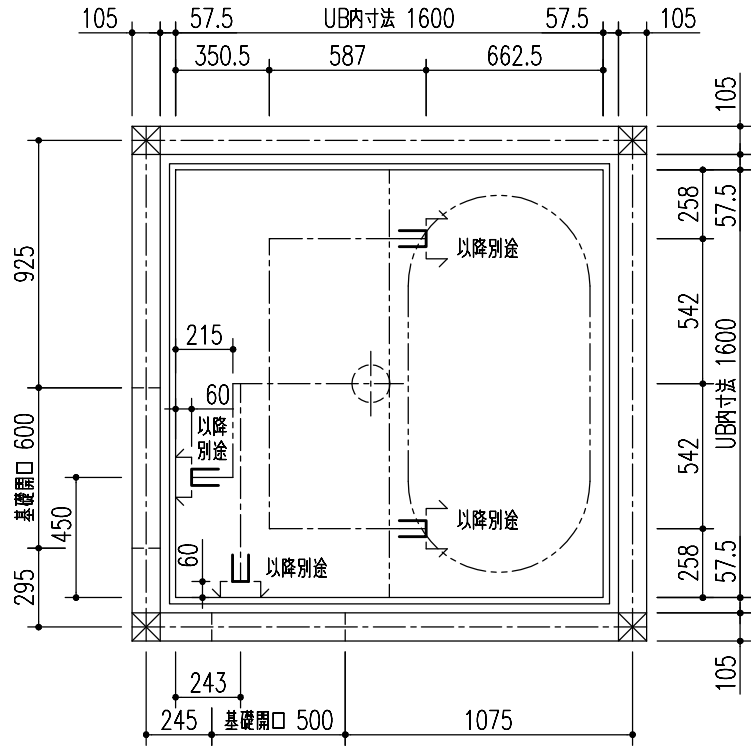

標準持出し位置


給水給湯接続部

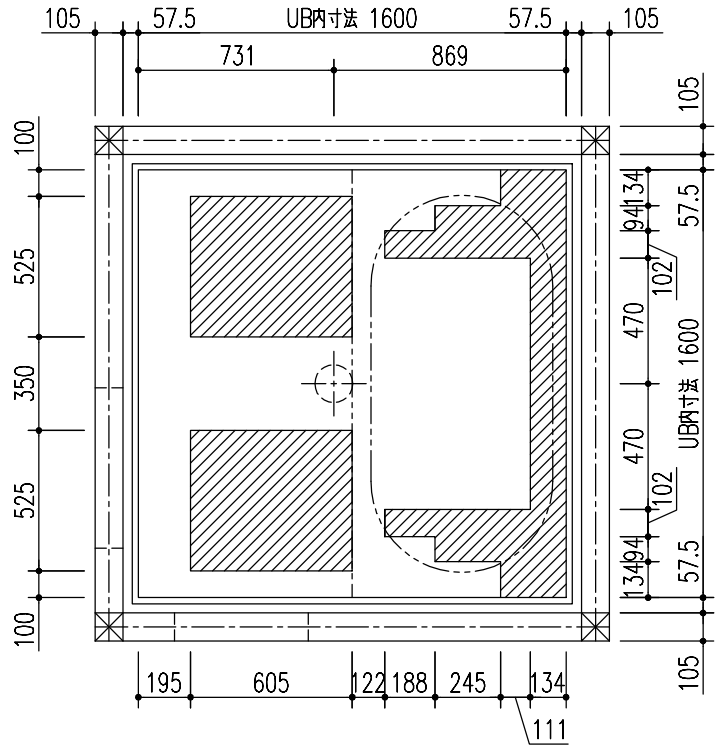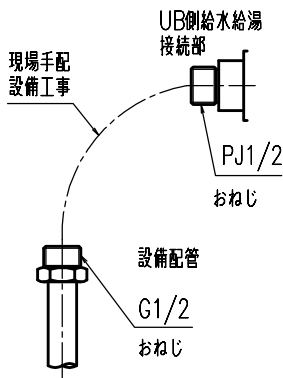

立上げ可能範囲

立上げ推奨位置

床支持位置

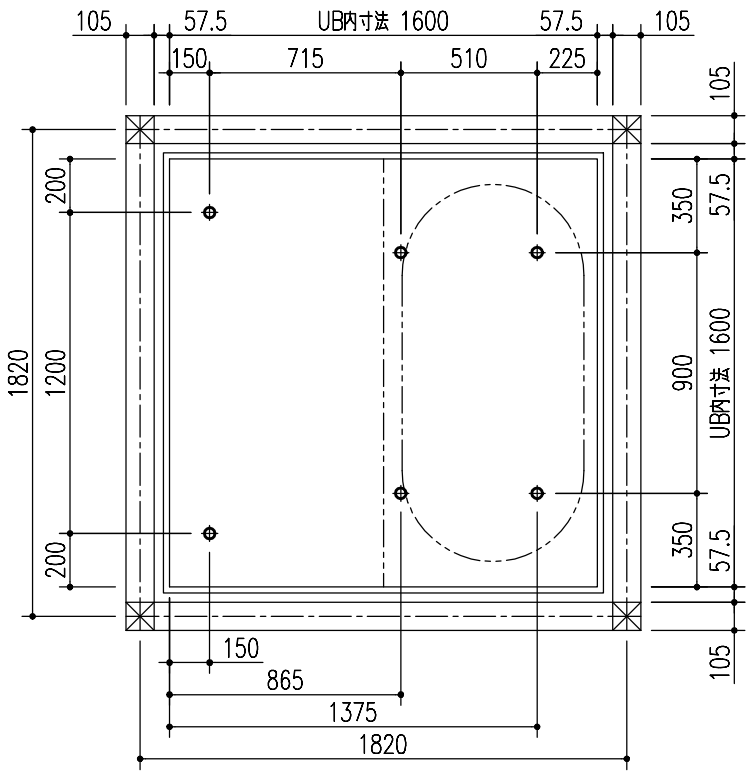

特記事項	受領印	物件名	石原章弘 様邸	図面	担当	栗野 友仁	検図	図番
		品名	詳細図 BMUS-1616LBZ-B+H,LR	縮尺				日付 2025.04.07
		名						株式会社 LIXIL

ドア取合

有効幅員:650mm

窓開口位置

現場の状況や窓により窓開口位置を設定する場合、以下の範囲で決めてください。

※壁幅いっぱいの大きさの窓の場合は、パネル左右のスペースを0としてください。

※（ ）内の寸法とする場合は、壁パネルの強度上、桟木等を使用し補強を行ってください。

<1枚のパネルに納まる場合>

<2枚のパネルにまたがる場合>

<器具とのクリアランス>


ドア横の管柱、間柱について

ドアが管柱、間柱にあたらないように十分考慮してください。


寸法はユニットサイズやドア位置ずらし、間仕切りユニットの有無によって異なる場合があります。仕様図でご確認ください。

特記事項	受領印	物件名	図面	担当	検図	図番
		石原章弘 様邸		栗野 友仁		日付 2025.04.07
		品名	縮尺	株式会社 LIXIL		
		BMUS-1616LBZ-B+H,LR				
		名				

照明

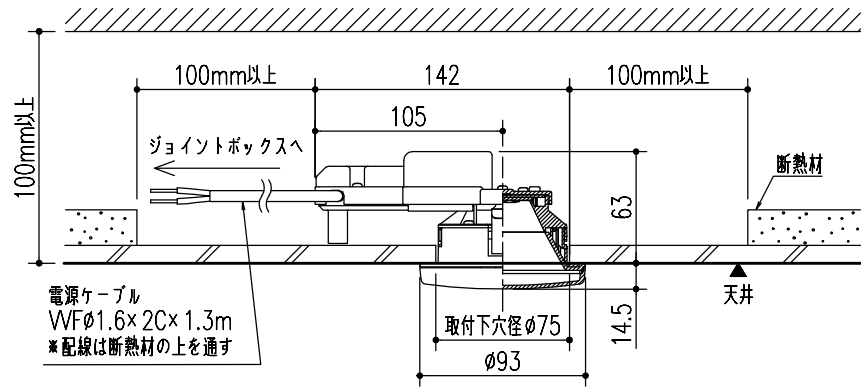



天井設置型照明は室外露出外殻から放熱しております。
その周辺100mmには保温・断熱材などを設置しないでください。
また、断熱材の落下など建築物が接触するおそれがある場合は、
建築側で防止策を講じて下さい。

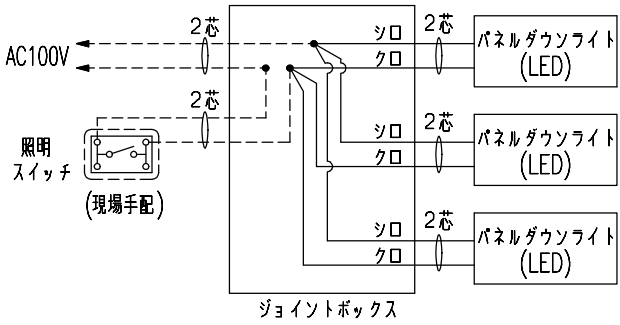

※浴室サイズ等により照明の数は異なります。


- 結線箇所 (電気工事)
- 配線 (現場手配・電気工事)

換気扇

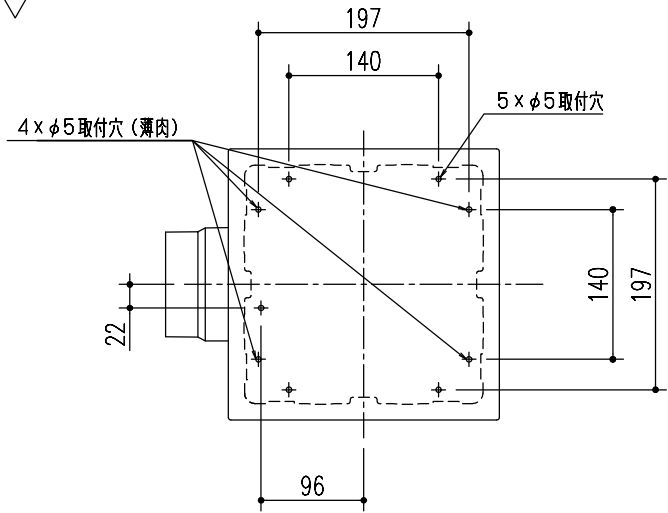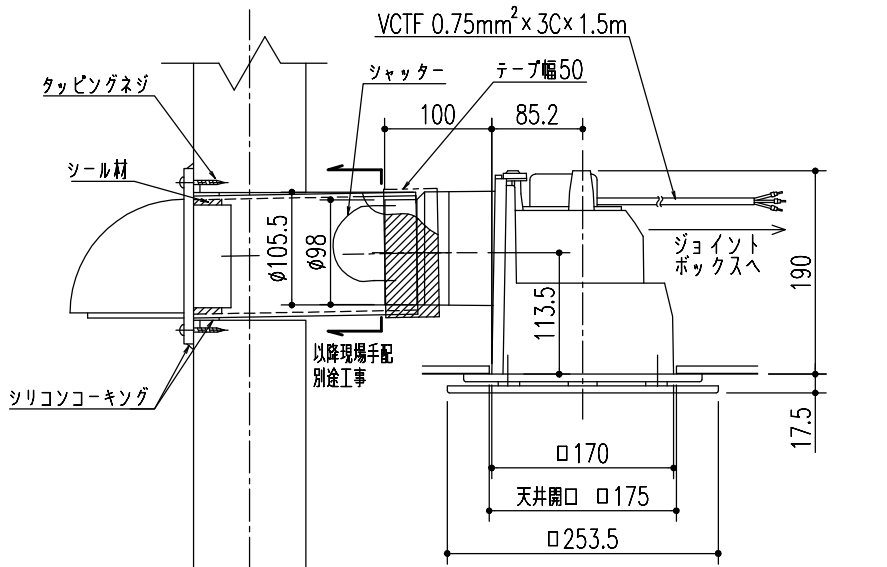

注1) 一次側電源線・アース線との結線工事、それ以降の配線工事、スイッチ取付け・結線工事は電気工事業者様の作業範囲となります。

結線図

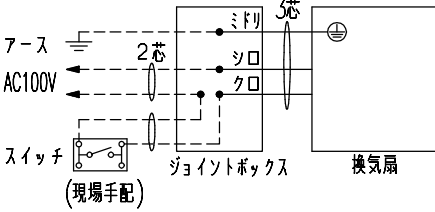


- 結線箇所 (電気工事)
- 配線 (現場手配・電気工事)

△ 警告
●電気工事は電気設備技術基準、内線規程など関連する法令・規程にしたがって、必ず「電気工事士」が行ってください。
●電線相互の接続は銅線用裸圧着スリーブを用いる等確実に工事してください。絶対に「手より」接続しないでください。
※電気工事が不適切な場合、火災や漏電の恐れがあります。
●電源線など各配線に、以下のことをしないでください。 ※火災、漏電や故障の恐れがあります。
・傷つける、無理に曲げる、無理な力を加える、束ねる、重いものを載せる、挟み込む。
●一次側に必ず漏電遮断器を設置してください。 ※感電する恐れがあります。

特記事項	受領印	物件名	図面	担当	検図	図番
		石原章弘 様邸		栗野 友仁		日付 2025.04.07
		品名	縮尺	株式会社 LIXIL		
		詳細図 BMUS-1616LBZ-B+H,LR				
		名				

注意）配線図の  は電気工事による接続箇所を示します。搭載する電気機器は配線図中の  に  と記入し、また不要な電気機器は斜線で消してください。

< 電気工事範囲 >

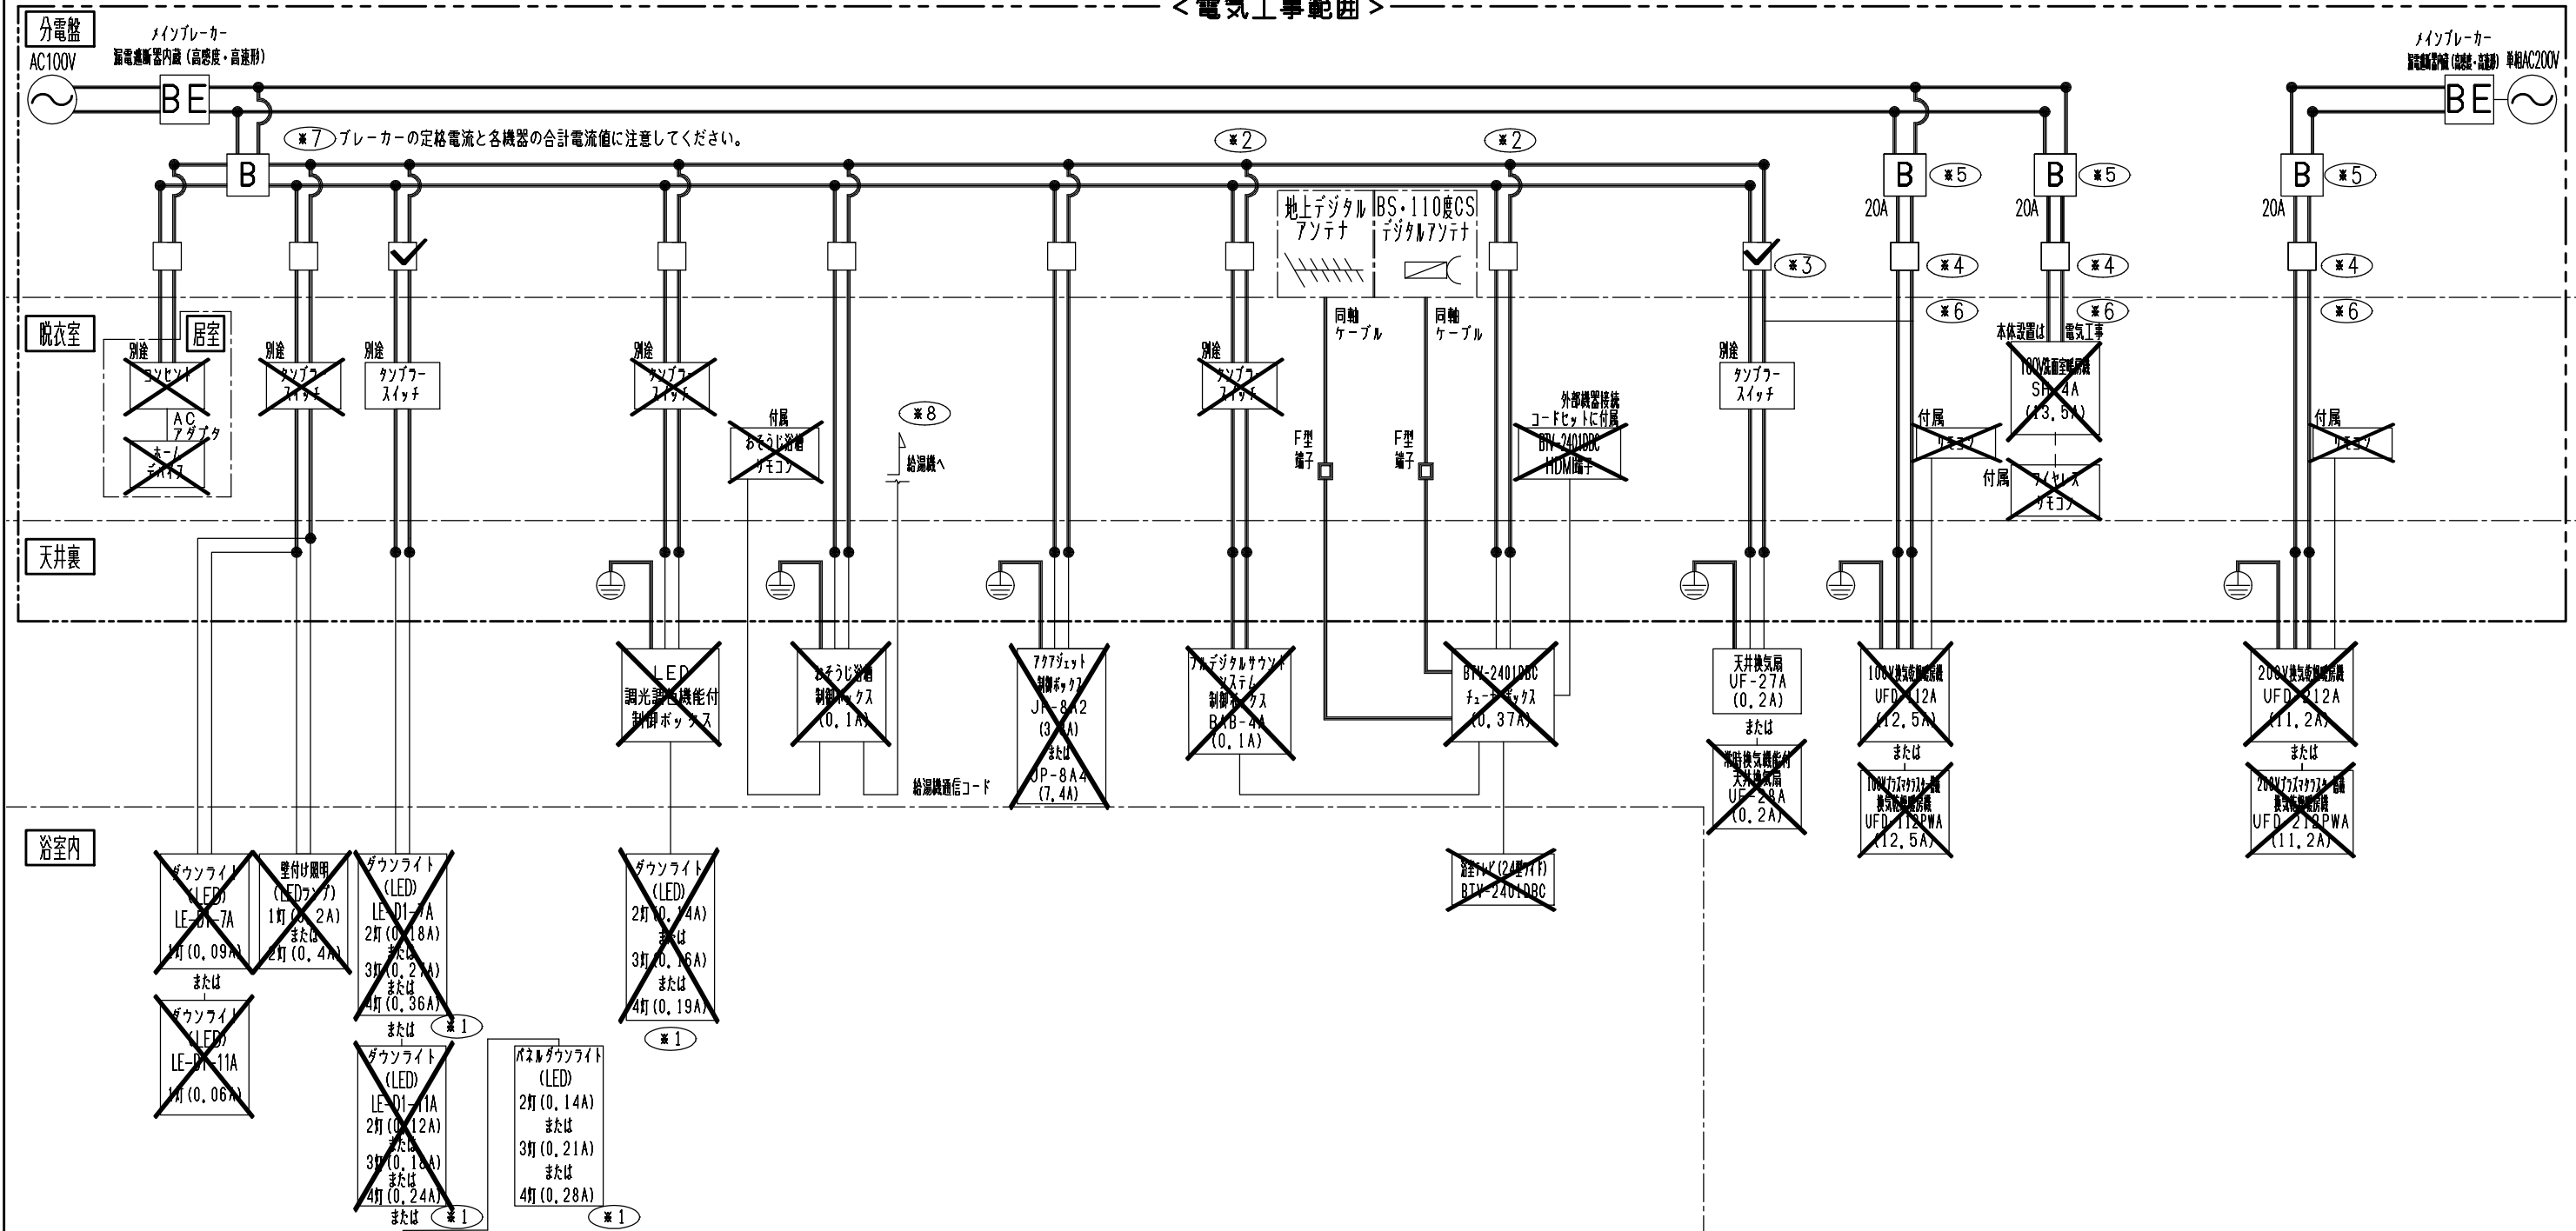

区分	照明	おそうじ浴槽	気泡浴槽	テレビ・サウンドシステム	換気設備	暖房設備・換気乾燥暖房機
----	----	--------	------	--------------	------	--------------

 **警告**

●電気工事は電気設備技術基準、内線規程など関連する法令・規程に従って、必ず電気工事士の資格を有する者が適切な方法で行ってください。 ※無資格者の工事や、電気工事士による不適切な工事は、火災や漏電を引き起こす恐れがあるほか、関係法令により処罰等されることがあります。

●電線相互の接続は銅線用裸圧着スリーブや差込形コネクタを用いる等確実に工事してください。絶対に「手より」接続しないでください。 ※電気工事が不適切な場合、火災や漏電の恐れがあります。

●アース工が必要な電気機器はD種接地工事を施した接地線と確実に接続してください。 ※漏電や故障の際に、感電する恐れがあります。

●電源線など各配線に、以下のことをしないでください。

- ・傷つける、無理に曲げる、無理な力を加える、束ねる、重いものを載せる、挟み込む ※火災、漏電や故障の恐れがあります。

●電源線、アース線やリモコンコード等の配線は、照明器具（ダウンライト等）や暖房機など熱器具から離して設置してください。 ※器具の熱で配線が溶断し、火災や漏電の恐れがあります。

●一次側に必ず漏電遮断器（高感度・高速形）を設置してください。 ※感電する恐れがあります。

●一次側の電源線、アース線、スイッチ配線と電気機器配線の結線部は、必ずジョイントボックス内に収めてください。 システムバスルームに同梱されているジョイントボックスを使用してください。 ※ほこり等により火災の恐れがあります。

- ※1：選択されたユニットサイズ、タイプ、オプションによって灯数が異なります。
- ※2：化粧台など浴室以外の照明器具との配線を分けてください。
※照明のon/offによってフルデジタルサウンドシステムへノイズが乗る可能性があります。
- ※3：換気扇を単独で設置する（換気乾燥暖房機を設置しない）場合を示します。
- ※4：換気乾燥暖房機を設置する場合、※3の経路はありません。
- ※5：運転初期に突入電流が発生しますので、換気乾燥暖房機単独で20Aの専用回路としてください。
※電気工事が不適切な場合、火災や漏電の恐れがあります。
- ※6：専用の配線用遮断機から配線し、途中にスイッチを設けないでください。
※誤った配線工事は、火災や漏電、故障の恐れがあります。
- ※7：ブレーカーの定格電流と各機器の合計電流値に注意してください。
- ※8：給湯機器と連動する場合に必要となります。

※以下のものは、システムバス取付作業に含まれておりません
・電源線、アース線の一次側配線工事、D種接地工事、漏電遮断器の調達および設置工事。
・各電気機器の電源線およびアース線と一次側配線との接続工事。
・脱衣室に設置するスイッチ（別途の表記があるもの）の調達。
・脱衣室に設置するスイッチの配線接続および設置工事（別途、付属とも）。

特記事項	受領印	物 件 名	石原章弘 様邸	図面	担当	検図	図
各電気機器の詳細については各々のオプション詳細図を 参照ください。					栗野 友仁		番
						日付 2025.04.07	
		品 名	縮尺	電気機器配線図 BMUS-1616LBZ-B+H,LR	株式会社 LIXIL		


排水管接続の注意点

浴槽排水時には最大約1.2L/sの流量が発生します。排水管の経路や、管内の状態によっては正しく排水されない場合があります。設計・取付の際は次の各項目を確認して下さい。

■ダブルトラップ

浴室以降の排水管経路上に、トラップが無いことを確認してください。（ダブルトラップの禁止）
ダブルトラップになっていると、「排水が流れない」「異臭がする（封水切れ）」などの異常につながります。
ダブルトラップは配管接続前に解消してください。
システムバスルーム設置後はダブルトラップの解除ができません。

【ダブルトラップの例】

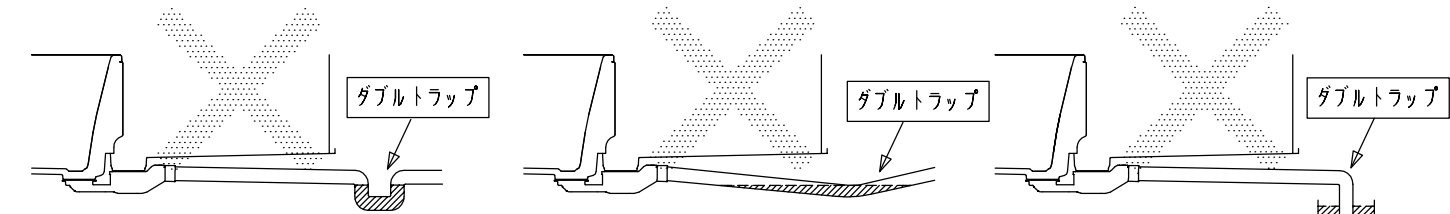


下に曲がった配管部分が、トラップになっている 横引き配管がたわみ、トラップになっている 配管の先が排水ます溜水内にあり、トラップになっている

■排水管内の詰まり


接続する排水管が、汚れなどで詰まっていないことを確認してください。
配管が細かったり、配管内が汚れ等で詰まっていると、「排水が流れない」「洗い場排水口から浴槽排水が溢れてくる」といった異常につながります。
汚れが付着して詰まっている場合、配管を接続する前に洗浄し汚れを取り除いてください。

【悪い例】

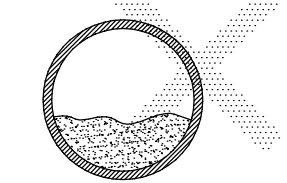

配管内に汚れなどの詰まりがある

【良い例】

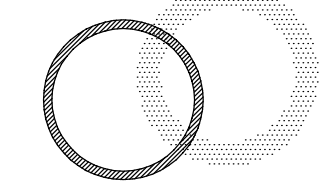


配管内に汚れなどの詰まりは取り除く

■排水管経路

排水管の経路によっては、排水異常となる場合があります。
次の事項にご注意のうえ設備業者さまと十分な事前打合せをお願い致します。

① システムバスルーム以降で排水管を縦方向に落とす場合


通気を設けるか、配管径を拡張、もしくは90°曲げ部に大曲リエルボ（LL）を使用する事をおすすめします。

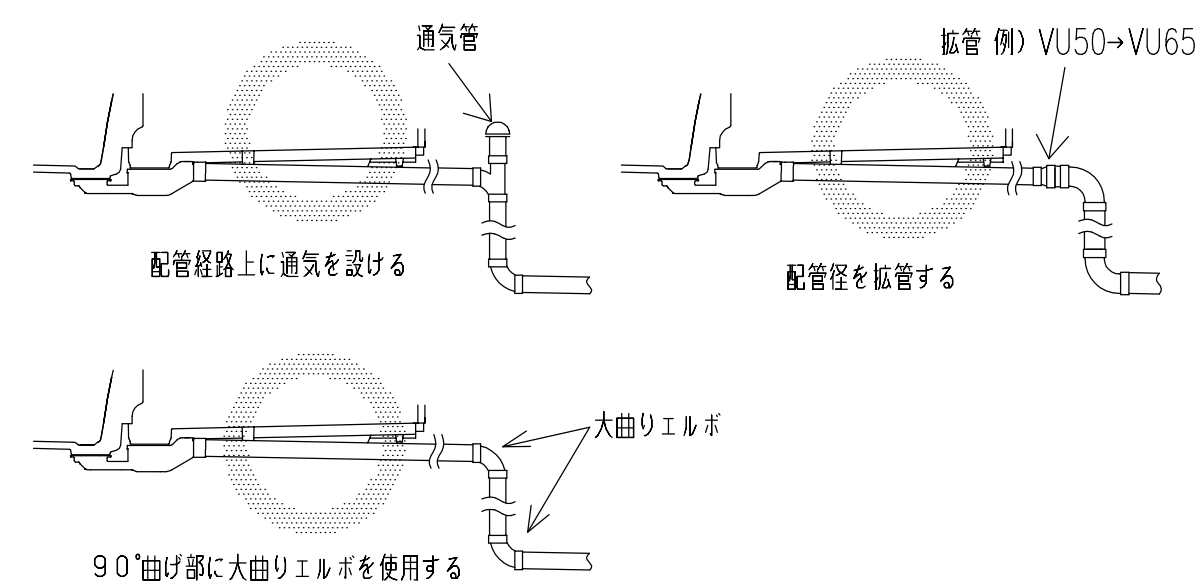

※浴槽排水時に排水口から「ゴボゴボ」と音が発生することがありますが、異常ではありません。


② システムバスルーム以降の横引き配管について

90°曲げ部に大曲リエルボ（LL）を使用するか、システムバスルームに近い位置で配管径を拡張する事をおすすめします。

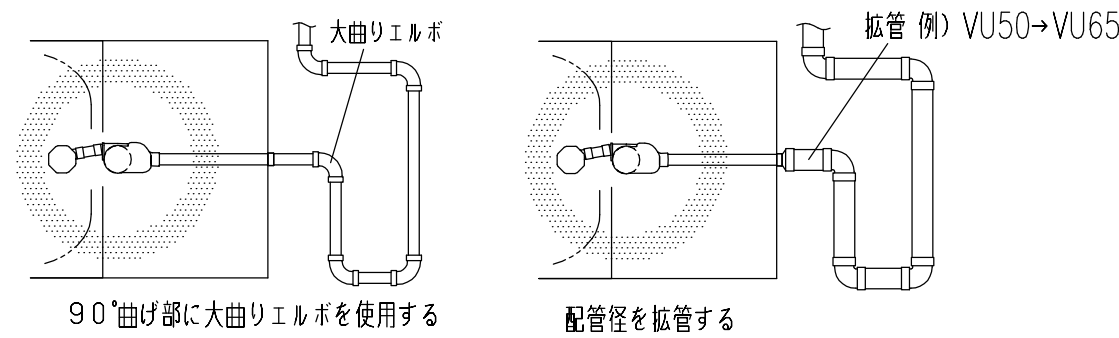



③ システムバスルーム床下の排水管経路について

- トラップ出口には同梱の継口配管を接続してください
 - 継口配管を使用しない場合
 - ・大曲リエルボを使用してください
 - ・1620-2サイズの場合、トラップ出口に接続する配管には、必ず切断長さ250mm以上の横引き経路を設けてください
- ※洗い場パンとの干渉回避や浴槽排水の流れを妨げないため

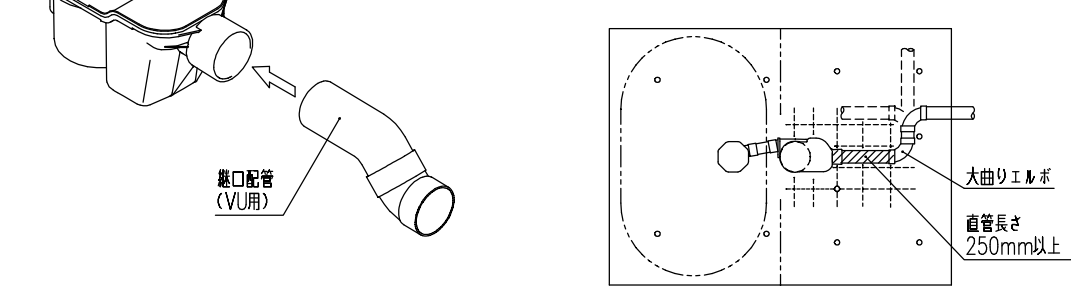



【排水管経路の悪い例】

十分な長さの横引き配管を設けずに曲げを繰り返したり、縦方向に落としている


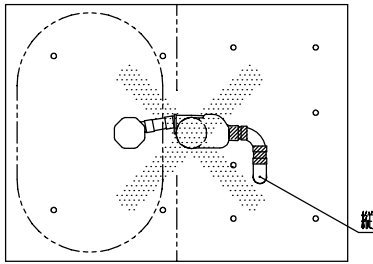
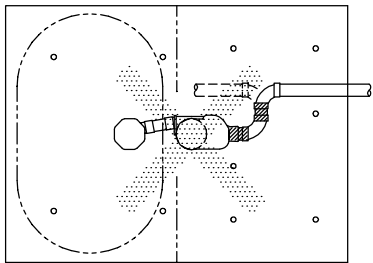


【排水管経路の良い例】

トラップから2曲がりまでの間に十分な長さの横引き経路を設けている

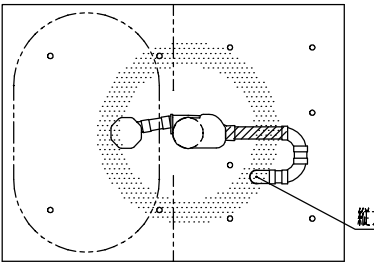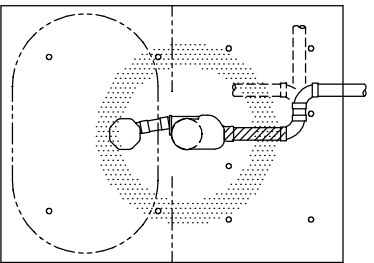

特記事項	受領印	物件名	図面	担当	検図	図番
		品名				日付
		排水管経路条件図	縮尺	株式会社 LIXIL		
		AX				

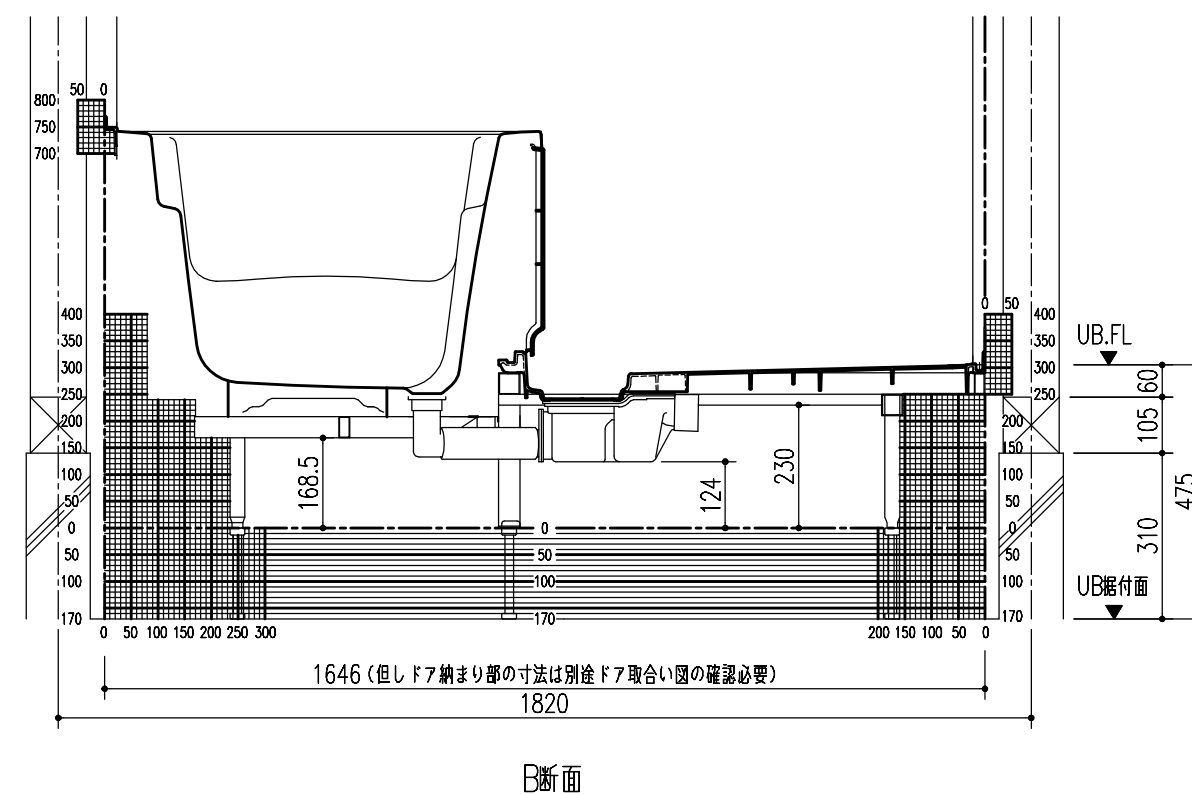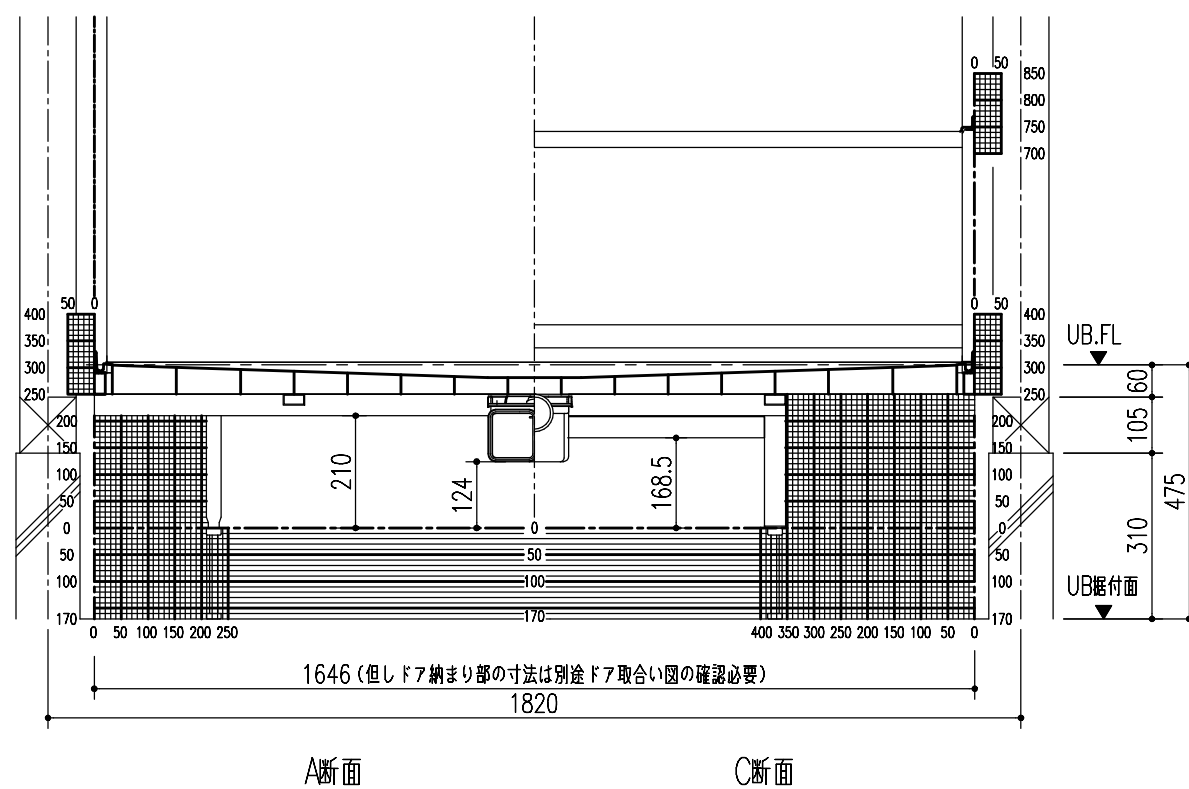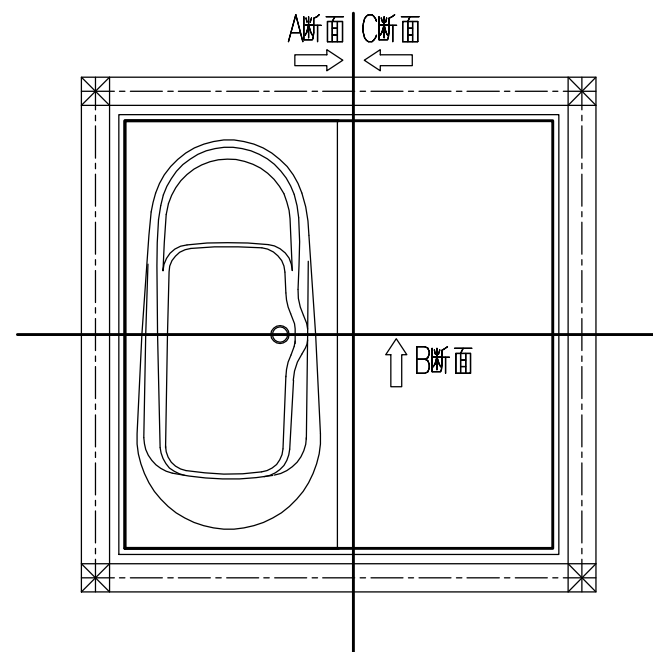

※ 本図はRタイプを示します。Lタイプは本図を左右反転したものになります。

特記事項	受領印	物	図面	担当	検図	図	
		件				番	
		名				日付	
		品	床下納まり	縮尺	株式会社 LIXIL		
			AX				
		名	1616サイズ(浴槽パンなし・ボルト脚仕様H475)				

●全面開口の場合

- ※ 奥行 390・490 の客用扉使用の場合、製品に 1/50 の水勾配がついております。そのため、バネル開口寸法 A および客用扉外寸法 B が水勾配分大きくくなります。詳しくは客用扉開口取付説明書をご確認ください。
- ※ 窓と客用扉を締結するための取付ねじは客用扉に同梱されていません。
- ※ 客用開口補強（アルミテープ）は別途施工が必要です。
- ※ 1 客用扉 1510P は、幅 (W) 1000×高さ (H) 1500 としても使用できます。

特記事項	受領印	物件名	図面	担当	検図	図番 日付
		品名	縮尺	株式会社 LIXIL		
		フリーサイズ・客額縁 詳細図 R-1010P,R-1510P R-1515P,R-1715P				