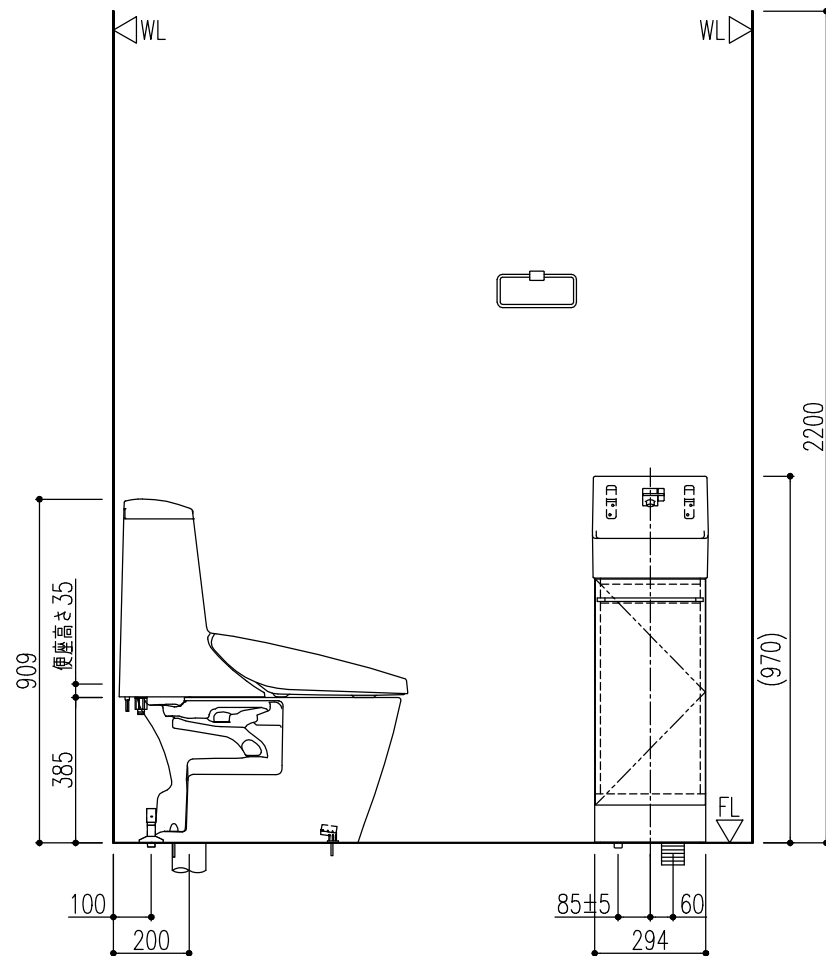
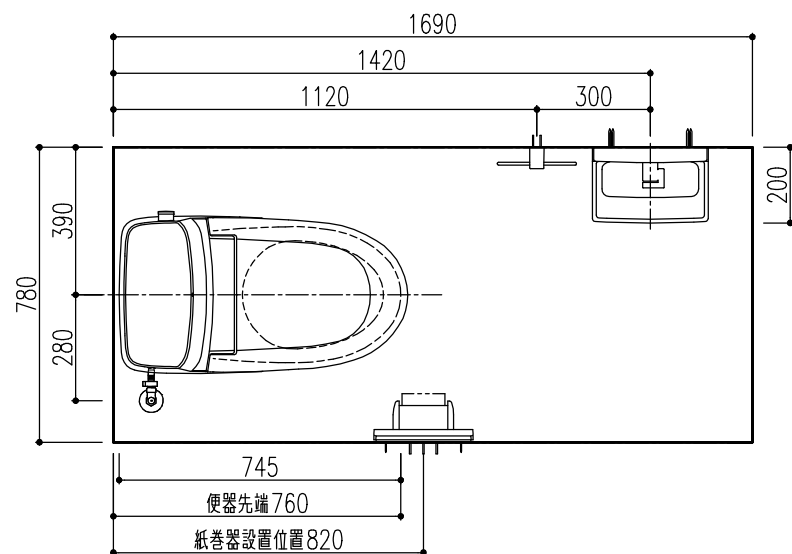
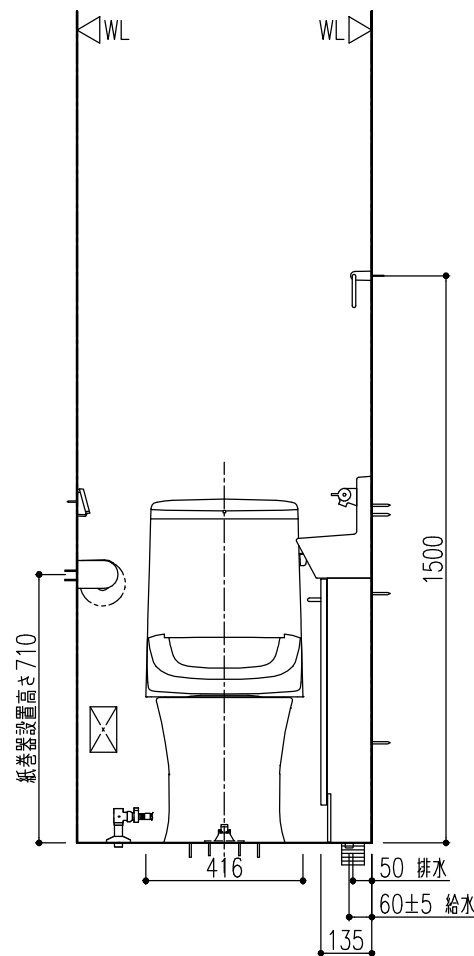


[illegible]

【共通】

※部品表の「図面」列に○がないものは図面表示されません。

・このプランの施工情報については事前に商品の施工説明書や工事用図面集にてご確認ください。

2枚目以降の機能図にも商品情報の記載があります。

・商品仕様・図面の改良や仕様変更等は、予告なく行う場合があります。

・壁面に取り付ける商品にはあらかじめ壁補強が必要です。必要な壁面工事は2枚目以降の機能図にてご確認ください。

・壁埋込みの必要な商品はあるかじめ商品に合わせた開口を行ってください。

・電源が必要な商品には、商品の仕様に合わせたコンセント設置等の電気工事(別途工事)を

あらかじめ行ってください。商品の施工説明書にて工事内容をご確認ください。

・コンセントは、電源コードの届く範囲で床面より高く水のかからない位置に設けてください。

また、コンセントの壁給水真下部設置や給水ホースとの接触は感電・火災の原因になりますので避けてください。

・扉等の建築物による干渉をご確認ください。

・アクセサリ類・手洗器の設置位置は参考寸法です。使いやすさに合わせて取付位置を決定ください。

・()内寸法は、参考寸法です。

・陶器寸法許容差はJIS A5207に準じています。

・結露水・小水によるシミの発生を防ぐため、トイレ床材には防水加工が施された床材をご使用ください。

【便器】

・洗淨水量：大5L、小3.8L

・製品両側面から 10mm以上の空間を確保してください。

・タンク上部に柵等を設置する場合は、床から1150mm以上の空間が必要です。

・一般地用、寒冷地用流動式兼用品です。

・トイレ内使用限界：-10℃以上、流動水量60L/h。

0℃を下回る場合は器具内の水を流動させてください。

・凍結防止には器具への通電が必要です。

・D種接地工事が必要です。アースターミナル付接地極付コンセントを使用してください。

・定格消費電力330W(タンク部)

・機能部電源コード長さ1000mm

- ・インバータ照明により誤作動する場合があります。

《重要》

排水管の立ち上げ高さは床仕上げ面から60±5mmにしてください。排水管が床仕上げ面と同じ高さの場合は市販の60mm立ち上げ用部材(持ち出しニップル)を別途手配ください。

【手洗器】

・給水圧力範囲：0.05~0.75MPa

・扉の開き代が必要なため、キャビネット側板から110mm以上空留を確保してください。

・建築側壁面に2mあたり3mmを超える不陸がないことを確認した上で設置してください。

不陸があるまま設置すると製品がひずむ場合があります。

- ・「維持管理性能」等級2、等級3対応品です。













・右吊元のみです。

・キャビネット部の巾木はあらかじめカットしてください。

	特記事項	物件名	石原章弘 様邸	案件No.	図面名	担当	図面	図番 : 株式会社 LIXIL
				A2502DDD0EEKHS	簡易取付設置図	葉野 友仁		
		仕様	ベ－シアシャワ－ト イレノEC05 床排水 一般地	見積No.	縮尺	日付		
				M25026646745-005-5	1/20	2025.04.07		


●アクセサリー 施工要領図

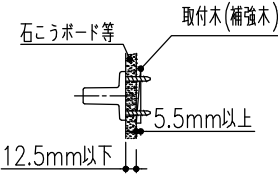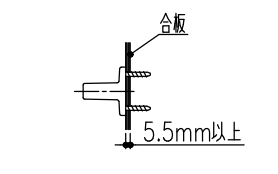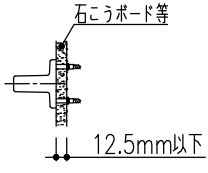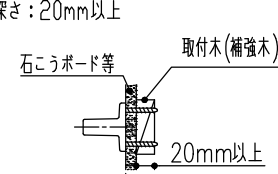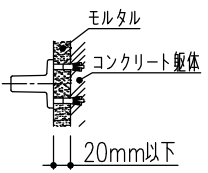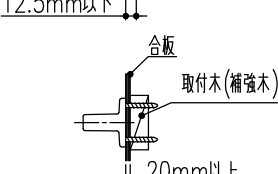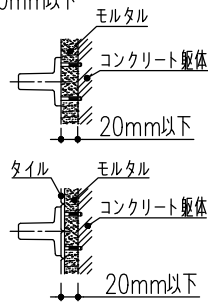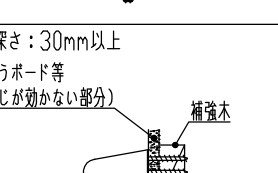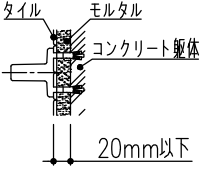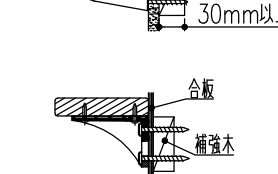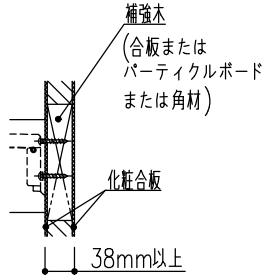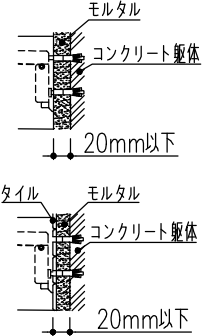壁取付アクセサリーの落下事故防止のため、取付部材（木ねじ、AYボルト等）の固定強度（種類・数）については十分配慮を行っておりますが、壁面の構造についても配慮いただくことが不可欠です。

アクセサリー種類	乾 式 壁			湿 式 壁	
	木 ね じ	木ねじ+プラスチックプラグ	パ ー テ ー シ ョ ン 壁	A Y ボ ル ト	木ねじ+プラスチックプラグ
紙巻器 化粧鏡 石けん入れ	ねじ込み深さ：5.5mm以上 	取付不可	取付不可	壁仕上材厚さ：20mm以下	取付不可
化粧鏡		石こうボード壁厚：9.5mm以上 12.5mm以下			
紙巻器 石けん入れ		取付不可			壁仕上材厚さ：20mm以下
紙巻器	ねじ込み深さ：20mm以上 				
フック タオル掛 化粧棚 紙巻器 タオルリング 化粧鏡 スベアペーパーホルダー サニタリーボックス	ねじ込み深さ：20mm以上 	取付不可			取付不可
アクセサリーパー 棚手すり 紙巻器 タオル棚 手すり 照明付鏡	ねじ込み深さ：30mm以上 石こうボード等 （ねじが効かない部分） 				
棚付二連紙巻器 横2連ストック付紙巻器 横4連ストック付紙巻器	合板の場合の厚さ：18mm以上 角材の場合の厚さ：30mm以上 		パーティション （化粧合板+補強木）の厚さ：38mm以上 	壁仕上材厚さ：20mm以下 	

	特記事項	物件名	石原章弘 様邸	案件No.	図面名	担当	図面	図番	株式会社 LIXIL
				A2502DDD0EEKHS	機能図	栗野 友仁			
		仕様	ベーシアシャワートイレ／ECO5 床排水 一般地	見積No.	縮尺	日付			
				M25026646745-005-5		2025.04.07			

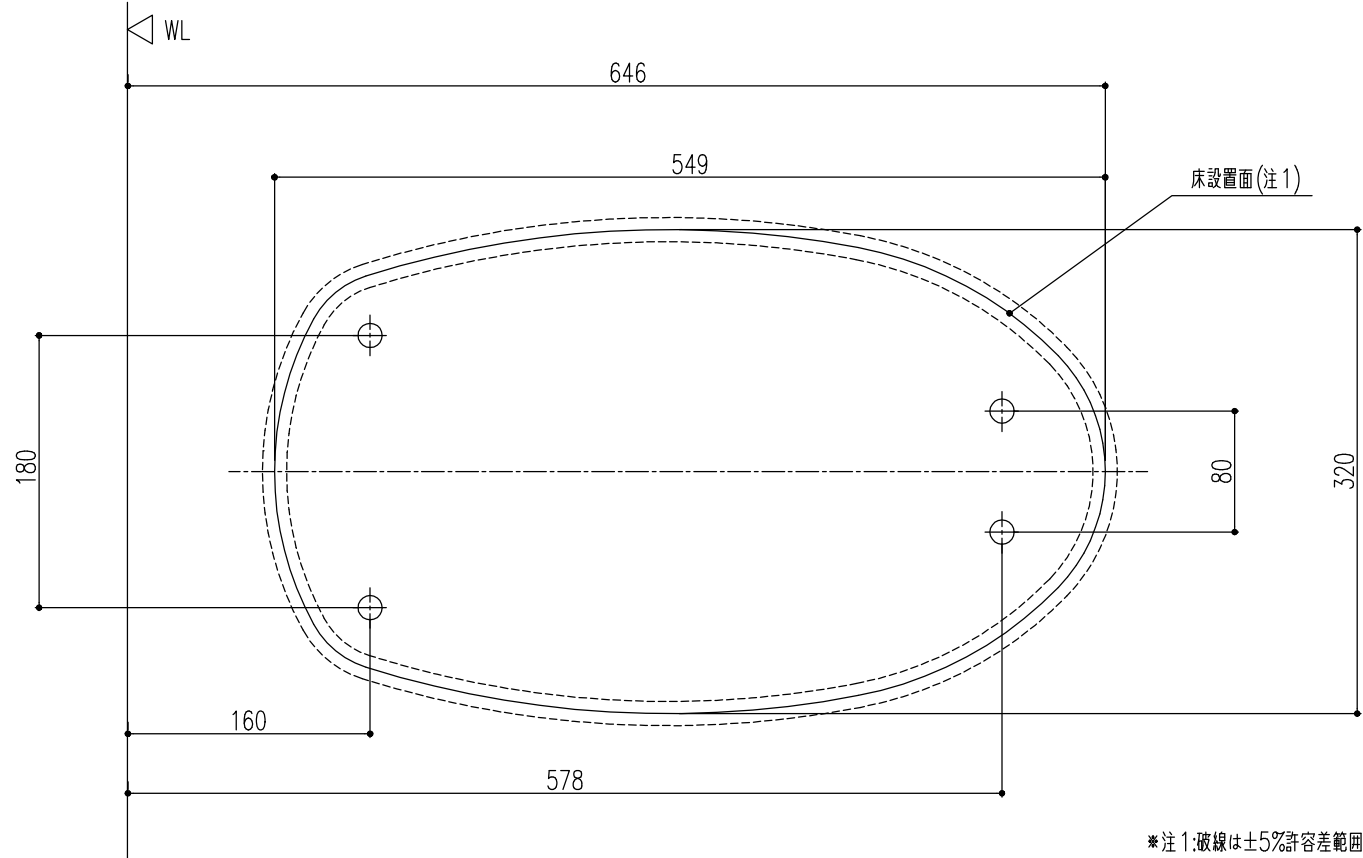
●便器床設置面寸法・固定穴寸法



●給排水の位置決めと取出し

給水管、排水管を取り出します。

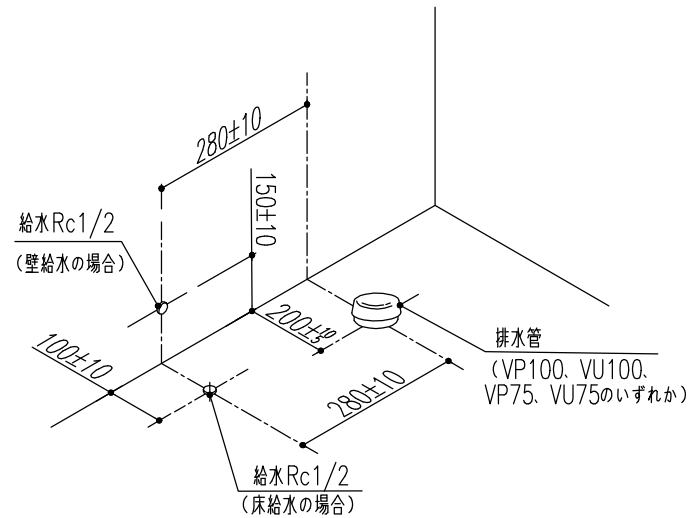- ※ 給水管、排水管を施工寸法通りに取り出します。
誤って排水管を壁寄りに取り出した場合は、タンクと壁が干渉して
施工できない恐れがあります。




●排水塩ビ管の接続

- * 接続は、塩ビ接着剤にて確実に行なって下さい。
- * 排水管の立ち上げ高さは、必ず $60\pm 5\text{mm}$ の位置で切断してください。

施工方法詳細の動画を以下から読み取ることができます。

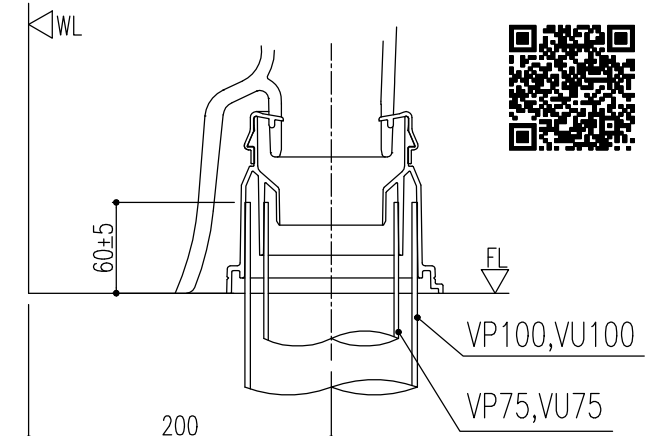
- ・ 通信料はお客様のご負担となります。
- ・ お使いの環境・端末によっては、閲覧できない場合があります。
- ・ 実物と動画のデザインが異なる場合があります。
- ・ 動画内に表示される商品名と品番・デザインが異なる場合がありますが、施工手順に影響ありません。




※注…立ち上げ寸法が60mm以下の場合は 既設配管に合った、
市販の60mm立ち上げ用部材(持ち出しニップル)を別途手配ください。
※注…防振シートを組み合わせる場合は5mm高くしてください。

●取付最小スペース

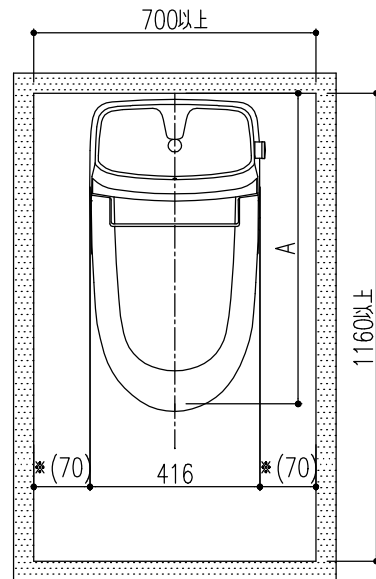- ※ 最小スペースはA寸法(前出寸法)
+ 400となり、便器排水方向や既設
配管により、異なります。
- A寸法は、床排水・床上排水(後抜き)
の場合760mm、床上排水(横抜き)
の場合860mmとなります。
- ご確認ください。
- ※ 右図の空間寸法は、衣服の着脱などの
行為に必要な最低寸法です。
- 手すりや紙巻器などの機器を併設する
場合は、必要に応じた広い空間が必要
になります。
- ※ 便器に向かって左右共に70mm以上
の空間を確保してください。




●便フタ開時寸法

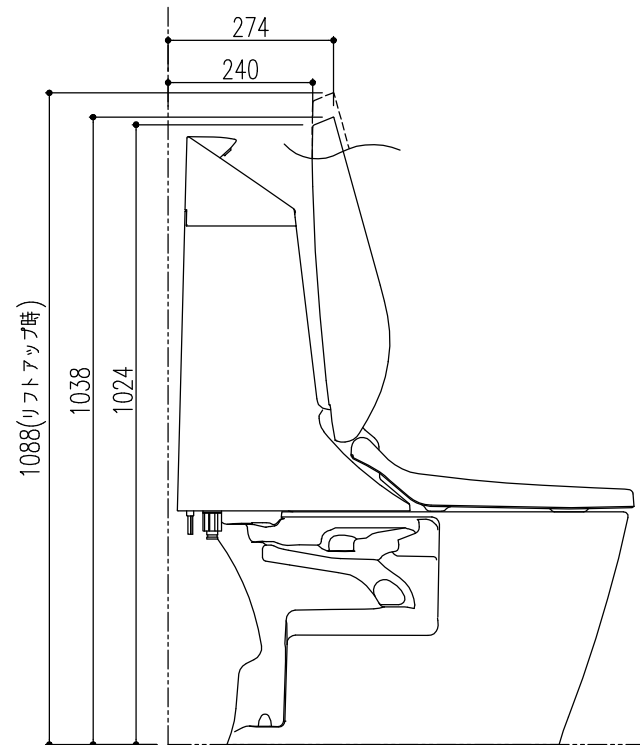


- ※ 上図は代表商品のイメージ図です。
※ 防振シートを組み合わせる場合は、全体が5mm高くなります。

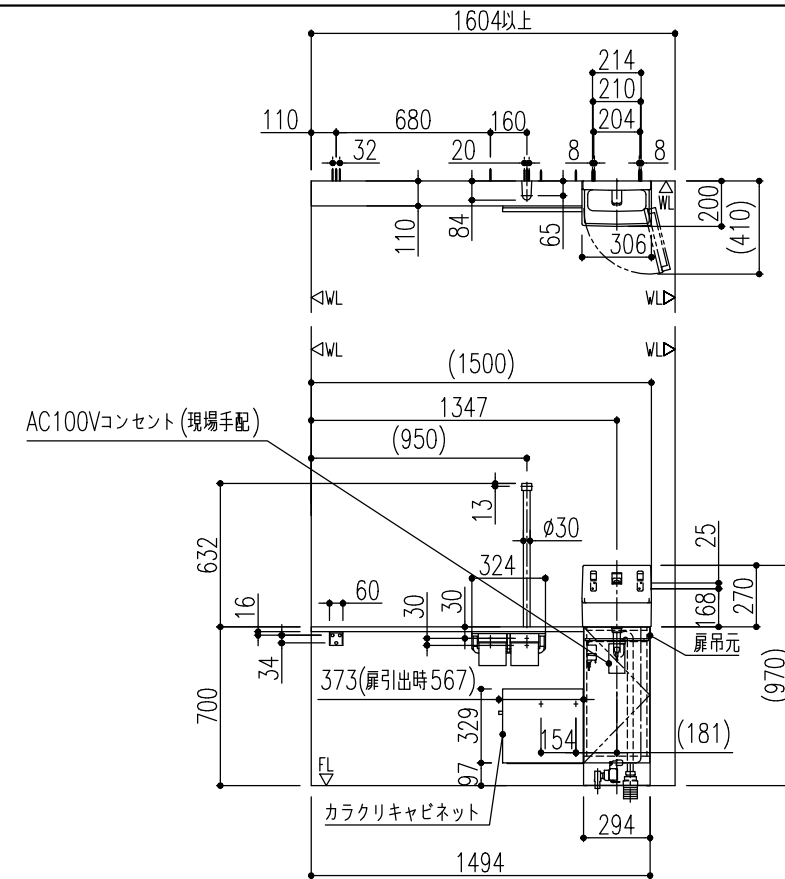●コフレルスリム(壁付)施工例



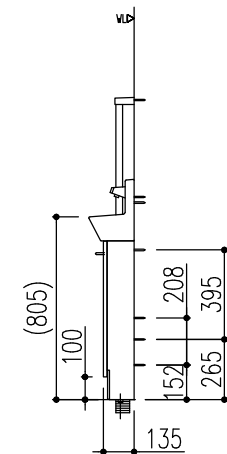- * この図はR仕様、カウンター1500タイプです。
- * ()内は、参考寸法です。
- * この図は代表商品のイメージ図です。



	特記事項	物件名	石原章弘 様邸	案件No.	図面名	担当	図面	図番 : 株式会社 LIXIL
				A2502DDD0EEKHS	機能図	栗野 友仁		
		仕様	ベアシャワートイレ/ECO5 床排水 一般地	見積No.	縮尺	日付		
				M25026646745-005-5		2025.04.07		

●コフレルスリム(壁付)給排水・コンセント位置		●補強木位置							
* 下図は1200サイズの場合を示し、 ()内寸法は、1500サイズの場合を示します。 【カウンター長さ注文サイズ対応】 * 下図は1000～1190の場合を示し、 ()内寸法は、1210～1490の場合を示します。 * 自動水栓の場合は下図を参照し、コンセントを設置してください。 * 温水自動水栓の場合は、D種接地工事が必要です。 アースターミナル付接地極付コンセントを使用してください。		* 下図は1200サイズの場合を示し、 ()内寸法は、1500サイズの場合を示します。 【カウンター長さ注文サイズ対応】 * 下図は1000～1190の場合を示し、 ()内寸法は、1210～1490の場合を示します。 * 取付強度を保つために、取付部に下地補強木 (厚さ30mm以上)を入れてください。							
	特記事項	物件名 仕様	石原章弘 様邸 ベーシアシャワートイレノEC05 床排水 一般地	案件No.	図面名	担当	図面	図番	
				A2502DDD0EEKHS	機能図	栗野 友仁		株式会社 LIXIL	
				見積No.	縮尺	日付			
				M25026646745-005-5		2025.04.07			