

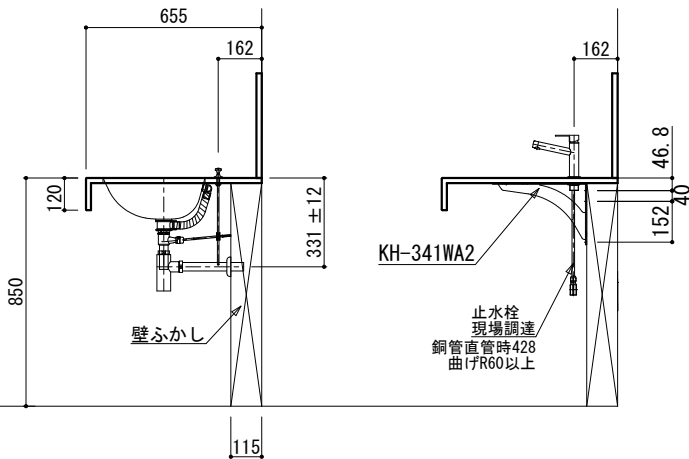
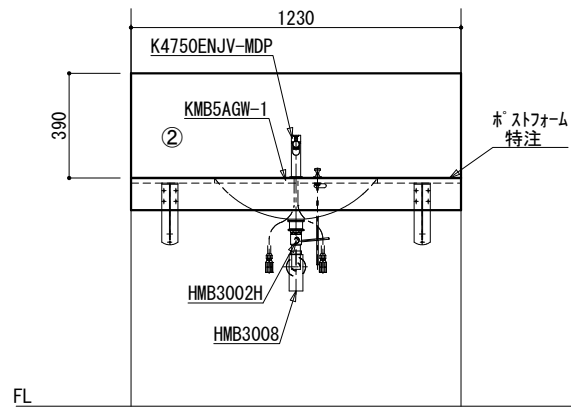
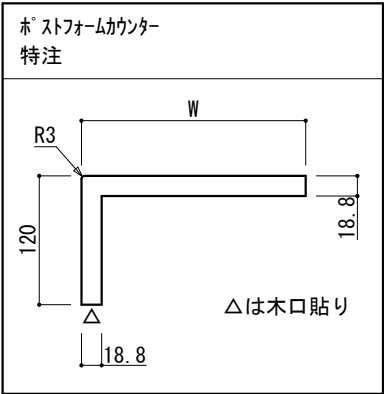



パーツ	色	仕様
①カウンター	TJ-10239K	ホ`ストフォーム 特注
②立ち上がり部材	TJ-10239K	ホ`ストフォーム KAAタイプ`
ボウル	KMB5AGW-1	シームアンダー`-取付 (フラット)
給水栓	K4750ENJV-MDP	
排水栓	HMB3002H	ヘアキャッチャー付
排水トラップ	HMB3008	
ブラケット	KH-341WA2	

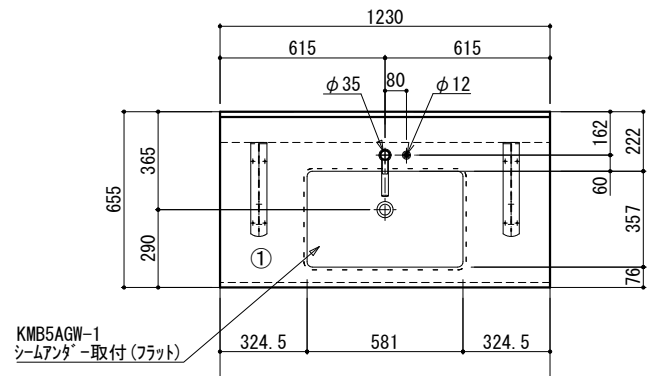

②立ち上がり部材

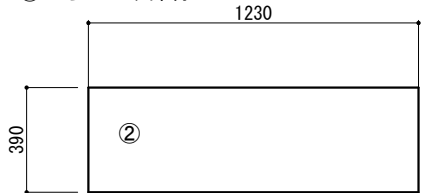

ホ`ストフォームカウンター
②K A Aタイプ`

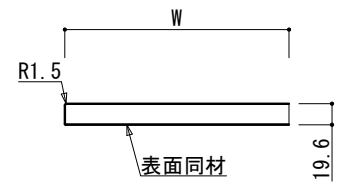

十分に強度のある下地に適切な施工を行ってください。

仕様書

△		
△		
△		
訂正	年月日	署名

承認	検図	設計	縮尺
		kezuka	1/20
		製図	年月日
		中迫	25. 05. 29



品名	アイカカウンターシステム スタイリッシュカウンター	品番
図名	LIFEFUND 様 石原章弘 様邸	図番 C126-5-K492-01