



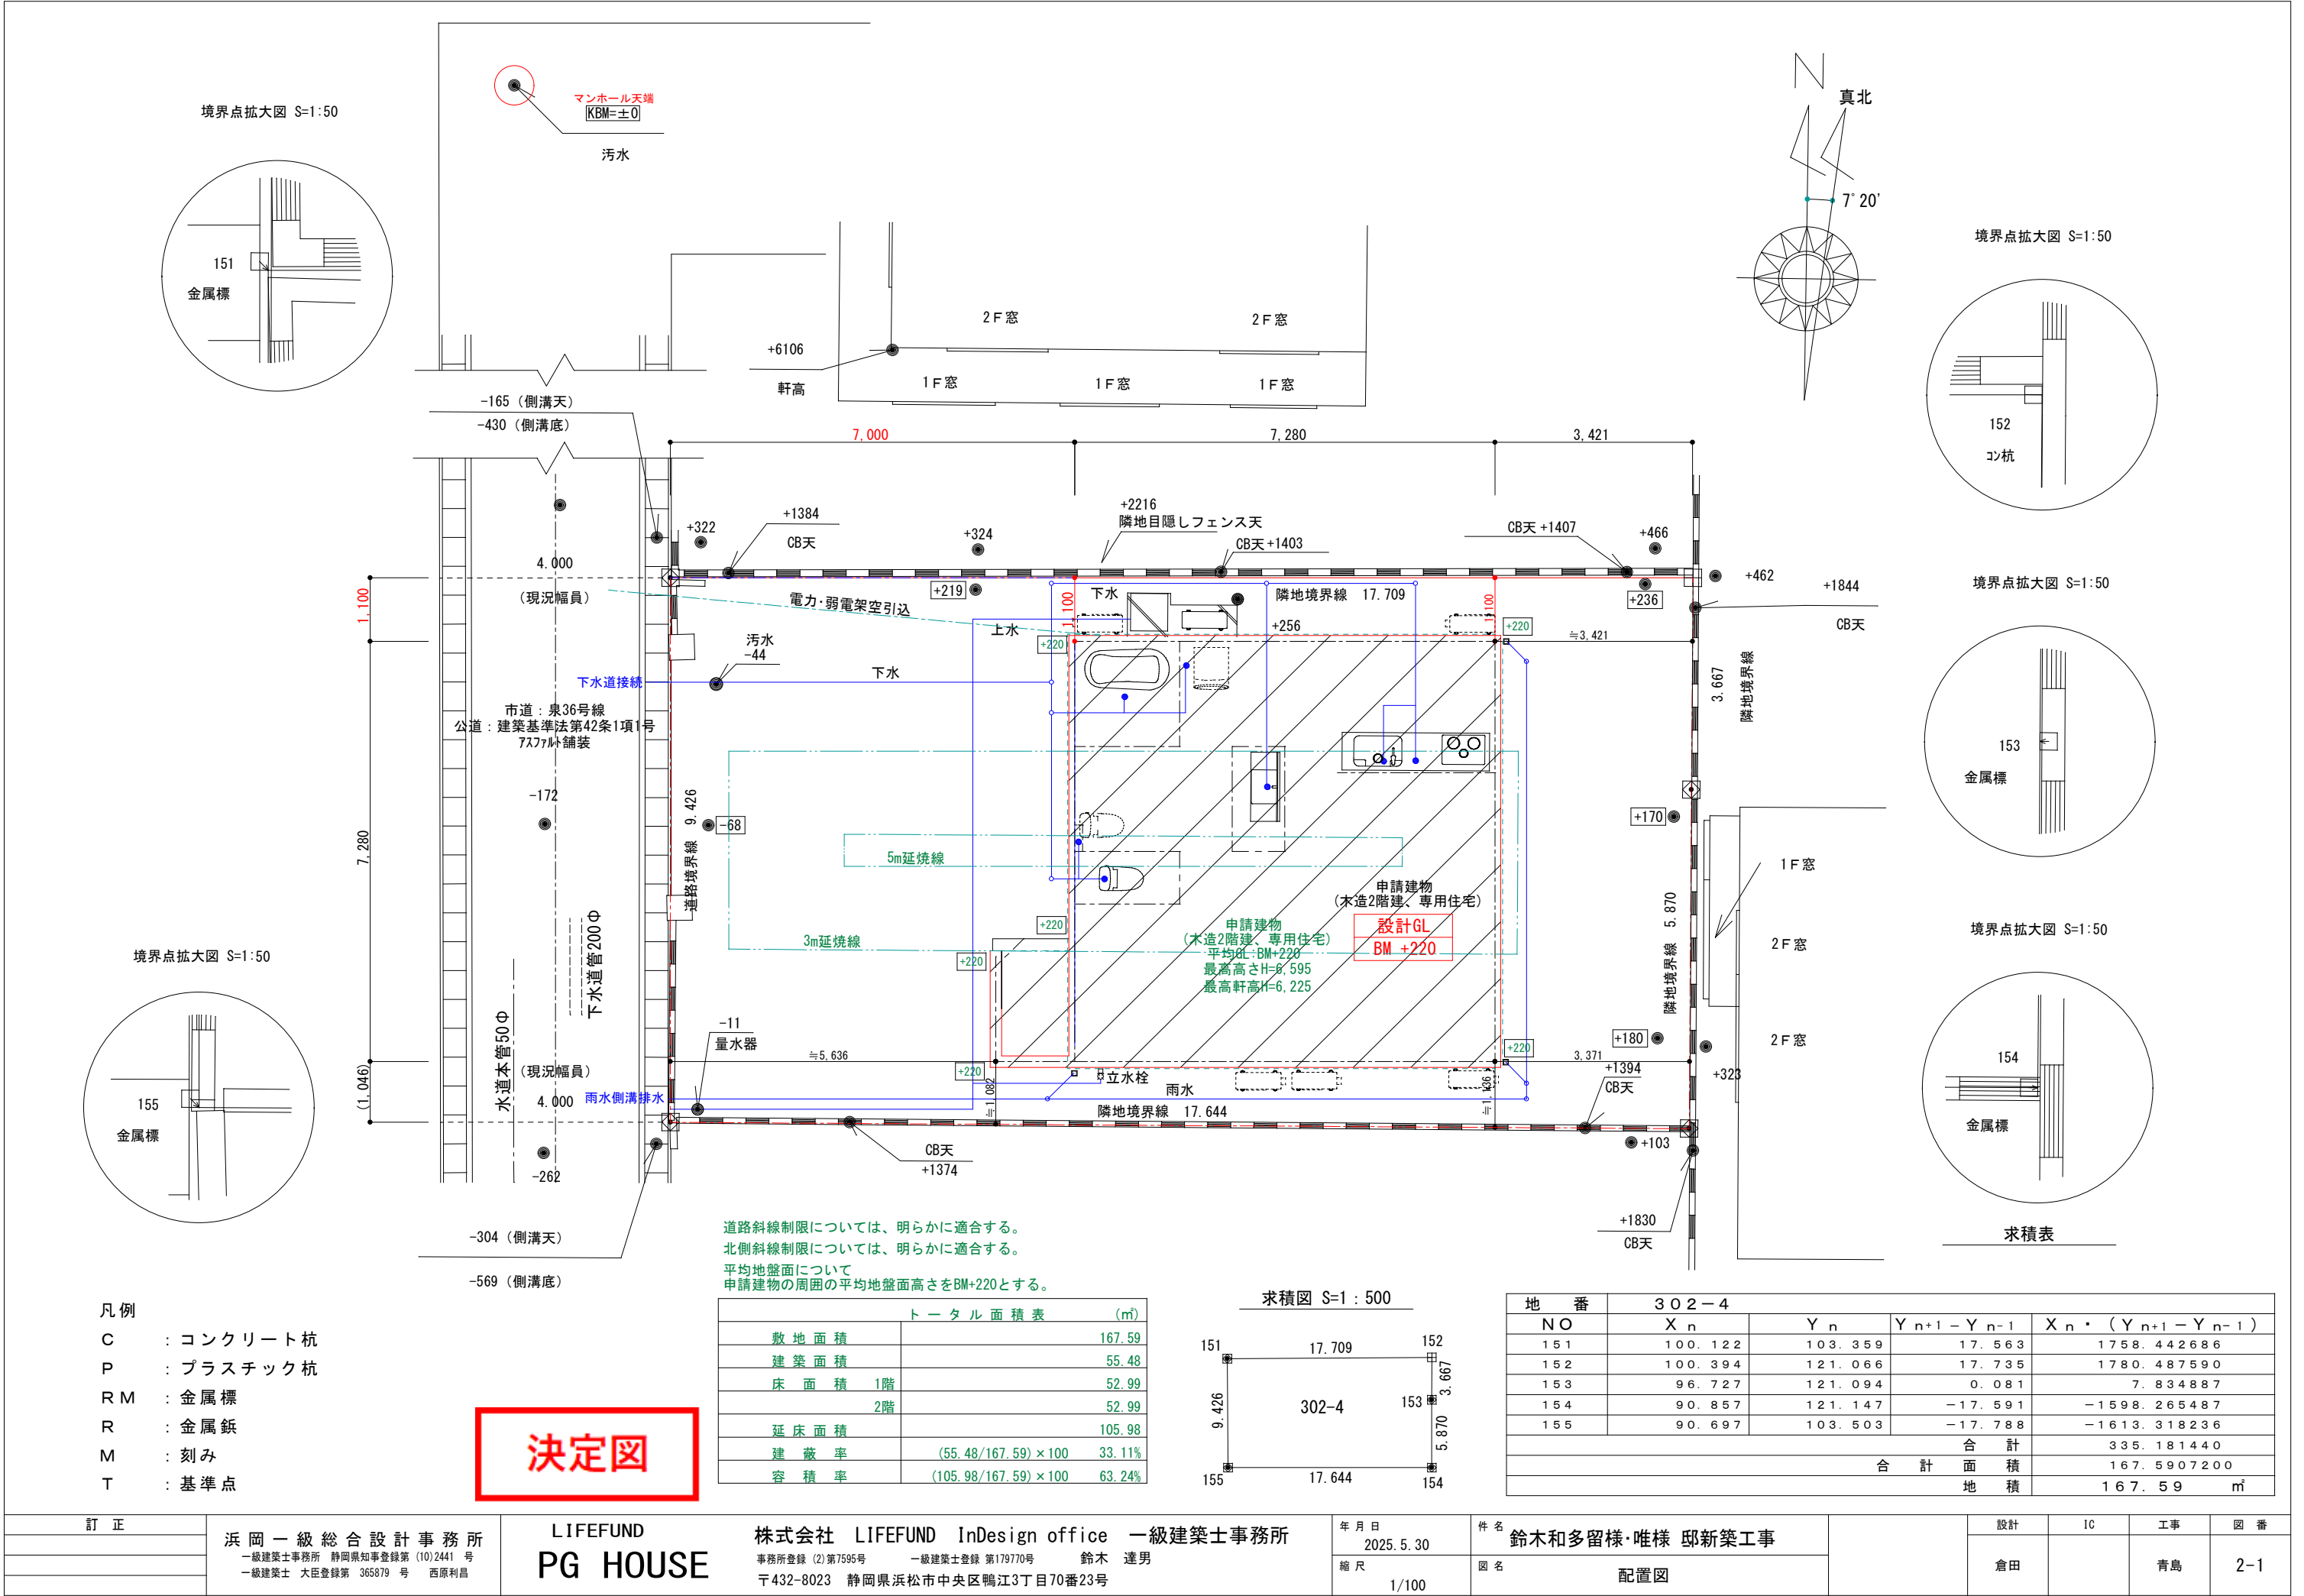

- 凡例
- C : コンクリート杭
 - P : プラスチック杭
 - RM : 金属標
 - R : 金属鉋
 - M : 刻み
 - T : 基準点

決定図

トータル面積表 (㎡)	
敷地面積	167.59
建築面積	55.48
床面積 1階	52.99
2階	52.99
延床面積	105.98
建蔽率	$(55.48/167.59) \times 100$ 33.11%
容積率	$(105.98/167.59) \times 100$ 63.24%

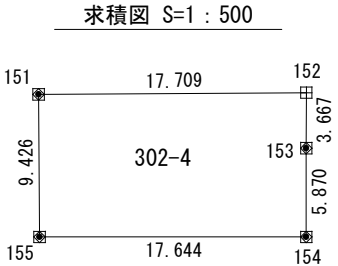

地番	302-4				
NO	X _n	Y _n	Y _{n+1} - Y _{n-1}	X _n * (Y _{n+1} - Y _{n-1})	
151	100.122	103.359	17.563	1758.442686	
152	100.394	121.066	17.735	1780.487590	
153	96.727	121.094	0.081	7.834887	
154	90.857	121.147	-17.591	-1598.265487	
155	90.697	103.503	-17.788	-1613.318236	
合計				335.181440	
合計面積				167.5907200	
地積				167.59 ㎡	