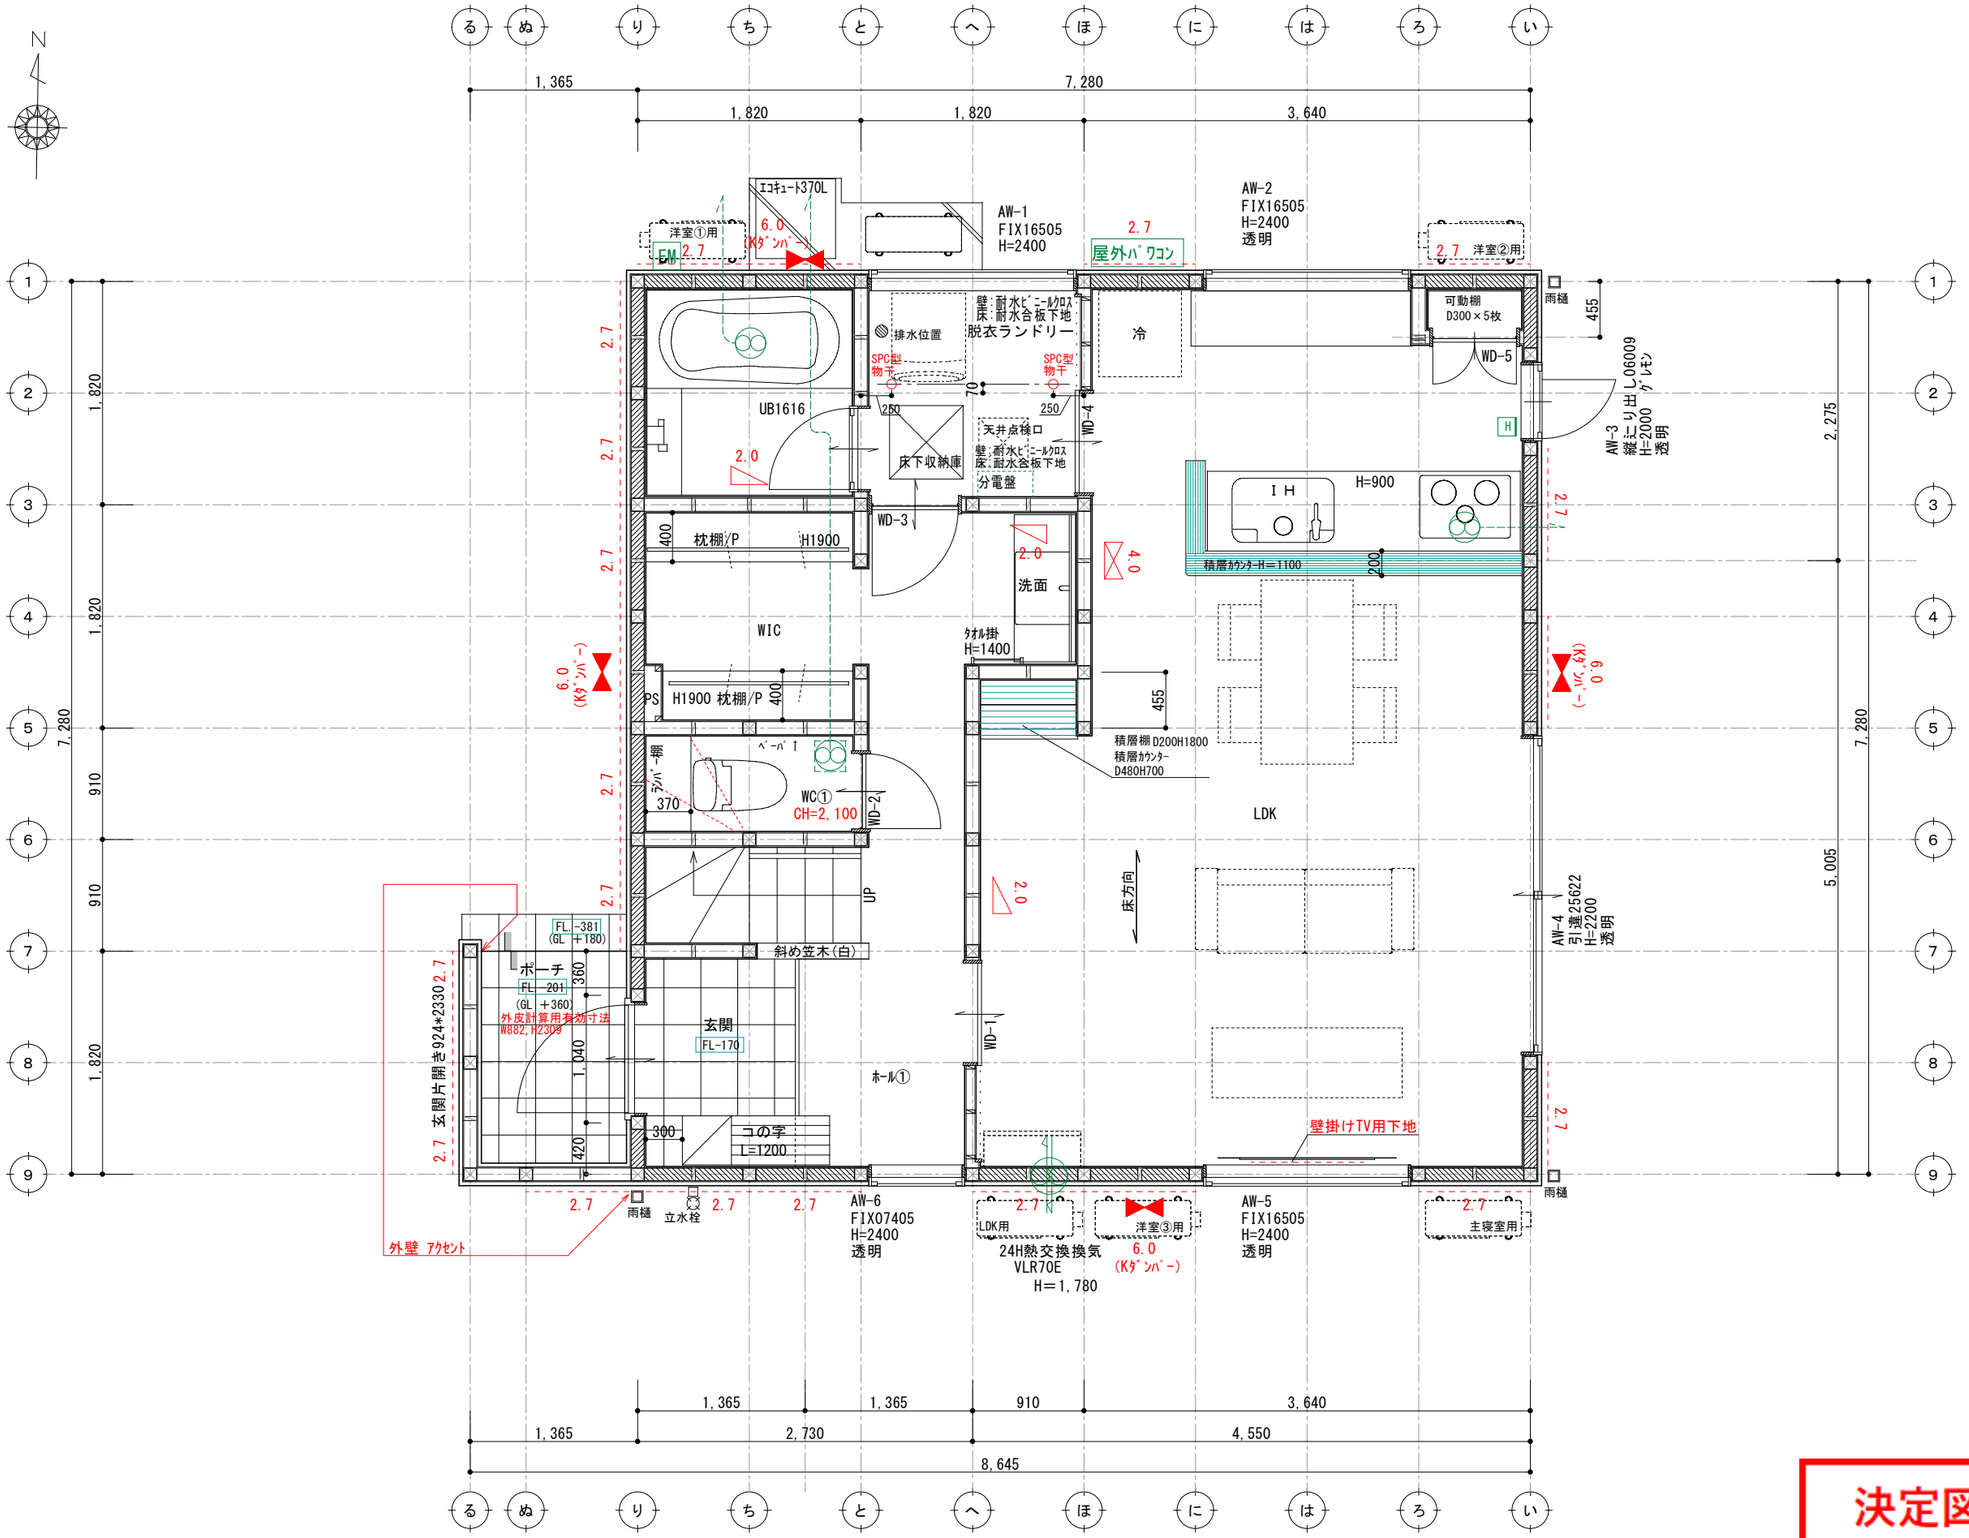

壁付け 住宅用火災報知器			数量
H 熱感知	熱感知器	電池式(単独型)	1
		露出型	

壁付け 住宅用火災報知器			数量
S 煙感知	煙感知器	電池式(単独型)	
		露出型	

※ 煙感知器は壁・梁より600mm以上離す
壁に取付ける場合、
天井から150mm以上500mm以内離す
換気扇・ｴｱｺﾝ吹出口から1500mm以上離す
※ 全室LED照明とする。
※ 標準天井高さ2,400
※ 特記無きガラスは型ガラス

＊凡例

- 管柱 (105×105)
- Kﾀﾞﾝﾊﾟｰ (3.30倍 FRM-0641)
- 片筋違い (2.00倍 45×90) (例 左:柱脚 右:柱頭)
- たすき掛筋違い (4.00倍 45×90)
- 構造用合板 (2.70倍) (t=9 ﾀｲｶﾞｰEXﾊｲﾊﾟｰ)
- 床点検口
- 天井点検口
- 換気扇
- 熱交換換気扇VLR-70

アドバンスシリーズ
スマートデザイン (外部)

凡例
- 1 コンセント 1ヶ口
- 2 コンセント 2ヶ口
- 3 コンセント 3ヶ口
- 1ET コンセント1ヶ口接地ターミナル付
- 2ET コンセント2ヶ口接地ターミナル付
- WP コンセント 防水型
- エアコン用コンセント
- 200V用コンセント
- WP 防雨入線プレート
- スイッチ
- 3 3路スイッチ
- 4 4路スイッチ
- 直結電源
- TV テレビ取出し口
- TEL 電話取出し口 (テレホンガイド)
- LAN LAN取出し口 (テレホンガイド)
- 壁照明
- リモコン(給湯関係・ルフロ)
- メーター
- 分電盤
- チャイム

決定図

※ACｺﾝｾﾝﾄ天井付け
※TVｱﾝﾃﾅ工事
※ｽｲｯﾁはFL+1100、ｺﾝｾﾝﾄはFL+200

訂正	浜岡一級総合設計事務所	PG HOUSE	株式会社 LIFEFUND InDesign office 一級建築士事務所	年月日	件名		設計	IC	工事	図番
	一級建築士事務所 静岡県知事登録第 (10)2441 号	ピージーハウス	事務所登録 (2)第7595号 一級建築士登録 第179770号 鈴木 達男	2025.5.30	鈴木和多留様・唯様 邸 新築工事		倉田		青島	3-1
	一級建築士 大臣登録第 365879 号 西原利昌		〒432-8023 静岡県浜松市中央区鴨江3丁目70番23号	縮尺 1/50	図名 1階平面図					