


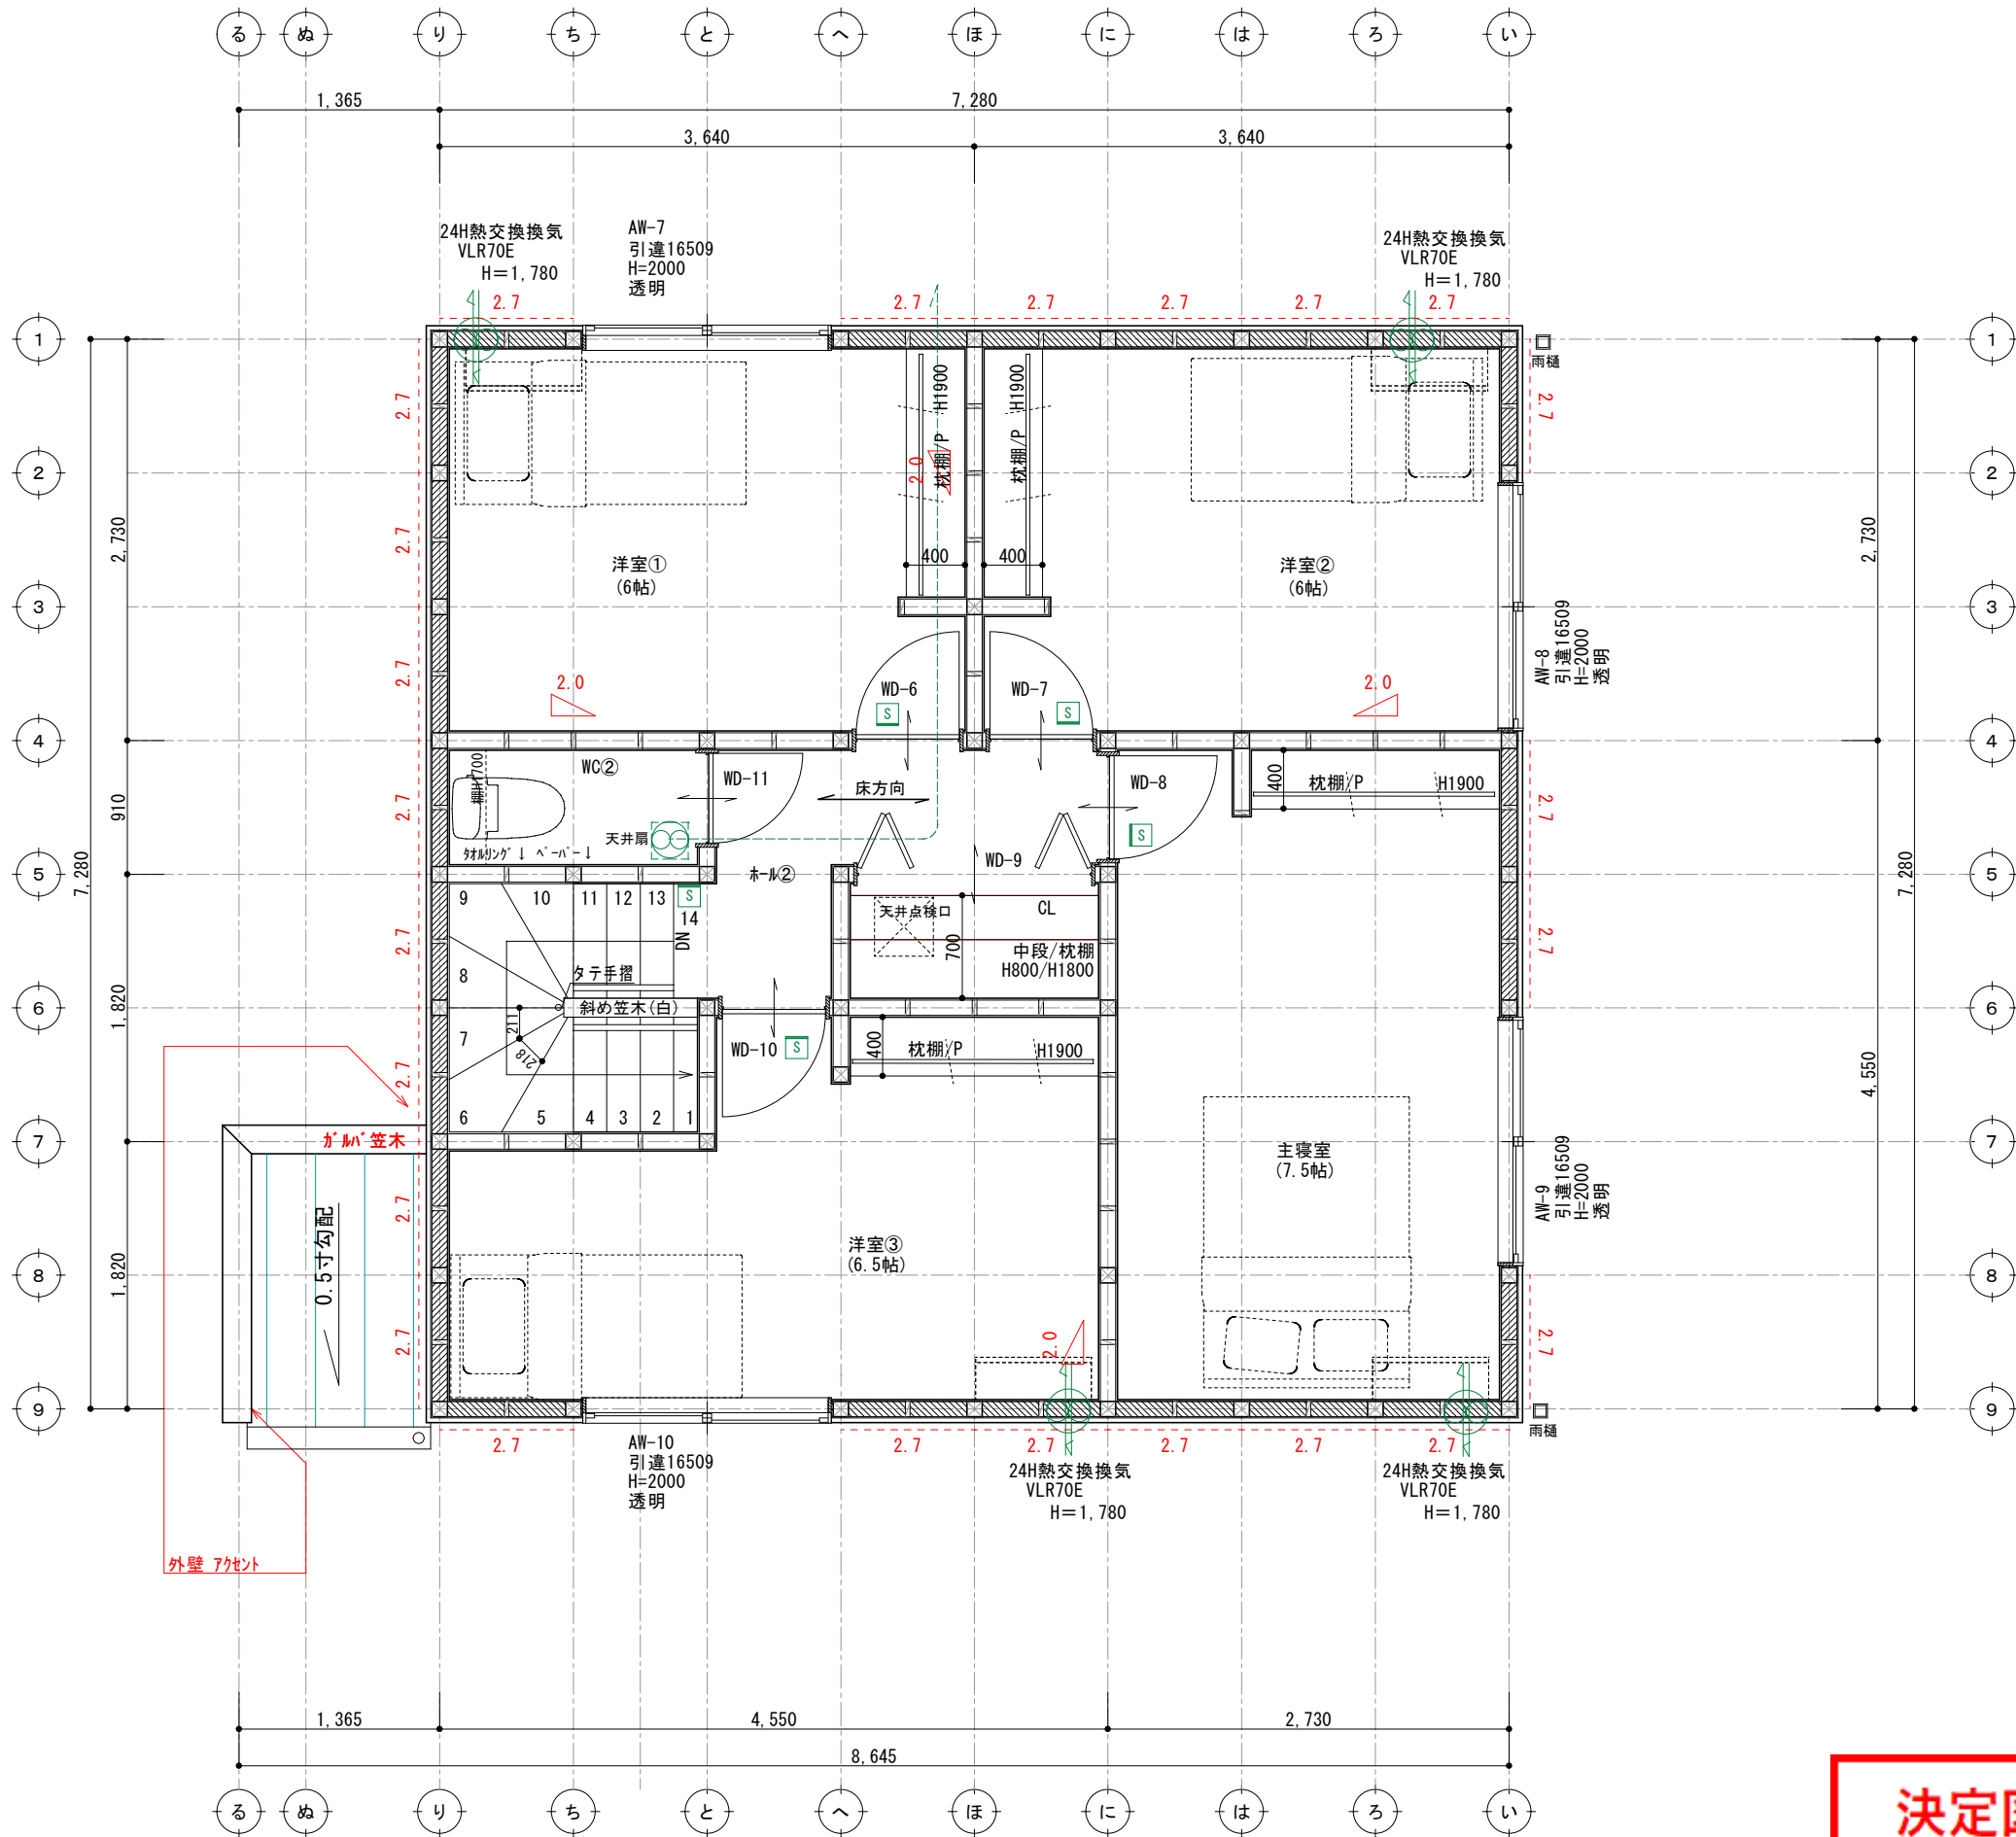

壁付け 住宅用火災報知器			数量
H 熱感知	熱感知器	電池式(単独型)	
		露出型	
壁付け 住宅用火災報知器			数量
S 煙感知	煙感知器	電池式(単独型)	4
		露出型	

※ 煙感知器は壁・梁より600mm以上離す
壁に取付ける場合、
天井から150mm以上500mm以内離す
換気扇・エアコン吹出口から1500mm以上離す

※ 全室LED照明とする。

※ 標準天井高さ2,400

※ 特記無きガラスは型ガラス

* 凡例

- 管柱 (105×105)
- Kダクト (3.30倍 FRM-0641)
- 片筋違い (2.00倍 45×90)
(例 左:柱脚 右:柱頭)
- たすき掛筋違い (4.00倍 45×90)
- 構造用合板 (2.70倍)
(t=9 3枚 EXハイパー)
- 床点検口
- 天井点検口
- 換気扇
- 熱交換換気扇VLR-70

アドバンスシリーズ

スマートデザイン (外部)

- 1 コンセント 1ヶ所
- 2 コンセント 2ヶ所
- 3 コンセント 3ヶ所
- 1ET コンセント1ヶ所接地ターミナル付
- 2ET コンセント2ヶ所接地ターミナル付
- WP コンセント 防水型
- エアコン用コンセント
- 200V用コンセント
- WP 防雨入線プレート
- スイッチ
- 3 3路スイッチ
- 4 4路スイッチ
- 直結電源
- TV テレビ取出口
- TEL 電話取出口 (テレホンガイド)
- LAN LAN取出口 (テレホンガイド)
- 壁照明
- リモコン (給湯関係・ルフロ)
- メーター
- 分電盤
- チャイム

※ACコンセント天井付け
※TVアンテナ工事
※スイッチはFL+1100、コンセントはFL+200

決定図

訂正	浜岡一級総合設計事務所 一級建築士事務所 静岡県知事登録第 (10)2441 号 一級建築士 大臣登録第 365879 号 西原利昌	PG HOUSE ピージーハウス	株式会社 LIFEFUND InDesign office 一級建築士事務所 事務所登録 (2) 第7595号 一級建築士登録 第179770号 鈴木 達男 〒432-8023 静岡県浜松市中央区鴨江3丁目70番23号	年月日 2025. 5. 30	件名 鈴木和多留様・唯様 邸 新築工事	設計 倉田	IC	工事 青島	図番 3-2
				縮尺 1/50	図名 2階平面図				