


太陽光パネル有

G 1

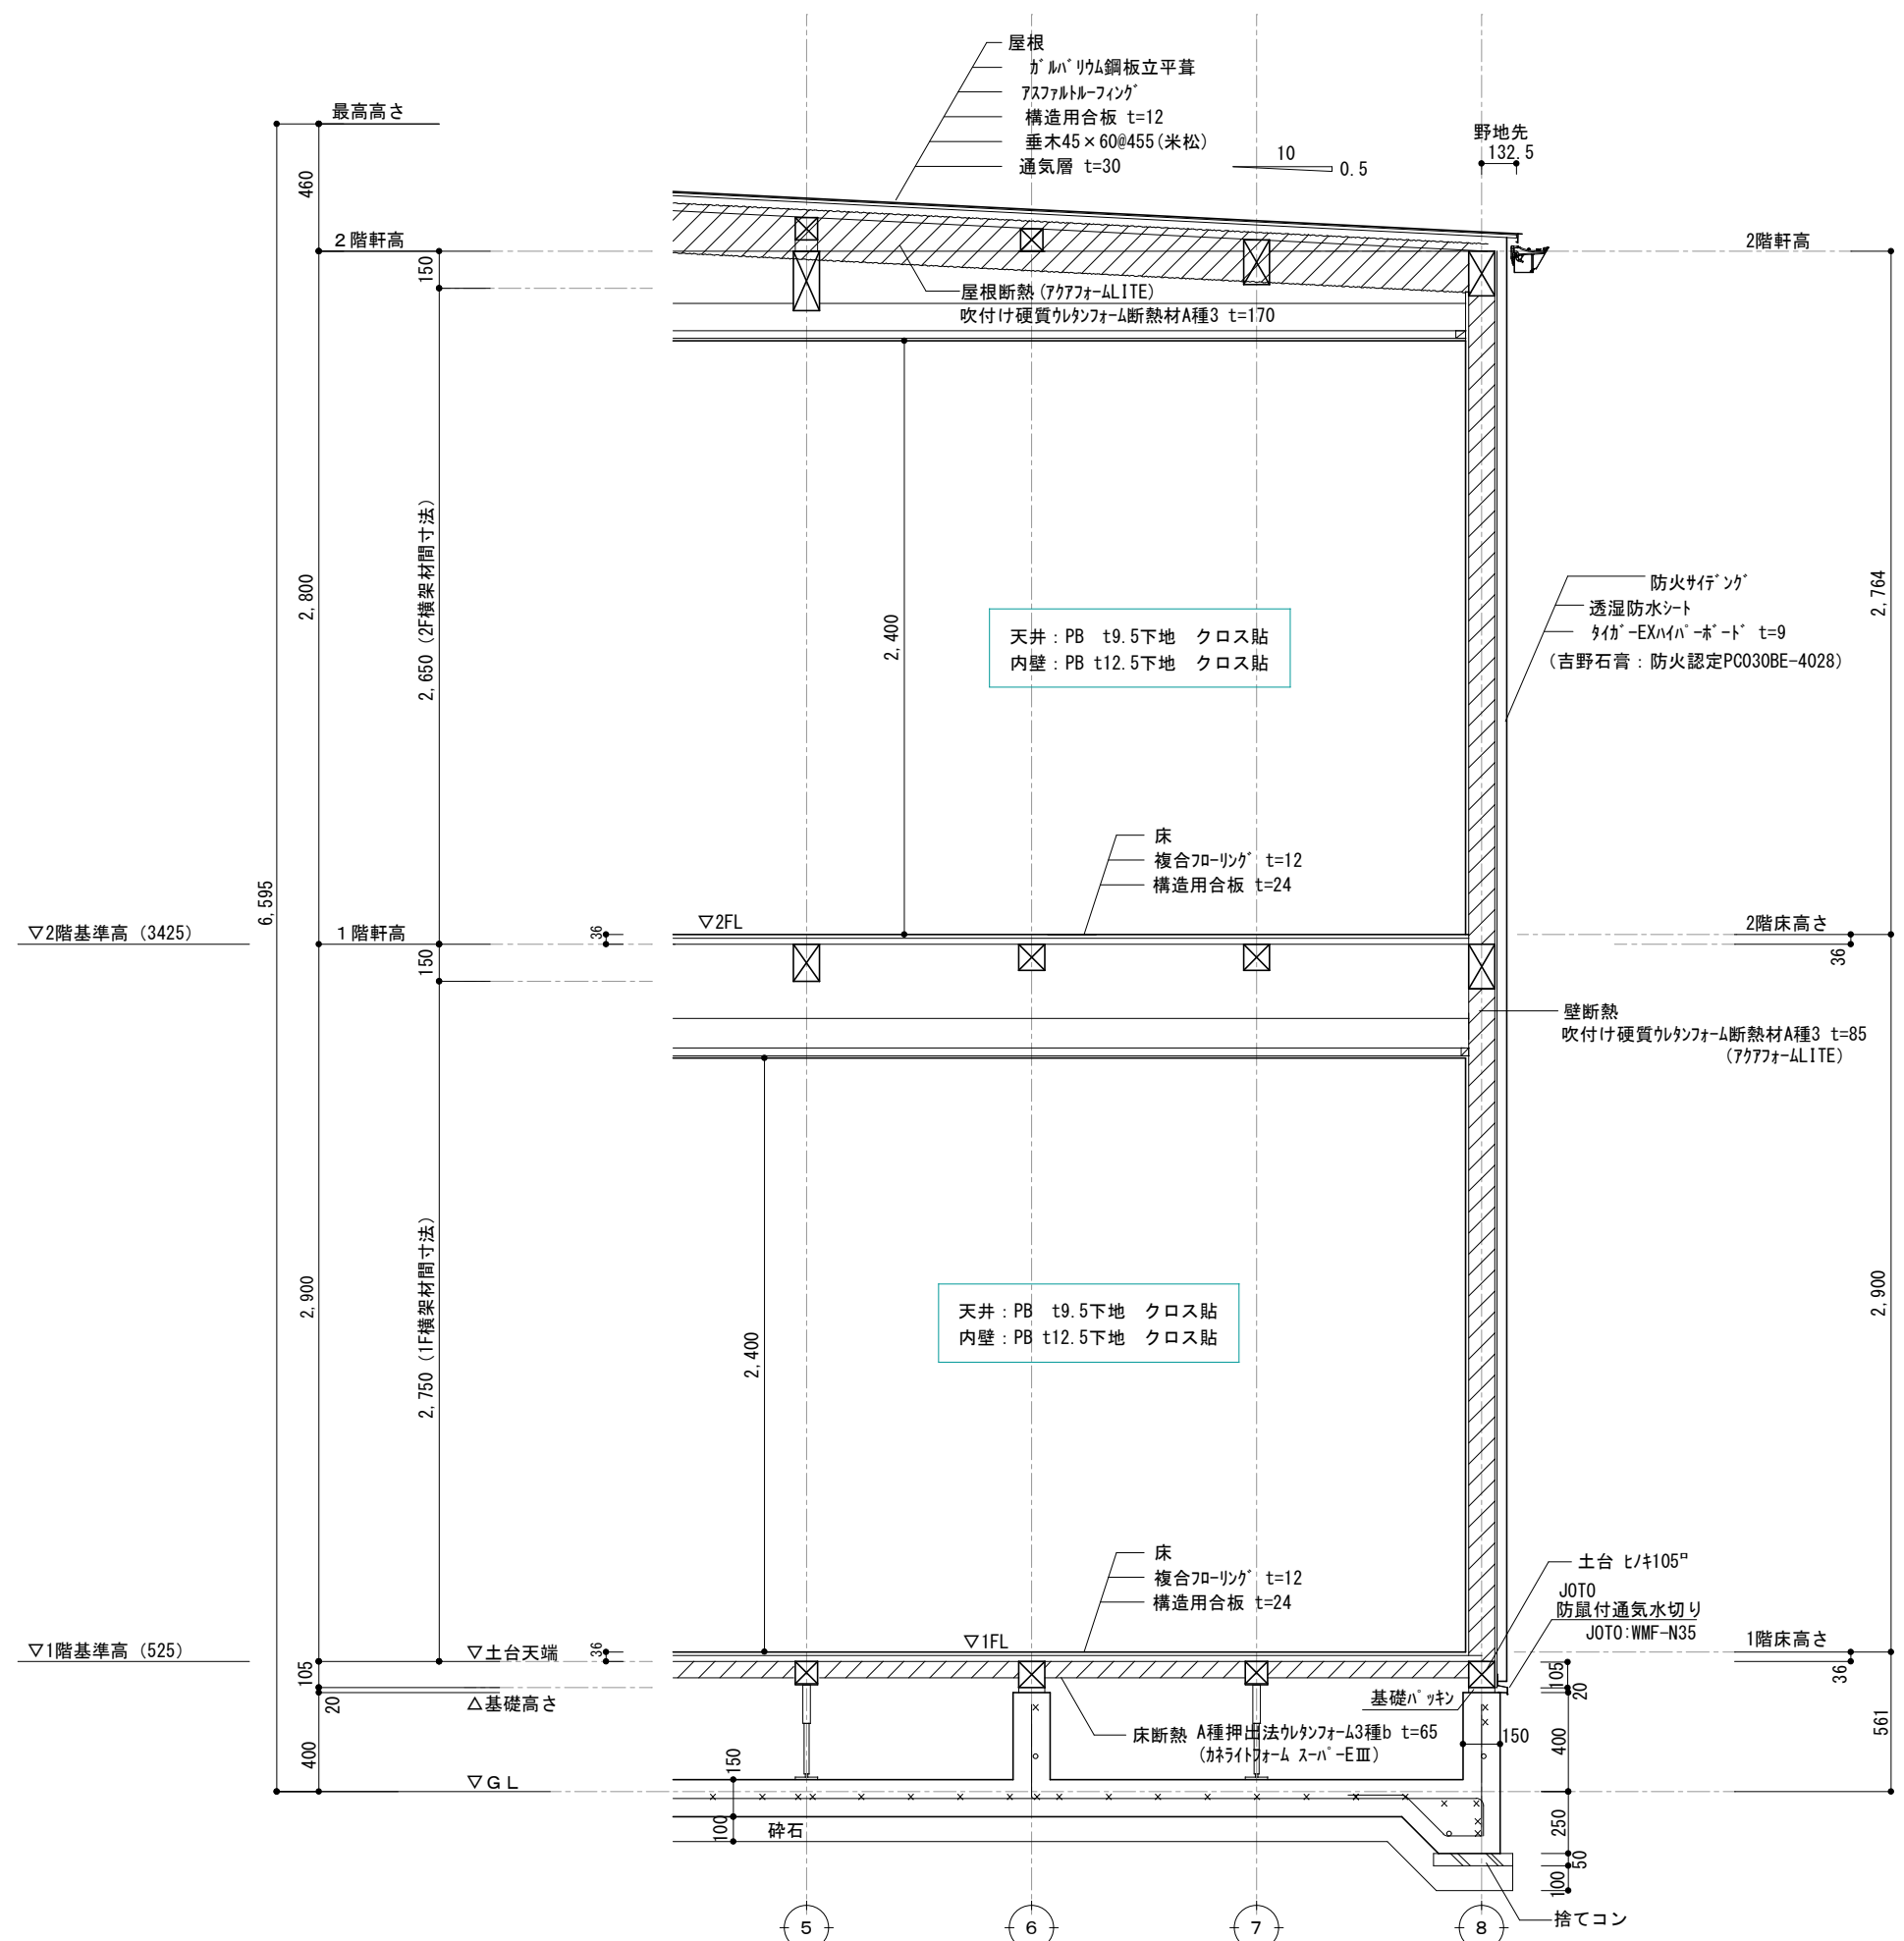

決定図

訂正	浜岡一級総合設計事務所 一級建築士事務所 静岡県知事登録第 (10)2441 号 一級建築士 大臣登録第 365879 号 西原利昌	PG HOUSE ピージーハウス	株式会社 LIFEFUND InDesign office 一級建築士事務所 事務所登録 (2) 第7595号 一級建築士登録 第179770号 鈴木 達男 〒432-8023 静岡県浜松市中央区鴨江3丁目70番23号	年月日 2025. 5. 30 縮尺 1/30	件名 鈴木和多留様・唯様 邸新築工事 図名 矩計図	設計 倉田	IC	工事 青島	図番 A-5
----	--	---------------------	---	----------------------------------	------------------------------------	----------	----	----------	-----------