


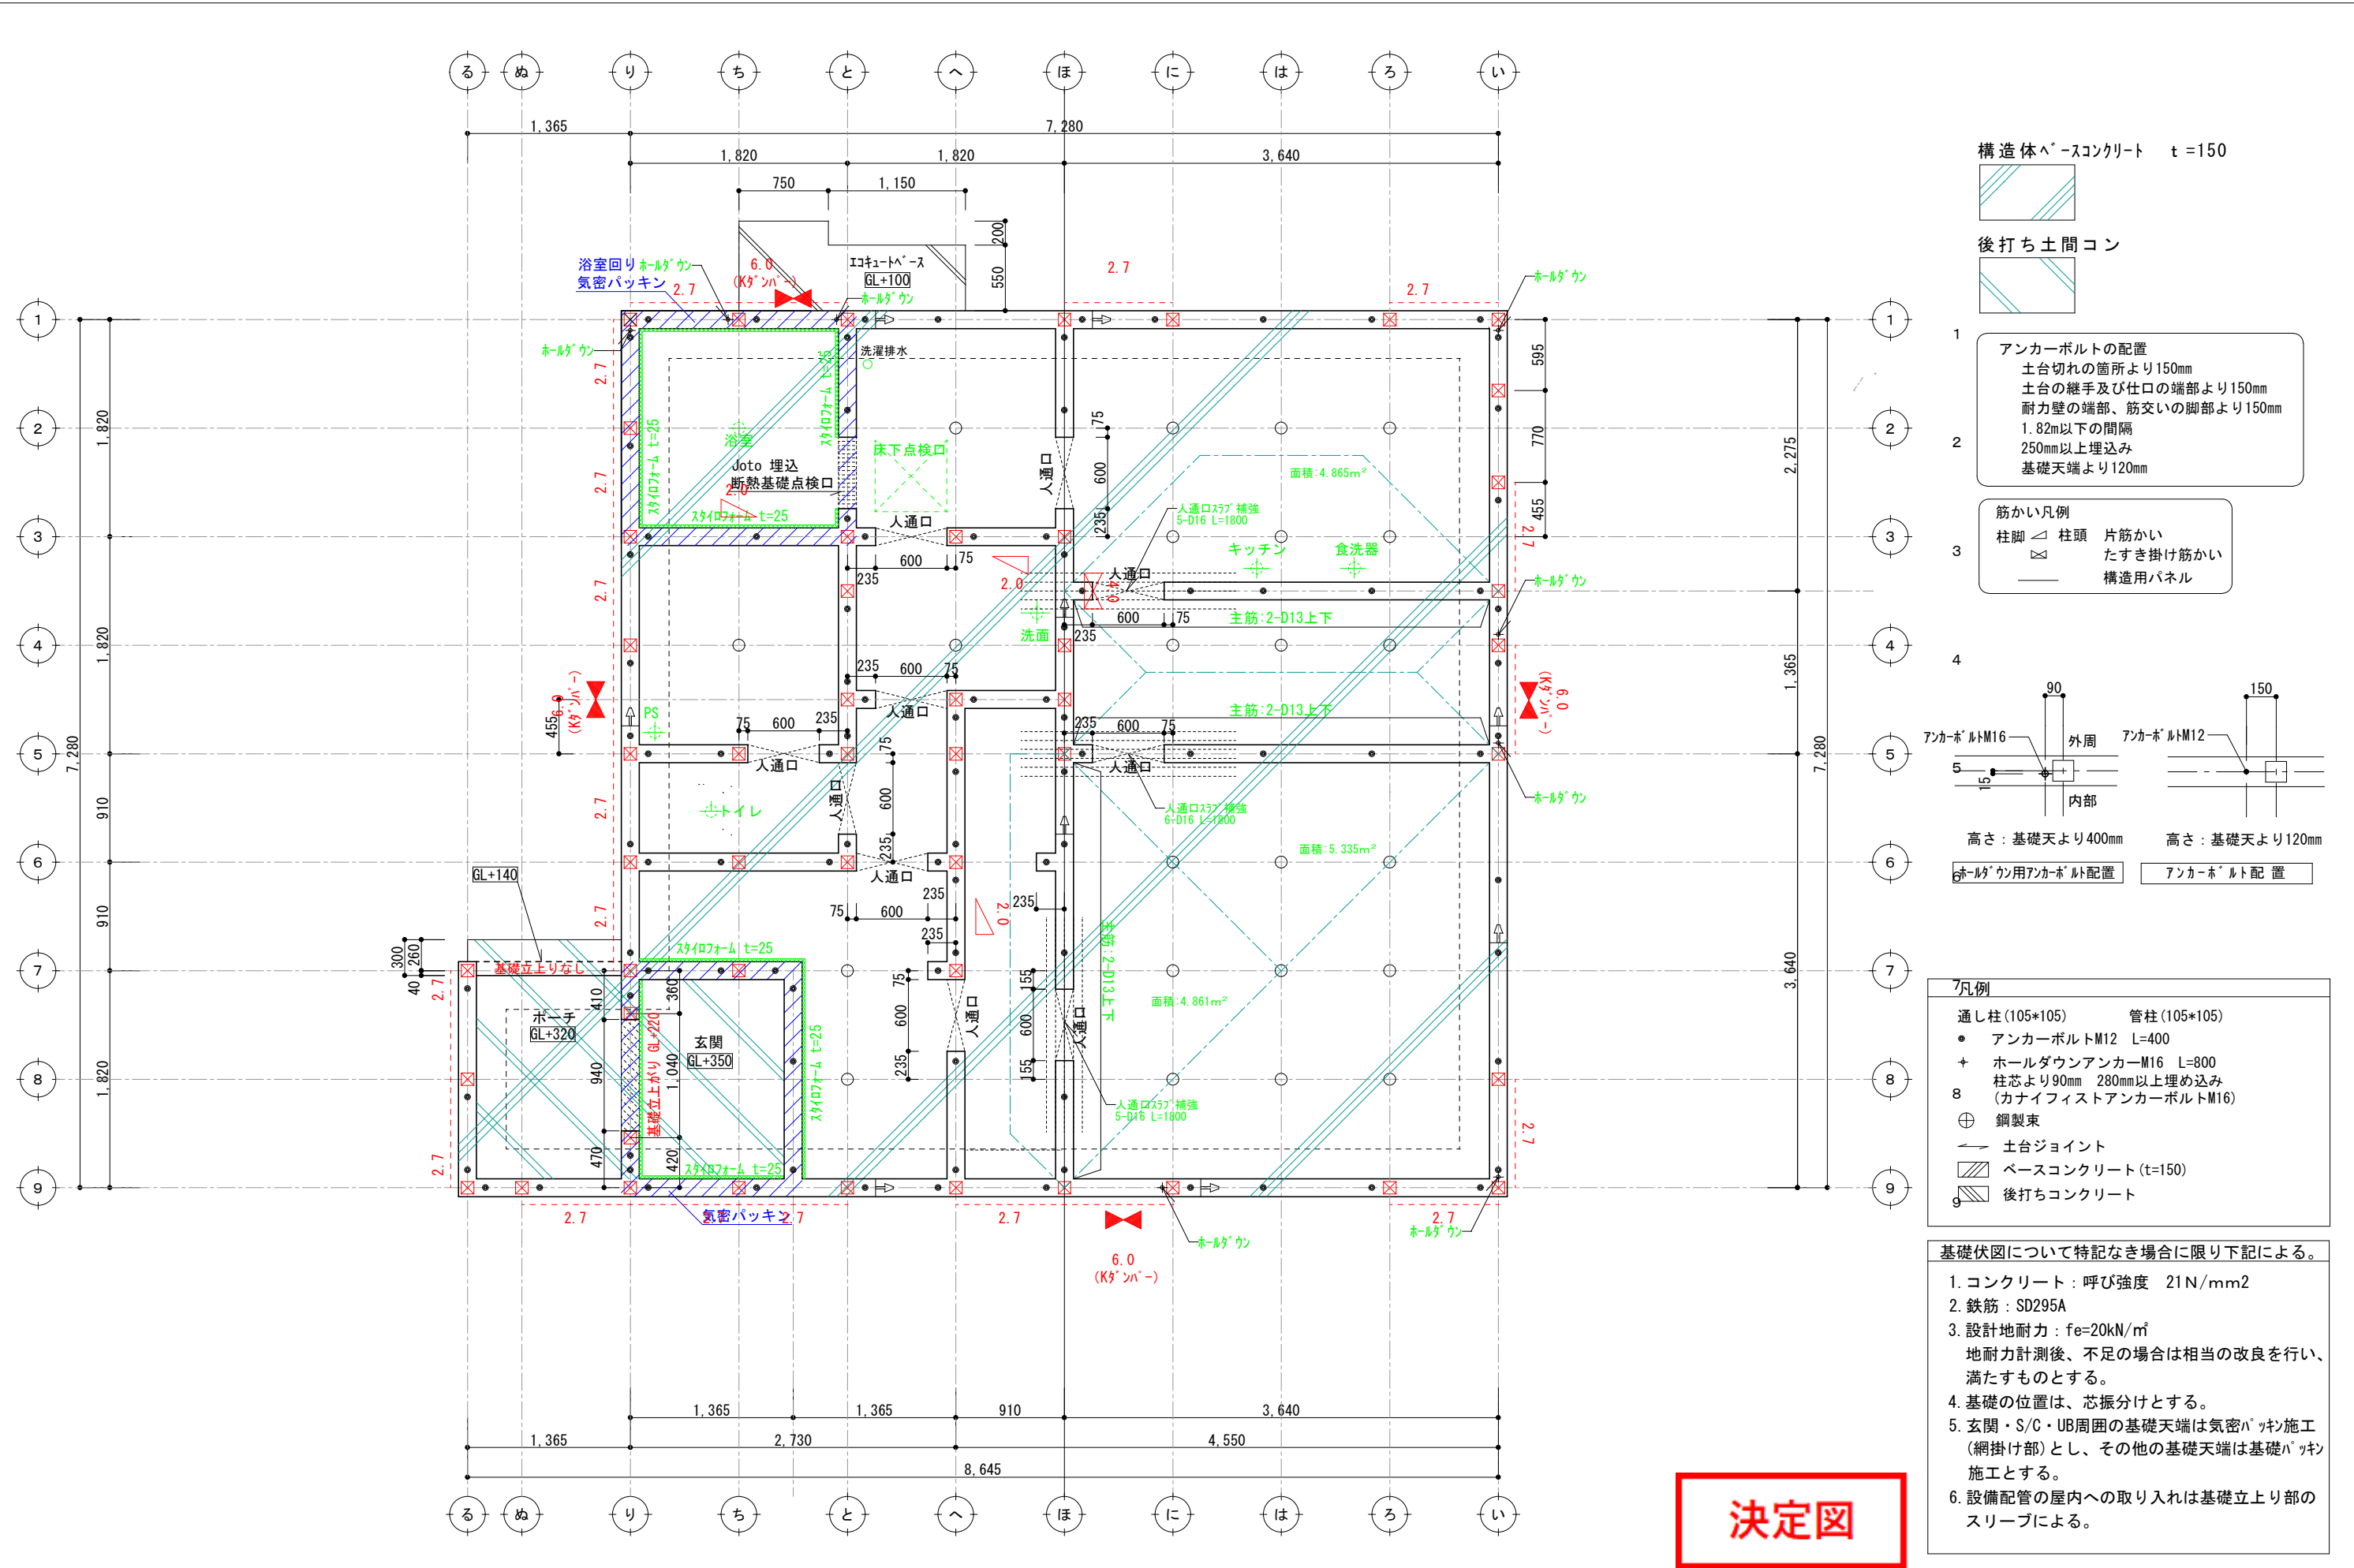

構造体ベースコンクリート t=150

後打ち土間コン

アンカーボルトの配置

土台切れの箇所より150mm

土台の継手及び仕口の端部より150mm

耐力壁の端部、筋交いの脚部より150mm

1.82m以下の間隔

250mm以上埋込み

基礎天端より120mm

筋かい凡例

柱脚 柱頭 片筋かい 片筋かい

たすき掛け筋かい 構造用パネル

7 凡例

通し柱 (105*105) 管柱 (105*105)

- アンカーボルト M12 L=400
- + ホールダウンアンカー M16 L=800
- 柱芯より90mm 280mm以上埋め込み (カナイフリストアンカーボルト M16)
- ⊕ 鋼製束
- 土台ジョイント
- ▨ ベースコンクリート (t=150)
- ▨ 後打ちコンクリート

基礎伏図について特記なき場合に限り下記による。

- コンクリート：呼び強度 21N/mm²
- 鉄筋：SD295A
- 設計地耐力：fe=20kN/m²
地耐力計測後、不足の場合は相当の改良を行い、満たすものとする。
- 基礎の位置は、芯振分けとする。
- 玄関・S/C・UB周囲の基礎天端は気密パッキン施工 (網掛け部) とし、その他の基礎天端は基礎パッキン施工とする。
- 設備配管の屋内への取り入れは基礎立上り部のスリーブによる。

決定図