



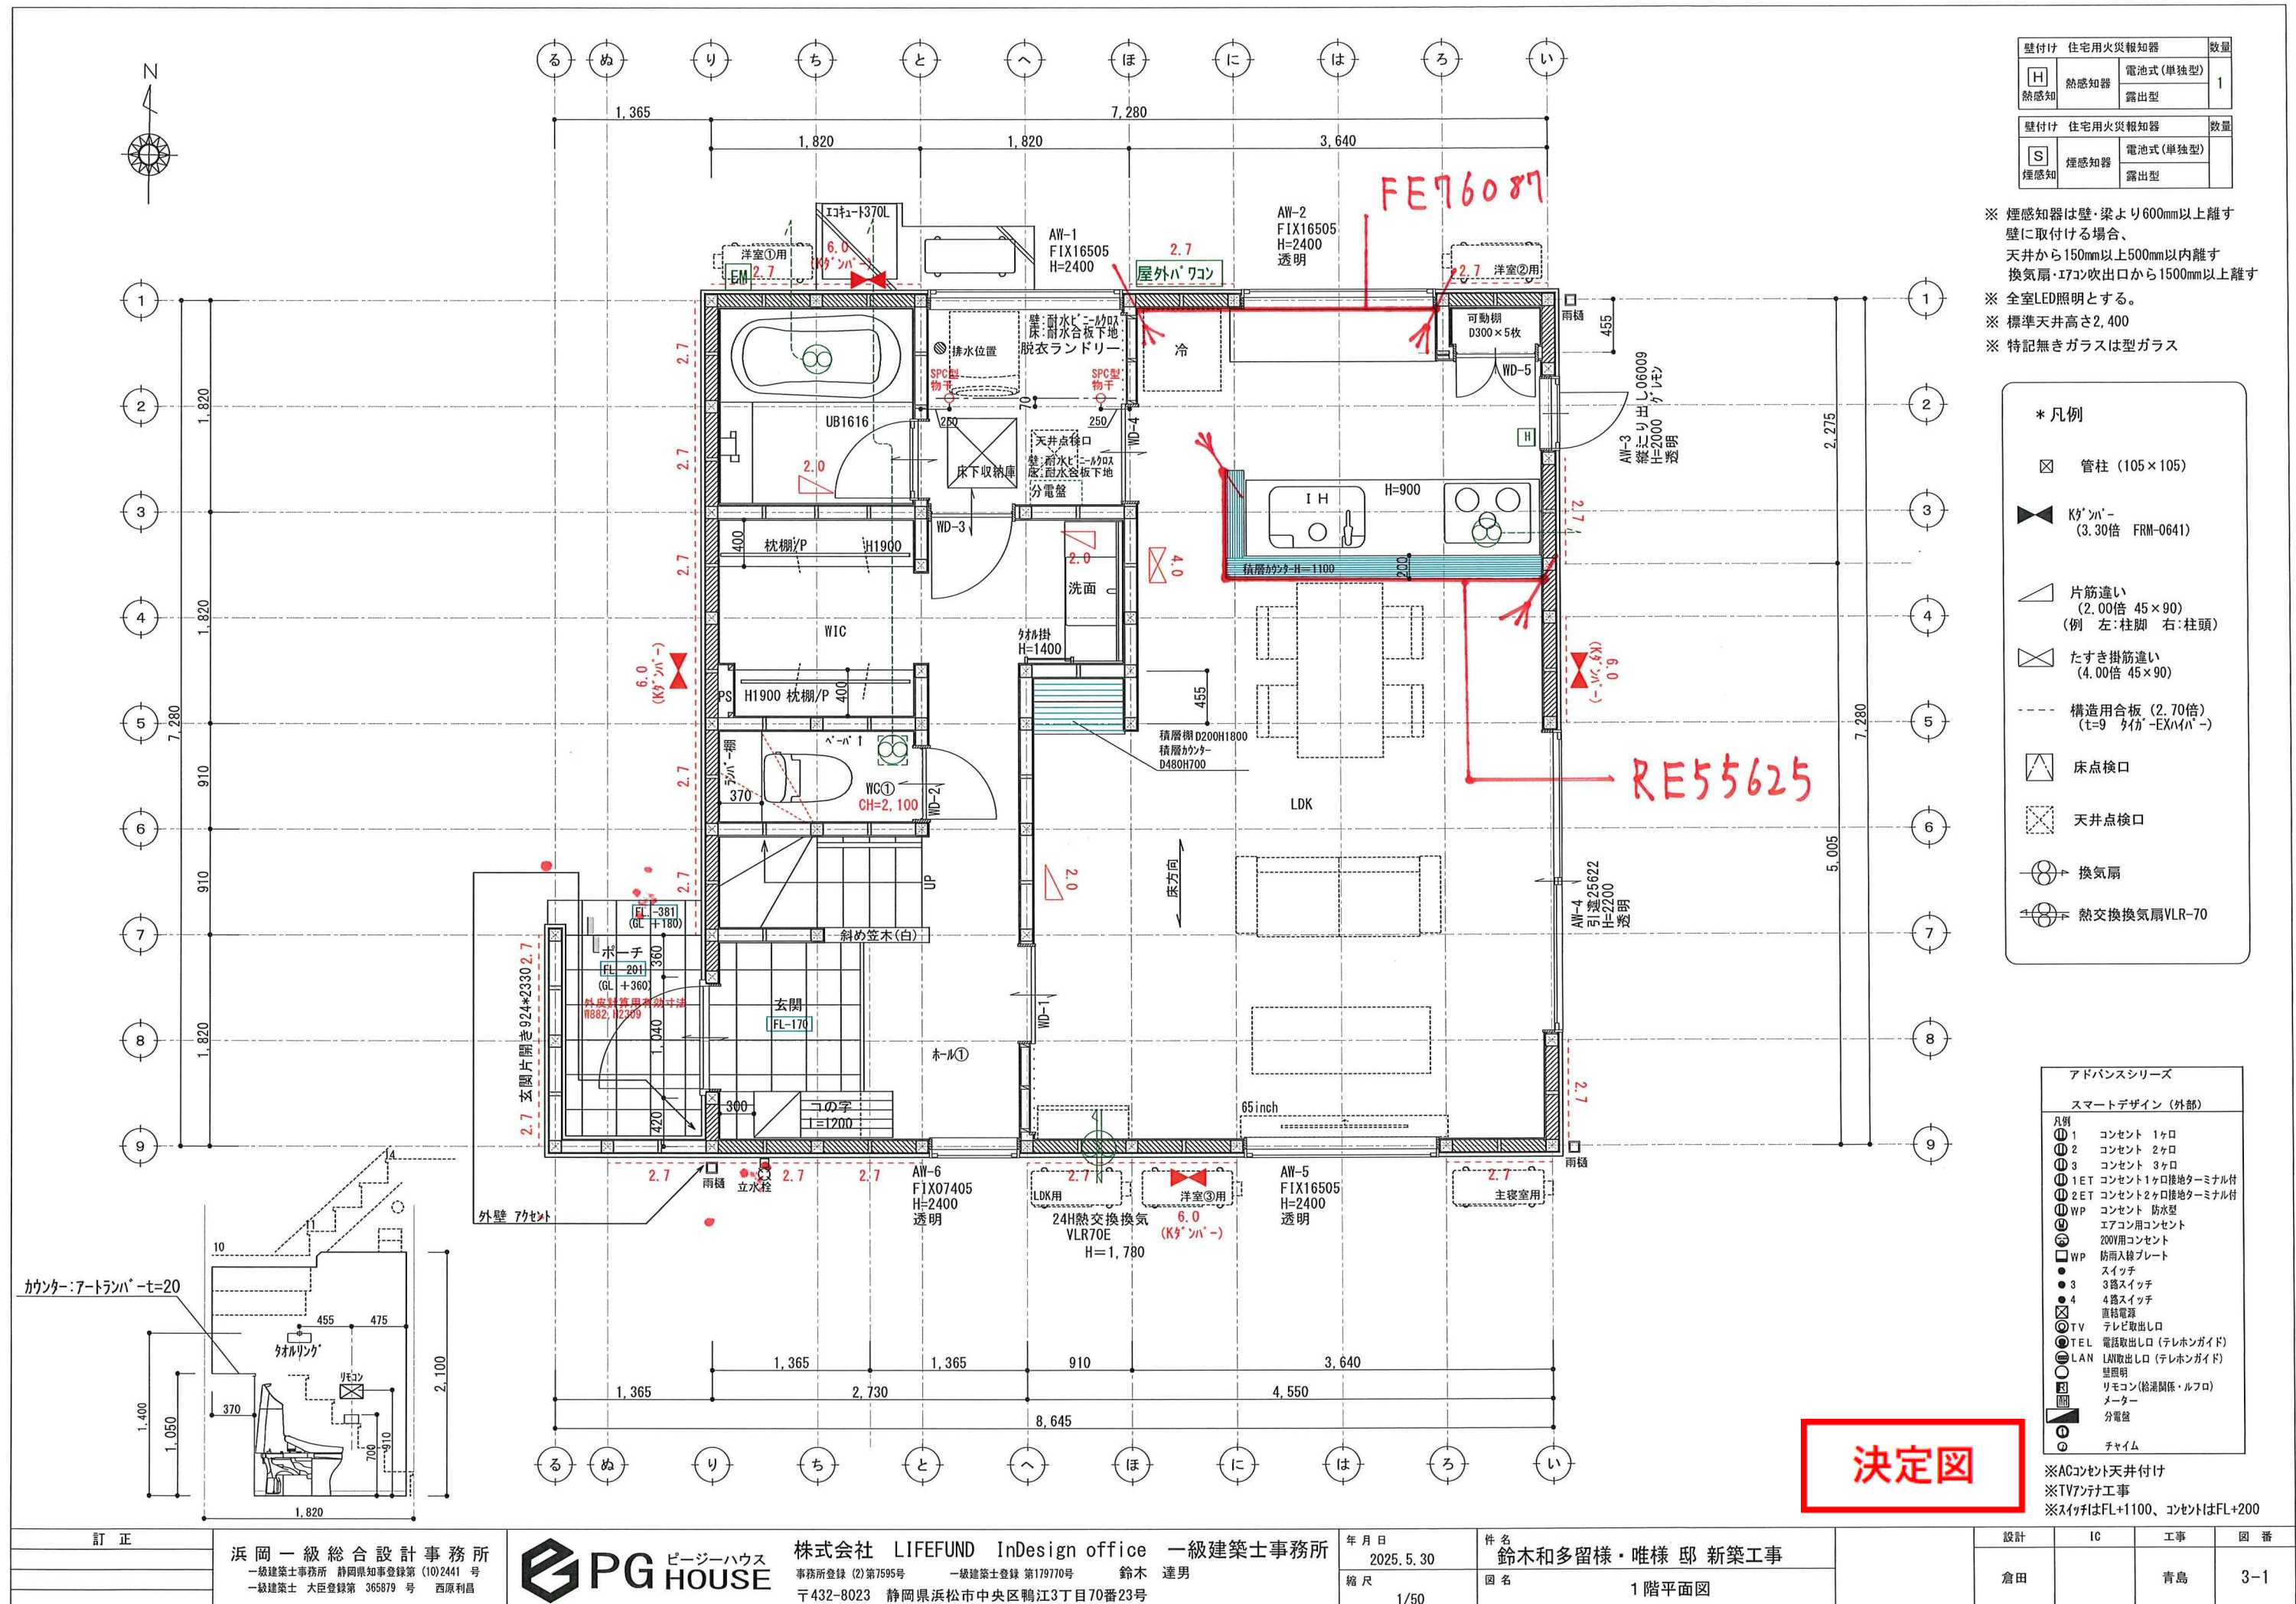

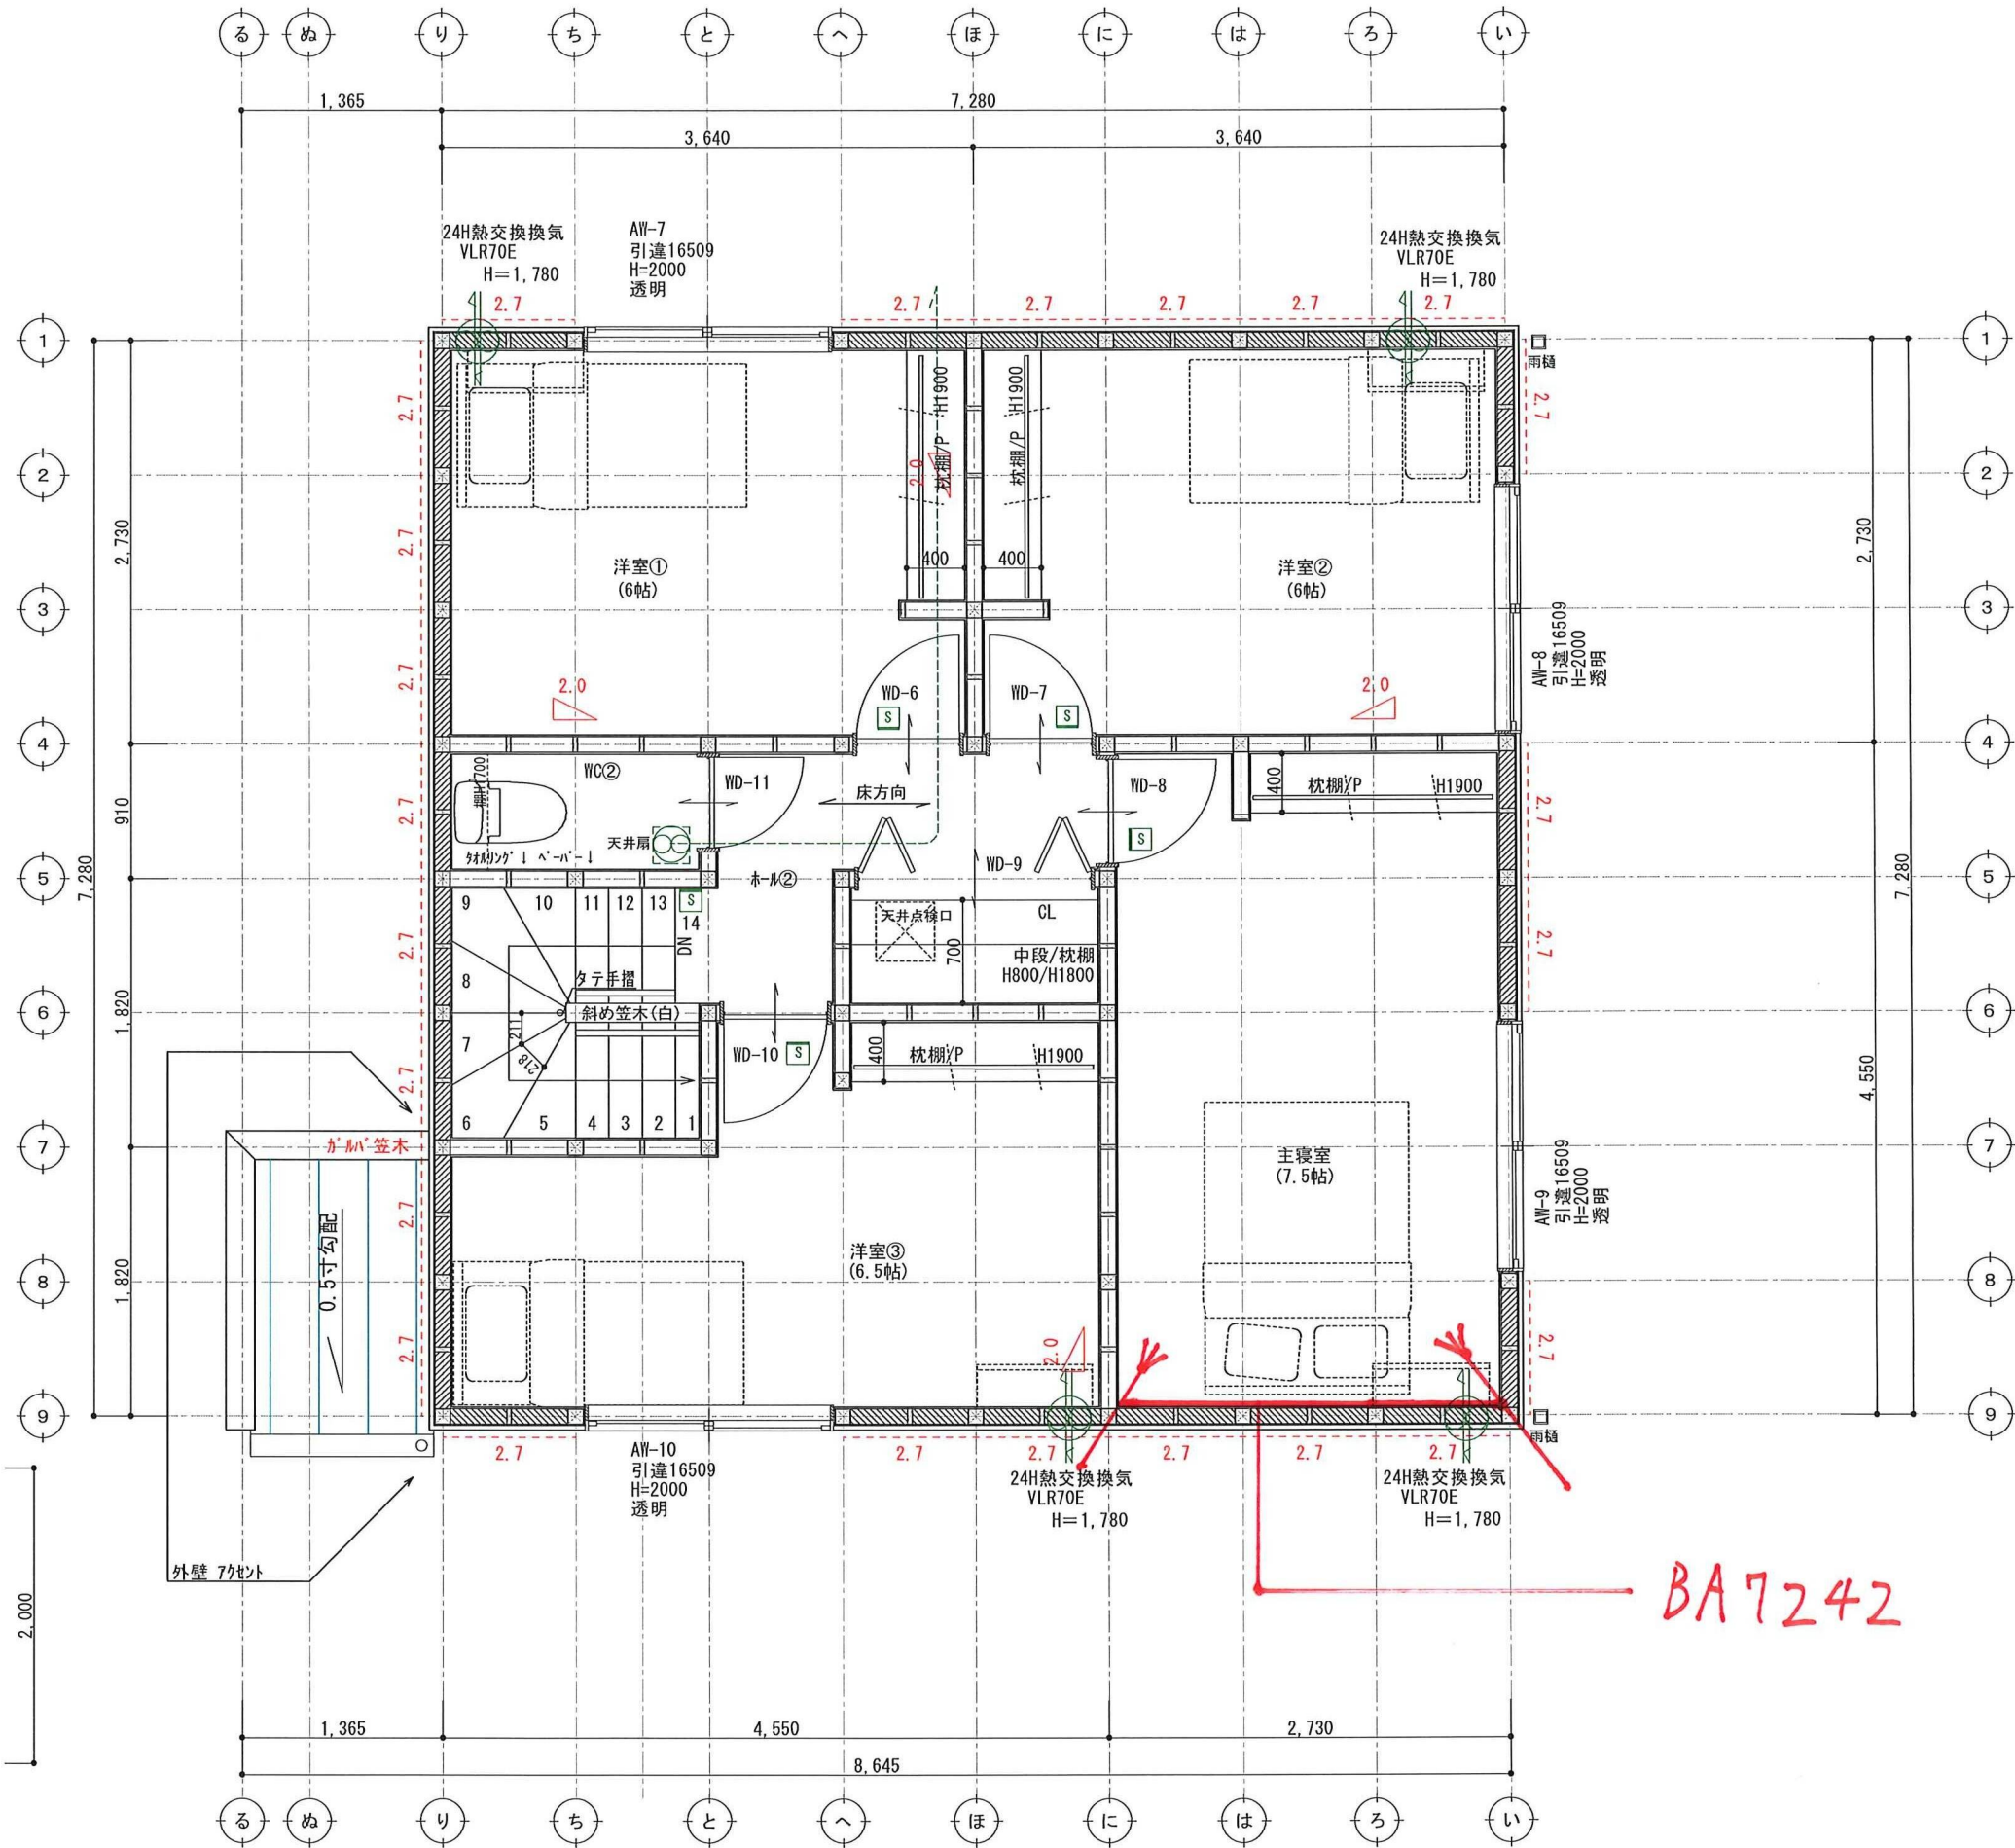

壁付付 住宅用火災報知器			数量
H 熱感知	熱感知器	電池式(単独型)	
		露出型	
壁付付 住宅用火災報知器			数量
S 煙感知	煙感知器	電池式(単独型)	4
		露出型	

※ 煙感知器は壁・梁より600mm以上離す
壁に取付ける場合、
天井から150mm以上500mm以内離す
換気扇・エアコン吹出口から1500mm以上離す
※ 全室LED照明とする。
※ 標準天井高さ2,400
※ 特記無きガラスは型ガラス

* 凡例	
☒	管柱 (105×105)
◀▶	K'パ- (3.30倍 FRM-0641)
△	片筋違い (2.00倍 45×90) (例 左:柱脚 右:柱頭)
⊗	たすき掛筋違い (4.00倍 45×90)
---	構造用合板 (2.70倍) (t=9 タイパ-EXハイパ-)
△	床点検口
⊗	天井点検口
↻	換気扇
↻	熱交換換気扇VLR-70

アドバンスシリーズ	
スマートデザイン (外部)	
凡例	
①	コンセント 1ヶ所
②	コンセント 2ヶ所
③	コンセント 3ヶ所
①ET	コンセント1ヶ所接地ターミナル付
②ET	コンセント2ヶ所接地ターミナル付
①WP	コンセント 防水型
②WP	エアコン用コンセント
③WP	200V用コンセント
WP	防雨入替プレート
●	スイッチ
●3	3路スイッチ
●4	4路スイッチ
⊗	直結電源
⊗TV	テレビ取出口
⊗TEL	電話取出口 (テレホンガイド)
⊗LAN	LAN取出口 (テレホンガイド)
⊗	壁照明
⊗	リモコン (給湯関係・ルフロ)
⊗	メーター
⊗	分電盤
⊗	チャイム

※ACコンセント天井付け
※TVアンテナ工事
※スイッチはFL+1100、コンセントはFL+200

