


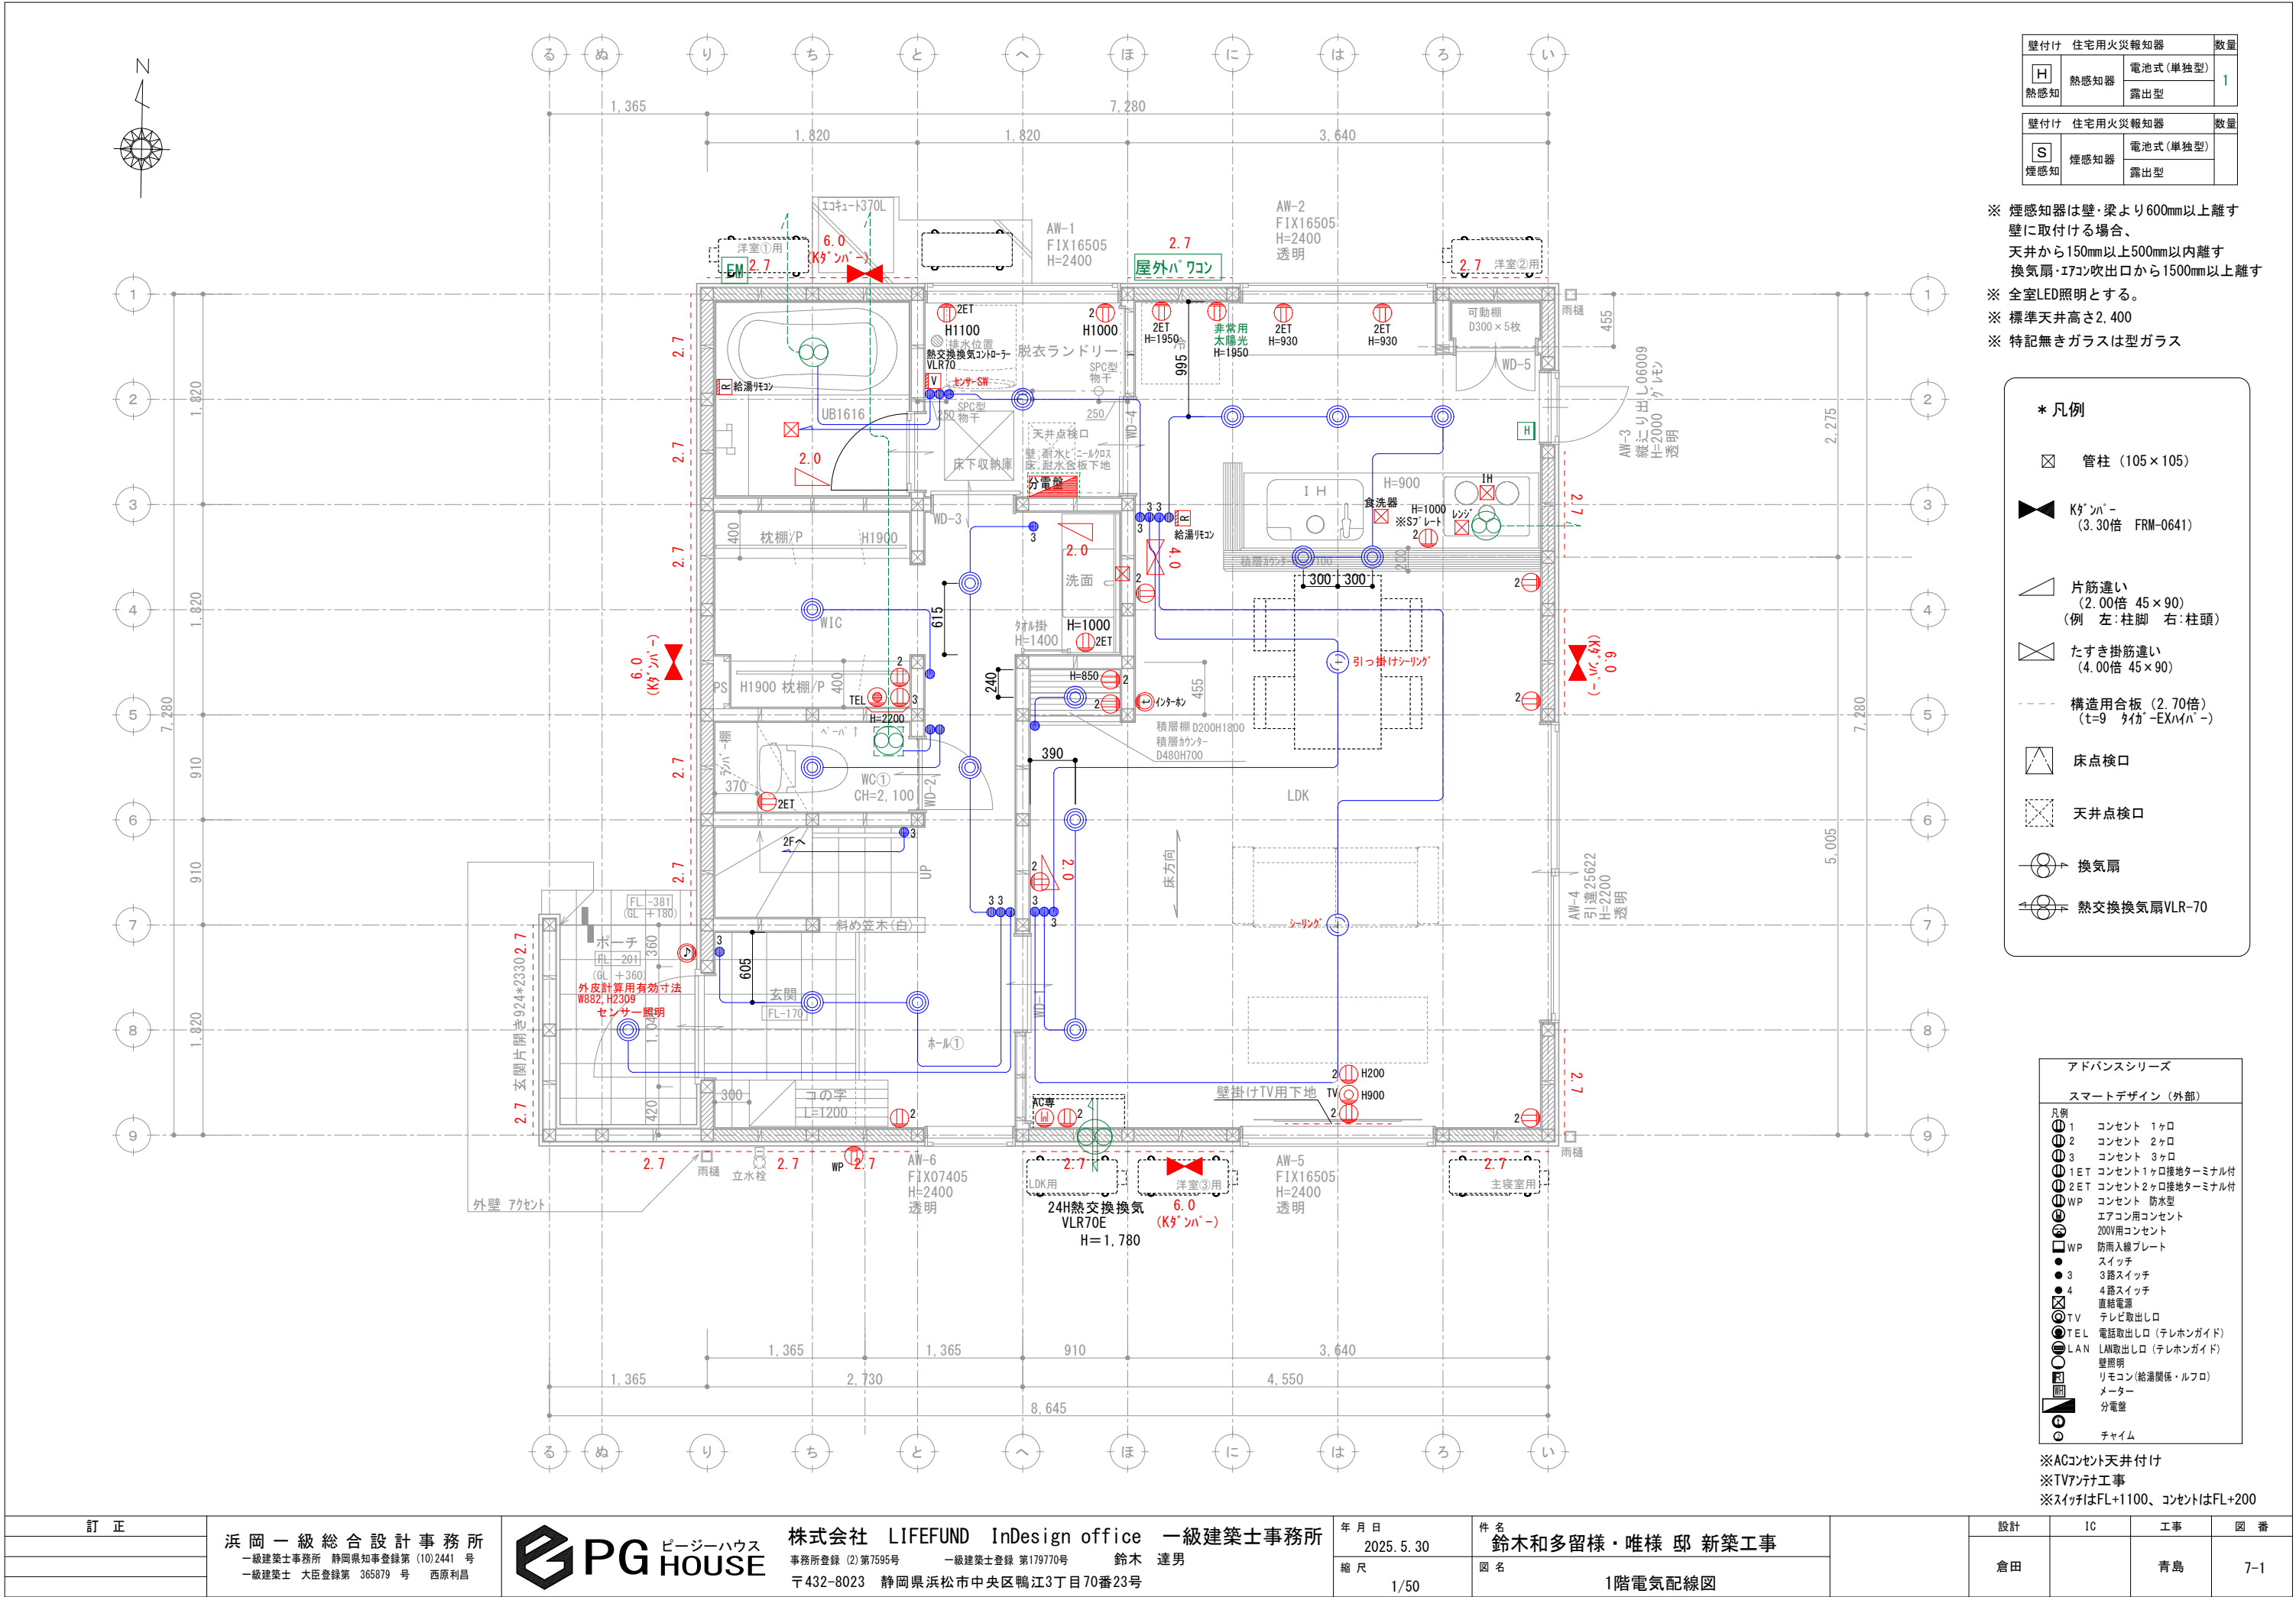

壁付け 住宅用火災報知器			数量
H 熱感知	熱感知器	電池式 (单独型)	1
		露出型	
壁付け 住宅用火災報知器			数量
S 煙感知	煙感知器	電池式 (单独型)	
		露出型	

※ 煙感知器は壁・梁より600mm以上離す
壁に取付ける場合、
天井から150mm以上500mm以内離す
換気扇・エアコン吹出口から1500mm以上離す

※ 全室LED照明とする。

※ 標準天井高さ2,400

※ 特記無きガラスは型ガラス

*** 凡例**

管柱 (105×105)

Kダクト (3.30倍 FRM-0641)

片筋違い (2.00倍 45×90)
(例 左:柱脚 右:柱頭)

たすき掛筋違い (4.00倍 45×90)

構造用合板 (2.70倍)
(t=9 材種-EXハイパー)

床点検口

天井点検口

換気扇

熱交換換気扇 VLR-70

アドバンスシリーズ			
スマートデザイン (外部)			
凡例	1	コンセント	1ヶ所
2	コンセント	2ヶ所	
3	コンセント	3ヶ所	
1ET	コンセント1ヶ所接地ターミナル付		
2ET	コンセント2ヶ所接地ターミナル付		
WP	コンセント 防水型		
EA	エアコン用コンセント		
200V	200V用コンセント		
WP	防雨入線プレート		
スイッチ	スイッチ		
3	3路スイッチ		
4	4路スイッチ		
直結電源	直結電源		
TV	テレビ取出口		
TEL	電話取出口 (テレホンガイド)		
LAN	LAN取出口 (テレホンガイド)		
壁照明	壁照明		
リモコン	リモコン (給湯関係・ルフロ)		
メーター	メーター		
分電盤	分電盤		
チャイム	チャイム		

※ACコンセント天井付け
※TVアンテナ工事
※スイッチはFL+1100、コンセントはFL+200