


| ■ 仕 様       |                   |   |                              | ■ HEAT20 G1                                        |  |
|-------------|-------------------|---|------------------------------|----------------------------------------------------|--|
| 断熱工事        |                   | ■ 床:カネライトフォーム t65                      ■ 土間床等の外周:スタイロフォームAT t25<br>■ 壁:アクアフォームLITE吹付 t85                      ■ 天井:アクファフォームLITE吹付 t170 |                              |                                                    |  |
| 床下換気        |                   | ■ 基礎パッキン                      JOTO                      (玄関・UB周り:気密基礎パッキン)                                                             |                              |                                                    |  |
| 防虫防蟻        |                   | ■ 土壌処理・木部                      ガントナーMC                                                                                                 |                              |                                                    |  |
| ■ 外 部 仕 上 表 |                   |   |                              | ■ 22条地域                                            |  |
| 部位          |                   | 仕上・仕様・メーカー   |                              | 色番・品番                                              |  |
| 屋根          |                   | ■ ガルバリウム鋼板(t0.35)UK立平 ニスクカラーPro GH<br>軒先通気金物 日本住環境株式会社【REV-15】                                                                         |                              | GHK01 Sブラック                                        |  |
| パラペット笠木     |                   | ■ ガルバリウム鋼板   |                              | GHK01 Sブラック                                        |  |
| 破風・鼻隠       |                   | ■ なし   |                              |                                                    |  |
| 雨樋          | (軒樋)              | ■ Panasonic サーフেসケアFS-I型   |                              | ブラック                                               |  |
|             | (縦樋)              | ■ Panasonic S30角樋   |                              | ブラック                                               |  |
| 軒天          | 屋根軒               | ■   |                              |                                                    |  |
|             | ポーチ軒              | ■ 神島化学 t= 6mm 軒天ボード エンボス   |                              | Wチャコールブラック                                         |  |
|             | バルコニー軒            | ■   |                              |                                                    |  |
| オーバーハング水切り  |                   | ■ ガルバリウム鋼板 ※外壁合わせ JOTO:HF-A3550   |                              | ブラック                                               |  |
| 外壁          | 通気金物(15mm)        | ■メイン   | Kmewエクセレージ・シックイフラット          | ラントダークグレー                                          |  |
|             | ※下地面材:タイガーEXハイパー  | ■アクセントA   | Kmew FLAT DESIGN PANEL フィエルテ | QFフィエルテ チタン アイロン                                   |  |
|             | 防火認定 PC030BE-4028 | ■アクセントB   | なし                           |                                                    |  |
| ポーチ         |                   | ■ 床 玄関に同じ   |                              | -                                                  |  |
| 基礎          |                   | ■ 立上り巾木: モルタル刷毛引き   |                              | -                                                  |  |
| 基礎水切り金物     |                   | ■ JOTO鋼板製 防鼠材付き水切り JOTO:WMF-N35   |                              | ブラック                                               |  |
| バルコニー       | 床・内壁              | ■ なし   |                              | -                                                  |  |
|             | 笠木                | ■ なし   |                              |                                                    |  |
| 外部建具        |                   | ■ LIXIL EW(アルゴンガス高遮熱仕様LowE複層ガラス グリーン)<br>・SD、TSは、メーカー設定によるが、オペレーターハンドル優先とする<br>・オペレーター付サッシの場合は固定網戸とする<br>・グレモンハンドル式サッシの場合は可動網戸とする      |                              | 外観 ブラック<br>内観 ホワイト<br>※樹脂パッキン・網戸付                  |  |
| シャッター       |                   | ■ なし   |                              |                                                    |  |
| 軒天通気金物      |                   |   |                              | ブラック                                               |  |
| 玄関扉         |                   | ■ LIXIL ジエスタ2 K2仕様<br>LIXILファミロック タグキー×3 (電池式)                                                                                         |                              | ドア型: M17 型<br>ドア色: チーク浮造<br>ハンドル: S型ハンドル<br>色 ブラック |  |
|             |                   |   |                              |                                                    |  |
| 外部物干し金物     |                   | ■   |                              |                                                    |  |
|             |                   |   |                              |                                                    |  |
| 換気フード       |                   | ■ 局所換気扇(トイレ 浴室 キッチンフード)<br>防火ダンパー無   |                              | 外気フード: ブラック                                        |  |
|             |                   | ■ ダクトレス熱交換換気システム (日本スティーベル株式会社)<br>VLR-70E<br>防火ダンパー無                                                                                  |                              | 外気フード: B ブラック<br>室内パネル ホワイト                        |  |

| ■ 構 造 概 要   |                   |                                                             |                                                                                                |                              |                                             |                         |
|-------------|-------------------|-------------------------------------------------------------|------------------------------------------------------------------------------------------------|------------------------------|---------------------------------------------|-------------------------|
| 基礎          | ■ RCベタ基礎コンクリート    |                                                             |                                                                                                |                              |                                             |                         |
| 通し柱・管柱      | ■ 構造用集成材 105×105  |                                                             |                                                                                                | 間柱                           | ■ 集成材                                       |                         |
| 土台          | ■ 桧 105×105       | 大引き                                                         | ■ 桧 90*90                                                                                      | 筋交い                          | ■ 構造用製材                                     | 火打梁 ■ 鋼製火打(当社基準により米松あり) |
| 桁・梁         | ■ 構造用製材及び集成材      |                                                             |                                                                                                | 制震装置                         | ■ Kダンパー (株)アイ・エム・エー                         |                         |
| ■ 設 備 装 着 品 |                   |                                                             |                                                                                                |                              |                                             |                         |
| 住宅設備        | 部位                | メーカー                                                        | 商品名 ※ 詳細は見積り、プレゼン参照                                                                            |                              | 見積りNo.                                      | (日付)                    |
|             | キッチン              | LIXIL                                                       | ■ ES I型 扉グレイジュスタック 天板ソルティホワイト キッチンパネル:フレッシュホワイト<br>標準食洗器 標準IH, サイトフードHVR(ホワイト) スリム取手ブラック       |                              | 見積り番号 : M25026703071-004-2<br>(日付) 2025.5.8 |                         |
|             | バックカウンタ<br>※オプション | LIXIL                                                       | ■ ES L1800(W900スライドストッカー&家電収納)                                                                 |                              | 見積り番号 : M25026703071-004-3<br>(日付) 2025.5.8 |                         |
|             | 浴室                | LIXIL                                                       | ■ AX1616 PGハウス標準仕様<br>アクセント壁:シルバーグレー 浴槽:ミナモ ホワイト 床:ページュ マグネットシェフ:ホワイト                          |                              | 見積り番号 : M25026703071-004-1<br>(日付) 2025.5.8 |                         |
|             | 1Fトイレ             | LIXIL                                                       | ■ ベーシアシャワートイレ 白 ● タオル掛け:<br>タンク手洗 無し ● 紙巻き器: CF-AA22H /WA                                      |                              | 見積り番号 : M25026703071-004-5<br>(日付) 2025.5.8 |                         |
|             | 2Fトイレ             | LIXIL                                                       | ■ ベーシアシャワートイレ 白 ● タオル掛け: KF-AA71D(パー)<br>タンク手洗 有り ● 紙巻き器: CF-AA22H /WA                         |                              | 見積り番号 : M25026703071-004-6<br>(日付) 2025.5.8 |                         |
|             | 洗面台               | LIXIL                                                       | ■ EV W1200(D500タイプ) 扉:グロスホワイト<br>[引出しタイプ シングルハンドシャワー スタンダードLED三面鏡<br>その他 ● タオル掛け: KF-AA71D(パー) |                              | 見積り番号 : M25026703071-004-4<br>(日付) 2025.5.8 |                         |
|             |                   | LIXIL                                                       | ■ なし                                                                                           |                              | 見積り番号 :<br>(日付)                             |                         |
|             |                   |                                                             |                                                                                                |                              |                                             |                         |
|             |                   |                                                             |                                                                                                |                              |                                             |                         |
| 給排水設備       | 給湯器               | ■ エコキュート370L Panasonic Sシリーズ スタンダードモデル 追い焚きフルオート            |                                                                                                |                              |                                             |                         |
|             | 排水                | ■ 下水                                                        |                                                                                                |                              |                                             |                         |
|             | 外水栓               | ■ 1 カ所 (平面図参照)                                              |                                                                                                | ■ 外部立栓柱: PVC製 水栓柱12型【前澤化成工業】 |                                             |                         |
|             | 外部ガーデンパン          | ■ 無し                                                        |                                                                                                |                              |                                             |                         |
|             | その他               | ■ 洗濯機用単水栓: 緊急止水弁付 ■ 洗濯機用排水: トラップ金物(標準)<br>■ 排水さや管(長期優良住宅仕様) |                                                                                                |                              |                                             |                         |
| ガス配管設備      | ■ なし (配置図・平面図参照)  |                                                             |                                                                                                |                              |                                             |                         |
| 電気設備        | インターホン            | ■ パナソニック VL-SZ30KL                                          |                                                                                                |                              |                                             |                         |
|             | TVアンテナ            | ■ UHF + BS・110度CS／CSアンテナ [2K・4K・8K対応] ■ホワイト                 |                                                                                                |                              |                                             |                         |
|             | エアコン              | ■ 設置場所:                                                     |                                                                                                |                              |                                             |                         |
|             | ソーラー              | ■ あり(Qセルズ) 12 枚 5.28 KW Re.RISE-G3 440 (1722×1134×30)       |                                                                                                |                              |                                             |                         |
|             | ※標準搭載             | ※メーカーのモデルチェンジ等で後継品に変更される可能性あり<br>■ 屋外パワコン                   |                                                                                                |                              |                                             |                         |
| その他         |                   |                                                             |                                                                                                |                              |                                             |                         |
|             |                   |                                                             |                                                                                                |                              |                                             | 決定図                     |

決定図

|  |                                                                                    |                                                                                               |   |                 |  |               |  |  |    |    |    |     |  |
|--|------------------------------------------------------------------------------------|-----------------------------------------------------------------------------------------------|---|-----------------|--|---------------|--|--|----|----|----|-----|--|
|  | 浜 岡 一 級 総 合 設 計 事 務 所<br>一級建築士事務所 静岡県知事登録第 (10)2441 号<br>一級建築士 大臣登録第 365879 号 西原利昌 |  PG HOUSE | 株式会社 LIFEFUND InDesign office 一級建築士事務所<br>事務所登録 (2)第7595号 一級建築士登録 第179770号 鈴木 達男<br>〒432-8023 静岡県浜松市中央区鴨江3丁目70番23号 | 年 月 日 2025/5/30 |  | 件名 鈴木和多留様・唯様邸 |  |  | 設計 | IC | 工務 | 図 番 |  |
|  |                                                                                    |                                                                                               |   | 縮尺              |  | 図面 仕上表 1      |  |  | 倉田 |    | 青島 | 1-1 |  |
|  |                                                                                    |                                                                                               |   |                 |  |               |  |  |    |    |    |     |  |
|  |                                                                                    |                                                                                               |   |                 |  |               |  |  |    |    |    |     |  |




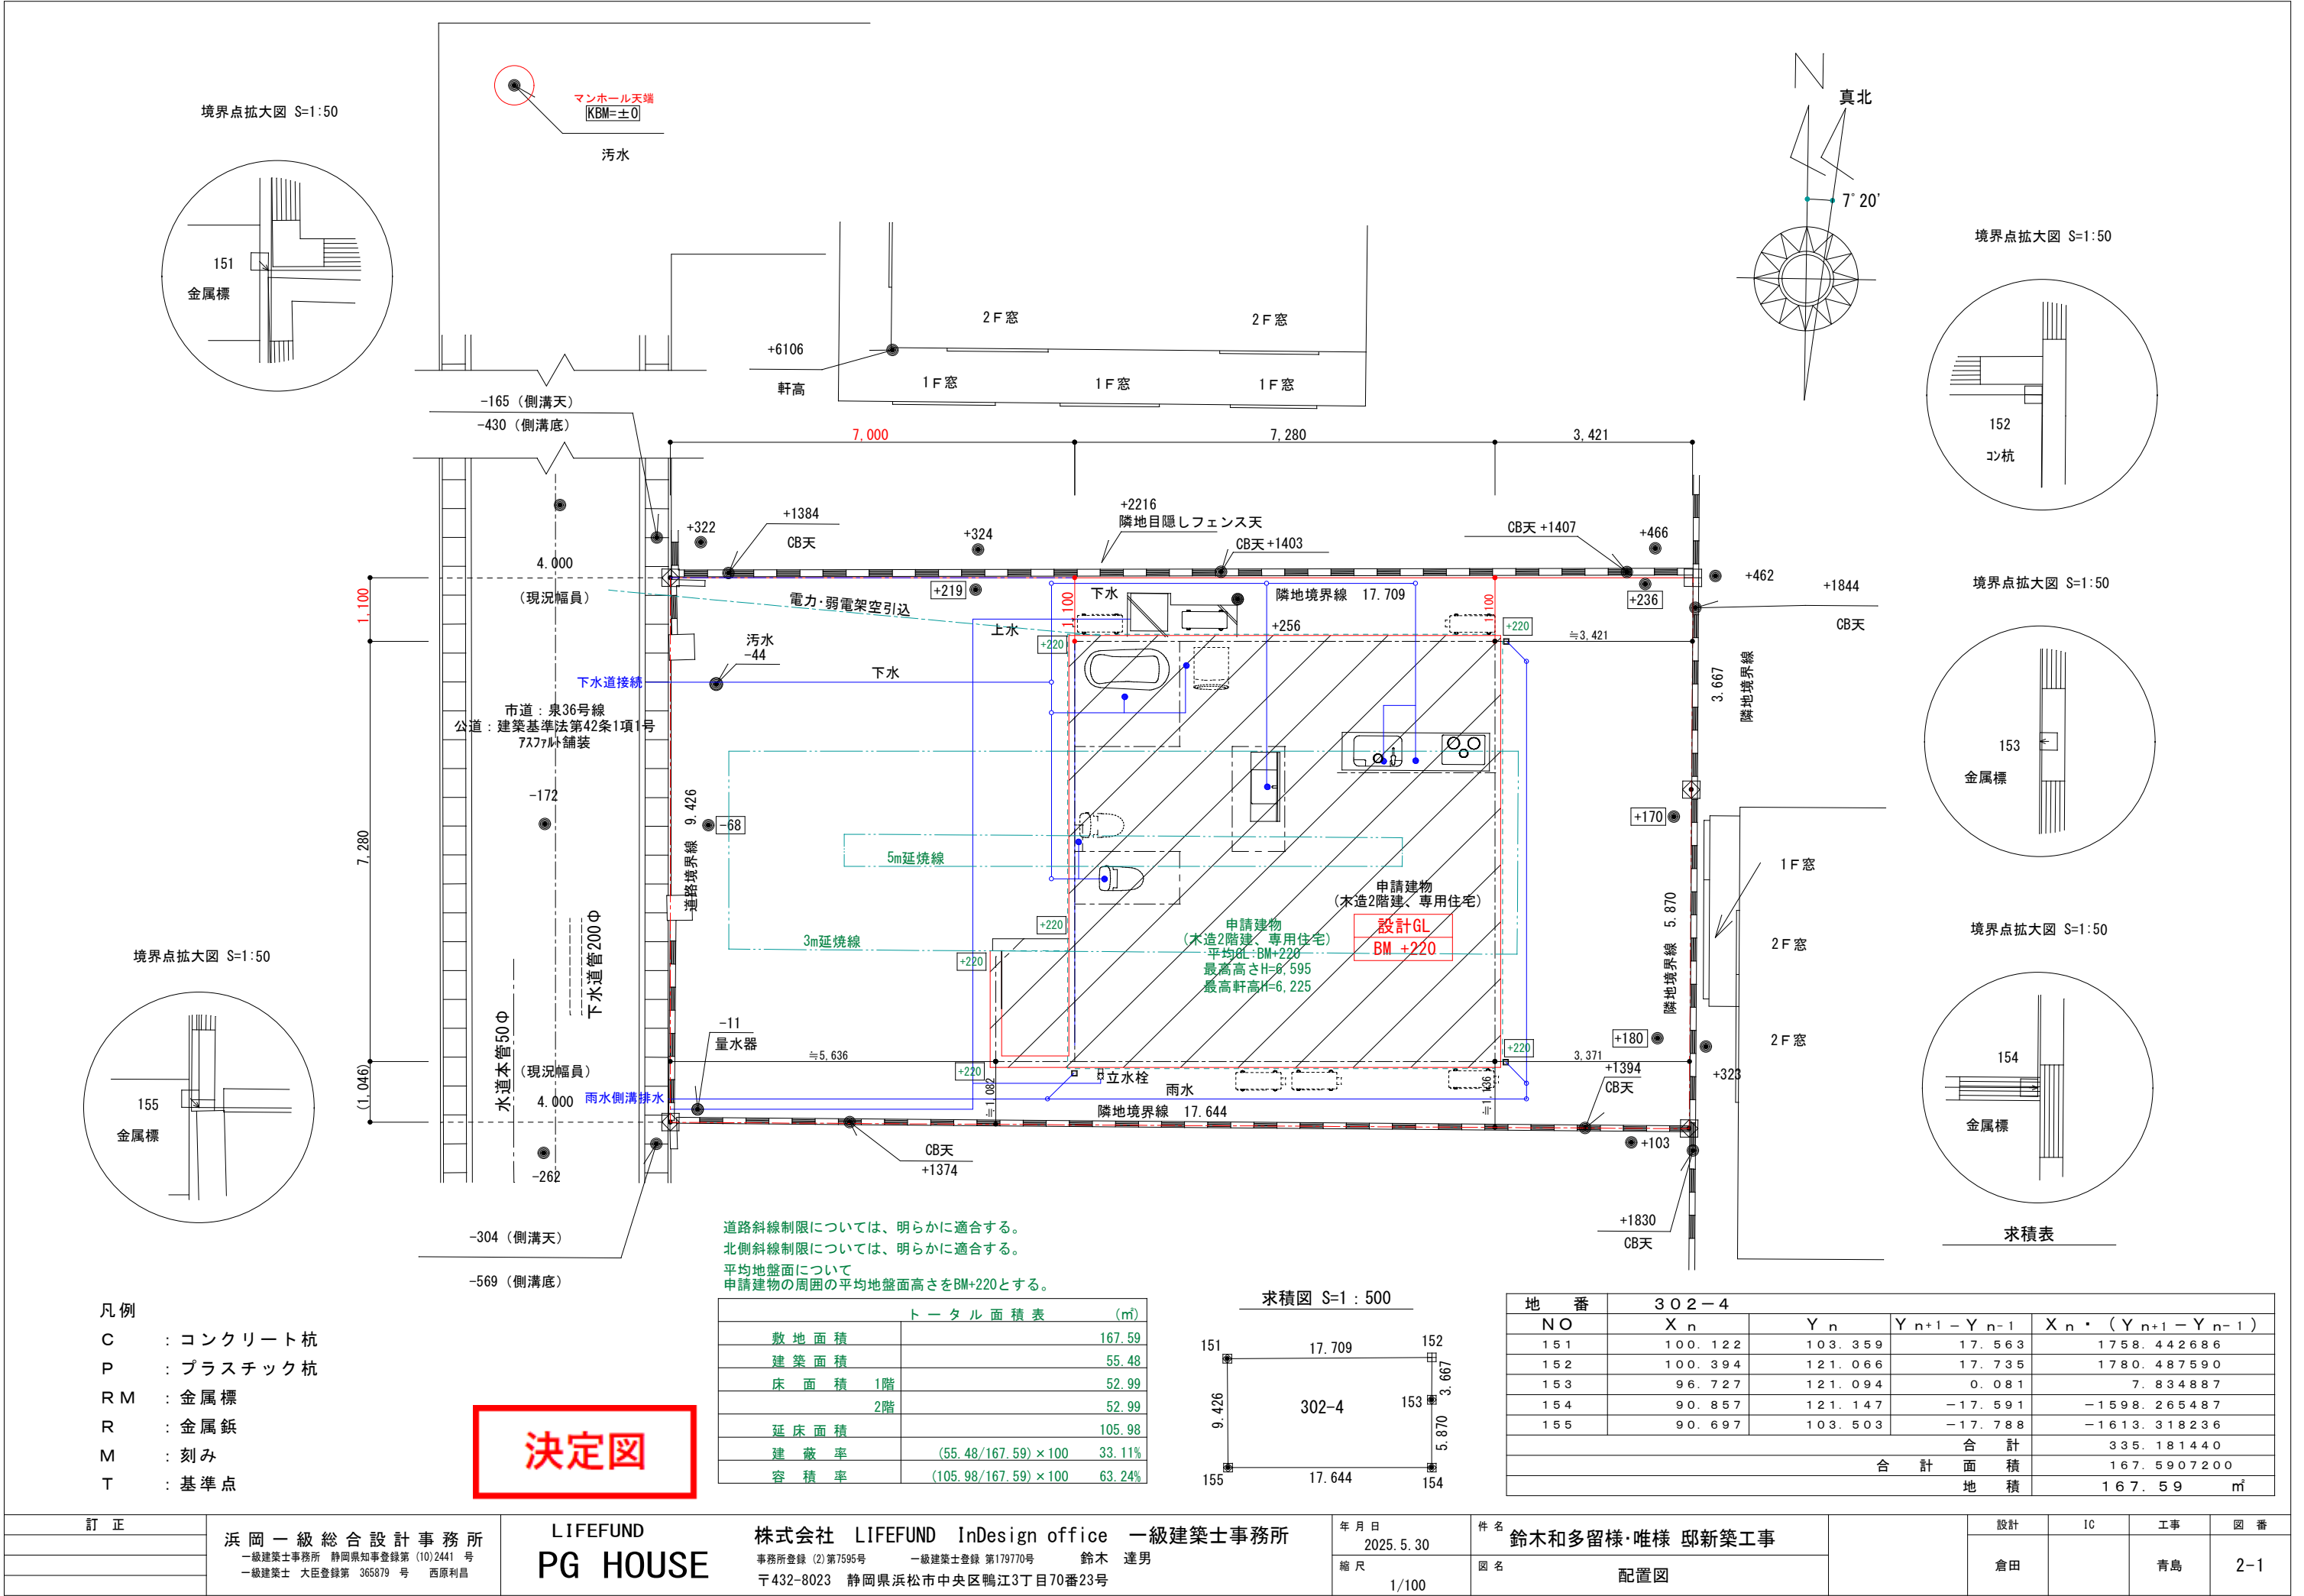


- 凡例
- C : コンクリート杭
  - P : プラスチック杭
  - RM : 金属標
  - R : 金属鉋
  - M : 刻み
  - T : 基準点

決定図

| トータル面積表 (㎡) |                                     |
|-------------|-------------------------------------|
| 敷地面積        | 167.59                              |
| 建築面積        | 55.48                               |
| 床面積 1階      | 52.99                               |
| 2階          | 52.99                               |
| 延床面積        | 105.98                              |
| 建蔽率         | $(55.48/167.59) \times 100$ 33.11%  |
| 容積率         | $(105.98/167.59) \times 100$ 63.24% |

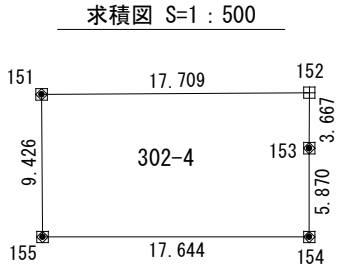

| 地番   | 302-4          |                |                                     |                                                         |  |
|------|----------------|----------------|-------------------------------------|---------------------------------------------------------|--|
| NO   | X <sub>n</sub> | Y <sub>n</sub> | Y <sub>n+1</sub> - Y <sub>n-1</sub> | X <sub>n</sub> * (Y <sub>n+1</sub> - Y <sub>n-1</sub> ) |  |
| 151  | 100.122        | 103.359        | 17.563                              | 1758.442686                                             |  |
| 152  | 100.394        | 121.066        | 17.735                              | 1780.487590                                             |  |
| 153  | 96.727         | 121.094        | 0.081                               | 7.834887                                                |  |
| 154  | 90.857         | 121.147        | -17.591                             | -1598.265487                                            |  |
| 155  | 90.697         | 103.503        | -17.788                             | -1613.318236                                            |  |
| 合計   |                |                |                                     | 335.181440                                              |  |
| 合計面積 |                |                |                                     | 167.5907200                                             |  |
| 地積   |                |                |                                     | 167.59 ㎡                                                |  |

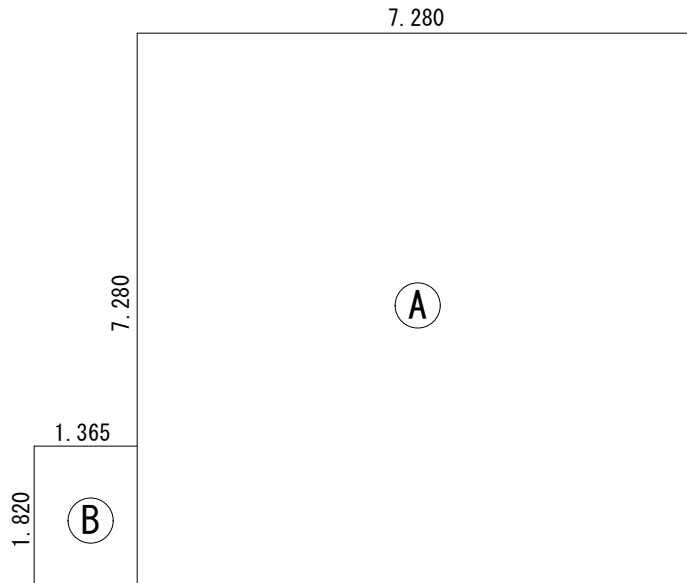


建築面積求積図 S=1/100

建築面積求積表

| 番号 | 計算式            | (m) | 面積 (㎡)           |
|----|----------------|-----|------------------|
| Ⓐ  | 7.280 × 7.280  |     | 52.9984          |
| Ⓑ  | 1.3650 × 1.820 |     | 2.4843           |
|    |                |     |                  |
| 合計 |                |     | 55.4827<br>55.48 |

(16.7坪)

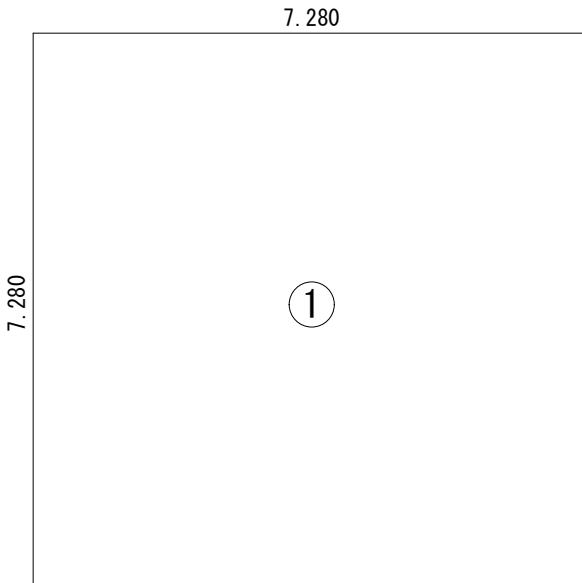


1階床面積図 S=1/100

1階床面積求積表

| 番号 | 計算式           | (m) | 面積 (㎡)           |
|----|---------------|-----|------------------|
| ①  | 7.280 × 7.280 |     | 52.9984          |
|    |               |     |                  |
|    |               |     |                  |
| 合計 |               |     | 52.9984<br>52.99 |

(16.0坪)

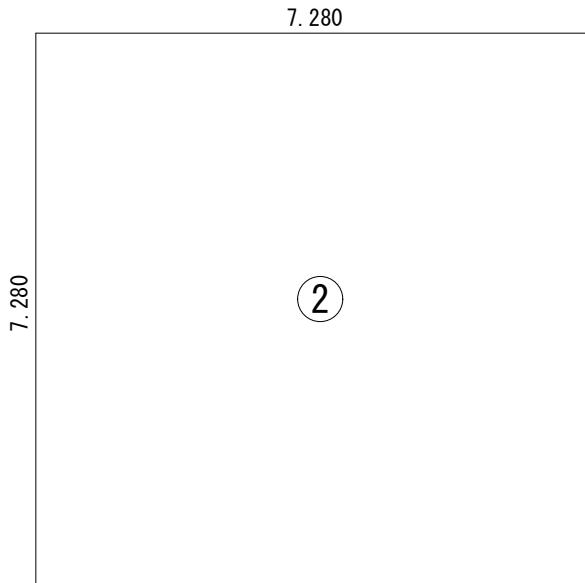

2階床面積図 S=1/100

2階床面積求積表

| 番号 | 計算式           | (m) | 面積 (㎡)           |
|----|---------------|-----|------------------|
| ②  | 7.280 × 7.280 |     | 52.9984          |
|    |               |     |                  |
|    |               |     |                  |
| 合計 |               |     | 52.9984<br>52.99 |

(16.0坪)


延べ床面積表

|       | 番号 | (m) | 面積 (㎡) |
|-------|----|-----|--------|
| 1階床面積 | ①  |     | 52.99  |
| 2階床面積 | ②  |     | 52.99  |
| 合計    |    |     | 105.98 |

(32.0坪)

決定図



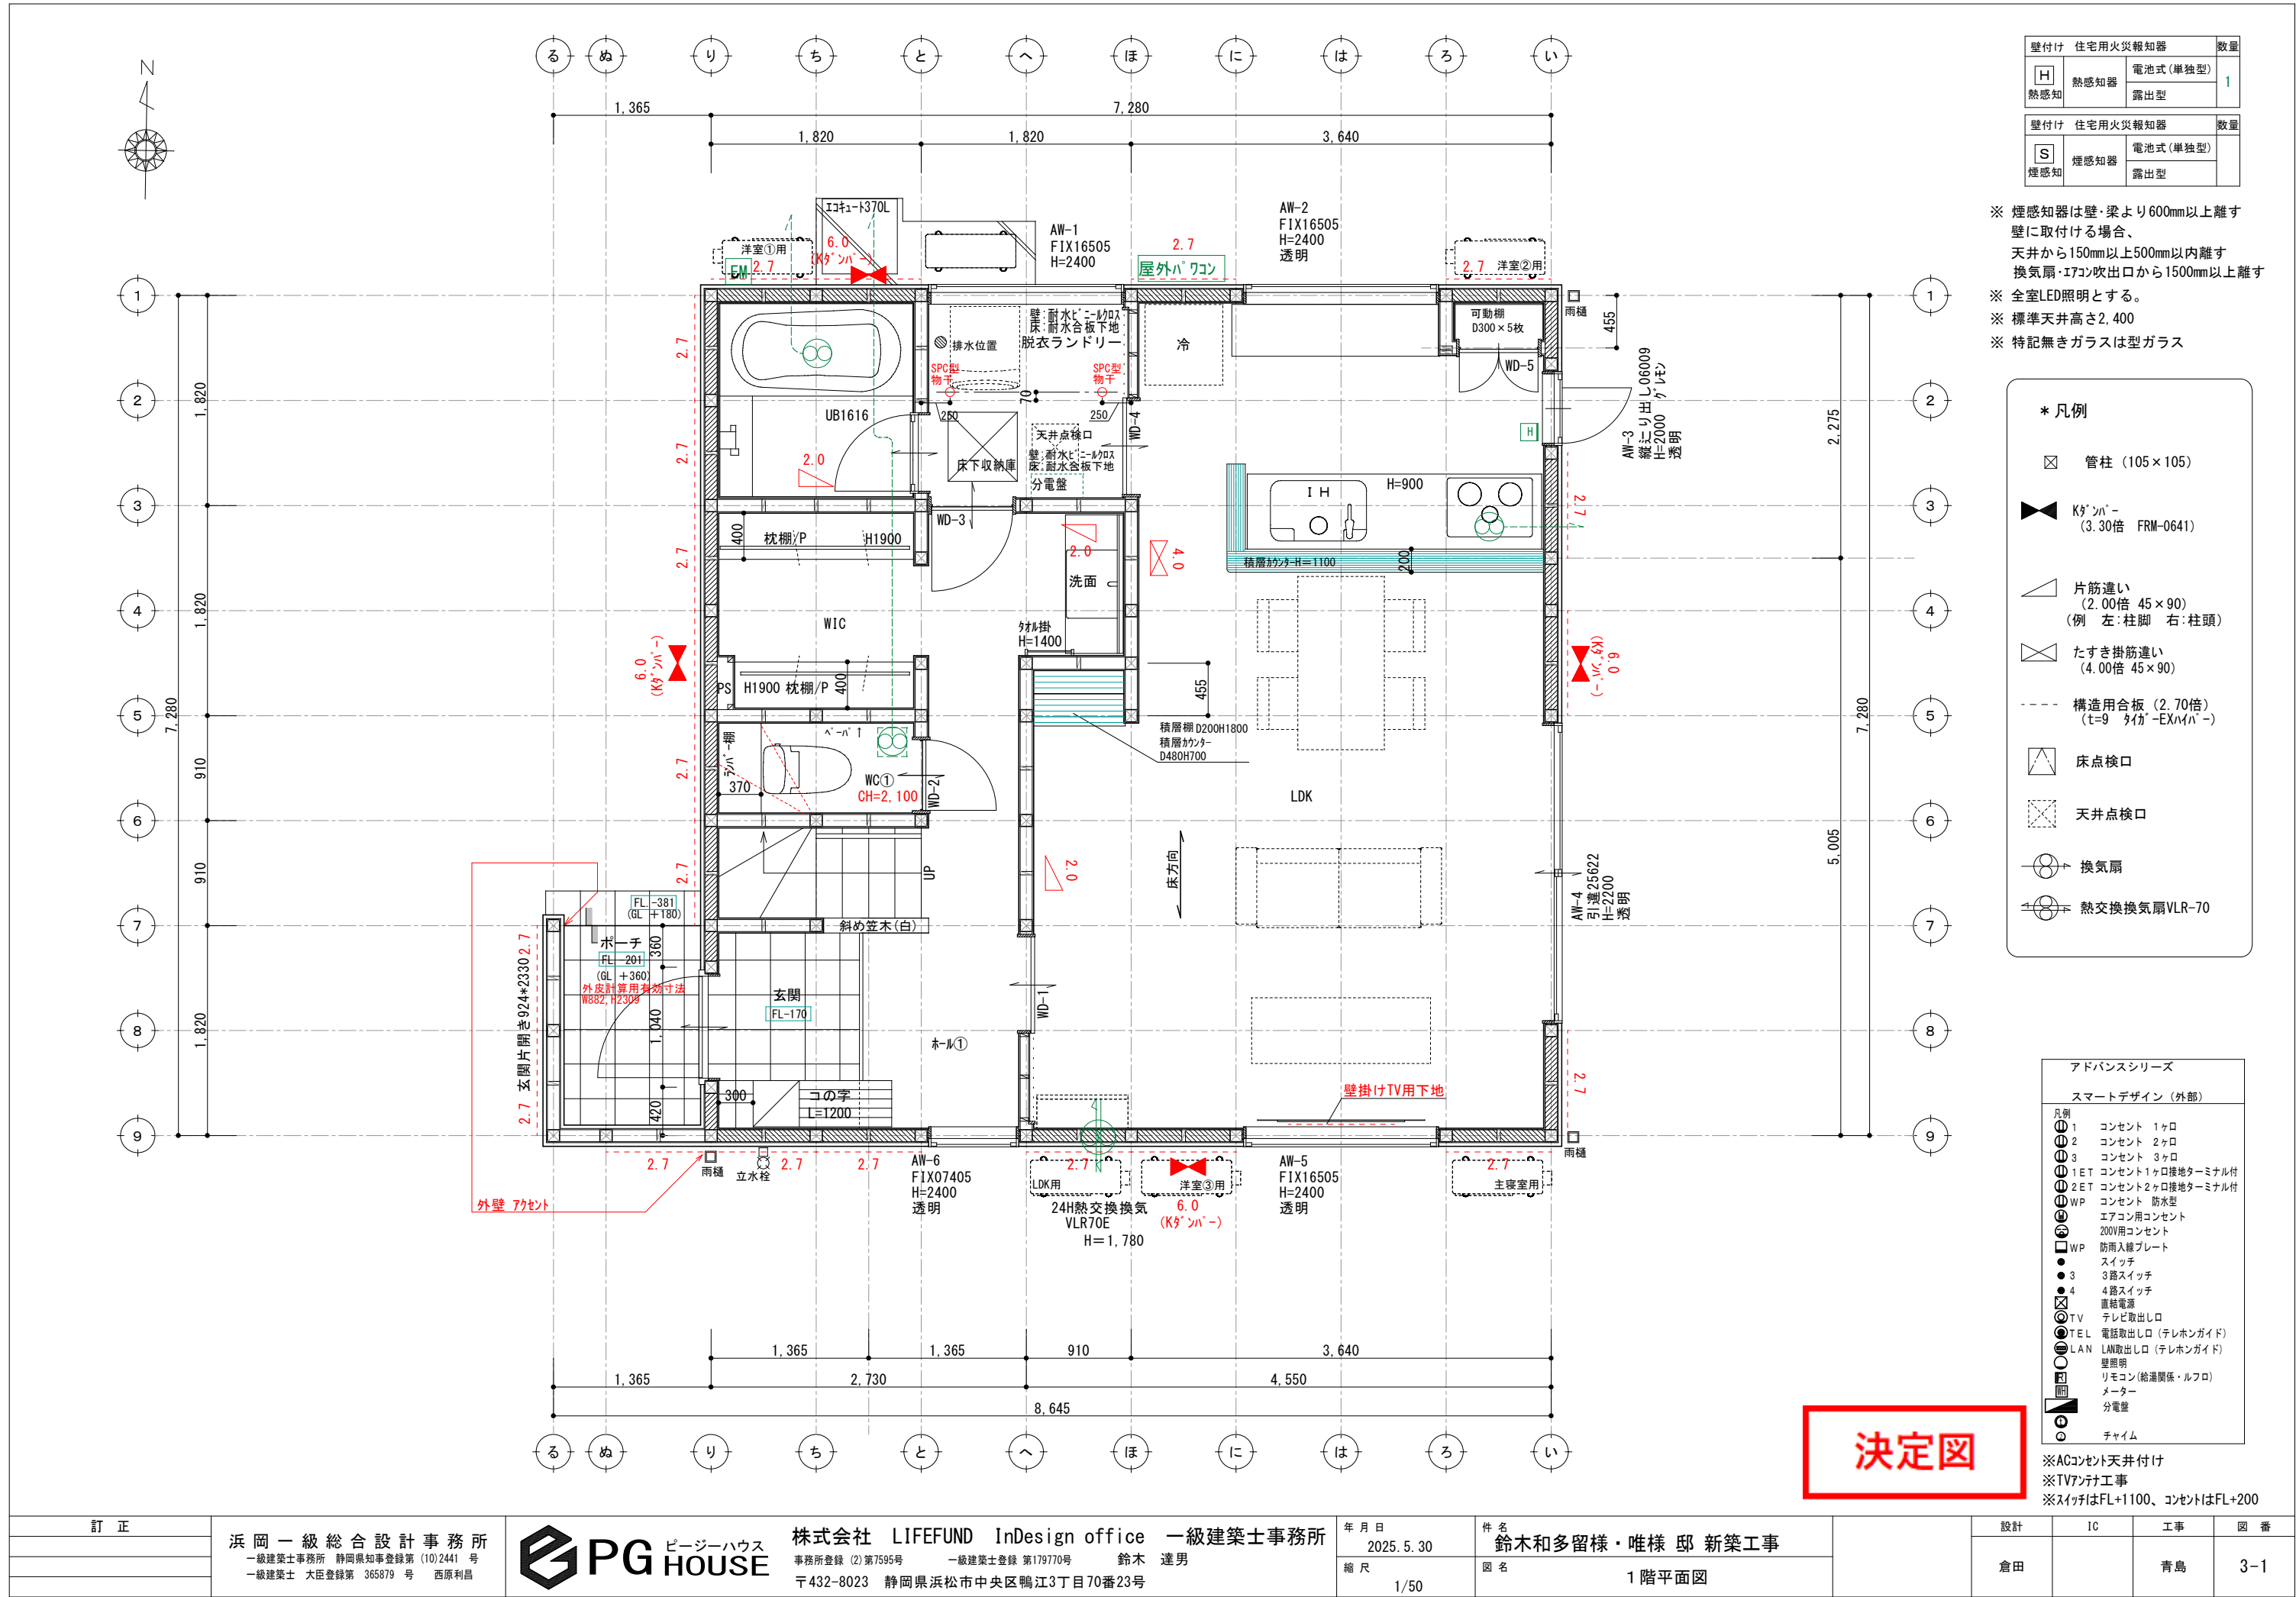

| 壁付け 住宅用火災報知器 |           |  | 数量 |
|--------------|-----------|--|----|
| H<br>熱感知     | 電池式 (単独型) |  | 1  |
|              | 露出型       |  |    |
| 壁付け 住宅用火災報知器 |           |  | 数量 |
| S<br>煙感知     | 電池式 (単独型) |  |    |
|              | 露出型       |  |    |

※ 煙感知器は壁・梁より600mm以上離す  
壁に取付ける場合、  
天井から150mm以上500mm以内離す  
換気扇・エアコン吹出口から1500mm以上離す

※ 全室LED照明とする。

※ 標準天井高さ2,400

※ 特記無きガラスは型ガラス

**\* 凡例**

管柱 (105×105)

Kタツバー (3.30倍 FRM-0641)

片筋違い (2.00倍 45×90)  
(例 左:柱脚 右:柱頭)

たすき掛筋違い (4.00倍 45×90)

構造用合板 (2.70倍)  
(t=9 材種-EXハイバ-)

床点検口


天井点検口

換気扇

熱交換換気扇VLR-70

| アドバンスシリーズ     |                  |           |
|---------------|------------------|-----------|
| スマートデザイン (外部) |                  |           |
| 凡例            | 1                | コンセント 1ヶ所 |
| 2             | コンセント 2ヶ所        |           |
| 3             | コンセント 3ヶ所        |           |
| 1ET           | コンセント1ヶ所接地ターミナル付 |           |
| 2ET           | コンセント2ヶ所接地ターミナル付 |           |
| WP            | コンセント 防水型        |           |
| WP            | エアコン用コンセント       |           |
| WP            | 200V用コンセント       |           |
| WP            | 防雨入線プレート         |           |
| ●             | スイッチ             |           |
| ●             | 3路スイッチ           |           |
| ●             | 4路スイッチ           |           |
| ●             | 直結電源             |           |
| TV            | テレビ取出口           |           |
| TEL           | 電話取出口 (テレホンガイド)  |           |
| LAN           | LAN取出口 (テレホンガイド) |           |
| 壁照明           | リモコン (給湯関係・ルフロ)  |           |
| メーター          | メーター             |           |
| 分電盤           | 分電盤              |           |
| チャイム          | チャイム             |           |

※ACコンセント天井付け  
※TVアンテナ工事  
※スイッチはFL+1100、コンセントはFL+200

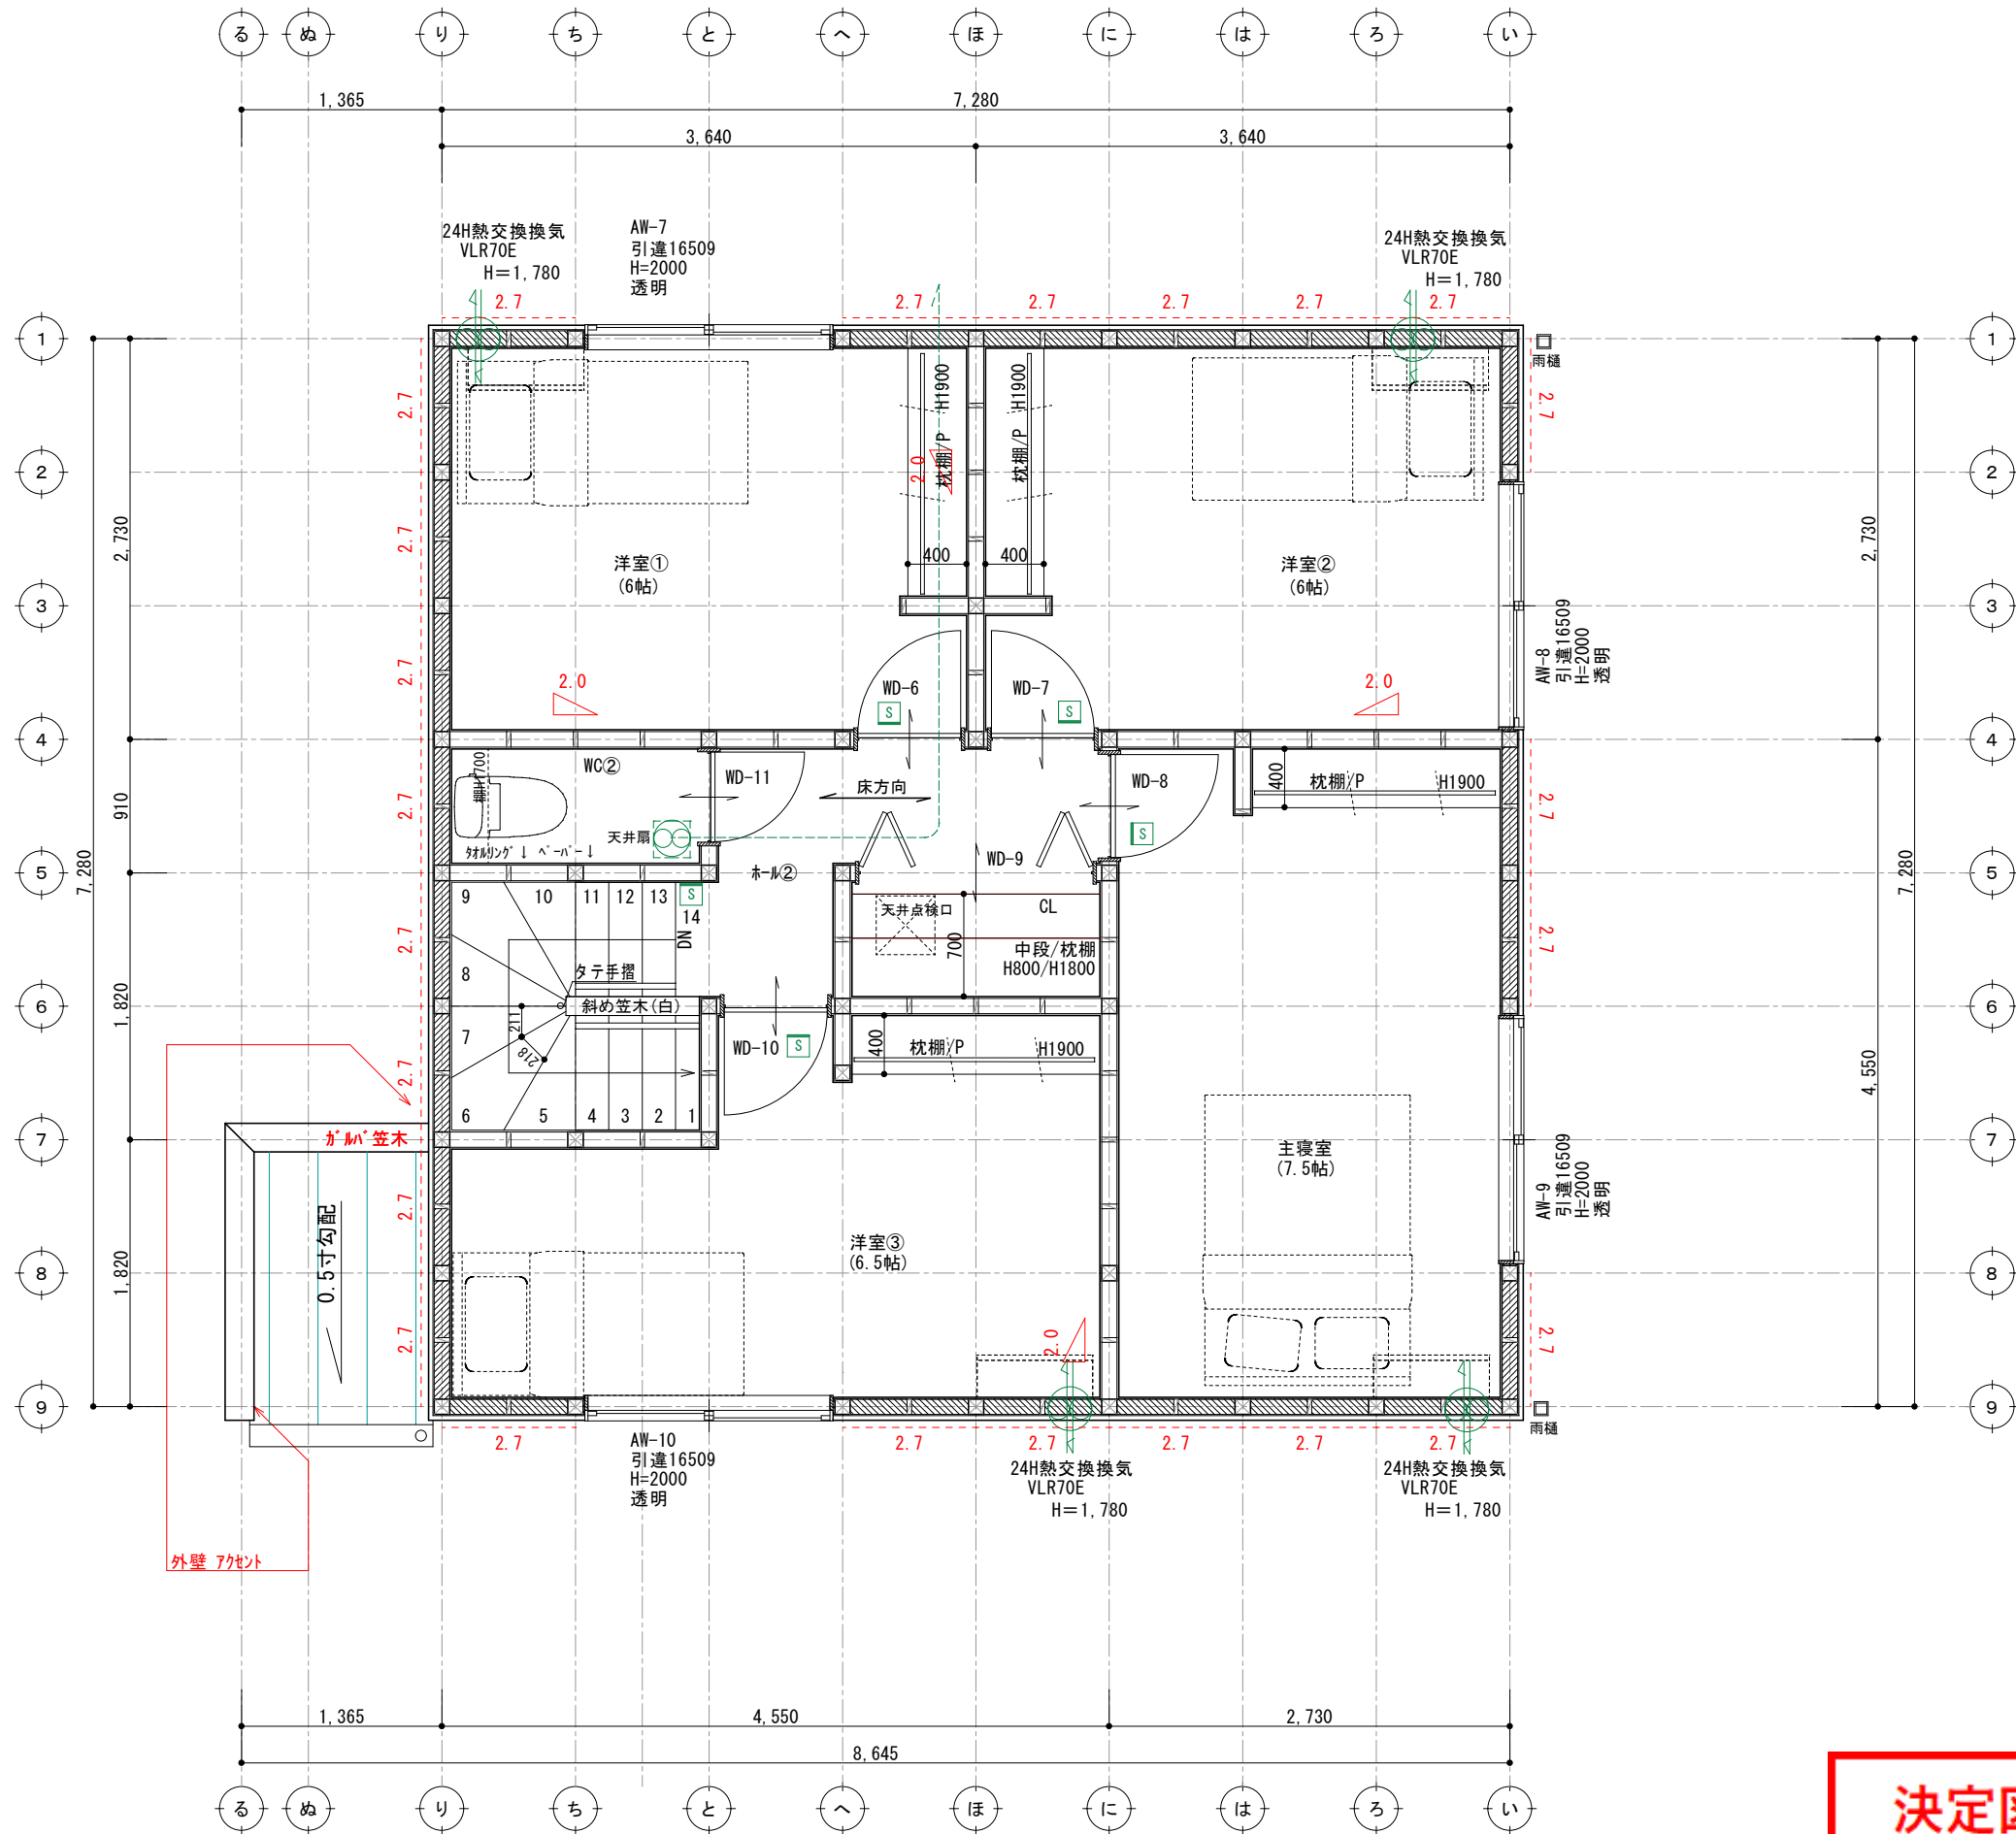

| 壁付け 住宅用火災報知器 |      |          | 数量 |
|--------------|------|----------|----|
| H<br>熱感知     | 熱感知器 | 電池式(単独型) | 4  |
|              |      | 露出型      |    |
| 壁付け 住宅用火災報知器 |      |          | 数量 |
| S<br>煙感知     | 煙感知器 | 電池式(単独型) | 4  |
|              |      | 露出型      |    |

※ 煙感知器は壁・梁より600mm以上離す  
壁に取付ける場合、  
天井から150mm以上500mm以内離す  
換気扇・エアコン吹出口から1500mm以上離す  
※ 全室LED照明とする。  
※ 標準天井高さ2,400  
※ 特記無きガラスは型ガラス

\* 凡例

- 管柱 (105×105)
- Kダクト (3.30倍 FRM-0641)
- 片筋違い (2.00倍 45×90)  
(例 左:柱脚 右:柱頭)
- たすき掛筋違い (4.00倍 45×90)
- 構造用合板 (2.70倍)  
(t=9 材種 EXハイパー)
- 床点検口
- 天井点検口
- 換気扇
- 熱交換換気扇VLR-70

アドバンスシリーズ

スマートデザイン (外部)


- 凡例
- 1 コンセント 1ヶ所
- 2 コンセント 2ヶ所
- 3 コンセント 3ヶ所
- 1ET コンセント1ヶ所接地ターミナル付
- 2ET コンセント2ヶ所接地ターミナル付
- WP コンセント 防水型
- エアコン用コンセント
- 200V用コンセント
- WP 防雨入線プレート
- スイッチ
- 3 3路スイッチ
- 4 4路スイッチ
- 直結電源
- TV テレビ取出口
- TEL 電話取出口 (テレホンガイド)
- LAN LAN取出口 (テレホンガイド)
- 壁照明
- リモコン (給湯関係・ルフロ)
- メーター
- 分電盤
- チャイム

※ACコンセント天井付け  
※TVアンテナ工事  
※スイッチはFL+1100、コンセントはFL+200

決定図



|    |                                                                          |                     |   |                    |                        |          |    |          |           |
|----|--------------------------------------------------------------------------|---------------------|---|--------------------|------------------------|----------|----|----------|-----------|
| 訂正 | 浜岡一級総合設計事務所<br>一級建築士事務所 静岡県知事登録第 (10)2441 号<br>一級建築士 大臣登録第 365879 号 西原利昌 | PG HOUSE<br>ピージーハウス | 株式会社 LIFEFUND InDesign office 一級建築士事務所<br>事務所登録 (2) 第7595号 一級建築士登録 第179770号 鈴木 達男<br>〒432-8023 静岡県浜松市中央区鴨江3丁目70番23号 | 年月日<br>2025. 5. 30 | 件名<br>鈴木和多留様・唯様 邸 新築工事 | 設計<br>倉田 | IC | 工事<br>青島 | 図番<br>3-2 |
|    |                                                                          |                     |   | 縮尺<br>1/50         | 図名<br>2階平面図            |          |    |          |           |

太陽光あり

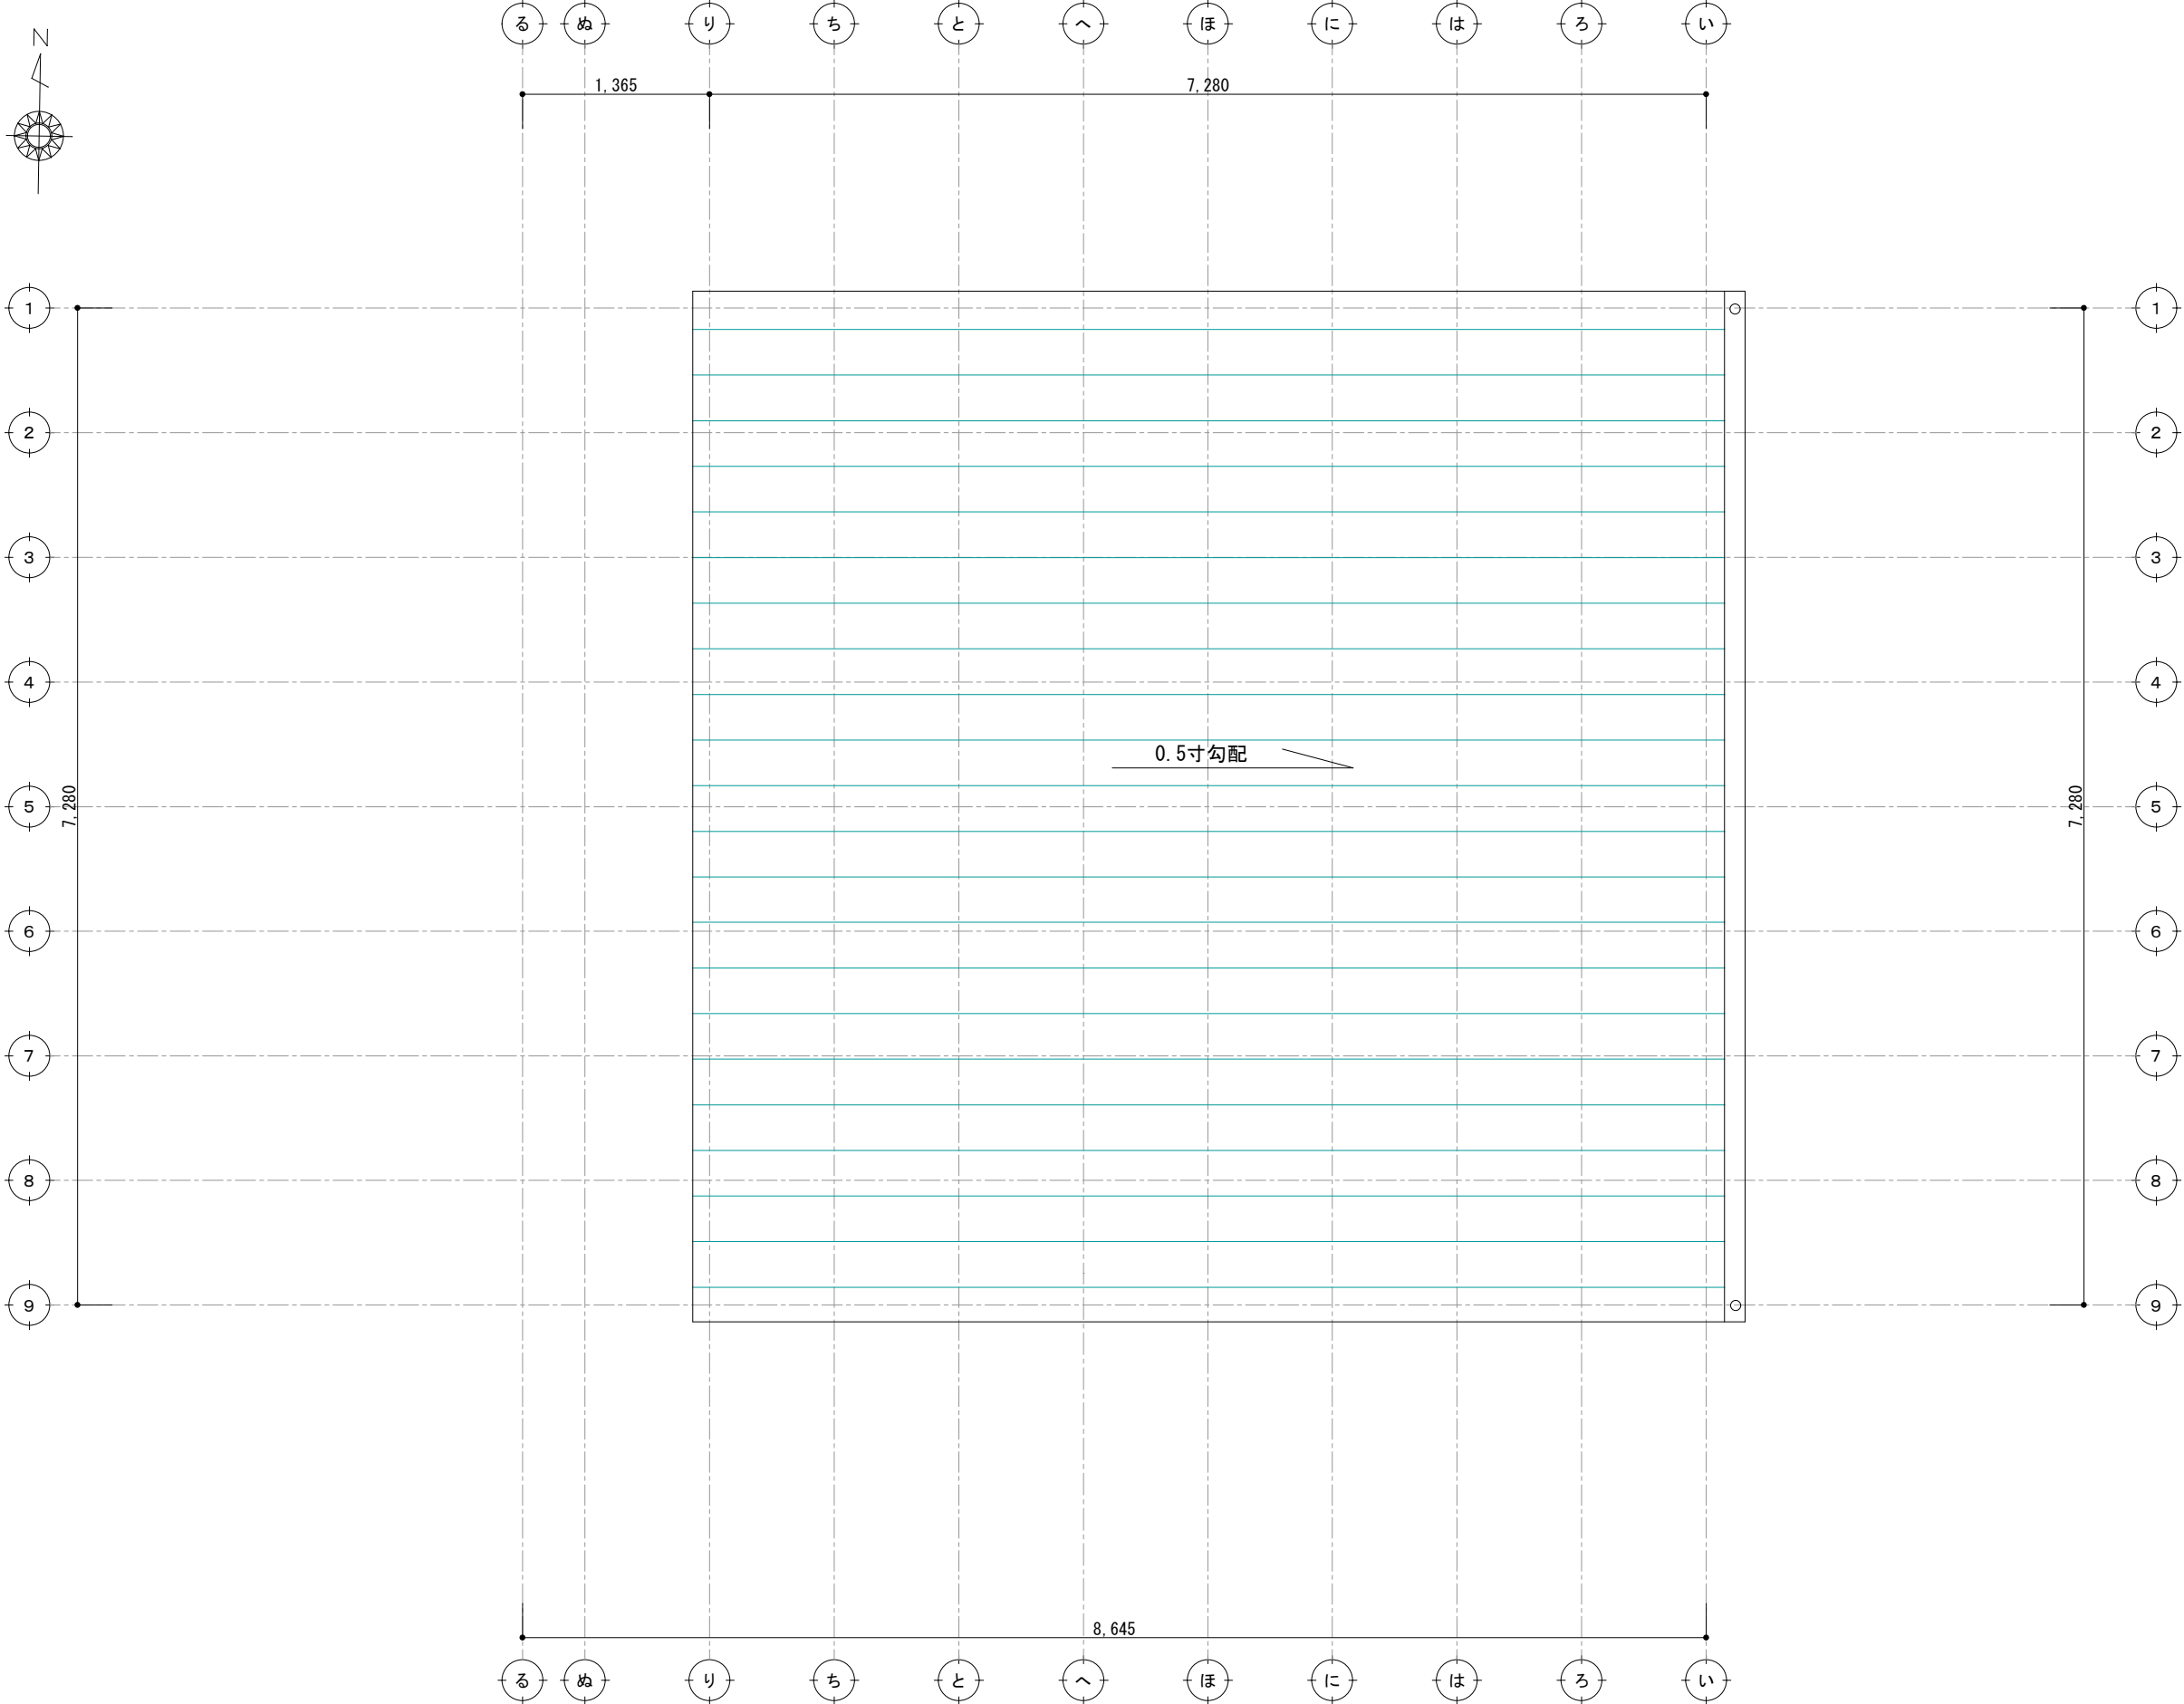

**決定図**

|     |                                                                                    |                                                                                              |   |                      |                         |                       |                 |
|-----|------------------------------------------------------------------------------------|----------------------------------------------------------------------------------------------|---|----------------------|-------------------------|-----------------------|-----------------|
| 訂 正 | 浜 岡 一 級 総 合 設 計 事 務 所<br>一級建築士事務所 静岡県知事登録第 (10)2441 号<br>一級建築士 大臣登録第 365879 号 西原利昌 |  PG HOUSE | 株式会社 LIFEFUND InDesign office 一級建築士事務所<br>事務所登録 (2) 第17595号 一級建築士登録 第179770号 鈴木 達男<br>〒432-8023 静岡県浜松市中央区鴨江3丁目70番23号 | 年 月 日<br>2025. 5. 30 | 件 名<br>鈴木和多留様・唯様 邸 新築工事 | 設計<br>IC<br>工事<br>図 番 | 倉田<br>青島<br>3-3 |
|     |                                                                                    |                                                                                              | 縮 尺<br>1/100   | 図 名<br>屋根伏図          |                         |                       |                 |

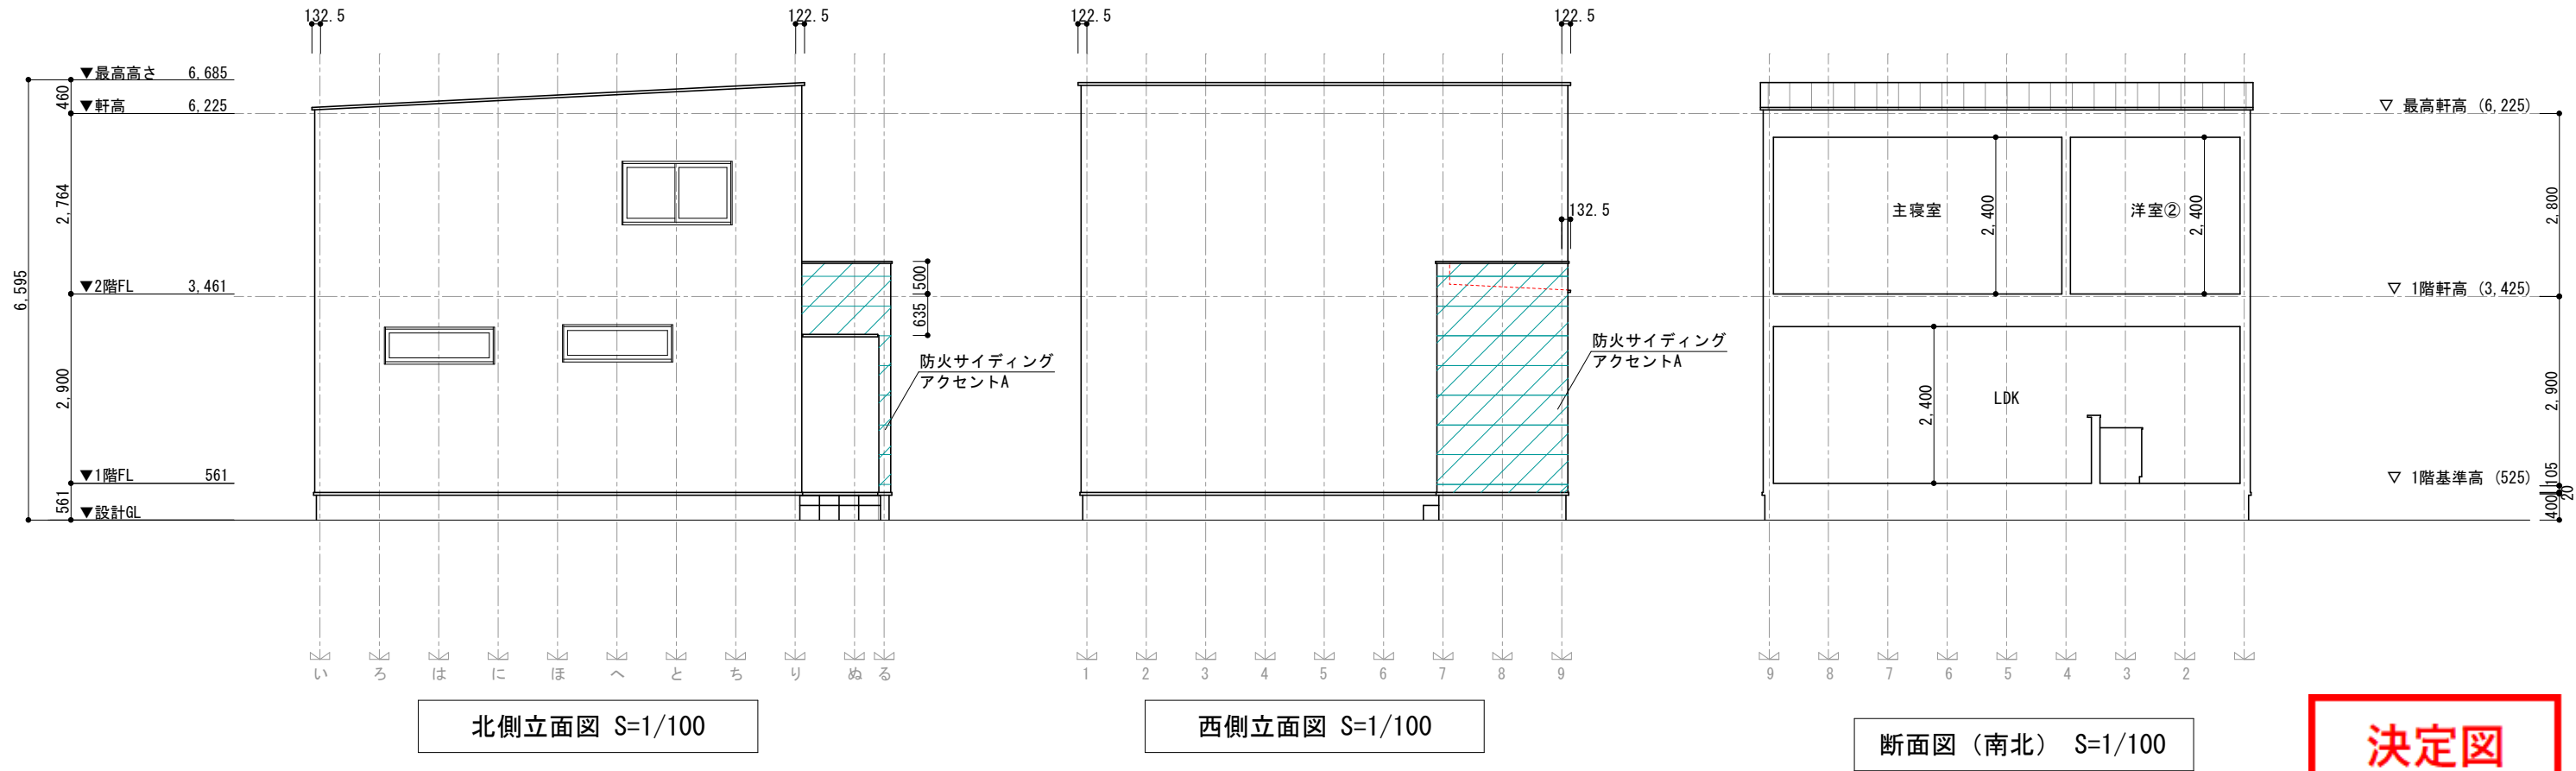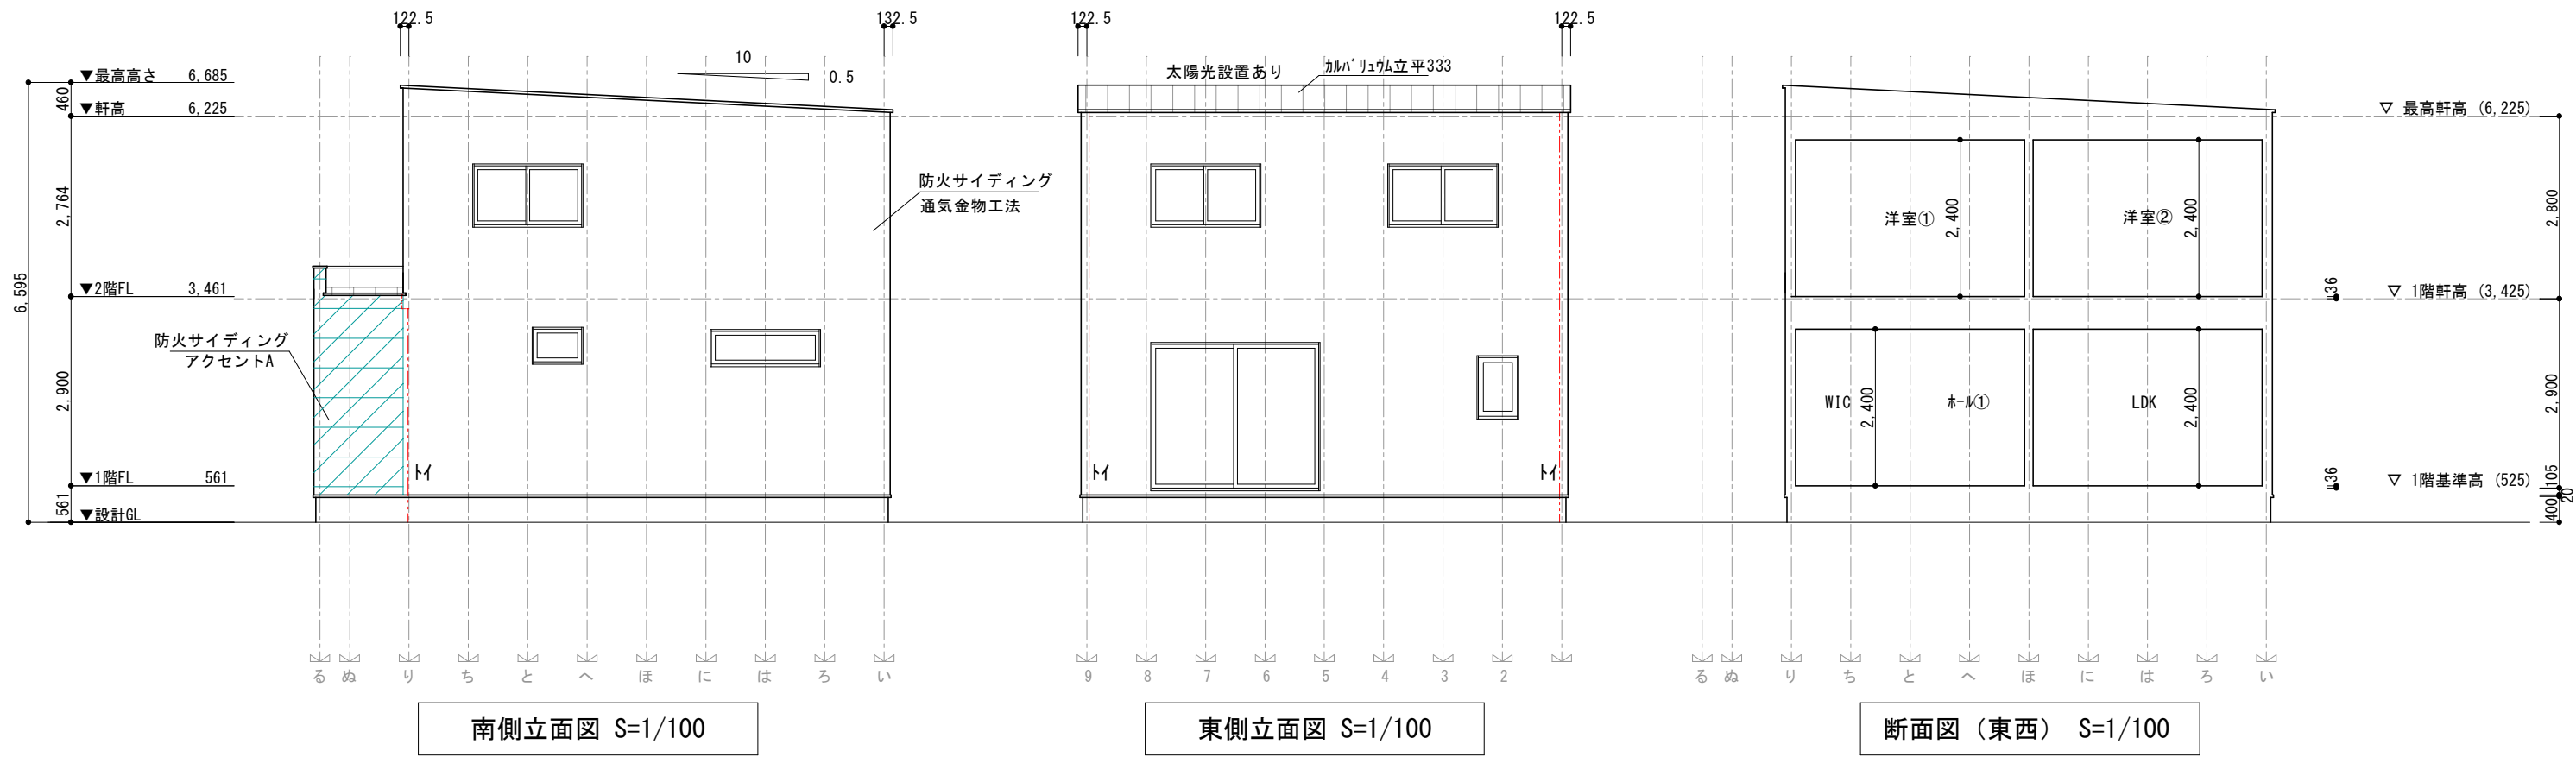


決定図

|    |                                                                          |                     |   |                                   |                                     |  |          |    |          |         |
|----|--------------------------------------------------------------------------|---------------------|---|-----------------------------------|-------------------------------------|--|----------|----|----------|---------|
| 訂正 | 浜岡一級総合設計事務所<br>一級建築士事務所 静岡県知事登録第 (10)2441 号<br>一級建築士 大臣登録第 365879 号 西原利昌 | PG HOUSE<br>ピージーハウス | 株式会社 LIFEFUND InDesign office 一級建築士事務所<br>事務所登録 (2) 第7595号 一級建築士登録 第179770号 鈴木 達男<br>〒432-8023 静岡県浜松市中央区鴨江3丁目70番23号 | 年月日<br>2025. 5. 30<br>縮尺<br>1/100 | 件名<br>鈴木和多留様・唯様 邸 新築工事<br>図名<br>立面図 |  | 設計<br>倉田 | IC | 工事<br>青島 | 図番<br>4 |
|----|--------------------------------------------------------------------------|---------------------|---|-----------------------------------|-------------------------------------|--|----------|----|----------|---------|




太陽光パネル有

G 1

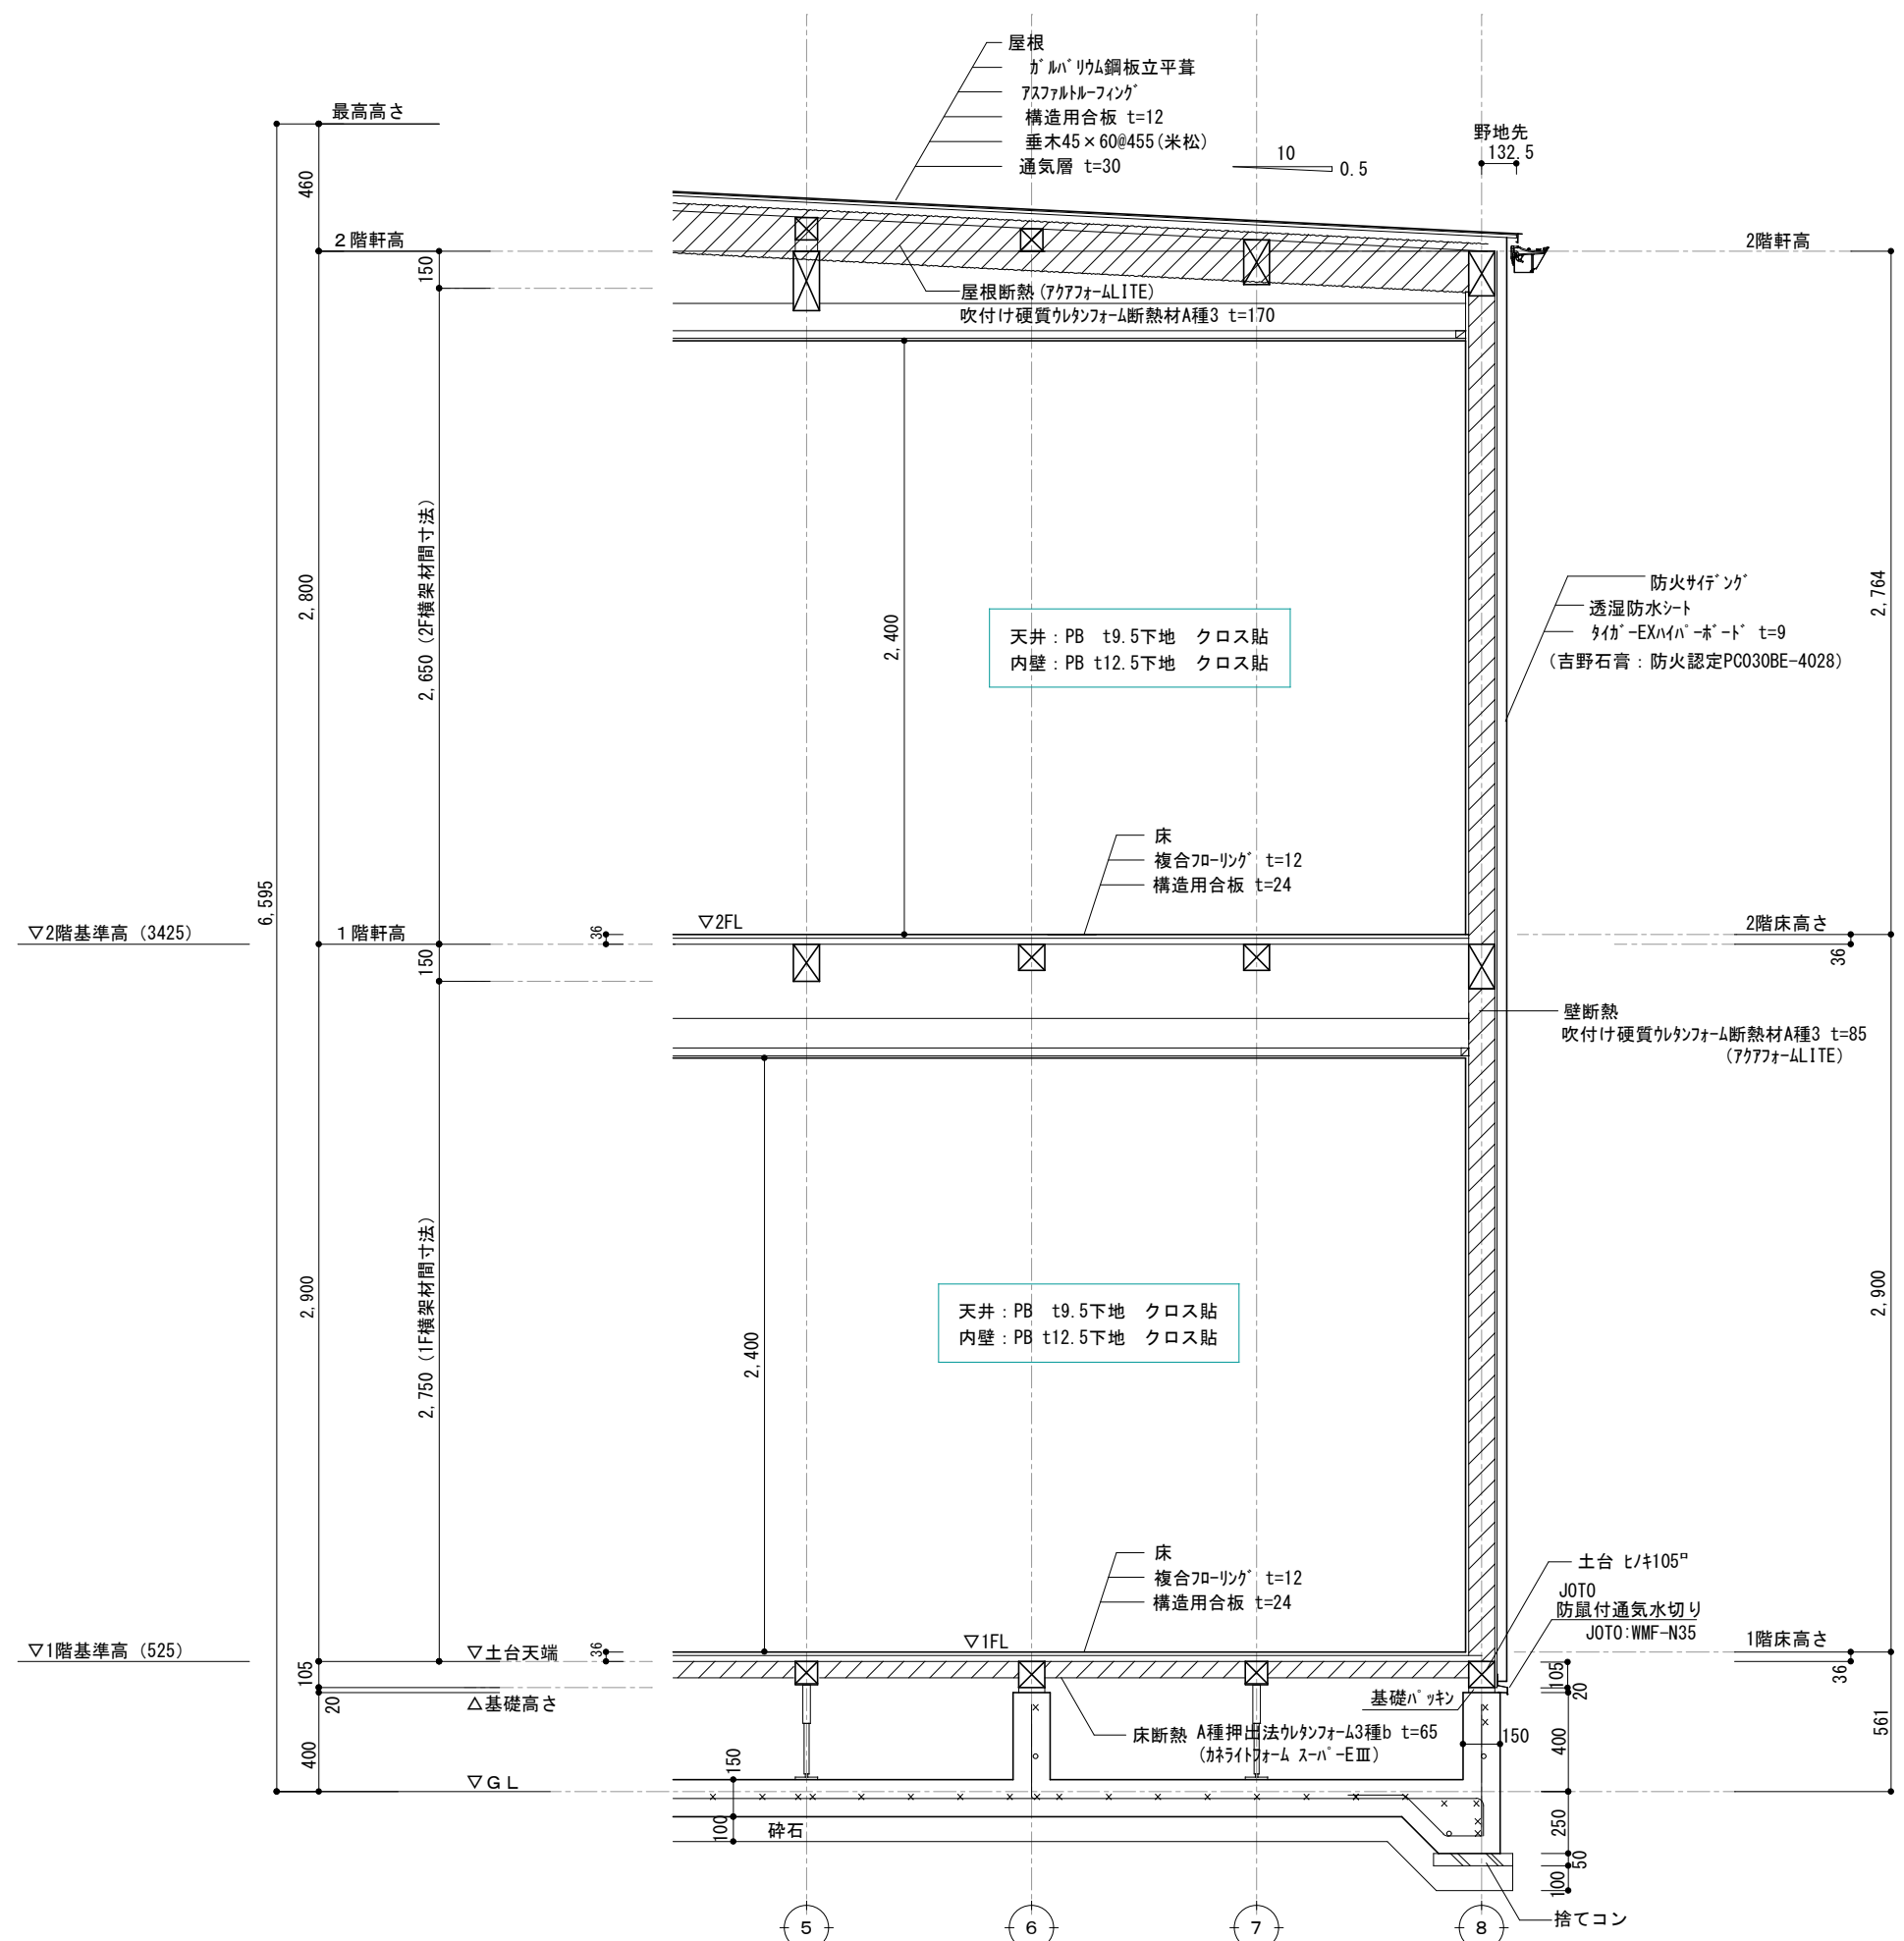


決定図


|     |                               |  |                                                                                      |                                         |  |             |                 |  |    |    |    |     |
|-----|-------------------------------|--|--------------------------------------------------------------------------------------|-----------------------------------------|--|-------------|-----------------|--|----|----|----|-----|
| 訂 正 | 浜 岡 一 級 総 合 設 計 事 務 所         |  |  | 株式会社 LIFEFUND InDesign office 一級建築士事務所  |  | 年 月 日       | 件 名             |  | 設計 | IC | 工事 | 図 番 |
|     | 一級建築士事務所 静岡県知事登録第 (10) 2441 号 |  |                                                                                      | 事務所登録 (2) 第7595号 一級建築士登録 第179770号 鈴木 達男 |  | 2025. 5. 30 | 鈴木和多留様・唯様 邸新築工事 |  |    |    |    |     |
|     | 一級建築士 大臣登録第 365879 号 西原利昌     |  |                                                                                      | 〒432-8023 静岡県浜松市中央区鴨江3丁目70番23号          |  | 縮 尺         | 図 名             |  |    |    |    |     |
|     |                               |  |                                                                                      |                                         |  | 1/30        | 矩計図             |  | 倉田 |    | 青島 | A-5 |

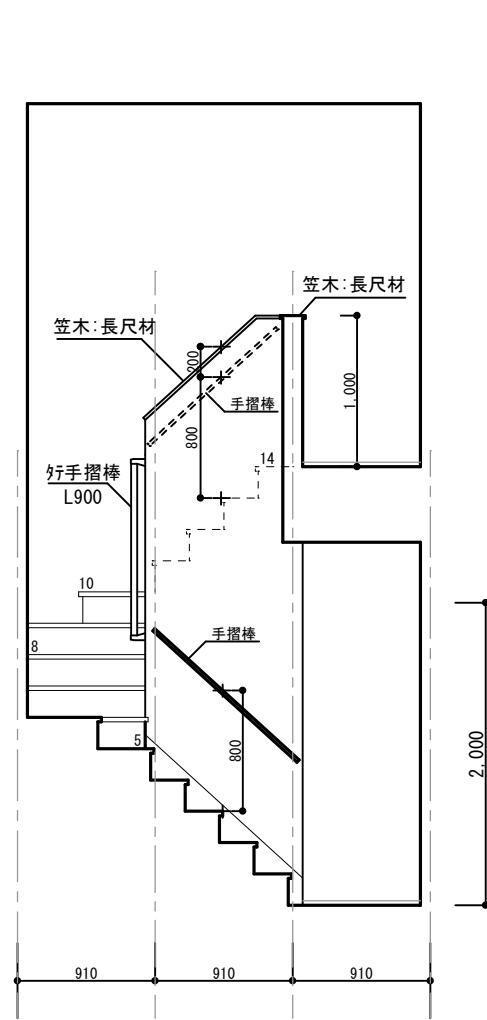

階段 北面

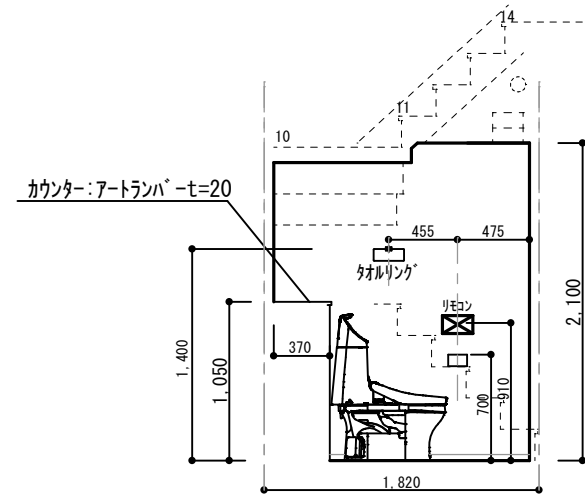


WC① 北面

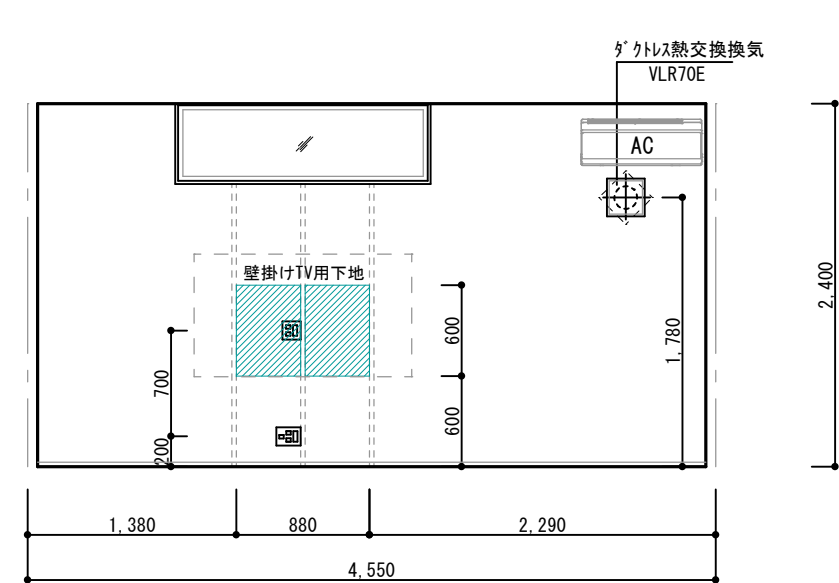

LDK 南面

決定図

|    |                                                                          |                      |   |                  |                        |  |          |    |     |
|----|--------------------------------------------------------------------------|----------------------|---|------------------|------------------------|--|----------|----|-----|
| 訂正 | 浜岡一級総合設計事務所<br>一級建築士事務所 静岡県知事登録第 (10)2441 号<br>一級建築士 大臣登録第 365879 号 西原利昌 | LIFEFUND<br>PG HOUSE | 株式会社 LIFEFUND InDesign office 一級建築士事務所<br>事務所登録 (2) 第7595号 一級建築士登録 第179770号 鈴木 達男<br>〒432-8023 静岡県浜松市中央区鴨江3丁目70番23号 | 年月日<br>2025.5.30 | 件名<br>鈴木和多留様・唯様 邸 新築工事 |  | 設計<br>IC | 工事 | 図番  |
|    |                                                                          |                      |   | 縮尺<br>1/50       | 図名<br>展開図-1            |  | 酒井       | 青島 | 6-1 |
|    |                                                                          |                      |   |                  |                        |  |          |    |     |

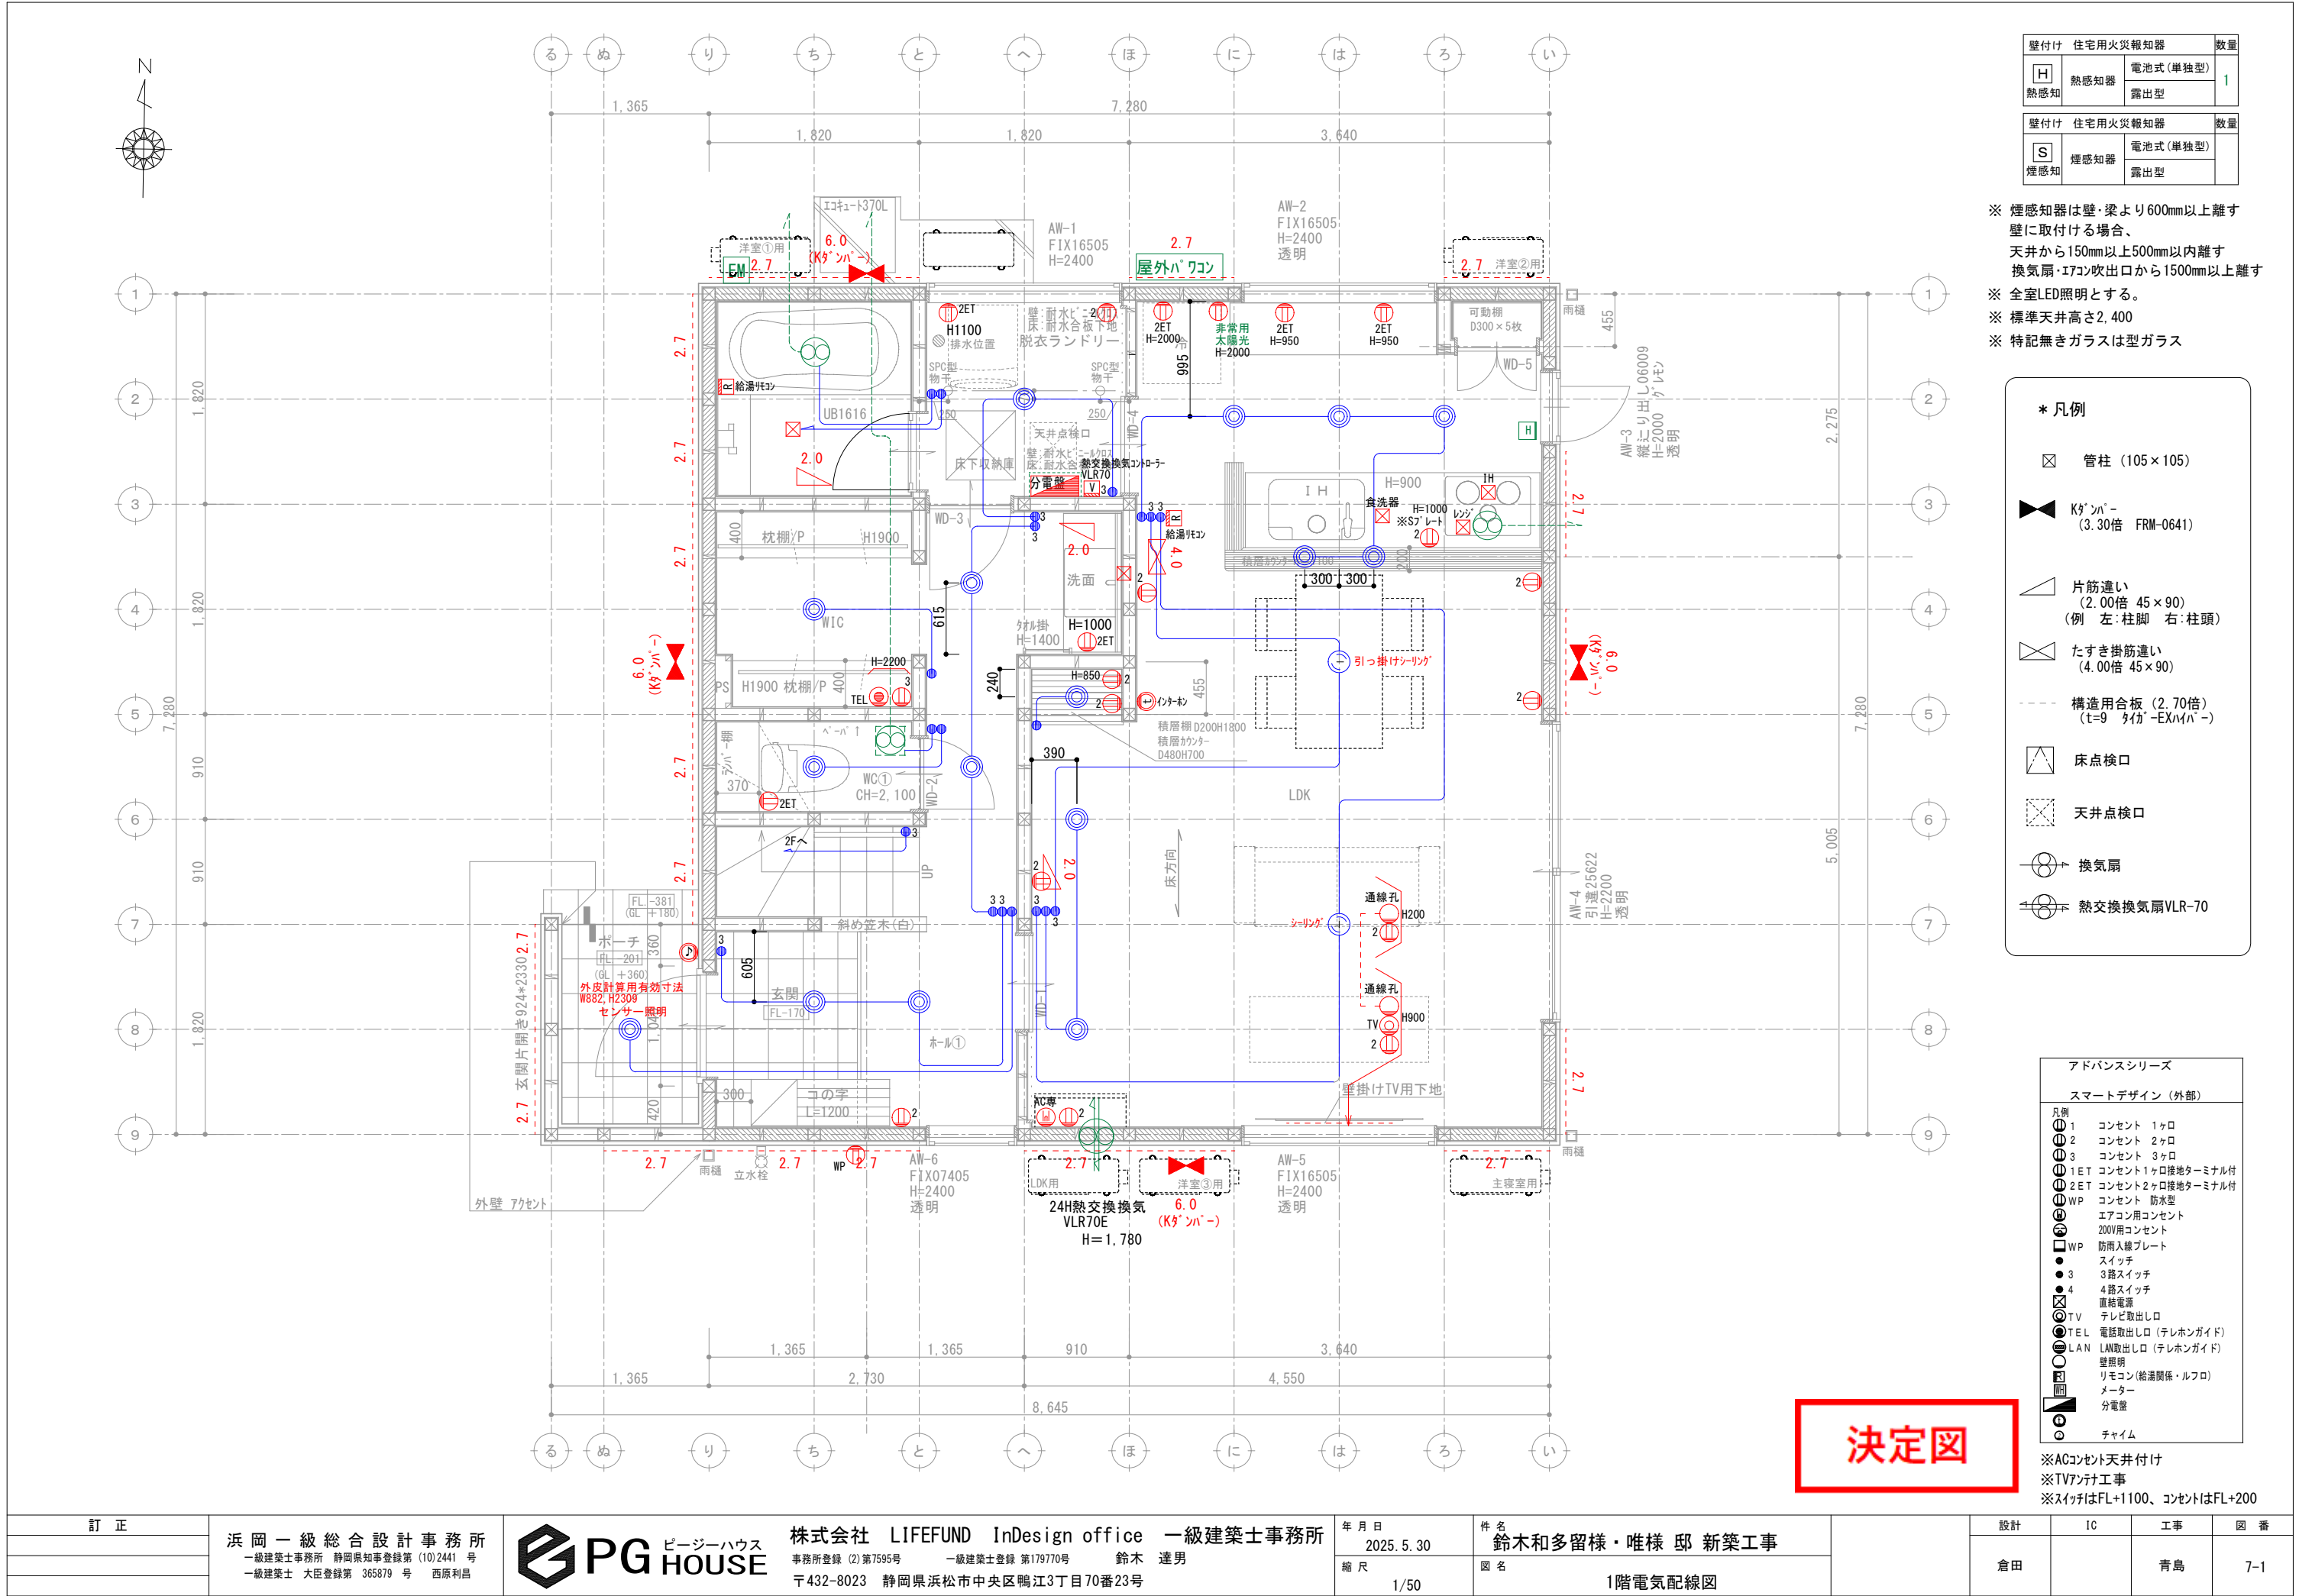

| 壁付け 住宅用火災報知器                          |      |          | 数量 |
|---------------------------------------|------|----------|----|
| <div><div>H</div><div>熱感知</div></div> | 熱感知器 | 電池式(単独型) | 1  |
|                                       |      | 露出型      |    |
| 壁付け 住宅用火災報知器                          |      |          | 数量 |
| <div><div>S</div><div>煙感知</div></div> | 煙感知器 | 電池式(単独型) |    |
|                                       |      | 露出型      |    |

※ 煙感知器は壁・梁より600mm以上離す  
壁に取付ける場合、  
天井から150mm以上500mm以内離す  
換気扇・エアコン吹出口から1500mm以上離す  
※ 全室LED照明とする。  
※ 標準天井高さ2,400  
※ 特記無きガラスは型ガラス

\* 凡例

管柱 (105×105)

Kダクト (3.30倍 FRM-0641)

片筋違い (2.00倍 45×90)  
(例 左:柱脚 右:柱頭)

たすき掛筋違い (4.00倍 45×90)

構造用合板 (2.70倍)  
(t=9 材種-EXハイパー)

床点検口


天井点検口

換気扇

熱交換換気扇VLR-70

| アドバンスシリーズ     |                  |       |     |
|---------------|------------------|-------|-----|
| スマートデザイン (外部) |                  |       |     |
| 凡例            | 1                | コンセント | 1ヶ所 |
| 2             | コンセント            | 2ヶ所   |     |
| 3             | コンセント            | 3ヶ所   |     |
| 1ET           | コンセント1ヶ所接地ターミナル付 |       |     |
| 2ET           | コンセント2ヶ所接地ターミナル付 |       |     |
| WP            | コンセント 防水型        |       |     |
| EA            | エアコン用コンセント       |       |     |
| 200V          | 200V用コンセント       |       |     |
| WP            | 防雨入線プレート         |       |     |
| スイッチ          | スイッチ             |       |     |
| 3             | 3路スイッチ           |       |     |
| 4             | 4路スイッチ           |       |     |
| 直結電源          | 直結電源             |       |     |
| TV            | テレビ取出口           |       |     |
| TEL           | 電話取出口 (テレホンガイド)  |       |     |
| LAN           | LAN取出口 (テレホンガイド) |       |     |
| 壁照明           | 壁照明              |       |     |
| リモコン          | リモコン (給湯関係・ルフロ)  |       |     |
| メーター          | メーター             |       |     |
| 分電盤           | 分電盤              |       |     |
| チャイム          | チャイム             |       |     |

※ACコンセント天井付け  
※TVアンテナ工事  
※スイッチはFL+1100、コンセントはFL+200

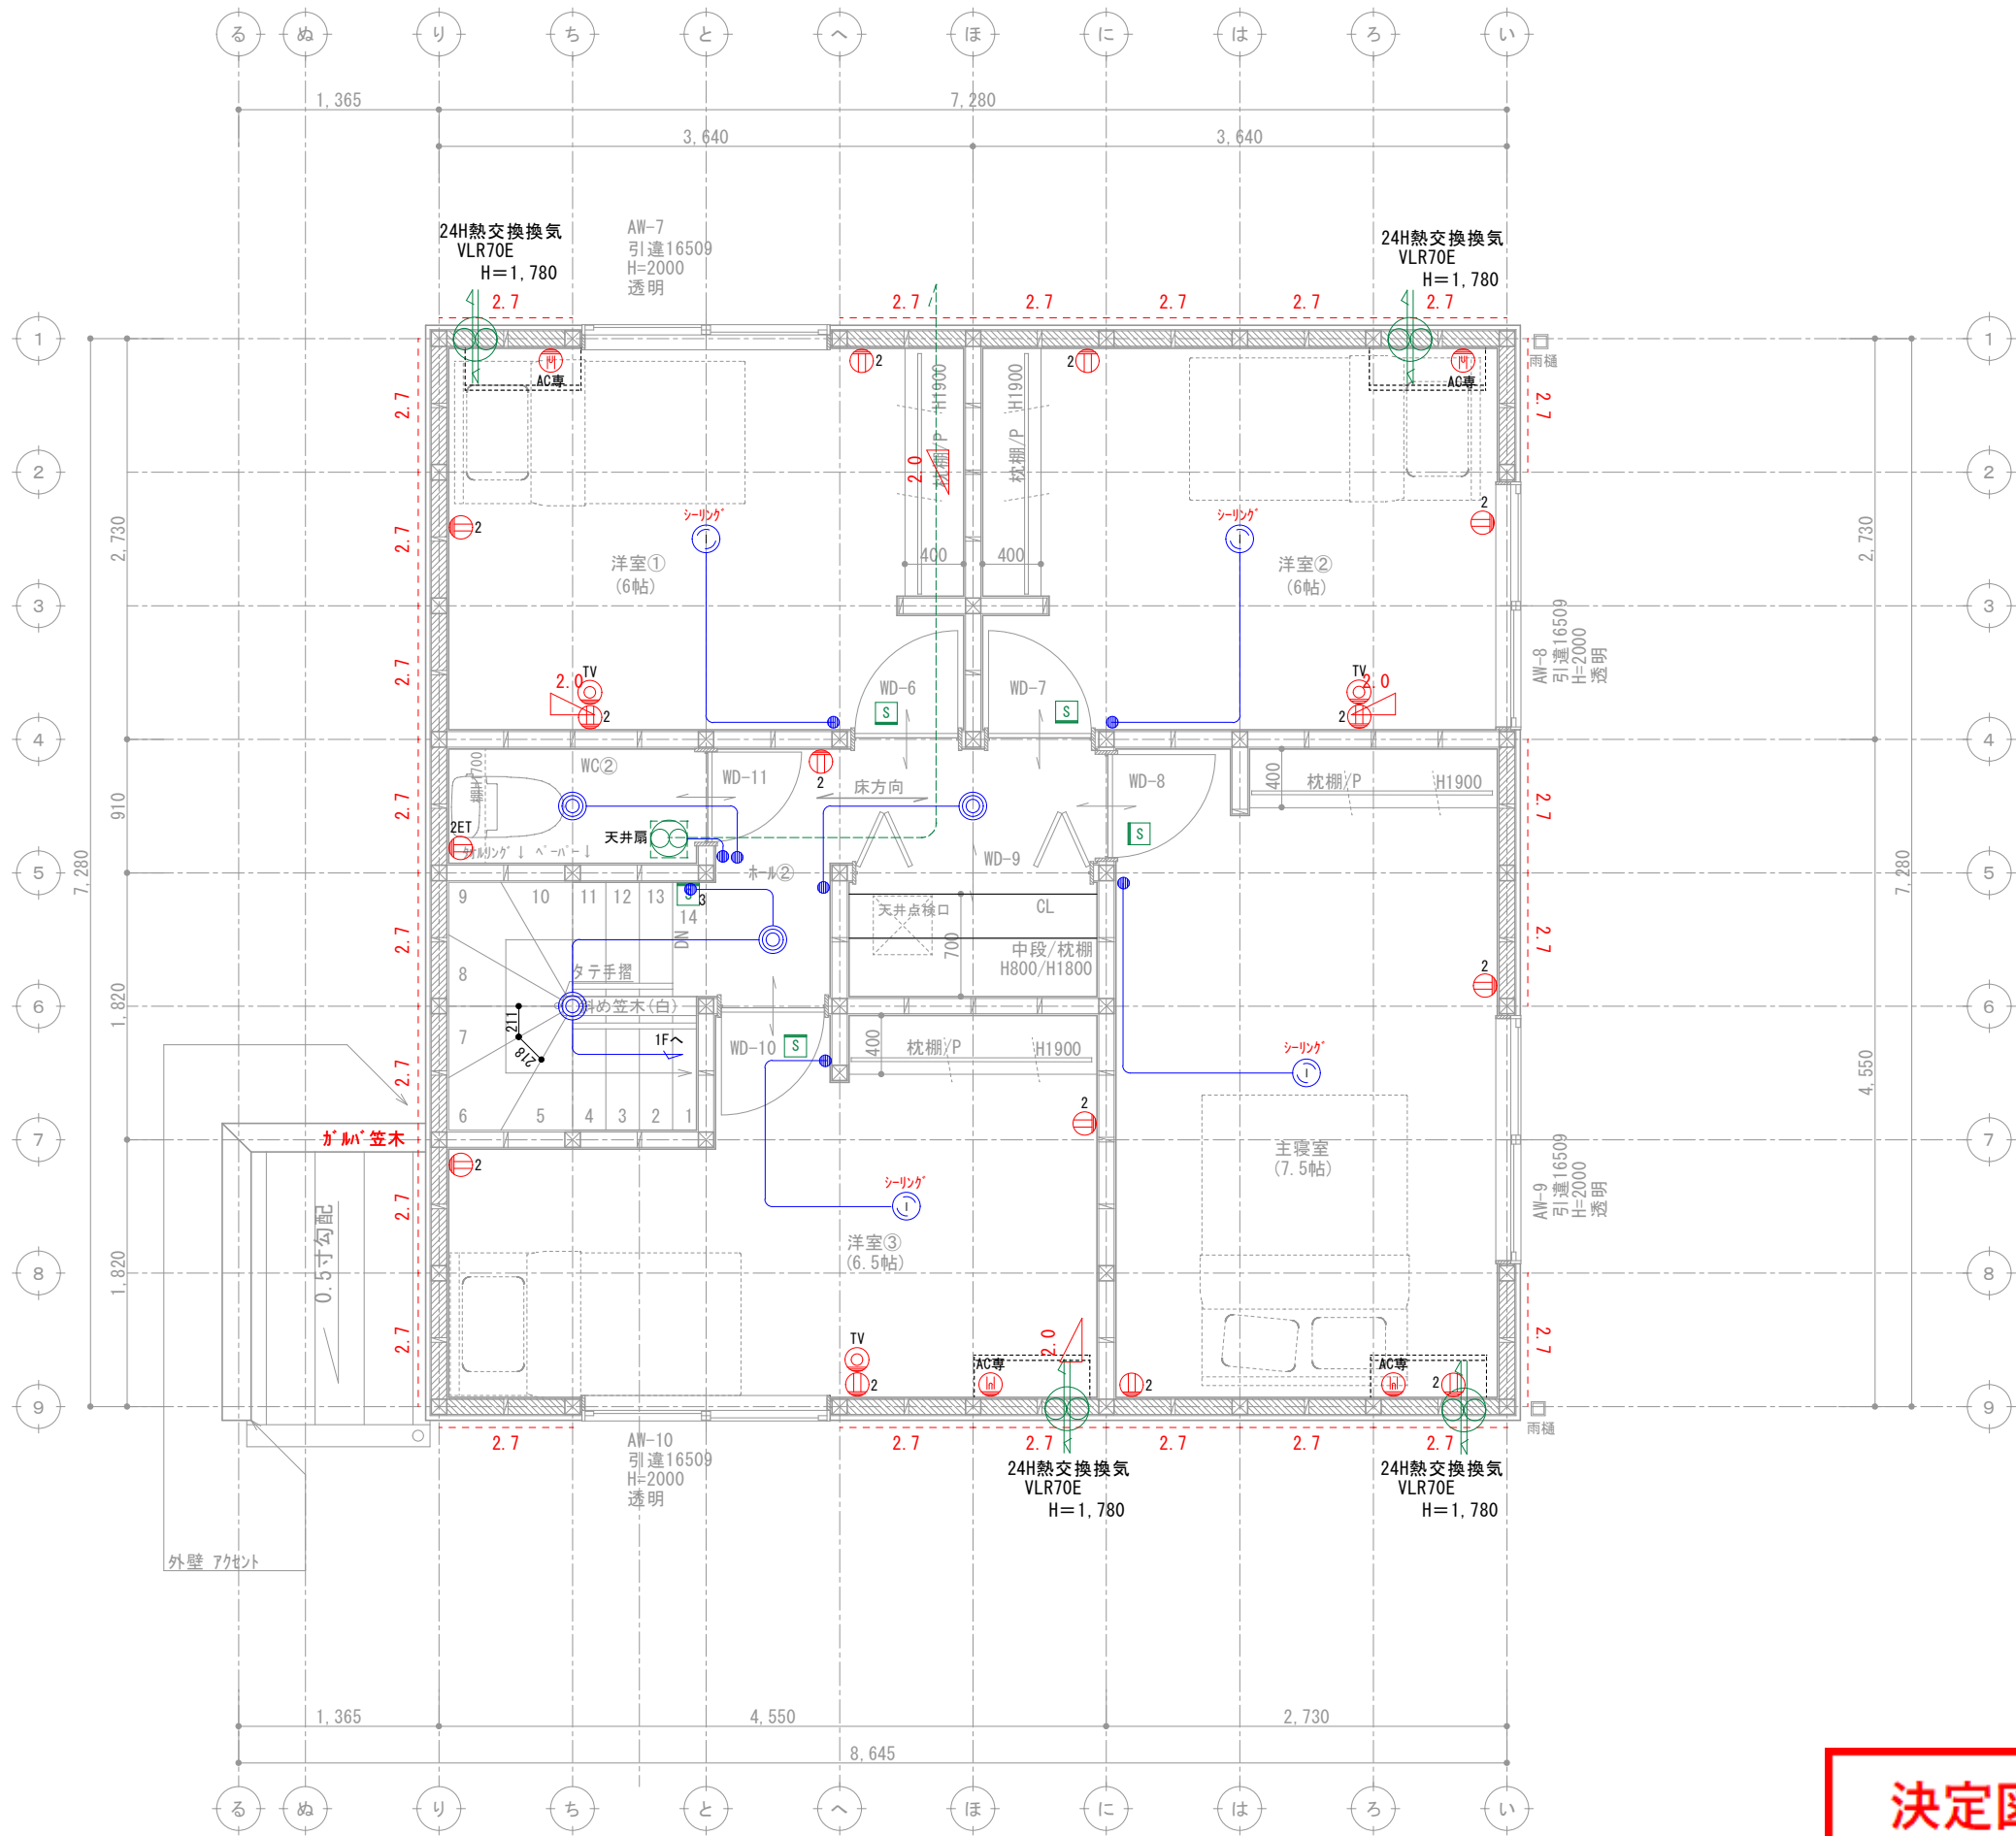

| 壁付け 住宅用火災報知器 |      |          | 数量 |
|--------------|------|----------|----|
| H<br>熱感知     | 熱感知器 | 電池式(単独型) | 4  |
|              |      | 露出型      |    |
| 壁付け 住宅用火災報知器 |      |          | 数量 |
| S<br>煙感知     | 煙感知器 | 電池式(単独型) | 4  |
|              |      | 露出型      |    |

※ 煙感知器は壁・梁より600mm以上離す  
壁に取付ける場合、  
天井から150mm以上500mm以内離す  
換気扇・エアコン吹出口から1500mm以上離す  
※ 全室LED照明とする。  
※ 標準天井高さ2,400  
※ 特記無きガラスは型ガラス

\* 凡例



- 管柱 (105×105)
- Kタツバ (3.30倍 FRM-0641)
- 片筋違い (2.00倍 45×90)  
(例 左:柱脚 右:柱頭)
- たすき掛筋違い (4.00倍 45×90)
- 構造用合板 (2.70倍)  
(t=9 3枚 EXハイパー)
- 床点検口
- 天井点検口
- 換気扇
- 熱交換換気扇VLR-70

| アドバンスシリーズ     |                  |       |     |
|---------------|------------------|-------|-----|
| スマートデザイン (外部) |                  |       |     |
| 凡例            | 1                | コンセント | 1ヶ所 |
| 2             | コンセント            | 2ヶ所   |     |
| 3             | コンセント            | 3ヶ所   |     |
| 1ET           | コンセント1ヶ所接地ターミナル付 |       |     |
| 2ET           | コンセント2ヶ所接地ターミナル付 |       |     |
| WP            | コンセント            | 防水型   |     |
| WP            | エアコン用コンセント       |       |     |
| WP            | 200V用コンセント       |       |     |
| WP            | 防雨入線プレート         |       |     |
| ●             | スイッチ             |       |     |
| ●             | 3路スイッチ           |       |     |
| ●             | 4路スイッチ           |       |     |
| ●             | 直結電源             |       |     |
| TV            | テレビ取出口           |       |     |
| TEL           | 電話取出口 (テレホンガイド)  |       |     |
| LAN           | LAN取出口 (テレホンガイド) |       |     |
| 壁照明           | リモコン (給湯関係・ルフロ)  |       |     |
| メーター          | メーター             |       |     |
| 分電盤           | 分電盤              |       |     |
| チャイム          | チャイム             |       |     |

※ACコンセント天井付け  
※TVアンテナ工事  
※スイッチはFL+1100、コンセントはFL+200

決定図



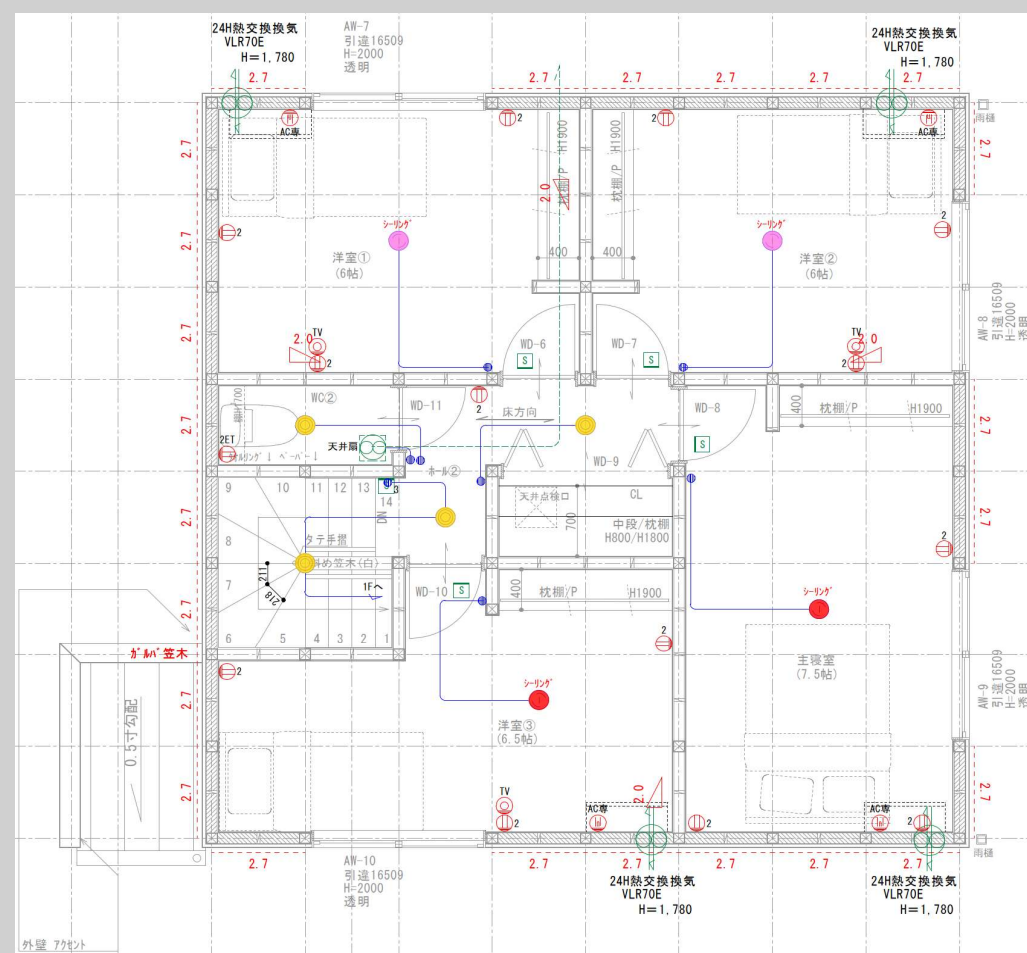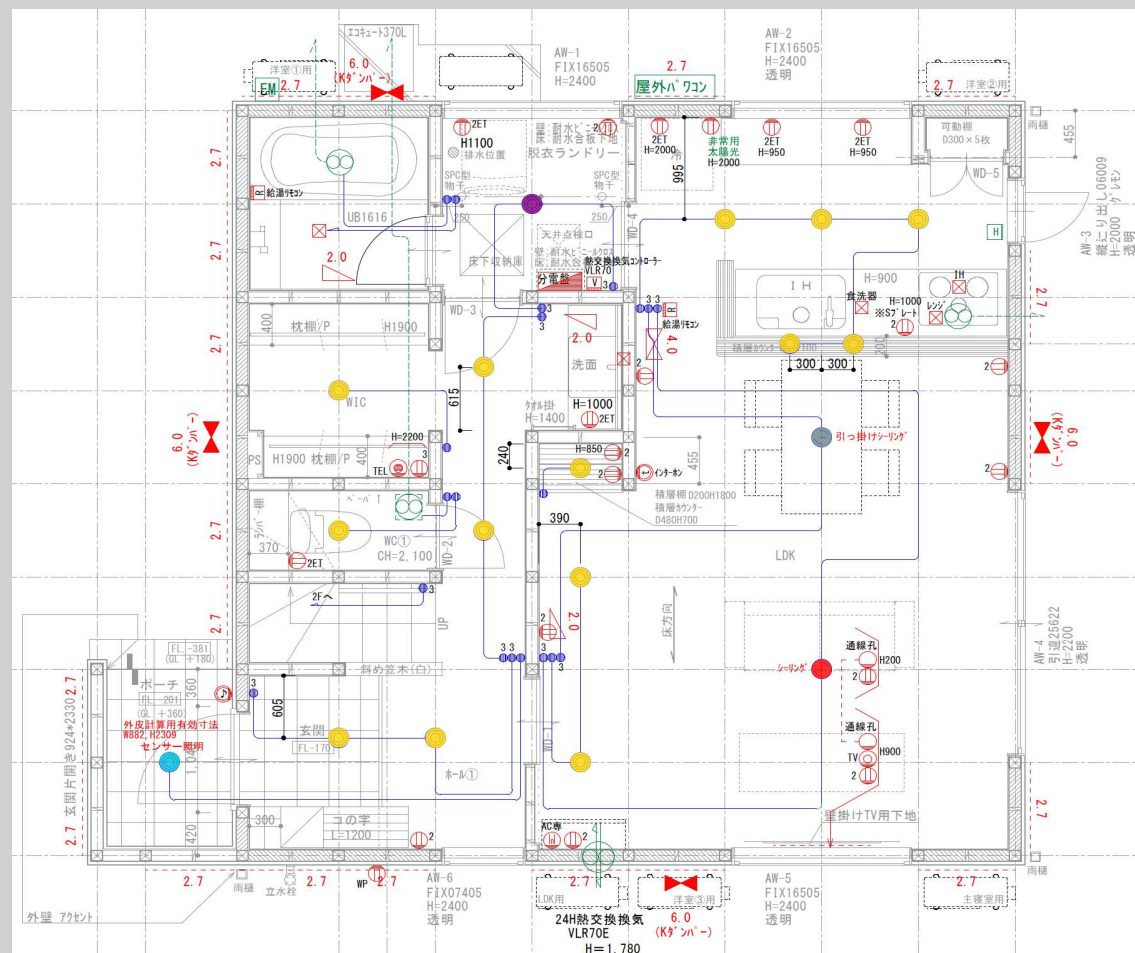

ト アホソ: VL-SZ30KL  
(Panasonic)



## 基本照明ダ ウンライト

## 脱衣ランドリー

ダ ウンライト

DDL\_6102AW

洋室①、洋室②

シーリング<sup>®</sup> ライト

**DCL\_40507**

LDK、洋室③、主寝室

●  $\times 3$

シーリング ライト

**DCL\_40508**

## 引っ掛けシーリング


●  $\times 1$




2025.5.30

(図面 7-3)



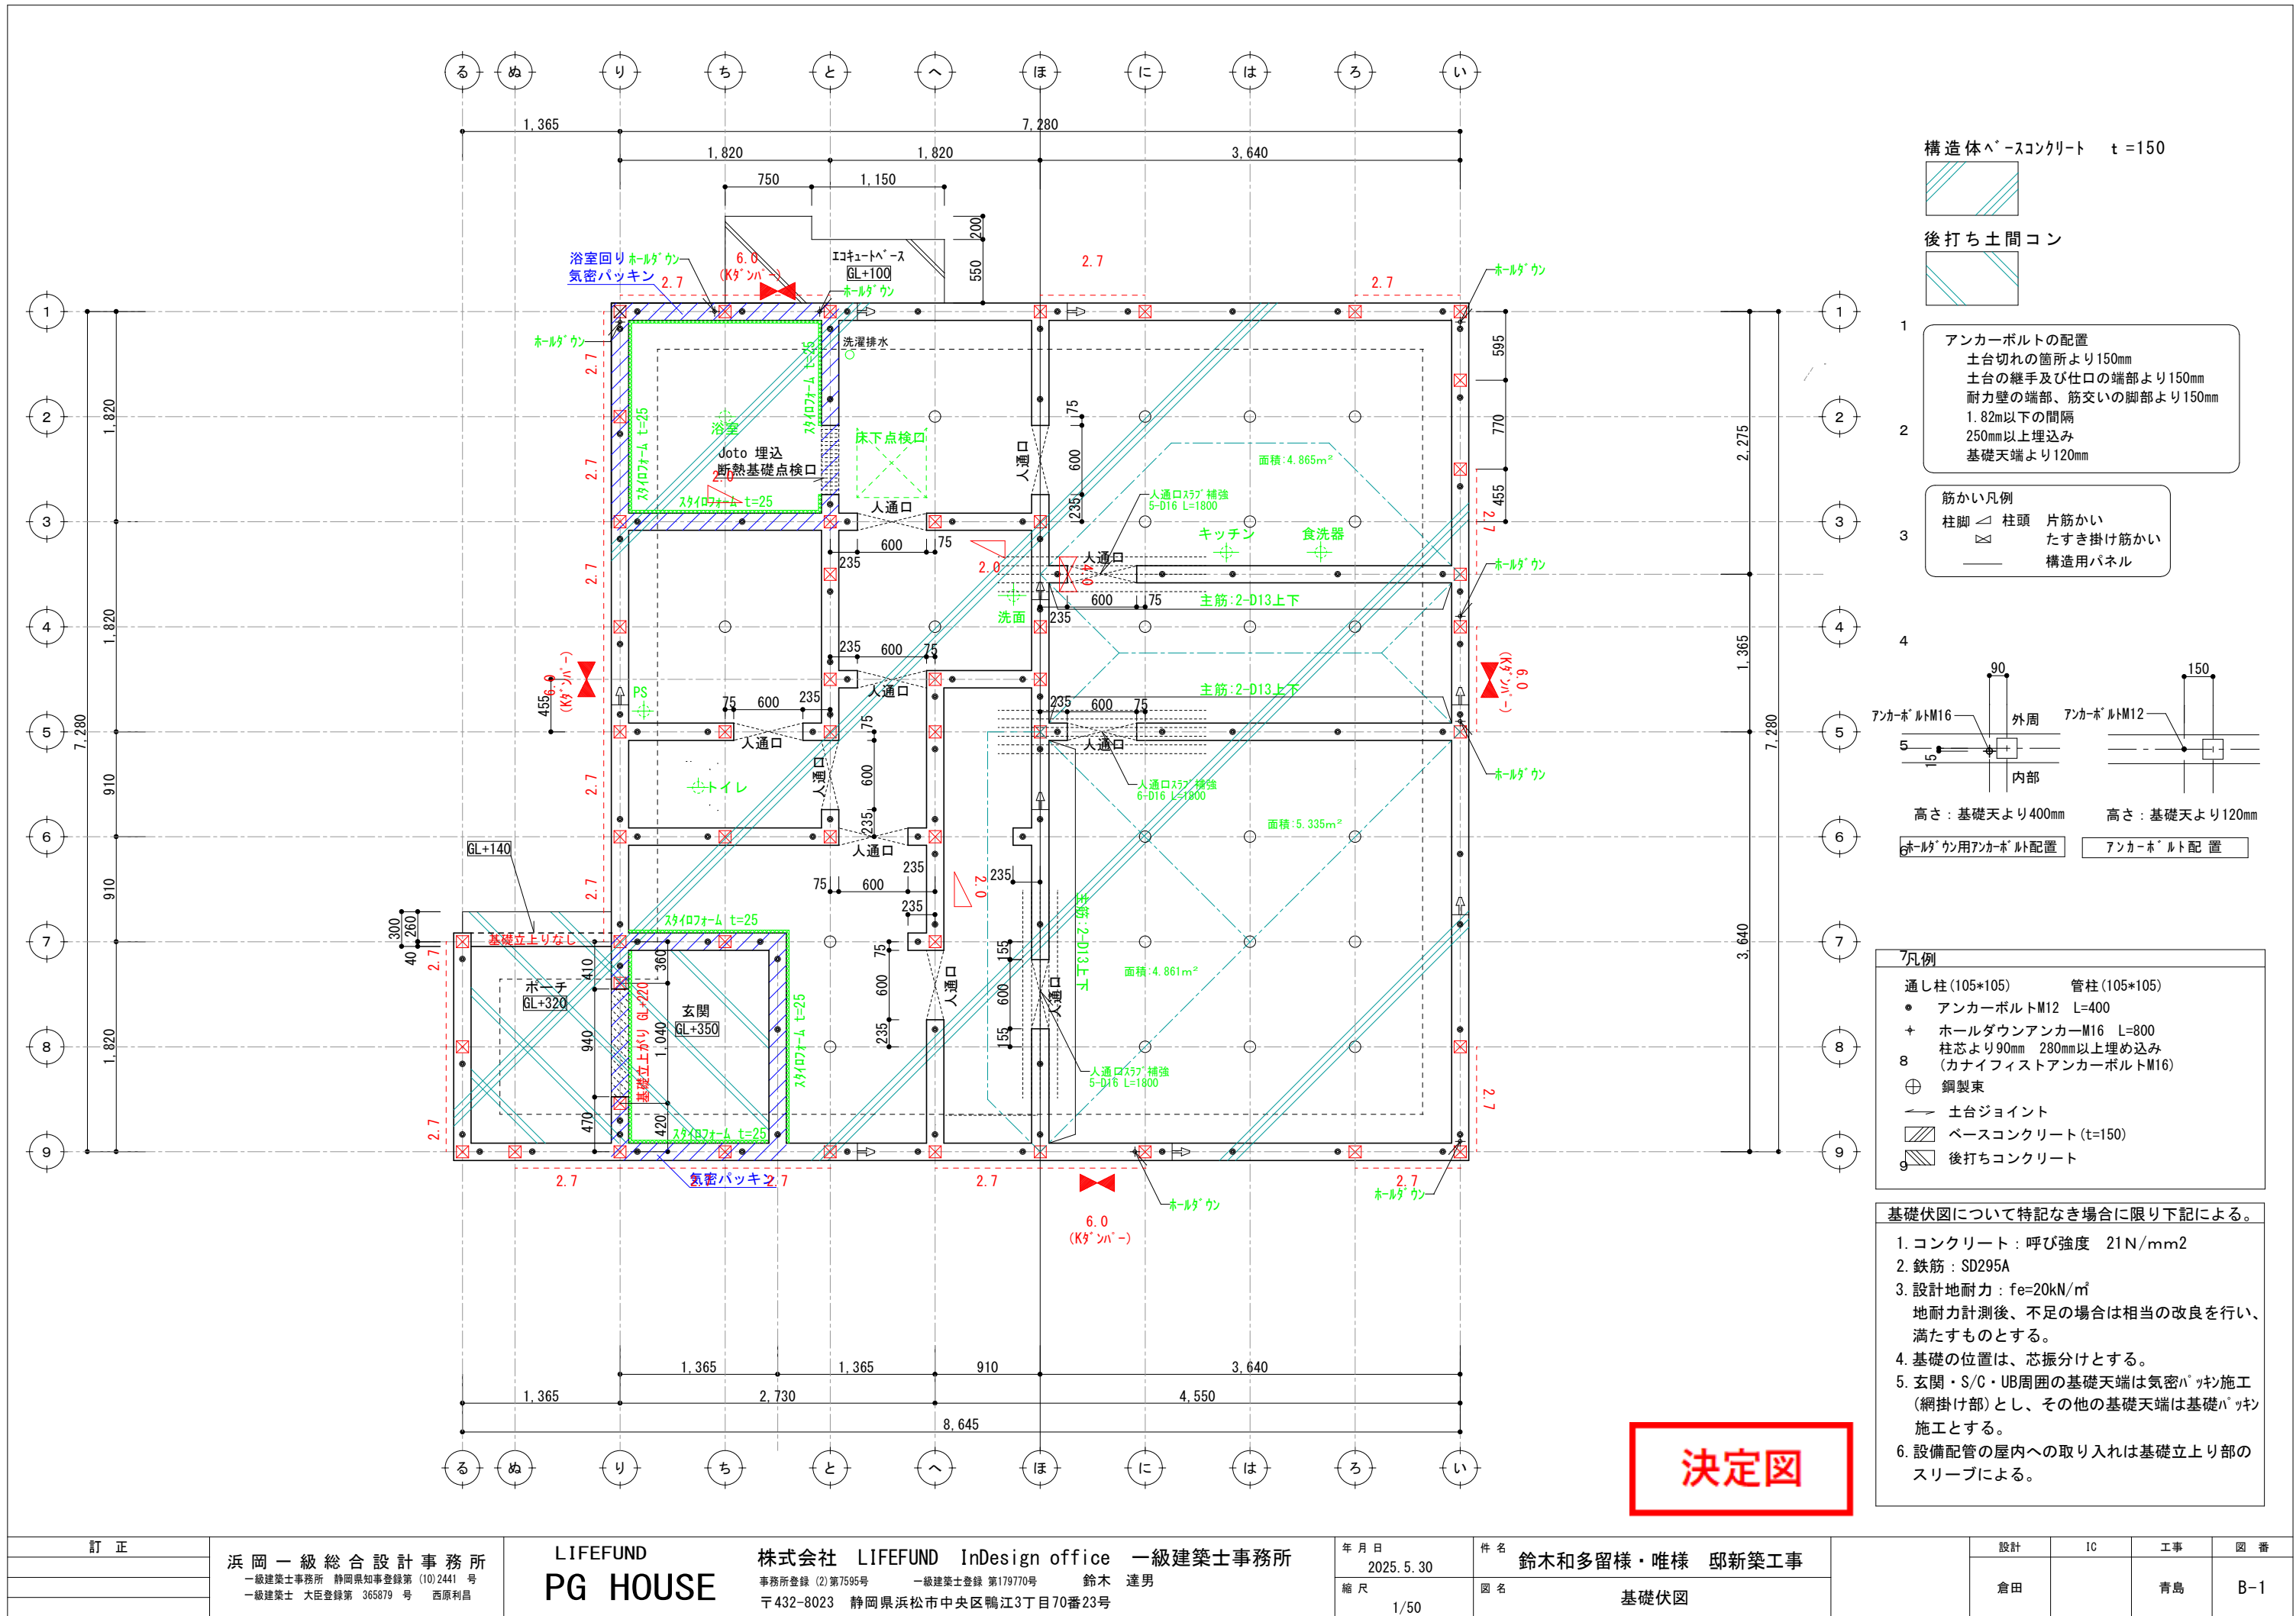

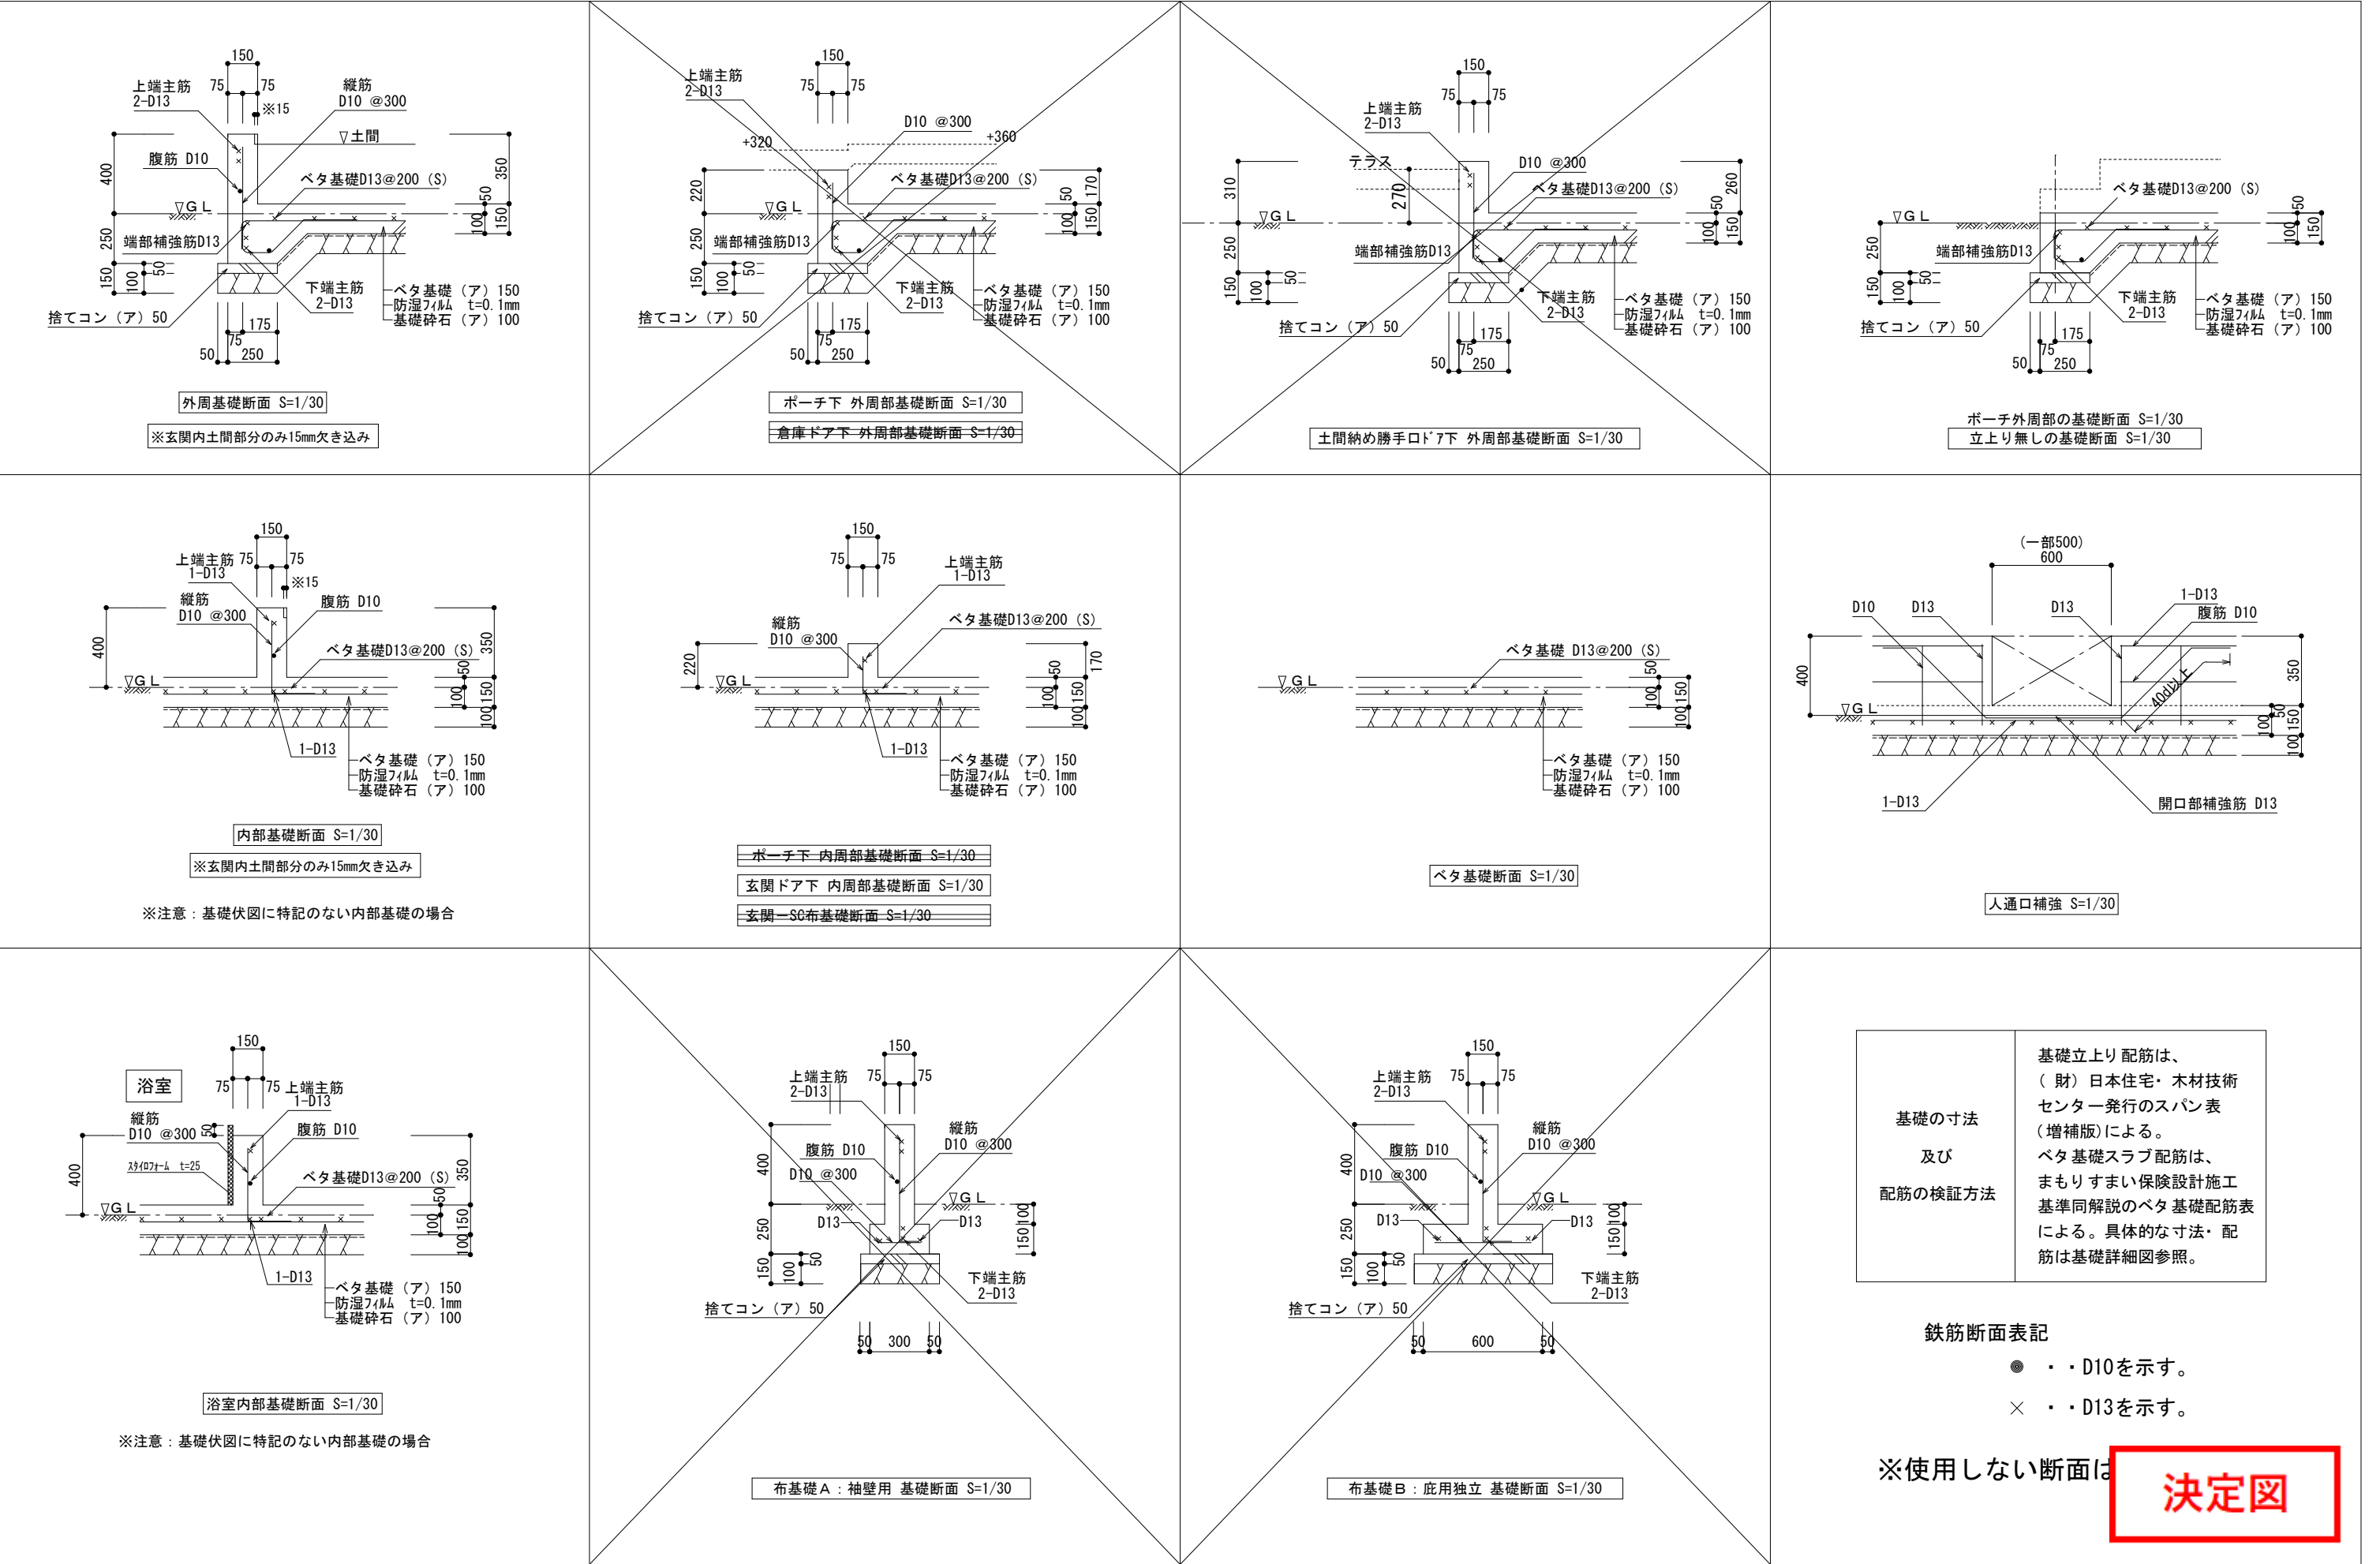

基礎の寸法  
及び  
配筋の検証方法


基礎立上り配筋は、  
(財)日本住宅・木材技術  
センター発行のスパン表  
(増補版)による。  
ベタ基礎スラブ配筋は、  
まもりすまい保険設計施工  
基準同解説のベタ基礎配筋表  
による。具体的な寸法・配  
筋は基礎詳細図参照。

鉄筋断面表記


●・・・D10を示す。  
×・・・D13を示す。

※使用しない断面は

**決定図**

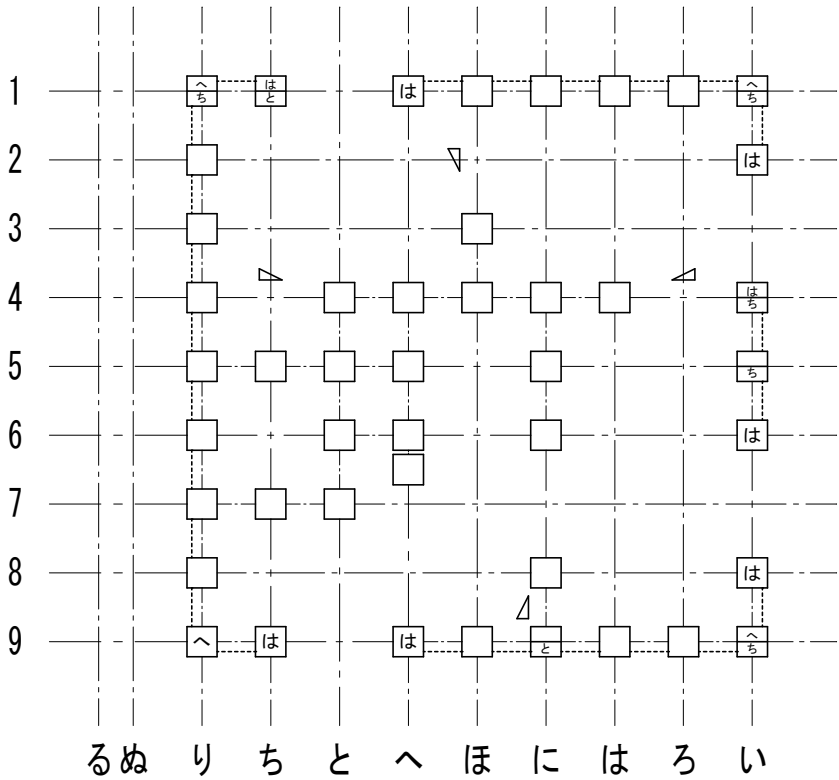

2階柱壁伏図

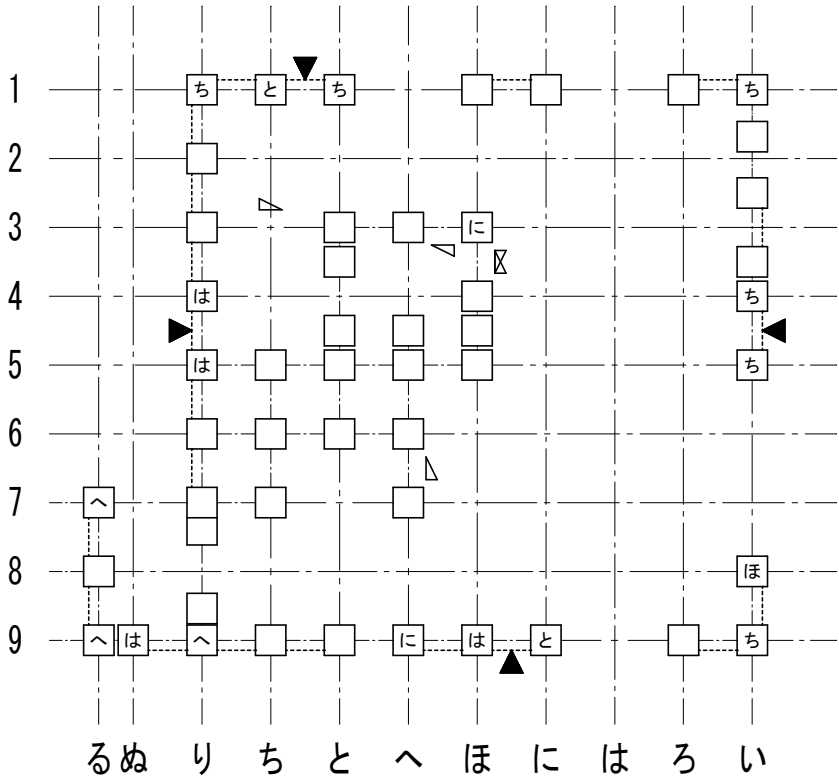

1階柱壁伏図

| 接合部凡例 <small>*接合部凡例はユーザ設定されたものです。</small> |                                |      |      |
|-------------------------------------------|--------------------------------|------|------|
| 記号                                        | 仕様（カナイ金物）                      | N    | 倍率   |
| SBCP                                      | スリムビルドコーナー75, チビクリCK(化粧柱の場合)   | 0.00 | 1.00 |
| SBCP                                      | スリムビルドコーナー75, チビクリCK(化粧柱の場合)   | 0.65 | 1.00 |
| SBCP                                      | は スリムビルドコーナー75                 | 1.00 | 1.00 |
| ARCG                                      | に アレントコーナー合板用                  | 1.40 | 2.20 |
| ARCG                                      | ほ アレントコーナー合板用                  | 1.60 | 2.20 |
| ARCG                                      | へ アレントコーナー合板用                  | 1.80 | 2.20 |
| HD15                                      | と ブレイブホールダウン B-HD15            | 2.80 | 3.60 |
| HD20                                      | ち ブレイブホールダウン B-HD20            | 3.70 | 4.70 |
| HD25                                      | り ブレイブホールダウン B-HD25            | 4.70 | 4.80 |
| HD30                                      | ぬ ブレイブホールダウン B-HD30            | 5.60 | 7.20 |
| J1                                        | る 腰掛け蟻若しくは大入れ蟻掛け+羽子板ボルト、短冊金物   |      | 1.90 |
| J2                                        | を 腰掛け蟻若しくは大入れ蟻掛け+羽子板ボルト、短冊金物×2 |      | 3.00 |

※表示なき金物は「は」とする。 梁継手・仕口用

| 接合部凡例 <small>*接合部凡例はユーザ設定されたものです。</small> |                                |      |      |
|-------------------------------------------|--------------------------------|------|------|
| 記号                                        | 仕様（タナカ金物）                      | N    | 倍率   |
| FCP                                       | フックコーナー, チビクリCK(化粧柱の場合)        | 0.00 | 1.00 |
| FCP                                       | フックコーナー, チビクリCK(化粧柱の場合)        | 0.65 | 1.00 |
| FCP                                       | は フックコーナー                      | 1.00 | 1.00 |
| CCP                                       | に シナコーナー                       | 1.40 | 2.20 |
| CCP                                       | ほ シナコーナー                       | 1.60 | 2.20 |
| CCP                                       | へ シナコーナー                       | 1.80 | 2.20 |
| HD15                                      | と ビス止めホールダウンU HD15             | 2.80 | 3.60 |
| HD20                                      | ち ビス止めホールダウンU HD20             | 3.70 | 4.70 |
| HD25                                      | り ビス止めホールダウンU HD25             | 4.70 | 4.80 |
| HD30                                      | ぬ ビス止めホールダウンU HD15×2 (HD35)    | 5.60 | 7.20 |
| J1                                        | る 腰掛け蟻若しくは大入れ蟻掛け+羽子板ボルト、短冊金物   |      | 1.90 |
| J2                                        | を 腰掛け蟻若しくは大入れ蟻掛け+羽子板ボルト、短冊金物×2 |      | 3.00 |

※表示なき金物は「は」とする。 梁継手・仕口用

| 筋かいの種類に応じた筋かいの端部の接合部の仕様 |           |                                                                                                |
|-------------------------|-----------|------------------------------------------------------------------------------------------------|
|                         | 筋かいの種類    | 接合部の仕様（構造方法）                                                                                   |
| イ                       | 鉄筋φ9      | 柱又は横架材を貫通し、三角座金を介してナット締め、又は鋼板添え板を用い鋼板を柱及び横架材にCN90, 8本平打ち                                       |
| ロ                       | 筋かい:15×90 | 柱・横架材を欠き込み、柱・横架材双方に対してN65, 5本平打ち                                                               |
| ハ                       | 筋かい:30×90 | 鋼板添え板t=1.6mmを筋かいに対してボルトφ12及びCN65, 3本平打ち、柱に対してCN65, 3本平打ち、横架材に対してCN65, 4本平打ち。筋かいプレートBP同等品       |
| ニ                       | 筋かい:45×90 | 鋼板添え板t=2.3mmを筋かいに対してボルトφ12及びスクリュー釘φ4.5L50, 7本平打ち、柱及び横架材に対してスクリュー釘φ4.5L50, 5本平打ち。筋かいプレートBP-2同等品 |
| ホ                       | 筋かい:90×90 | 柱又は横架材にボルトφ12mmを用いて一面剪断接合                                                                      |


| 胴差と通し柱の接合部の仕様 |                                                                 |                                           |
|---------------|-----------------------------------------------------------------|-------------------------------------------|
|               | 胴差と通し柱の条件                                                       | 仕口                                        |
| T1            | 通し柱の片側に胴差が来る場合                                                  | 胴差を柱にかたぎ大入れ短ほぞ差しの上、羽子板ボルト、かね折り金物又は同等以上の仕口 |
| T2            | 通し柱の両側に胴差が来る場合                                                  | 胴差を柱にかたぎ大入れ短ほぞ差しの上、短冊金物又は、同等以上の仕口で胴差相互を緊結 |
| T3            | 通し柱と胴差の接合部の近くに90×90以上の筋かいが来る場合(通し柱が建物の出隅にあるか、筋かい壁が外壁と直交して接する場合) | 胴差を通し柱に、15KN用引き寄せ金物を水平に用いて緊結              |

決定図







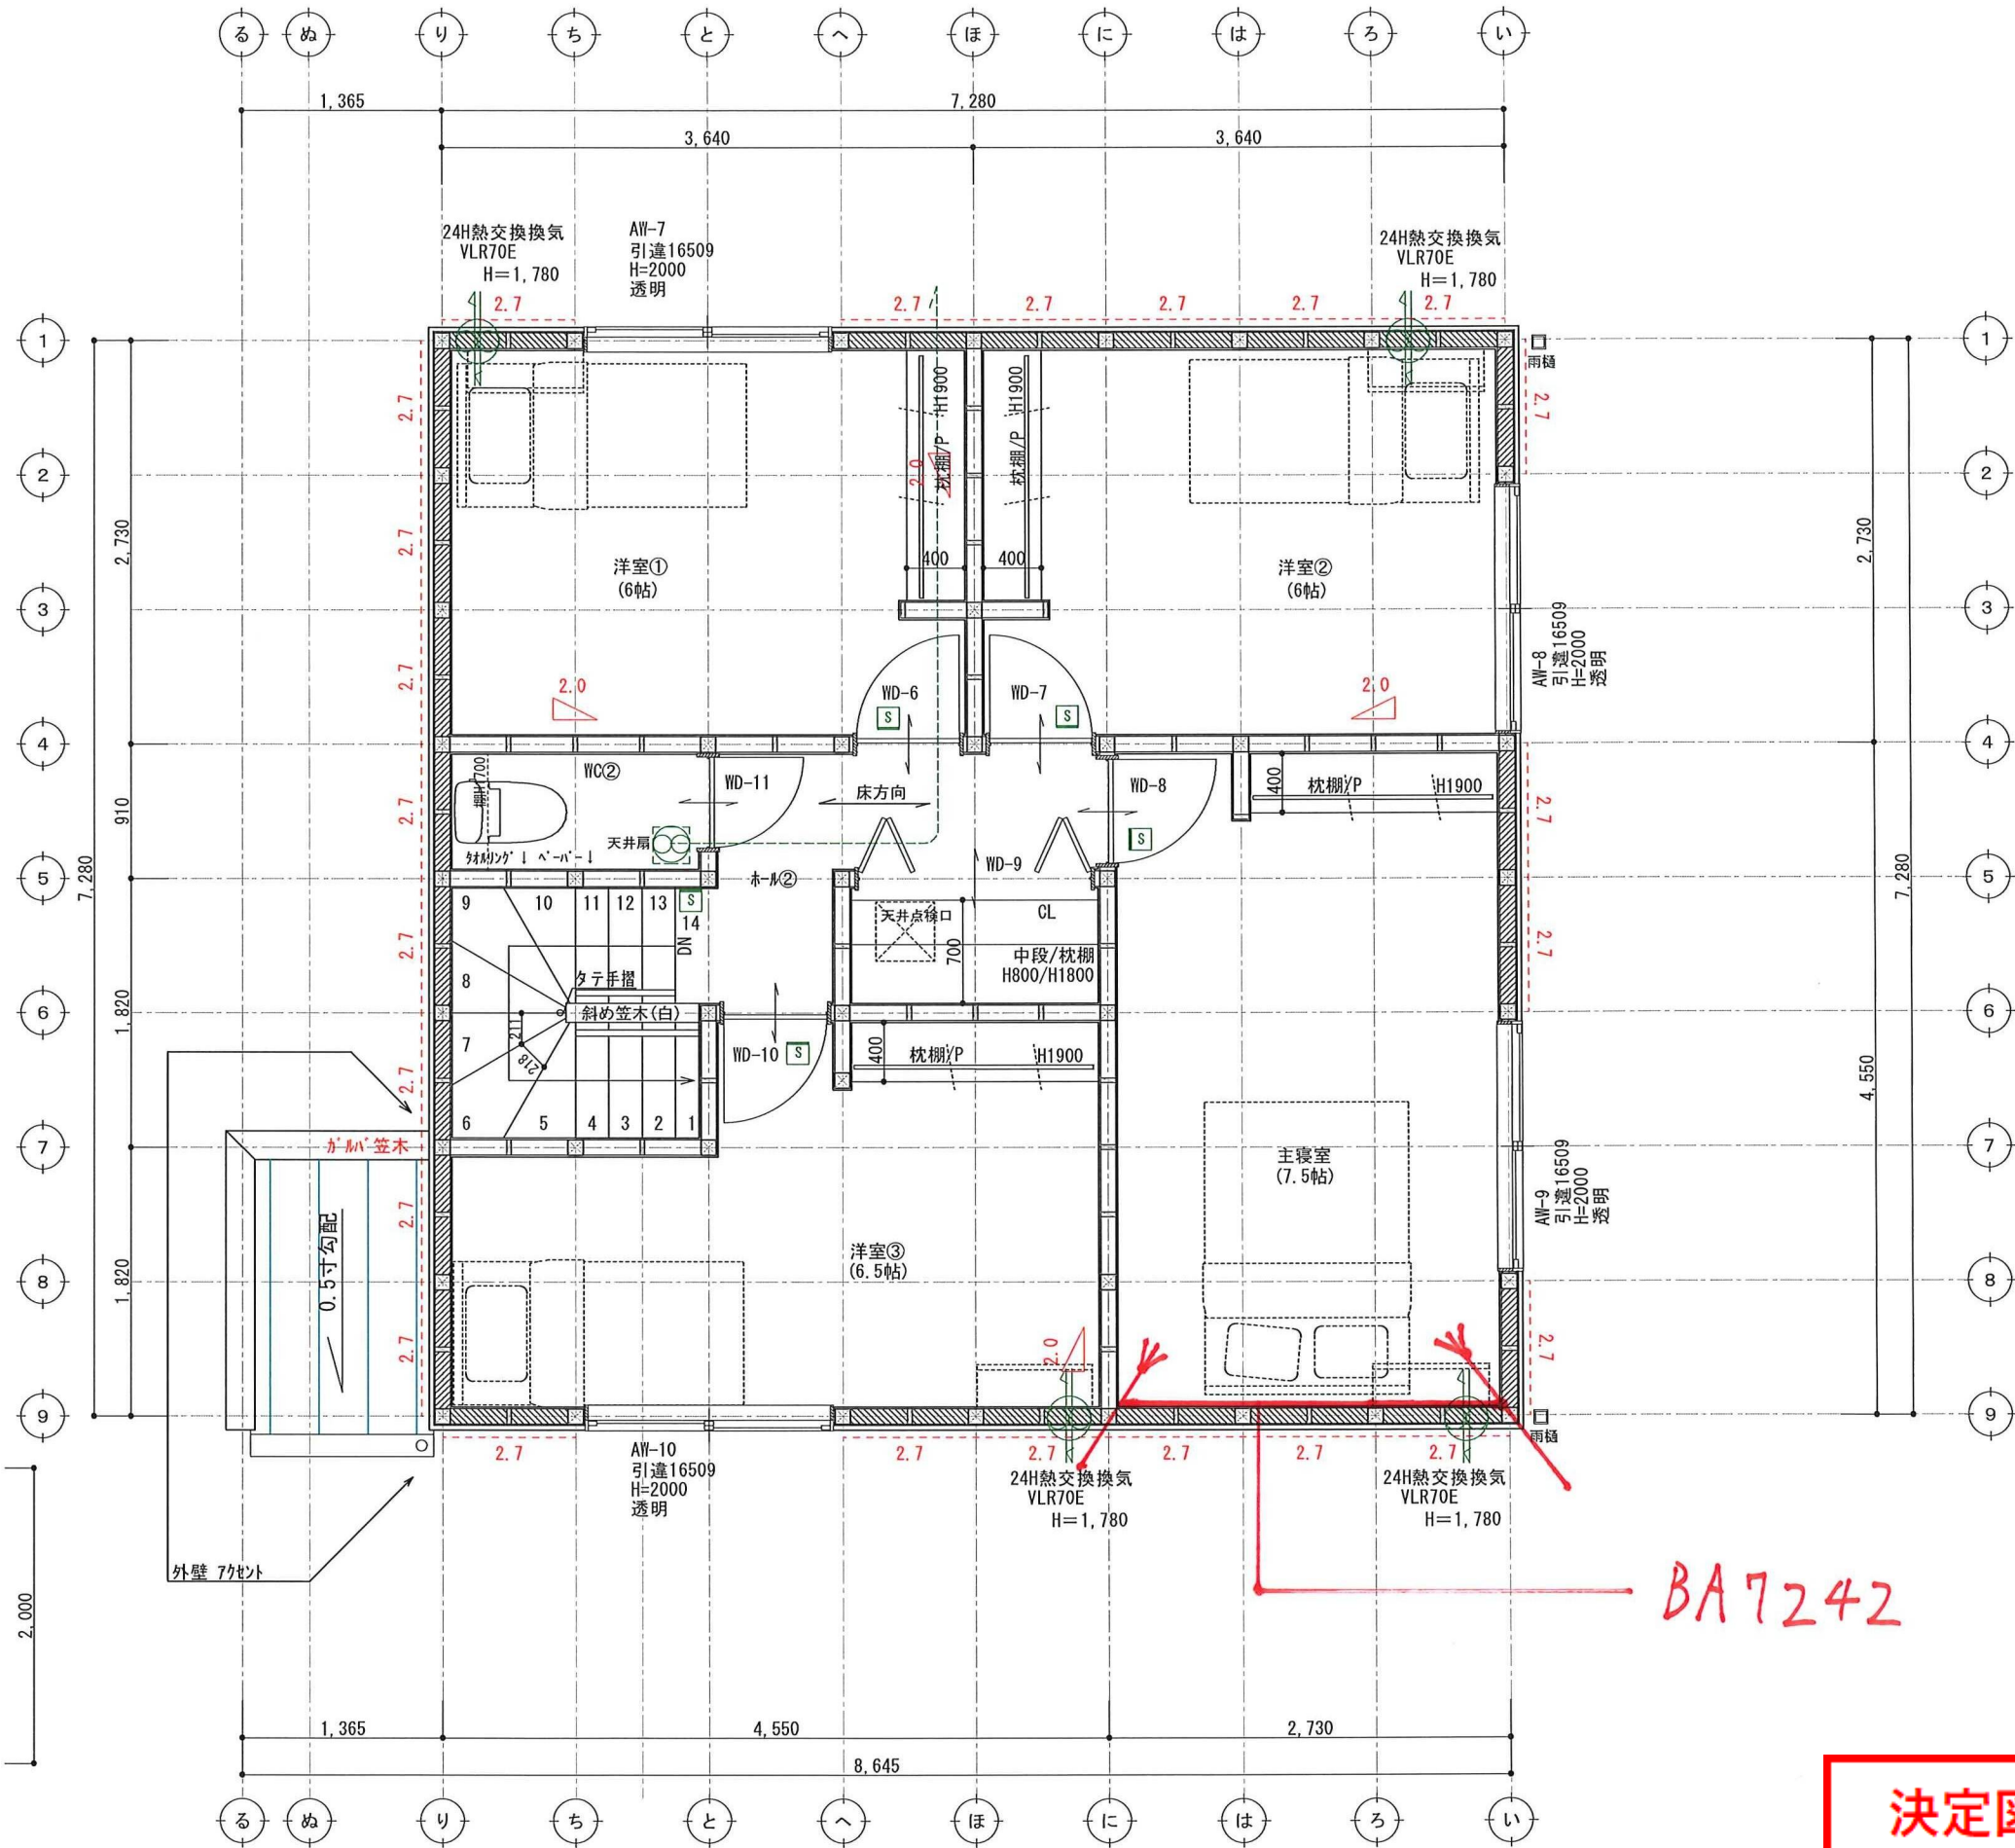

| 壁付付 住宅用火災報知器                |      |          | 数量 |
|-----------------------------|------|----------|----|
| <div>H</div> <div>熱感知</div> | 熱感知器 | 電池式(単独型) |    |
|                             |      | 露出型      |    |
| 壁付付 住宅用火災報知器                |      |          | 数量 |
| <div>S</div> <div>煙感知</div> | 煙感知器 | 電池式(単独型) | 4  |
|                             |      | 露出型      |    |

※ 煙感知器は壁・梁より600mm以上離す  
壁に取付ける場合、  
天井から150mm以上500mm以内離す  
換気扇・エアコン吹出口から1500mm以上離す  
※ 全室LED照明とする。  
※ 標準天井高さ2,400  
※ 特記無きガラスは型ガラス

\* 凡例

- ☒ 管柱 (105×105)
- ◀▶ K'ハバ (3.30倍 FRM-0641)
- △ 片筋違い (2.00倍 45×90)  
(例 左:柱脚 右:柱頭)
- ⊠ たすき掛筋違い (4.00倍 45×90)
- 構造用合板 (2.70倍)  
(t=9 タイガ-EXハイパー)
- △ 床点検口
- ⊠ 天井点検口
- ⊙ 換気扇
- ⊙ 熱交換換気扇VLR-70

| アドバンスシリーズ     |     |                  |     |
|---------------|-----|------------------|-----|
| スマートデザイン (外部) |     |                  |     |
| 凡例            | 1   | コンセント            | 1ヶ所 |
| ①             | 2   | コンセント            | 2ヶ所 |
| ②             | 3   | コンセント            | 3ヶ所 |
| ③             | 1ET | コンセント1ヶ所接地ターミナル付 |     |
| ④             | 2ET | コンセント2ヶ所接地ターミナル付 |     |
| ⑤             | WP  | コンセント 防水型        |     |
| ⑥             | ⑦   | エアコン用コンセント       |     |
| ⑧             | ⑨   | 200V用コンセント       |     |
| ⑩             | WP  | 防雨入替プレート         |     |
| ⑪             | ⑫   | スイッチ             |     |
| ⑬             | ⑭   | 3路スイッチ           |     |
| ⑮             | ⑯   | 4路スイッチ           |     |
| ⑰             | ⑱   | 直結電源             |     |
| ⑲             | ⑳   | テレビ取出口           |     |
| ㉑             | ㉒   | 電話取出口 (テレホンガイド)  |     |
| ㉓             | ㉔   | LAN取出口 (テレホンガイド) |     |
| ㉕             | ㉖   | 壁照明              |     |
| ㉗             | ㉘   | リモコン(給湯関係・ルフロ)   |     |
| ㉙             | ㉚   | メーター             |     |
| ㉛             | ㉜   | 分電盤              |     |
| ㉝             | ㉞   | チャイム             |     |

※ACコンセント天井付け  
※TVアンテナ工事  
※スイッチはFL+1100、コンセントはFL+200

決定図

BA7242