
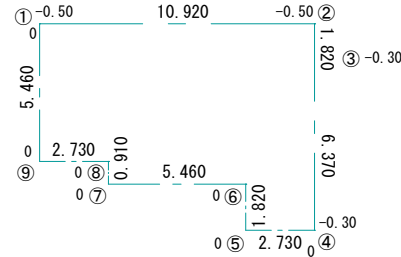


湖西市境宿地内

G2

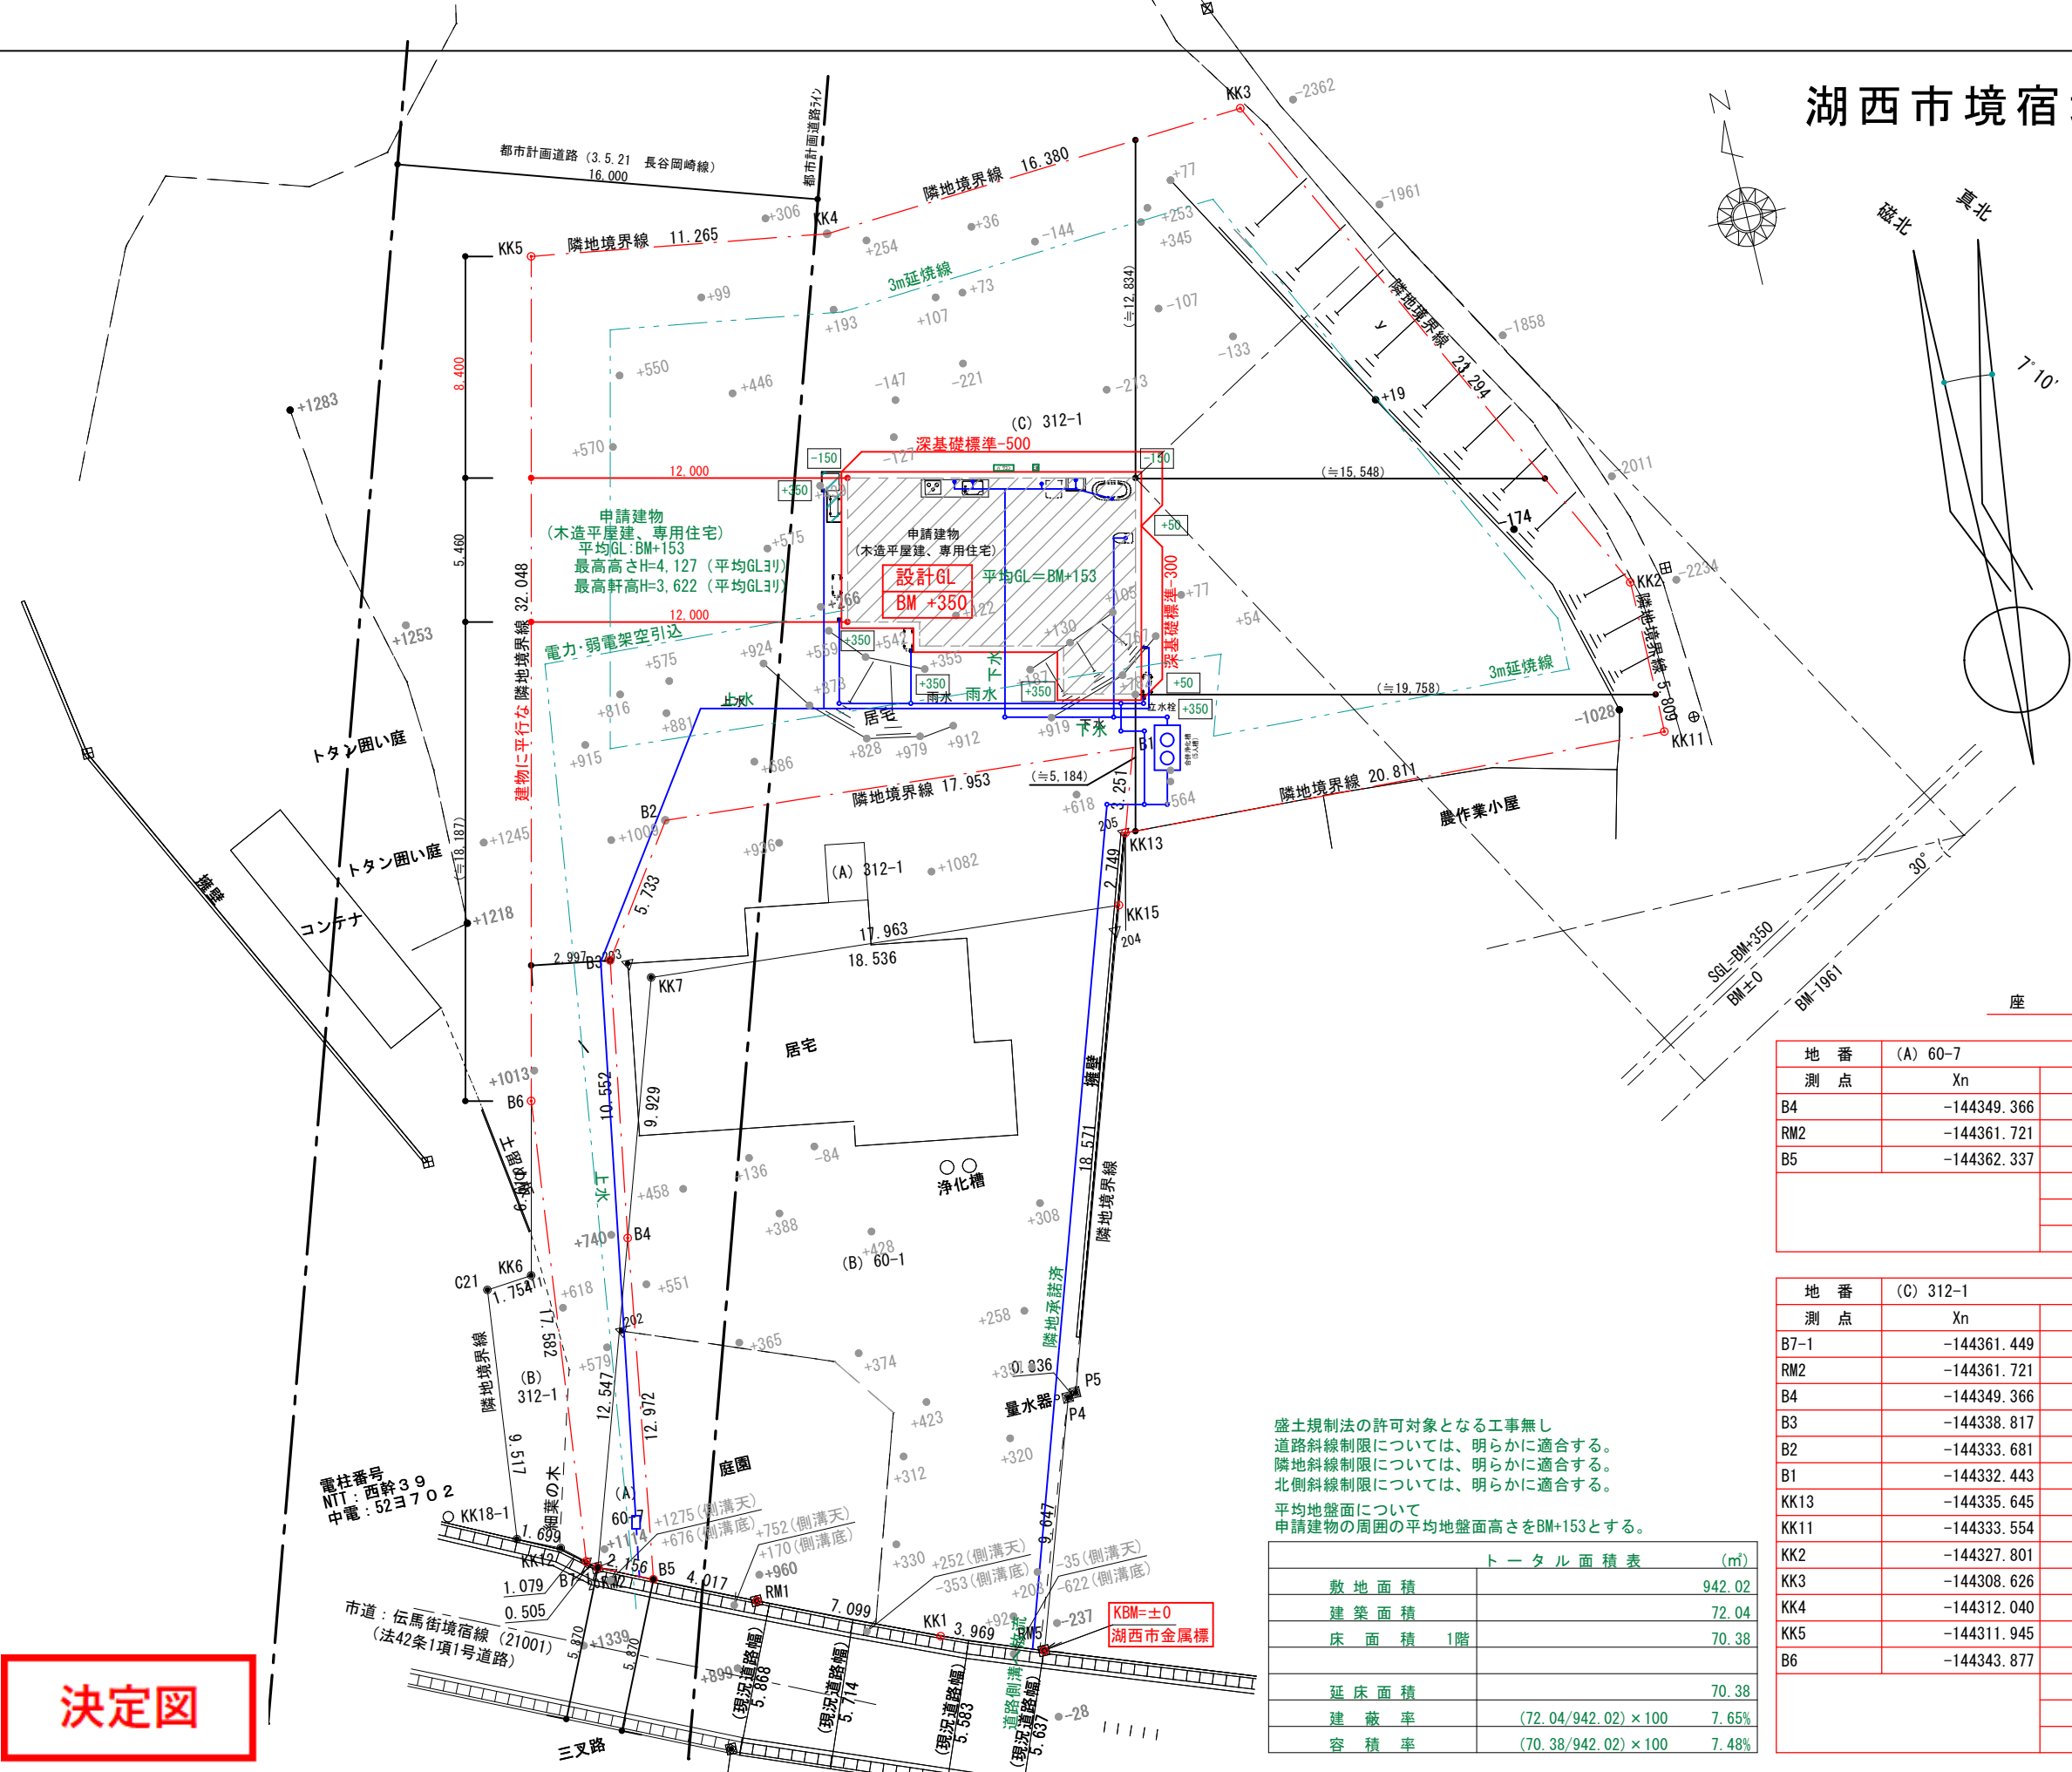

①-②	-0.50*10.92	=-5.46
②-③	-0.2*1.820*1/2	=-0.182
③-④	-0.30*6.37	=-1.911
④-⑤	0	
⑤-⑥	0	
⑥-⑦	0	
⑦-⑧	0	
⑧-⑨	0	
⑨-①	0	
計		-7.533
周長		10.92+1.82+6.37+2.73+1.82+5.46+0.91+2.73+5.46
		=38.22
		-7.533÷38.22=-0.19709576138 → -0.197 (m)

平均地盤面算定図 S=1/300

座 標 求 積 表

地 番	(A) 60-7			
測 点	Xn	Yn	(Xn+1 - Xn-1) Yn	距 離
B4	-144349.366	-92026.025	-56688.031400	12.547
RM2	-144361.721	-92028.212	1193697.937852	2.156
B5	-144362.337	-92026.146	-1136983.033830	12.972
		倍 面 積	26.872622	
		面 積	13.4363110	
		地 積	13.43	

地 番	(C) 312-1			
測 点	Xn	Yn	(Xn+1 - Xn-1) Yn	距 離
B7-1	-144361.449	-92028.637	1642158.998628	0.505
RM2	-144361.721	-92028.212	-1111976.885596	12.547
B4	-144349.366	-92026.025	-2107764.076600	10.552
B3	-144338.817	-92025.795	-1443424.594575	5.733
B2	-144333.681	-92023.248	-586556.182752	17.953
B1	-144332.443	-92005.338	180698.483832	3.251
KK13	-144335.645	-92005.899	102218.553789	20.811
KK11	-144333.554	-91985.193	-721531.853892	5.809
KK2	-144327.801	-91985.996	-2293026.908288	23.294
KK3	-144308.626	-91999.222	-1449999.737942	16.380
KK4	-144312.040	-92015.242	305398.588198	11.265
KK5	-144311.945	-92026.507	2929847.903359	32.048
B6	-144343.877	-92029.228	4555814.902912	17.582
		倍 面 積	1857.191073	
		面 積	928.5955365	
		地 積	928.59	

盛土規制法の許可対象となる工事無し
道路斜線制限については、明らかに適合する。
隣地斜線制限については、明らかに適合する。
北側斜線制限については、明らかに適合する。
平均地盤面について
申請建物の周囲の平均地盤面高さをBM+153とする。

トータル面積表 (㎡)	
敷地面積	942.02
建築面積	72.04
床面積 1階	70.38
延床面積	70.38
建蔽率	(72.04/942.02) × 100 7.65%
容積率	(70.38/942.02) × 100 7.48%

決定図