


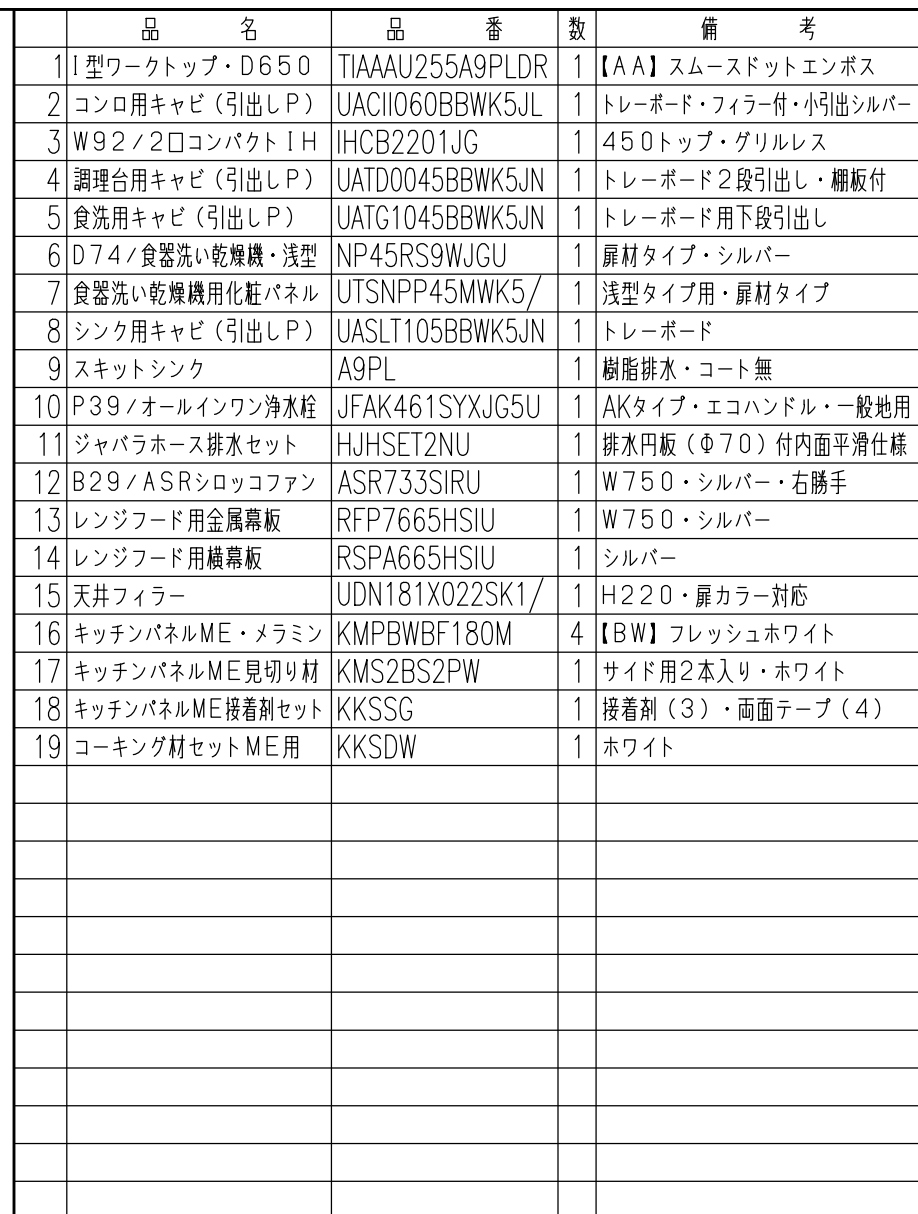


特記事項
扉色 WK5:ホワイトスタッコ
取手 [J]スリム取手（シルバー）
ワークトップカラー 【AA】スムースドットエンボス

物件名	田村雅子 様邸
仕様	ES21

案件No.	図面名	担当	図面
A2505DDDD0EKVLT	レイアウト図	栗野 友仁	
見積No.	縮尺	日付	
M25057451912-003-2	1/30	2025.06.10	

株式会社 LIXIL

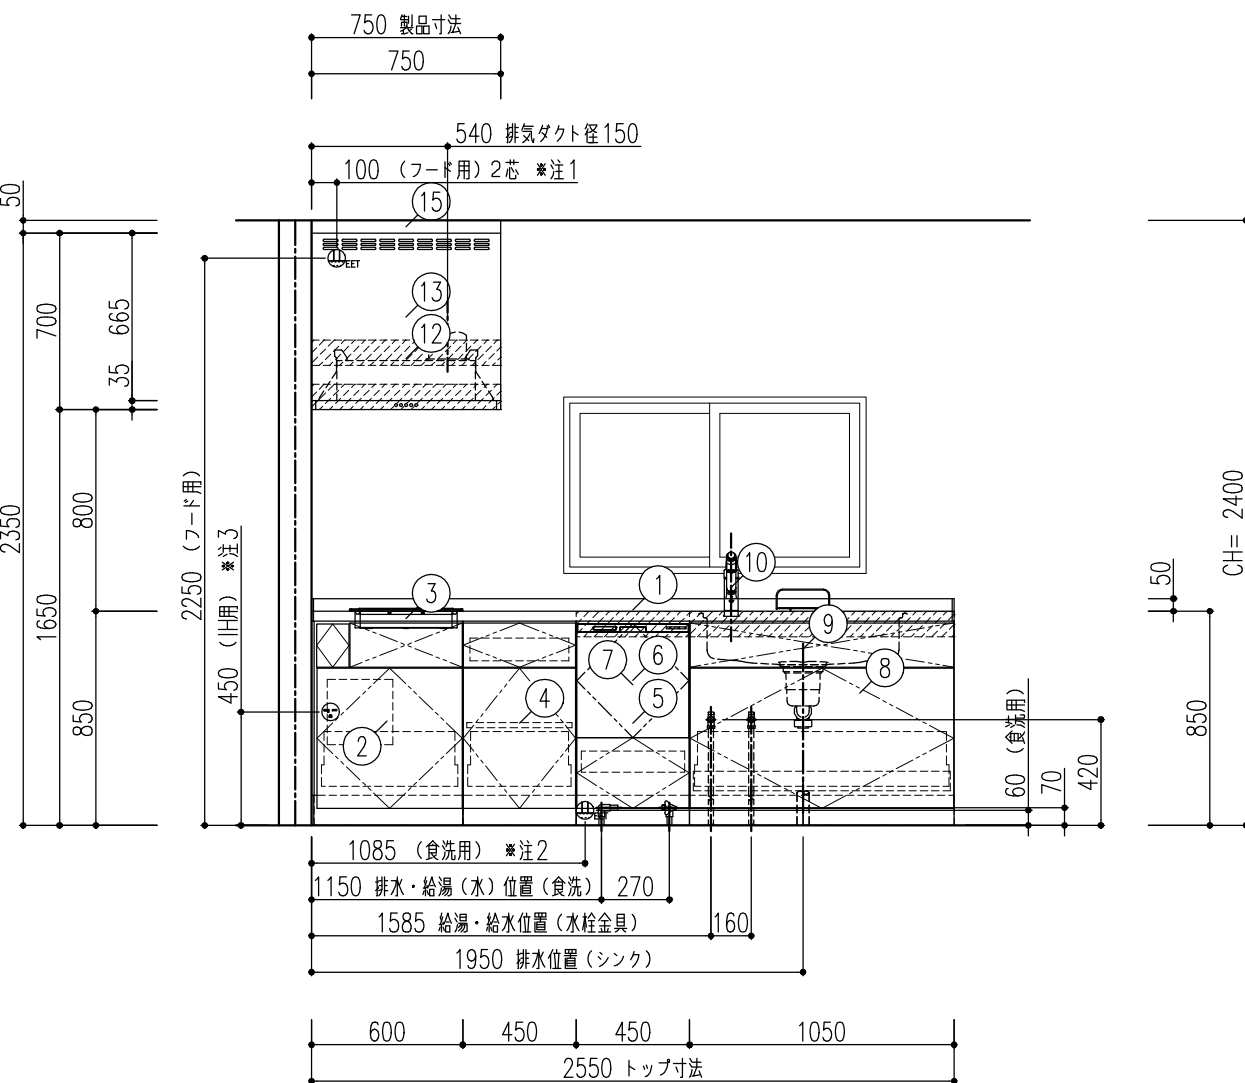

注1) 125V・15A 2極接地極付アースターミナル付コンセント【専用】(フード用)
注2) 125V・15A 2極接地極付アースターミナル付コンセント 側板取付【専用】
注3) 250V・20A 2極接地極付コンセント(コンセントベース固定)【専用】

【ご注意】



- 壁面仕上材(キッチンパネル・タイルなど)の貼付下端位置が変わります。〔機能図参照〕
- 記載のキャビネット寸法は扉前面での呼び寸法です。キャビネット本体の寸法・扉厚み等は商品ガイドの巻末資料をご確認ください。
- 記載のワークトップ、カウンター、エンドパネル、サイドパネルの寸法は呼び寸法です。詳細寸法は商品ガイドの巻末資料をご確認ください。
- 電気・ガス・給排水・換気等は法令・規定に従って有資格者が行ってください。
- 水道工事は排水配管工事となります。
- 取付・設置に際し、各製品の取付・設置説明書や図面の機能図を必ずお読み下さい。
- レンジフードにはアース線は同梱されておりません。別途 御用意願います。
- 内線規程上、各機器のプラグ仕様に関わらず建築側には接地極付コンセントを推奨しています。
- 壁付けでレンジフード上に天井フィラーを設置する場合は、横壁に下地が必要となります。下地位置は、機能図を参照願います。
- レンジフード電源プラグ仕様: 2芯電源プラグ(アース工事がが必要です。)
- 食器洗い乾燥機配管は、給水接続か給湯接続かお客様に確認したうえで施工願います。
- 食洗機内配管の詳細については必ず別添の機能図をご確認ください。

A3 20250610NGB5-0

面

C面

注3) 250V・20A 2極接地極付コンセント（コンセントベース固定）【専用】

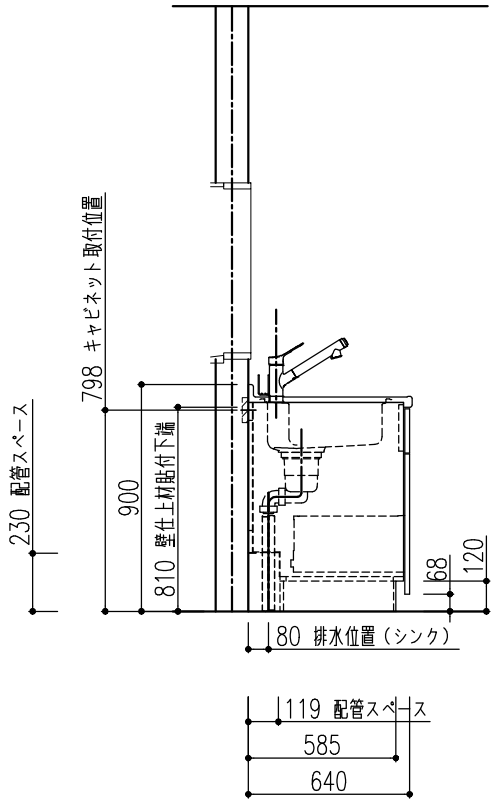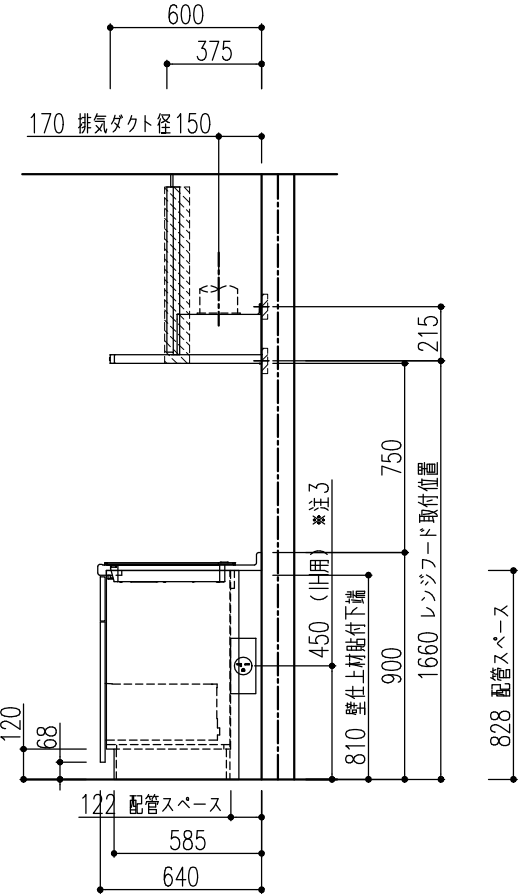

特記事項 扉色 WK5:ホワイトスタッコ 取手 [J]スリム取手 (シルバー) ワークトップカラー 【AA】 スムースドットエンボス	物件名	田村雅子 様邸	案件No.	A2505DDD0EKVLT	図面名	納まり図	担当	栗野 友仁	図面	図番	株式会社 LIXIL
	仕様	ES21	見積No.	M25057451912-003-2	縮尺	1/30	日付		2025.06.10		

■壁面仕上材（キッチンパネル、タイルなど）取付注意事項〔貼付下端位置〕

●キッチンパネルの貼付下端位置

キッチンパネルの貼付下端位置にご注意ください。

キッチンパネル

壁

810mm

(キッチンパネル貼付下端位置)

ワークトップ高さ：850mm以外の場合は、
下表を参照してください。

ワークトップ高さ	キッチンパネル貼付下端位置
900	860
875	835
825	785
800	760

●上表はキッチンパネルの場合です。ステンレスパネルの場合は、キッチンパネルの「取付・設置説明書」を参照してください。

《ワークトップ高さ：850mmの場合》

■壁面仕上材（キッチンパネル）取付注意事項〔貼付向き〕

●キッチンパネルの貼付向き

キッチンパネルの貼付向きにご注意ください。

【単位：mm】

レンジフード

ウォールキャビ（開き扉）

クイックポケット
クイックパレット

850

700

880

620

850

700

880

620

850

700

880

620

850

700

880

620

横貼り

縦貼り

フロアキャビ

横

縦

《バックガード：なし、ワークトップ高さ：850mm、ウォールキャビ高さ：700mmの場合》

《キッチンパネル 貼付方向》
総高さ：2350mmの場合

キッチンパネル貼付方向	ウォールキャビ		
	開き扉	クイックポケット クイックパレット	
	H700	H600 H500	H700 (620) H600 (520)
横			縦

【ご注意】
リシェル以外のクイックパレットは、キャビネットの背板高さがショート（－80mm）しておりませんので、『開き扉』のキッチンパネル貼付方向に合せてください。

■床の不陸に関して

7mm以下

7mm以下

床の不陸は、7mm以下に抑えるようにしてください。不陸が大きい場合は、現場責任者に床の修正を依頼してください。
※キャビネット取付時には不陸調整スペーサー等で水平になるように設置してください。

レンジフード取付注意事項（壁面取付時）

レンジフードを取付ける場合は下地の材が厚み30mm以上、幅100mm以上、ビス固定位置が材の端部から25mm以上であることを確認してください。
また、壁強度などの詳細は「レンジフード設置説明書」を必ず事前に確認してください。

取付位置については、取付設置図を確認してください。

参考図_CLS. SER. NST. ASR. ADR. RVJ. GSR. BFRS. TARシリーズ
（※RVJ. GSRシリーズの場合はレンジフードパネルの取付下地は不要です。）

12mm以上の合板または0.8mm以上の鋼板

レンジフード取付下地

100mm

30mm以上

100mm以上

335

レンジフードパネル取付下地

【正面】

【側面】

参考図_FED. HVR. NSDシリーズ（サイドマントルタイプ）

30mm以上

100mm以上

レンジフード取付下地

【正面】

【側面】

参考図_NBHシリーズ

レンジフード取付下地

30mm以上

100mm以上

【正面】

【側面】


特記事項 扉色 WK5:ホワイトスタック 取手 [J]スリム取手（シルバー） ワークトップカラー 【AA】スムーズドットエンボス	物件名 仕様	田村雅子 様邸 ES21	案件No.	図面名	担当	図面	図番
			A2505DDDD0EKVLT	機能図	栗野 友仁		株式会社 LIXIL
			見積No.	縮尺	日付		
			M25057451912-003-2		2025.06.10		

A3

20250610NGB5-01

■天井フィラーの取付（レンジフード上部）

レンジフード横に壁がくるレイアウト時は、横壁にも取付枠が必要になります。

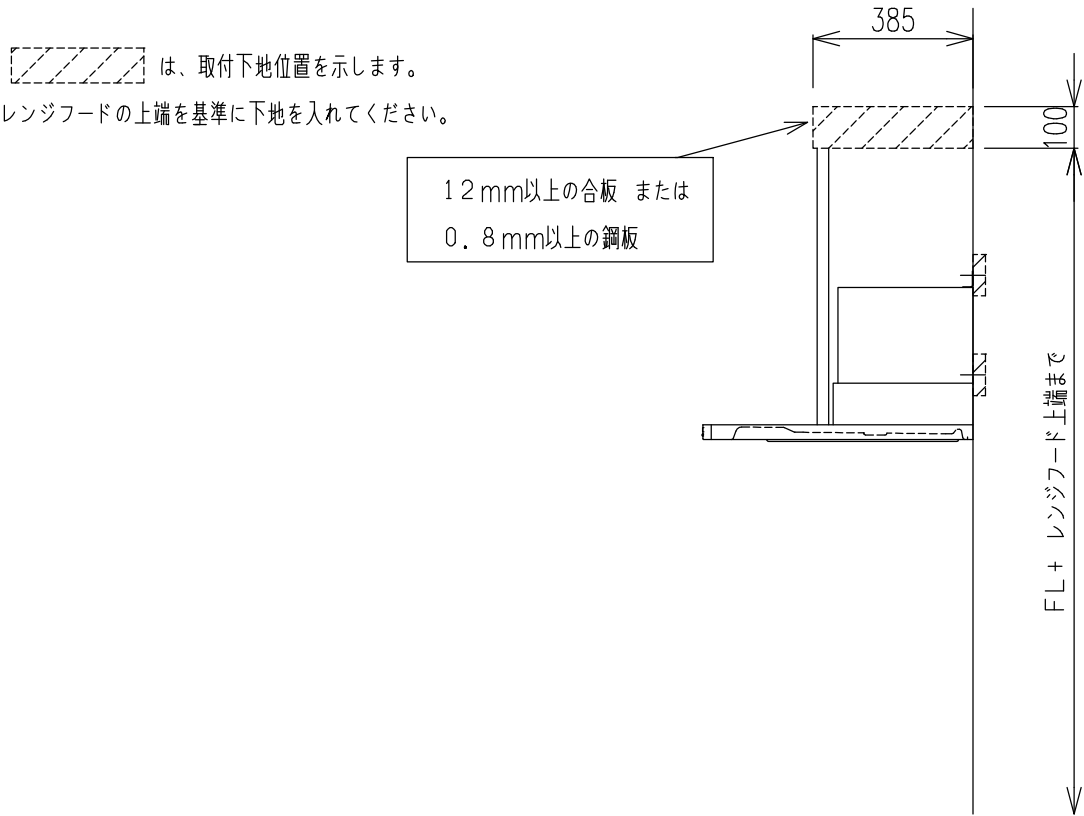

■ASRフード

■左タイプ（L）

■右タイプ（R）

電源線位置（S=Free）

給気3P：100V出力用コネクター（SRS100V用）
アース端子

排気2P：電動シャッター
取付用コネクター（HDS150用）

電源プラグ（2P）
機外長：1m

LED照明（3W）

変化寸法表・質量表

品番	A	B	質量
ASR-93*SI/W	900	800	13.5
ASR-73*SI/W	750	650	13.0
ASR-63*SI/W	600	500	12.5

4. 製品名の末尾の（ ）にはワザンシリーズによって記号が入る場合があります。
3. 品番のSI/Wは色調を示します。（SI：シルバー、W：ホワイト）
2. 本図は右排気を示します。左排気は対称（電源線位置は除く）となります。
注）1. 排気方向は上方・後方・左右排気です。（後方・左右排気の場合は別売のL型ダクトを使用）

付属品

座付ねじシルバー（φ4.8×45）	2本
座付ねじブラック（φ5.1×45）	2本
ソフトテープ	1本


静圧－風量 曲線

7部詳細（S=1/2）

■IHヒーター用コンセント推奨位置図 / 側面設置の場合


- ※コンセントや電源プラグが、引き出しおよびIHヒーター用仕切板（オプション）に接触しないように注意してください。
- ※木製キッチンの配管スペース付キャビネットは、キャビネット内にコンセントを取り付けるスペースがありませんので、別売のコンセントベース（W-SOCKET-B）などを使用して配管スペース内にコンセントを設置してください。

キッチン高さ	コンセント下端高さ	コンセントセンター高さ
800	355	400
850	405	450
900	455	500

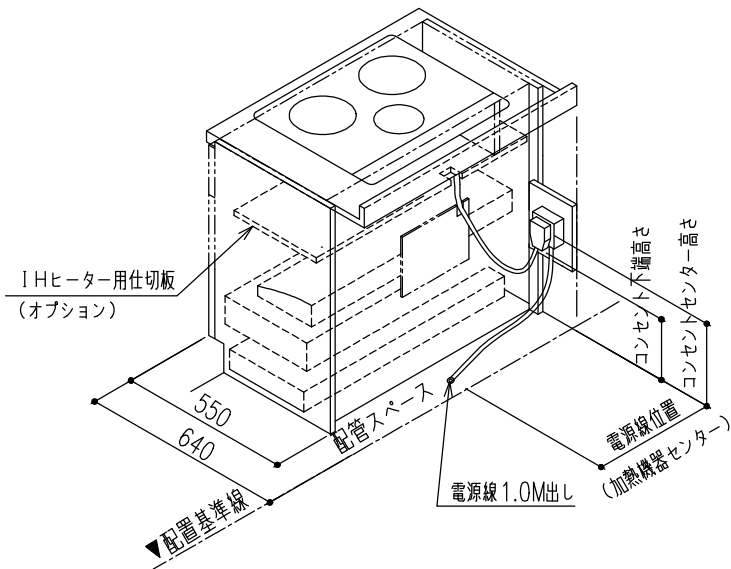

注意：引き出しおよびIHヒーター用仕切板（オプション）に接触しないように上記寸法を参照してください。

■食器洗い乾燥機内配管図 床立上げ配管例

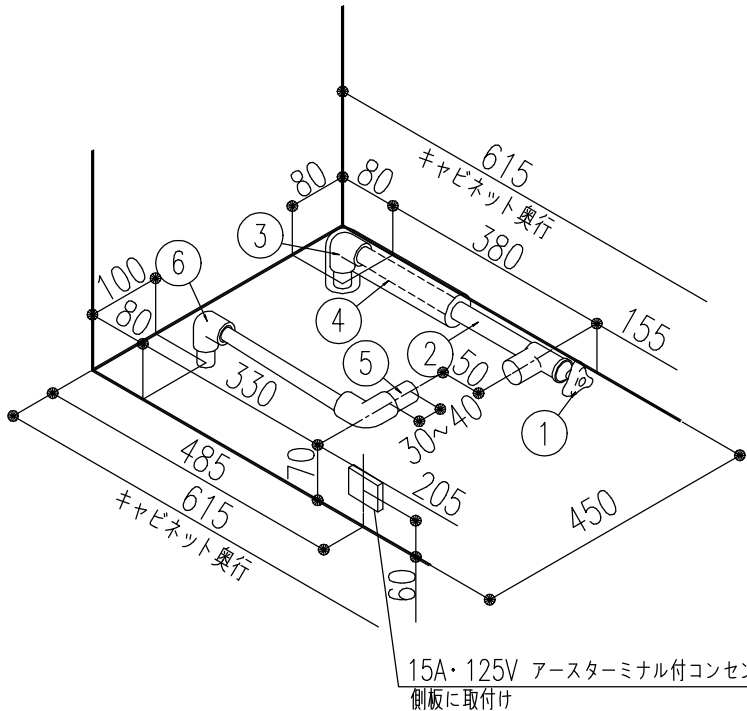

注意：配管立ち上げ位置は必ず本図の位置に立ち上げて下さい。

※給水接続か給湯接続かお客様に確認したうえで施工願います。

給水（給湯の場合は耐熱配管）

①アングル型止水栓（ハンドル式・固定ゴマタイプ）

※必ず固定ゴマタイプをご使用ください。

落としゴマタイプを使用すると、水栓内でゴマが移動し、ゴトゴト音を生じる恐れがあります。

②硬質塩化ビニルライニング鋼管（相当品）

③RC1/2ソケット

④断熱材（Φ48）

排水（耐熱塩ビ使用のこと）

⑤排水パイプHT20

⑥HTエルボ


※配水管先端のエルボを上向きにしないでください。

キャビネットに当たるため、排水ホース折れの原因になります。

■ 止水栓図（床立上げ）

床立上げ配管

配管立ち上げ寸法は、止水栓芯までの高さを示しています。

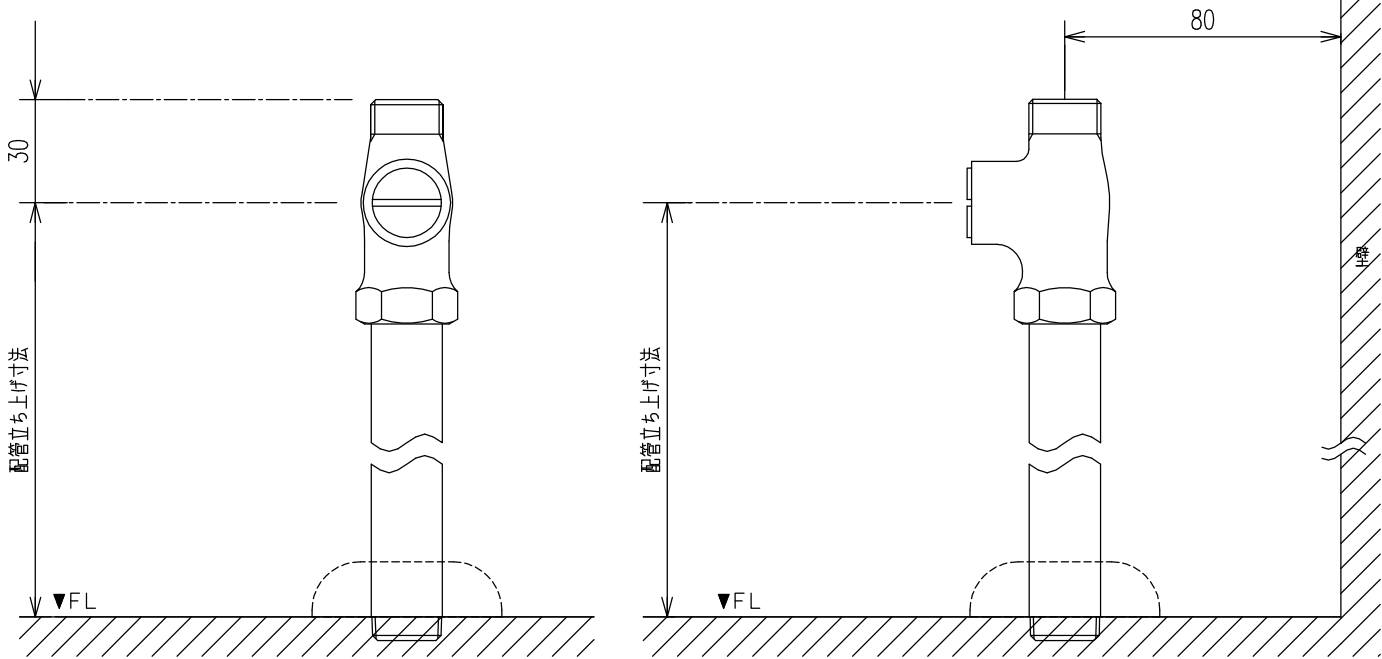

特記事項 扉色 WK5:ホワイトスタック 取手 [J]スリム取手（シルバー） ワークトップカラー 【AA】 スムースドットエンボス	物件名	田村雅子 様邸	案件No.	図面名	担当	図面	図番
	仕様		A2505DDD0EKVLT	機能図	栗野 友仁		株式会社 LIXIL
		ES21	見積No.	縮尺	日付		
			M25057451912-003-2			2025.06.10	

■ キッチン取付者さま向け 動画コンテンツ ■

商品取付けの注意点を2次元コードでご視聴いただけます。

取付日より前に、是非ご確認ください。

1 ページ目

■ キッチン取付者さま向け 動画コンテンツ ■

商品取付けの注意点を2次元コードでご視聴いただけます。

取付日より前に、是非ご確認ください。

1 ページ目

■ キッチン取付者さま向け 動画コンテンツ ■


商品取付けの注意点を2次元コードでご視聴いただけます。

取付日より前に、是非ご確認ください。

1 ページ目

荷扱い・搬入


荷扱い・搬入

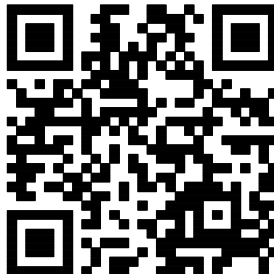

作成日：2024年10月01日

荷扱い・搬入

荷扱い・搬入

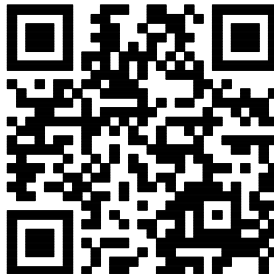


作成日：2024年10月01日



荷扱い・搬入

荷扱い・搬入

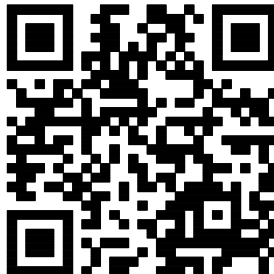

作成日：2024年10月01日

カウンター開梱搬入「養生ツール」

カウンター開梱搬入 「養生ツール」のご紹介



作成日：2024年10月01日

カウンター開梱搬入「養生ツール」

カウンター開梱搬入 「養生ツール」のご紹介



作成日：2024年10月01日




カウンター開梱搬入「養生ツール」

カウンター開梱搬入 「養生ツール」のご紹介





作成日：2024年10月01日


不陸の確認と調整

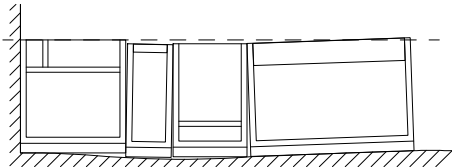

作成日：2024年02月07日

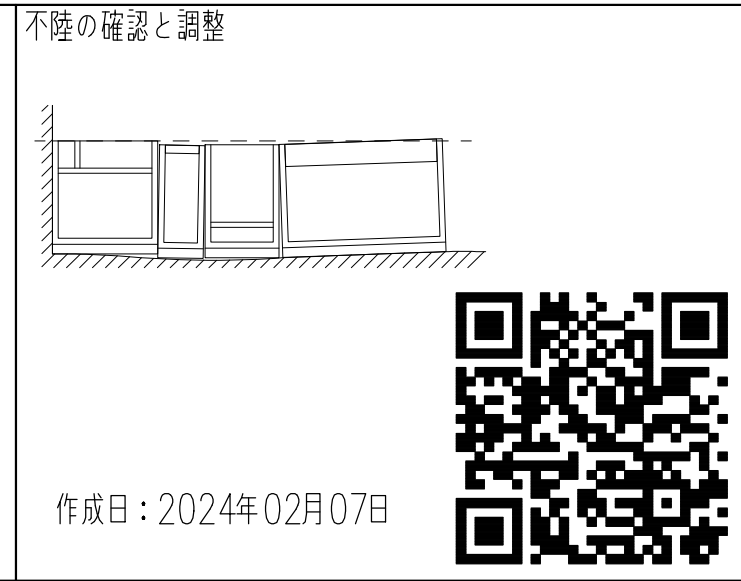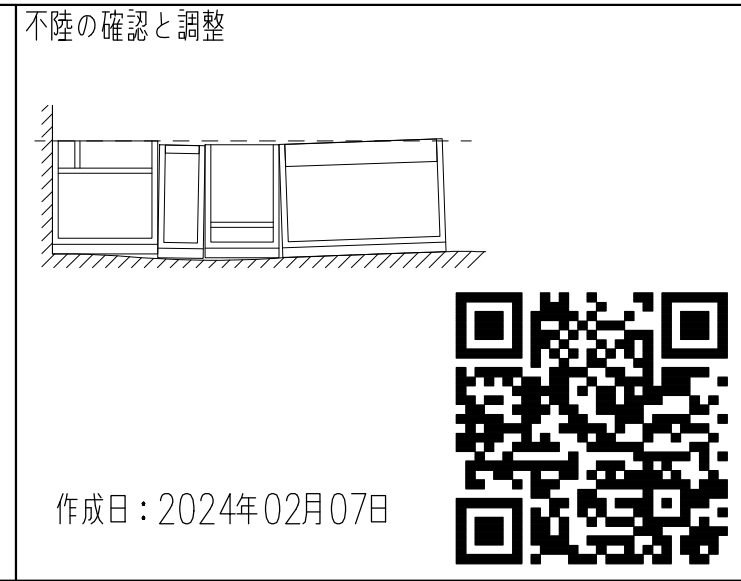

不陸の確認と調整

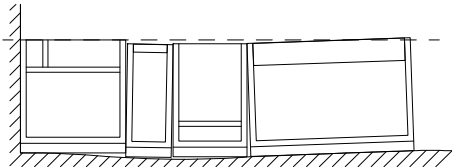

作成日：2024年02月07日



マグネット キッチンパネル

マグネット キッチンパネル 「取付・設置」ポイント



作成日：2024年03月06日

マグネット キッチンパネル

マグネット キッチンパネル 「取付・設置」ポイント



作成日：2024年03月06日




マグネット キッチンパネル

マグネット キッチンパネル 「取付・設置」ポイント



作成日：2024年03月06日


人造大理石カウンターL型キッチン

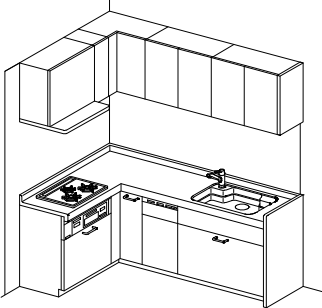

作成日：2024年02月07日




人造大理石カウンターL型キッチン

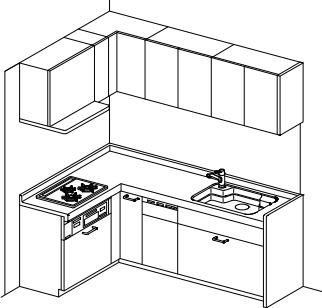



作成日：2024年02月07日




センターキッチン（ペニンシュラ型）

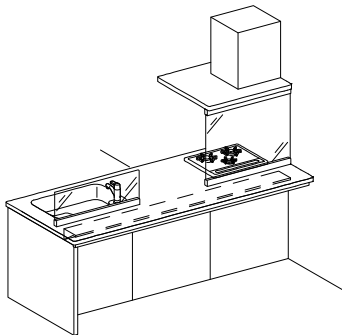

作成日：2024年02月07日

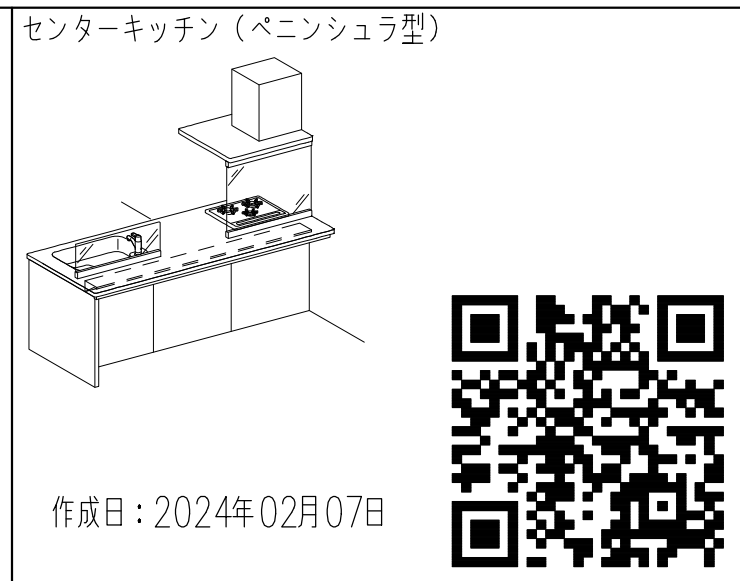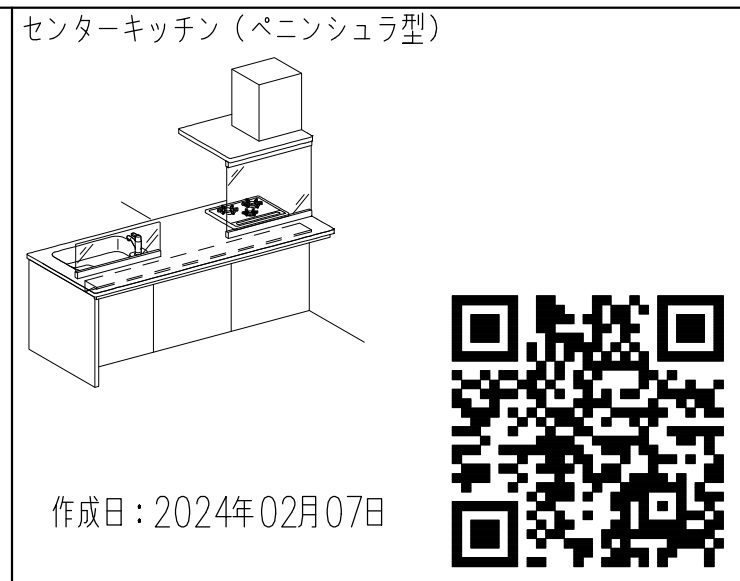

センターキッチン（ペニンシュラ型）

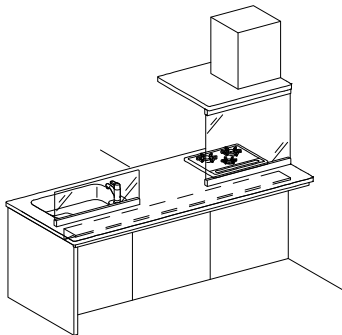






作成日：2024年02月07日



		特記事項 扉色 WK5:ホワイトスタック 取手 [J]スリム取手 (シルバー) ワークトップカラー 【AA】 スムースドットエンボス	物件名	田村雅子 様邸		案件No.		図面名	担当	図面	図番 : 株式会社 LIXIL
						A2505DDD0EKVLT		機能図	栗野 友仁		
			仕様	ES21		見積No.		縮尺	日付		
						M25057451912-003-2			2025.06.10		

■ キッチン取付者さま向け 動画コンテンツ ■

商品取付けの注意点を2次元コードでご視聴いただけます。
取付日より前に、是非ご確認ください。

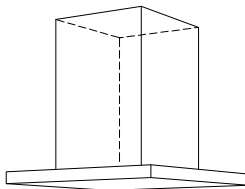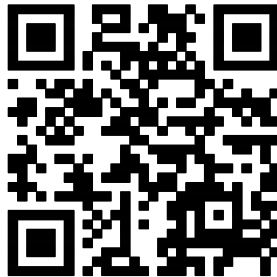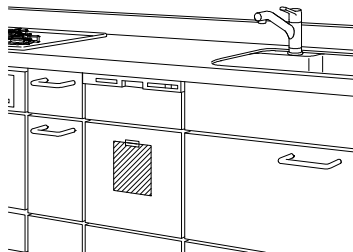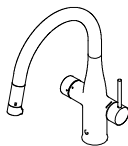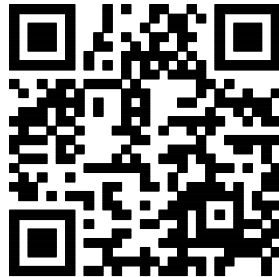センターフード型レンジフード (天吊りフード)  作成日：2024年06月03日 		I H加熱機器関連 I H加熱機器 仕切り板 作成日：2024年02月07日 		食器洗い乾燥機  作成日：2024年02月07日 		ミネラル浄水栓 Greentap  作成日：2024年06月03日 			
特記事項 扉色 WK5:ホワイトスタッコ 取手 [J]スリム取手 (シルバー) ワークトップカラー 【AA】スムースドットエンボス		物件名 田村雅子 様邸 仕様 ES21		案件No.		図面名	担当	図面	図番
				A2505DDDD0EKVLT		機能図	栗野 友仁		株式会社 LIXIL
				見積No.		縮尺	日付		
				M25057451912-003-2			2025.06.10		