

■ 仕 様				■ HEAT20 G2	
断熱工事		■ 床:カネライトフォーム t90 ■ 土間床等の外周:スタイロフォームAT t50 ■ 壁:アクアフォームLITE吹付 t90 ■ 天井:アクファフォームLITE吹付 t220			
床下換気		■ 基礎パッキン JOTO (玄関・UB周り:気密基礎パッキン)			
防虫防蟻		■ 土壌処理・木部 ガントナーMC			
■ 外 部 仕 上 表				■ 22条地域	
部位		仕上・仕様・メーカー		色番・品番	
屋根		■ ガルバリウム鋼板(t0.35)UK立平 ニスクカラーPro GH 軒先通気金物 日本住環境株式会社【REV-15】		GHK01 Sブラック	
パラペット笠木		■ なし			
破風・鼻隠		■ なし			
雨樋	(軒樋)	■ Panasonic サーフেসケアFS-I型		ブラック	
	(竖樋)	■ Panasonic S30角樋		ブラック	
軒天	屋根軒	■ ニチハ軒天5 木目調 910×1820×5		ライト	
	ポーチ軒	■ ニチハ軒天5 木目調 910×1820×5		ライト	
	バルコニー軒	■			
オーバーハング水切り		■ なし			
外壁	通気金物(15mm)	■メイン	Kmew エクセレージ 光セラ15	シマンフラット ラント チタン ライトグレー	
	※下地面材:タイガーEXハイパー	■アクセントA	なし		
	防火認定 PC030BE-4028	■アクセントB	なし		
玄関ポーチ		■ 床 玄関タイルに同じ		-	
基礎		■ 立上り巾木: モルタル刷毛引き		-	
基礎水切り金物		■ JOTO鋼板製 防鼠材付き水切り JOTO:WMF-N35		ブラック	
バルコニー	床・内壁	■ なし		-	
	笠木	■ なし			
外部建具		■ LIXIL EW(アルゴンガス高遮熱仕様LowEトリプルガラス クリア) ・SD、TSは、メーカー設定によるが、オペレーターハンドル優先とする ・オペレーター付サッシの場合は固定網戸とする ・グレモンハンドル式サッシの場合は可動網戸とする		外観 ブラック 内観 ホワイト ※樹脂パッキン・網戸付	
シャッター		■ 洋室①/手動 ・ LDK/電動			
軒天通気金物					
玄関扉		■ LIXIL ジエスタ2 K2仕様 LIXILファミロック タグキー×3 (電池式)		ドア型: M14 型 ドア色: クリエモカ ハンドル: S型ハンドル 色 ブラック	
外部物干し金物		■			
換気フード		■ 局所換気扇(トイレ 浴室 キッチンフード) 防火ダンパー無		外気フード: ブラック	
		■ ダクトレス熱交換換気システム (日本スティーベル株式会社) VLR-70E 防火ダンパー無		外気フード: B ブラック 室内パネル ホワイト	



■ 構 造 概 要					
基礎	■ RCベタ基礎コンクリート				
通し柱・管柱	■ 構造用集成材 105×105		間柱	■ 集成材	
土台	■ 桧 105×105	大引き	■ 桧 90*90	筋交い	■ 構造用製材 火打梁 ■ 鋼製火打(当社基準により米松あり)
桁・梁	■ 構造用製材及び集成材		制震装置	■ Kダンパー (株)アイ・エム・エー	
■ 設 備 装 着 品					
住宅設備	部位	メーカー	商品名 ※ 詳細は見積り、プレゼン参照	見積りNo.	(日付)
	キッチン	LIXIL	■ ES I型 扉ホワイトスリット 天板ステンレス キッチンパネル:フレッシュホワイト 標準食洗器 標準IH、壁付レンジフードASR(シルバー) スリム取手シルバー	見積り番号 : M25057451912-004-2 (日付) 2025.6.11	
	浴室	LIXIL	■ AX1616 PGハウス標準仕様 アクセント壁:マーフィルベージュ 浴槽:ミナモ ホワイト 床:ホワイト マグネットシェフ:ホワイト	見積り番号 : M25057451912-004-1 (日付) 2025.6.11	
	1Fトイレ	LIXIL	■ ベーシアシャワートイレ 白 ● タオル掛け: KF-AA71D(白) タンク手洗 有り ● 紙巻き器: CF-AA22H /WA	見積り番号 : M25057451912-004-4 (日付) 2025.6.11	
	洗面台	LIXIL	■ EV W750(D500タイプ) 扉:グロスホワイト [引出しタイプ シングルハンドシャワー スタンダードLED三面鏡 その他 ● タオル掛け: KF-AA71D(白)	見積り番号 : M25057451912-004-3 (日付) 2025.6.11	
	浴室 手すりバー 2カ所 1階トイレ 手すりバー 1カ所				
給排水設備	給湯器	■ エコキュート370L Panasonic Sシリーズ スタンダードモデル 追い焚きフルオート			
	排水	■ 合併浄化槽 5人槽 ポンプアップ無			
	外水栓	■ 1 カ所 (平面図参照)	■ 外部立栓柱: PVC製 水栓柱12型【前澤化成工業】		
	外部ガーデンパン	■ 無し			
	その他	■ 洗濯機用単水栓: 緊急止水弁付 ■ 洗濯機用排水: トラップ金物(標準) ■ 排水さや管(長期優良住宅仕様)			
ガス配管設備		■ なし (配置図・平面図参照)			
電気設備	インターホン	■ パナソニック VL-SE31XL			
	TVアンテナ	■ UHF + BS・110度CS／CSアンテナ [2K・4K・8K対応] ■ホワイト			
	エアコン	■ 設置場所:			
	ソーラー	■ あり(Qセルズ) 12 枚 5.28 KW Re.RISE-G3 440 (1722×1134×30)			
	※標準搭載	※メーカーのモデルチェンジ等で後継品に変更される可能性あり ■ 屋外パワコン エネルギーマネジメントシステム Cube J			
その他					
決定図					

決定図

	浜 岡 一 級 総 合 設 計 事 務 所 一級建築士事務所 静岡県知事登録第 (10)2441 号 一級建築士 大臣登録第 365879 号 西原利昌	 PG HOUSE	株式会社 LIFEFUND InDesign office 一級建築士事務所 事務所登録 (2)第7595号 一級建築士登録 第179770号 鈴木 達男 〒432-8023 静岡県浜松市中央区鴨江3丁目70番23号	年 月 日	2025.8.1	件名	田村雅子様		設計	IC	工務	図 番
				縮尺		図面	仕上表 1		酒井		青島	1-1

湖西市境宿地内

G2

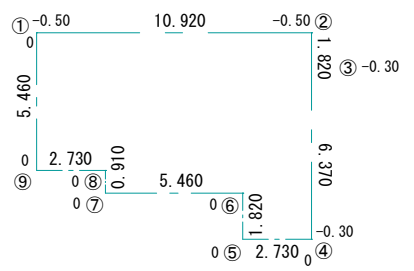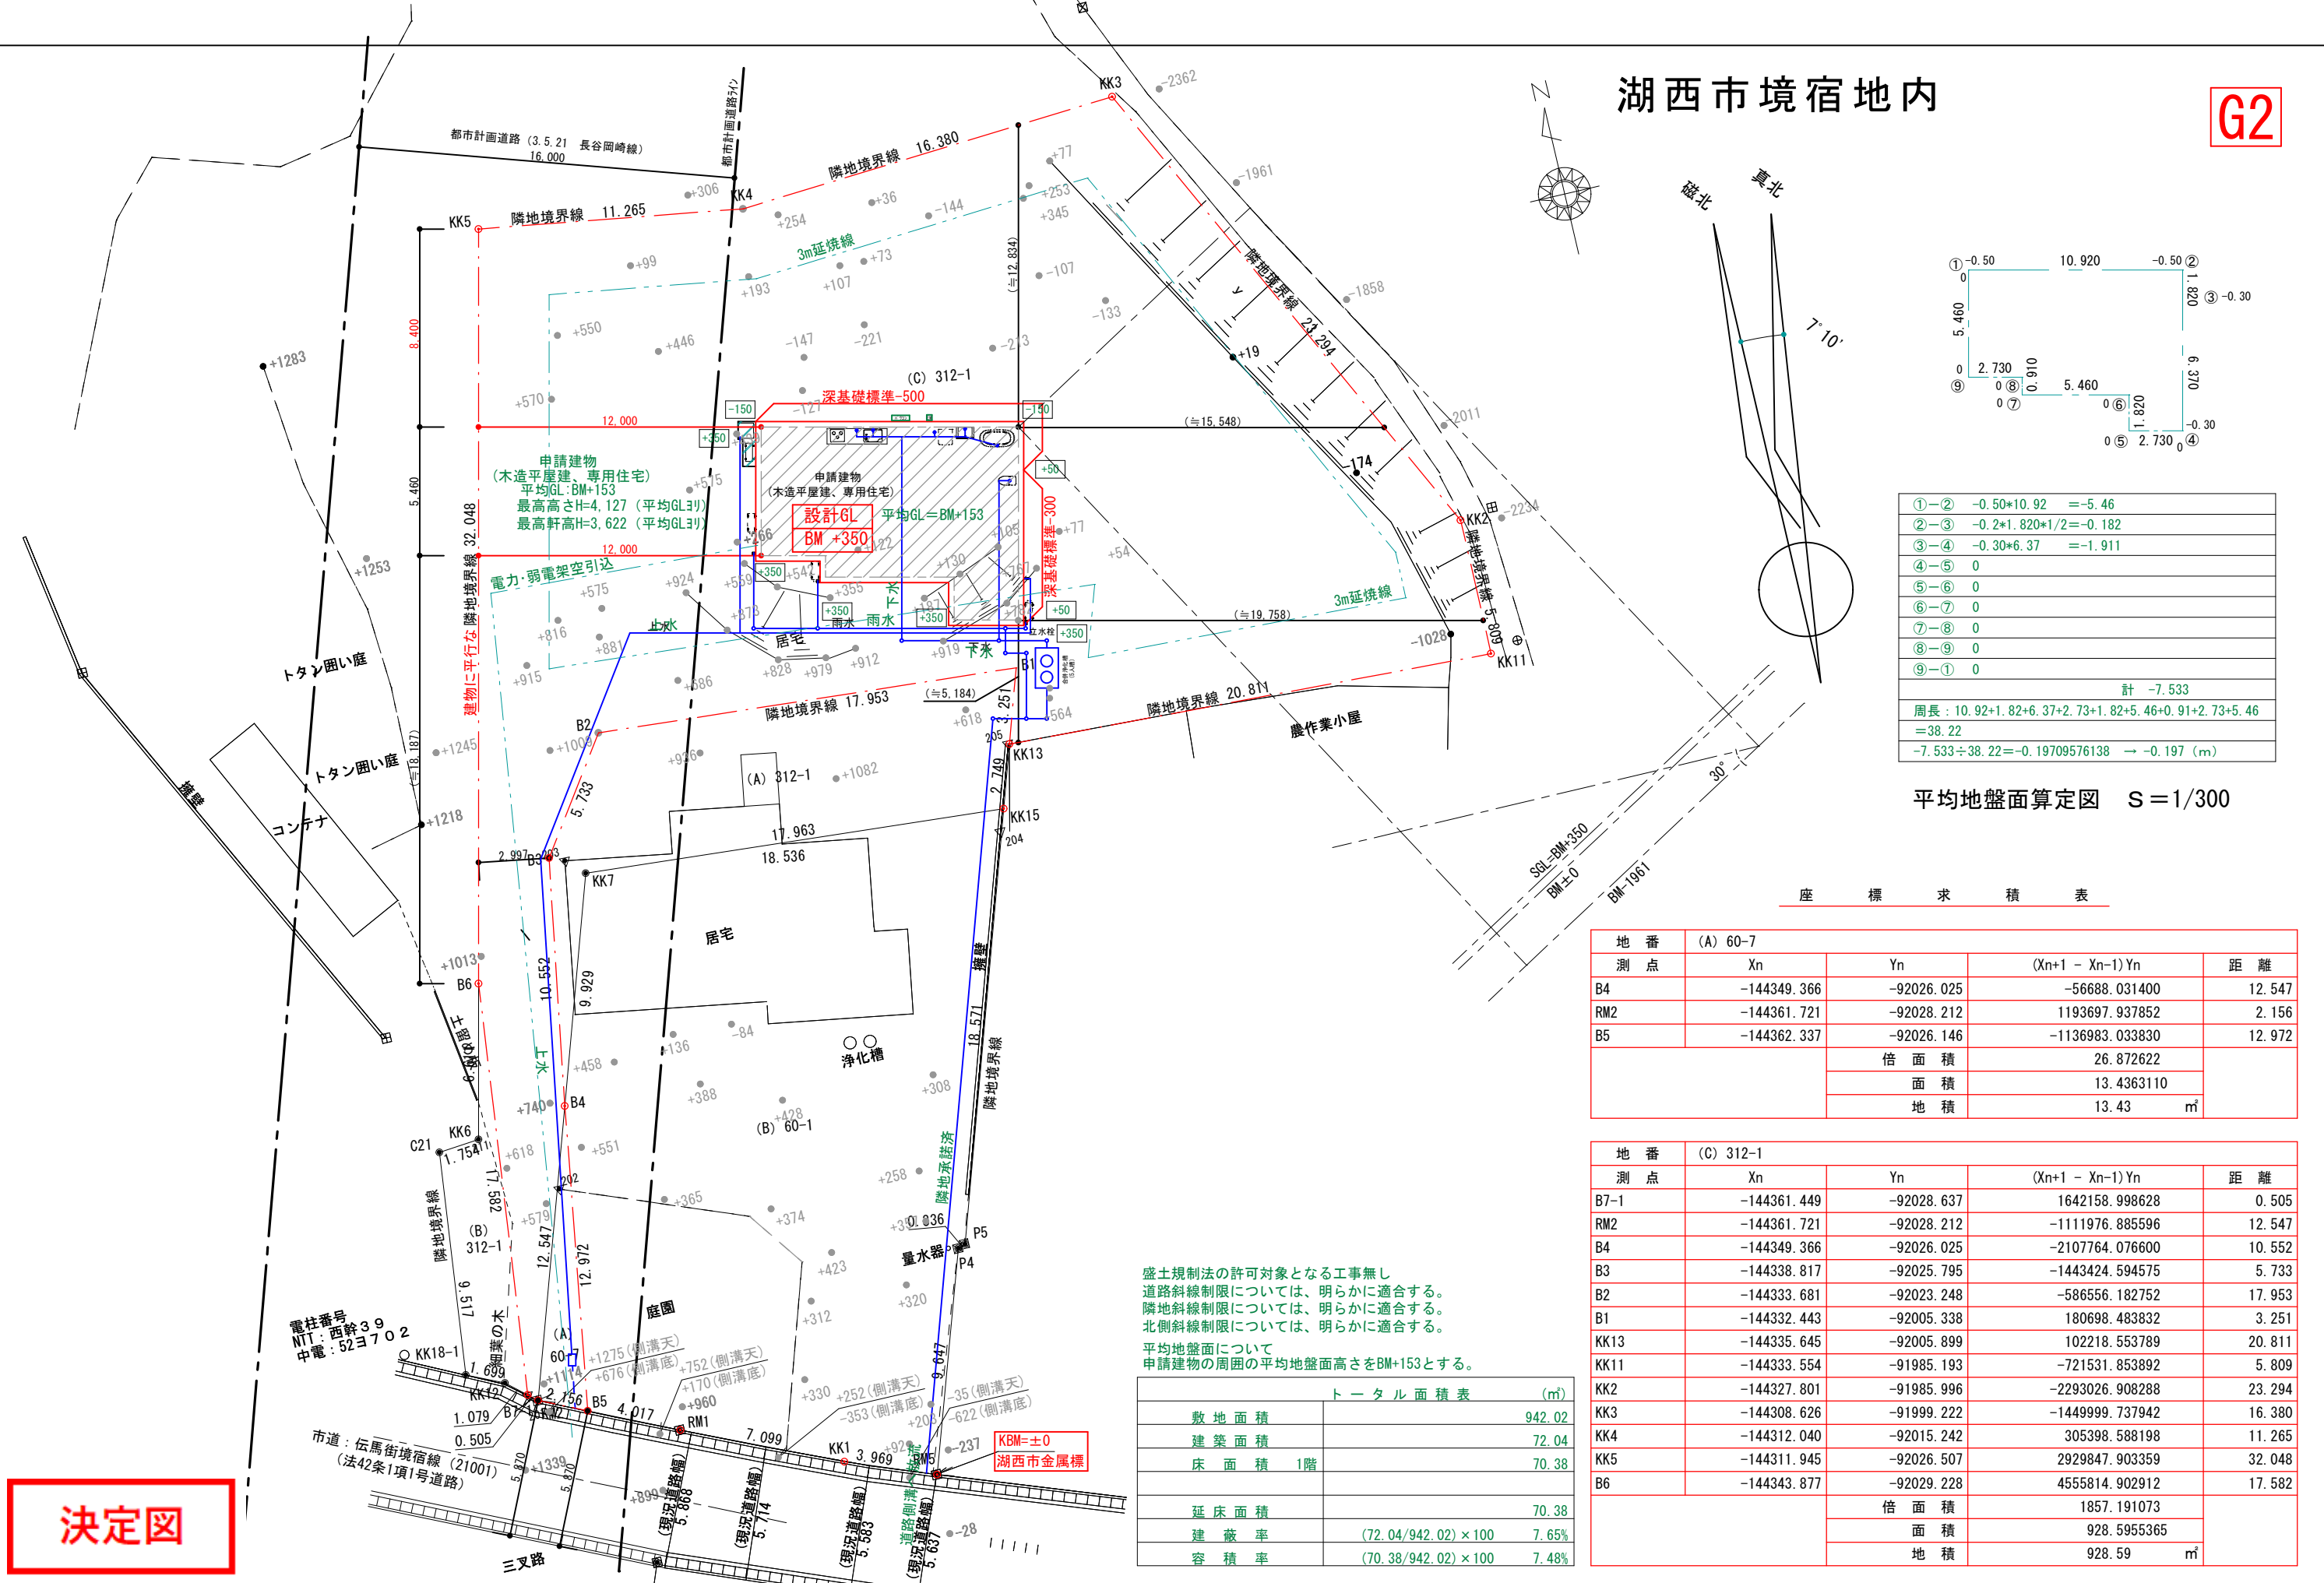

①-②	-0.50*10.92	=-5.46
②-③	-0.2*1.820*1/2	=-0.182
③-④	-0.30*6.37	=-1.911
④-⑤	0	
⑤-⑥	0	
⑥-⑦	0	
⑦-⑧	0	
⑧-⑨	0	
⑨-①	0	
計		-7.533
周長		10.92+1.82+6.37+2.73+1.82+5.46+0.91+2.73+5.46
		=38.22
		-7.533÷38.22=-0.19709576138 → -0.197 (m)

平均地盤面算定図 S=1/300

座 標 求 積 表


地 番	(A) 60-7			
測 点	Xn	Yn	(Xn+1 - Xn-1) Yn	距 離
B4	-144349.366	-92026.025	-56688.031400	12.547
RM2	-144361.721	-92028.212	1193697.937852	2.156
B5	-144362.337	-92026.146	-1136983.033830	12.972
		倍 面 積	26.872622	
		面 積	13.4363110	
		地 積	13.43	m ²

地 番	(C) 312-1			
測 点	Xn	Yn	(Xn+1 - Xn-1) Yn	距 離
B7-1	-144361.449	-92028.637	1642158.998628	0.505
RM2	-144361.721	-92028.212	-1111976.885596	12.547
B4	-144349.366	-92026.025	-2107764.076600	10.552
B3	-144338.817	-92025.795	-1443424.594575	5.733
B2	-144333.681	-92023.248	-586556.182752	17.953
B1	-144332.443	-92005.338	180698.483832	3.251
KK13	-144335.645	-92005.899	102218.553789	20.811
KK11	-144333.554	-91985.193	-721531.853892	5.809
KK2	-144327.801	-91985.996	-2293026.908288	23.294
KK3	-144308.626	-91999.222	-1449999.737942	16.380
KK4	-144312.040	-92015.242	305398.588198	11.265
KK5	-144311.945	-92026.507	2929847.903359	32.048
B6	-144343.877	-92029.228	4555814.902912	17.582
		倍 面 積	1857.191073	
		面 積	928.5955365	
		地 積	928.59	m ²


盛土規制法の許可対象となる工事無し
道路斜線制限については、明らかに適合する。
隣地斜線制限については、明らかに適合する。
北側斜線制限については、明らかに適合する。
平均地盤面について
申請建物の周囲の平均地盤面高さをBM+153とする。

トータル面積表 (m ²)	
敷地面積	942.02
建築面積	72.04
床面積 1階	70.38
延床面積	70.38
建蔽率	(72.04/942.02) × 100 = 7.65%
容積率	(70.38/942.02) × 100 = 7.48%

決定図

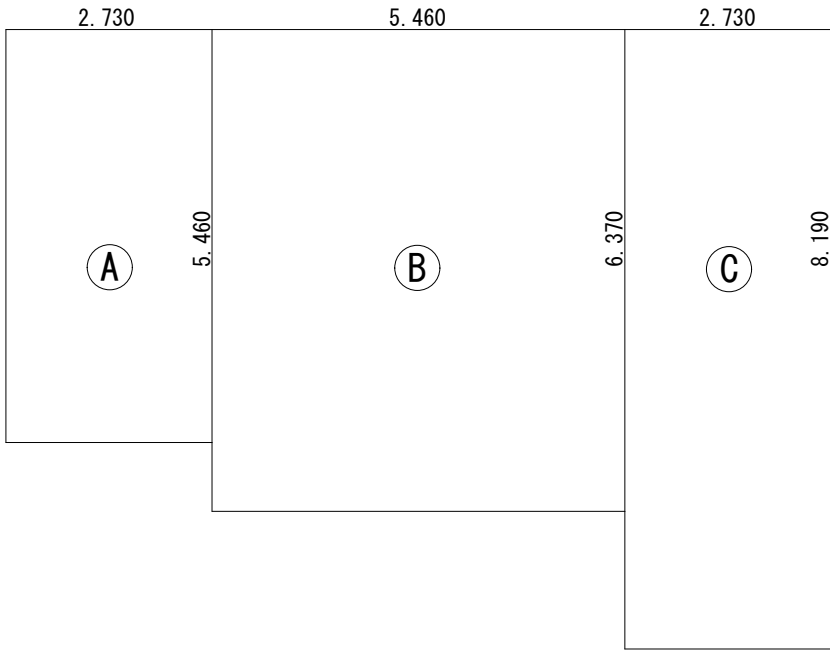

建築面積求積図 S=1/100

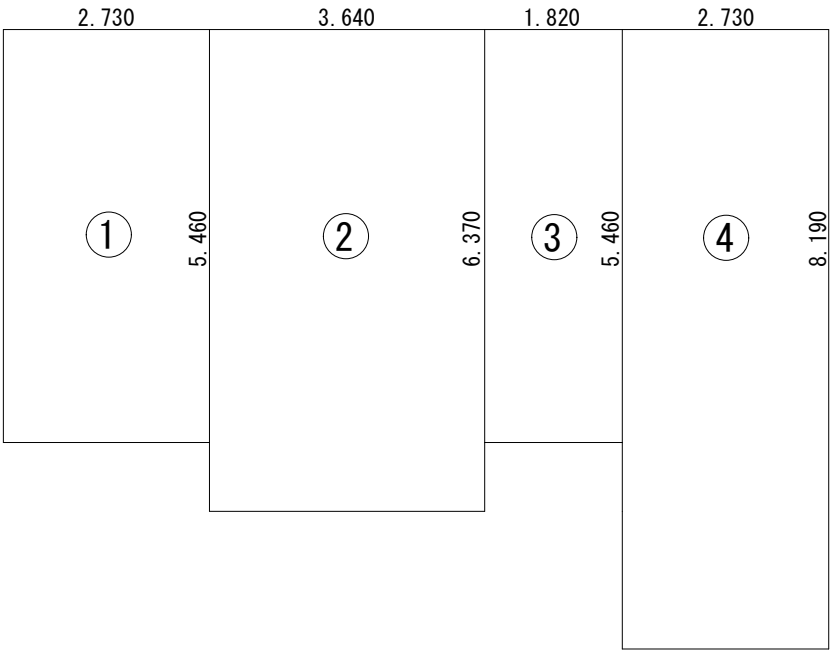

1階床面積図 S=1/100

建築面積求積表

番号	計算式	(m)	面積 (㎡)
Ⓐ	2.730 × 5.460		14.9058
Ⓑ	5.460 × 6.370		34.7802
Ⓑ	2.730 × 8.190		22.3587
合計			72.0447 72.04

(21.7坪)

1階床面積求積表

番号	計算式	(m)	面積 (㎡)
①	2.730 × 5.460		14.9058
②	3.640 × 6.370		23.1868
③	1.820 × 5.460		9.9372
④	2.730 × 8.190		22.3587
合計			70.3885 70.38


(21.2坪)


延べ床面積表

	番号	(m)	面積 (㎡)
1階床面積	① ② ③ ④		70.3885
2階床面積			
合計			70.3885 70.38

(21.2坪)


決定図

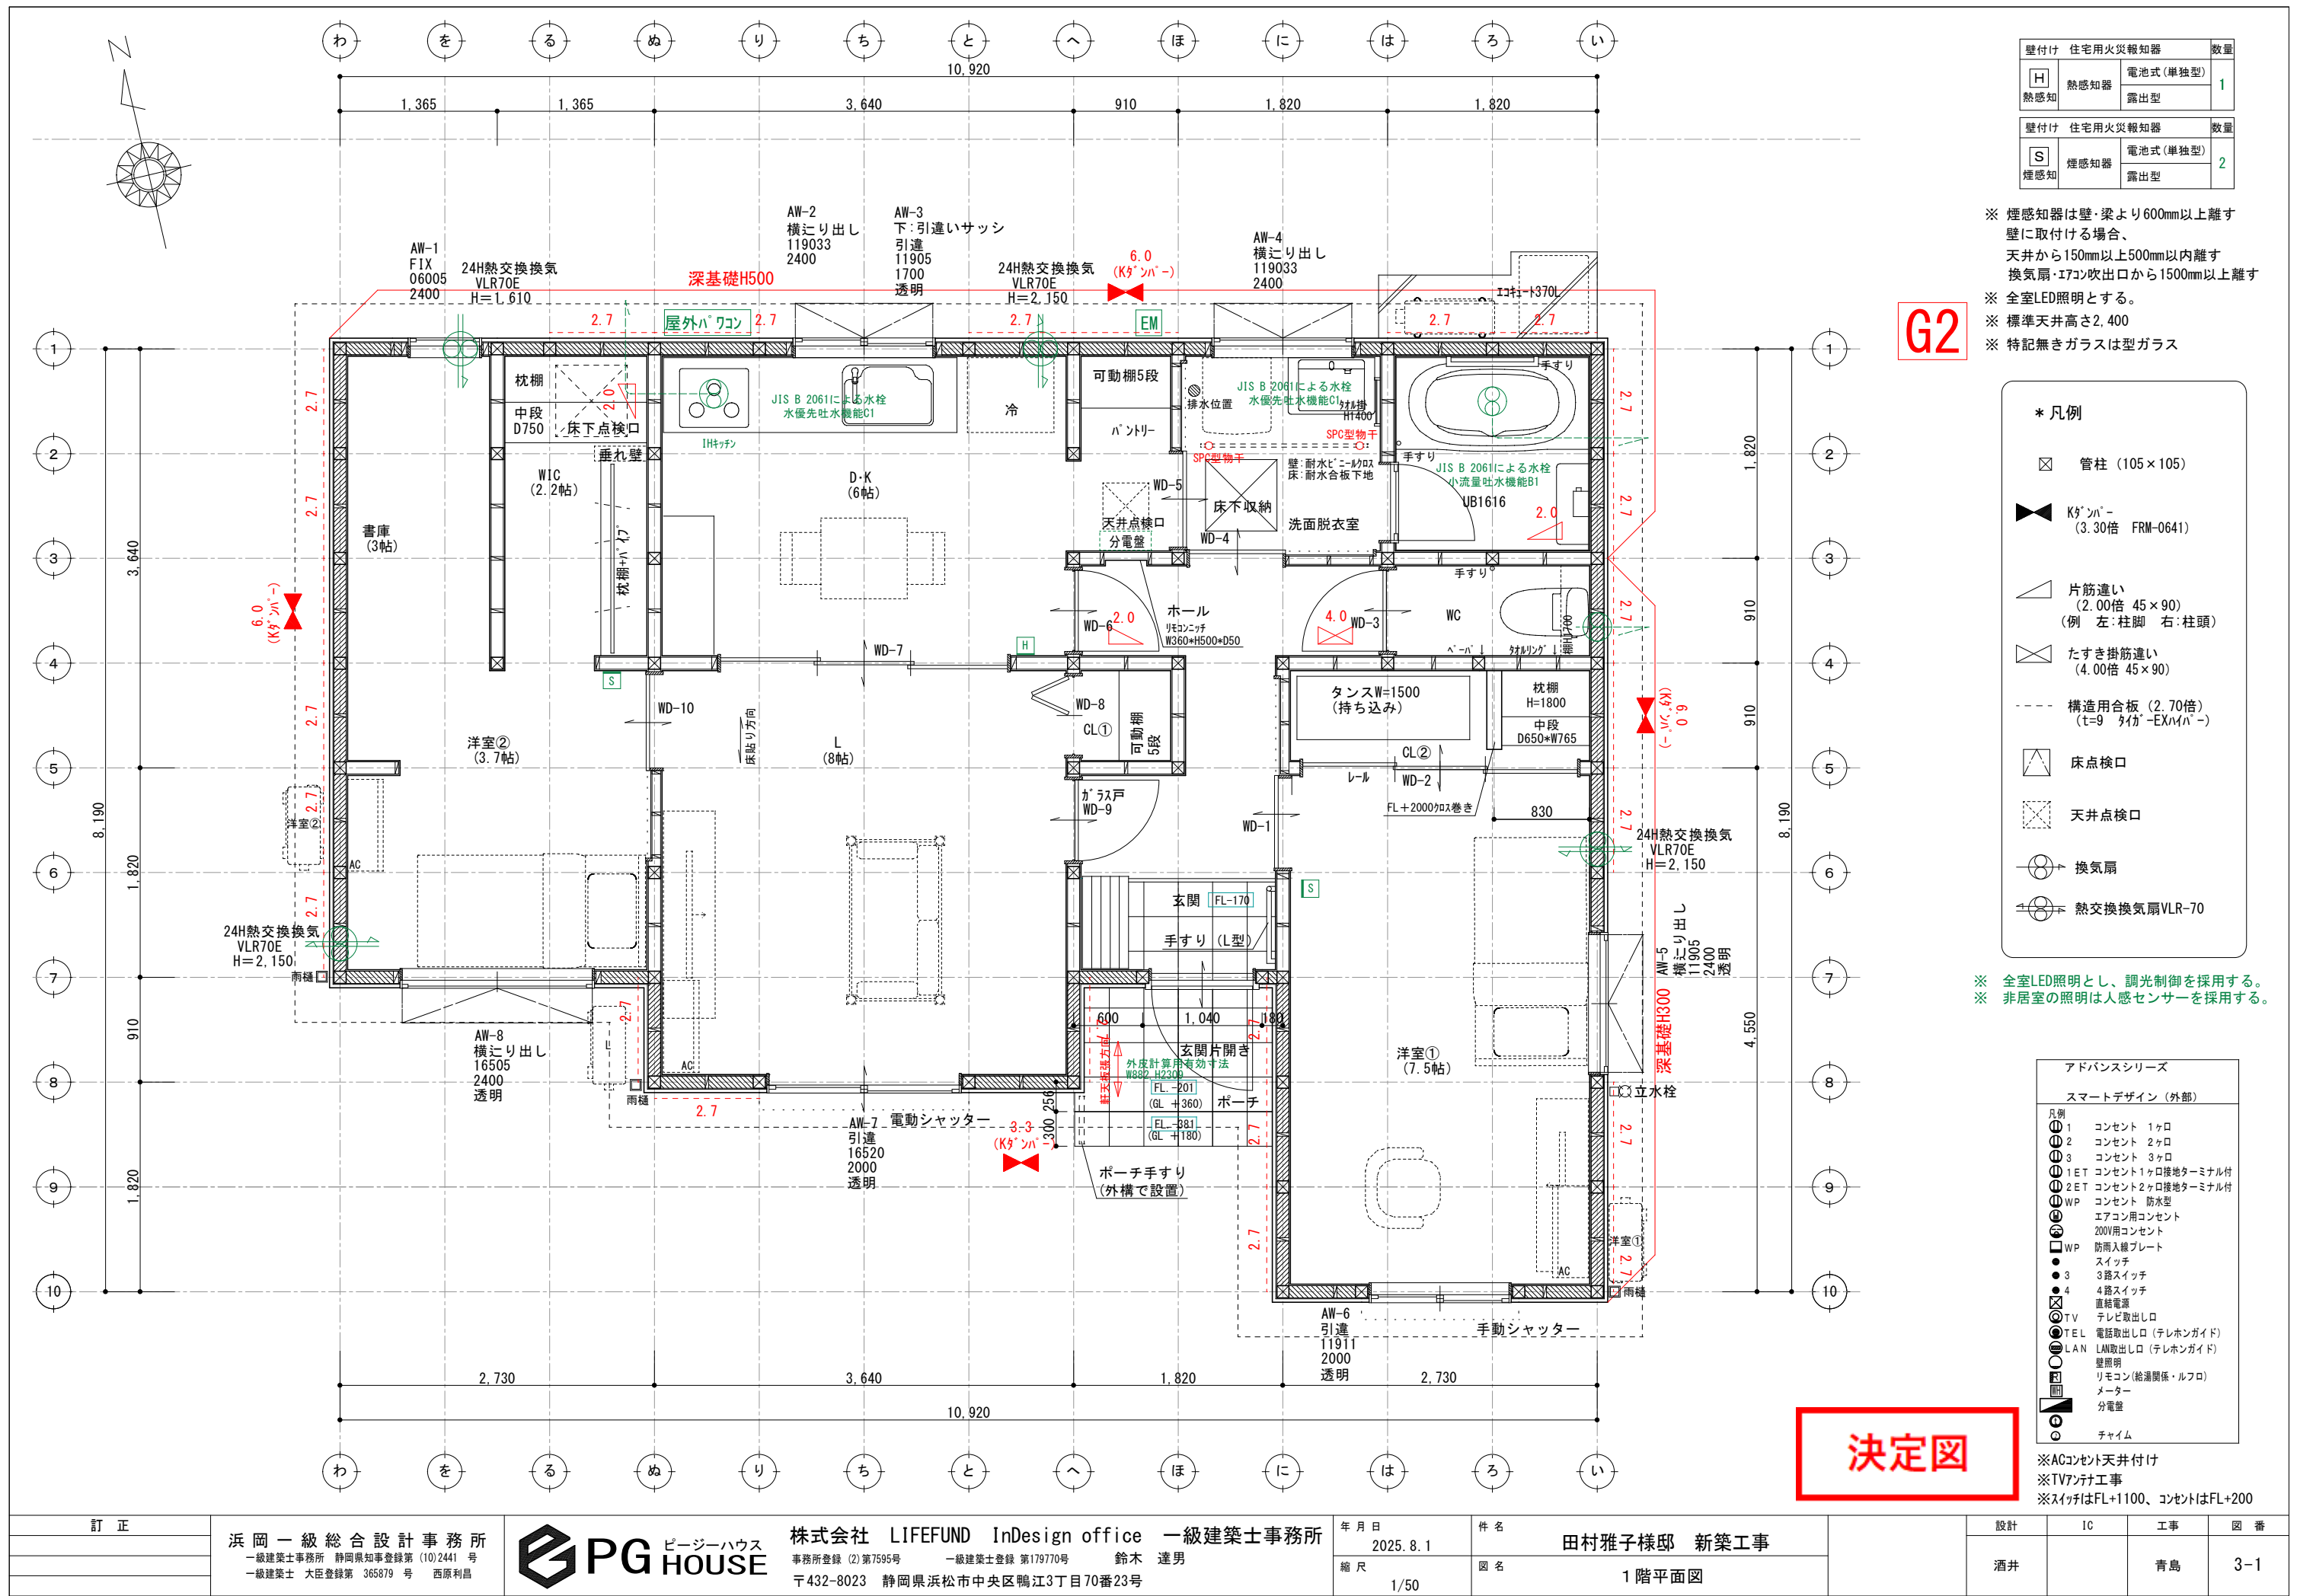

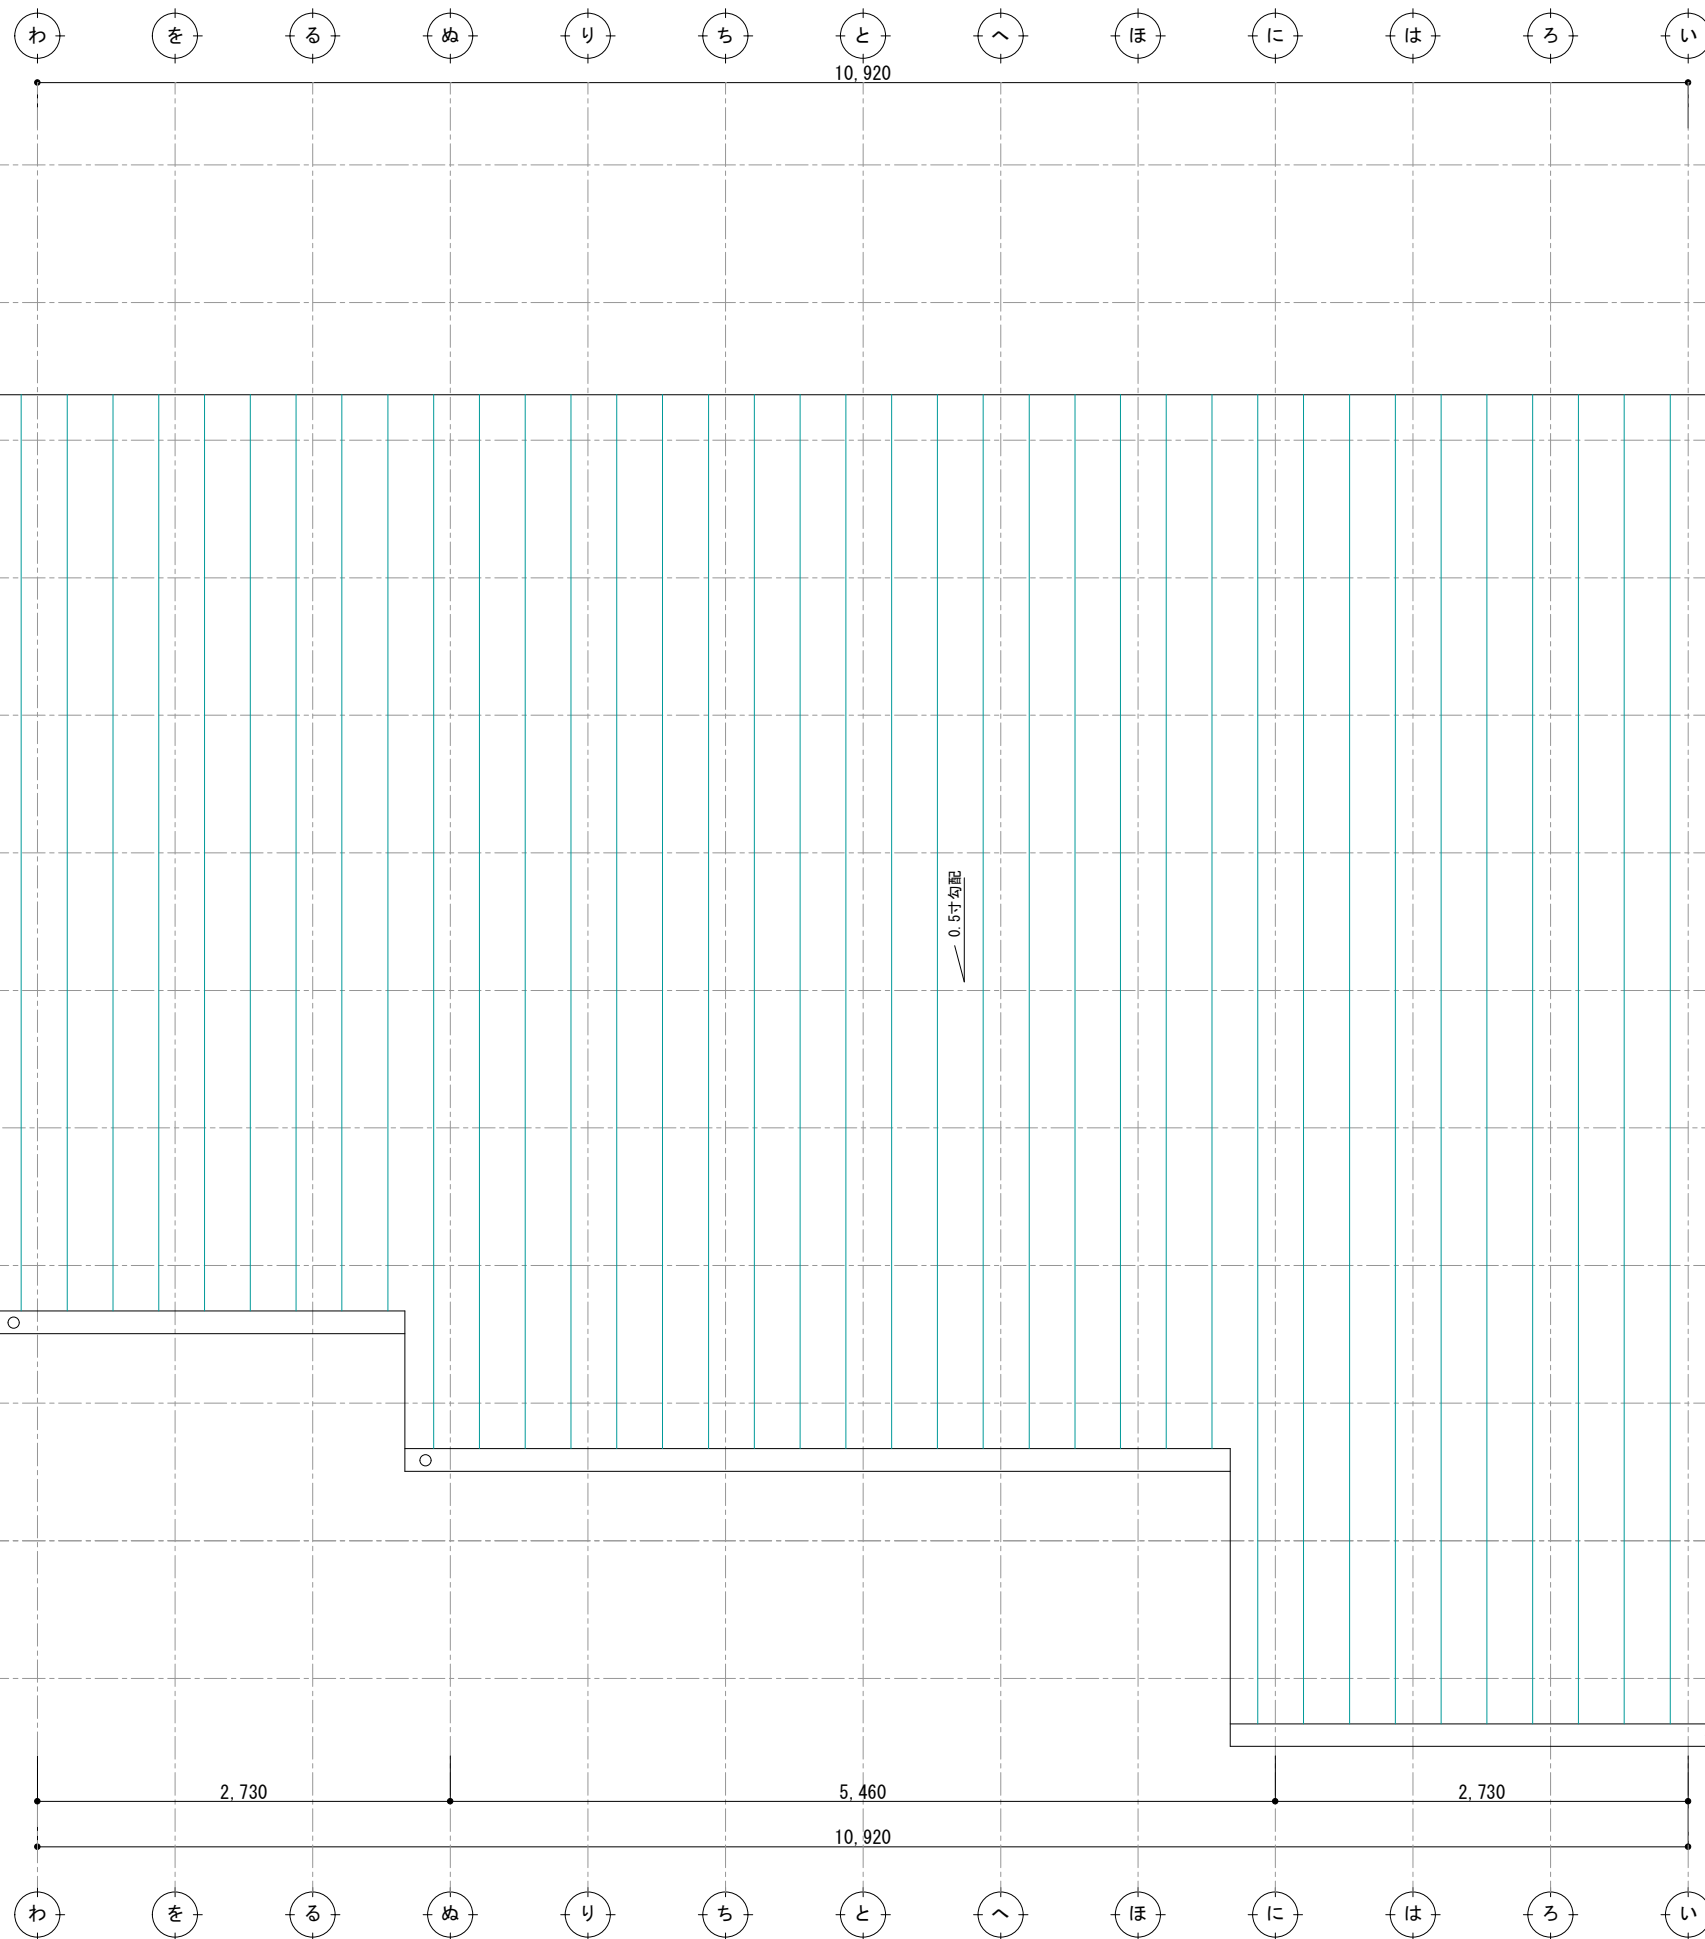


決定図

訂 正	浜 岡 一 級 総 合 設 計 事 務 所 一級建築士事務所 静岡県知事登録第 (10)2441 号 一級建築士 大臣登録第 365879 号 西原利昌		株式会社 LIFEFUND InDesign office 一級建築士事務所 事務所登録 (2) 第7595号 一級建築士登録 第179770号 鈴木 達男 〒432-8023 静岡県浜松市中央区鴨江3丁目70番23号	年 月 日	件 名		設計	IC	工事	図 番
				2025. 8. 1	田村雅子様邸 新築工事					
				縮 尺	図 名					
				1/100	屋根伏図		酒井		青島	3-3

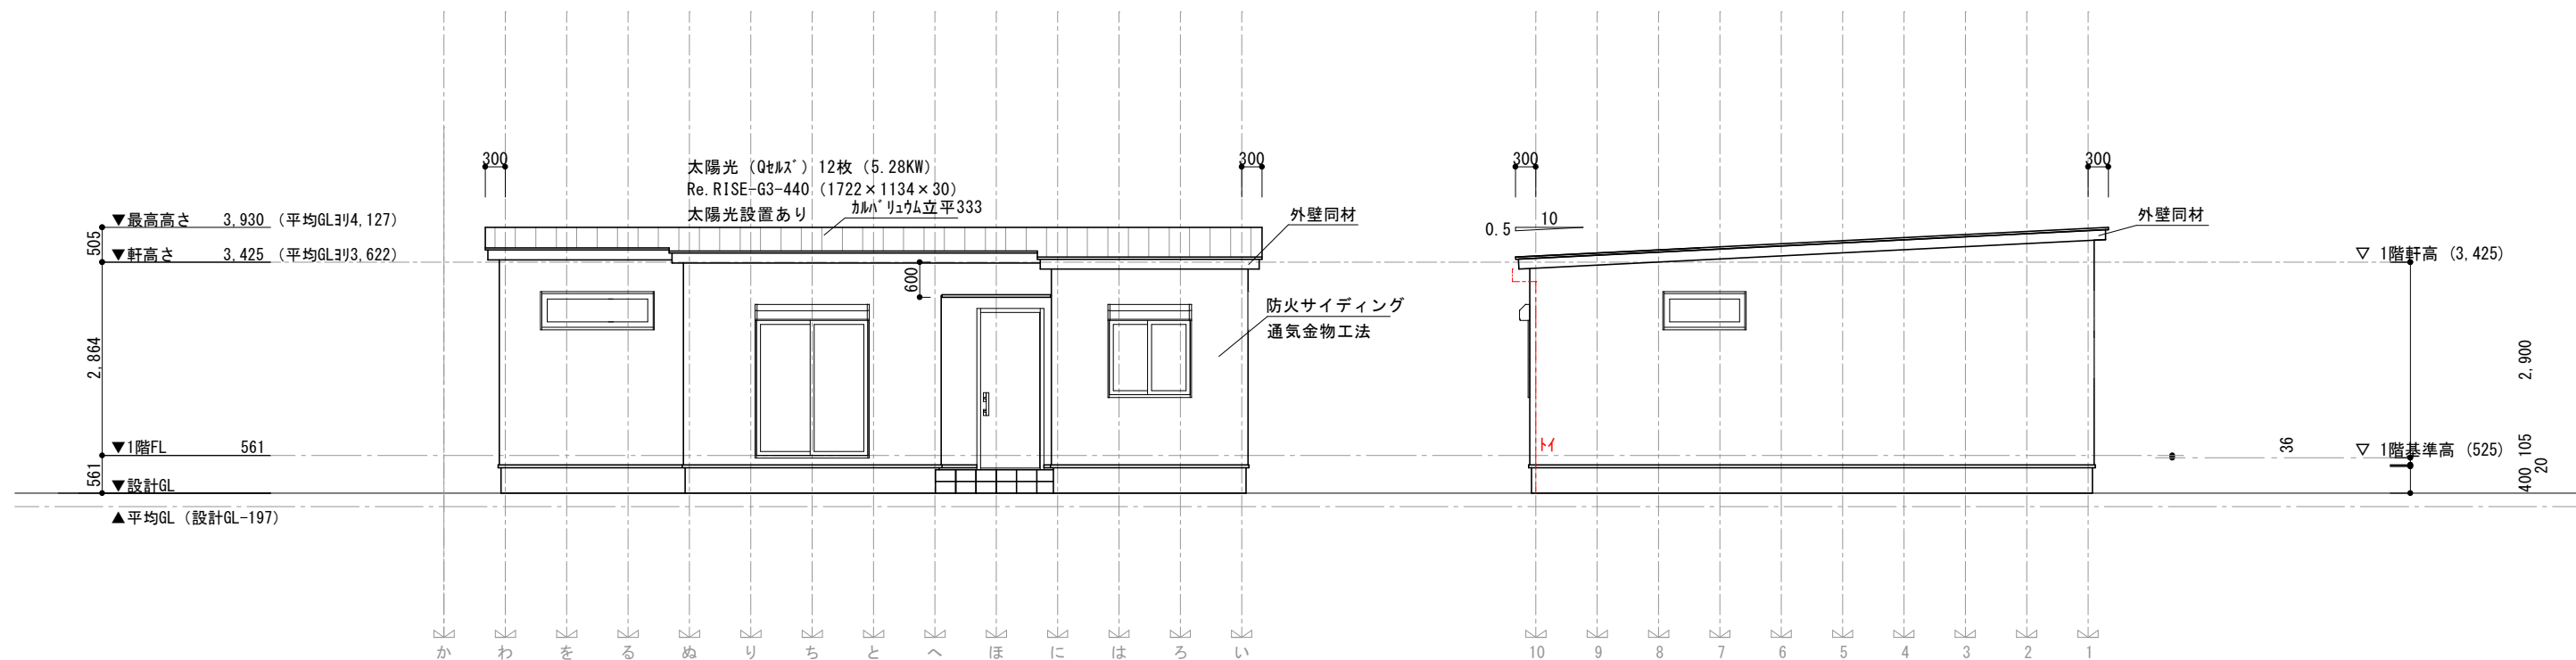

南側立面図 S=1/100


東側立面図 S=1/100

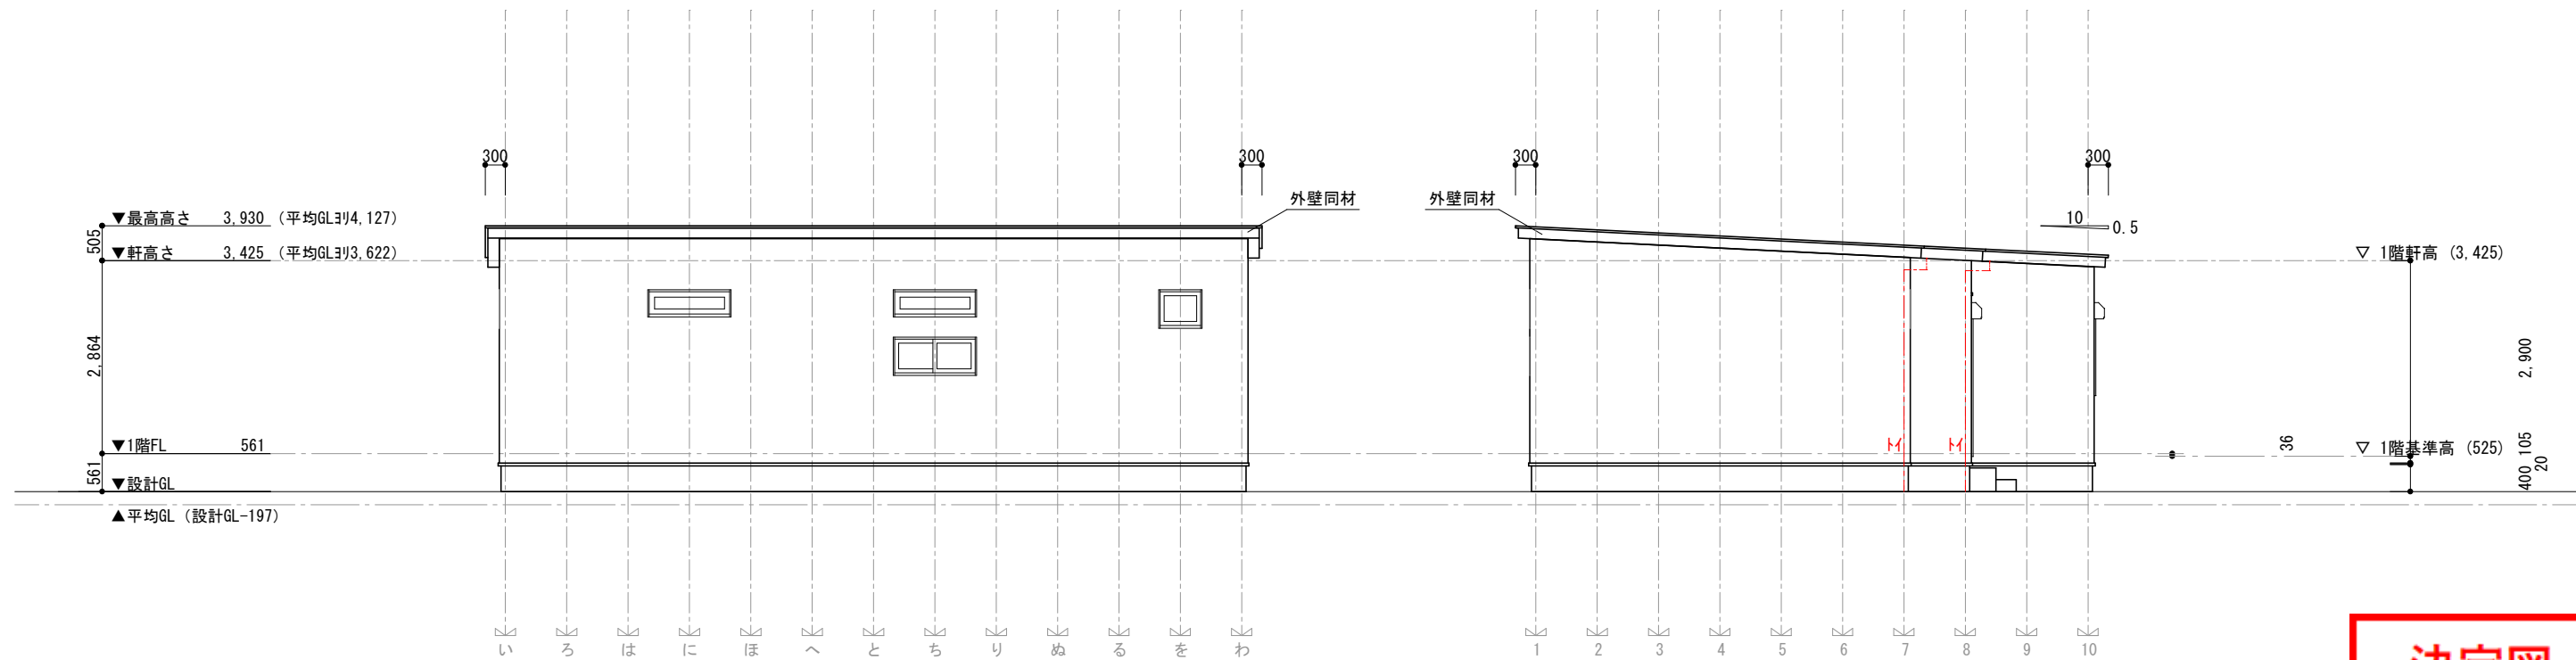

北側立面図 S=1/100


西側立面図 S=1/100

決定図

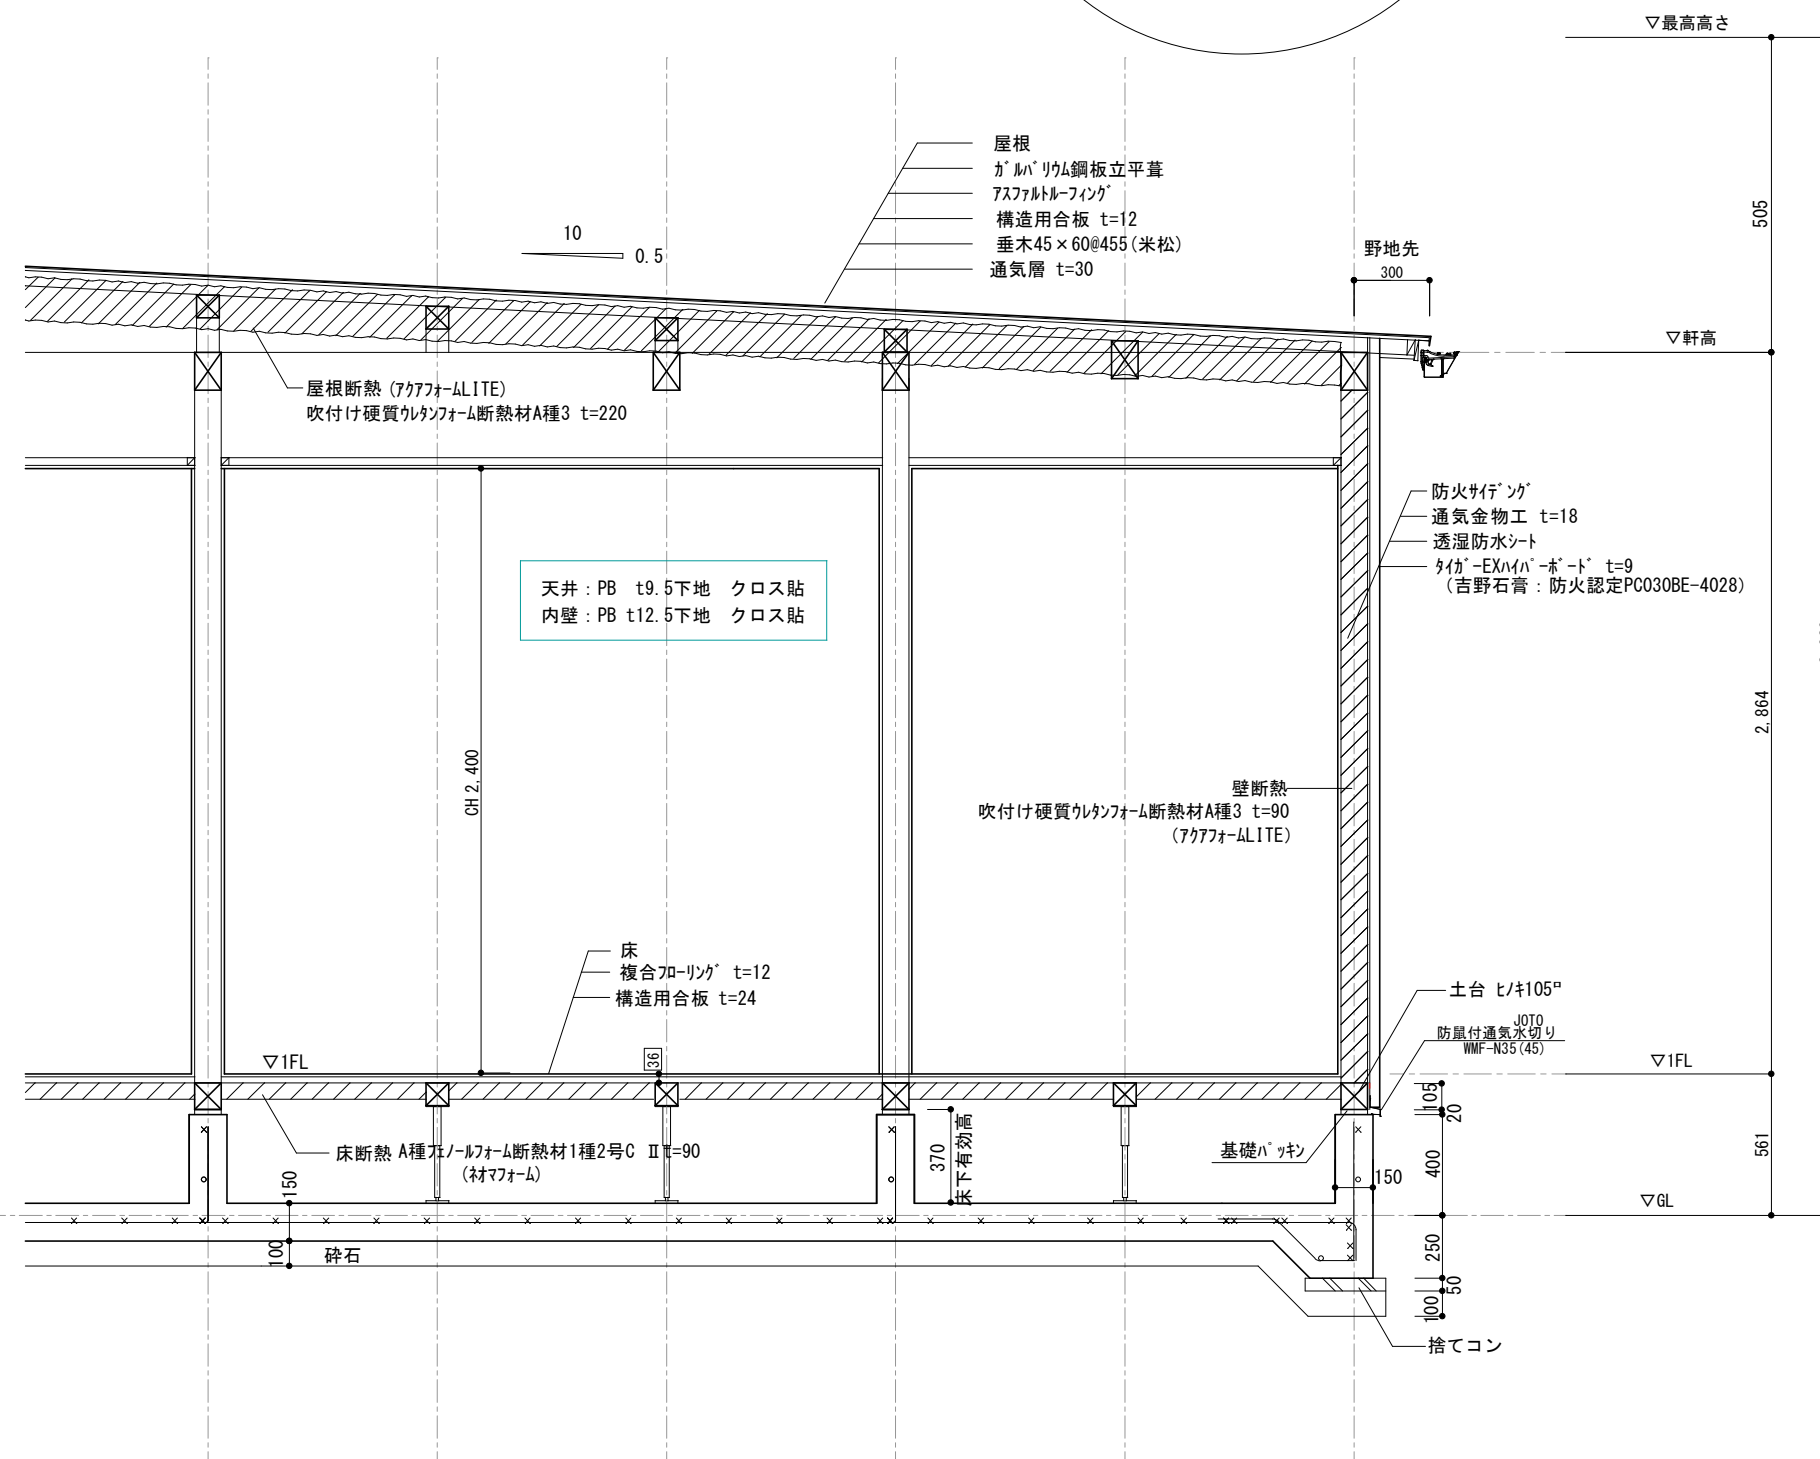


決定図

訂 正	浜 岡 一 級 総 合 設 計 事 務 所 一級建築士事務所 静岡県知事登録第 (10)2441 号 一級建築士 大臣登録第 365879 号 西原利昌	 PG HOUSE	株式会社 LIFEFUND InDesign office 一級建築士事務所 事務所登録 (2)第7595号 一級建築士登録 第179770号 鈴木 達男 〒432-8023 静岡県浜松市中央区鴨江3丁目70番23号	年 月 日 2025. 8. 1	件 名 田村雅子様 邸新築工事		設計	IC	工事	図 番
				縮 尺 1/30	図 名 矩計図		酒井		青島	5

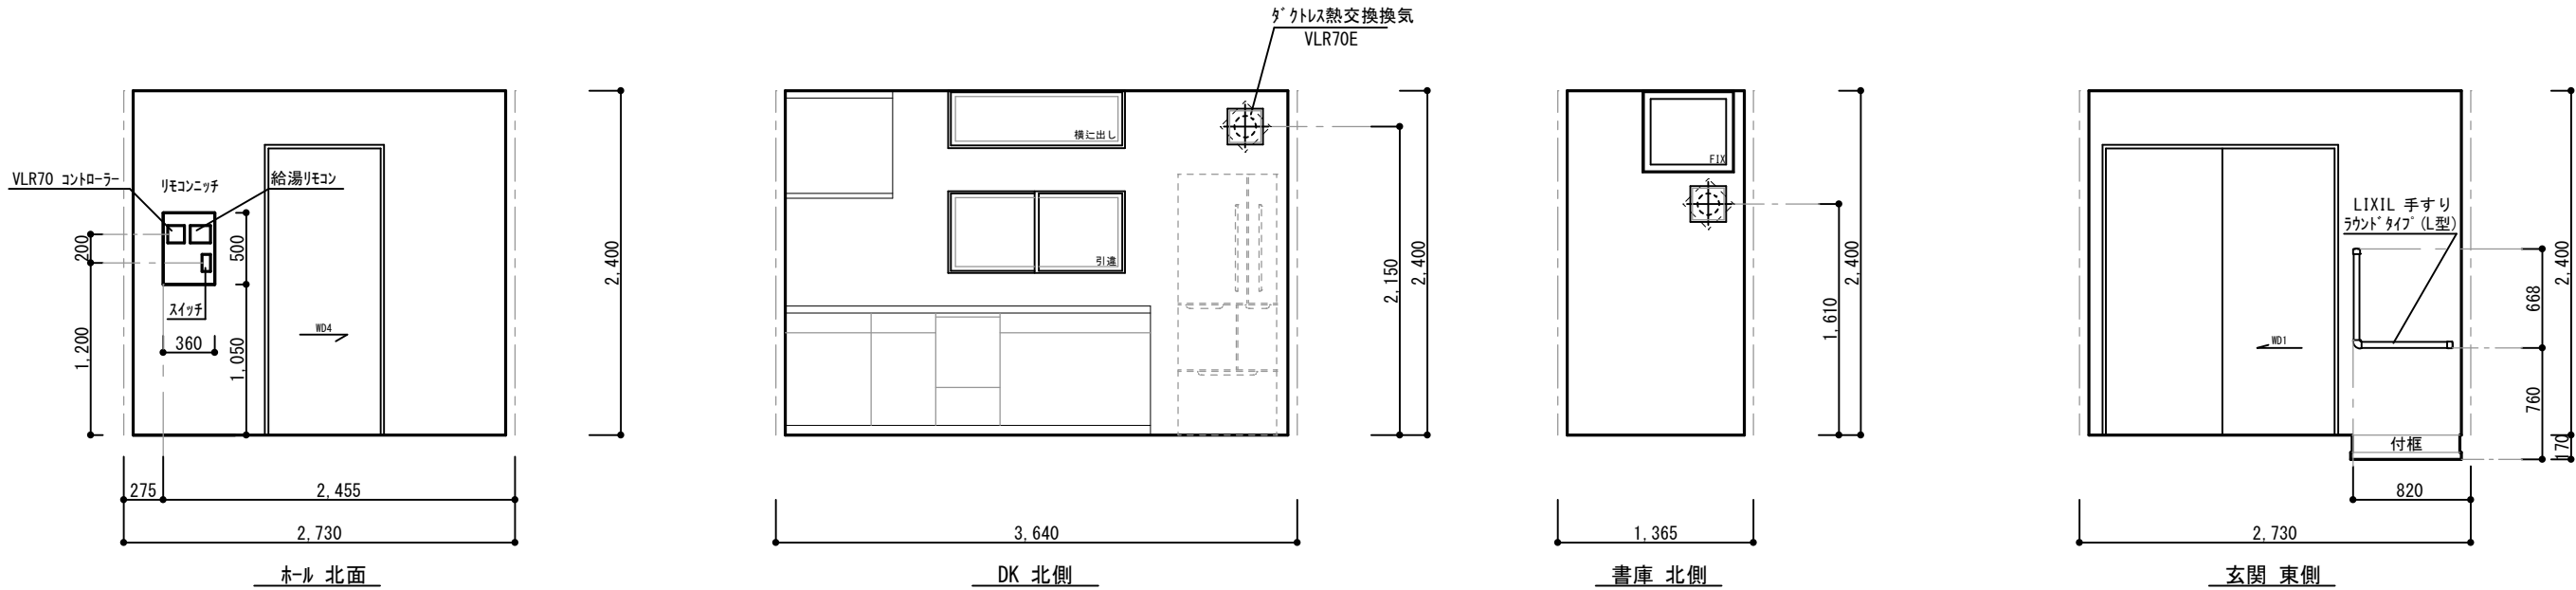


決定図

訂正	浜岡一級総合設計事務所 一級建築士事務所 静岡県知事登録第 (10)2441 号 一級建築士 大臣登録第 365879 号 西原利昌	LIFEFUND PG HOUSE	株式会社 LIFEFUND InDesign office 一級建築士事務所 事務所登録 (2) 第7595号 一級建築士登録 第179770号 鈴木 達男 〒432-8023 静岡県浜松市中央区鴨江3丁目70番23号	年月日 2025.8.1	件名 田村雅子様 新築工事		設計	IC	工事	図番
				縮尺 1/50	図名 展開図-1		酒井		青島	6-1

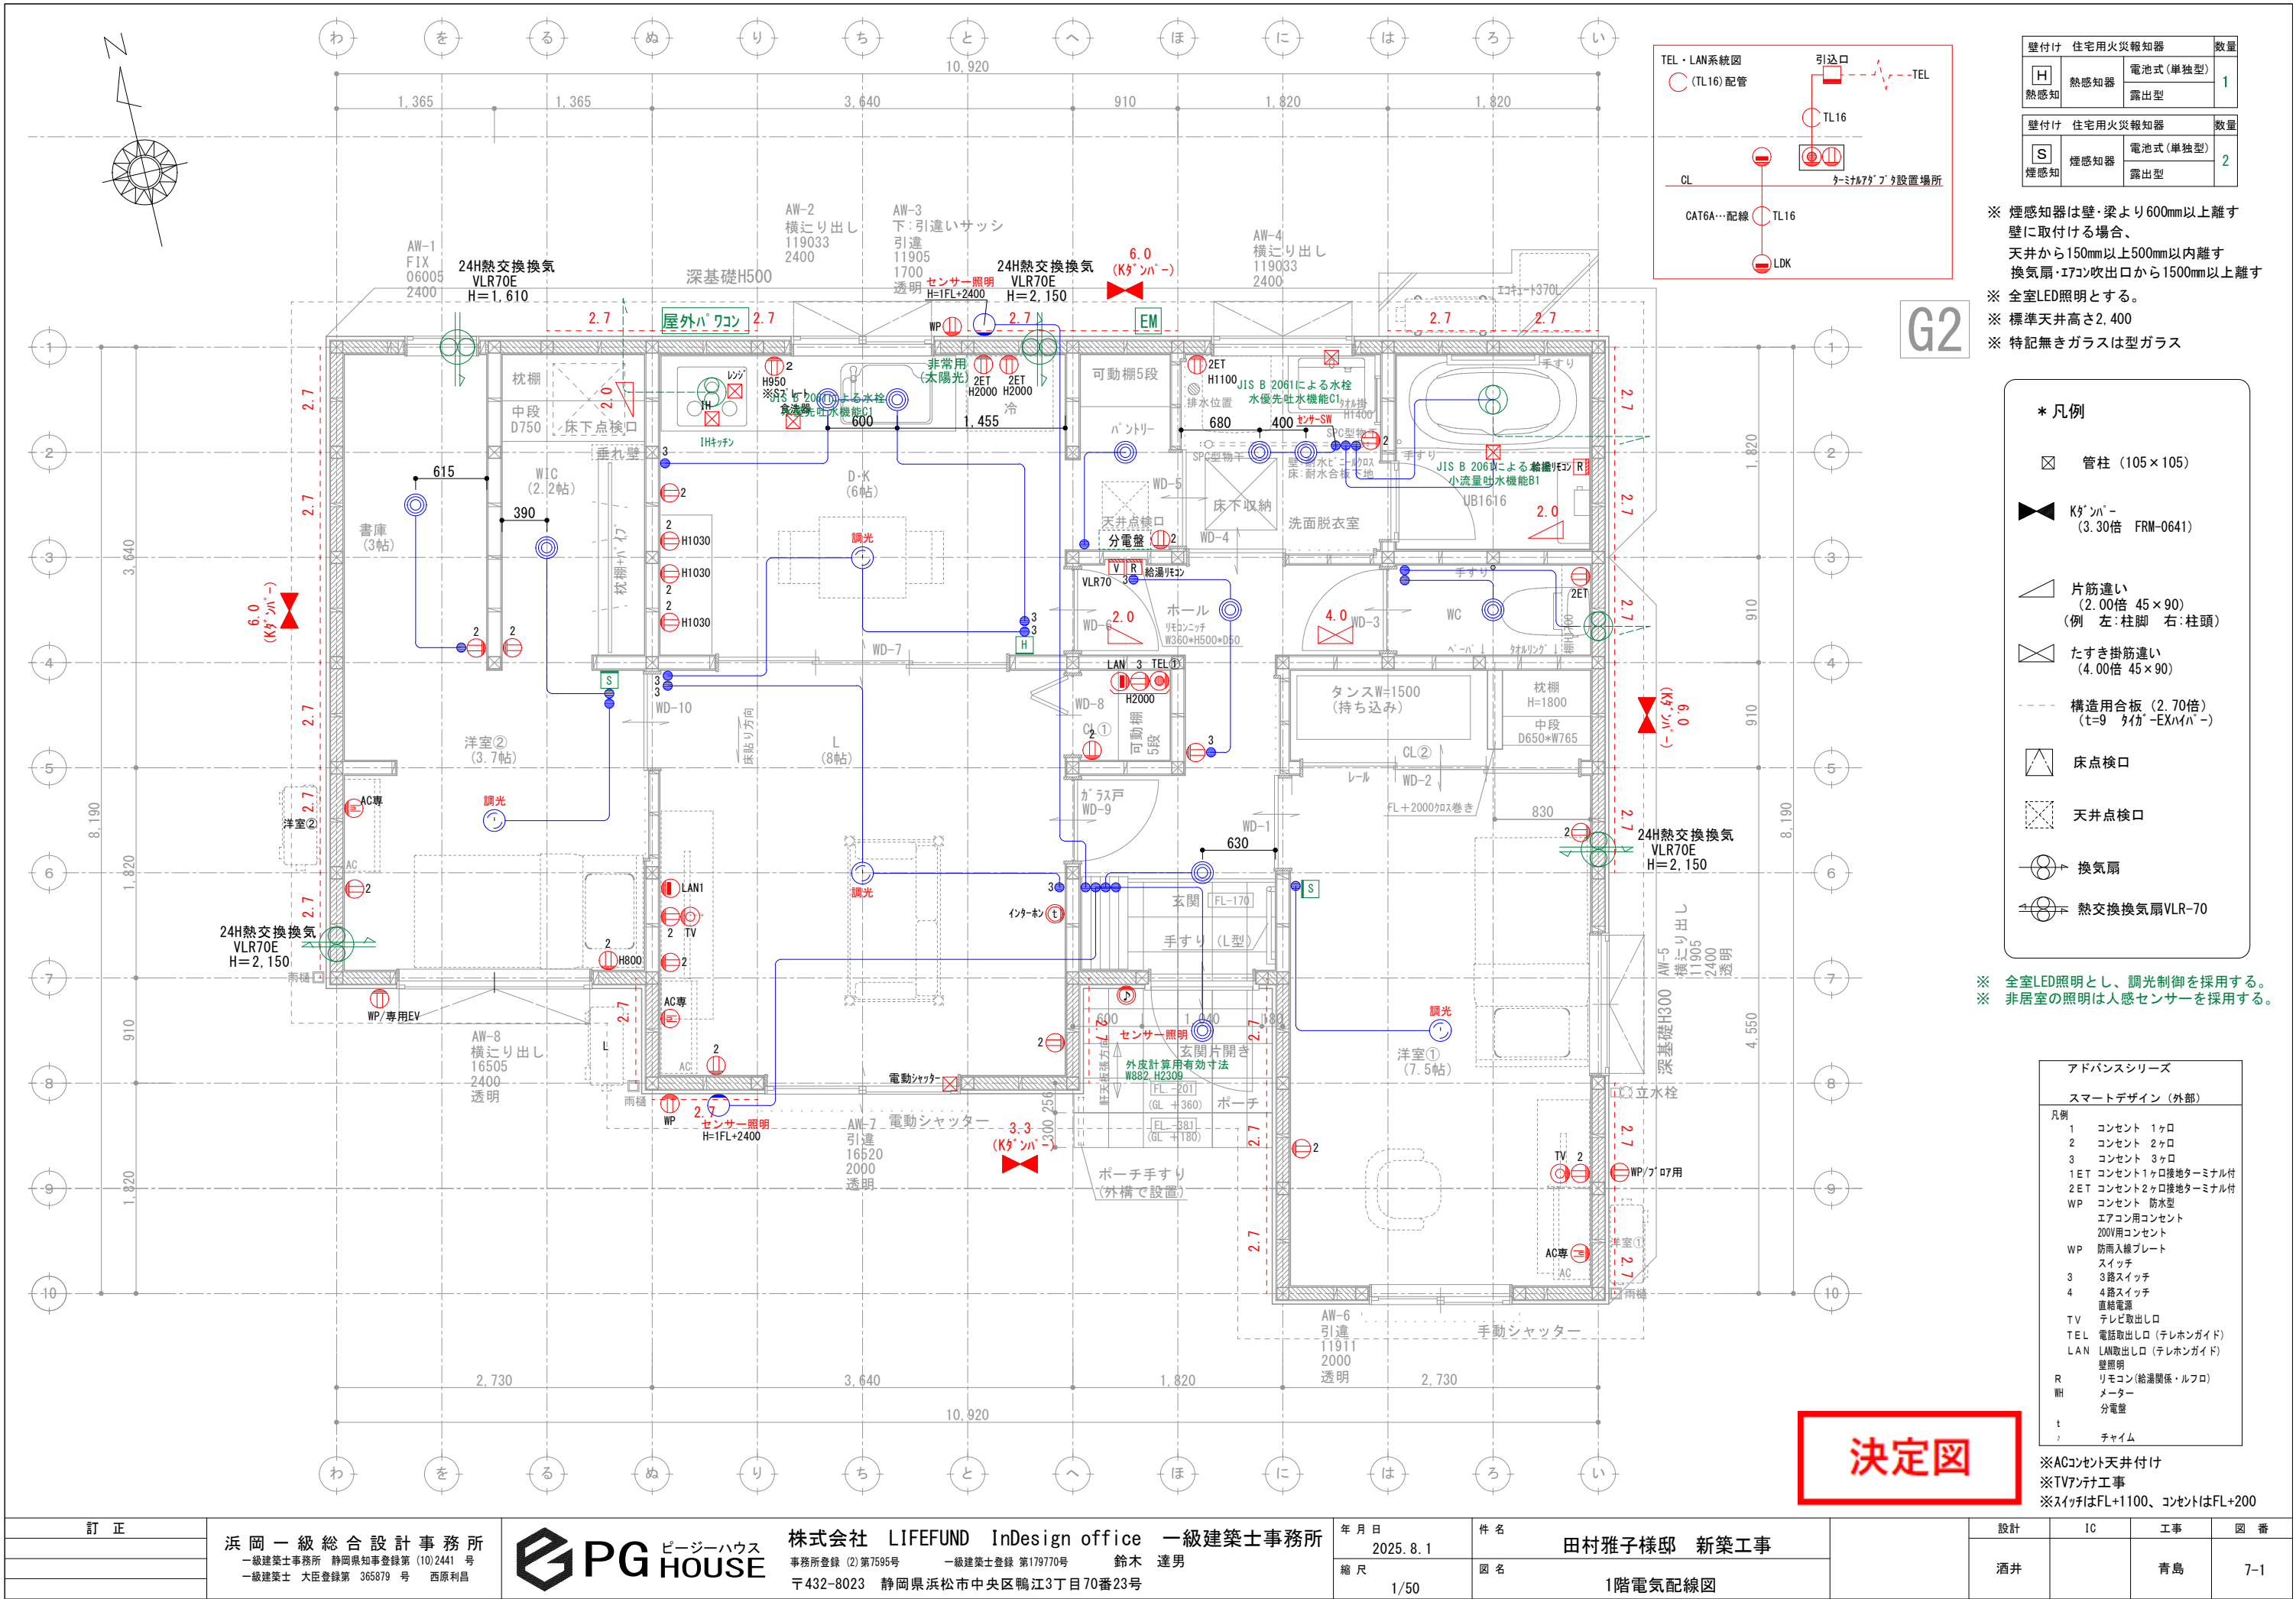

決定図

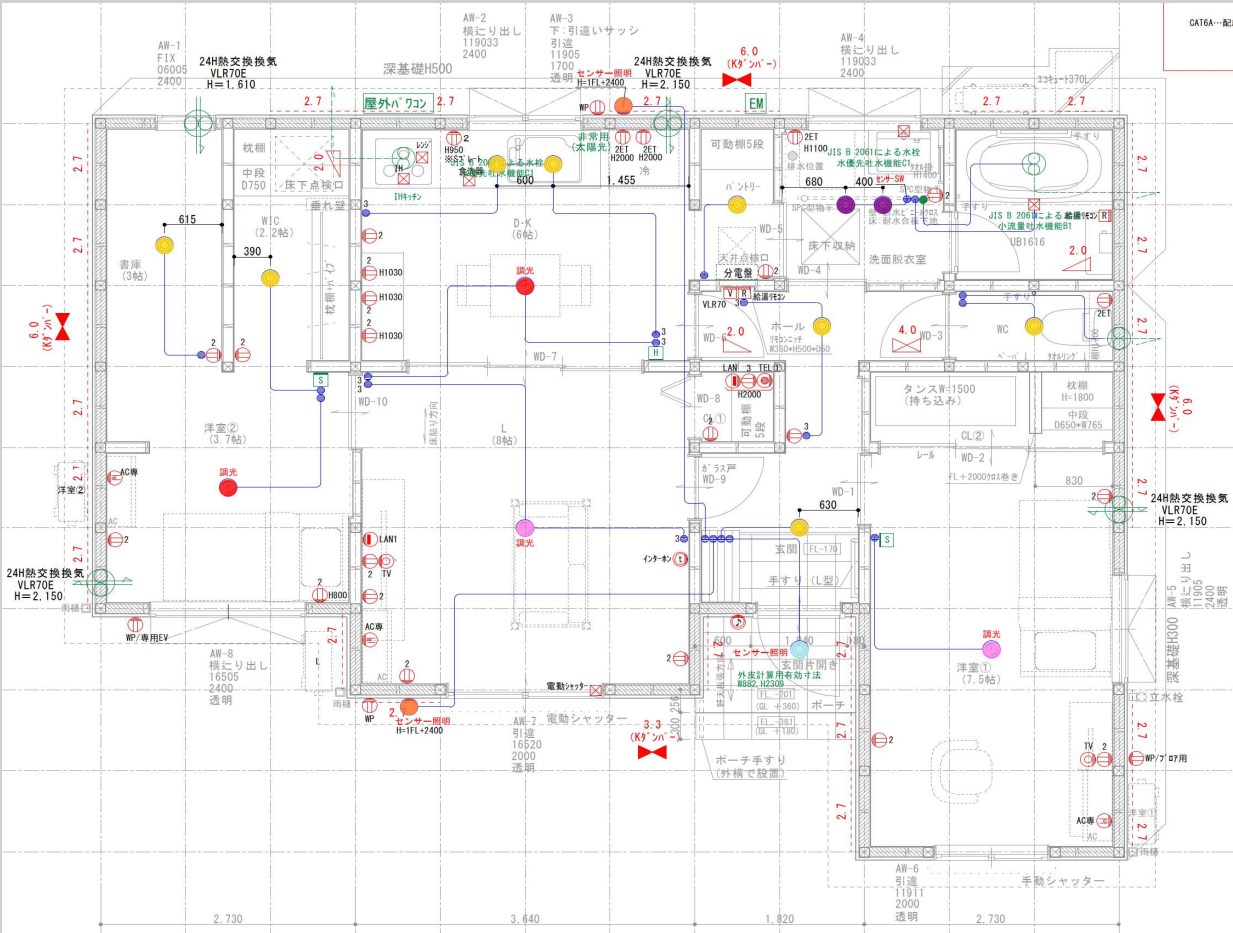

1階

ドアホン：VL-SE31XL
(Panasonic)



内部SW：アドバンス
マットホワイト



ポーチ灯

×1

センサー付きダウナイト

DDL_4496YW

基本照明ダウナイト

×8

DDL_6102YW

洗面脱衣室

×2

ダウナイト

DDL_6102AW

L、洋室①

×2

シーリングライト

DCL_40508

D、洋室②

×2

シーリングライト

DCL_40507

洗面脱衣室

×1

センサー-SW

WTA_14119W

外部

×2

外部灯

AU_55959

高気密Se形
人感センサー

連動マルチタイプ

電球色 2700K・Ra83

DDL-4496 YW

¥16,800(税抜) (LED内蔵)

定格光束 420lm 消費電力 7.7W

LED 7.7W 白熱灯60W相当

●アルミダイカスト 白塗装

●アクリル 乳白(マット)

●径φ111 埋込穴φ100 埋込深80mm 0.5kg

●14VA

●点灯照度調節機能付(暗・明切)

●点灯保持時間(1分)

●広範囲パネル付 AC100V

●遮り点灯可能 LED調光タイプ60VAまで

LED非調光タイプ不可

●光源寿命50,000時間

●取付可能天井厚5~25mm

●調光器併用不可

防雨形 温度保護機能付

電圧 100V

電流 80mA

LED不可

COBタイプ | 高気密Se形

電球色 / 2700K・Ra83

DDL-6102 YW

¥3,600-(税抜) (LED内蔵)

定格光束 消費電力 照度(1m) 消費電力

440lm 4.6W 95.6lm/W

LED 4.6W 白熱灯60W相当

●銅板 白塗装

●アクリル 乳白(マット)

●径φ116 埋込穴φ100 埋込深70mm 0.3kg

●8VA

●広範囲パネル付

●AC100V

●光源寿命60,000時間

●取付可能天井厚5~25mm

●調光器併用不可

防雨形 温度保護機能付

電圧 100V

電流 70mA

LED不可

COBタイプ | 高気密Se形

電球色 / 3500K・Ra83

DDL-6102 AW

¥3,600-(税抜) (LED内蔵)

定格光束 消費電力 照度(1m) 消費電力

470lm 4.6W 102.1lm/W

LED 4.6W 白熱灯60W相当

●銅板 白塗装

●アクリル 乳白(マット)

●径φ116 埋込穴φ100 埋込深70mm 0.3kg

●8VA

●広範囲パネル付

●AC100V

●光源寿命60,000時間

●取付可能天井厚5~25mm

●調光器併用不可

防雨形 温度保護機能付

電圧 100V

電流 70mA

LED不可

タイマー付リモコンブルレス | 調色調光タイプ

DCL-40508

昼光色 / 6500K・Ra83 ~ 電球色 / 2700K・Ra83

LED 34W 定格光束 消費電力 照度(1m) 消費電力

4280lm 34W 126.4lm/W

¥26,000-(税抜) (LED内蔵)

●アクリル 乳白(マット)

●径φ510 高さ128mm 1.6kg

●フルレリースイッチ付(全灯・点灯・常夜灯)

●調光機能付(6500K~2700K)

●調色機能付(5%~100%)

●調光器併用不可

●AC100V

●光源寿命40,000時間

●消費効率(全光束) 100lm/W

●調光器併用不可

●シーメントローラーは使用できません。

クリック取付式

カバー取付式

55° DP-40091 可能 電圧 100V 電流 34W

タイマー付リモコンブルレス | 調色調光タイプ

DCL-40507

昼光色 / 6500K・Ra83 ~ 電球色 / 2700K・Ra83

LED 29.5W 定格光束 消費電力 照度(1m) 消費電力

3698lm 29.5W 125.3lm/W

¥22,000-(税抜) (LED内蔵)

●アクリル 乳白(マット)

●径φ510 高さ128mm 1.6kg

●フルレリースイッチ付(全灯・点灯・常夜灯)

●調光機能付(6500K~2700K)

●調色機能付(5%~100%)

●調光器併用不可

●AC100V

●光源寿命40,000時間

●消費効率(全光束) 100lm/W

●調光器併用不可

●シーメントローラーは使用できません。

クリック取付式

カバー取付式

55° DP-40091 可能 電圧 100V 電流 29.5W

◆RAS(3A) (親器)

3線 / 4線式

WTA14119W

壁取付 熱線センサ付自動スイッチ(親器)

(検知後連続動作時間 約10秒~30分可変形)

(明るさセンサ・手動スイッチ付)(マットホワイト)

3A 100V AC

プレート別売

人感センサ付タイマー付
ON-OFFタイプ

100W相当

AU 55959

¥39,800(税抜)

電球色 2700K・Ra83 8.3W 740lm 89.1lm/W

LED

本体：アルミダイカスト・サテンブラック塗装

パネル：ガラス・透明

●重量 1.0kg

●光束維持時間:40,000時間

●照度センサ付

●センサモード切替可能

●点灯照度調節可能

●点灯時間切替可能:約30秒/1分/3分/5分/10分

(点灯中に動作を感知するとセンサが作動し点灯時間が延長されます)

●照射近接検知 10cm

●灯具を下に向けた場合は感知エリアが狭くなります

●調光器併用不可

●17VA(100V)

N型 R型

防雨型

電圧 100V

電流 8.3W

LED不可

外部：スマートデザインシリーズ
ホワイトシルバー



決定図

PG House


田村雅子様

邸新築工事

Lighting Plan

2025.8.1

(図面 7-3)

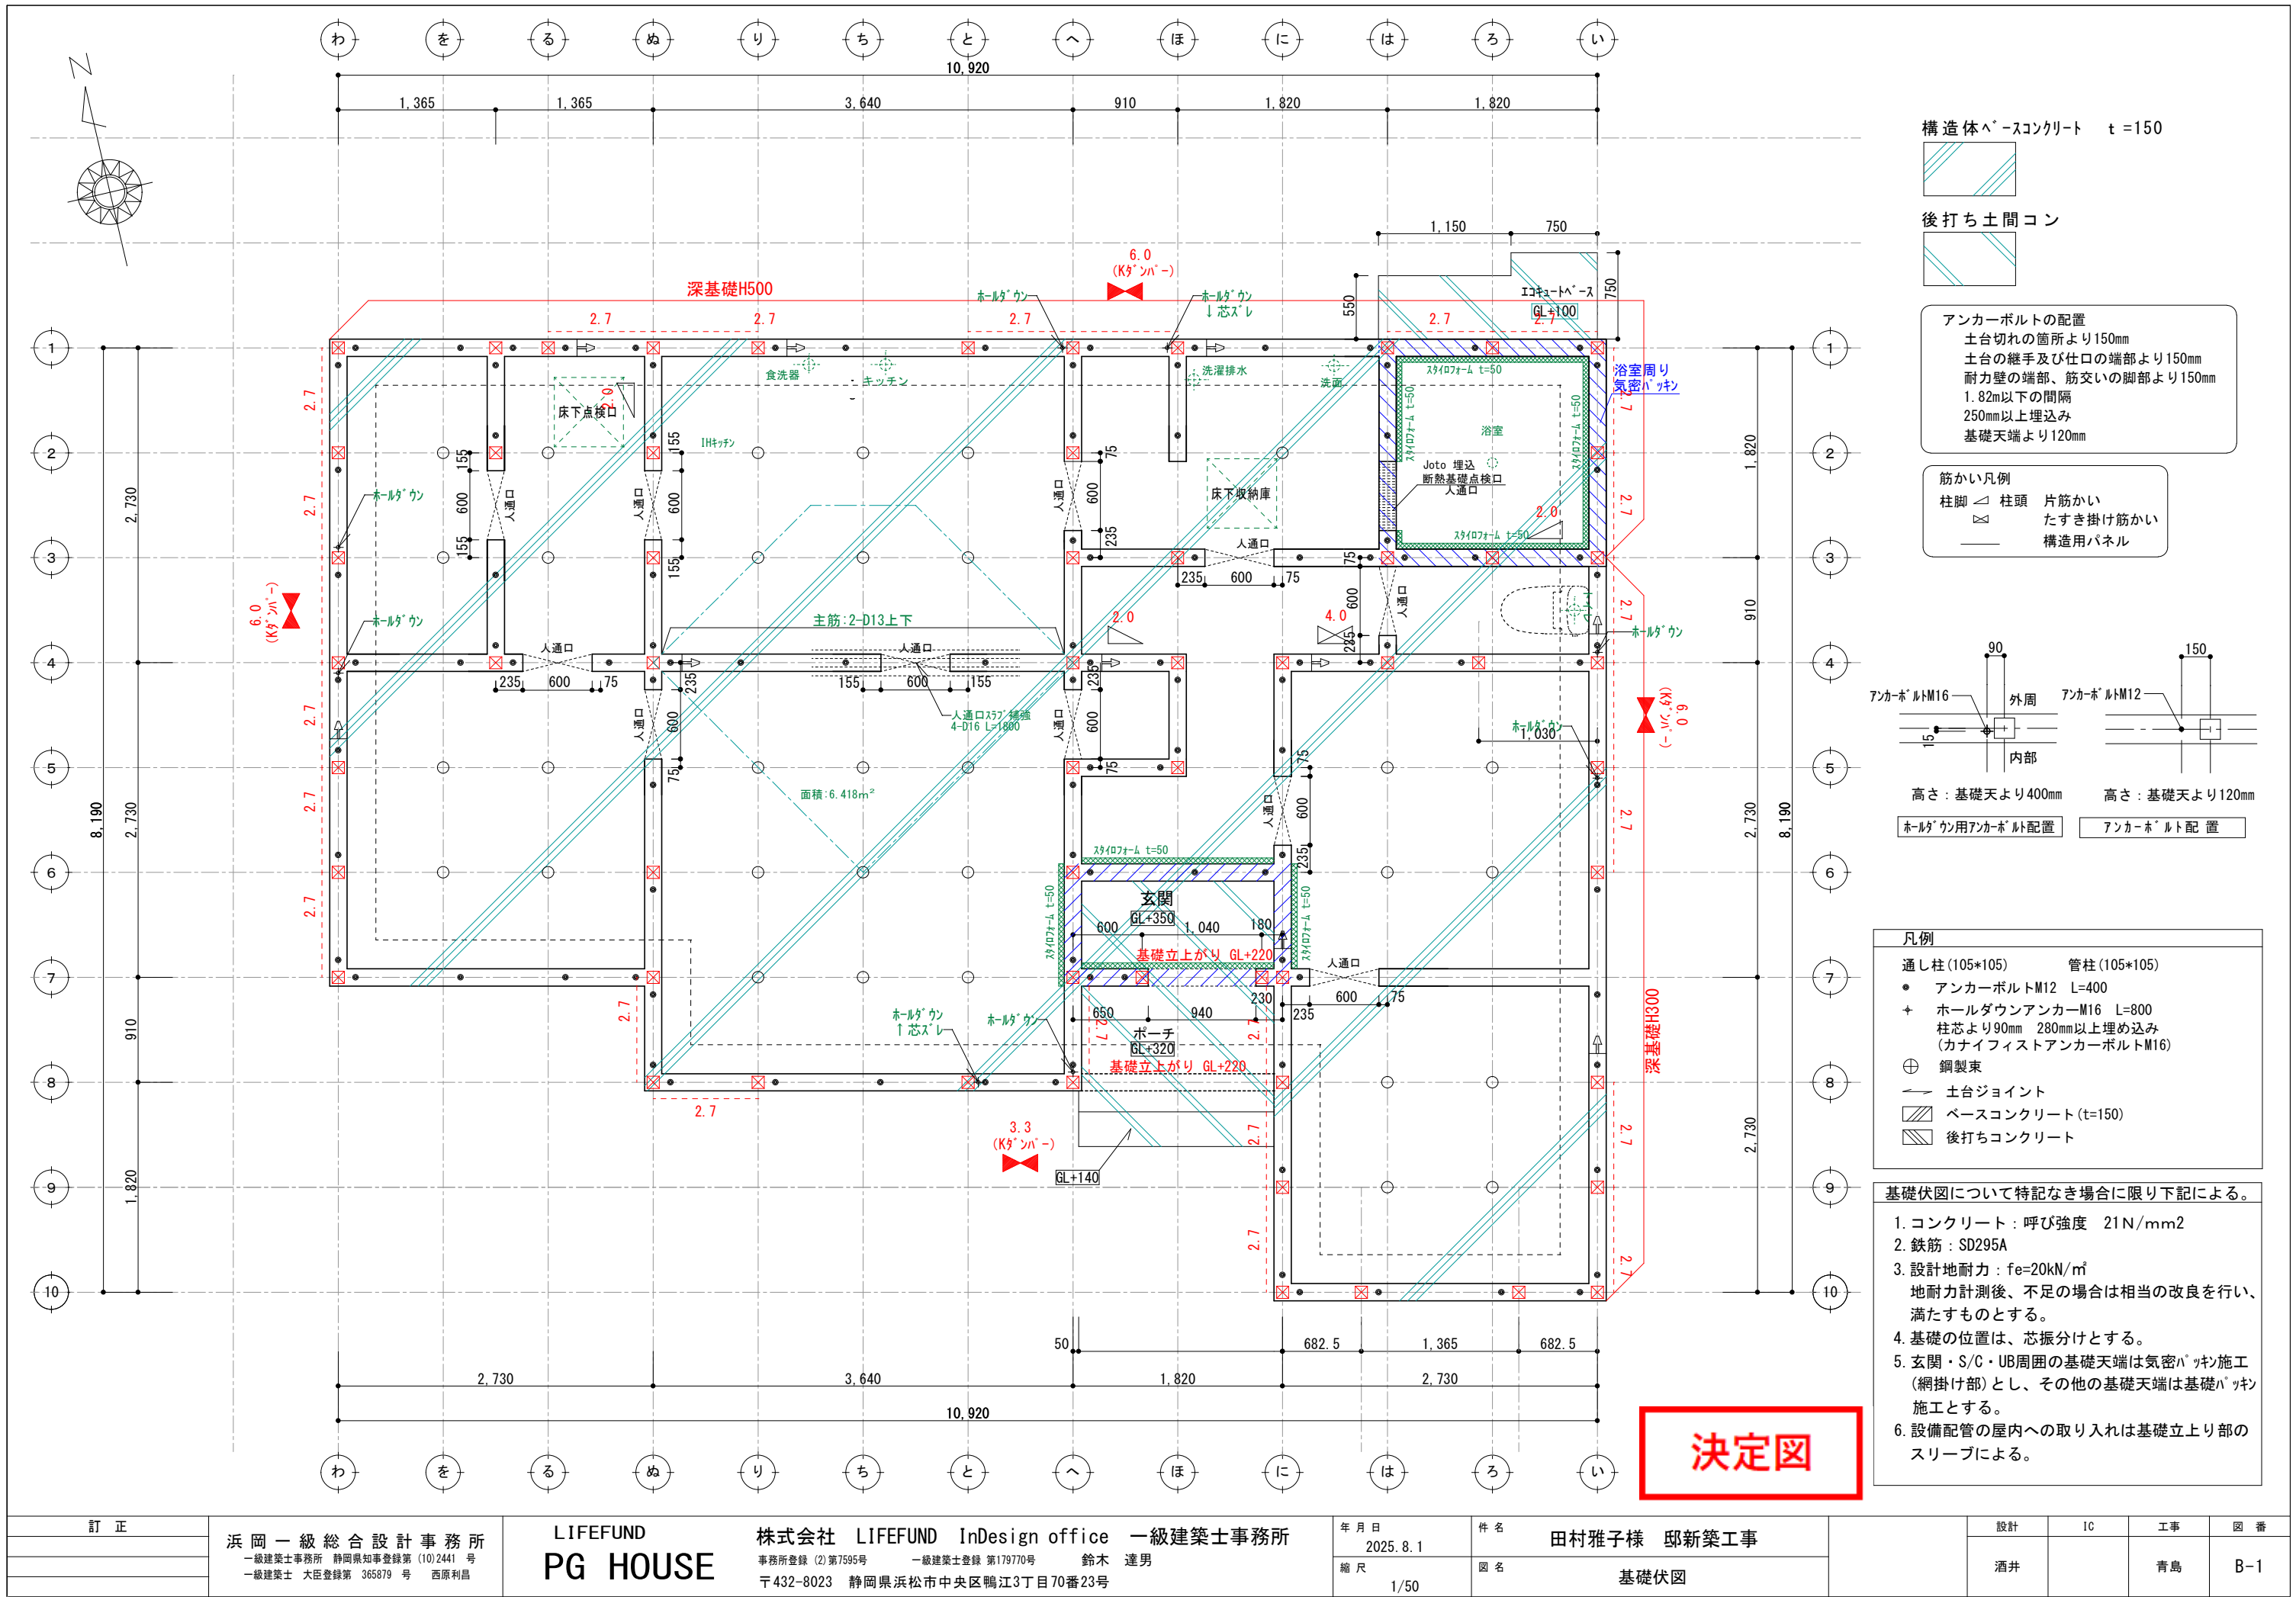

構造体ベースコンクリート t=150


後打ち土間コン

アンカーボルトの配置

- 土台切れの箇所より150mm
- 土台の継手及び仕口の端部より150mm
- 耐力壁の端部、筋交いの脚部より150mm
- 1.82m以下の間隔
- 250mm以上埋込み
- 基礎天端より120mm

筋かい凡例

- 柱脚 柱頭 片筋かい
- たすき掛け筋かい
- 構造用パネル

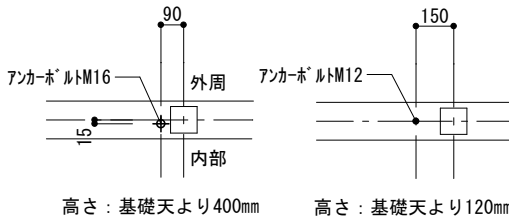

ホールダウン用アンカーボルト配置

アンカーボルト配置


凡例

- 通し柱 (105*105) 管柱 (105*105)
- アンカーボルトM12 L=400
- ホールダウンアンカーM16 L=800
- 柱芯より90mm 280mm以上埋め込み (カナイフリストアンカーボルトM16)
- 鋼製束
- 土台ジョイント
- ベースコンクリート (t=150)
- 後打ちコンクリート

基礎伏図について特記なき場合に限り下記による。

- コンクリート: 呼び強度 21N/mm²
- 鉄筋: SD295A
- 設計地耐力: fe=20kN/m²
地耐力計測後、不足の場合は相当の改良を行い、満たすものとする。
- 基礎の位置は、芯振分けとする。
- 玄関・S/C・UB周囲の基礎天端は気密パッキン施工 (網掛け部) とし、その他の基礎天端は基礎パッキン施工とする。
- 設備配管の屋内への取り入れは基礎立上り部のスリーブによる。

			基礎の寸法 及び 配筋の検証方法 基礎立上り配筋は、 (財)日本住宅・木材技術 センター発行のスパン表 (増補版)による。 ベタ基礎スラブ配筋は、 まもりすまい保険設計施工 基準同解説のベタ基礎配筋表 による。具体的な寸法・配 筋は基礎詳細図参照。 鉄筋断面表記 ●・・・D10を示す。 ×・・・D13を示す。 ※使用しない断面は 決定図												
訂正	浜岡一級総合設計事務所 一級建築士事務所 静岡県知事登録第 (10)2441 号 一級建築士 大臣登録第 365879 号 西原利昌	PG HOUSE	株式会社 LIFEFUND InDesign office 一級建築士事務所 事務所登録 (2)第7595号 一級建築士登録 第179770号 鈴木 達男 〒432-8023 静岡県浜松市中央区鴨江3丁目70番23号	年月日 2025. 8. 1 縮尺 1/30	件名 田村雅子様 邸新築工事 図名 基礎断面リスト		<table><tr><td>設計</td><td>I C</td><td>工務</td><td>図番</td></tr><tr><td>酒井</td><td></td><td>青島</td><td>B-2</td></tr></table>	設計	I C	工務	図番	酒井		青島	B-2
設計	I C	工務	図番												
酒井		青島	B-2												

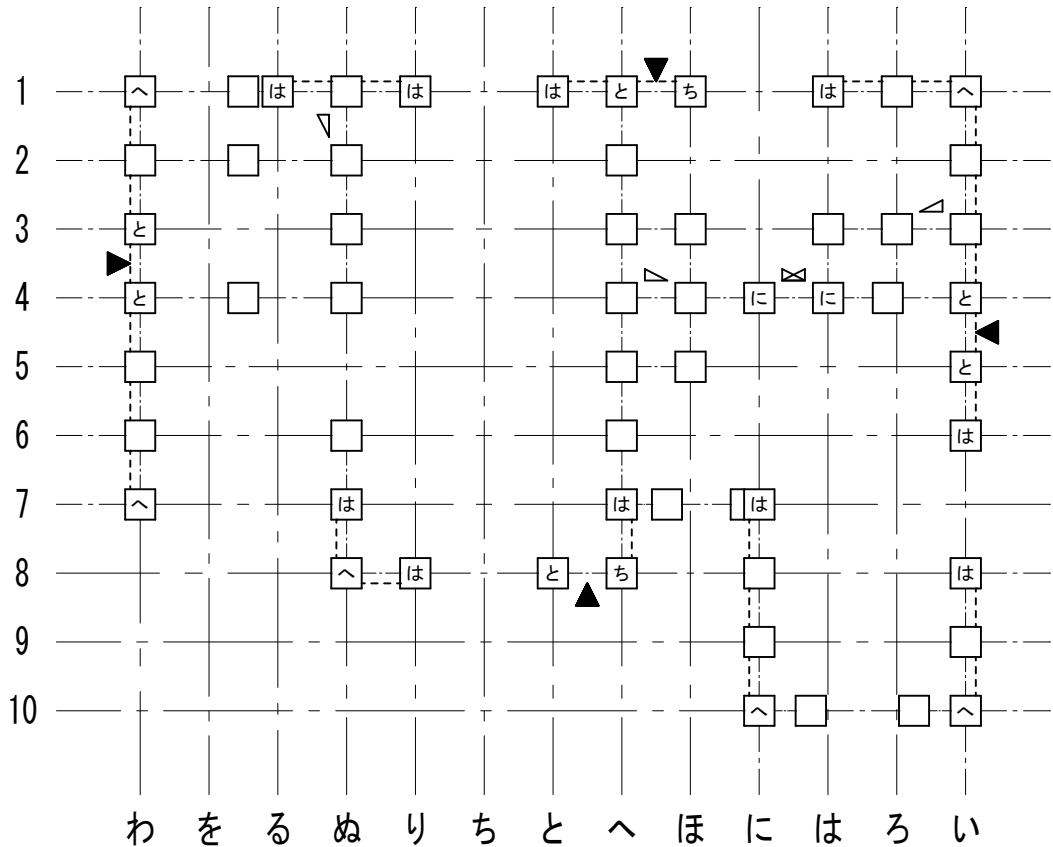

1 階柱壁伏図

接合部凡例				*接合部凡例はユーザ設定されたものです。	
記号	仕様（カナイ金物）		N	倍率	
SBCP	スリムビルドコーナー75, チビクリCK(化粧柱の場合)		0.00	1.00	
SBCP	スリムビルドコーナー75, チビクリCK(化粧柱の場合)		0.65	1.00	
SBCP	は	スリムビルドコーナー75	1.00	1.00	
ARCG	に	アレントコーナー合板用	1.40	2.20	
ARCG	ほ	アレントコーナー合板用	1.60	2.20	
ARCG	へ	アレントコーナー合板用	1.80	2.20	
HD15	と	ブレイブホールダウン B-HD15	2.80	3.60	
HD20	ち	ブレイブホールダウン B-HD20	3.70	4.70	
HD25	り	ブレイブホールダウン B-HD25	4.70	4.80	
HD30	ぬ	ブレイブホールダウン B-HD30	5.60	7.20	
J1	る	腰掛け蟻若しくは大入れ蟻掛け+羽子板ボルト、短冊金物		1.90	
J2	を	腰掛け蟻若しくは大入れ蟻掛け+羽子板ボルト、短冊金物×2		3.00	

※表示なき金物は「は」とする。

梁継手・仕口用
梁継手・仕口用

接合部凡例				*接合部凡例はユーザ設定されたものです。	
記号	仕様（タナカ金物）		N	倍率	
FCP	フックコーナー, チビクリCK(化粧柱の場合)		0.00	1.00	
FCP	フックコーナー, チビクリCK(化粧柱の場合)		0.65	1.00	
FCP	は	フックコーナー	1.00	1.00	
CCP	に	シナコーナー	1.40	2.20	
CCP	ほ	シナコーナー	1.60	2.20	
CCP	へ	シナコーナー	1.80	2.20	
HD15	と	ビス止めホールダウンU HD15	2.80	3.60	
HD20	ち	ビス止めホールダウンU HD20	3.70	4.70	
HD25	り	ビス止めホールダウンU HD25	4.70	4.80	
HD30	ぬ	ビス止めホールダウンU HD15×2 (HD35)	5.60	7.20	
J1	る	腰掛け蟻若しくは大入れ蟻掛け+羽子板ボルト、短冊金物		1.90	
J2	を	腰掛け蟻若しくは大入れ蟻掛け+羽子板ボルト、短冊金物×2		3.00	

※表示なき金物は「は」とする。

梁継手・仕口用
梁継手・仕口用

筋かいの種類に応じた筋かいの端部の接合部の仕様		
	筋かいの種類	接合部の仕様（構造方法）
イ	鉄筋φ9	柱又は横架材を貫通し、三角座金を介してナット締め、又は鋼板添え板を用い鋼板を柱及び横架材にCN90, 8本平打ち
ロ	筋かい:15×90	柱・横架材を欠き込み、柱・横架材双方に対してN65, 5本平打ち
ハ	筋かい:30×90	鋼板添え板t=1.6mmを筋かいに対してボルトφ12及びCN65, 3本平打ち、柱に対してCN65, 3本平打ち、横架材に対してCN65, 4本平打ち。筋かいプレートBP同等品
ニ	筋かい:45×90	鋼板添え板t=2.3mmを筋かいに対してボルトφ12及びスクリュー釘φ4.5L50, 7本平打ち、柱及び横架材に対してスクリュー釘φ4.5L50, 5本平打ち。筋かいプレートBP-2同等品
ホ	筋かい:90×90	柱又は横架材にボルトφ12mmを用いて一面剪断接合

胴差と通し柱の接合部の仕様		
	胴差と通し柱の条件	仕口
T1	通し柱の片側に胴差が来る場合	胴差を柱にかたぎ大入れ短ほぞ差しの上、羽子板ボルト、かね折り金物又は同等以上の仕口
T2	通し柱の両側に胴差が来る場合	胴差を柱にかたぎ大入れ短ほぞ差しの上、短冊金物又は、同等以上の仕口で胴差相互を緊結
T3	通し柱と胴差の接合部の近くに90×90以上の筋かいが来る場合(通し柱が建物の出隅にあるか、筋かい壁が外壁と直交して接する場合)	胴差を通し柱に、15KN用引き寄せ金物を水平に用いて緊結

決定図