
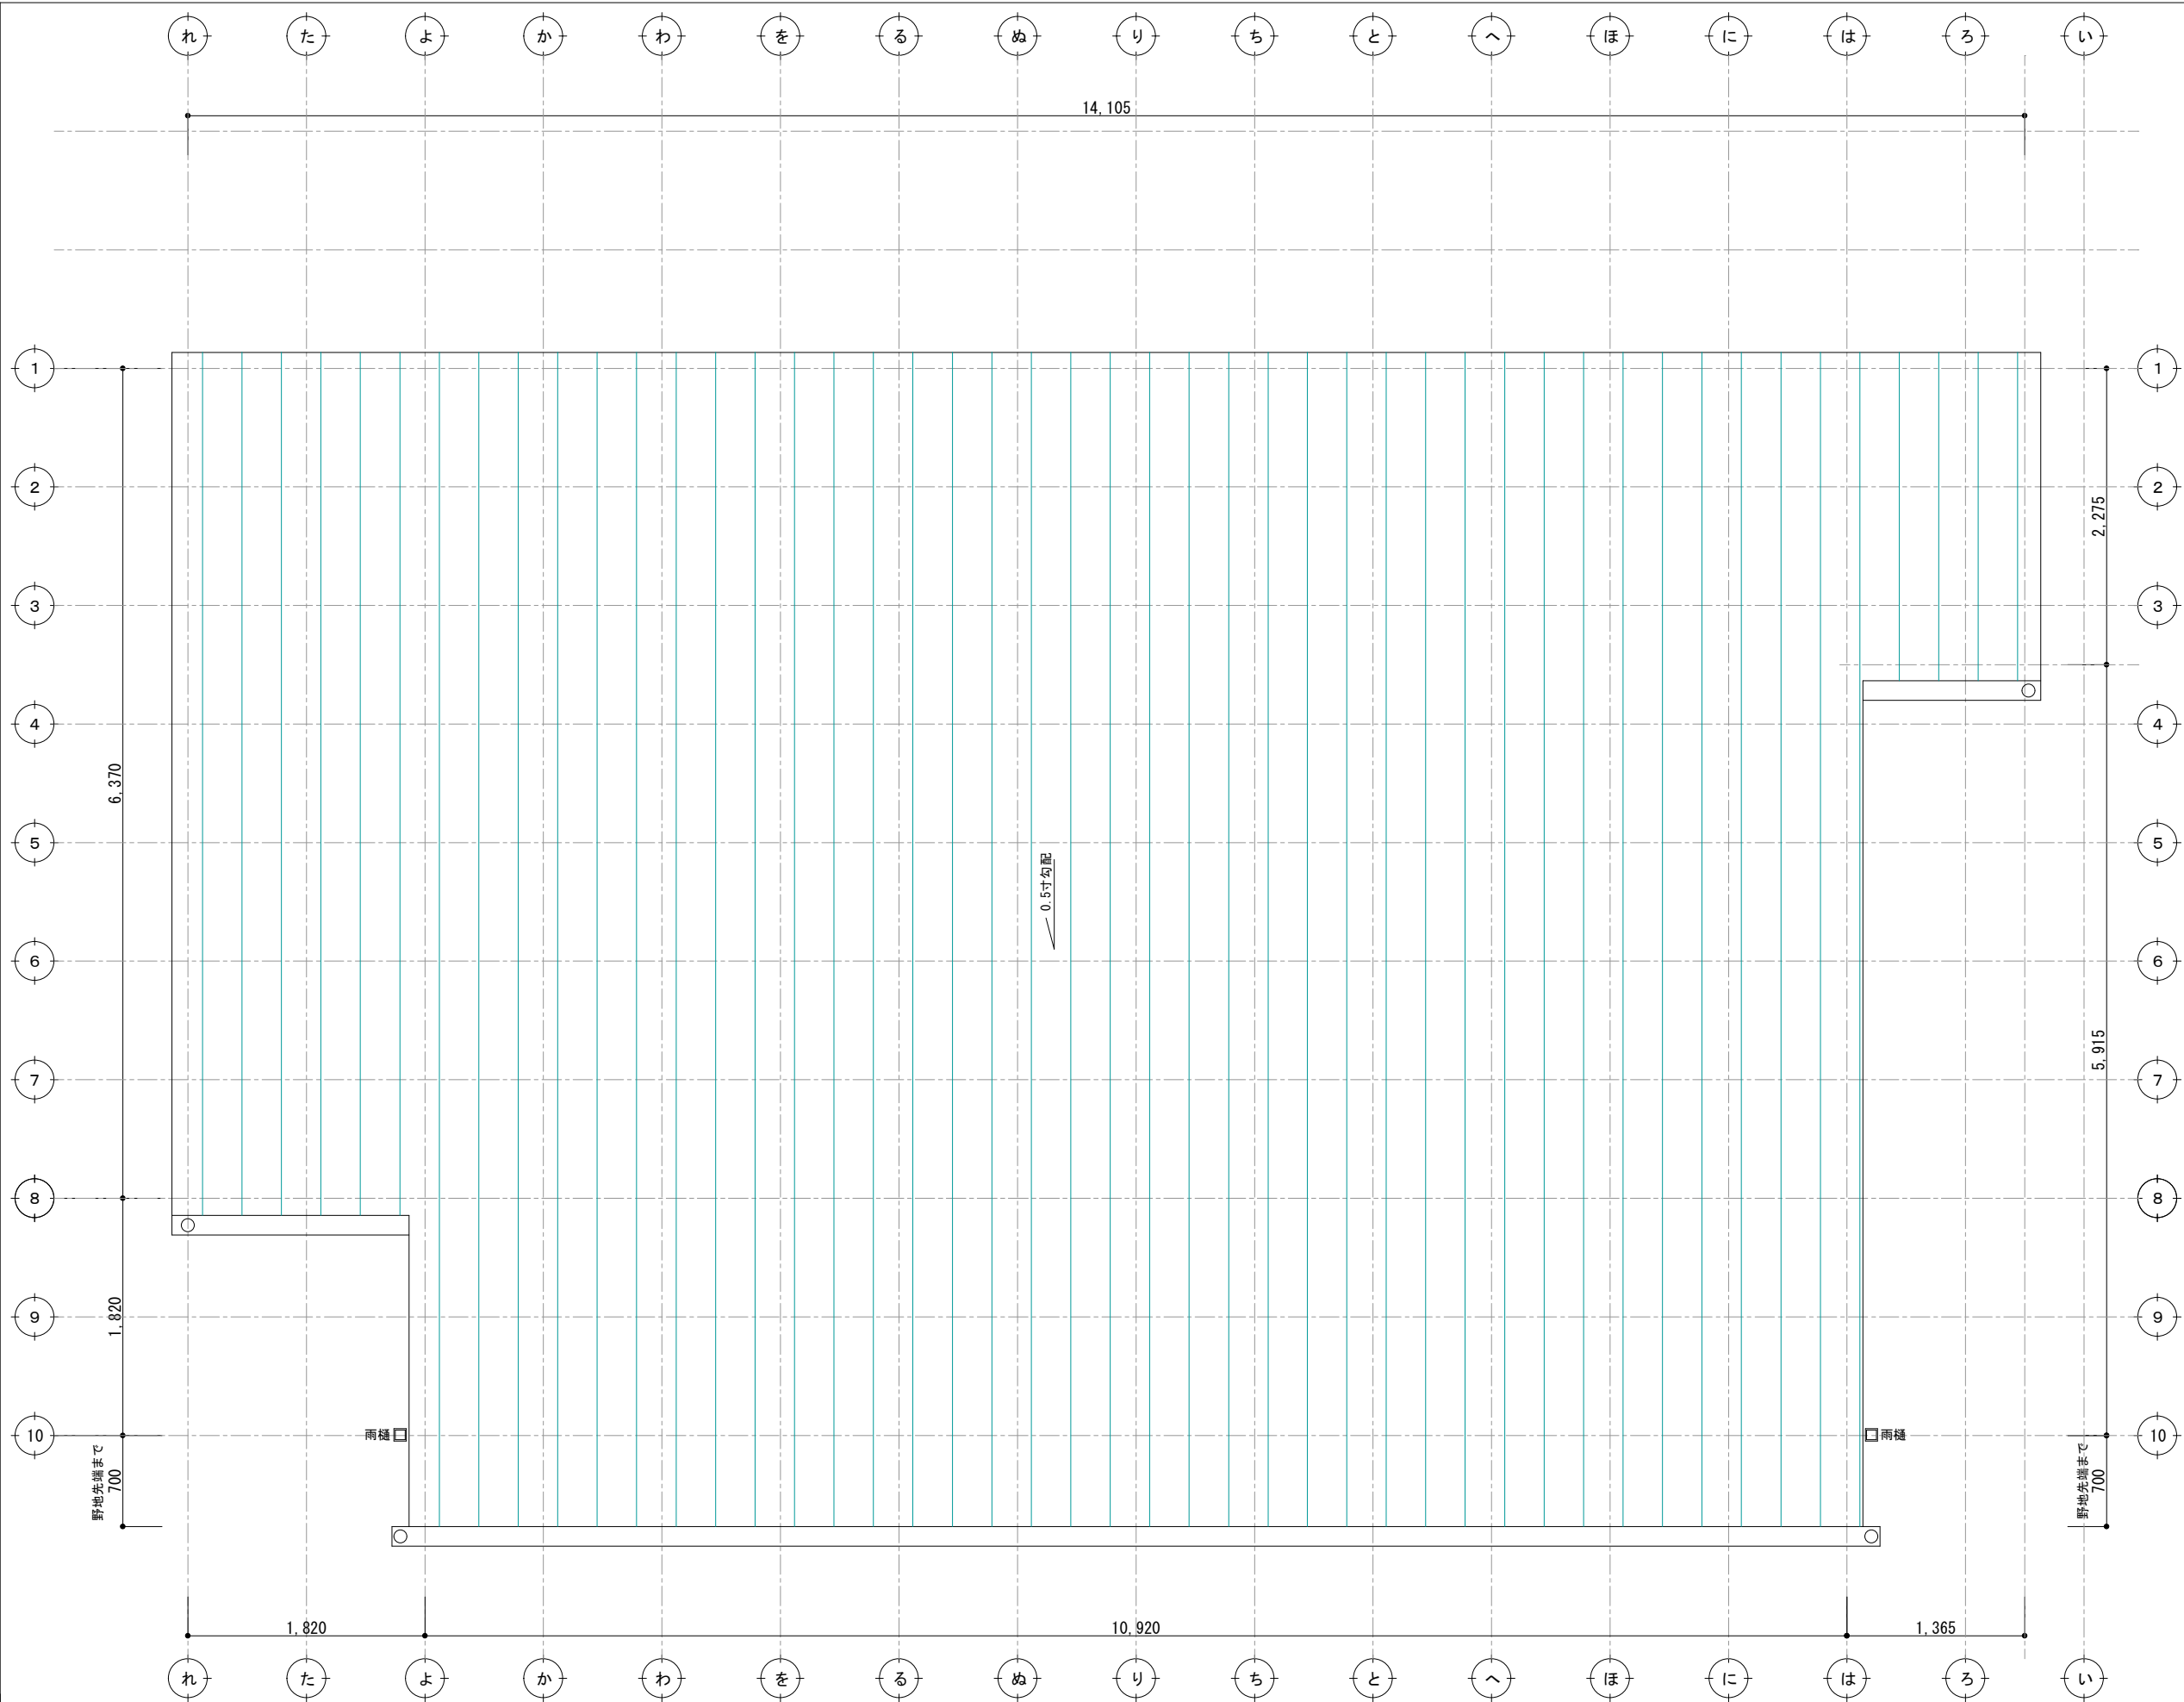


GX住宅
(Cube J付)
太陽光あり

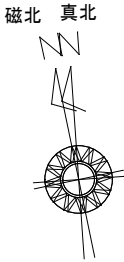

決定図

訂 正	浜 岡 一 級 総 合 設 計 事 務 所 一級建築士事務所 静岡県知事登録第 (10)2441 号 一級建築士 大臣登録第 365879 号 西原利昌		株式会社 LIFEFUND InDesign office 一級建築士事務所 事務所登録 (2) 第7595号 一級建築士登録 第179770号 鈴木 達男 〒432-8023 静岡県浜松市中央区鴨江3丁目70番23号	年 月 日	件 名	設計	IC	工事	図 番
				2025. 7. 11	南頼伸様・日香梨様邸 新築工事				
				縮 尺	図 名				
				1/100	屋根伏図	酒井		青島	