
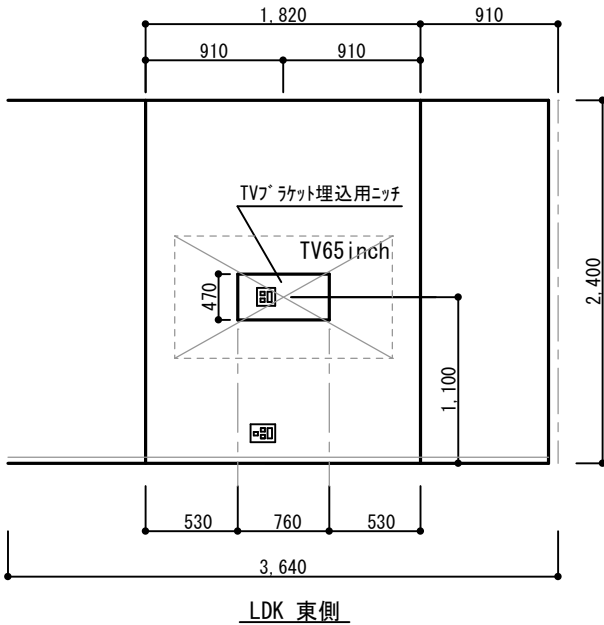
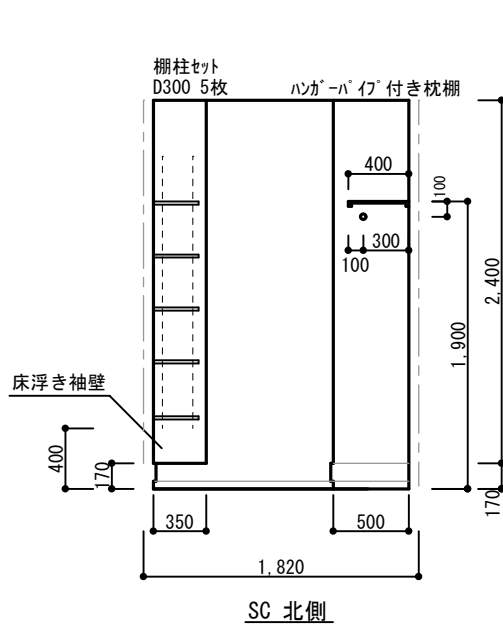


LDK 東側 断面図 (1/30)

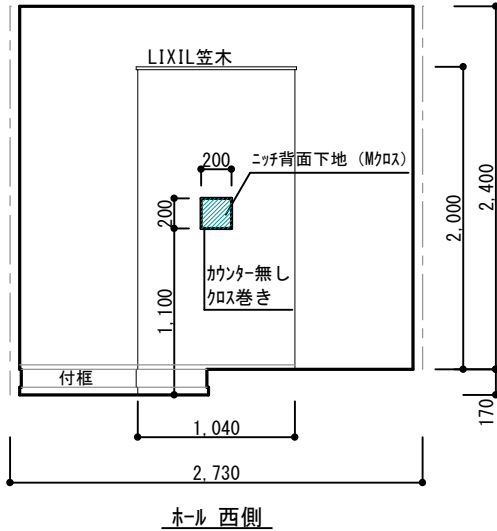

決定図

訂正	浜岡一級総合設計事務所 一級建築士事務所 静岡県知事登録第 (10)2441 号 一級建築士 大臣登録第 365879 号 西原利昌	LIFEFUND PG HOUSE	株式会社 LIFEFUND InDesign office 一級建築士事務所 事務所登録 (2)第7595号 一級建築士登録 第179770号 鈴木 達男 〒432-8023 静岡県浜松市中央区鴨江3丁目70番23号	年月日 2025. 7. 11	件名 南頼伸様・日香梨様 新築工事		設計	IC	工事	図番
				縮尺 1/50	図名 展開図-1		酒井		青島	6-1