



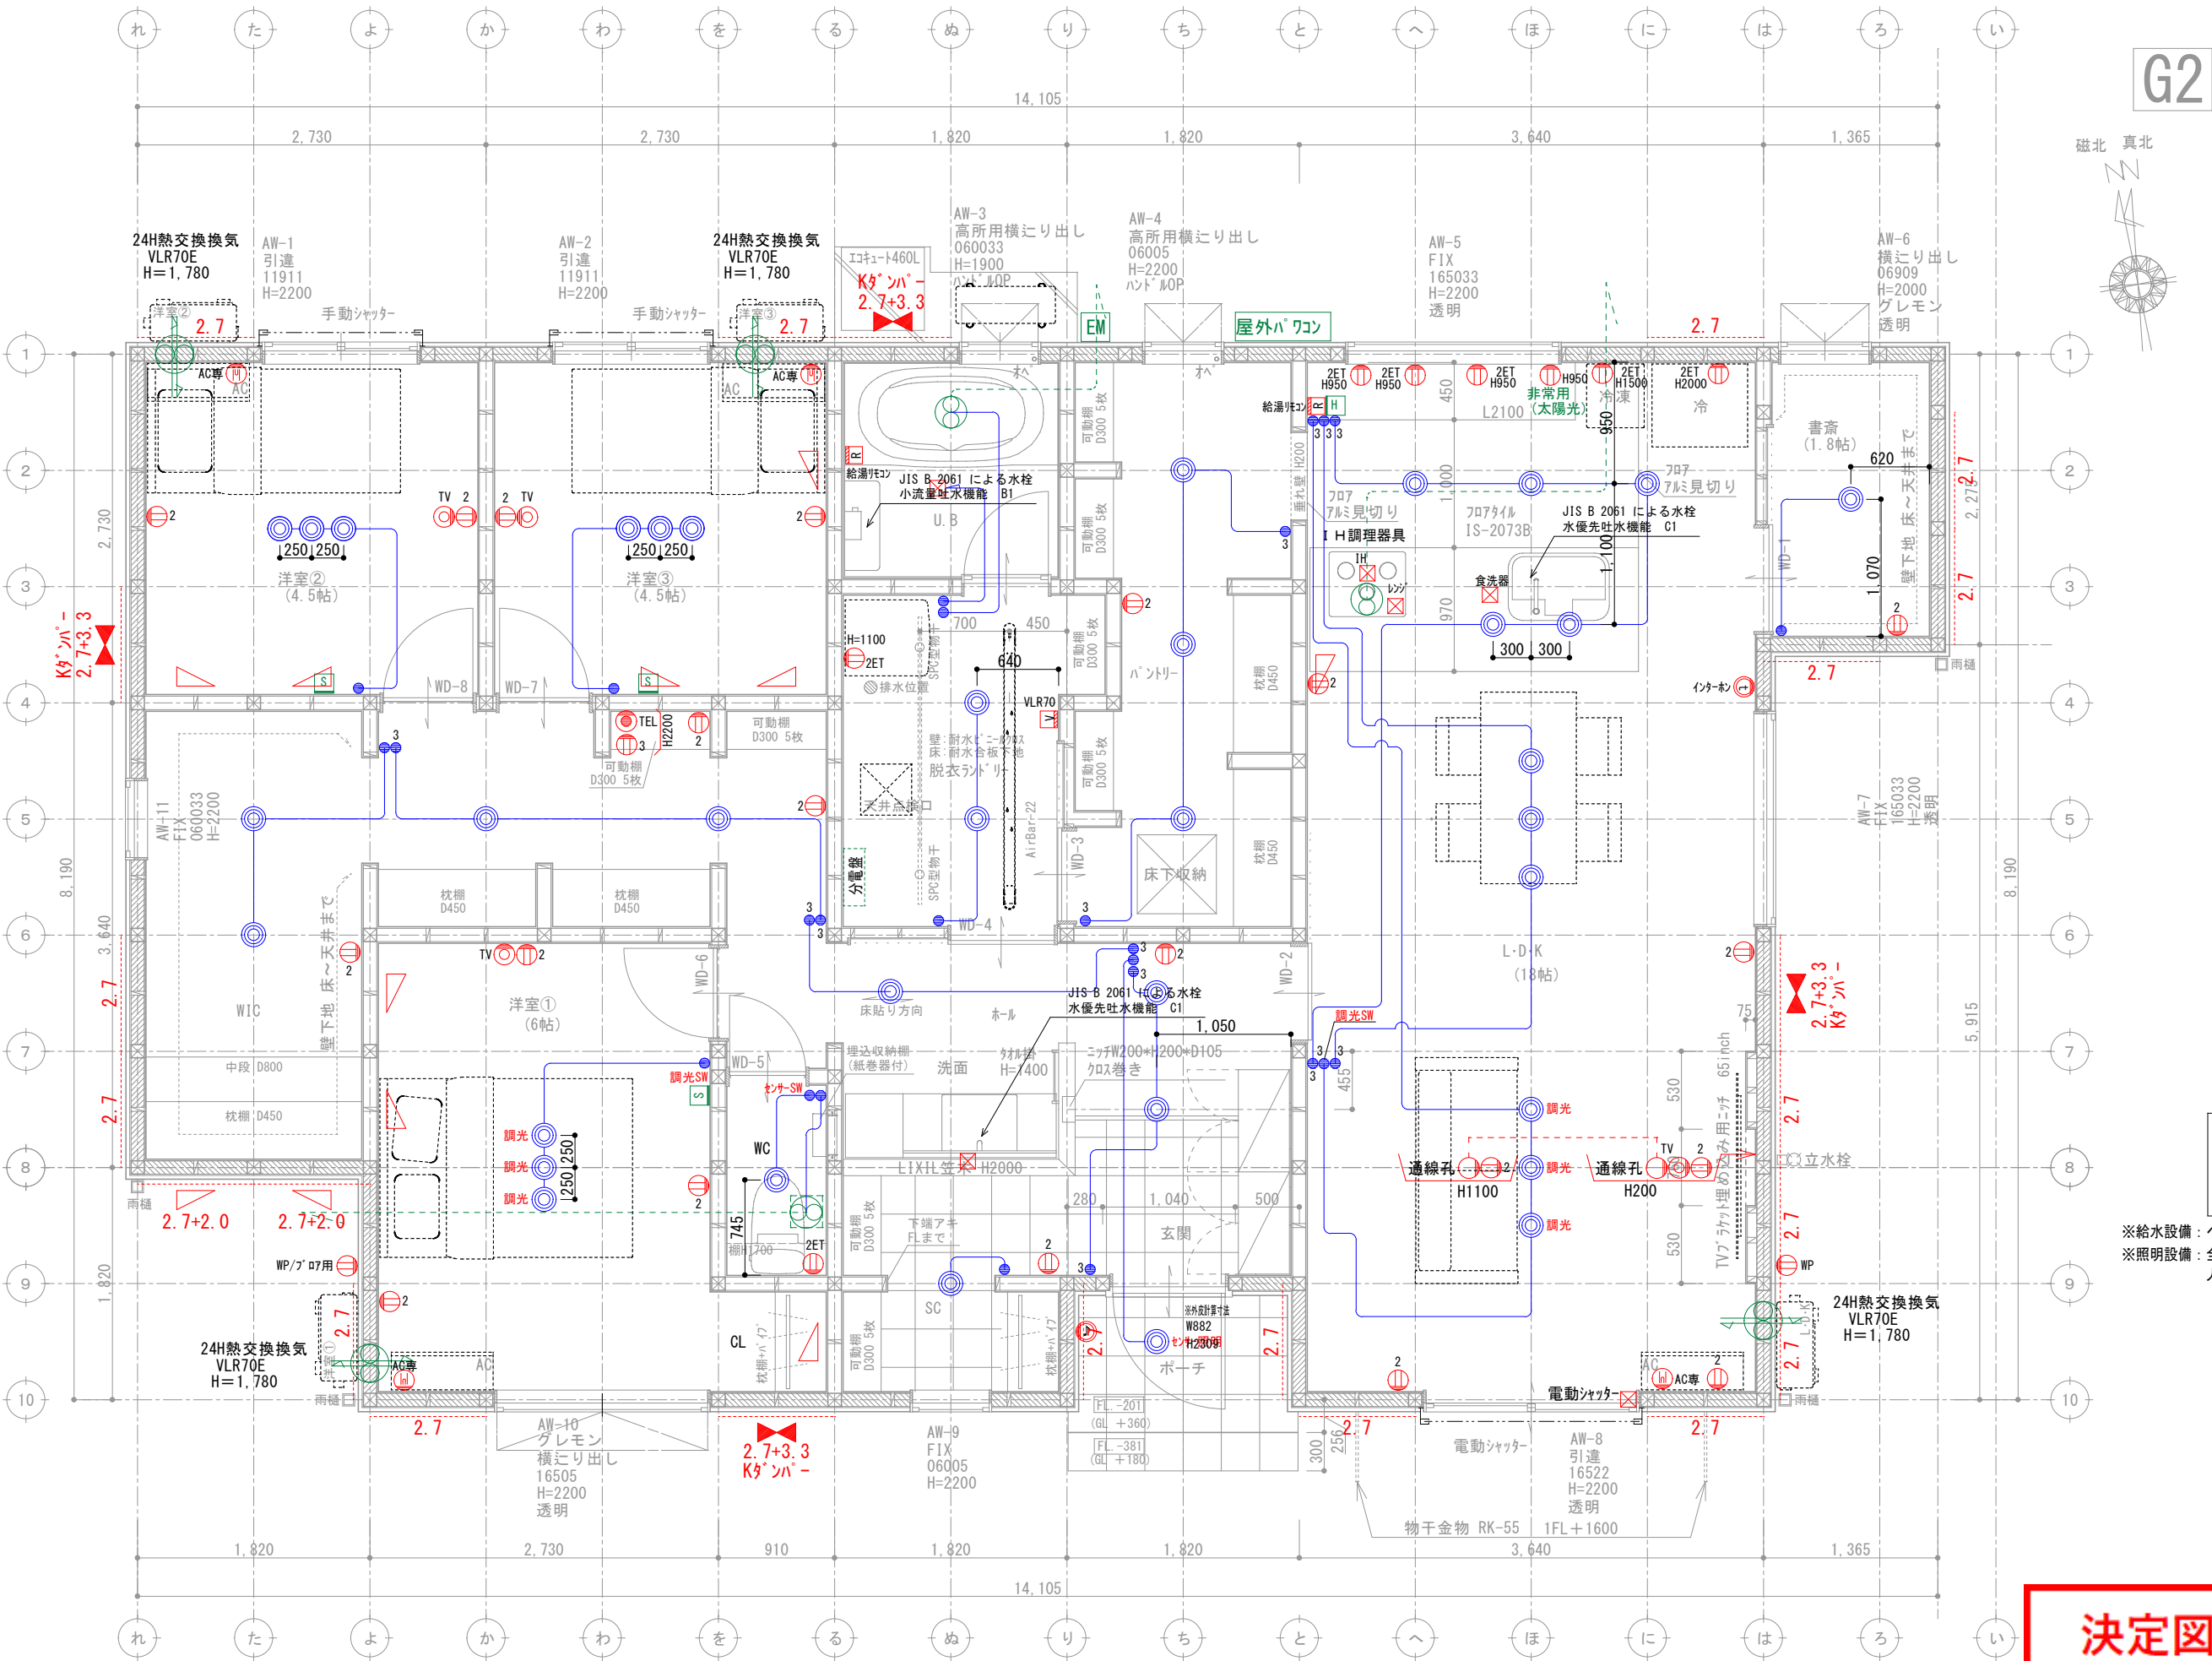

G2

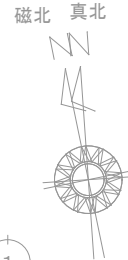

壁付け 住宅用火災報知器			数量
H	熱感知器	電池式(単独型)	1
	露出型		
壁付け 住宅用火災報知器			数量
S	煙感知器	電池式(単独型)	3
	露出型		

※ 煙感知器は壁・梁より600mm以上離す
壁に取付ける場合、
天井から150mm以上500mm以内離す
換気扇・エアコン吹出口から1500mm以上離す
※ 全室LED照明とする。
※ 標準天井高さ2,400
※ 特記無きガラスは型ガラス

- * 凡例**
- 管柱 (105×105)
 - Kタンパー (3.30倍 FRM-0641)
 - 片筋違い (2.00倍 45×90)
(例 左:柱脚 右:柱頭)
 - たすき掛筋違い (4.00倍 45×90)
 - 構造用合板 (2.70倍)
(t=9 タタキ EXハイパー)
(標準仕様 2.7倍: FRM-0678)
(入隅仕様 2.7倍: FRM-0734)
 - 床点検口
 - 天井点検口
 - 換気扇
 - 熱交換換気扇 VLR-70

脱衣ランドリー 仕上材
天井: ア9.5PB下地ビニルクロス貼り
壁: ア12.5PB下地ビニルクロス貼り
床: ア24+15耐水合板下地77タイル張り

※給水設備: ヘッダー分岐後の全配管径は13mm以下とする
※照明設備: 全室LED照明とし居室においては調光制御、非居室においては
人感センサーを使用する

- ① 3 コンセント 3ヶ所
- ② 1ET コンセント1ヶ所接地ターミナル付
- ③ 2ET コンセント2ヶ所接地ターミナル付
- ④ WP コンセント 防水型
- ⑤ エアコン用コンセント
- ⑥ 200V用コンセント
- ⑦ WP 防雨入線プレート
- ⑧ スイッチ
- ⑨ 3路スイッチ
- ⑩ 4路スイッチ
- ⑪ 直結電源
- ⑫ TV テレビ取出口
- ⑬ TEL 電話取出口 (テレホンガイド)
- ⑭ LAN LAN取出口 (テレホンガイド)
- ⑮ 壁照明
- ⑯ リモコン (給湯関係・ルフロ)
- ⑰ メーター
- ⑱ 分電盤
- ⑲ チャイム

※ACコンセント天井付け
※TVアンテナ工事
※スイッチはFL+1100、コンセントはFL+200

決定図