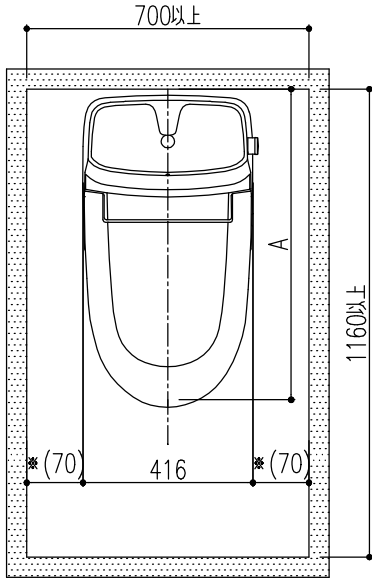
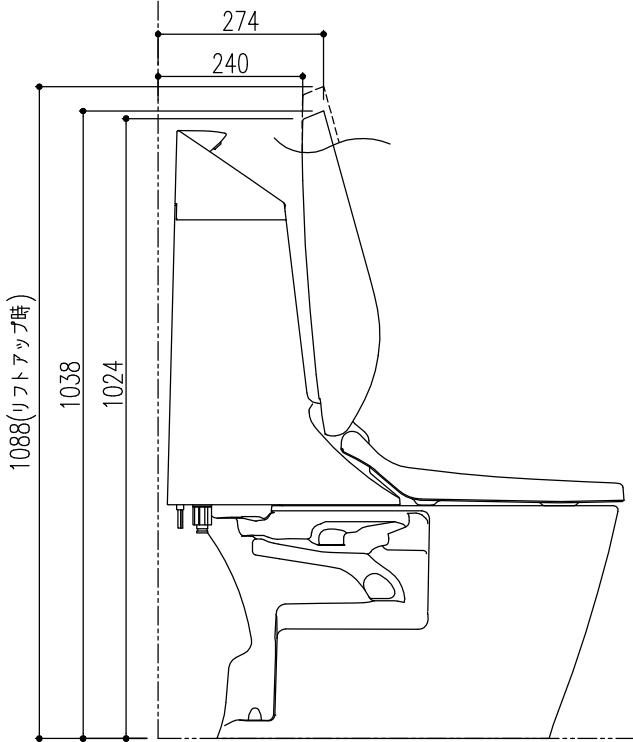


●キャビネット 施工要領図				●TSF-211U 施工完了図					
壁取付キャビネット取付部材の固定強度については十分配慮を行っておりますが、壁面の構造についても配慮いただくことが不可欠です。 ●ボード類直張り ●ボード類胴縁取付け ●タイル仕上げ ●モルタル仕上げ ●タイル仕上げ ※壁本体がコンクリートブロックの場合は、中空部はモルタル詰めしてください。				注意：施工にはボンドコークなどの壁クロス補修用のコーキング剤が必要です。 壁開口 311±2 308 200 壁開口深さ 70mm以上 △WL 4-Ø4.5×38 334 119 70 35 18 202 507 727 (800) FL 4-Ø4×40 35 28 167 55 377 壁開口 485±2 53 88 ※（ ）内は、参考寸法です。					
●便器床設置面寸法・固定穴寸法				●給排水の位置決めと取出し		●排水塩ビ管の接続			
△WL 646 549 180 160 578 320 80 床設置面(注1) ※注1:破線は±5%許容差範囲				給水管、排水管を取り出します。 ※ 給水管、排水管を施工寸法通りに取り出します。 誤って排水管を壁寄りに取り出した場合は、タンクと壁が干渉して施工できない恐れがあります。 給水Rc1/2 (壁給水の場合) 280±10 150±10 200±10 280±10 排水管 (VP100. VU100. VP75. VU75のいずれか) 給水Rc1/2 (床給水の場合) 100±10		※ 接続は、塩ビ接着剤にて確実に行なって下さい。 ※ 排水管の立ち上げ高さは、必ず60±5mmの位置で切断してください。 施工方法詳細の動画を以下から読み取ることができます。 ・ 通信料はお客様のご負担となります。 ・ お使いの環境・端末によっては、閲覧できない場合があります。 ・ 実物と動画のデザインが異なる場合があります。 ・ 動画内に表示される商品名と品番・デザインが異なる場合がありますが、施工手順に影響ありません。 △WL 60±5 200 VP100,VU100 VP75,VU75 ※注…立ち上げ寸法が60mm以下の場合は 既設配管に合った、市販の60mm立ち上げ用部材(持ち出しニップル)を別途手配ください。 ※注…防振シートを組み合わせる場合は5mm高くしてください。 			
	特記事項	物件名	南頼伸 様邸		案件No.	図面名	担当	図面	図番
		仕様	ベアシアシャワートイレノECO5 床排水 一般地		A2504DDD0EJ5AG	機能図	栗野 友仁		株式会社 LIXIL
					見積No.	縮尺	日付		
					M25047203833-003-5		2025.06.23		

●取付最小スペース		●便フタ開時寸法							
※ 最小スペースはA寸法(前出寸法) + 400となり、便器排水方向や既設配管により、異なります。 A寸法は、床排水・床上排水(後抜き)の場合760mm、床上排水(横抜き)の場合860mmとなります。 ご確認ください。 ※ 右図の空間寸法は、衣服の着脱などの行為に必要な最低寸法です。 手すりや紙巻器などの機器を併設する場合は、必要に応じた広い空間が必要になります。 ※ 便器に向かって左右共に70mm以上の空間を確保してください。 		 ※ 上図は代表商品のイメージ図です。 ※ 防振シートを組み合わせる場合は、全体が5mm高くなります。							
	特記事項	物件名	南頼伸 様邸	案件No.	図面名	担当	図面	図番	
				A2504DDD0EJ5AG	機能図	栗野 友仁		株式会社 LIXIL	
		仕様	ベーシアシャワートイレノECO5 床排水 一般地	見積No.	縮尺	日付			
				M25047203833-003-5		2025.06.23			