



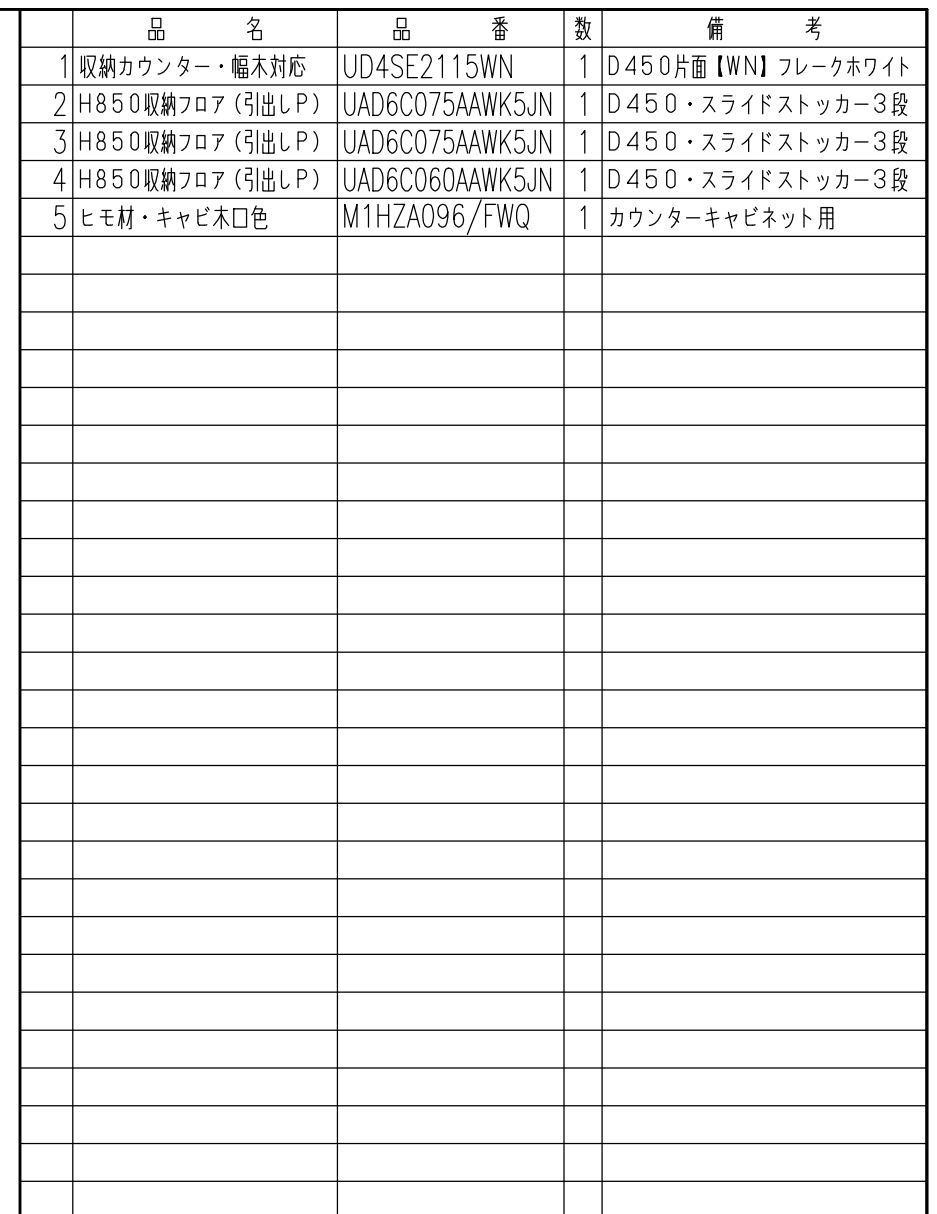


特記事項 扉色 WK5:ホワイトスタッコ 取手 [J]スリム取手(シルバー)	物件名	南頼伸 様邸	案件No.	図面名	担当	図面	図番 : 株式会社 LIXIL
			A2504DDD0EJ5AG	レイアウト図	栗野 友仁		
	仕様	ES21	見積No.	縮尺	日付		
			M25047203833-003-3	1/30	2025.06.23		

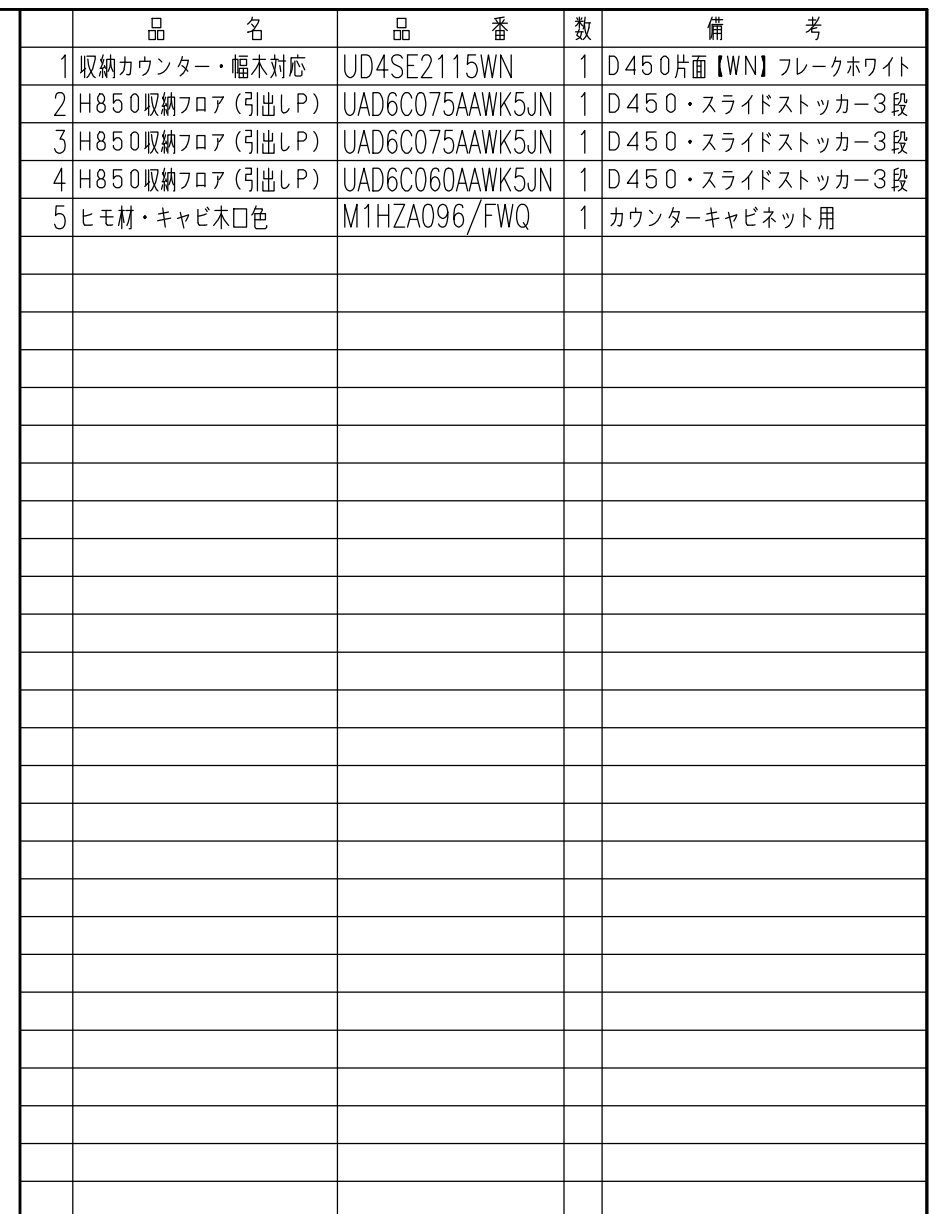

特記事項 扉色 WK5:ホワイトスタッコ 取手 [J]スリム取手(シルバー)	物件名	南頼伸 様邸	案件No.	図面名	担当	図面	図番 : 株式会社 LIXIL
			A2504DDD0EJ5AG	納まり図	栗野 友仁		
	仕様	ES21	見積No.	縮尺	日付		
			M25047203833-003-3	1/30	2025.06.23		

■ 床の不陸に関して

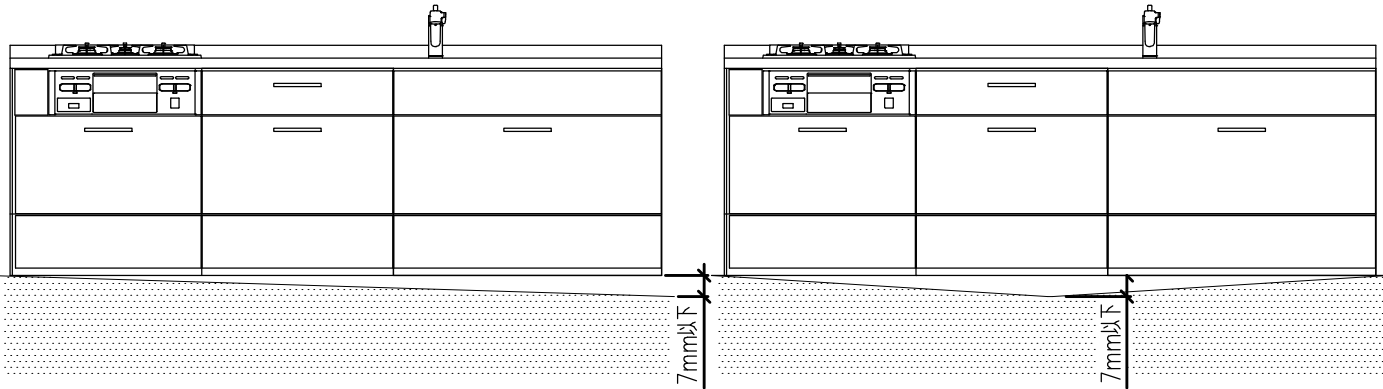

床の不陸は、7mm以下に抑えるようにしてください。不陸が大きい場合は、現場責任者に床の修正を依頼してください。
※キャビネット取付時には不陸調整スペーサー等で水平になるように設置してください。


特記事項 扉色 WK5:ホワイトスタック 取手 [J]スリム取手（シルバー）	物件名	南頼伸 様邸	案件No.	図面名	担当	図面	図番
			A2504DDD0EJ5AG	機能図	栗野 友仁		株式会社 LIXIL
	仕様	ES21	見積No.	縮尺	日付		
			M25047203833-003-3		2025.06.23		

■ キッチン取付者さま向け 動画コンテンツ ■

商品取付けの注意点を２次元コードでご視聴いただけます。
取付日より前に、是非ご確認ください。

荷扱い・搬入


荷扱い・搬入

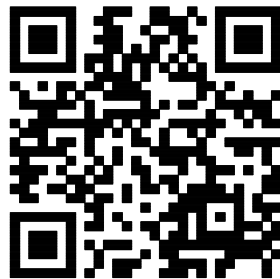

作成日：2024年10月01日



カウンター開梱搬入「養生ツール」

カウンター開梱搬入 「養生ツール」のご紹介

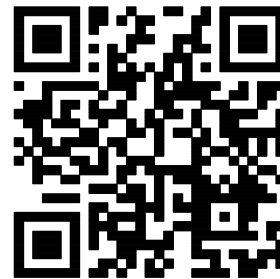

作成日：2024年10月01日

不陸の確認と調整

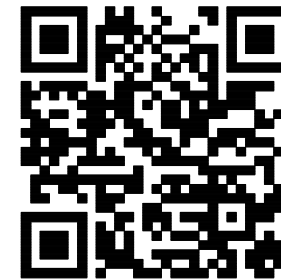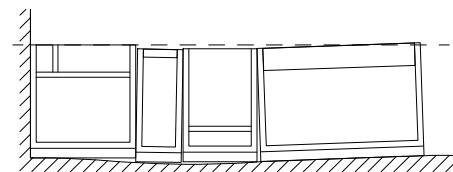

作成日：2024年02月07日



マグネットキッチンパネル

マグネット キッチンパネル 「取付・設置」ポイント





作成日：2024年03月06日

人造大理石カウンターL型キッチン

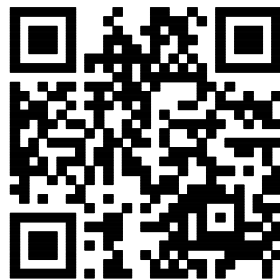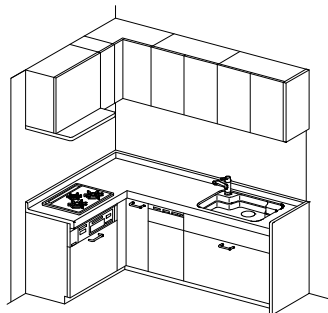

作成日：2024年02月07日

センターキッチン（ペニンシュラ型）

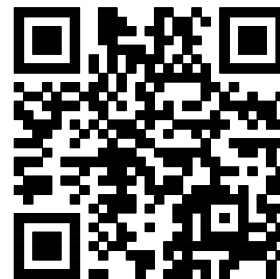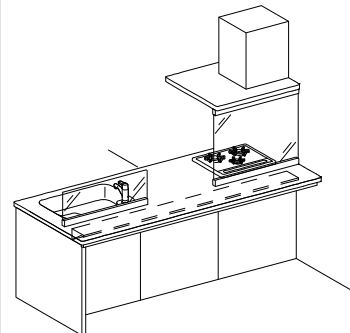

作成日：2024年02月07日

特記事項	
扉色	WK5:ホワイトスタッコ
取手	[J]スリム取手(シルバー)

物件名	仕様
-----	----

南頼伸 様邸

ES21

案件No.

A2504DDDD0EJ5AG

見積No.

M25047203833-003-3

图面名

機能図

担当

栗野 友仁

面図

図番：

--	--




株元

INDEX

株式会社 LIXIL

■ キッチン取付者さま向け 動画コンテンツ ■

商品取付けの注意点を2次元コードでご視聴いただけます。
取付日より前に、是非ご確認ください。

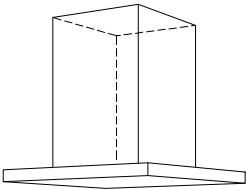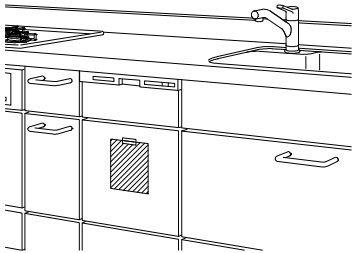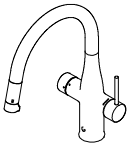センターフード型レンジフード (天吊りフード)  作成日：2024年06月03日 	I H加熱機器関連 I H加熱機器 仕切り板 作成日：2024年02月07日 	食器洗い乾燥機  作成日：2024年02月07日 	ミネラル浄水栓 Greentap  作成日：2024年06月03日 
---	--	--	---

--	--	--	--

--	--	--	--

特記事項 扉色 WK5:ホワイトスタッコ 取手 [J]スリム取手 (シルバー)	物件名	南頼伸 様邸	案件No.	図面名	担当	図面	図番
			A2504DDD0EJ5AG	機能図	栗野 友仁		株式会社 LIXIL
	仕様	ES21	見積No.	縮尺	日付		
			M25047203833-003-3		2025.06.23		