
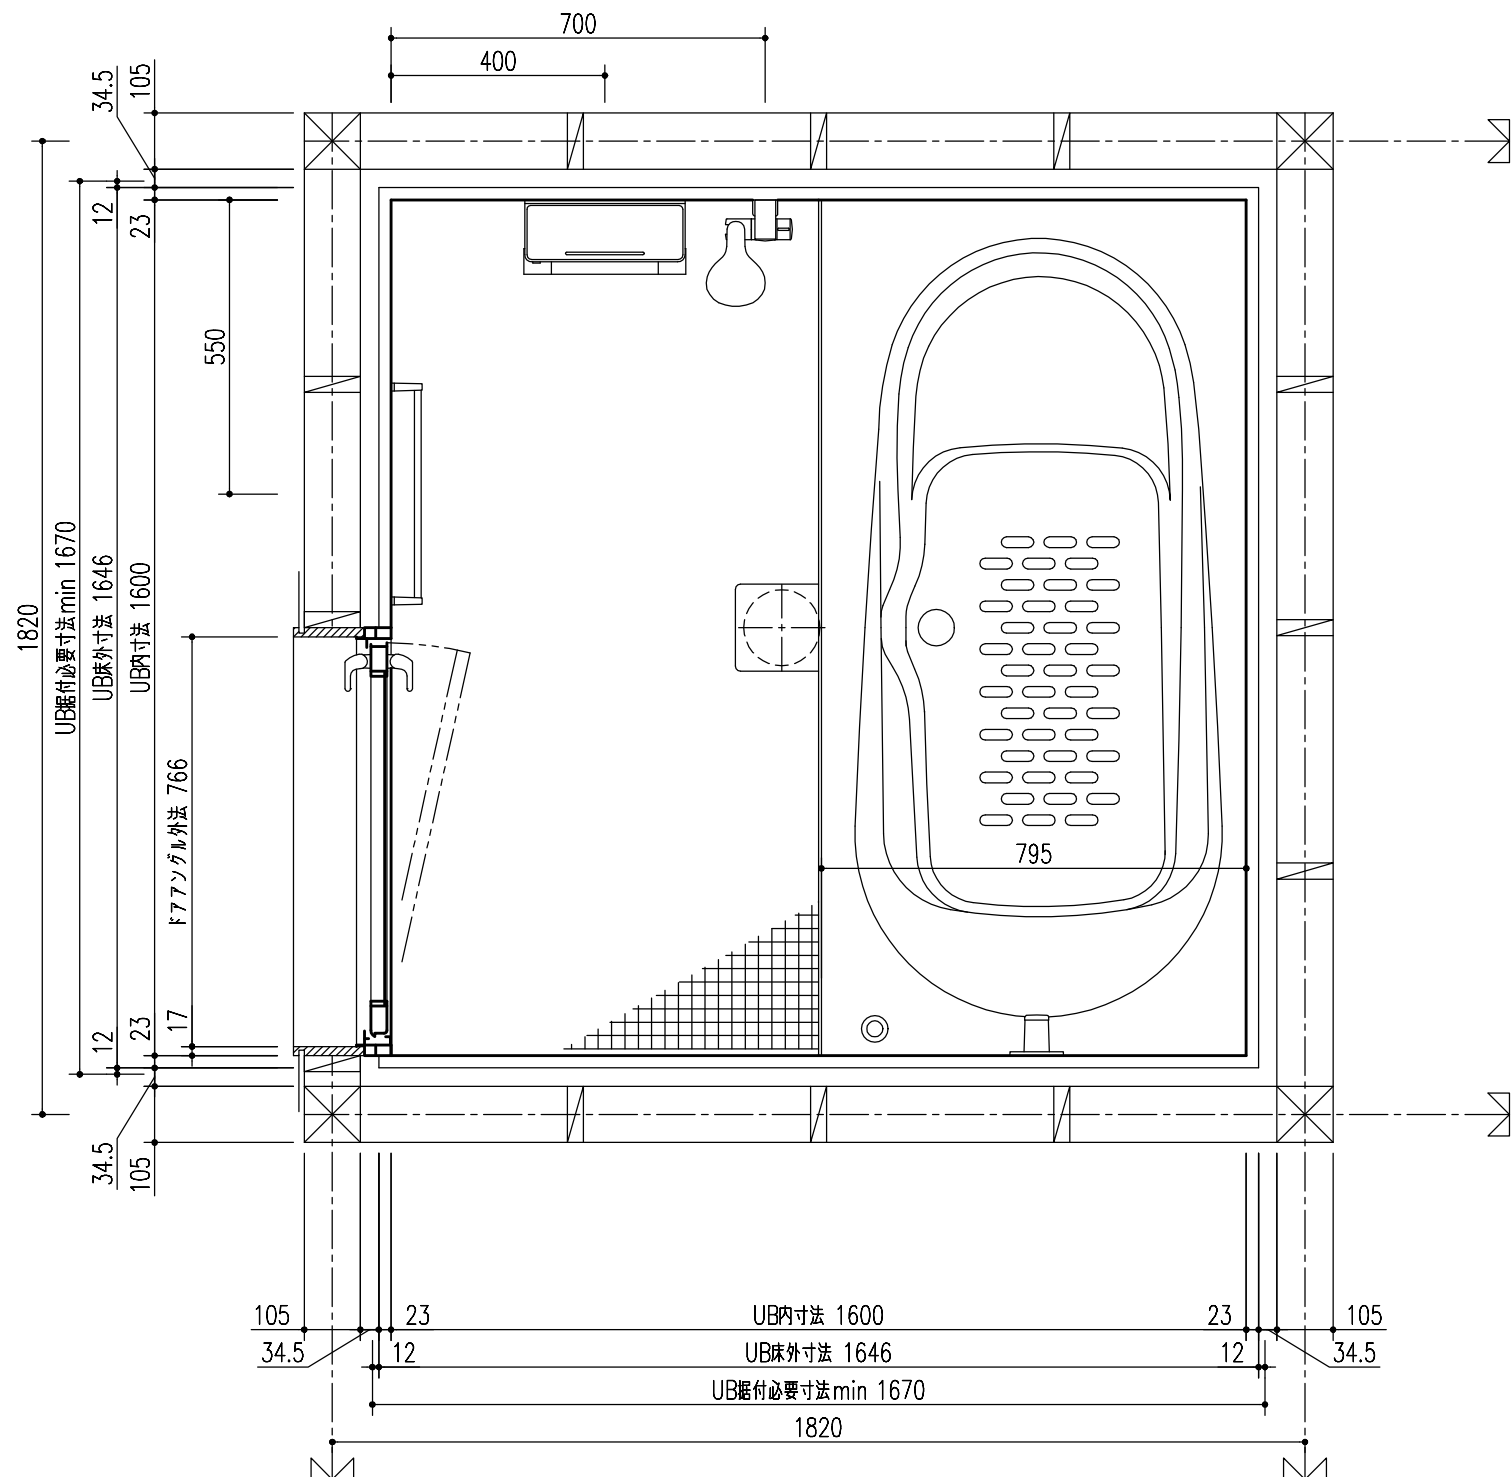
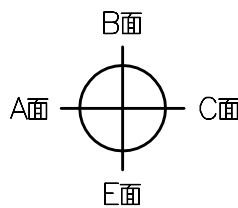


BMUS-1616LBZ-B

[illegible]

天井見上げ図

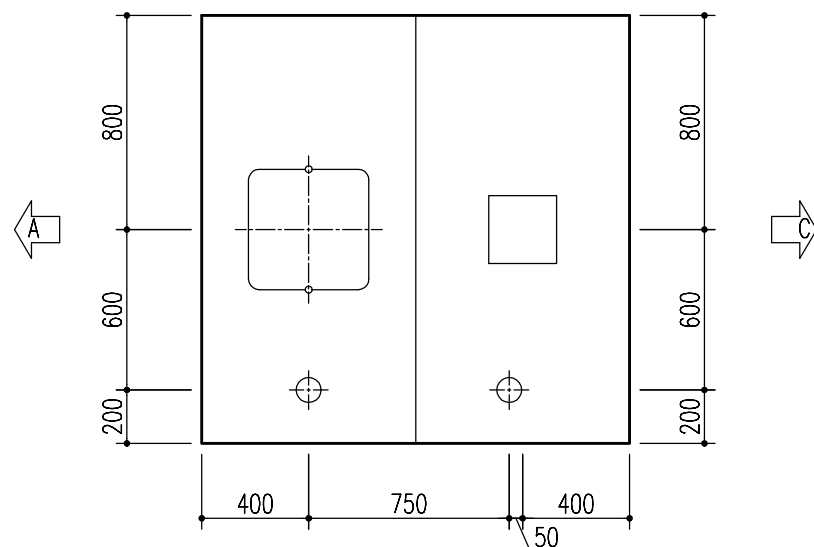





※ UB据付必要寸法はドア部の寸法を含みません。ドア部の寸法は詳細図のドア取合をご確認ください。

※取付ける機器により、UB据付必要寸法は異なります。

詳しくは、カタログの「工務店さまへ（取付け前の確認事項）」をご確認ください。

※プラスオプションの追加マグネットアイテムは仕様図には表示されません。

特記事項	受領印	物件名	南頼伸 様邸	図面	担当	検図	図番
		品名	仕様図 BMUS-1616LBZ-B+H,LC		栗野 友仁		日付 2025.06.23
				縮尺	株式会社 LIXIL		

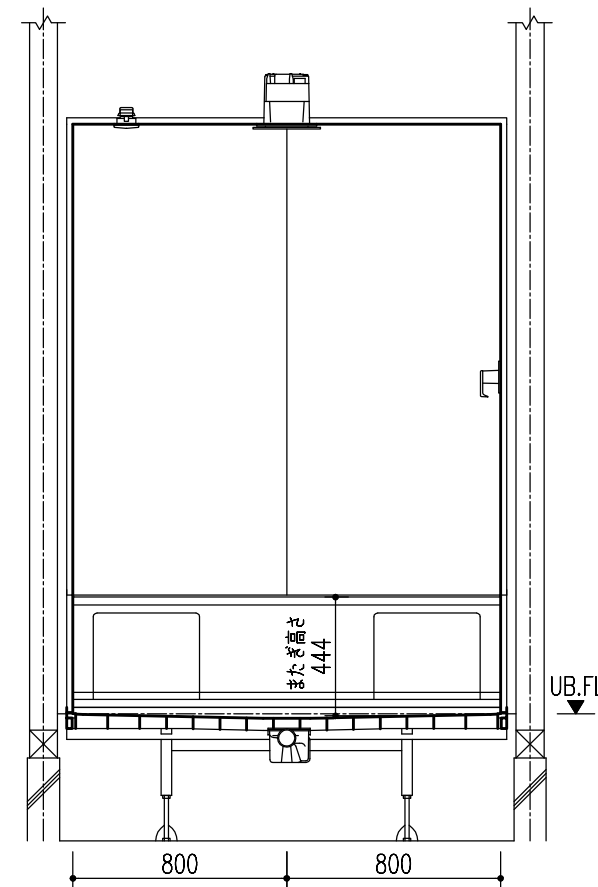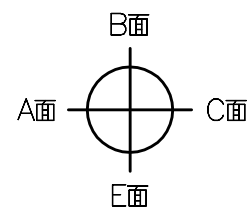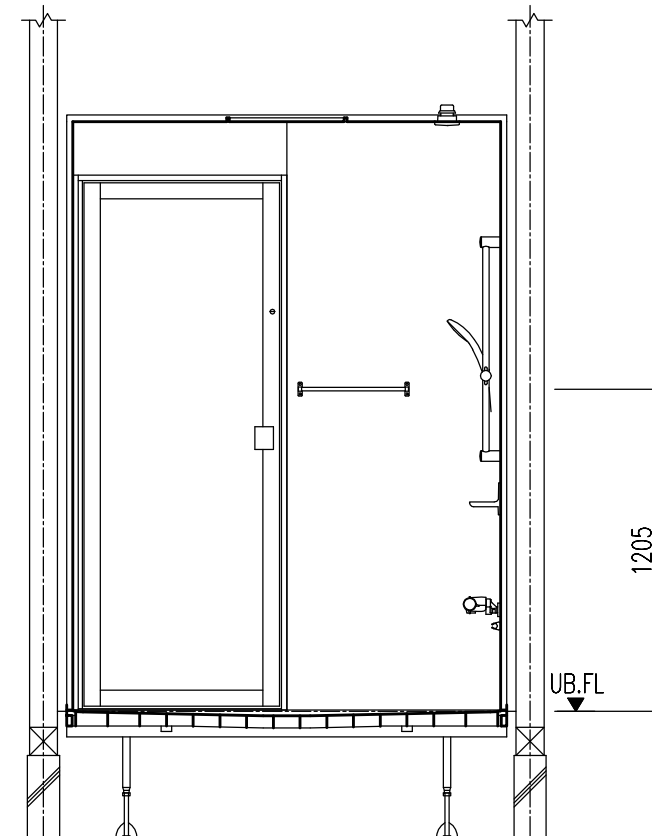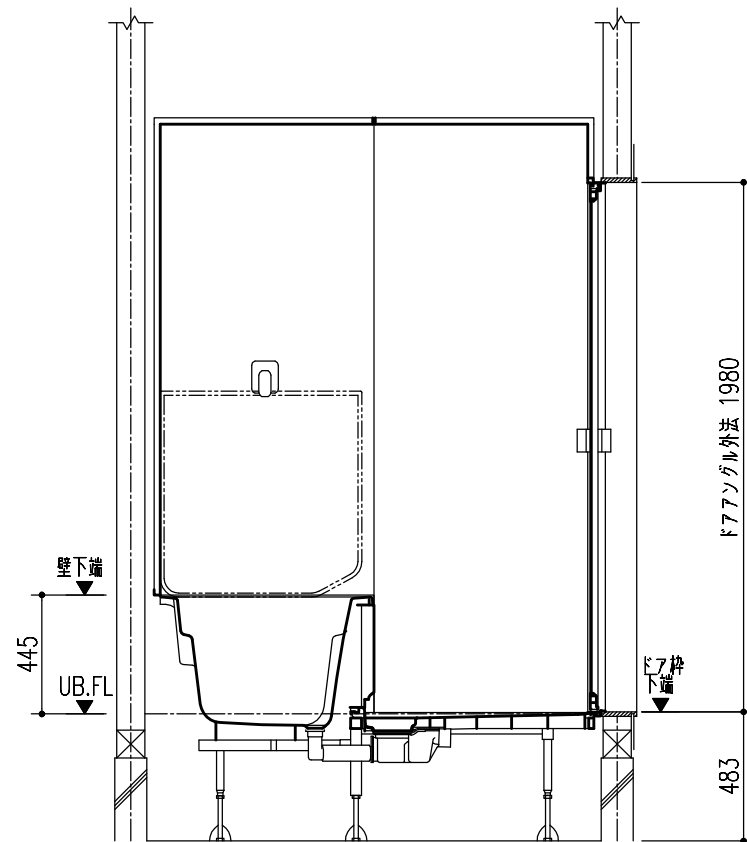

特記事項	受領印	物件名	南頼伸 様邸	図面	担当	検図	図番
		品名	仕様図 BMUS-1616LBZ-B+H,LC		栗野 友仁		日付 2025.06.23
				縮尺	株式会社 LIXIL		

配管接続部詳細図

配管の接続をスムーズに行うためにユニットバス取付前に下記の準備をお願いします。


(1)給水、給湯、排水の一次側は所定の位置に立ち上げておいてください。

(2)排水を脱衣室側(ドア下等)へ抜く場合は、基礎部に開口を設けるか、束構造にして排水管を抜いてください。

シャワーの種類により水栓金具の入口での必要給湯圧力が異なります。詳細はカタログを確認してください。



給水給湯配管立上げ位置

点検口止め

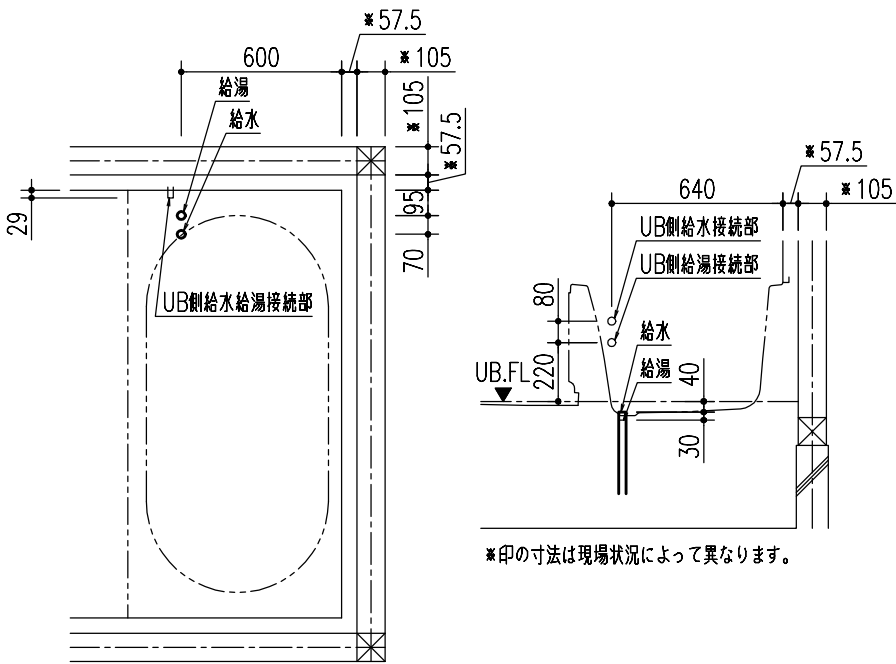

※印の寸法は現場状況によって異なります。

追いだき配管立上位置図

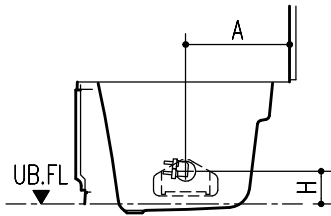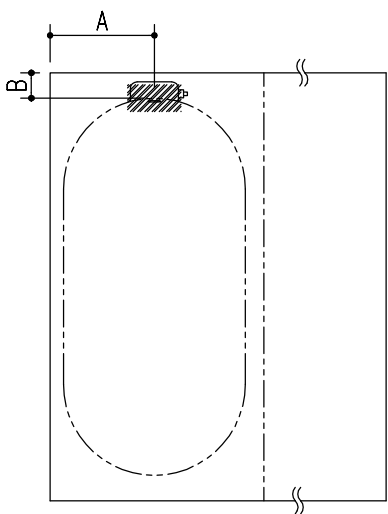



浴槽	A	B	H
ミナモイッド浴槽	506	231	113
1600フィド浴槽	589	247	113
1600ミナモ浴槽	374	231	113
1600エコベンチ浴槽	389	456	103
1600ストレートライン浴槽	369	252	113
1600ロング浴槽	355	194	113
1300ミナモ浴槽	384	132	113
1300ストレートライン浴槽	369	160	113
1200ミナモ浴槽	387	130	113
1150ミナモ浴槽	387	130	113

※図はR勝手の場合です。L勝手の場合は左右反転になります。

※追いだき循環アダプターは現場手配になります。


雑排水管

浴槽側の配管持出し位置・排水管立上位置は専用の配管キット(オプション)を使用した場合の位置です。

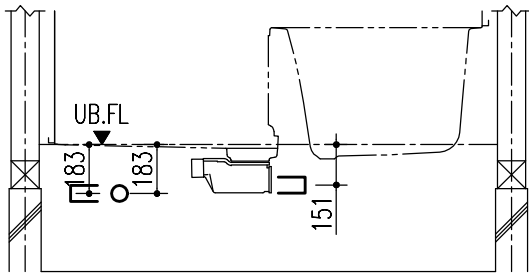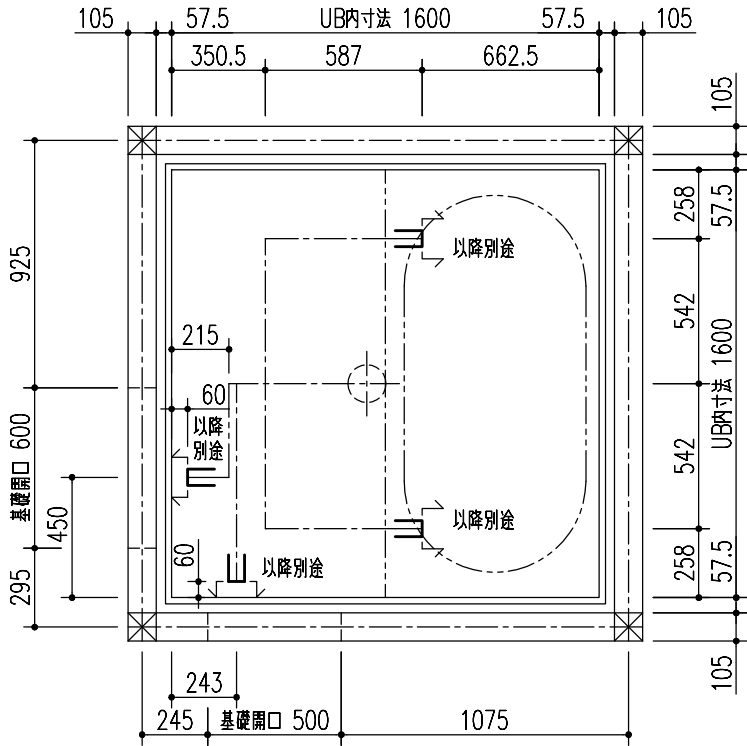

標準持出し位置


給水給湯接続部

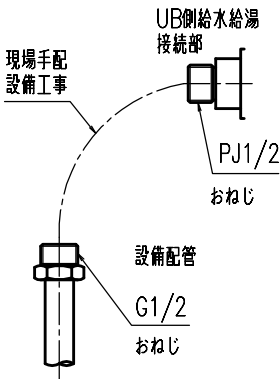


特記事項	受領印	物件名	図面	担当	検図	図番
		南頼伸 様邸		栗野 友仁		日付 2025.06.23
		品名	縮尺	株式会社 LIXIL		
		BMUS-1616LBZ-B+H,LC				
		名				

特記事項	受領印	物件名 南頼伸 様邸	図面	担当	検図	図番	
				栗野 友仁		日付 2025.06.23	
		品名 詳細図 BMUS-1616LBZ-B+H,LC	縮尺	株式会社 LIXIL			

照明

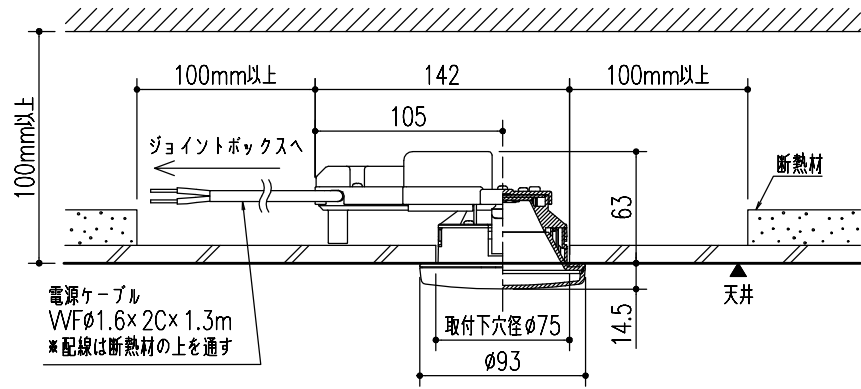




天井設置型照明は室外露出外殻から放熱しております。
その周辺100mmには保温・断熱材などを設置しないでください。
また、断熱材の落下など建築物が接触するおそれがある場合は、
建築側で防止策を講じて下さい。

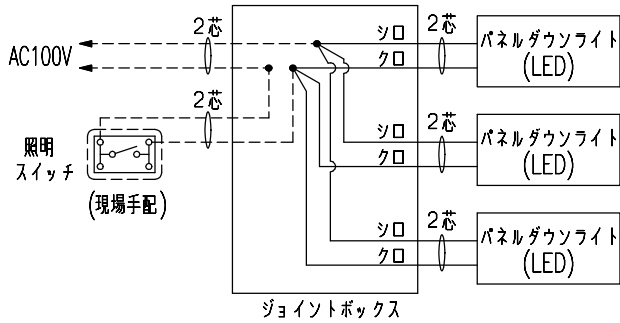

※浴室サイズ等により照明の数は異なります。

- 結線箇所 (電気工事)
- 配線 (現場手配・電気工事)

換気扇

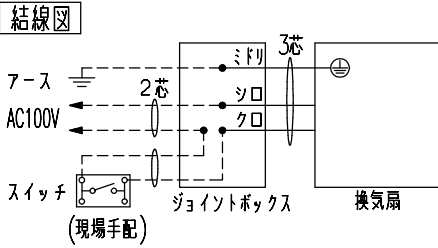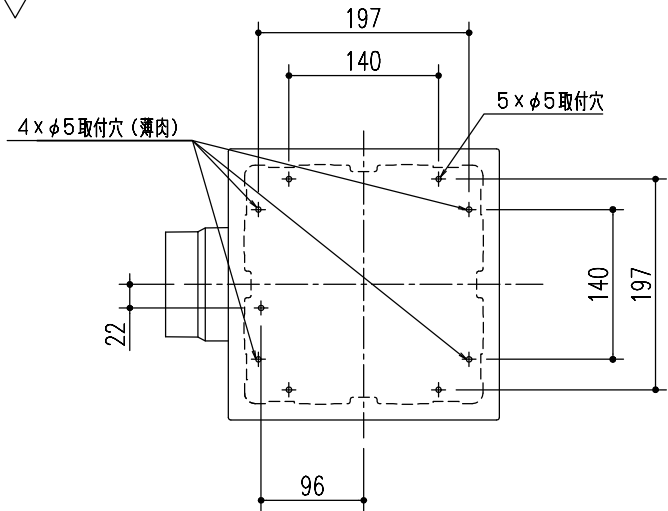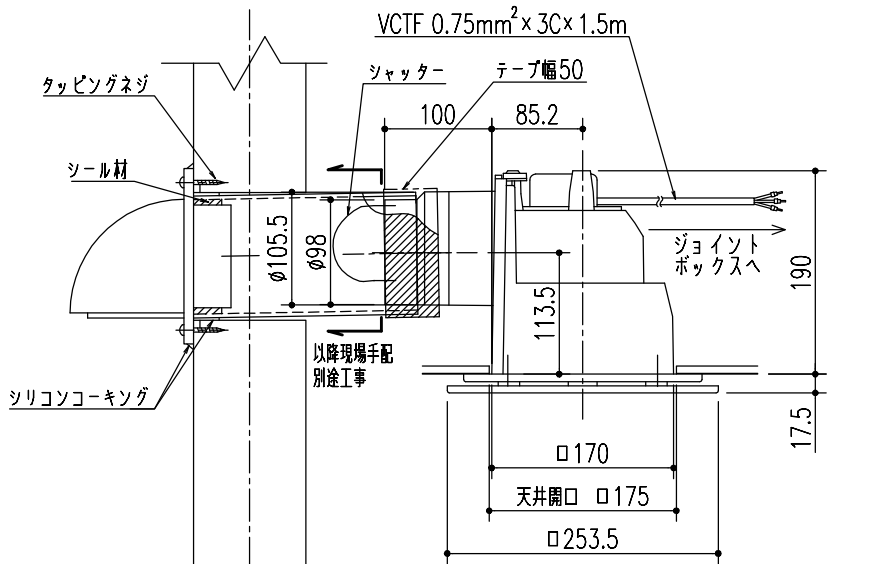


- 結線箇所 (電気工事)
- 配線 (現場手配・電気工事)

注1) 一次側電源線・アース線との結線工事、それ以降の配線工事、スイッチ取付け・結線工事は電気工事業者様の作業範囲となります。

警告
●電気工事は電気設備技術基準、内線規程など関連する法令・規程にしたがって、必ず「電気工事士」が行ってください。
●電線相互の接続は銅線用裸圧着スリーブを用いる等確実に工事してください。絶対に「手より」接続しないでください。
※電気工事が不適切な場合、火災や漏電の恐れがあります。
●電源線など各配線に、以下のことをしないでください。 ※火災、漏電や故障の恐れがあります。
・傷つける、無理に曲げる、無理な力を加える、束ねる、重いものを載せる、挟み込む。
●一次側に必ず漏電遮断器を設置してください。 ※感電する恐れがあります。

特記事項	受領印	物件名	図面	担当	検図	図番
		南頼伸 様邸		栗野 友仁		日付 2025.06.23
		品名	縮尺	株式会社 LIXIL		
		詳細図 BMUS-1616LBZ-B+H,LC				
		名				

< 電氣工事範圍 >

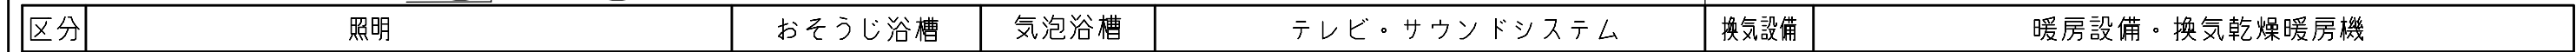


- ※以下のものは、システムバス取付作業に含まれておりません
- ・電線線、アース線の一次側配線工事、D種接地工事、漏電遮断器の調達および設置工事。
- ・各電気機器の電線線およびアース線と一次側配線との接続工事。
- ・脱衣室に設置するスイッチ（別録の表記があるもの）の調達。
- ・脱衣室に設置するスイッチの配線接続および設置工事（別録、付属とも）。

特記事項	受領印	物件名	南頼伸 様邸	図面	担当	検図	図番
各電気機器の詳細については各々のオプション詳細図を参照ください。					栗野 友仁		日付 2025.06.23
		品名	電気機器配線図 BMUS-1616LBZ-B+H,LC	縮尺	株式会社 LIXIL		

排水管接続の注意点
浴槽排水時には最大約1.2L/sの流量が発生します。排水管の経路や、管内の状態によっては正しく排水されない場合があります。設計・取付の際は次の各項目を確認して下さい。


■ダブルトラップ
浴室以降の排水管経路上に、トラップが無いことを確認してください。（ダブルトラップの禁止）
ダブルトラップになっていると、「排水が流れない」「異臭がする（封水切れ）」などの異常につながります。
ダブルトラップは配管接続前に解消してください。
システムバスルーム設置後はダブルトラップの解除ができません。

【ダブルトラップの例】

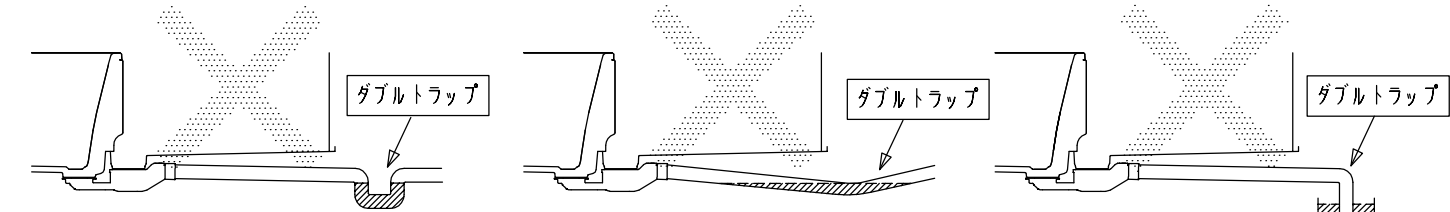


下に曲がった配管部分が、トラップになっている 横引き配管がたわみ、トラップになっている 配管の先が排水ます溜水内にあり、トラップになっている

■排水管内の詰まり
接続する排水管が、汚れなどで詰まっていないことを確認してください。
配管が細かったり、配管内が汚れ等で詰まっていると、「排水が流れない」「洗い場排水口から浴槽排水が溢れてくる」といった異常につながります。
汚れが付着して詰まっている場合、配管を接続する前に洗浄し汚れを取り除いてください。

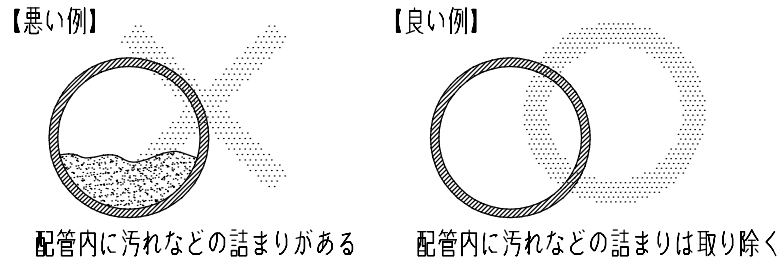


■排水管経路
排水管の経路によっては、排水異常となる場合があります。
次の事項にご注意のうえ設備業者さまと十分な事前打合せをお願い致します。

- ① システムバスルーム以降で排水管を縦方向に落とす場合
通気を設けるか、配管径を拡張、もしくは90°曲げ部に大曲リエルボ（LL）を使用する事をおすすめします。

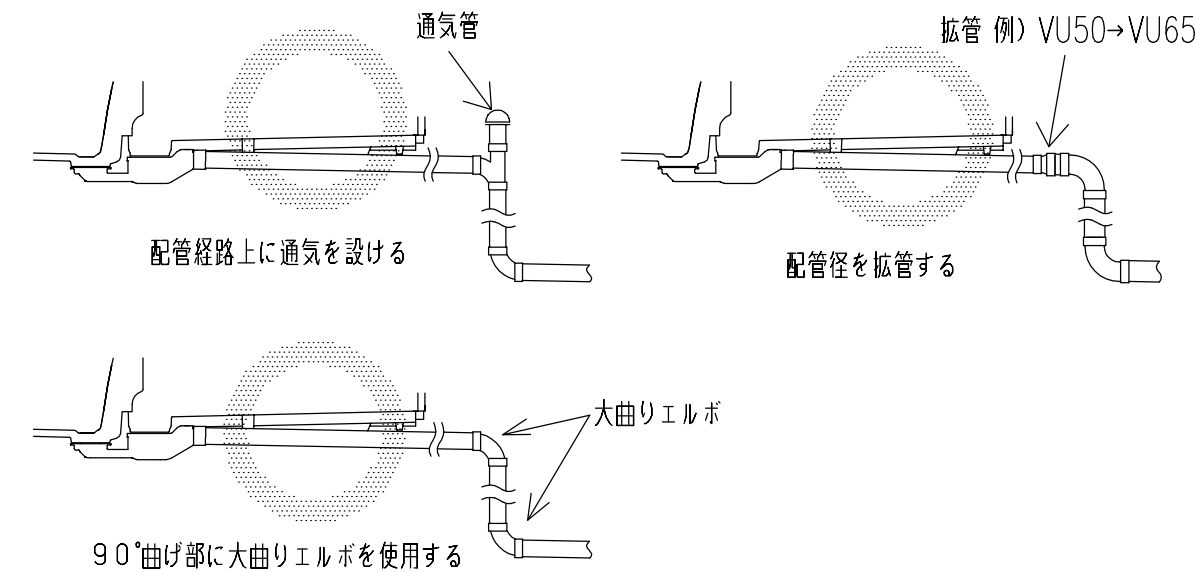



※浴槽排水時に排水口から「ゴボゴボ」と音が発生することがありますが、異常ではありません。

- ② システムバスルーム以降の横引き配管について
90°曲げ部に大曲リエルボ（LL）を使用するか、システムバスルームに近い位置で配管径を拡張する事をおすすめします。


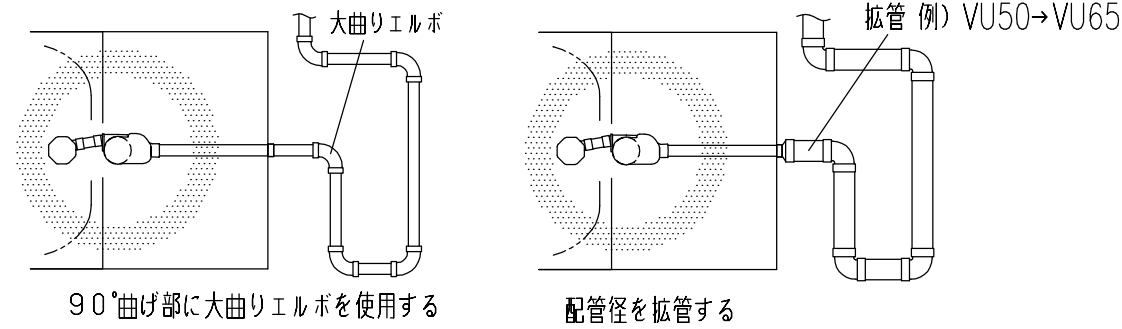


- ③ システムバスルーム床下の排水管経路について



- トラップ出口には同梱の継口配管を接続してください
 - 継口配管を使用しない場合
 - ・大曲リエルボを使用してください
 - ・1620-2サイズの場合、トラップ出口に接続する配管には、必ず切断長さ250mm以上の横引き経路を設けてください
- ※洗い場パンとの干渉回避や浴槽排水の流れを妨げないため

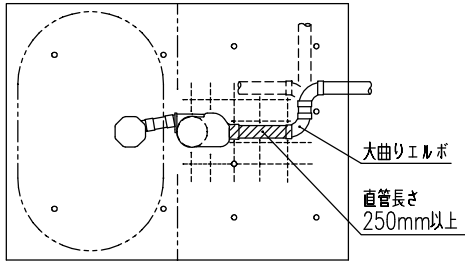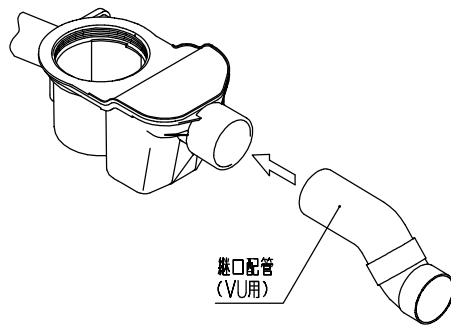




【排水管経路の悪い例】
十分な長さの横引き配管を設けずに曲げを繰り返したり、縦方向に落としている

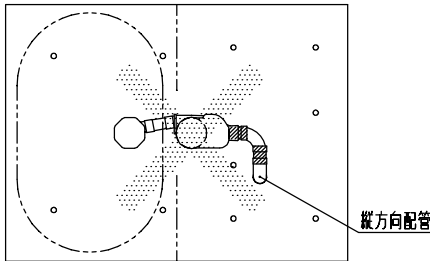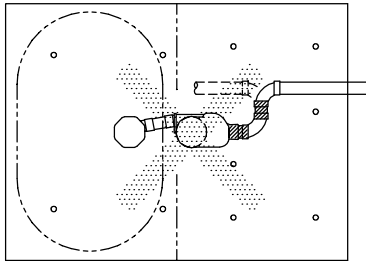

【排水管経路の良い例】
トラップから2曲がりまでの間に十分な長さの横引き経路を設けている

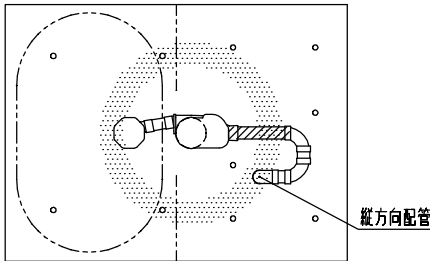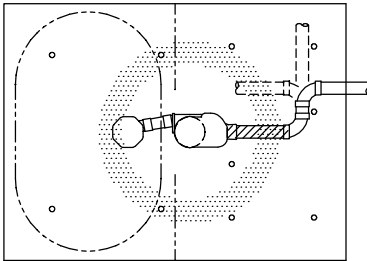

特記事項	受領印	物件名	図面	担当	検図	図番
		品名				日付
		排水管経路条件図	縮尺	株式会社 LIXIL		
		AX				

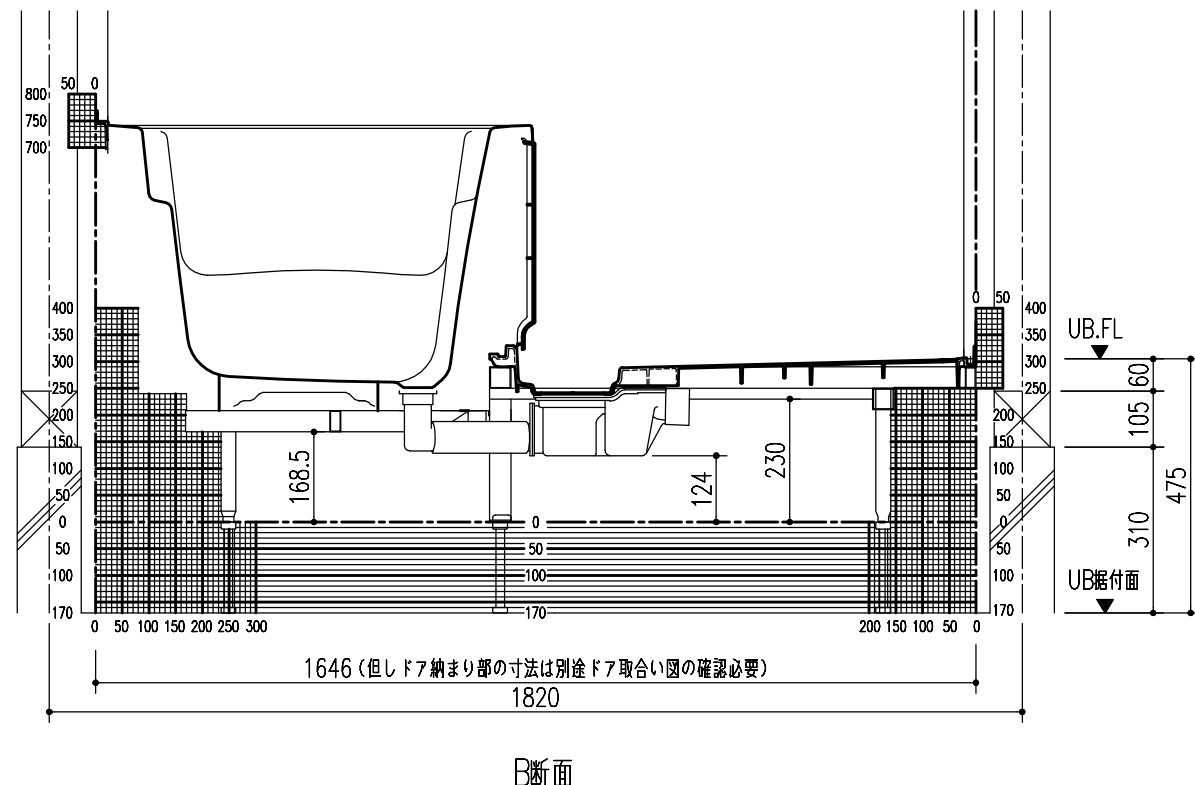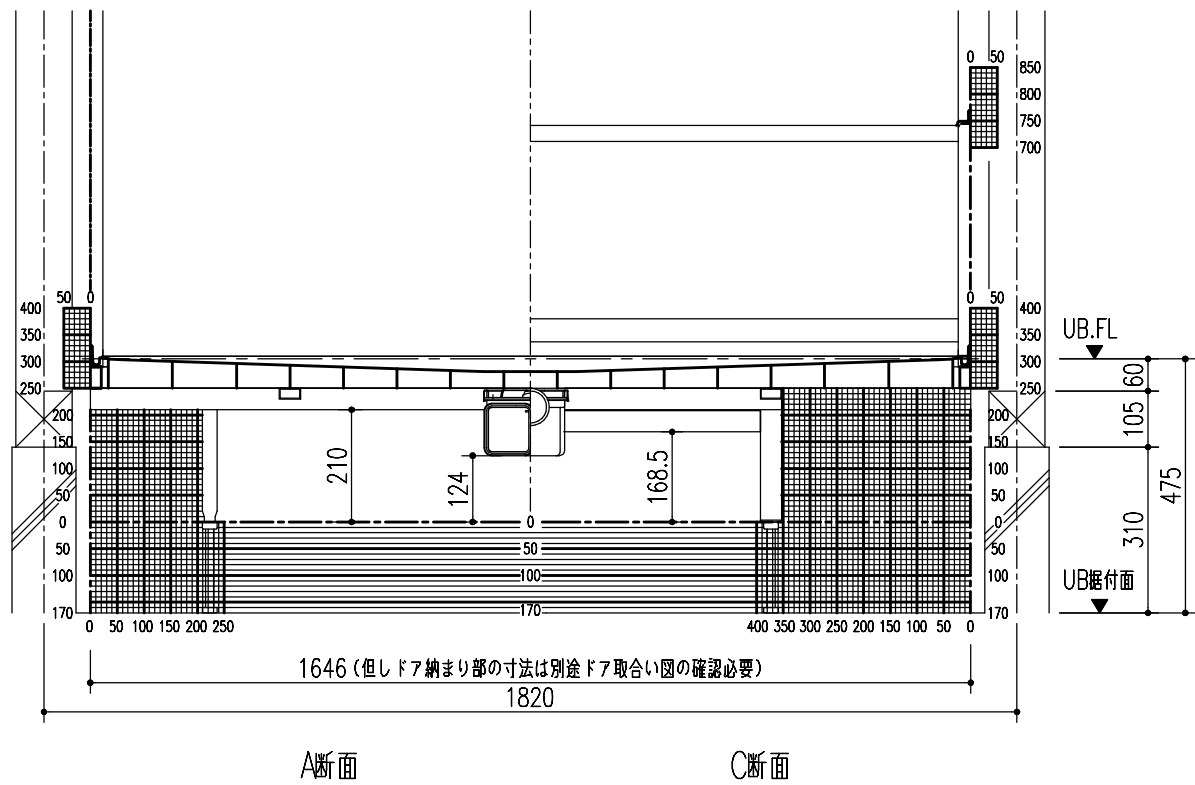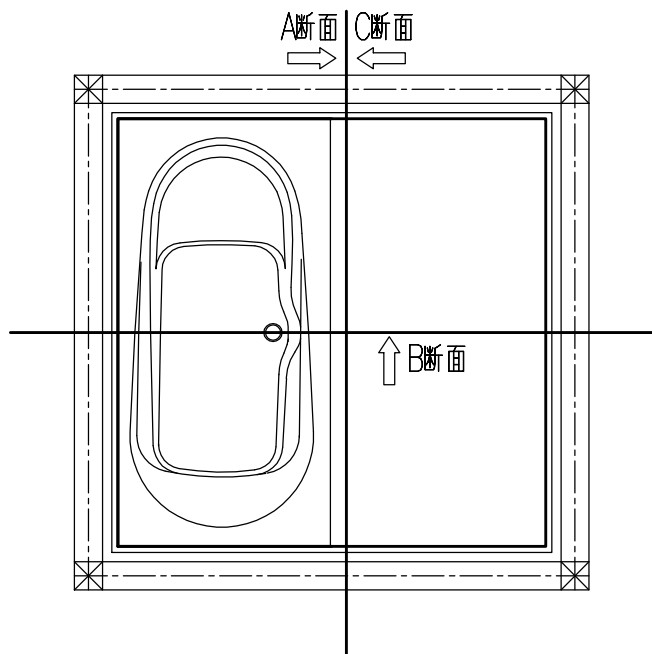

※ 本図はRタイプを示します。Lタイプは本図を左右反転したものになります。

特記事項	受領印	物 件 名	図面	担当	検図	図 番
		品 名	縮尺			日付
		床下納まり AX 1616サイズ(浴槽バンなし・ボルト脚仕様H475)		株式会社 LIXIL		