

■ 仕 様		■ HEAT20 G2
断熱工事	■ 床:ネオフォーム t90 ■ 土間床等の外周:スタイロフォームAT t50 ■ 壁:アクアフォームLITE吹付 t90 ■ 天井:アクファフォームLITE吹付 t220	
床下換気	■ 基礎パッキン JOTO (玄関・UB周り:気密基礎パッキン)	
防虫防蟻	■ 土壌処理・木部 ガントナーMC	


■ 外 部 仕 上 表			■ 22条地域
部位		仕上・仕様・メーカー	色番・品番
屋根		■ ガルバリウム鋼板(t0.35)UK立平 ニスカラーPro GH 軒先通気金物 日本住環境株式会社【REV-15】	GHK01 Sブラック
パラペット笠木		■ なし	
破風・鼻隠		■ なし	
雨樋	(軒樋)	■ Panasonic サーフেসケアFS-I型	ブラック
	(縦樋)	■ Panasonic 瞬水S15	ブラック
軒天	屋根軒	■ 神島化学 t= 6mm 軒天ボード エンボス	Wチャコールブラック
	ポーチ軒	■ 神島化学 t= 6mm 軒天ボード エンボス	Wチャコールブラック
	バルコニー軒	■ なし	
オーバーハング水切り		■ なし	
外壁 通気金物(15mm)	■メイン	KMEW 光セラ/スーパーシール	和ボーター ハイド チタン ブラック
	■アクセントA	なし	
	■アクセントB	なし	
※下地面材:タイガーEXハイパー 防火認定 PC030BE-4028			
玄関ポーチ		■ 床 玄関タイルに同じ	-
基礎		■ 立上り巾木: モルタル刷毛引き	-
基礎水切り金物		■ JOTO鋼板製 防鼠材付き水切り JOTO:WMF-N35	ブラック
バルコニー	床・内壁	■ なし	-
	笠木	■ なし	
外部建具		■ LIXIL EW(アルゴンガス高遮熱仕様LowEトリプルガラス クリア) ・SD、TSは、メーカー設定によるが、オペレーターハンドル優先とする ・オペレーター付サッシの場合は固定網戸とする ・グレモンハンドル式サッシの場合は可動網戸とする	外観 ブラック 内観 ホワイト ※樹脂パッキン・網戸付
シャッター		■ LDK 掃き出し窓 電動 洋室② 洋室③ 引違窓 手動	
軒天通気金物			
玄関扉		■ LIXIL ジエスタ2 K2仕様 LIXILファミロック タグキー×3 (電池式)	ドア型: M17 型 ドア色: クリエール ハンドル: S型ハンドル 色 ブラック
外部物干し金物		■ 川口技研 RK-55型	ブラック
換気フード		■ 局所換気扇(トイレ 浴室 キッチンフード) 防火ダンパー無 ■ ダクトレス熱交換換気システム (日本スティーベル株式会社) VLR-70E 防火ダンパー無	外気フード: ブラック 外気フード: ブラック 室内パネル マッドグレー


■ 構 造 概 要			
基礎	■ RCベタ基礎コンクリート		
通し柱・管柱	■ 構造用集成材 105×105		間柱 ■ 集成材
土台	■ 桧 105×105 大引き ■ 桧 90*90	筋交い	■ 構造用製材 火打梁 ■ 鋼製火打(当社基準により米松あり)
桁・梁	■ 構造用製材及び集成材		制震装置 ■ Kダンパー (株)アイ・エム・エー

■ 設 備 装 着 品							
住宅設備	部位	メーカー	商品名	※ 詳細は見積り、プレゼン参照	見積りNo.	(日付)	
	キッチン	LIXIL	■ ES 1型 扉ホワイトストック 天板ツルティホワイト キッチンパネルフレッシュホワイト シンクキレイシンクシュガーホワイト 食洗器/リンナイフロントオープンを検討 サイドフードHVR(ホワイト) スリム取手シルバー		見積り番号 : M25047203833-004-2 (日付) 2025.6.23		
	バックカウンタ ※オプション	LIXIL	■ カウンタータイプ W2100(W750スライドストッカー×2+W600スライドストッカー)		見積り番号 : M25047203833-004-3 (日付) 2025.6.23		
	浴室	LIXIL	■ AX1616 PGハウス標準仕様 開き戸ホワイト マグネット組フタフック ホワイト アクセント壁:ペリンボンミニット 浴槽:エコベンチ ホワイト 床:ホワイト マグネットシェフ:ホワイト		見積り番号 : M25047203833-004-1 (日付) 2025.6.23		
	1フトイレ	LIXIL	■ ベーシアシャワートイレ 白 ● タオル掛け: - タンク手洗 無し ● 紙巻き器: 埋込収納		見積り番号 : M25047203833-004-5 (日付) 2025.6.23		
	洗面台	LIXIL	■ EV W1200(D500タイプ) 扉: 扉ホワイト[引出しタイプ シングルハンドシャワー スタンダードLED三面鏡] その他 ● タオル掛け:KF-AA71D(バー)		見積り番号 : M25047203833-004-4 (日付) 2025.6.23		
	1フトイレ	LIXIL	■ 埋込収納棚 紙巻器付 TSF-21 IU/LP ホワイト		M25047203833-004-5 2025.6.23		
給排水設備	給湯器	■ エコキュート460L Panasonic Sシリーズ スタンダードモデル 追い焚きフルオート					
	排水	■ 合併浄化槽 5人槽 ポンプアップ無					
	外水栓	■ 1 カ所 (平面図参照)	■ 外部立栓柱: PVC製 水栓柱12型【前澤化成工業】				
	外部ガーデンパン	■ 無し					
	その他	■ 洗濯機用単水栓: 緊急止水弁付		■ 洗濯機用排水:トラップ金物(標準)			
		■ 排水さや管(長期優良住宅仕様)					
ガス配管設備		■ なし (配置図・平面図参照)					
電気設備	インターホン	■ パナソニック VL-SE31XL					
	TVアンテナ	■ UHF + BS・110度CS/CSアンテナ [2K・4K・8K対応] ■ホワイト					
	エアコン	■ 設置場所:					
	ソーラー	■ あり(Qセルズ) 12 枚 5.28 KW Re.RISE-G3 440 (1722×1134×30)					
	※標準搭載	※メーカーのモデルチェンジ等で後継品に変更される可能性あり ■ 屋外パワコン エネルギーマネジメントシステム Cube J					
その他							
					決定図		

決定図

	浜 岡 一 級 総 合 設 計 事 務 所 一級建築士事務所 静岡県知事登録第 (10)2441 号 一級建築士 大臣登録第 365879 号 西原利昌	 PG HOUSE	株式会社 LIFEFUND InDesign office 一級建築士事務所 事務所登録 (2)第7595号 一級建築士登録 第179770号 鈴木 達男 〒432-8023 静岡県浜松市中央区鴨江3丁目70番23号	年 月 日	件名		設計 IC 工務 図 番
				2025.7.11	南 頼伸様・日香梨様		
				縮尺	図面		
					仕上表 1		
						酒井	青島 1-1

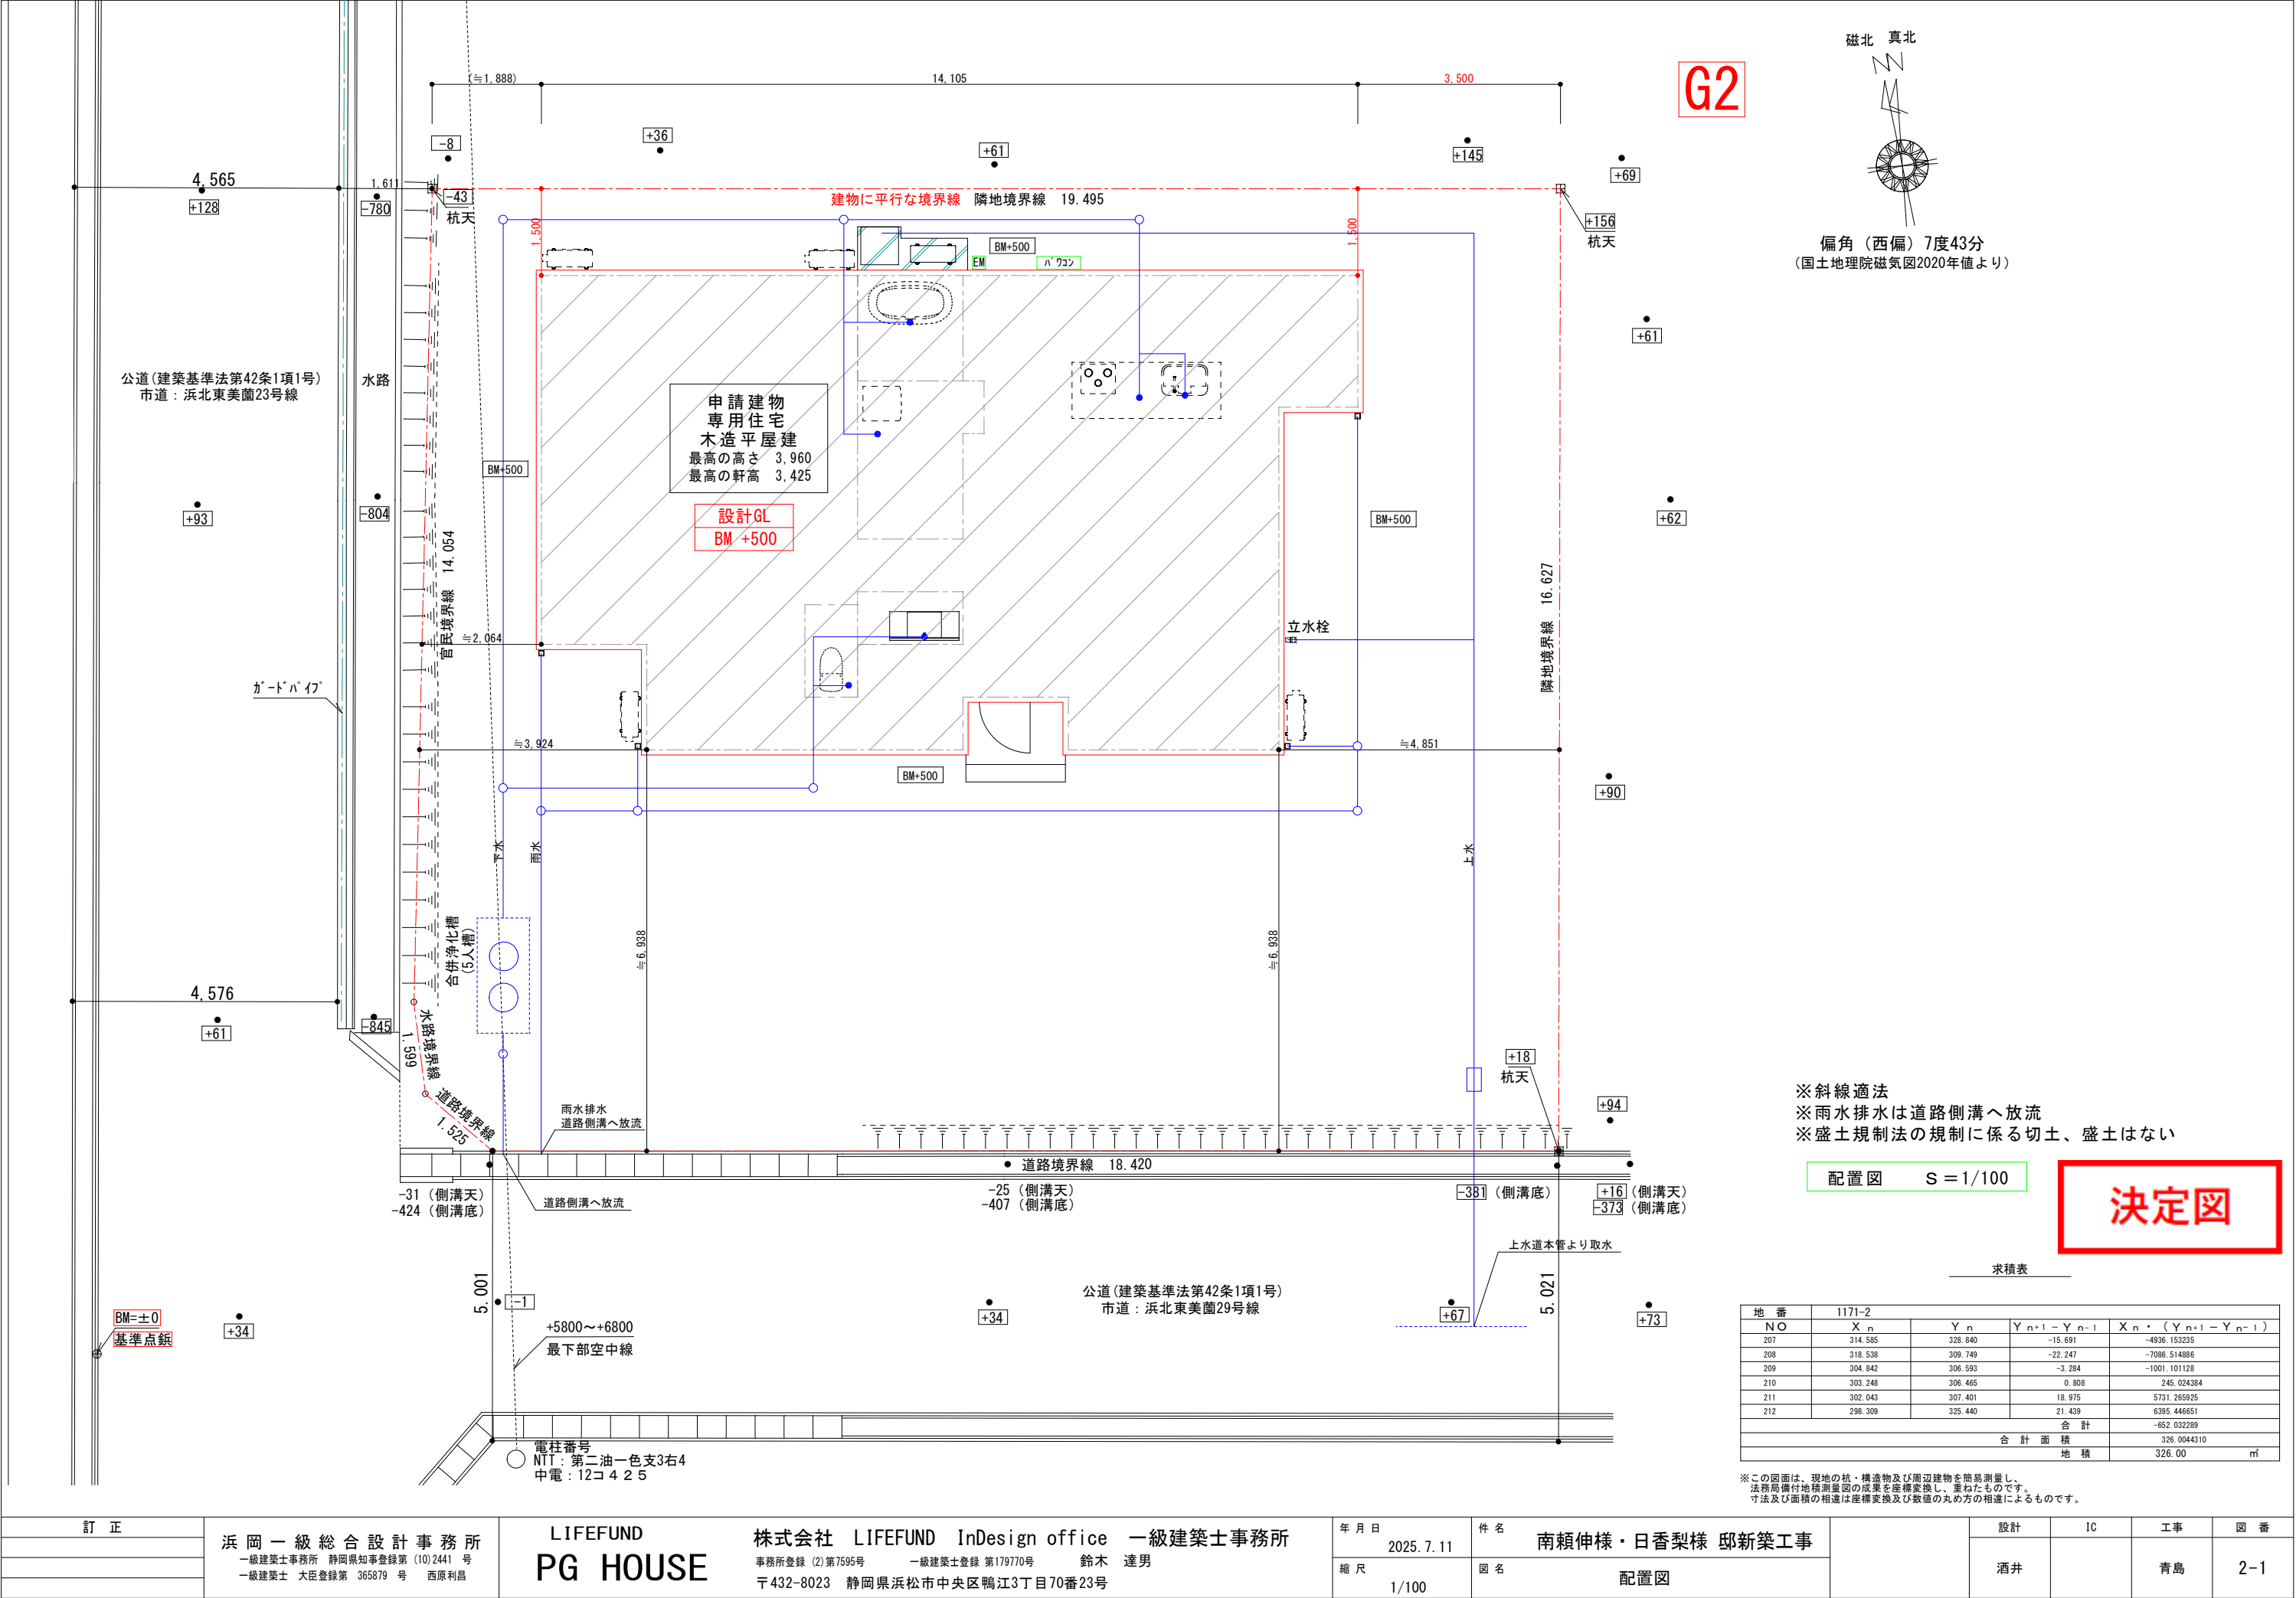


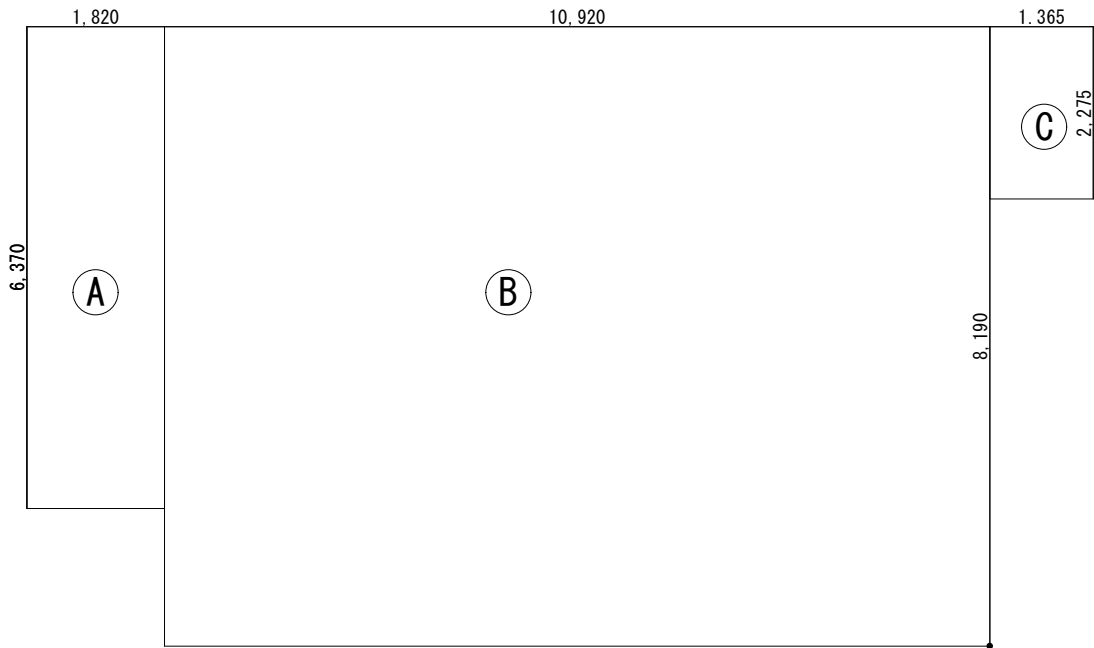

建築面積求積図 S=1/100

建築面積求積表

番号	計算式	(m)	面積 (㎡)
Ⓐ	1. 820 × 6. 370		11. 5934
Ⓑ	10. 920 × 8. 190		89. 4348
Ⓒ	1. 365 × 2. 275		3. 1054
合計			104. 1336 104. 13 (31. 5坪)

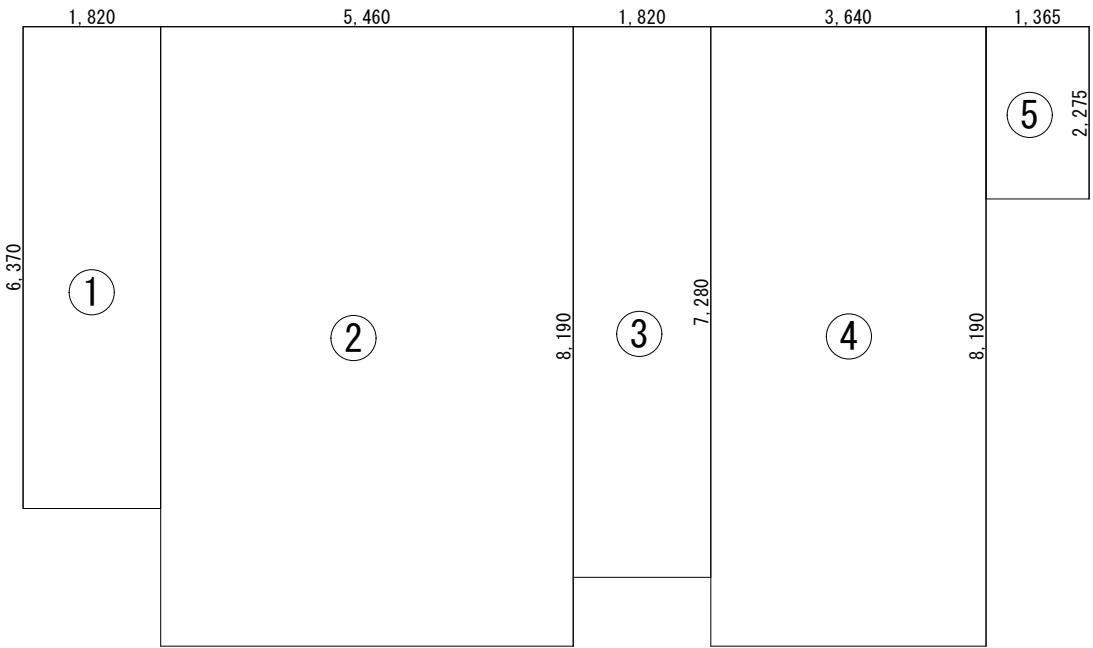

1階床面積図 S=1/100


1階床面積求積表

番号	計算式	(m)	面積 (㎡)
①	1. 820 × 6. 370		11. 5934
②	5. 460 × 8. 190		44. 7174
③	1. 820 × 7. 280		13. 2496
④	3. 640 × 8. 190		29. 8116
⑤	1. 365 × 2. 275		3. 1054
合計			102. 4774 102. 47 (30. 9坪)

延べ床面積表

	番号	(m)	面積 (㎡)
1階床面積	① ② ③ ④ ⑤		102. 47
2階床面積			
合計			102. 47 (30. 9坪)

決定図

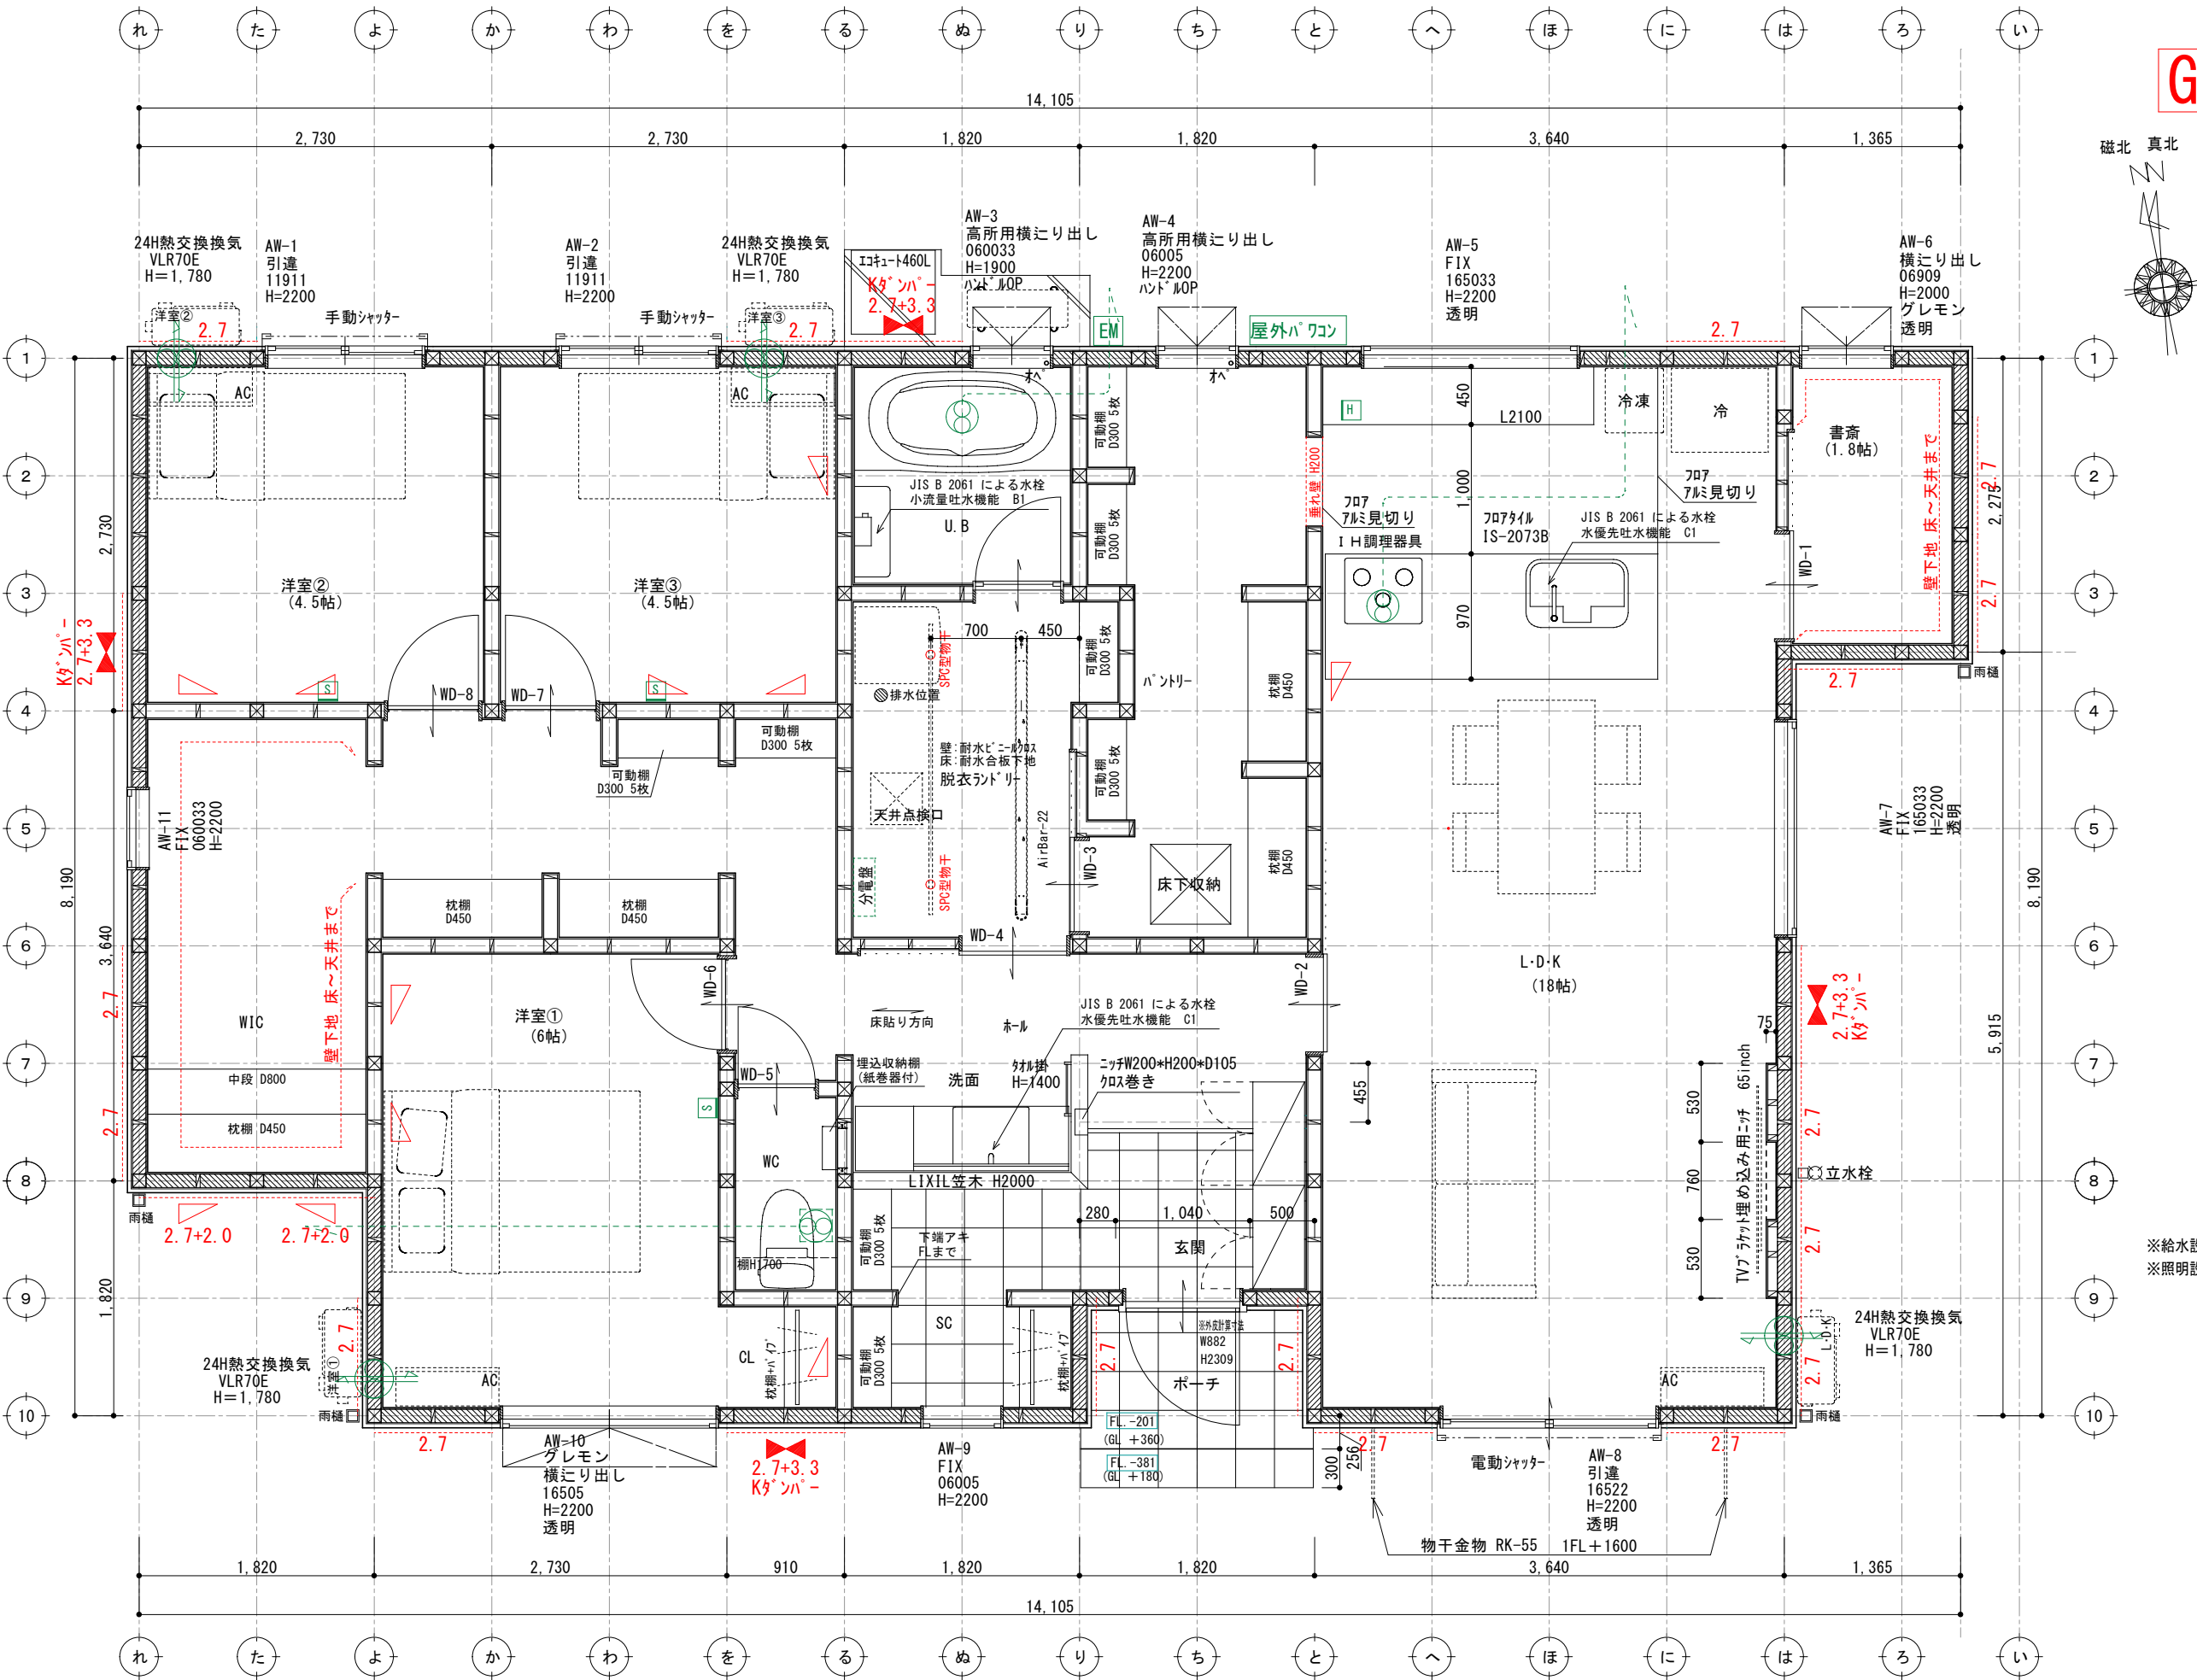

G2

壁付け 住宅用火災報知器			数量
H	熱感知器	電池式(単独型)	1
	露出型		
壁付け 住宅用火災報知器			数量
S	煙感知器	電池式(単独型)	3
	露出型		

- ※ 煙感知器は壁・梁より600mm以上離す
壁に取付ける場合、
天井から150mm以上500mm以内離す
換気扇・エアコン吹出口から1500mm以上離す
- ※ 全室LED照明とする。
- ※ 標準天井高さ2,400
- ※ 特記無きガラスは型ガラス

* 凡例

- ☒ 管柱 (105×105)
- ▲ Kダクト (3.30倍 FRM-0641)
- △ 片筋違い (2.00倍 45×90)
(例 左:柱脚 右:柱頭)
- ⊠ たすき掛筋違い (4.00倍 45×90)
- 構造用合板 (2.70倍)
(t=9 タカ-EXハイパー)
(標準仕様 2.7倍: FRM-0678)
(入隅仕様 2.7倍: FRM-0734)
- ⊠ 天井点検口
- ⊙ 換気扇
- ⊙ 熱交換換気扇 VLR-70

脱衣ランドリー 仕上材



- 天井: ア9.5PB下地ビニルクロス貼り
壁: ア12.5PB下地ビニルクロス貼り
床: ア24+15耐水合板下地フロアタイル張り

- ※給水設備: ヘッダー分岐後の全ての配管径は13A以下とする
- ※照明設備: 全室LED照明とし居室においては調光制御、非居室においては
人感センサーを採用する

決定図


訂正	浜岡一級総合設計事務所 一級建築士事務所 静岡県知事登録第 (10)2441 号 一級建築士 大臣登録第 365879 号 西原利昌	PG HOUSE ピージーハウス	株式会社 LIFEFUND InDesign office 一級建築士事務所 事務所登録 (2) 第7595号 一級建築士登録 第179770号 鈴木 達男 〒432-8023 静岡県浜松市中央区鴨江3丁目70番23号	年月日 2025. 7. 11 縮尺 1/50	件名 南頼伸様・日香梨様邸 新築工事 図名 1階平面図	設計 酒井	IC	工事 青島	図番
----	--	---------------------	---	----------------------------------	--------------------------------------	----------	----	----------	----

GX住宅
(Cube J付)
太陽光あり

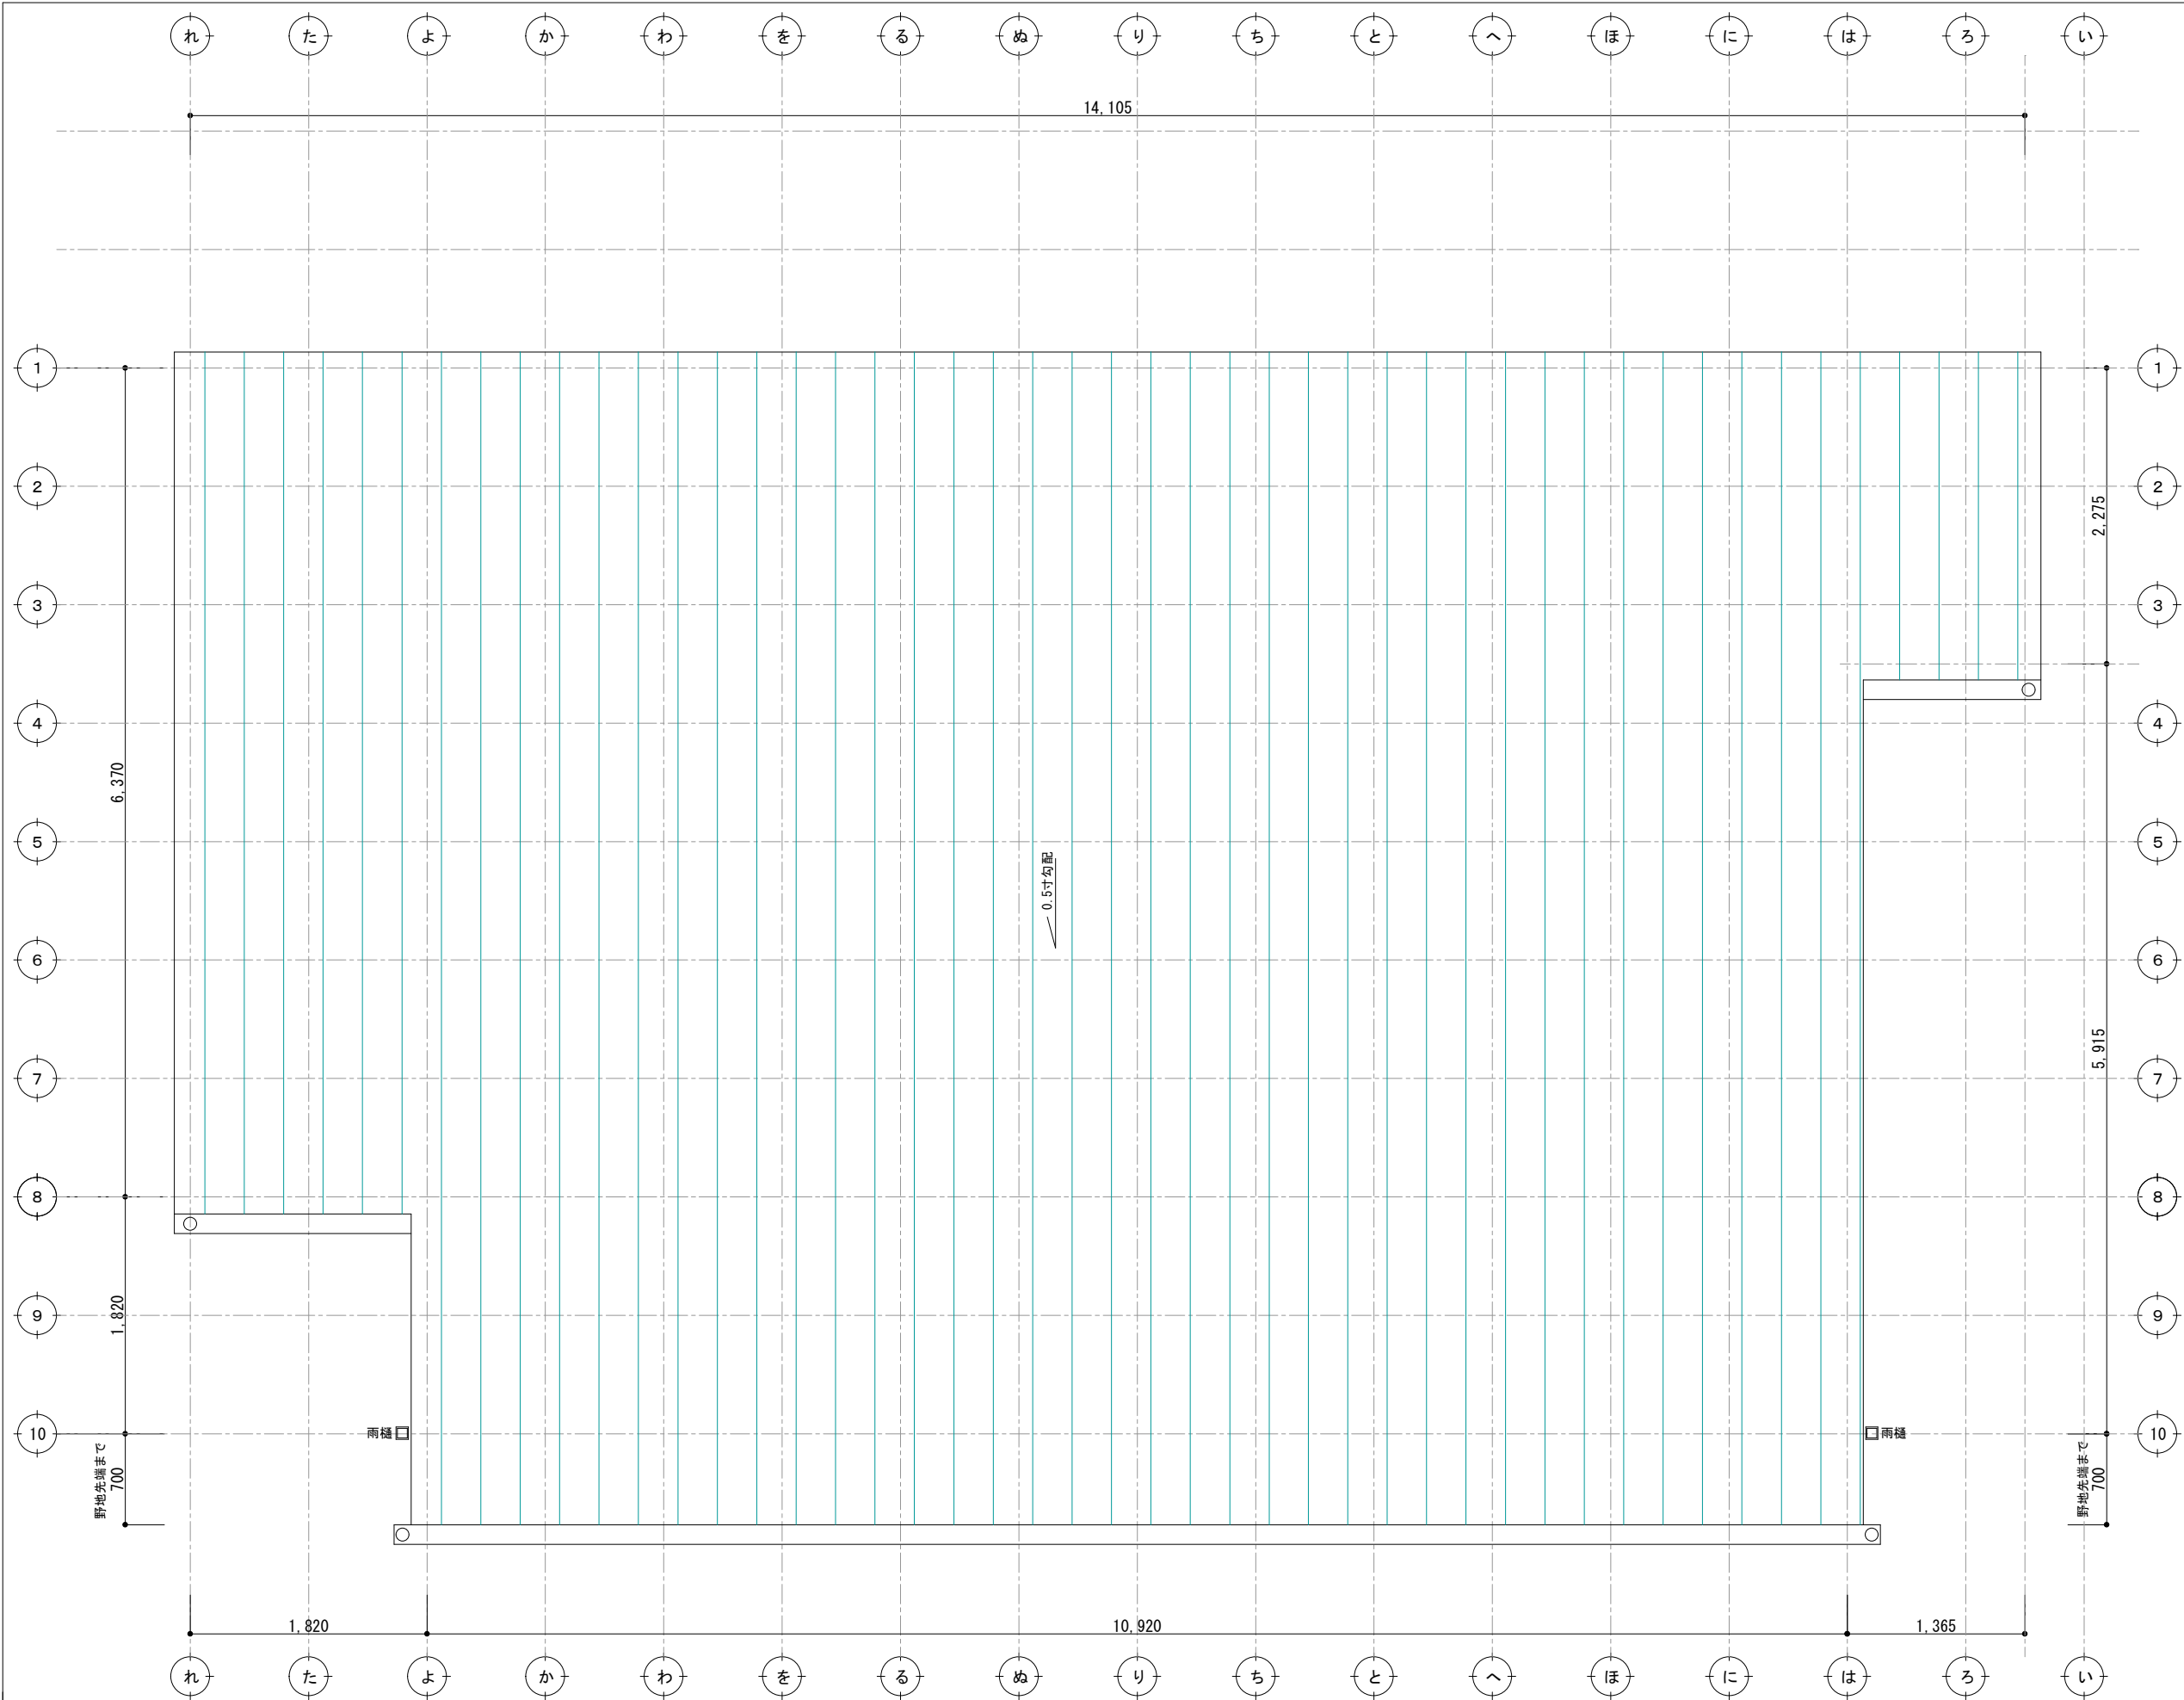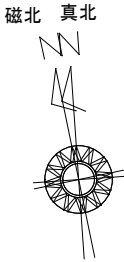


決定図

訂 正	浜 岡 一 級 総 合 設 計 事 務 所 一級建築士事務所 静岡県知事登録第 (10)2441 号 一級建築士 大臣登録第 365879 号 西原利昌	 PG HOUSE	株式会社 LIFEFUND InDesign office 一級建築士事務所 事務所登録 (2) 第7595号 一級建築士登録 第179770号 鈴木 達男 〒432-8023 静岡県浜松市中央区鴨江3丁目70番23号	年 月 日	件 名	設計	IC	工事	図 番
				2025. 7. 11	南頼伸様・日香梨様邸 新築工事				
				縮 尺	図 名				
				1/100	屋根伏図				
						酒井		青島	

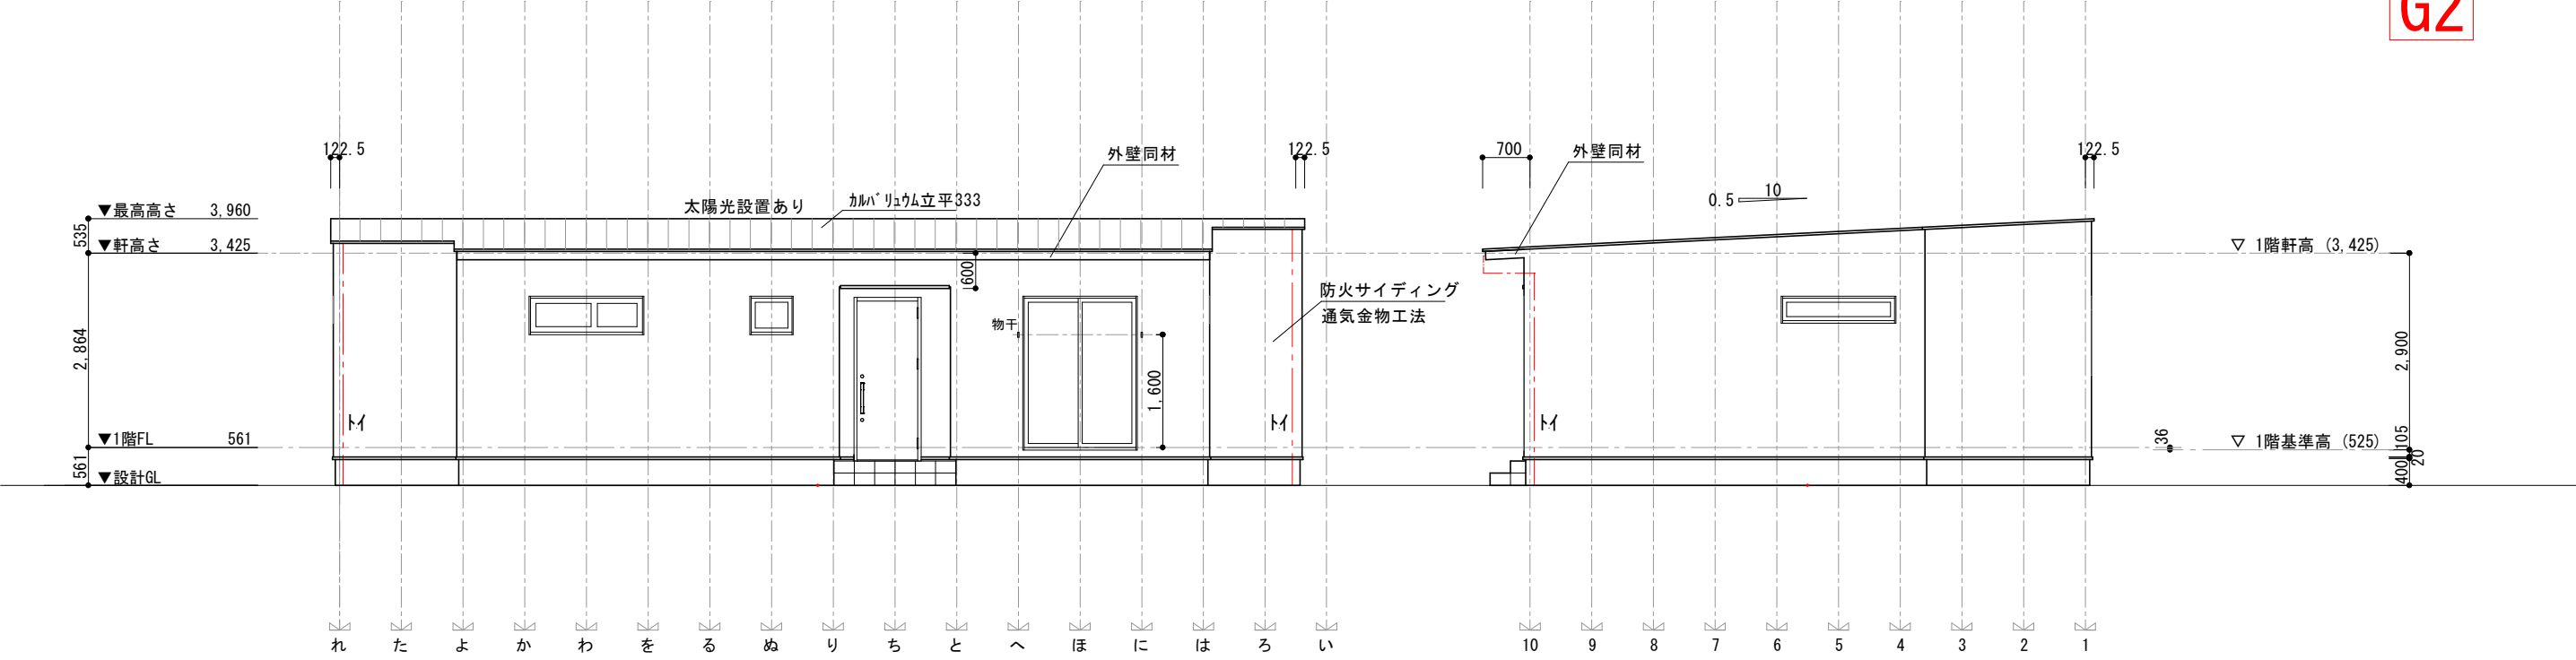

南側立面図 S=1/100



東側立面図 S=1/100

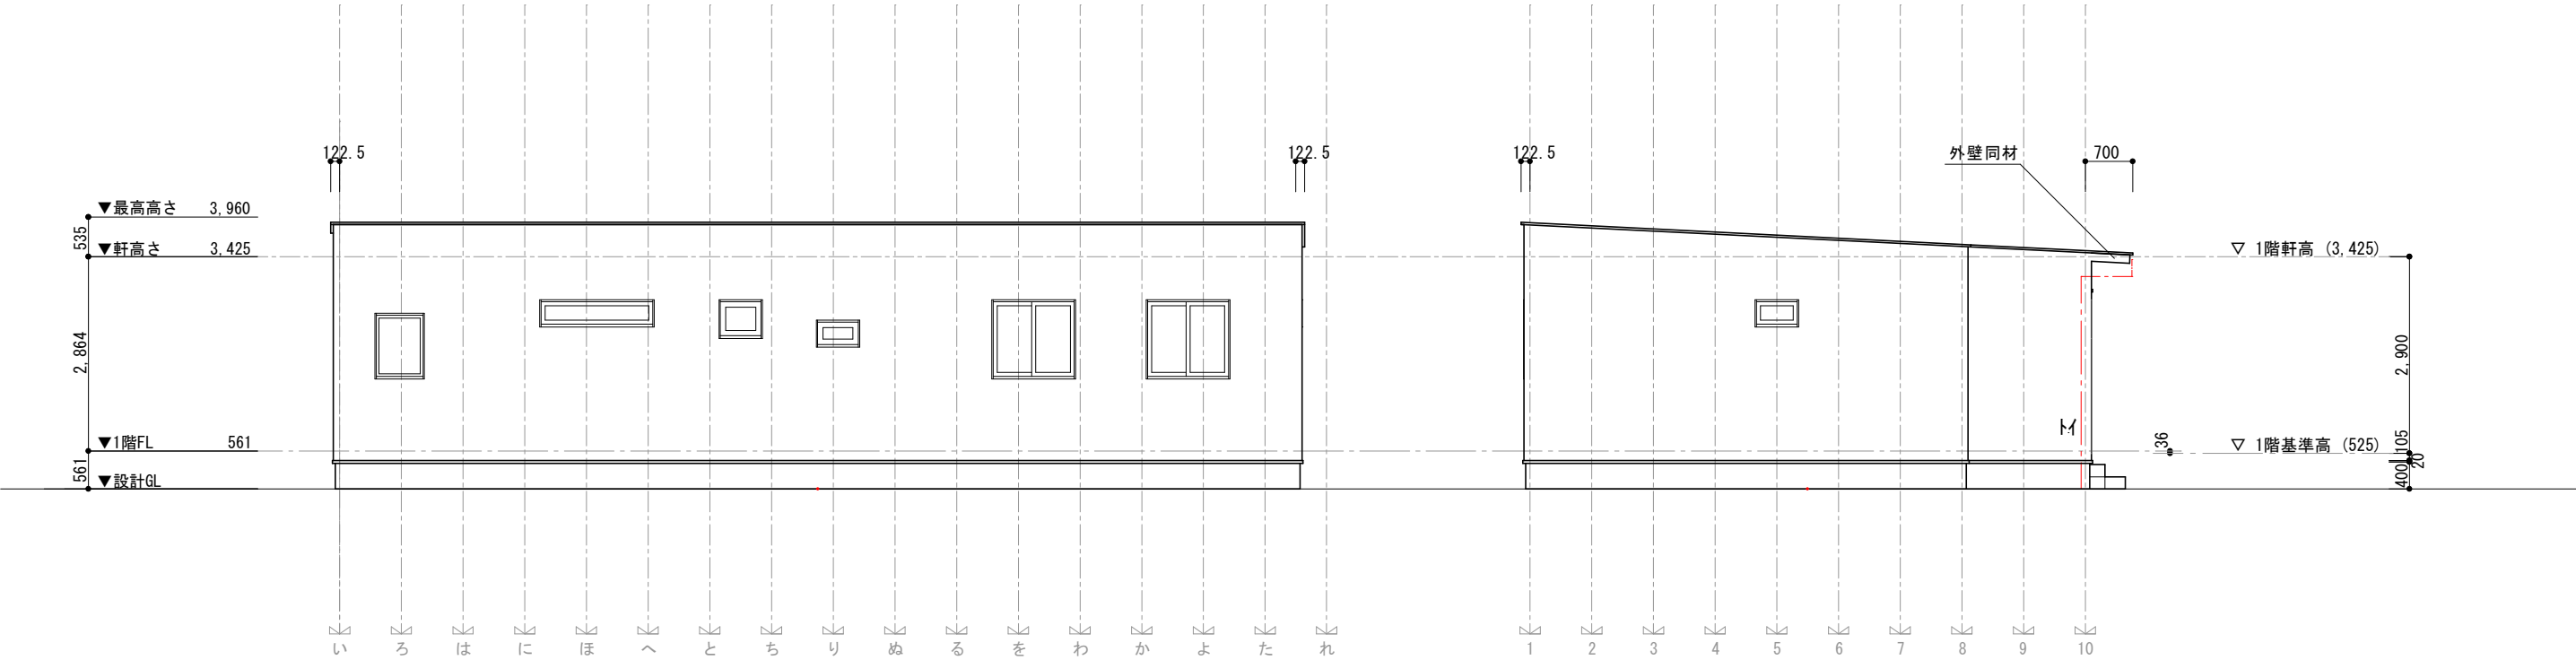

北側立面図 S=1/100




西側立面図 S=1/100

決定図

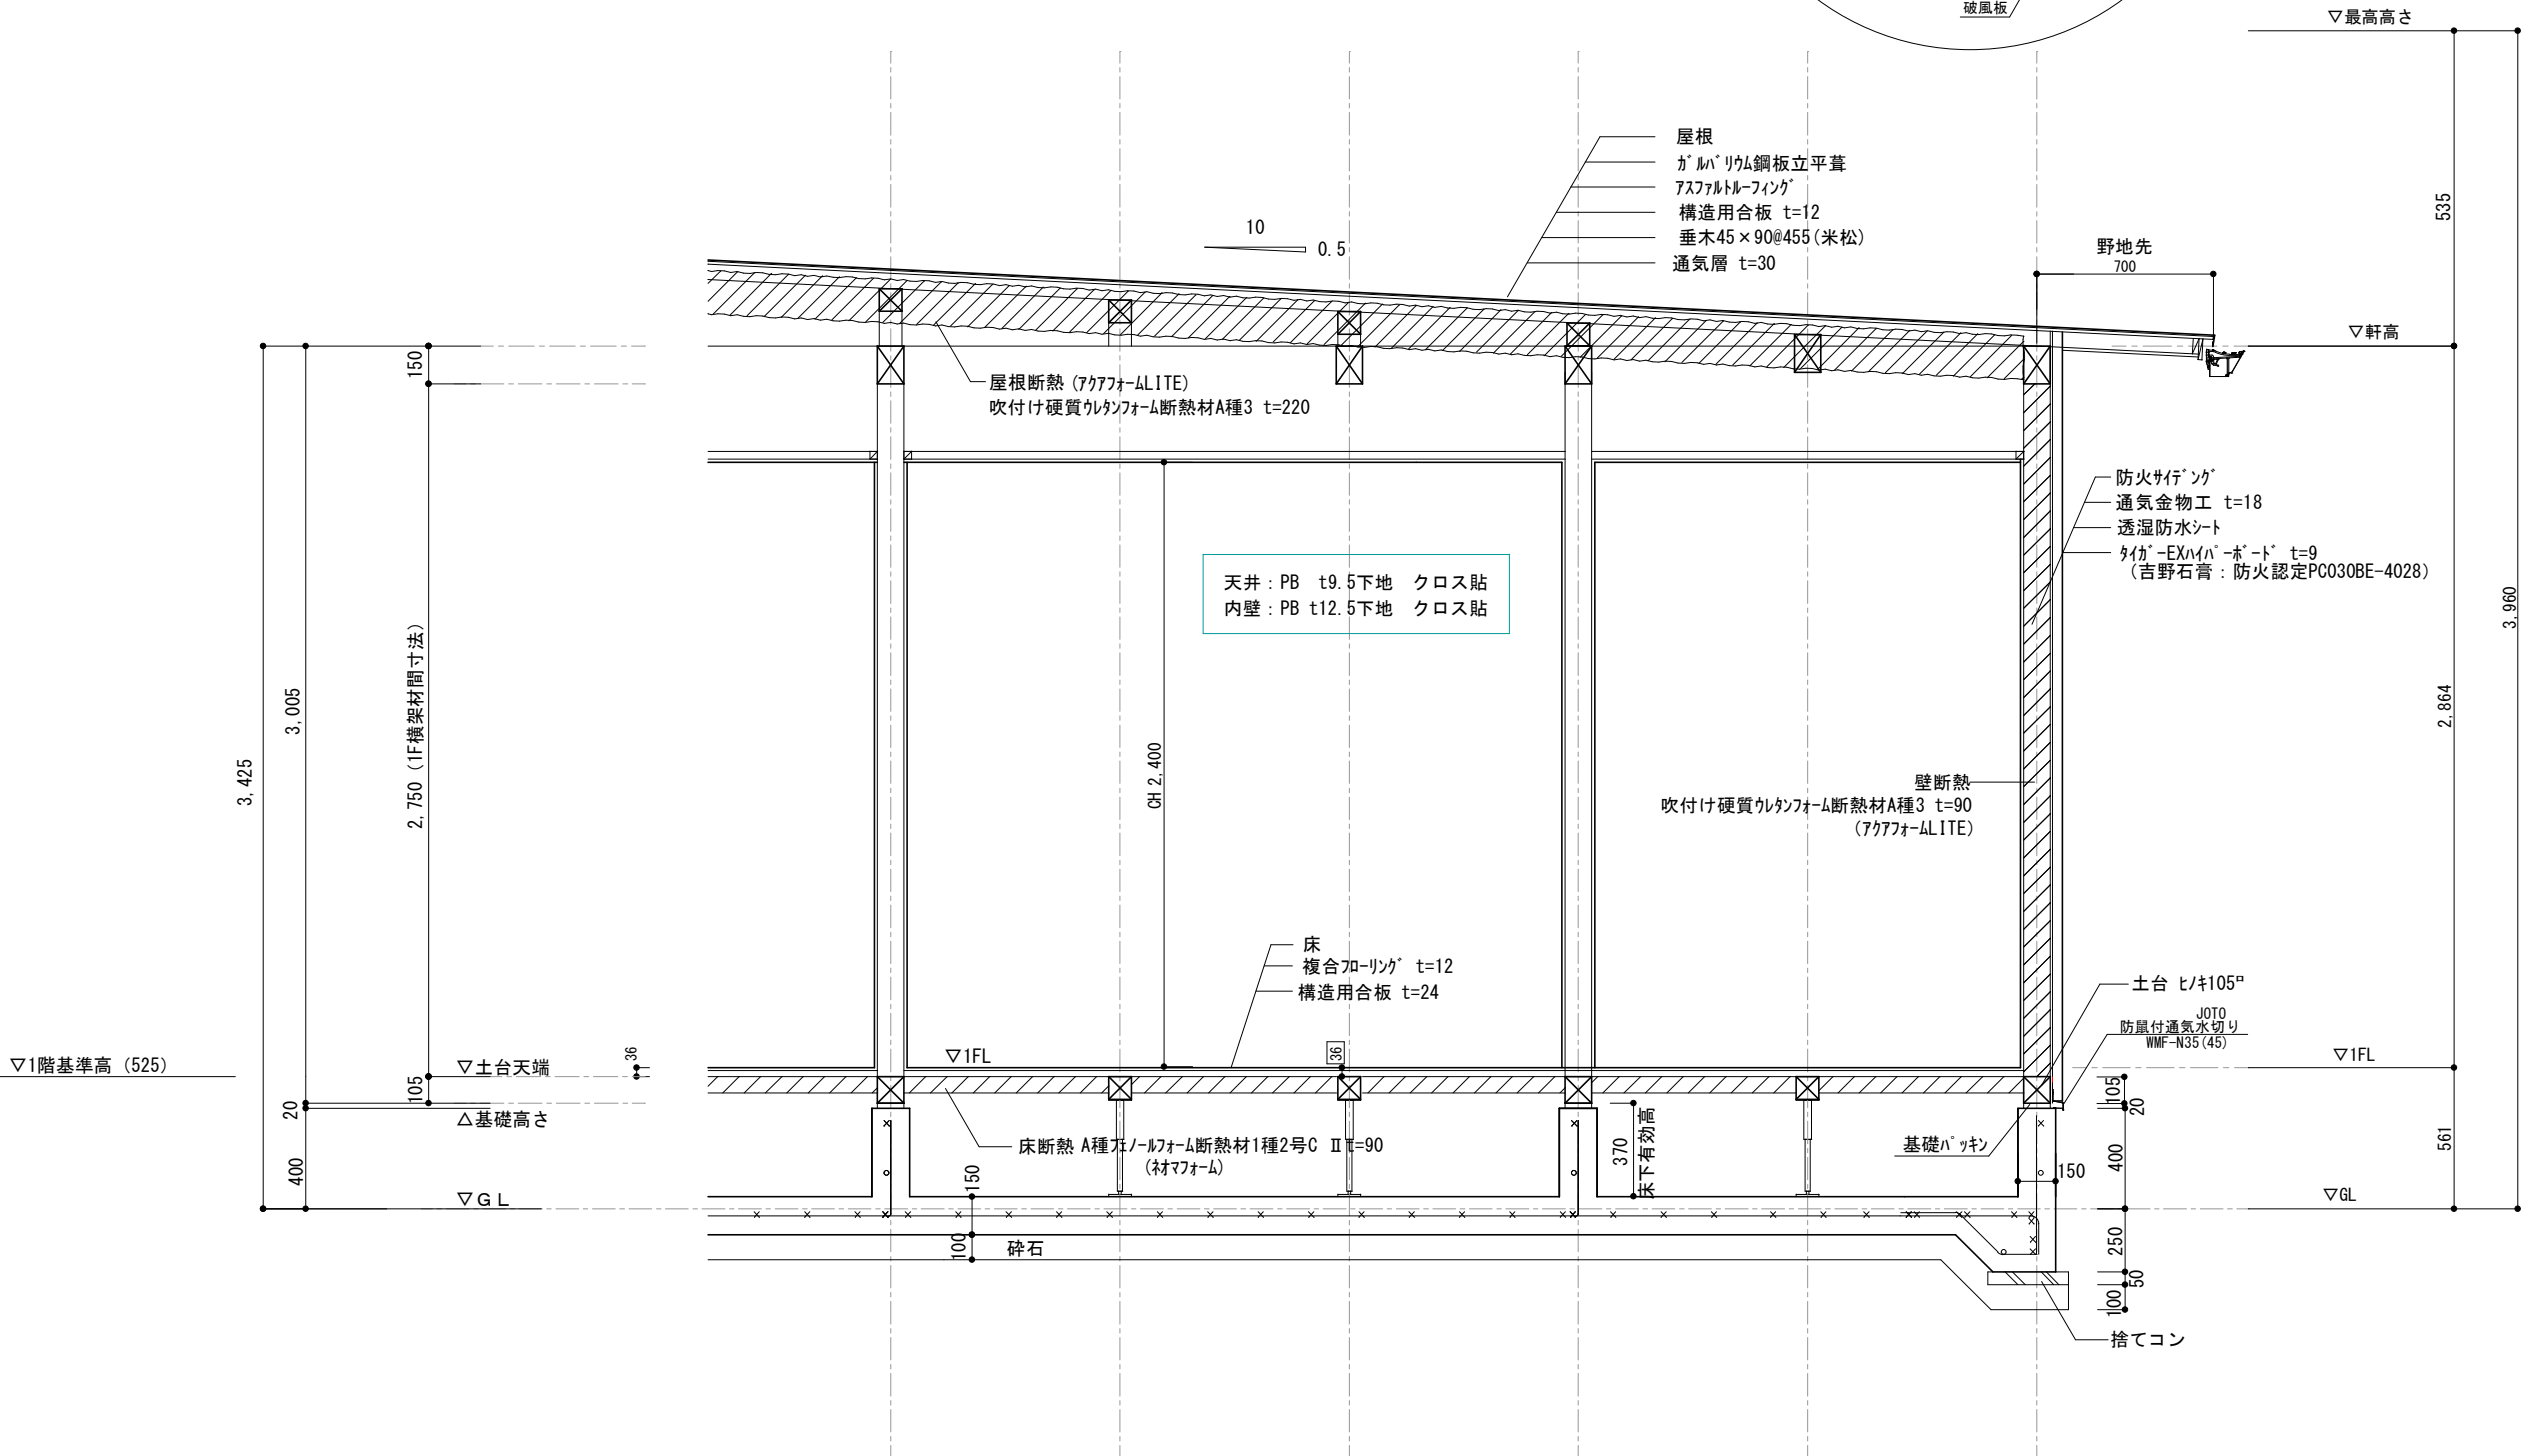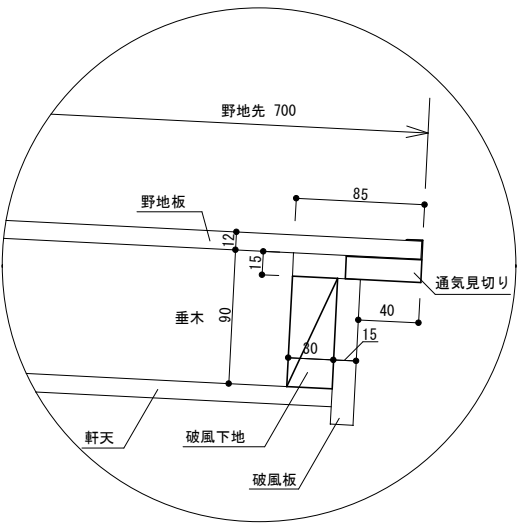


決定図

訂正	浜岡一級総合設計事務所 一級建築士事務所 静岡県知事登録第 (10)2441 号 一級建築士 大臣登録第 365879 号 西原利昌		株式会社 LIFEFUND InDesign office 一級建築士事務所 事務所登録 (2) 第7595号 一級建築士登録 第179770号 鈴木 達男 〒432-8023 静岡県浜松市中央区鴨江3丁目70番23号	年月日 2025. 7. 11	件名 南頼伸様・日香梨様 邸新築工事	設計 IC 工事 図番	酒井 青島 5
				縮尺 1/30	図名 矩計図		

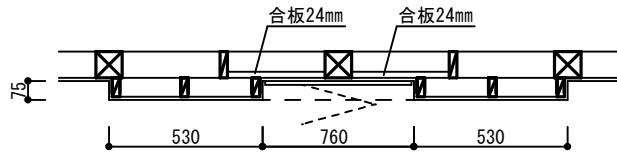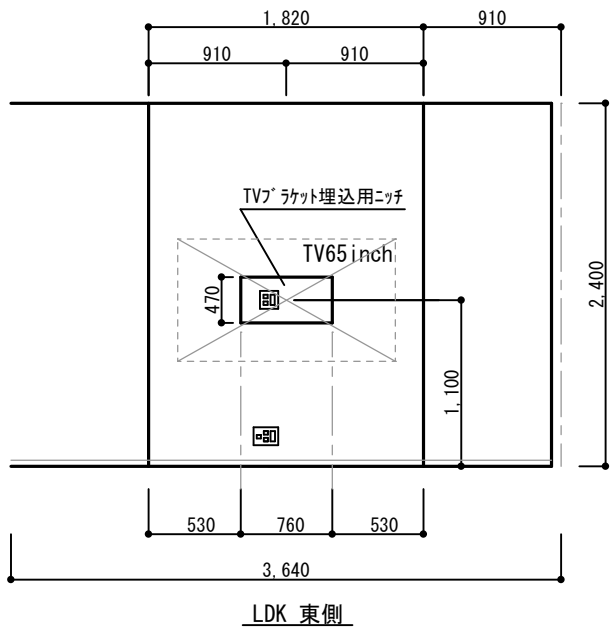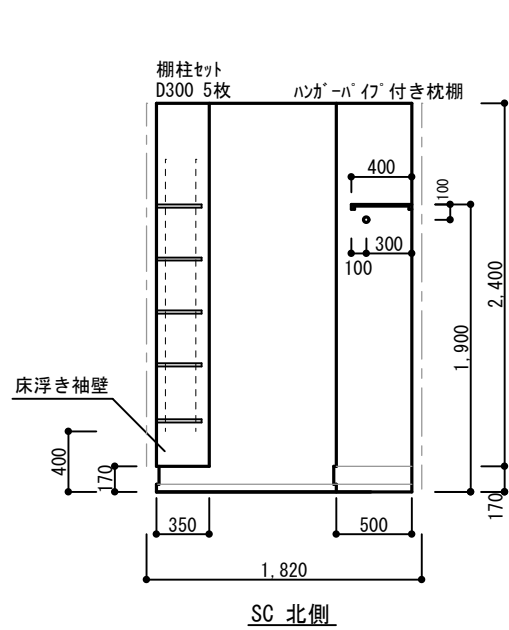


LDK 東側 断面図 (1/30)

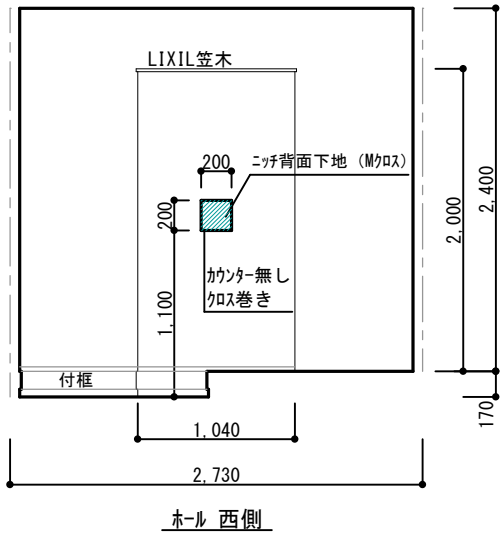


決定図

訂正	浜岡一級総合設計事務所 一級建築士事務所 静岡県知事登録第 (10)2441 号 一級建築士 大臣登録第 365879 号 西原利昌	LIFEFUND PG HOUSE	株式会社 LIFEFUND InDesign office 一級建築士事務所 事務所登録 (2)第7595号 一級建築士登録 第179770号 鈴木 達男 〒432-8023 静岡県浜松市中央区鴨江3丁目70番23号	年月日 2025. 7. 11	件名 南頼伸様・日香梨様 新築工事		設計	IC	工事	図番
				縮尺 1/50	図名 展開図-1		酒井		青島	6-1

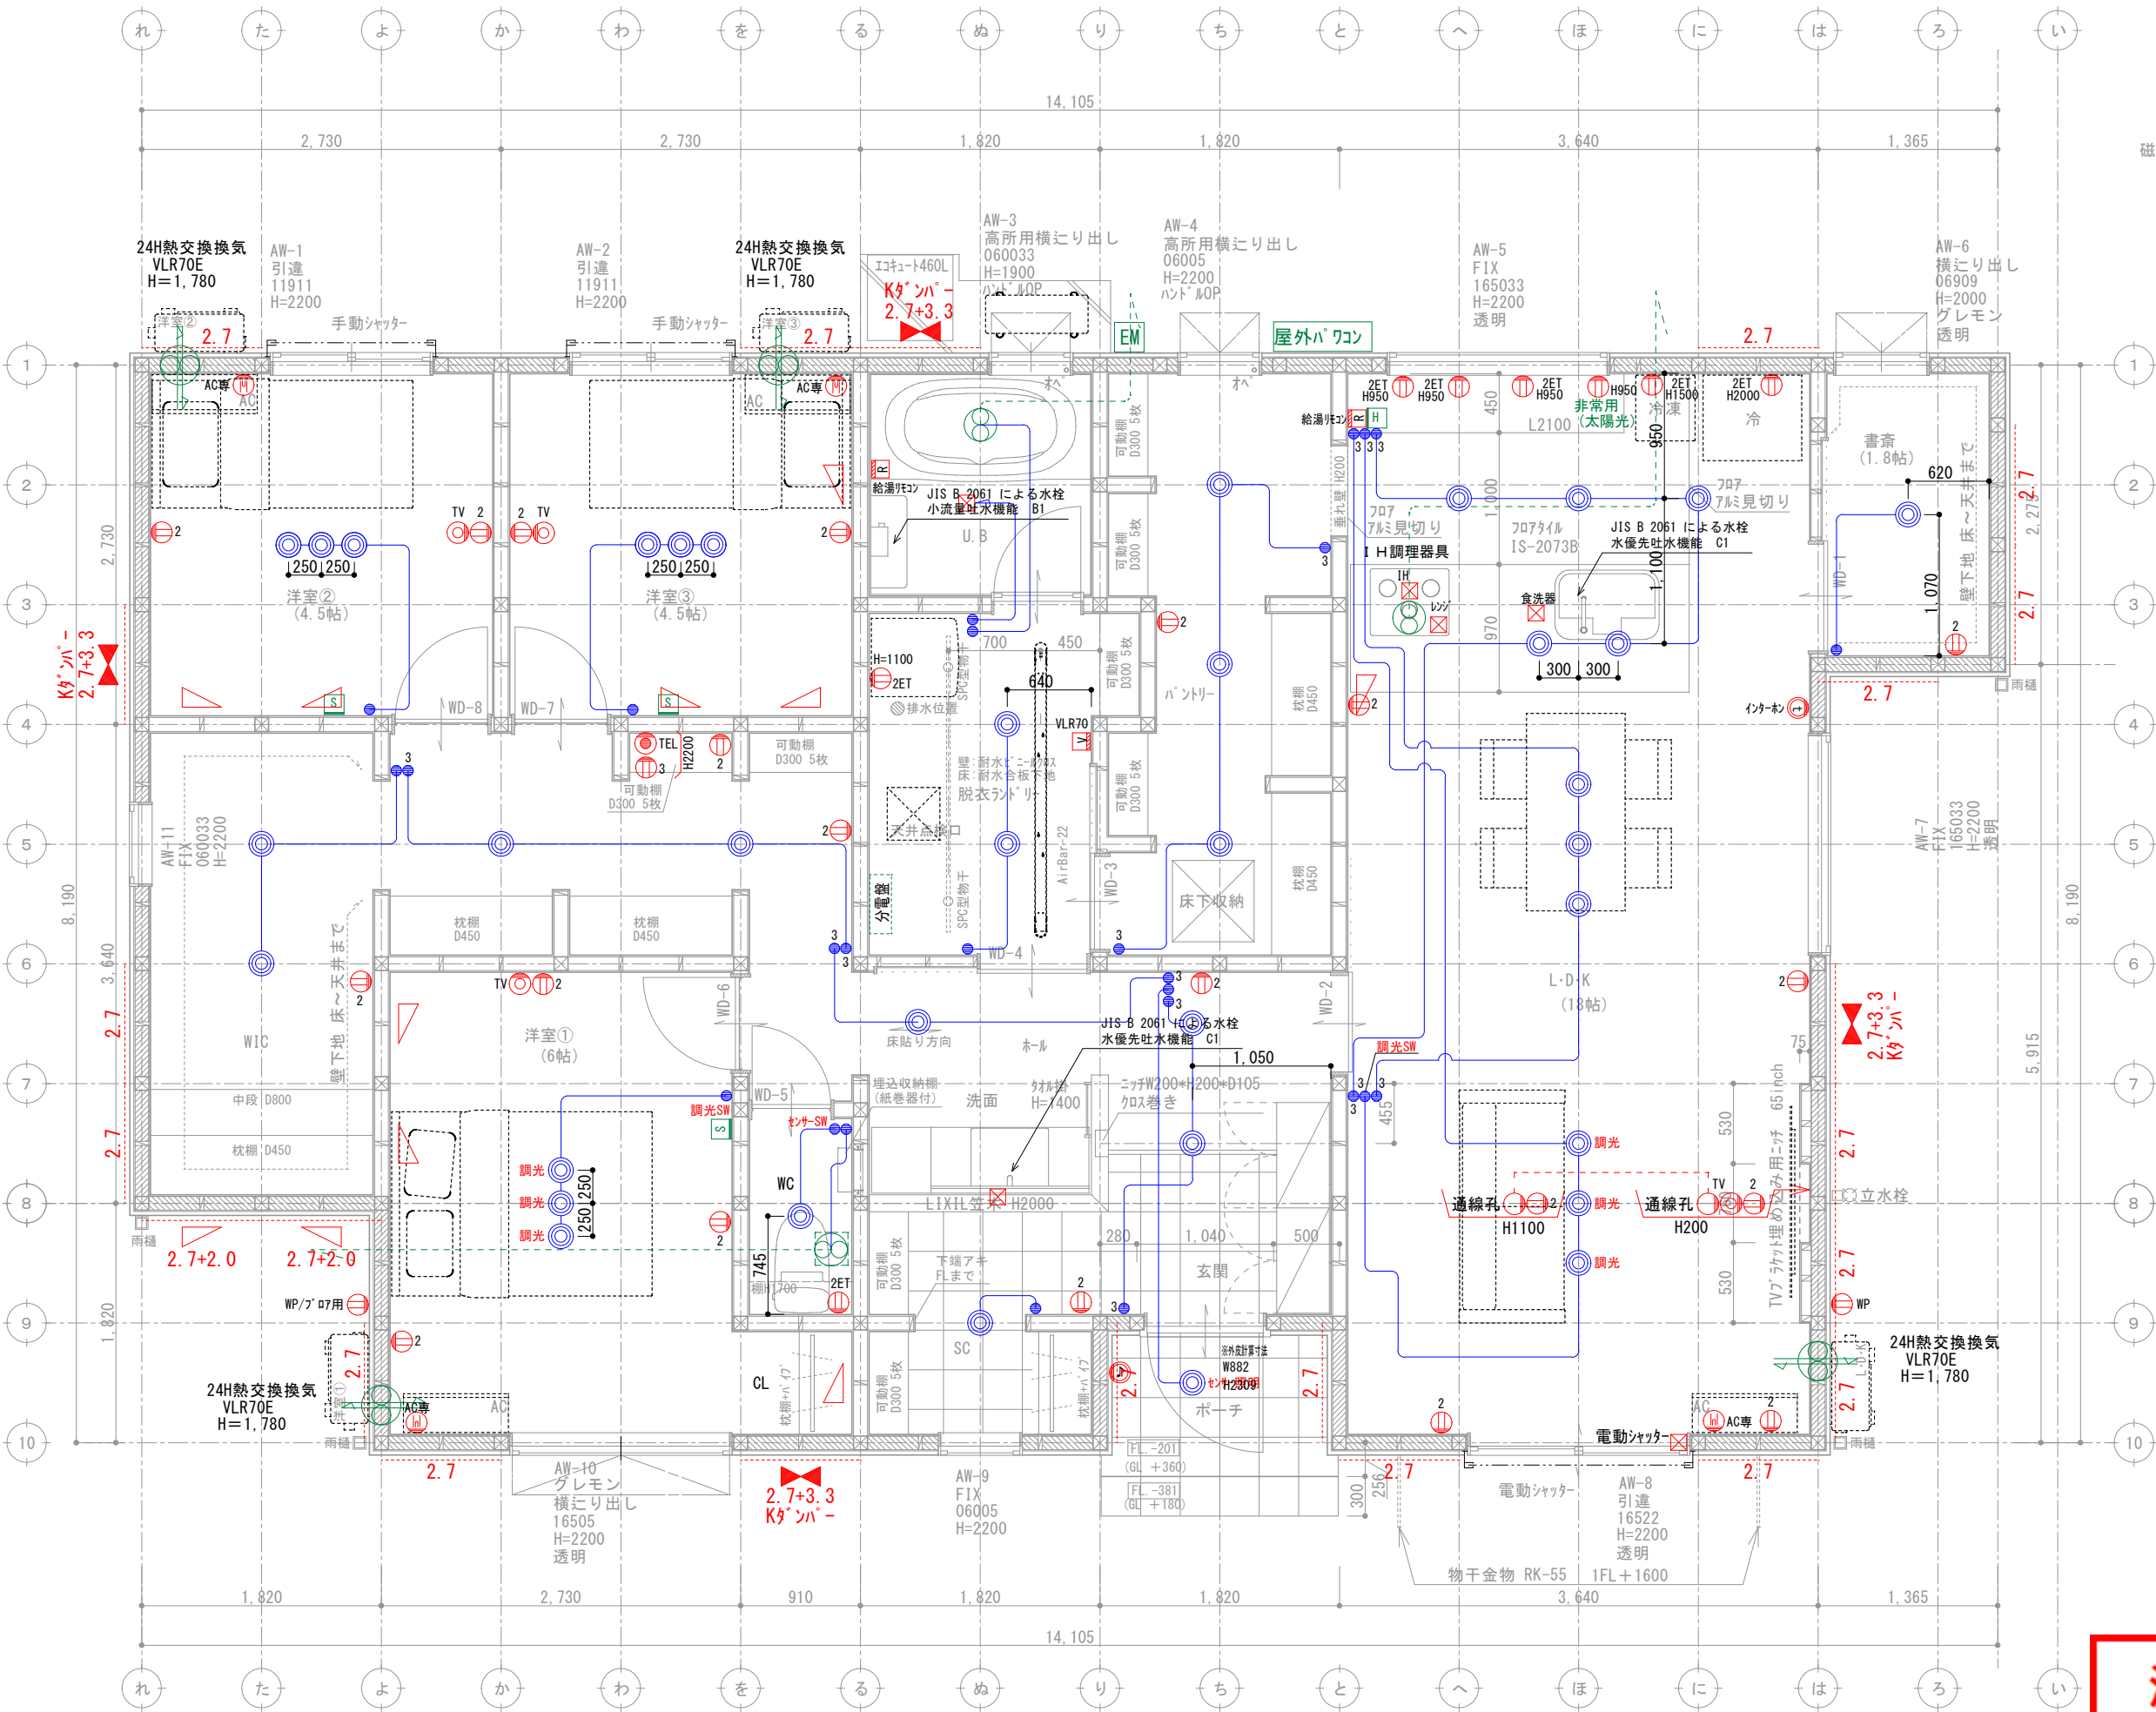

G2

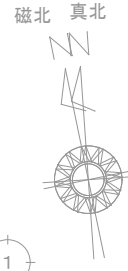

壁付け 住宅用火災報知器			数量
H	熱感知器	電池式(単独型)	1
	熱感知器	露出型	
壁付け 住宅用火災報知器			数量
S	煙感知器	電池式(単独型)	3
	煙感知器	露出型	

※ 煙感知器は壁・梁より600mm以上離す
壁に取付ける場合、
天井から150mm以上500mm以内離す
換気扇・エアコン吹出口から1500mm以上離す
※ 全室LED照明とする。
※ 標準天井高さ2,400
※ 特記無きガラスは型ガラス

- * 凡例**
- 管柱 (105×105)
 - Kタンパー (3.30倍 FRM-0641)
 - 片筋違い (2.00倍 45×90)
(例 左:柱脚 右:柱頭)
 - たすき掛筋違い (4.00倍 45×90)
 - 構造用合板 (2.70倍)
(t=9 タタキ EXハイパー)
(標準仕様 2.7倍: FRM-0678)
(入隅仕様 2.7倍: FRM-0734)
 - 床点検口
 - 天井点検口
 - 換気扇
 - 熱交換換気扇 VLR-70


脱衣ランドリー 仕上材
天井: ア9.5PB下地ビニルクロス貼り
壁: ア12.5PB下地ビニルクロス貼り
床: ア24+15耐水合板下地77タイル張り

※給水設備: ヘッダー分岐後の全配管径は13mm以下とする
※照明設備: 全室LED照明とし居室においては調光制御、非居室においては
人感センサーを使用する

- ① 3 コンセント 3ヶ所
- ② 1ET コンセント1ヶ所接地ターミナル付
- ③ 2ET コンセント2ヶ所接地ターミナル付
- ④ WP コンセント 防水型
- ⑤ エアコン用コンセント
- ⑥ 200V用コンセント
- ⑦ WP 防雨入線プレート
- ⑧ スイッチ
- ⑨ 3路スイッチ
- ⑩ 4路スイッチ
- ⑪ 直結電源
- ⑫ TV テレビ取出口
- ⑬ TEL 電話取出口 (テレホンガイド)
- ⑭ LAN LAN取出口 (テレホンガイド)
- ⑮ 壁照明
- ⑯ リモコン (給湯関係・ルフロ)
- ⑰ メーター
- ⑱ 分電盤
- ⑲ チャイム

※ACコンセント天井付け
※TVアンテナ工事
※スイッチはFL+1100、コンセントはFL+200

決定図

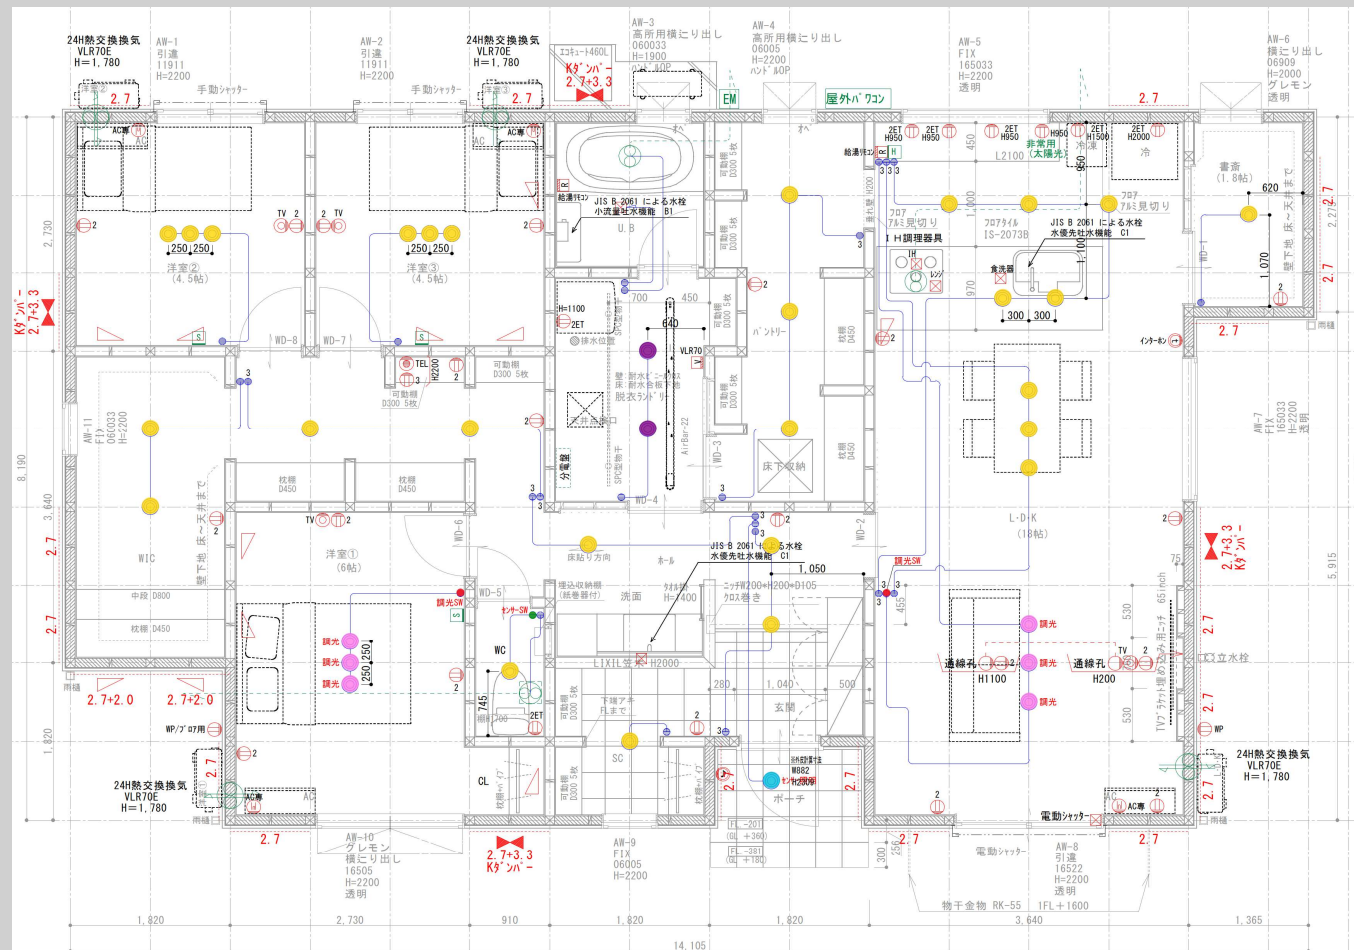

1階

ト アホン: VL-SZ30KL
(Panasonic)



ポーチ灯

● $\times 1$

センサー付きタ ウンライト

DDL_4496YB



基本照明ダ ウンライト

● $\times 27$

DDL_6102YW



脱衣ランドリー

● $\times 2$

ダウライト

DDL_6102AW



LDK、洋室①

● $\times 6$

調光ダウナイト

DDL_6002YWG



LDK、洋室①

● $\times 2$

調光SW

WTA_57583WK



トイレ


● $\times 1$

センサー-SW

WTA_14119W



外部：スマートデザインシリーズ
ブラック

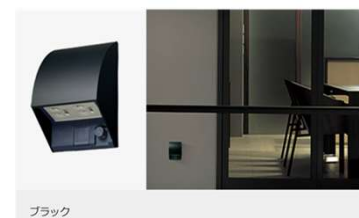

決定図

2025.7.11


(図面 7-3)

PG House

南 頼伸様・日香梨様

邸新築工事

Lighting Plan

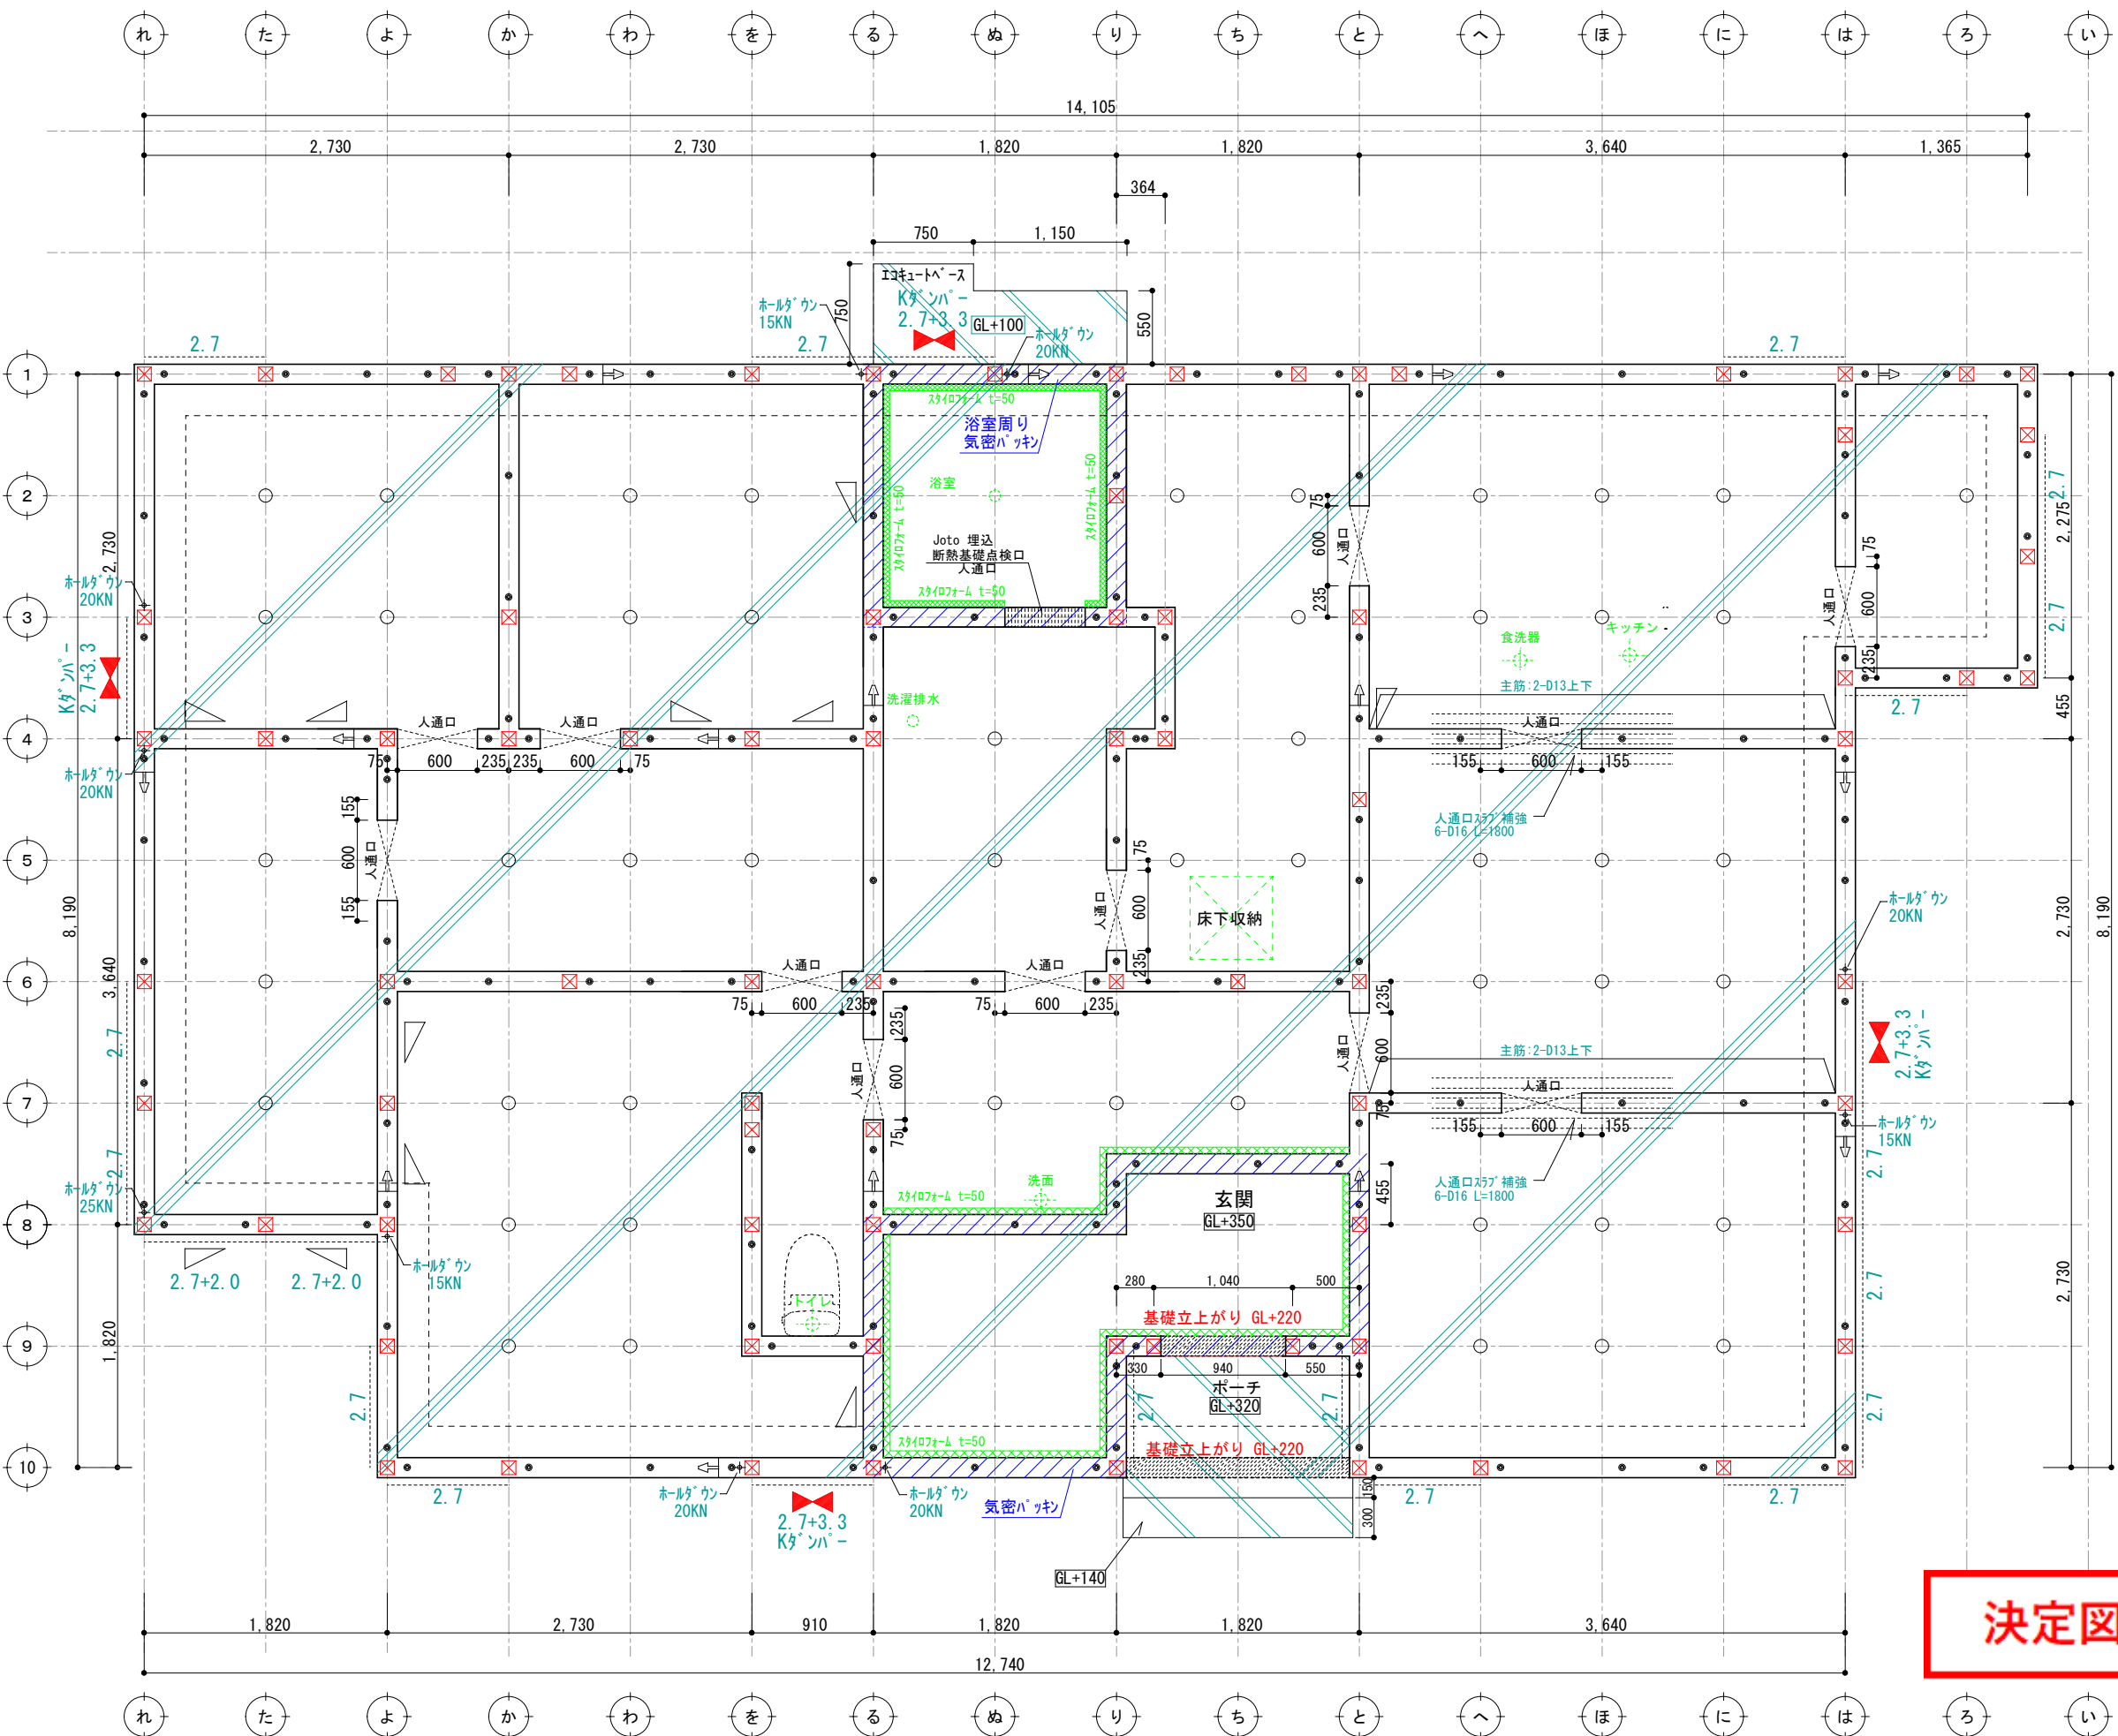


G2

構造体ベースコンクリート t=150

後打ち土間コン

アンカーボルトの配置
土台切れの箇所より150mm
土台の継手及び仕口の端部より150mm
耐力壁の端部、筋交いの脚部より150mm
1.82m以下の間隔
250mm以上埋込み
基礎天端より120mm


筋かい凡例
柱脚 柱頭 片筋かい
たすき掛け筋かい
構造用パネル

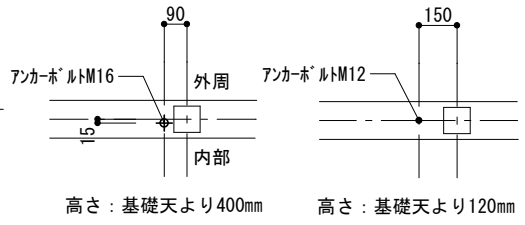


高さ：基礎天より400mm 高さ：基礎天より120mm
ホールダウン用アンカーボルト配置 アンカーボルト配置

- 凡例
- 通し柱 (105*105) 管柱 (105*105)
 - アンカーボルトM12 L=400
 - + ホールダウンアンカーM16 L=800
柱芯より90mm 280mm以上埋め込み
(カナフリストアンカーボルトM16)
 - ⊕ 鋼製束
 - 土台ジョイント
 - ▨ ベースコンクリート (t=150)
 - ▨ 後打ちコンクリート

- 基礎伏図について特記なき場合に限り下記による。
1. コンクリート：呼び強度 21N/mm²
 2. 鉄筋：SD295A
 3. 設計地耐力： $f_e=20\text{kN/m}^2$
地耐力計測後、不足の場合は相当の改良を行い、満たすものとする。
 4. 基礎の位置は、芯振分けとする。
 5. 玄関・S/C・UB周囲の基礎天端は気密パッキン施工（網掛け部）とし、その他の基礎天端は基礎パッキン施工とする。
 6. 設備配管の屋内への取り入れは基礎立上り部のスリーブによる。

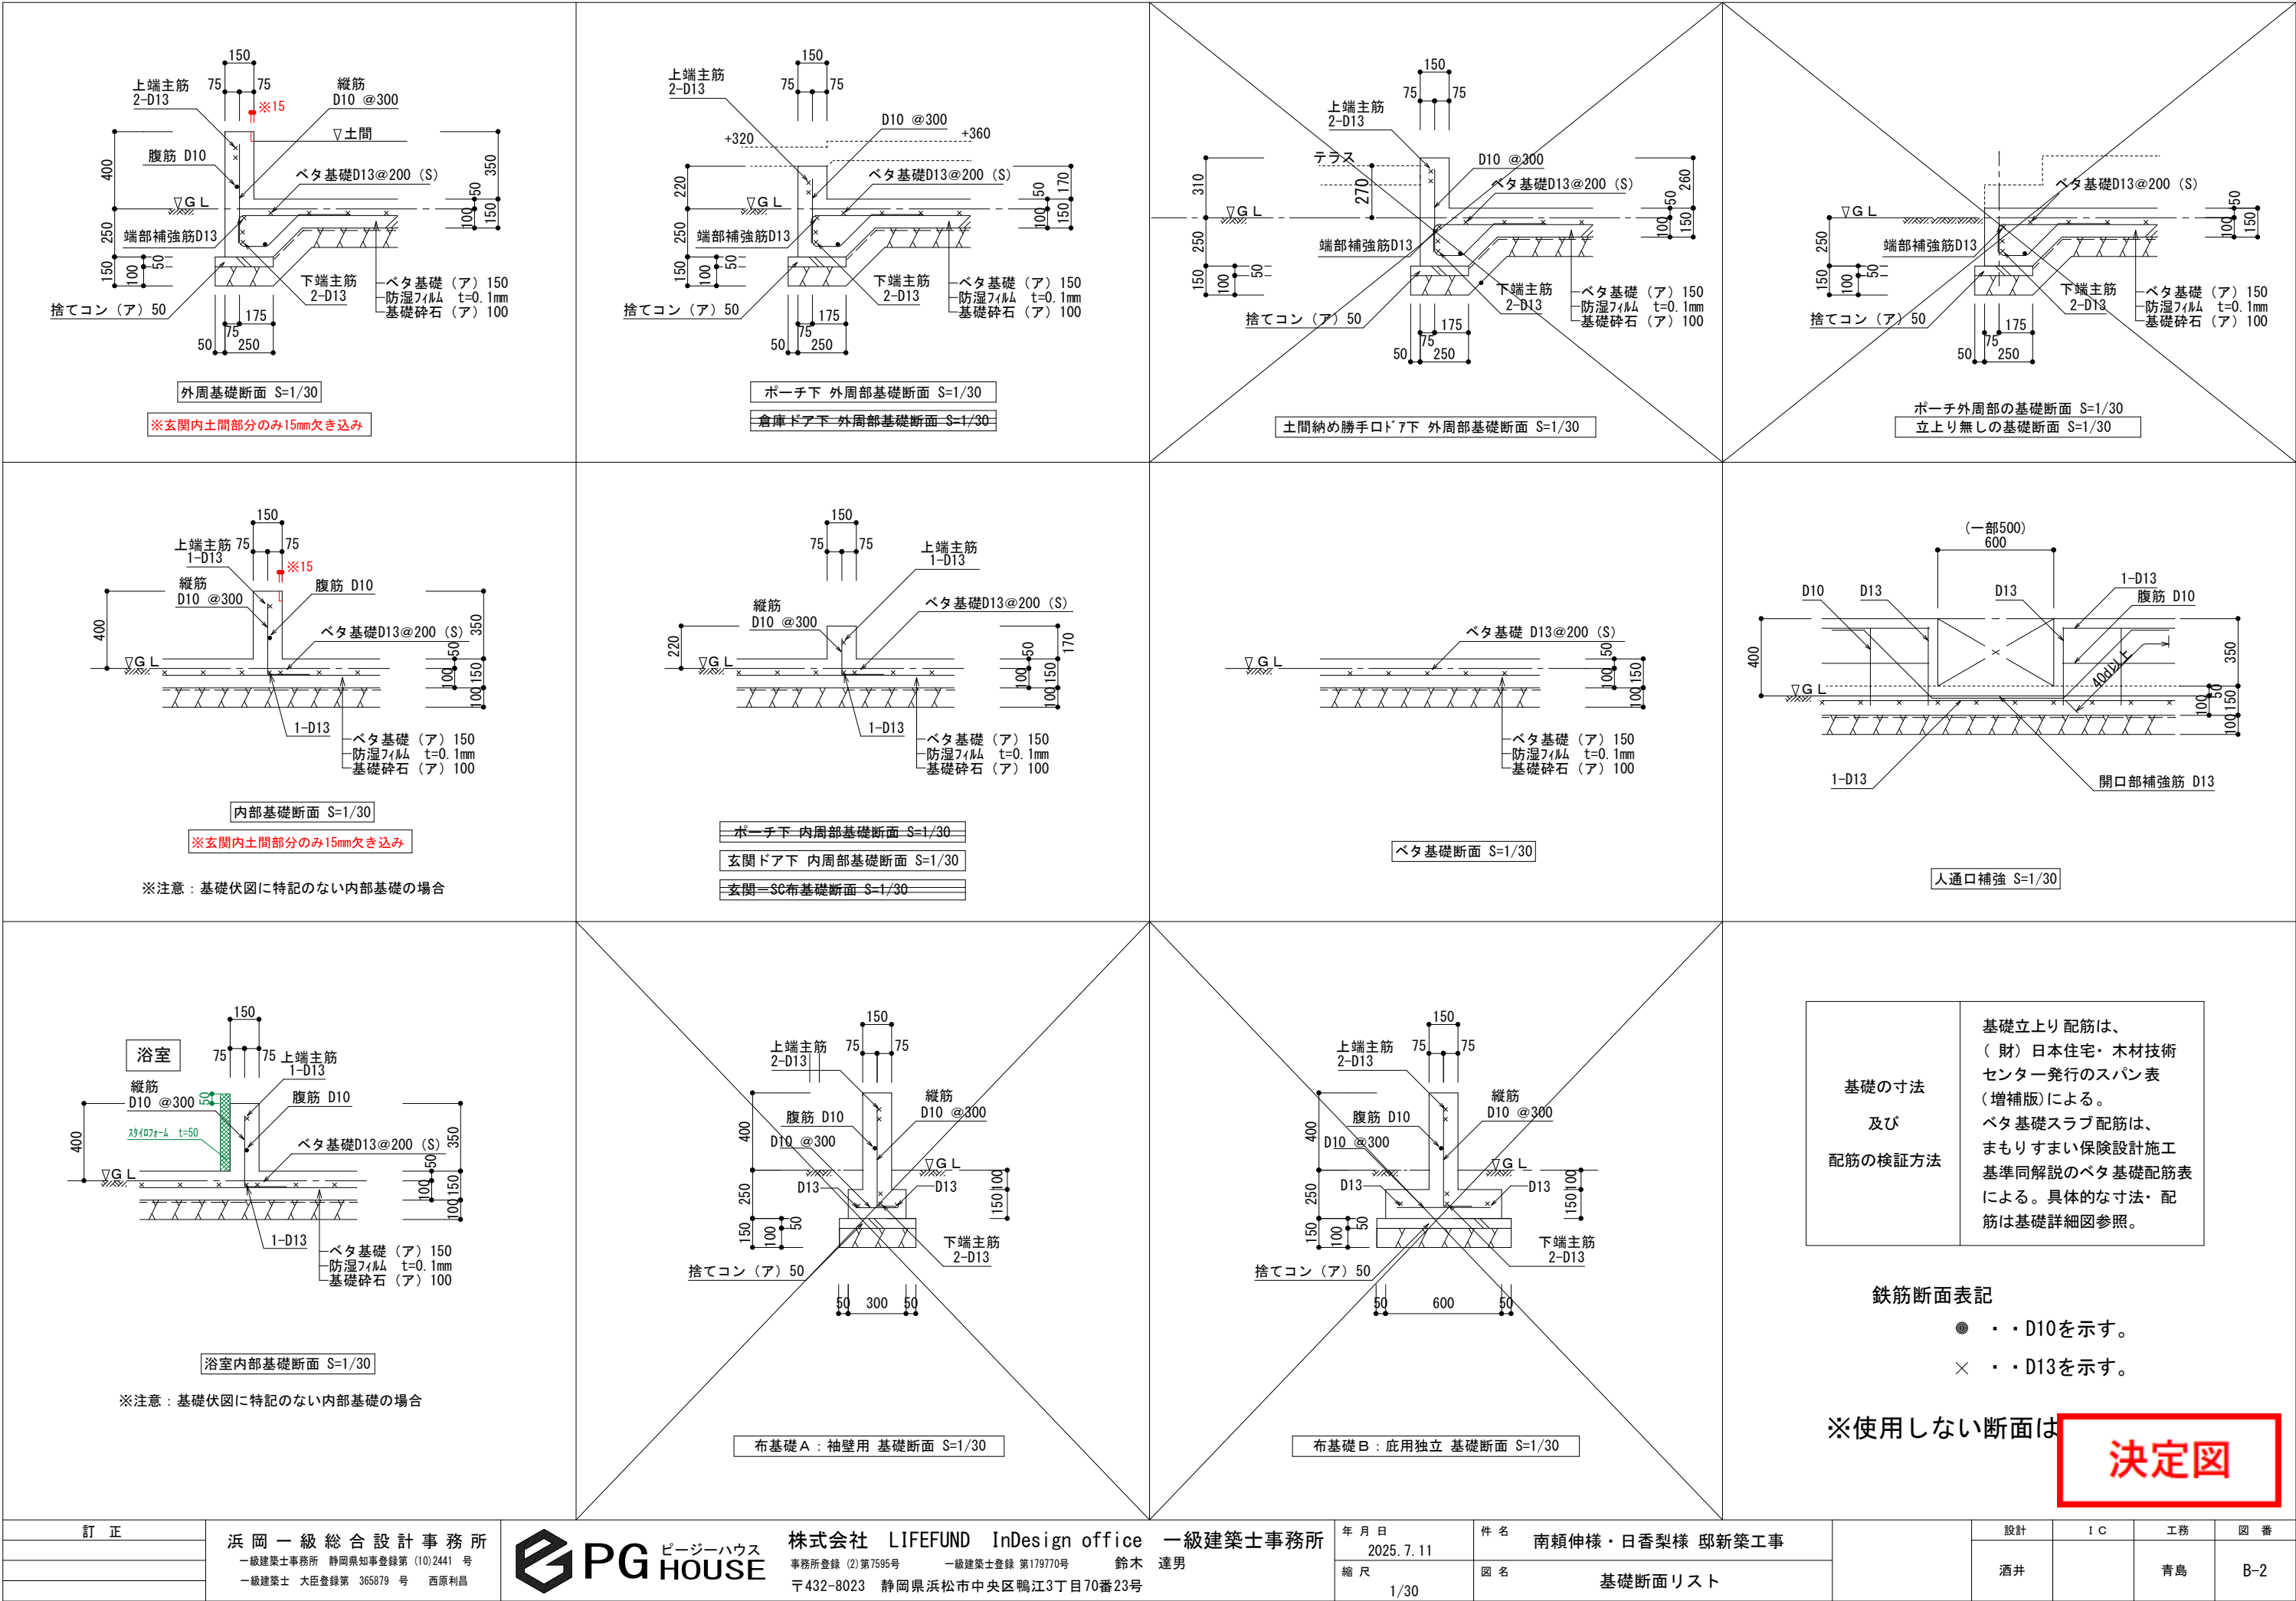

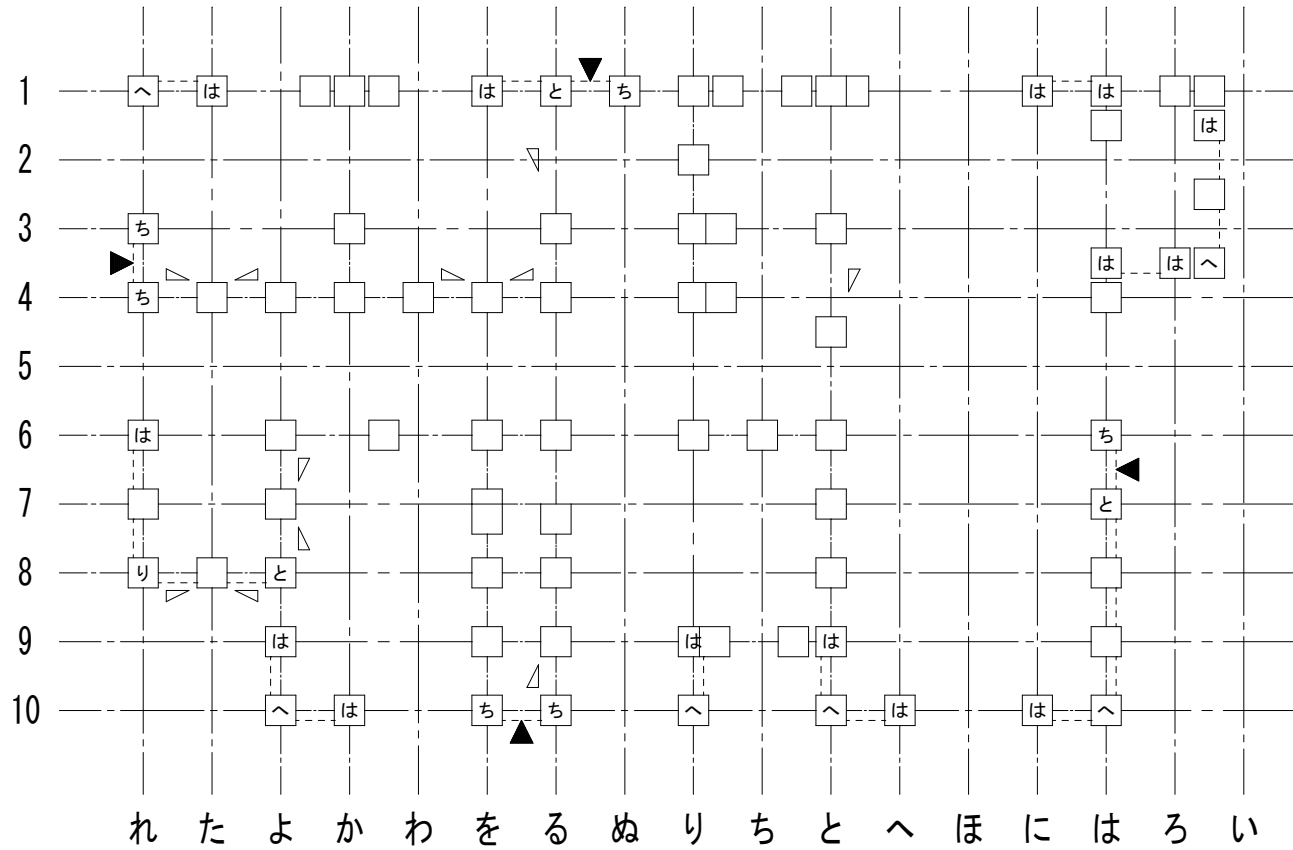

1 階柱壁伏図

接合部凡例				*接合部凡例はユーザ設定されたものです。	
記号	仕様（カナイ金物）		N	倍率	
SBCP	スリムビルドコーナー75, チビクリCK (化粧柱の場合)		0.00	1.00	
SBCP	スリムビルドコーナー75, チビクリCK (化粧柱の場合)		0.65	1.00	
SBCP	は	スリムビルドコーナー75	1.00	1.00	
ARCG	に	アレントコーナー合板用	1.40	2.20	
ARCG	ほ	アレントコーナー合板用	1.60	2.20	
ARCG	へ	アレントコーナー合板用	1.80	2.20	
HD15	と	ブレイブホールダウン B-HD15	2.80	3.60	
HD20	ち	ブレイブホールダウン B-HD20	3.70	4.70	
HD25	り	ブレイブホールダウン B-HD25	4.70	4.80	
HD30	ぬ	ブレイブホールダウン B-HD30	5.60	7.20	
J1	る	腰掛け蟻若しくは大入れ蟻掛け+羽子板*ルト、短冊金物		1.90	梁継手・仕口用 梁継手・仕口用
J2	を	腰掛け蟻若しくは大入れ蟻掛け+羽子板*ルト、短冊金物×2		3.00	

※表示なき金物は「は」とする。

接合部凡例				*接合部凡例はユーザ設定されたものです。	
記号	仕様（タナカ金物）		N	倍率	
FCP	フックコーナー, チビクリCK (化粧柱の場合)		0.00	1.00	
FCP	フックコーナー, チビクリCK (化粧柱の場合)		0.65	1.00	
FCP	は	フックコーナー	1.00	1.00	
CCP	に	シナコーナー	1.40	2.20	
CCP	ほ	シナコーナー	1.60	2.20	
CCP	へ	シナコーナー	1.80	2.20	
HD15	と	ビス止めホールダウンU HD15	2.80	3.60	
HD20	ち	ビス止めホールダウンU HD20	3.70	4.70	
HD25	り	ビス止めホールダウンU HD25	4.70	4.80	
HD30	ぬ	ビス止めホールダウンU HD15×2 (HD35)	5.60	7.20	
J1	る	腰掛け蟻若しくは大入れ蟻掛け+羽子板*ルト、短冊金物		1.90	梁継手・仕口用 梁継手・仕口用
J2	を	腰掛け蟻若しくは大入れ蟻掛け+羽子板*ルト、短冊金物×2		3.00	

※表示なき金物は「は」とする。

筋かいの種類に応じた筋かいの端部の接合部の仕様		
	筋かいの種類	接合部の仕様（構造方法）
イ	鉄筋φ9	柱又は横架材を貫通し、三角座金を介してナット締め、又は鋼板添え板を用い鋼板を柱及び横架材にCN90, 8本平打ち
ロ	筋かい:15×90	柱・横架材を欠き込み、柱・横架材双方に対してN65, 5本平打ち
ハ	筋かい:30×90	鋼板添え板t=1.6mmを筋かいに対してボルトφ12及びCN65, 3本平打ち、柱に対してCN65, 3本平打ち、横架材に対してCN65, 4本平打ち。筋かいプレートBP同等品
ニ	筋かい:45×90	鋼板添え板t=2.3mmを筋かいに対してボルトφ12及びスクリュー釘φ4.5L50, 7本平打ち、柱及び横架材に対してスクリュー釘φ4.5L50, 5本平打ち。筋かいプレートBP-2同等品
ホ	筋かい:90×90	柱又は横架材にボルトφ12mmを用いて一面剪断接合

胴差と通し柱の接合部の仕様		
	胴差と通し柱の条件	仕口
T1	通し柱の片側に胴差が来る場合	胴差を柱にかたぎ大入れ短ほぞ差しの上、羽子板ボルト、かね折り金物又は同等以上の仕口
T2	通し柱の両側に胴差が来る場合	胴差を柱にかたぎ大入れ短ほぞ差しの上、短冊金物又は、同等以上の仕口で胴差相互を緊結
T3	通し柱と胴差の接合部の近くに90×90以上の筋かいが来る場合（通し柱が建物の出隅にあるか、筋かい壁が外壁と直交して接する場合）	胴差を通し柱に、15KN用引き寄せ金物を水平に用いて緊結

決定図

707貼り分け指示書

G2

壁付け 住宅用火災報知器			数量
H	熱感知器	電池式(単独型)	1
	熱感知器	露出型	
壁付け 住宅用火災報知器			数量
S	煙感知器	電池式(単独型)	1
	煙感知器	露出型	

- ※ 煙感知器は壁・梁より600mm以上離す
壁に取付ける場合、
天井から150mm以上500mm以内離す
換気扇・エアコン吹出口から1500mm以上離す
- ※ 全室LED照明とする。
- ※ 標準天井高さ2,400
- ※ 特記無きガラスは型ガラス

* 凡例

- ☒ 管柱 (105×105)
- ◀▶ Kダクト (3.30倍 FRM-0641)
- △ 片筋違い (2.00倍 45×90)
(例 左:柱脚 右:柱頭)
- ⊠ たすき掛筋違い (4.00倍 45×90)
- 構造用合板 (2.70倍)
(t=9 9材 EXハイパー)
- ◻ 床点検口
- ⊠ 天井点検口
- ⊙ 換気扇
- ⊙ 熱交換換気扇VLR-70

アドバンスシリーズ

スマートデザイン (外部)

- 凡例
- ① コンセント 1ヶ所
 - ② コンセント 2ヶ所
 - ③ コンセント 3ヶ所
 - ④ ET コンセント1ヶ所接地ターミナル付
 - ⑤ ET コンセント2ヶ所接地ターミナル付
 - WP コンセント 防水型
 - エアコン用コンセント
 - 200V用コンセント
 - WP 防雨入線プレート
 - スイッチ
 - 3路スイッチ
 - 4路スイッチ
 - 直結電源
 - TV テレビ取出口
 - TEL 電話取出口 (テレホンガイド)
 - LAN LAN取出口 (テレホンガイド)
 - 壁照明
 - リモコン (給湯関係・ルフロ)
 - メーター
 - 分電盤
 - チャイム

- ※ACコンセント天井付け
- ※TVアンテナ工事
- ※スイッチはFL+1100、コンセントはFL+200

決定図

