
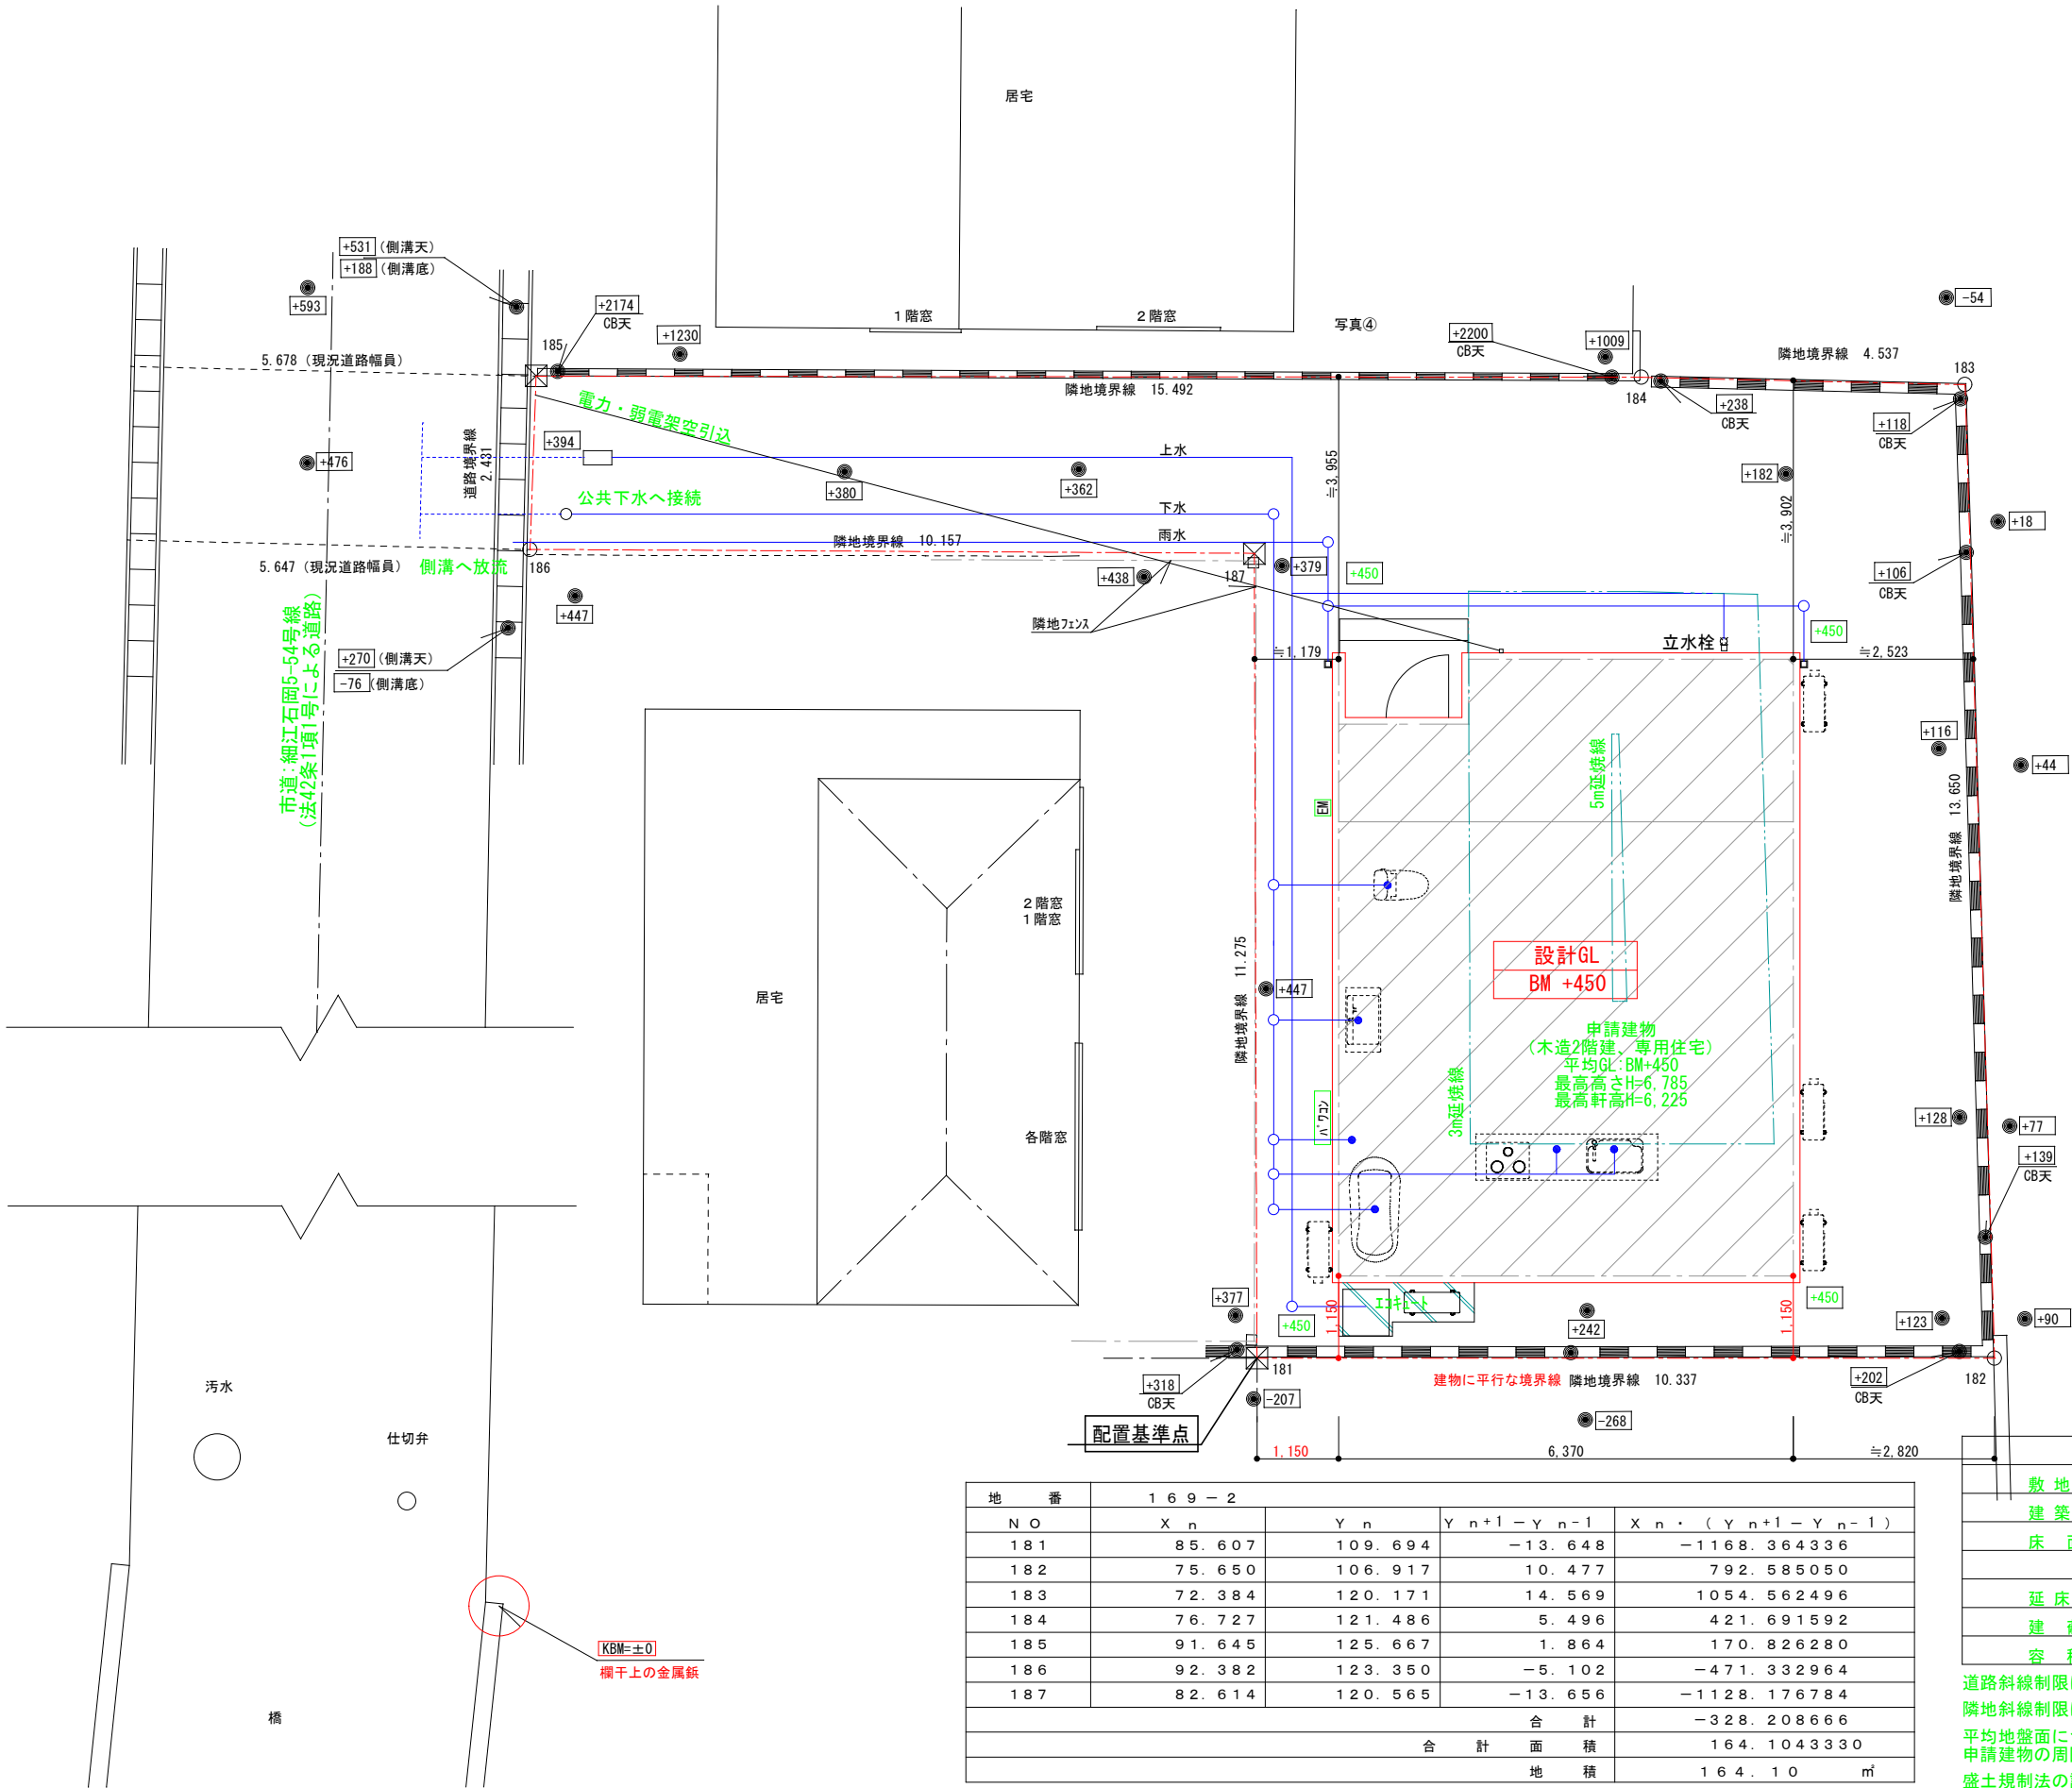


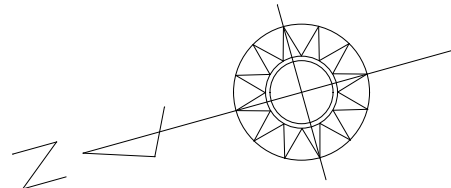

決定図

地 番	1 6 9 - 2				
N O	X _n	Y _n	Y _{n+1} - Y _{n-1}	X _n × (Y _{n+1} - Y _{n-1})	
1 8 1	8 5 . 6 0 7	1 0 9 . 6 9 4	- 1 3 . 6 4 8	- 1 1 6 8 . 3 6 4 3 3 6	
1 8 2	7 5 . 6 5 0	1 0 6 . 9 1 7	1 0 . 4 7 7	7 9 2 . 5 8 5 0 5 0	
1 8 3	7 2 . 3 8 4	1 2 0 . 1 7 1	1 4 . 5 6 9	1 0 5 4 . 5 6 2 4 9 6	
1 8 4	7 6 . 7 2 7	1 2 1 . 4 8 6	5 . 4 9 6	4 2 1 . 6 9 1 5 9 2	
1 8 5	9 1 . 6 4 5	1 2 5 . 6 6 7	1 . 8 6 4	1 7 0 . 8 2 6 2 8 0	
1 8 6	9 2 . 3 8 2	1 2 3 . 3 5 0	- 5 . 1 0 2	- 4 7 1 . 3 3 2 9 6 4	
1 8 7	8 2 . 6 1 4	1 2 0 . 5 6 5	- 1 3 . 6 5 6	- 1 1 2 8 . 1 7 6 7 8 4	
合 計				- 3 2 8 . 2 0 8 6 6 6	
合 計 面 積				1 6 4 . 1 0 4 3 3 3 0	
地 積				1 6 4 . 1 0 m ²	

トータル面積表		(㎡)
敷地面積		164.10
建築面積		55.06
床面積	1階	53.41
	2階	55.06
延床面積		108.47
建蔽率	(55.06/164.10) × 100	33.56%
容積率	(108.47/164.10) × 100	66.10%

道路斜線制限については、明らかに適合する。
隣地斜線制限については、明らかに適合する。
平均地盤面について
申請建物の周囲の平均地盤面高さをBM+450とする。
盛土規制法の許可対象となる工事なし。