


【注意】


- 壁面仕上材（キッチンパネル・タイルなど）の貼付下端位置が変わります。 [機能図参照]
- 記載のキャビネット寸法は扉前面での呼び寸法です。キャビネット本体の寸法・扉厚等は商品ガイドの巻末資料をご確認ください。
- 記載のワークトップ、カウンター、エンドパネル、サイドパネルの寸法は呼び寸法です。詳細寸法は商品ガイドの巻末資料をご確認ください。
- レンジフード電源プラグ仕様：2芯電源プラグ（アース工が必要です。）

案件No.	図面名	担当	図面	図番 : 株式会社 LIXIL
A2503DDDD0EGDPJ	レイアウト図	栗野 友仁		
見積No.	縮尺	日付		
M25047301367-009-2	1/30	2025.06.03		

B面

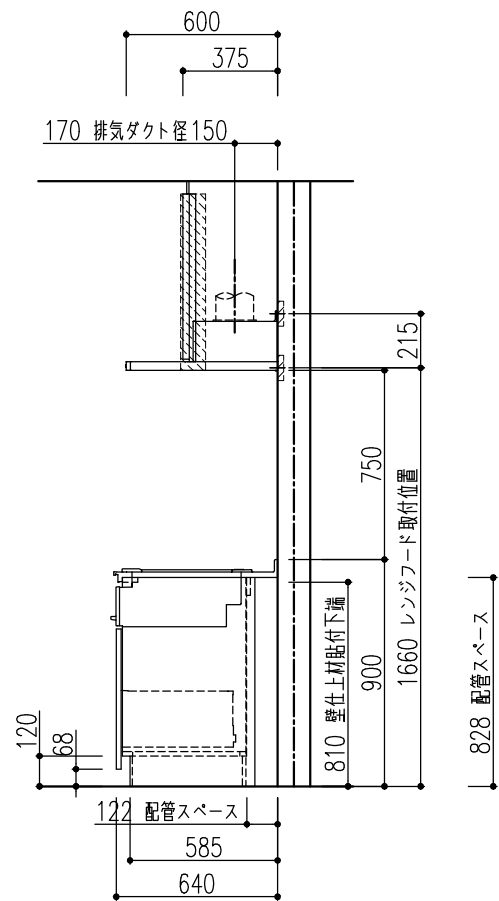

C面

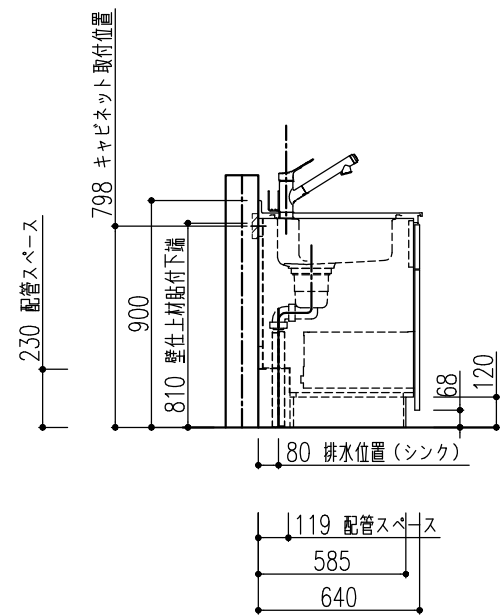


	特記事項 扉色 VK5:グレージュスタック 取手 [R]スリム取手 (シャインニッケル) ワークトップカラー 【DW】 ソルティホワイト	物件名	山 寄 悟 様 邸	案件No.	図面名	担当	図面	図番
				A2503DDD0EGDPJ	納まり図	栗野 友仁		
		仕様	ES21	見積No.	縮尺	日付		
				M25047301367-009-2	1/30	2025.06.03		

株式会社 LIXIL

■壁面仕上材（キッチンパネル）取付注意事項〔貼付向き〕

●キッチンパネルの貼付向き

キッチンパネルの貼付向きにご注意ください。

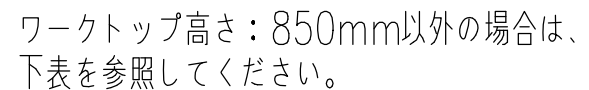

ワークトップ高さ	キッチンパネル 貼付下端位置
900	860
875	835
825	785
800	760

●上表はキッチンパネルの場合です。ステンレスパネルの場合は、キッチンパネルの「取付・設置説明書」を参照してください。

【単位：mm】

ワークトップ高 850 (ワークトップ高)

壁面寸法 800 (壁面寸法)

レンジフード高 700 (レンジフード高)

クイックポケット・クイックパレット高 620 (クイックポケット・パレット用キャビ高さ)

レンジフード

ウォールキャビ (開き扉)

クイックポケット
クイックパレット

横 貼り

縦 貼り


フロアキャビ

《バックガード：なし、ワークトップ高さ：850mm、ウォールキャビ高さ：700mmの場合》


	ウォールキャビ		
	開き扉		クイックボケット クイックバレット
	H700	H600 H500	H700 (620) H600 (520)
キッチンパネル 貼付方向	横	縦	

【ご注意】
リシエル以外のクイックパレットは、
キャビネットの背板高さがショート
（-80mm）してありませんので、
『開き扉』のキッチンパネル貼付方向
に合せてください。


■レンジフード取付注意事項（壁面取付時）

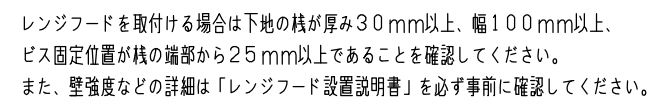


取付位置については、取付設置図を確認してください。

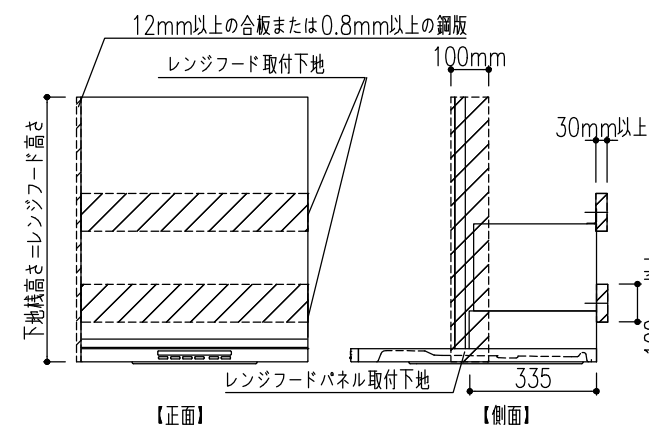

参考図 FED、HVR、NSDシリーズ（サイドマントルタイプ）

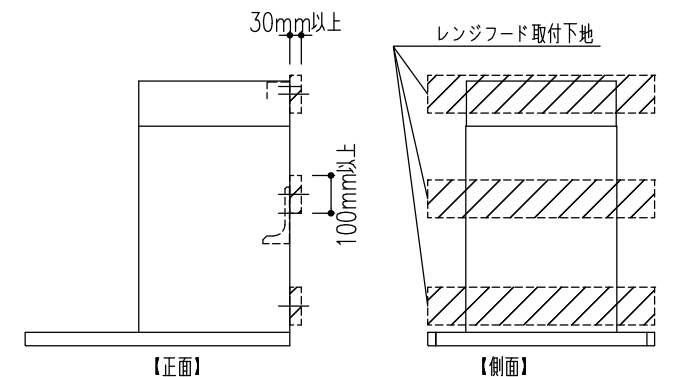

参考図 NBHシリーズ

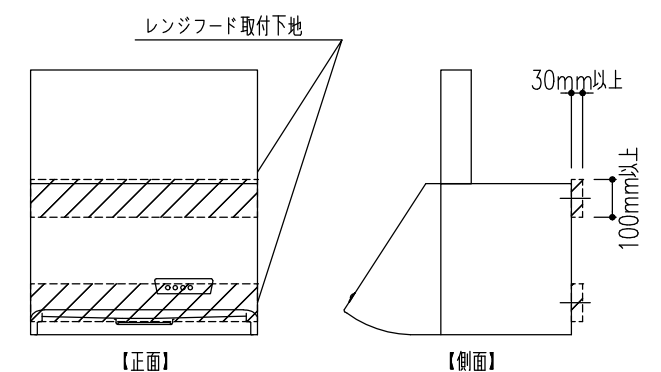


※キャビネット取付時には不陸調整スペーサー等で水平になるように設置してください。


特記事項 扉色 VK5:グレージュスタック 取手 [R]スリム取手（シャインニッケル） ワークトップカラー 【DW】ソルティホワイト	物件名	山 寄 悟 様 邸	案件No.	図面名	担当	図面	図番：
			A2503DD00EGDPJ	機能図	栗野 友仁		
	仕様	ES21	見積No.	縮尺	日付		株式会社 LIXIL
			M25047301367-009-2		2025.06.03		

■天井フィラーの取付（レンジフード上部）

レンジフード横に壁がくるレイアウト時は、横壁にも取付桎が必要になります。

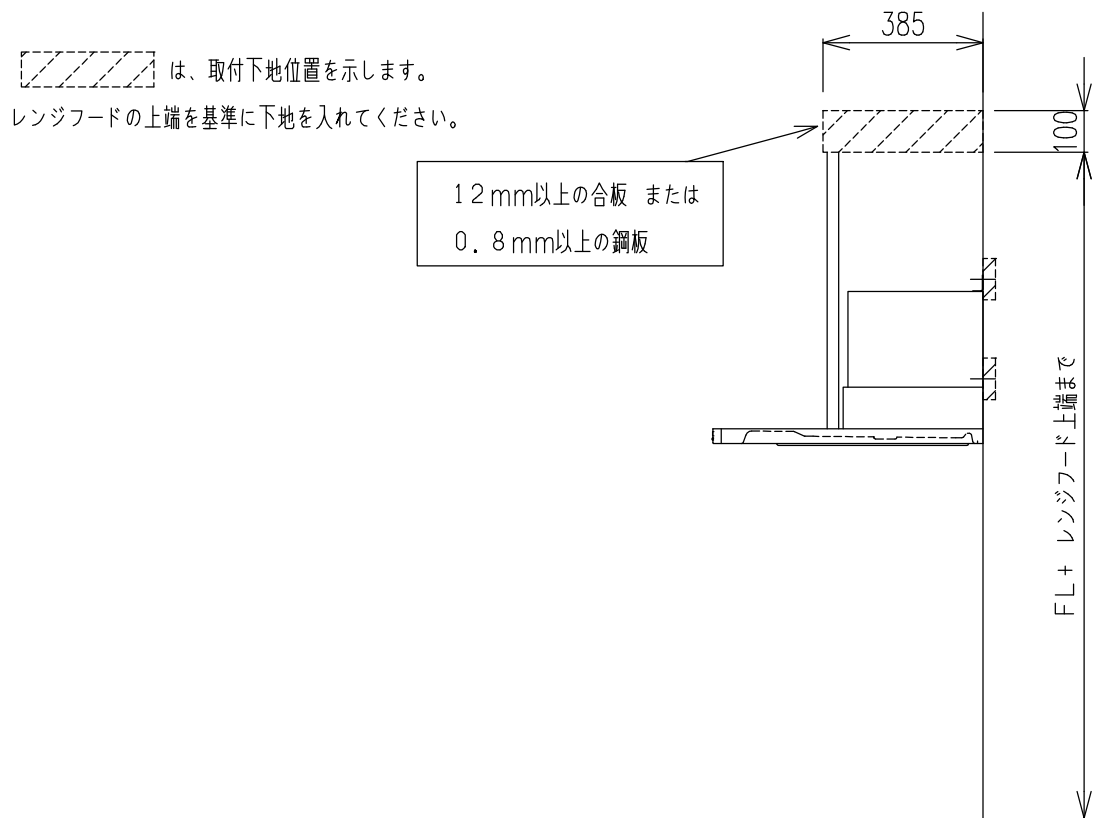

■ ASRフード

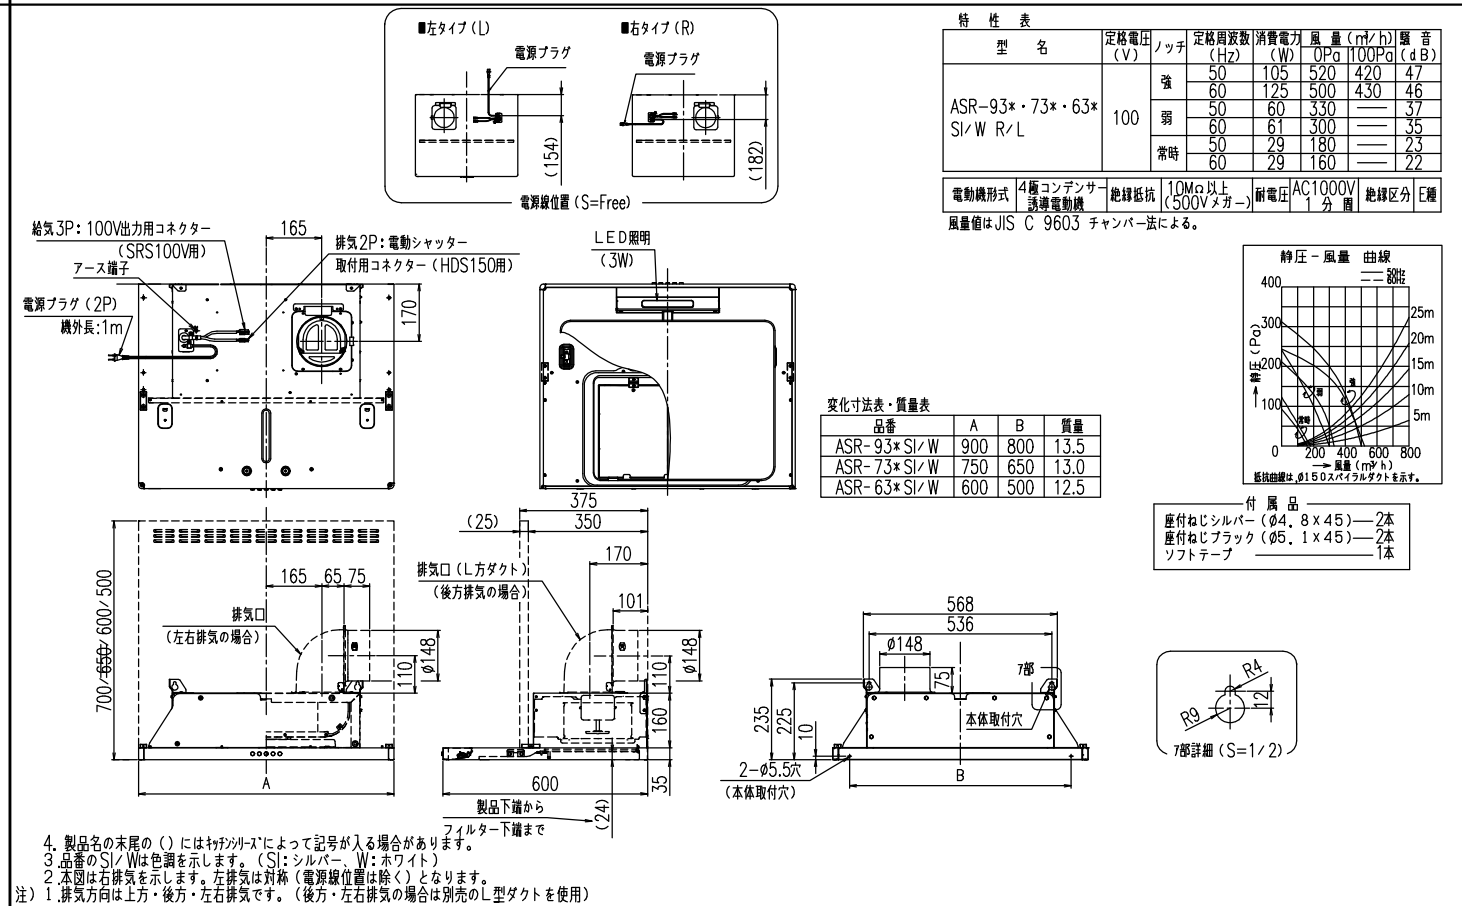


■ IHヒーター用コンセント推奨位置図 / 壁付設置の場合

※コンセントや電源プラグが、引き出しおよびIHヒーター用仕切板（オプション）に接触しないように注意してください。


※木製キャビネットの配管スペース付キャビネットを使用する場合は点検口裏の配管スペース内にコンセントを設置してください。

キッチン高さ	電源線高さ
800	400
850	450
900	500

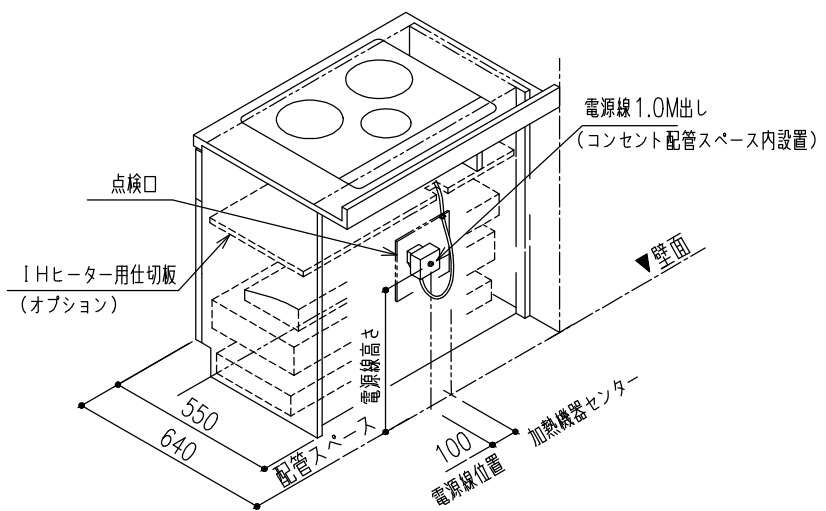

注意：引き出しおよびIHヒーター用仕切板（オプション）に接触しないように上記寸法を参照してください。

■食器洗い乾燥機内配管図 床立上げ配管例

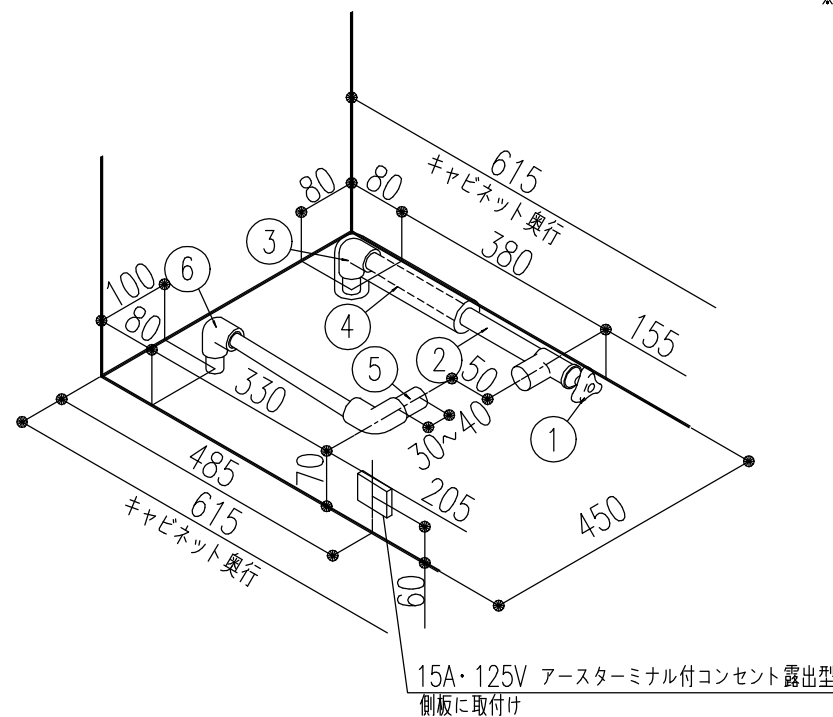

注意：配管立ち上げ位置は必ず本図の位置に立ち上げて下さい。

※給水接続か給湯接続かお客様に確認したうえで施工願います。

給水（給湯の場合は耐熱配管）

①アンゲル型止水栓（ハンドル式・固定ゴマタイプ）

※必ず固定ゴマタイプをご使用ください。

落としゴマタイプを使用すると、水栓内でコマが移動し、ゴトゴト音を生じる恐れがあります。

②硬質塩化ビニルライニング鋼管（相当品）

③RC1/2ソケット

④断熱材 (Φ48)

排水（耐熱塩ビ使用のこと）

⑤排水パイプHT20

⑥HTエルボ

※配水管先端のエルボを上向きにしないでください。


キャビネットに当たるため、排水ホース折れの原因になります。

特記事項 扉色 VK5:グレンジュスタコ 取手 [R]スリム取手 (シャインニッケル) ワークトップカラー 【DW】ソルティホワイト	物件名	山崎 悟 様邸	案件No. A2503DDD0EGDPJ	図面名 機能図	担当 栗野 友仁	図面	図番 : 株式会社 LIXIL
	仕様	ES21	見積No. M25047301367-009-2	縮尺	日付 2025.06.03		

■ 止水栓図（床立上げ）

床立上げ配管






配管立ち上げ寸法は、止水栓芯までの高さを示しています。

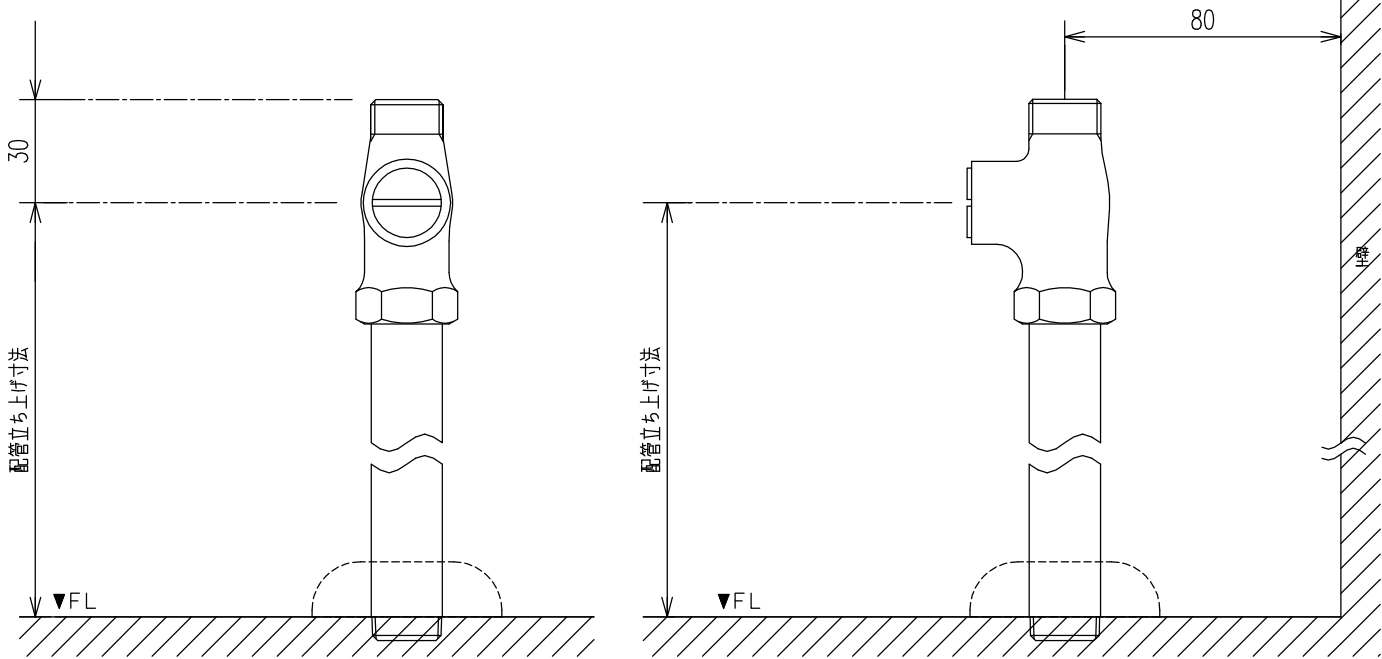

特記事項 扉色 VK5:グレージュスタック 取手 [R]スリム取手（シャインニッケル） ワークトップカラー 【DW】ソルティホワイト	物件名	山 寄 悟 様 邸	案件No.	図面名	担当	図面	図番
			A2503DDD0EGDPJ	機能図	栗野 友仁		株式会社 LIXIL
	仕様	ES 2 1	見積No.	縮尺	日付		
			M25047301367-009-2		2025.06.03		






■ キッチン取付者さま向け 動画コンテンツ ■

商品取付けの注意点を２次元コードでご視聴いただけます。
取付日より前に、是非ご確認ください。

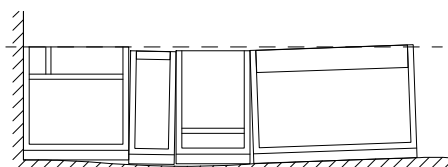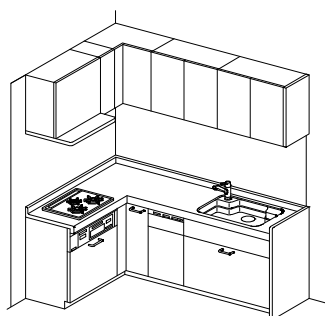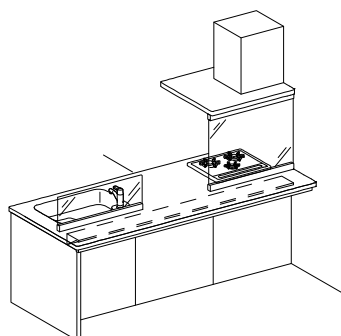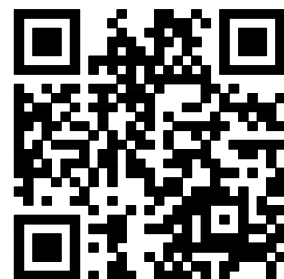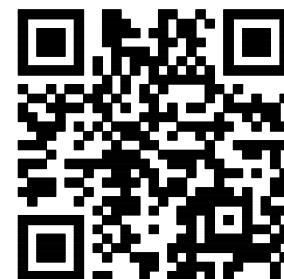荷扱い・搬入		カウンター開梱搬入「養生ツール」		不陸の確認と調整		マグネットキッチンパネル			
荷扱い・搬入		カウンター開梱搬入 「養生ツール」のご紹介				マグネット キッチンパネル 「取付・設置」ポイント			
									
作成日：2024年10月01日		作成日：2024年10月01日		作成日：2024年02月07日		作成日：2024年03月06日			
人造大理石カウンターL型キッチン		センターキッチン（ペニンシュラ型）							
									
									
作成日：2024年02月07日		作成日：2024年02月07日							

■ キッチン取付者さま向け 動画コンテンツ ■

商品取付けの注意点を2次元コードでご視聴いただけます。
取付日より前に、是非ご確認ください。

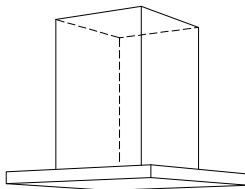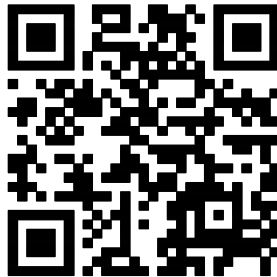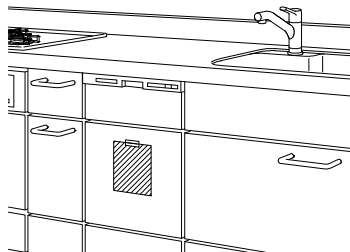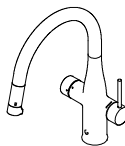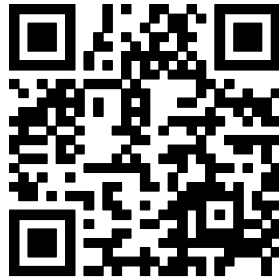センターフード型レンジフード (天吊りフード)  作成日：2024年06月03日 		I H加熱機器関連 I H加熱機器 仕切り板 作成日：2024年02月07日 		食器洗い乾燥機  作成日：2024年02月07日 		ミネラル浄水栓 Greentap  作成日：2024年06月03日 		
特記事項 扉色 VK5:グレージュスタック 取手 [R]スリム取手 (シャインニッケル) ワークトップカラー 【DW】ソルティホワイト		物件名 山寄悟 様邸 仕様 ES21	案件No.		図面名	担当	図面	図番
			A2503DDD0EGDPJ		機能図	栗野 友仁		株式会社 LIXIL
			見積No.		縮尺	日付		
			M25047301367-009-2			2025.06.03		