
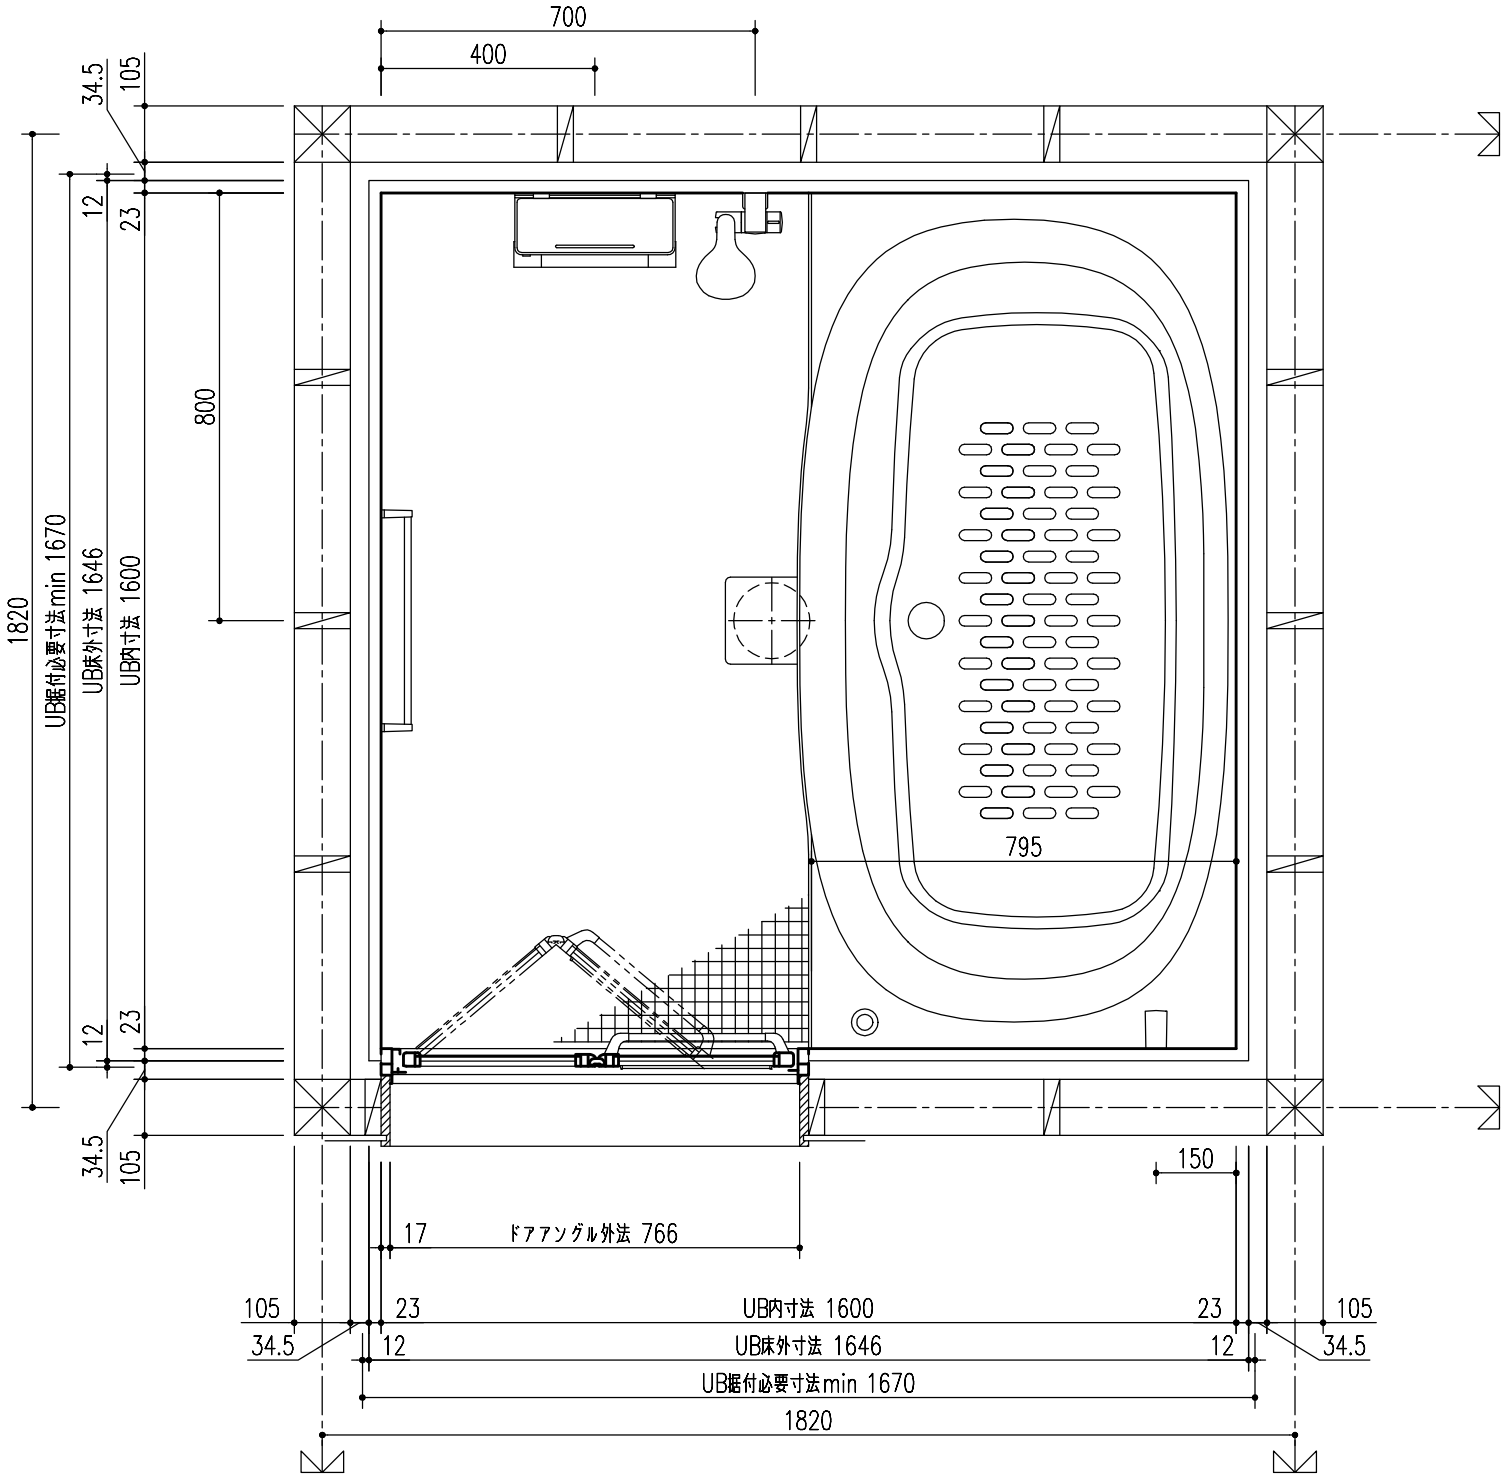


BMUS-1616LBZ-B



部位／項目	仕様（寸法単位：mm）	備考（色柄・品番等）	壁穴加工
床	FRP 単色 バックくるりんボイ排水口	U61	
壁	アクセントパネル(器具面):Lパネル(ハイクラス) ベースパネル:Lパネル(ベーシッククラス)	HT614,LE301	
天井	化粧鋼板複合パネル	UE103	
ドア	折り戸:アルミアルマイト処理(キレイドア) 面 材:型板調樹脂板	VDY-8002006L(81)/WM	
浴槽	FRP ミナモ浴槽(浴槽内法 1501W×802D×480H) プッシュフソウェイ排水栓(メタル調) サーモバスS(浴槽保温材・薄型保温2枚組蓋<ホワイト>) 組蓋フック<ホワイト> エプロン<ホワイト>	NW1	現場開口
水栓金具	洗い場側:壁付サーモ水栓(LS)<ブラック> シャワー:スイッチ付エコアクアシャワー<メタル調-ブラック> メタル調ホース	BF-BD147TX-J12PU/N11. A-10315-PU BF-SL6MBGE(1.7)-PU/N11	
シャワーホースフック	マグネットシャワーホースホルダー<グレー>	SHH-4/N55	
照明	パネルダウンライト(防湿型) 電球色LED 2灯	LE-D1-10A(1.3M)/1L	
タオル掛	アルミパイプ L400 ブラケット:樹脂製	TB-400E-K	現場開口
鏡	防湿型化粧鏡 300W×600H	KGM-3060(1)S	
収納	マグネットシェルフ 300W<ブラック> ※強度上、ポンプボトルのポンプを棚上で押さないでください。	NT-300A(2)-1S/N11	
スライドバー	スライドバー<ホワイト> L800	BF-27B(800)-PU3	現場開口
換気扇	天井換気扇 アルミダクトホース付	UF-27A	
給水管	PJ1/2 おねじ止		
給湯管	PJ1/2 おねじ止		
雑排水管	塩ビ管 VU50		
追いだき	浴槽穴加工φ50 水受けトレイ付		
窓	フリーサイズ窓額縁キット 窓開口補強セット	R-1510P-24/W WR-122S	現場開口
保温仕様	洗い場床防水バン保温 床気密材セット トラップ保温 エプロン保温		

天井見上げ図

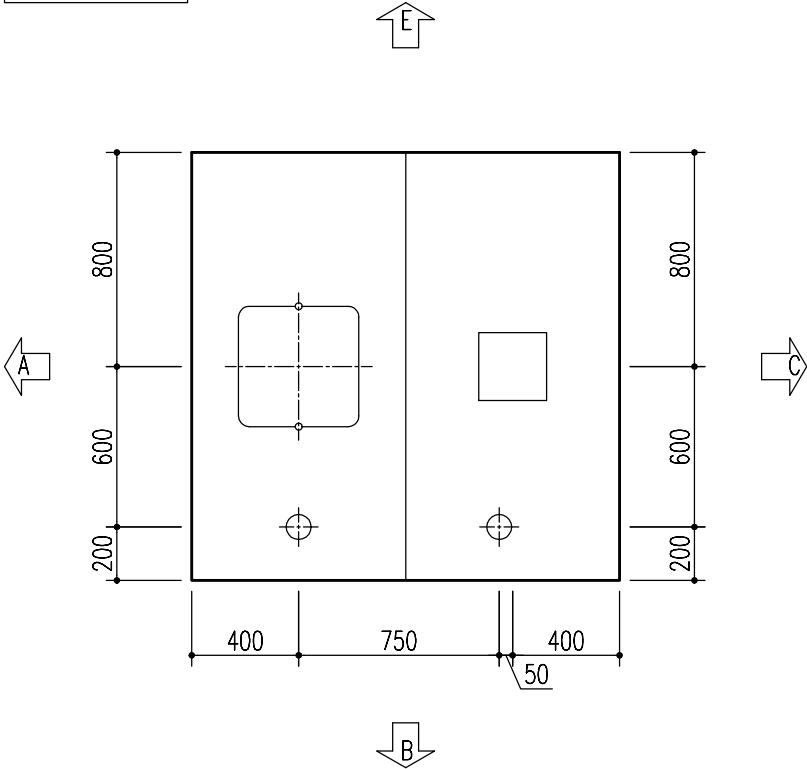

- ※ UB据付必要寸法はドア部の寸法を含みません。ドア部の寸法は詳細図のドア取合をご確認ください。
- ※ 取付ける機器により、UB据付必要寸法は異なります。
詳しくは、カタログの「工務店さまへ（取付け前の確認事項）」をご確認ください。
- ※ プラスオプションの追加マグネットアイテムは仕様図には表示されません。

特記事項	受領印	物件名	図面	担当	検図	図番
		山寄 悟 様邸		栗野 友仁		日付 2025.06.03
		仕様図	縮尺	株式会社 LIXIL		
		BMUS-1616LBZ-B+H,LR				

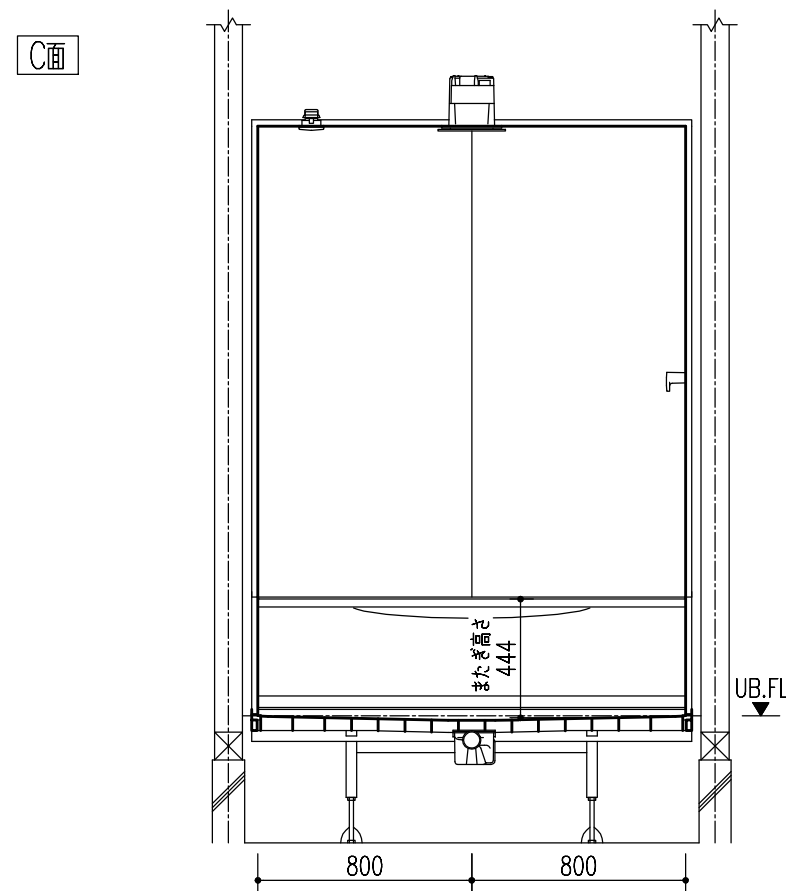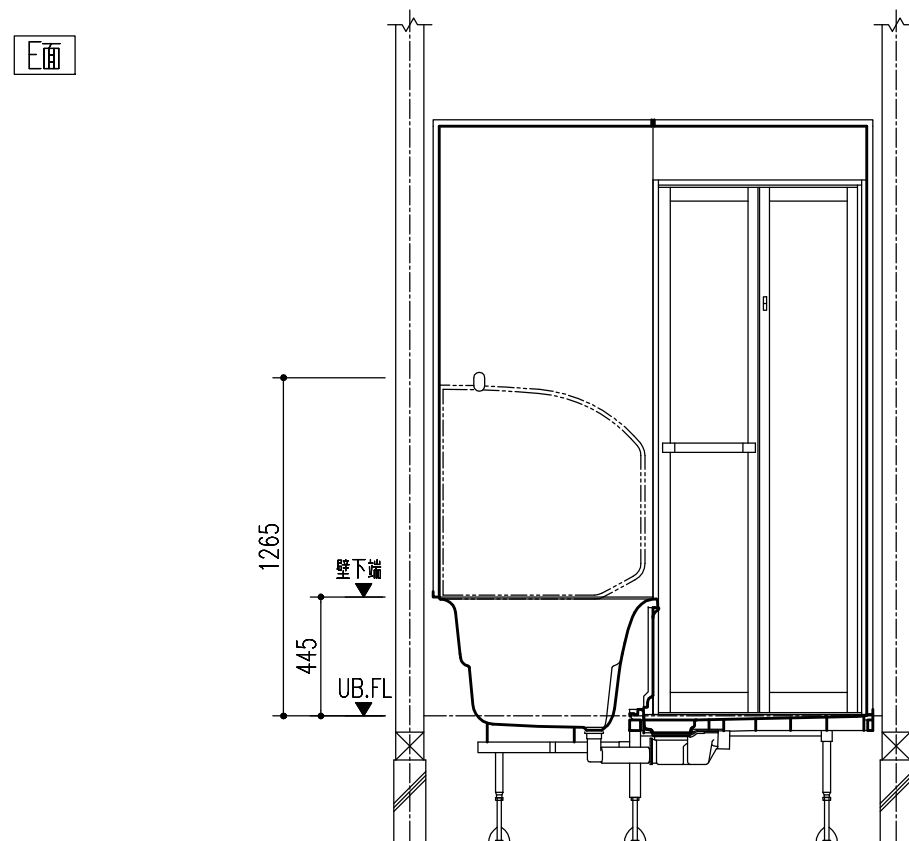

特記事項	受領印	物件名	山寄 悟 様邸	図面	担当	検図	図番
		品名	仕様図 BMUS-1616LBZ-B+H,LR		薬野 友仁		日付 2025.06.03
				縮尺	株式会社 LIXIL		

配管接続部詳細図

配管の接続をスムーズに行うためにユニットバス取付前に下記の準備をお願いします。


(1)給水、給湯、排水の一次側は所定の位置に立ち上げておいてください。

(2)排水を脱衣室側(ドア下等)へ抜く場合は、基礎部に開口を設けるか、束構造にして排水管を抜いてください。

シャワーの種類により水栓金具の入口での必要給湯圧力が異なります。詳細はカタログを確認してください。



給水給湯配管立上げ位置

点検口止め

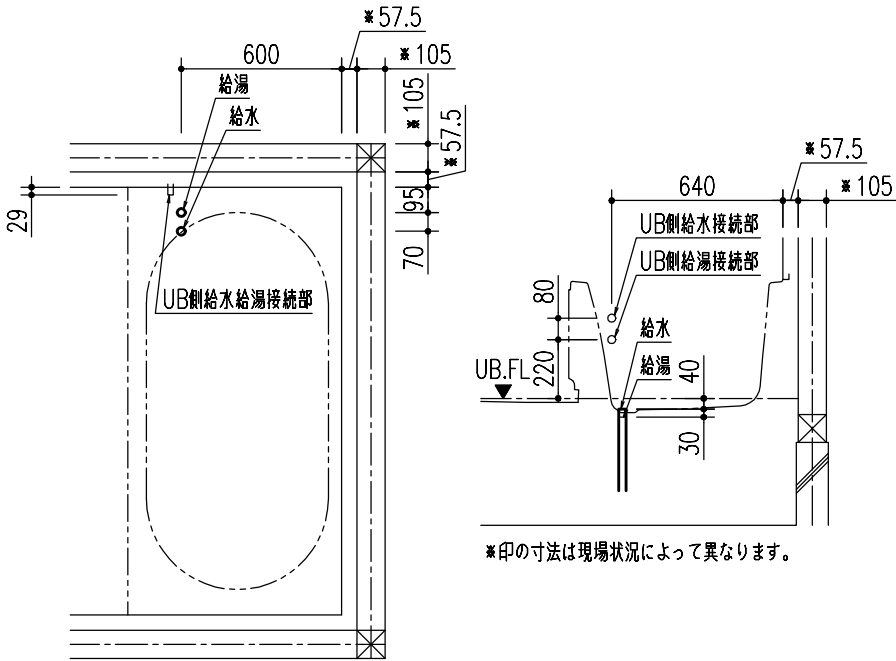

※印の寸法は現場状況によって異なります。

追いだき配管立上位置図

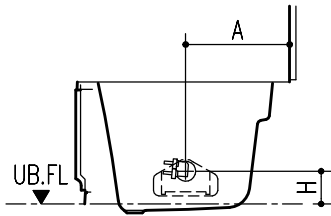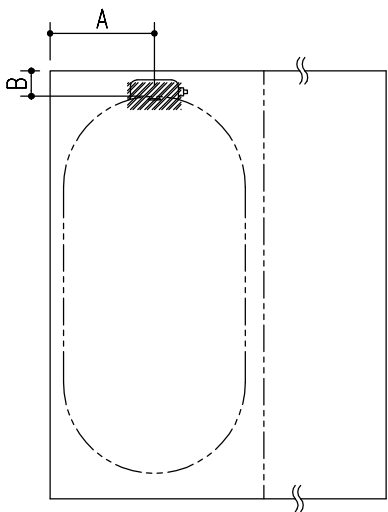



浴槽	A	B	H
ミナモイド浴槽	506	231	113
1600フイド浴槽	589	247	113
1600ミナモ浴槽	374	231	113
1600エコベンチ浴槽	389	456	103
1600ストレートライン浴槽	369	252	113
1600ロング浴槽	355	194	113
1300ミナモ浴槽	384	132	113
1300ストレートライン浴槽	369	160	113
1200ミナモ浴槽	387	130	113
1150ミナモ浴槽	387	130	113

※図はR勝手の場合です。L勝手の場合は左右反転になります。

※追いだき循環アダプターは現場手配になります。


雑排水管

浴槽側の配管持出し位置・排水管立上位置は専用の配管キット(オプション)を使用した場合の位置です。

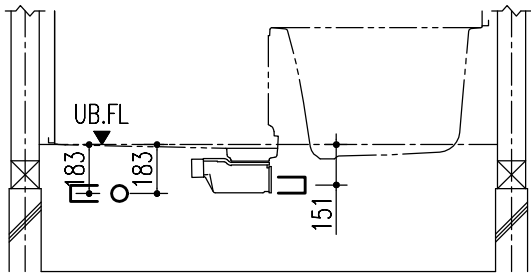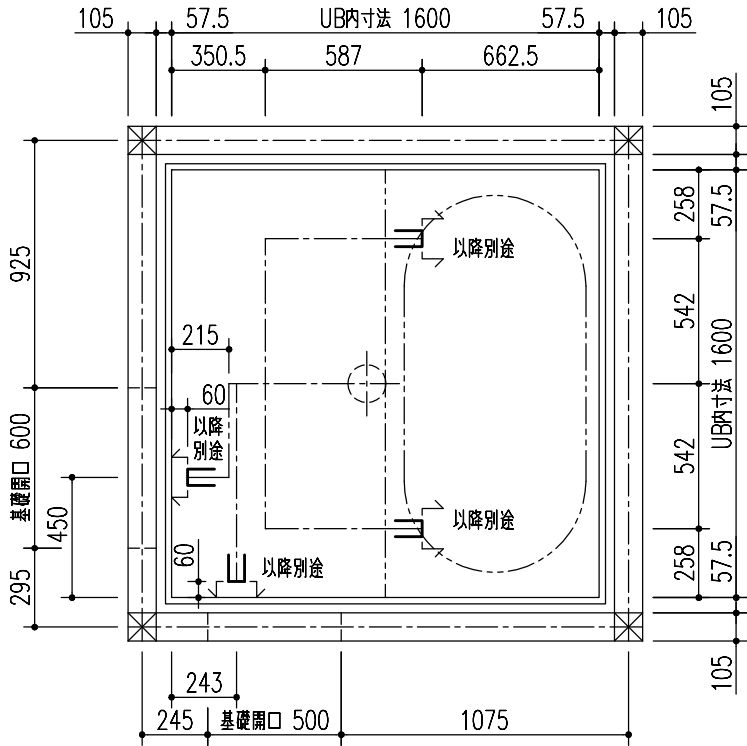

標準持出し位置


給水給湯接続部

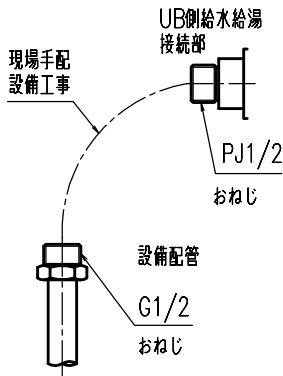

特記事項	受領印	物件名	図面	担当	検図	図番
		山寄 悟 様邸		栗野 友仁		日付 2025.06.03
		品名	縮尺	株式会社 LIXIL		
		BMUS-1616LBZ-B+H,LR				
		名				


ドア取合

有効幅員:650mm

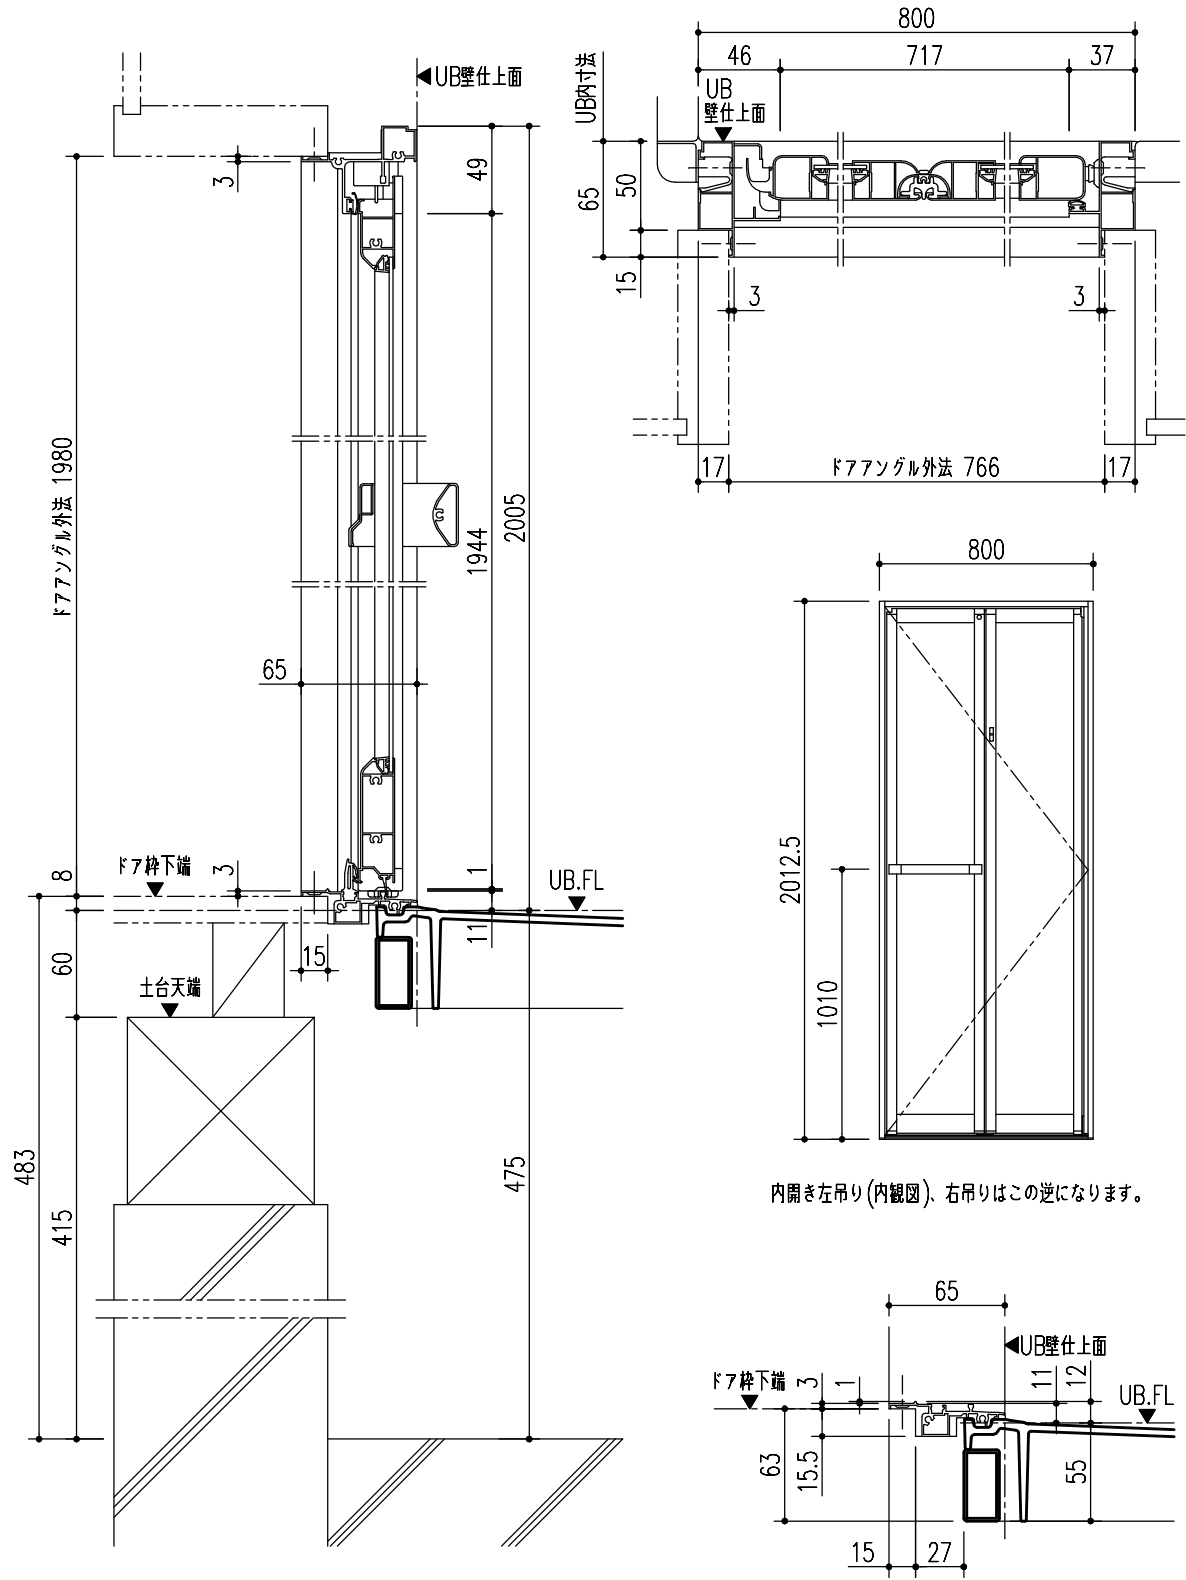


ドア横の管柱、間柱について

ドアが管柱、間柱にあたらないように十分考慮してください。
寸法はユニットサイズやドア位置ずらし、間仕切りユニットの有無によって異なる場合があります。仕様図でご確認ください。

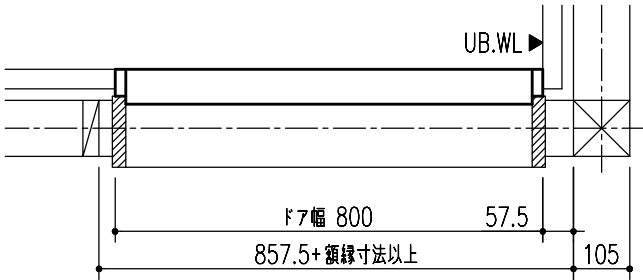


窓開口位置

現場の状況や窓により窓開口位置を設定する場合、以下の範囲で決めてください。
※壁幅いっぱいの大きさの窓の場合は、パネル左右のスペースを0としてください。
※（ ）内の寸法とする場合は、壁パネルの強度上、桟木等を使用し補強を行ってください。

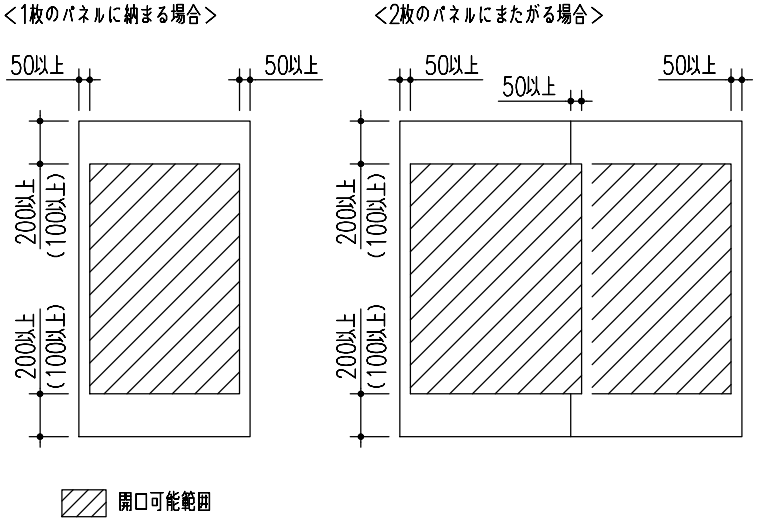


壁に取り付けられる器具と干渉しないように開口位置を決めてください。
主な器具との必要クリアランスは以下の図を参照してください。
窓開口をまたぐ位置には、握りバー/スライドフック付握りバー/スライドバーを取付できません。

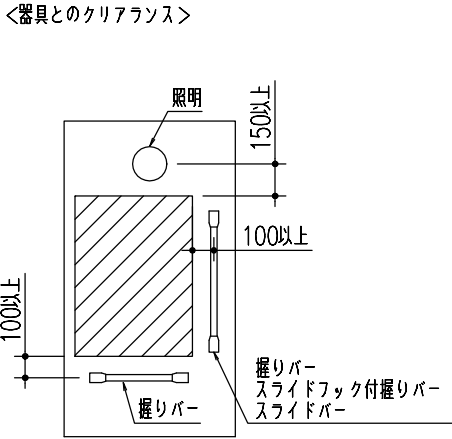


特記事項	受領印	物件名	図面	担当	検図	図番
		山寄 悟 様邸		栗野 友仁		日付 2025.06.03
		詳細図	縮尺	株式会社 LIXIL		
		BMUS-1616LBZ-B+H,LR				

照明



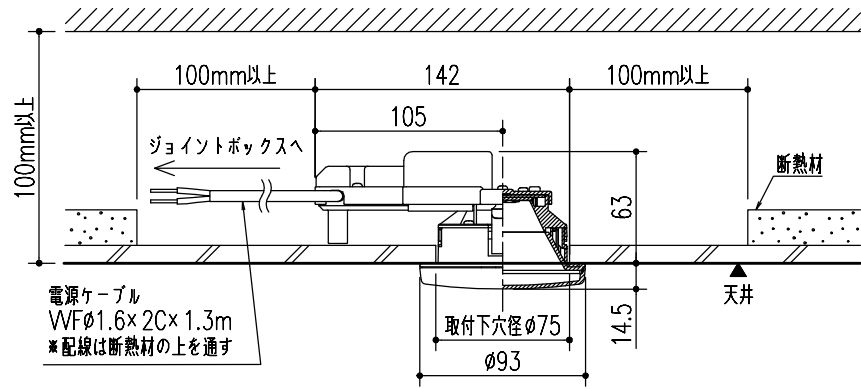


天井設置型照明は室外露出外殻から放熱しております。
その周辺100mmには保温・断熱材などを設置しないでください。
また、断熱材の落下など建築物が接触するおそれがある場合は、
建築側で防止策を講じて下さい。

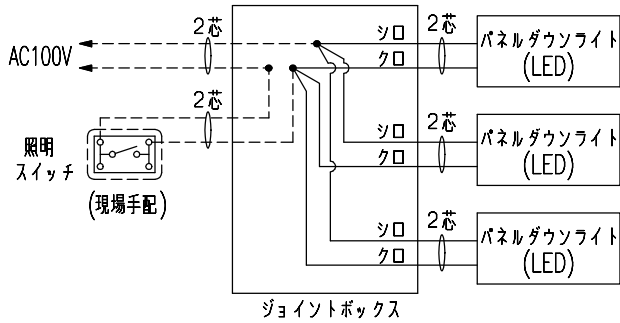

- 結線箇所 (電気工事)
- 配線 (現場手配・電気工事)

換気扇

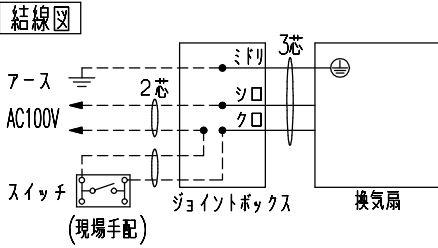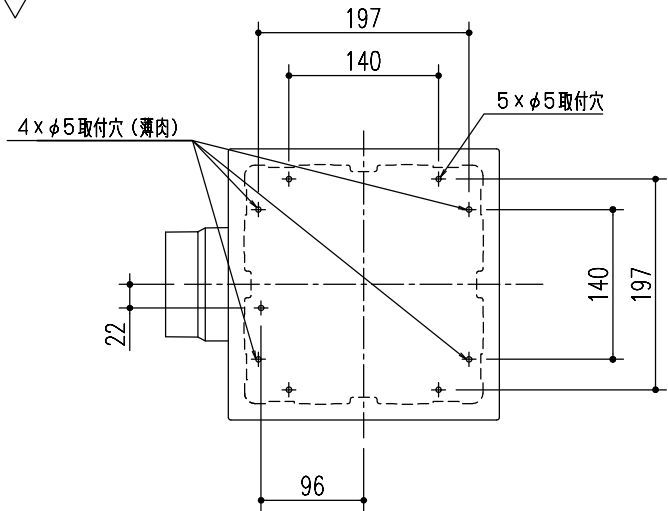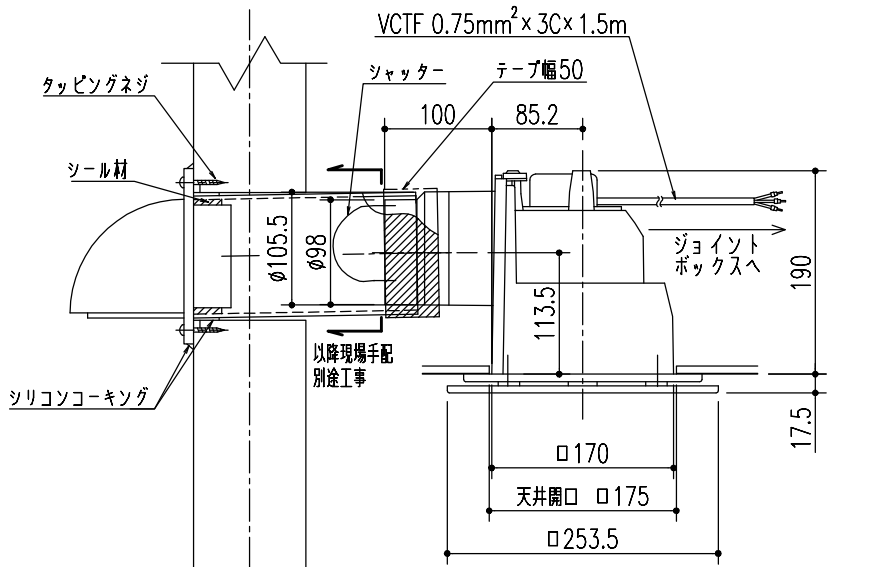

- 結線箇所 (電気工事)
- 配線 (現場手配・電気工事)


注1) 一次側電源線・アース線との結線工事、それ以降の配線工事、スイッチ取付け・結線工事は電気工事業者様の作業範囲となります。

△ 警告
●電気工事は電気設備技術基準、内線規程など関連する法令・規程にしたがって、必ず「電気工事士」が行ってください。
●電線相互の接続は銅線用裸圧着スリーブを用いる等確実に工事してください。絶対に「手より」接続しないでください。
※電気工事が不適切な場合、火災や漏電の恐れがあります。
●電源線など各配線に、以下のことをしないでください。 ※火災、漏電や故障の恐れがあります。
・傷つける、無理に曲げる、無理な力を加える、束ねる、重いものを載せる、挟み込む。
●一次側に必ず漏電遮断器を設置してください。 ※感電する恐れがあります。

特記事項	受領印	物件名	図面	担当	検図	図番
		山寄 悟 様邸		栗野 友仁		日付 2025.06.03
		品名	縮尺	株式会社 LIXIL		
		BMUS-1616LBZ-B+H,LR				
		名				

注意）配線図の  は電気工事による接続箇所を示します。搭載する電気機器は配線図中の  に  と記入し、また不要な電気機器は斜線で消してください。

< 電気工事範囲 >

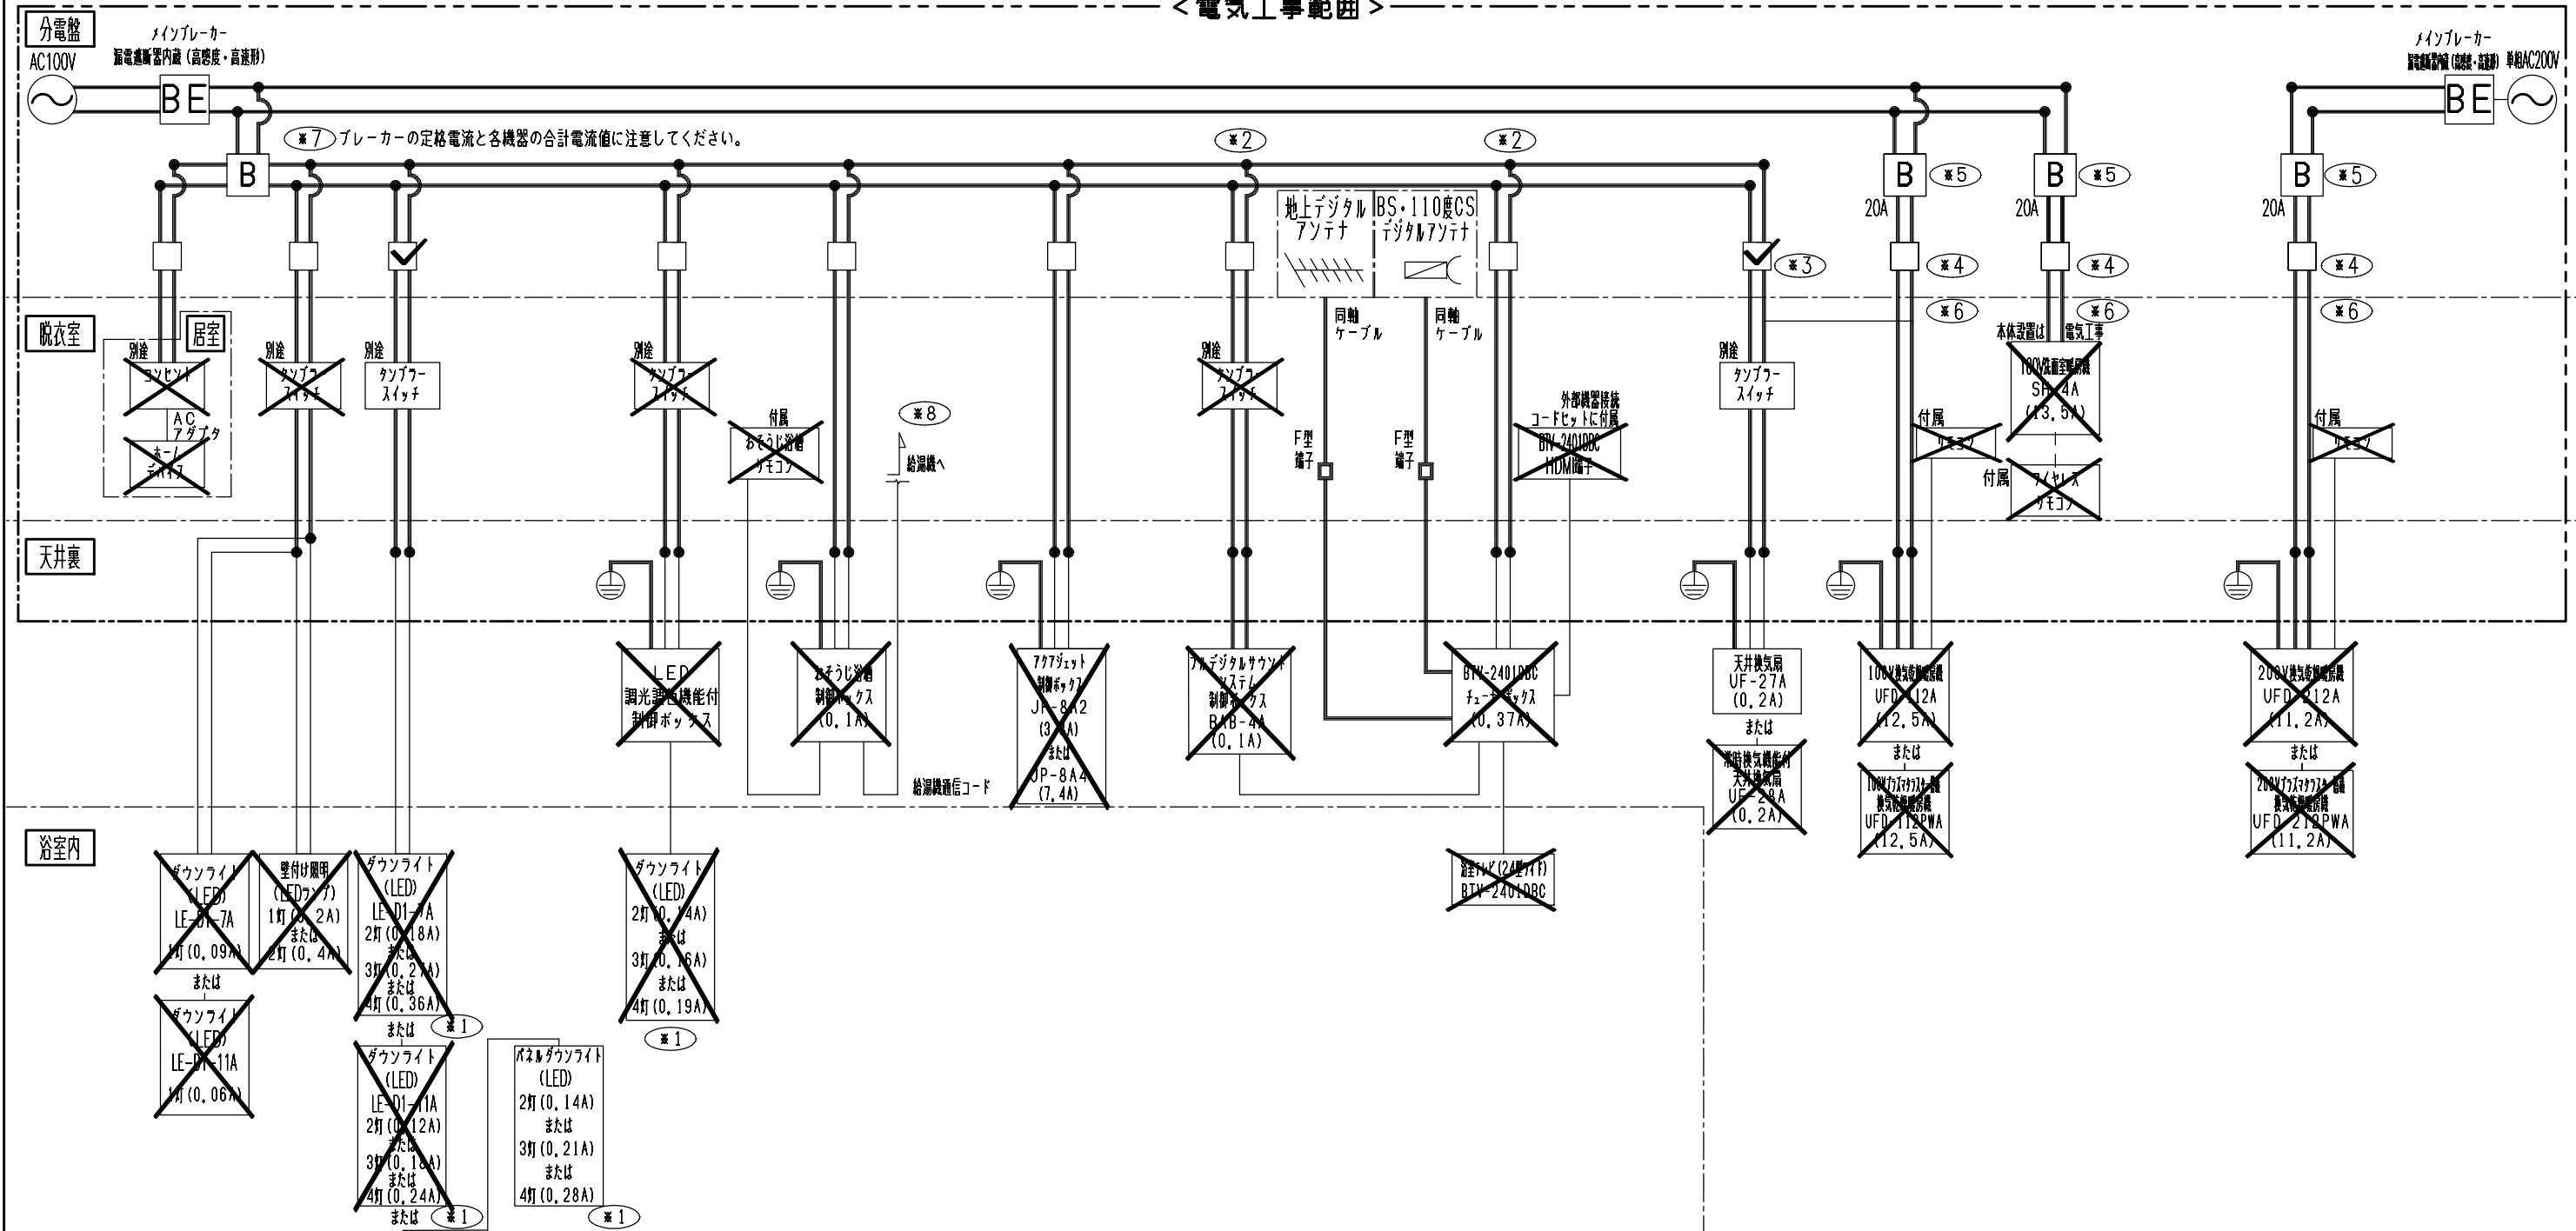

区分	照明	おそうじ浴槽	気泡浴槽	テレビ・サウンドシステム	換気設備	暖房設備・換気乾燥暖房機
----	----	--------	------	--------------	------	--------------

- ※1：選択されたユニットサイズ、タイプ、オプションによって灯数が異なります。
- ※2：化粧台など浴室以外の照明器具との配線を分けてください。
※照明のon/offによってフルデジタルサウンドシステムへノイズが乗る可能性があります。
- ※3：換気扇を単独で設置する（換気乾燥暖房機を設置しない）場合を示します。
- ※4：換気乾燥暖房機を設置する場合、※3の経路はありません。
- ※5：運転初期に突入電流が発生しますので、換気乾燥暖房機単独で20Aの専用回路としてください。
※電気工事が不適切な場合、火災や漏電の恐れがあります。
- ※6：専用の配線用遮断機から配線し、途中にスイッチを設けないでください。
※誤った配線工事は、火災や漏電、故障の恐れがあります。
- ※7：ブレーカーの定格電流と各機器の合計電流値に注意してください。
- ※8：給湯機器と連動する場合に必要となります。

⚠ 警告

- 電気工事は電気設備技術基準、内線規程など関連する法令・規程に従って、必ず電気工事士の資格を有する者が適切な方法で行ってください。 ※無資格者の工事や、電気工事士による不適切な工事は、火災や漏電を引き起こす恐れがあるほか、関係法令により処罰等されることがあります。
- 電線相互の接続は銅線用裸圧着スリーブや差込形コネクタを用いる等確実に工事してください。絶対に「手より」接続しないでください。
※電気工事が不適切な場合、火災や漏電の恐れがあります。
- アース工事が必要な電気機器はD種接地工事を施した接地線と確実に接続してください。
※漏電や故障の際に、感電する恐れがあります。
- 電源線など各配線に、以下のことをしないでください。
 - ・傷つける、無理に曲げる、無理な力を加える、束ねる、重いものを載せる、挟み込む ※火災、漏電や故障の恐れがあります。
- 電源線、アース線やリモコンコード等の配線は、照明器具（ダウンライト等）や暖房機など熱器具から離して設置してください。
※器具の熱で配線が溶断し、火災や漏電の恐れがあります。
- 一次側に必ず漏電遮断器（高感度・高速形）を設置してください。 ※感電する恐れがあります。
- 一次側の電源線、アース線、スイッチ配線と電気機器配線の結線部は、必ずジョイントボックス内に収めてください。
システムバスルームに同梱されているジョイントボックスを使用してください。 ※ほこり等により火災の恐れがあります。


- ※以下のものは、システムバス取付作業に含まれておりません
 - ・電源線、アース線の一次側配線工事、D種接地工事、漏電遮断器の調達および設置工事。
 - ・各電気機器の電源線およびアース線と一次側配線との接続工事。
 - ・更衣室に設置するスイッチ（別途の表記があるもの）の調達。
 - ・更衣室に設置するスイッチの配線接続および設置工事（別途、付属とも）。

特記事項	受領印	物件名	図面	担当	検図	図番
各電気機器の詳細については各々のオプション詳細図を参照ください。		山寄 悟 様邸		栗野 友仁		日付 2025.06.03
		品名	縮尺	株式会社 LIXIL		
		電気機器配線図 BMUS-1616LBZ-B+H,LR				
		名				

排水管接続の注意点
浴槽排水時には最大約1.2L/sの流量が発生します。排水管の経路や、管内の状態によっては正しく排水されない場合があります。設計・取付の際は次の各項目を確認して下さい。

■ダブルトラップ
浴室以降の排水管経路上に、トラップが無いことを確認してください。（ダブルトラップの禁止）
ダブルトラップになっていると、「排水が流れない」「異臭がする（封水切れ）」などの異常につながります。
ダブルトラップは配管接続前に解消してください。
システムバスルーム設置後はダブルトラップの解除ができません。


【ダブルトラップの例】

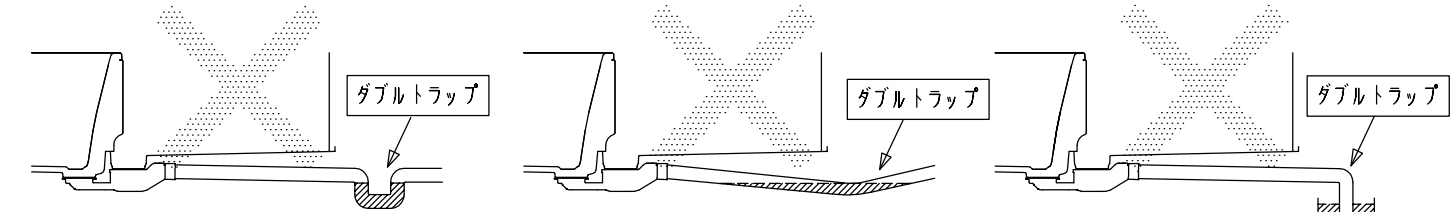

下に曲がった配管部分が、トラップになっている
横引き配管がたわみ、トラップになっている
配管の先が排水ます溜水内にあり、トラップになっている


■排水管内の詰まり
接続する排水管が、汚れなどで詰まっていないことを確認してください。
配管が細かったり、配管内が汚れ等で詰まっていると、「排水が流れない」「洗い場排水口から浴槽排水が溢れてくる」といった異常につながります。
汚れが付着して詰まっている場合、配管を接続する前に洗浄し汚れを取り除いてください。

【悪い例】

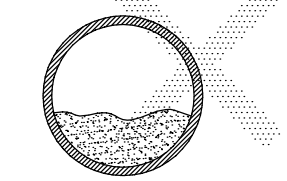

配管内に汚れなどの詰まりがある

【良い例】


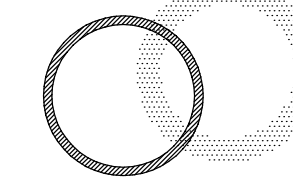


配管内に汚れなどの詰まりは取り除く

■排水管経路


排水管の経路によっては、排水異常となる場合があります。
次の事項にご注意のうえ設備業者さまと十分な事前打合せをお願い致します。

- ① システムバスルーム以降で排水管を縦方向に落とす場合
通気を設けるか、配管径を拡張、もしくは90°曲げ部に大曲リエルボ（LL）を使用する事をおすすめします。

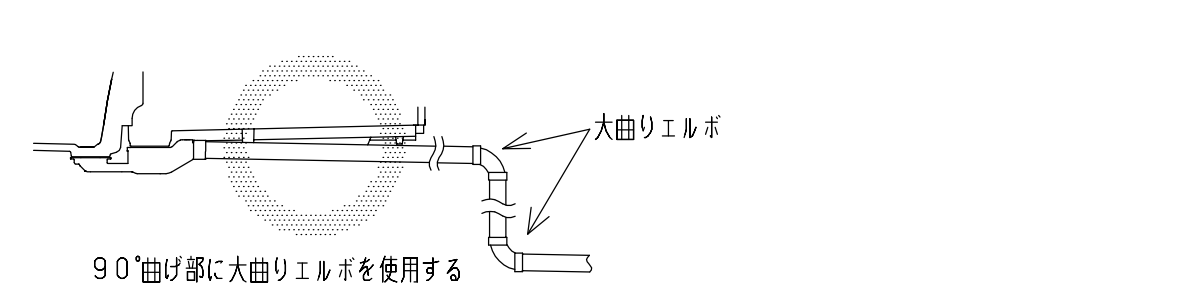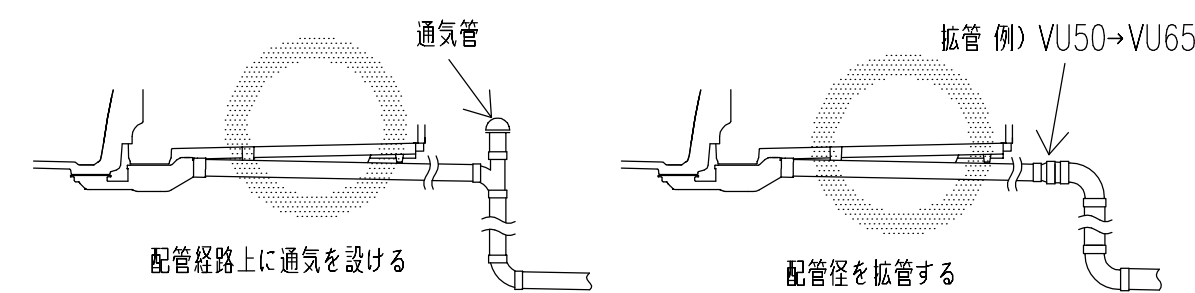


配管経路上に通気を設ける
配管径を拡張する
90°曲げ部に大曲リエルボを使用する
※浴槽排水時に排水口から「ゴボゴボ」と音が発生することがありますが、異常ではありません。

- ② システムバスルーム以降の横引き配管について
90°曲げ部に大曲リエルボ（LL）を使用するか、システムバスルームに近い位置で配管径を拡張する事をおすすめします。

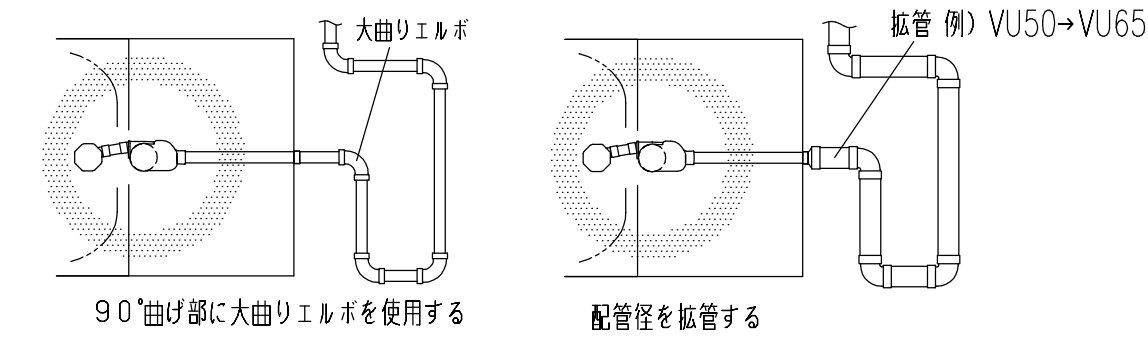



- ③ システムバスルーム床下の排水管経路について

- トラップ出口には同梱の継口配管を接続してください
 - 継口配管を使用しない場合
 - ・大曲リエルボを使用してください
 - ・1620-2サイズの場合、トラップ出口に接続する配管には、必ず切断長さ250mm以上の横引き経路を設けてください
- ※洗い場パントの干渉回避や浴槽排水の流れを妨げないため

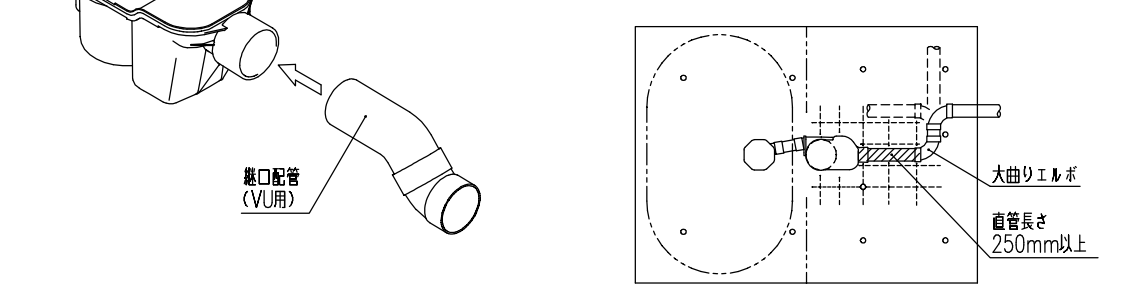

【排水管経路の悪い例】



十分な長さの横引き配管を設けずに曲げを繰り返したり、縦方向に落としている

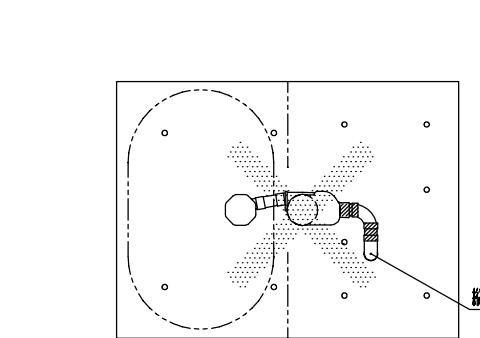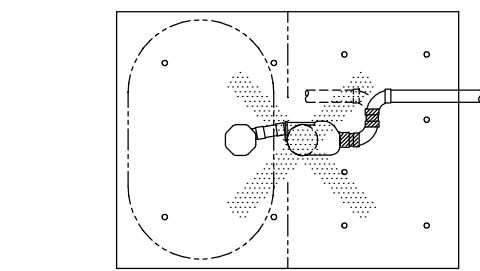

縦方向配管




【排水管経路の良い例】

トラップから2曲がりまでの間に十分な長さの横引き経路を設けている

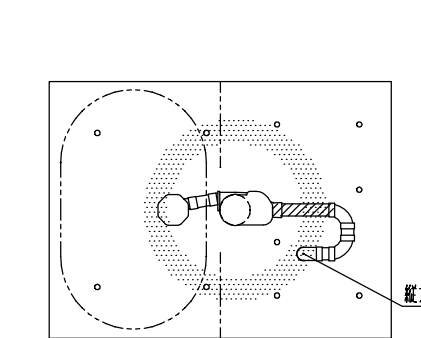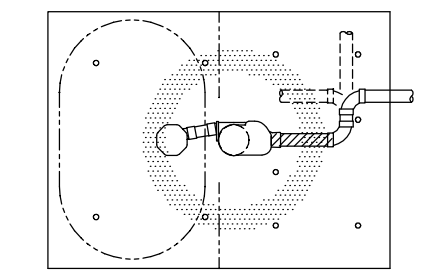

縦方向配管

特記事項	受領印	物件名	図面	担当	検図	図番
		品名				日付
		排水管経路条件図	縮尺	株式会社 LIXIL		
		AX				

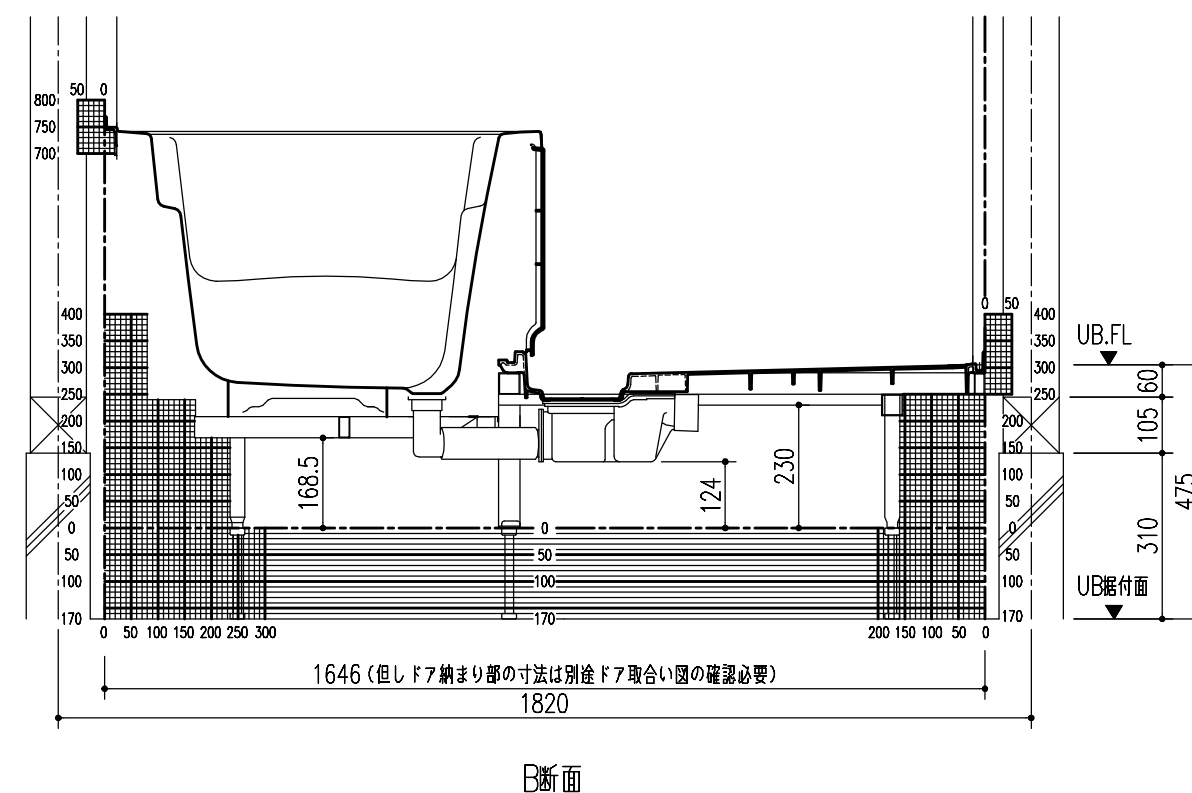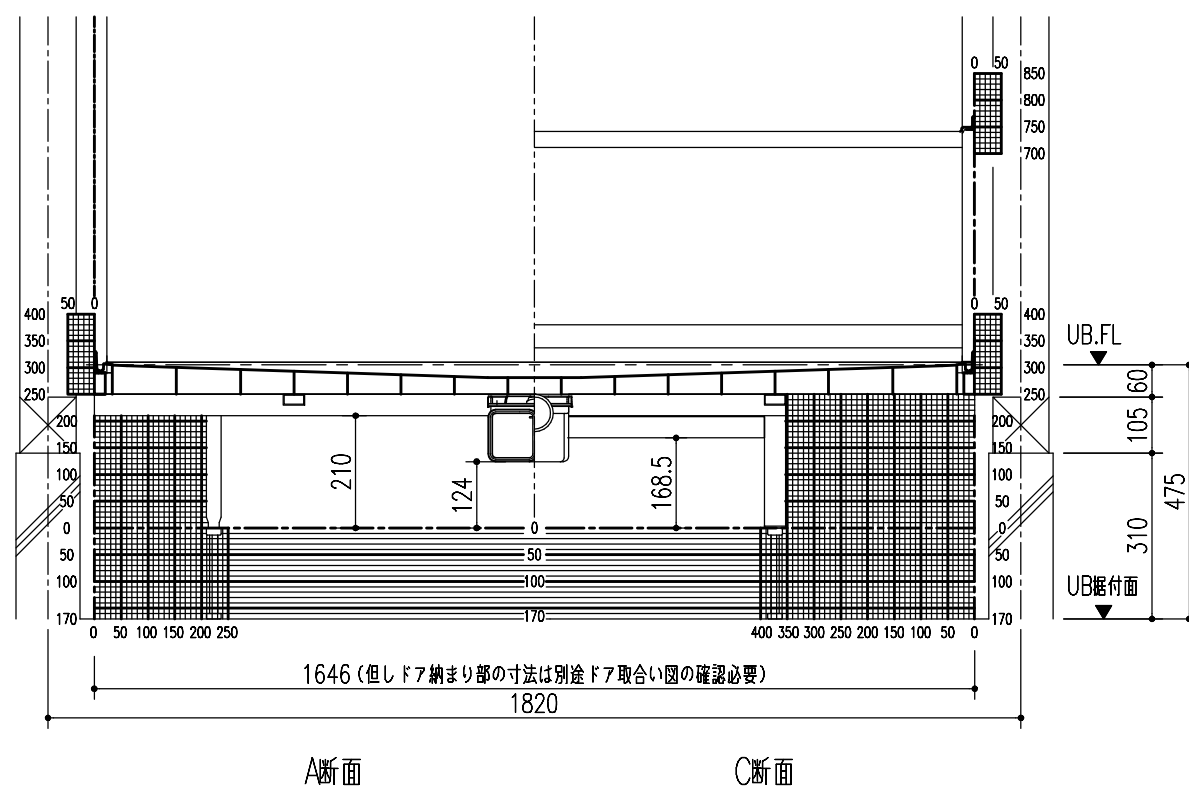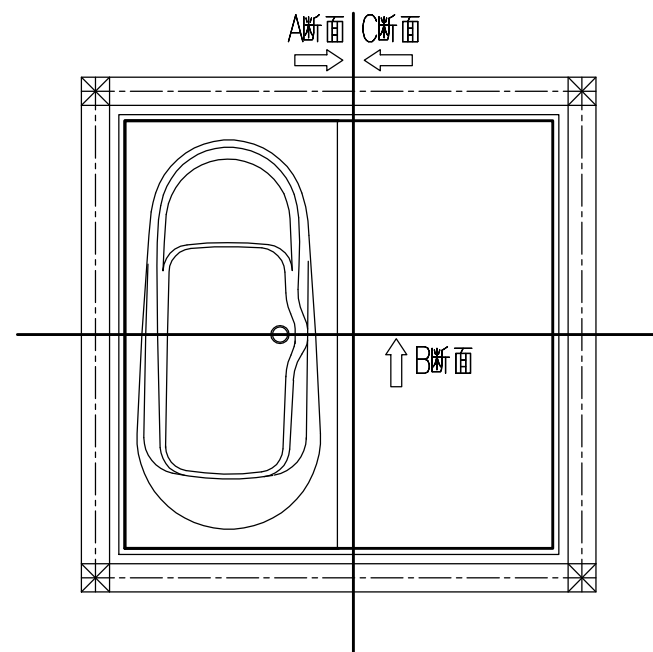




※ 本図はRタイプを示します。Lタイプは本図を左右反転したものになります。

特記事項	受領印	物	図面	担当	検図	図	
		件				番	
		名				日付	
		品	床下納まり	縮尺	株式会社 LIXIL		
			AX				
		名	1616サイズ(浴槽パンなし・ボルト脚仕様H475)				

●全面開口の場合

- ※ 奥行 390・490 の零額録使用の場合、製品に 1/50 の水勾配がついております。
そのため、パネル開口寸法 A および零額録外寸法 B が水勾配分大きくなります。
詳しくは零額録同梱取付説明書をご確認ください。
- ※ 窓と零額録を締結するための取付ねじは零額録に同梱されていません。
- ※ 窓開口補強（アルミテープ）は別販手配が必要です。
- ※ 1 零額録 1510P は、幅（W）1000×高さ（H）1500 としても使用できます。

特記事項	受領印	物件名	図面	担当	検図	図番
						日付
		品名	縮尺	株式会社 LIXIL		
		フリーサイズ'客領録 詳細図 R-1010P,R-1510P R-1515P,R-1715P				

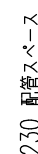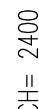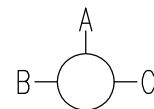


【注意】


- 壁面仕上材（キッチンパネル・タイルなど）の貼付下端位置が変わります。〔機能図参照〕
- 記載のキャビネット寸法は扉前面での呼び寸法です。キャビネット本体の寸法・扉厚等は商品ガイドの巻末資料をご確認ください。
- 記載のワークトップ、カウンター、エンドパネル、サイドパネルの寸法は呼び寸法です。詳細寸法は商品ガイドの巻末資料をご確認ください。
- レンジフード電源プラグ仕様：2芯電源プラグ（アース工が必要です。）

案件No.	図面名	担当	図面	図番 : 株式会社 LIXIL
A2503DDDD0EGDPJ	レイアウト図	栗野 友仁		
見積No.	縮尺	日付		
M25047301367-009-2	1/30	2025.06.03		

B面

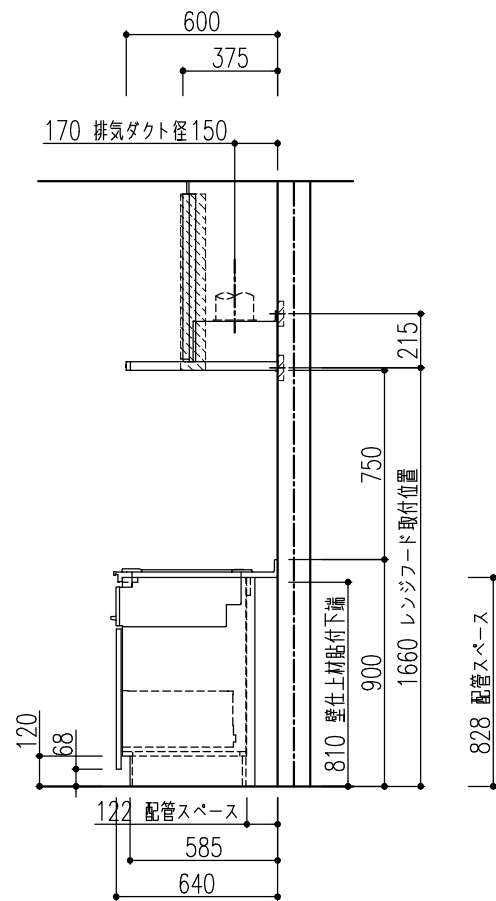

C面

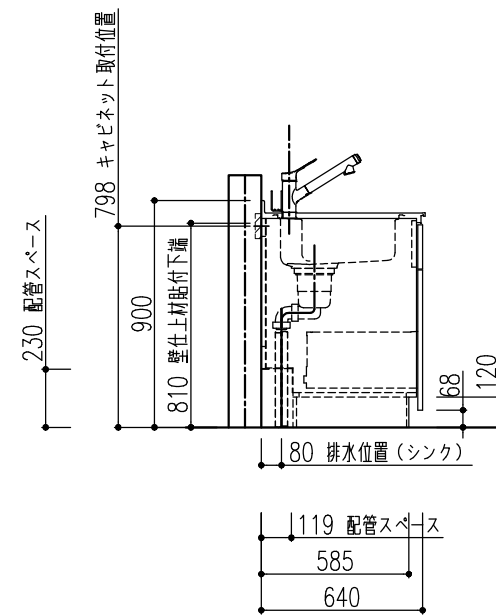


特記事項 扉色 VK5:グレージュスタック 取手 [R]スリム取手 (シャインニッケル) ワークトップカラー 【DW】ソルティホワイト	物件名	山寄 悟 様邸	案件No.	図面名	担当	図面	図番
	仕様	ES 2 1	A2503DDD0EGDPJ	納まり図	栗野 友仁		株式会社 LIXIL
			見積No.	縮尺	日付		
			M25047301367-009-2	1/30	2025.06.03		

■壁面仕上材（キッチンパネル）取付注意事項〔貼付向き〕

●キッチンパネルの貼付向き


キッチンパネルの貼付向きにご注意ください。

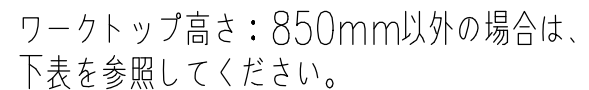

ワークトップ高さ	キッチンパネル 貼付下端位置
900	860
875	835
825	785
800	760

●上表はキッチンパネルの場合です。ステンレスパネルの場合は、キッチンパネルの「取付・設置説明書」を参照してください。

《ワークトップ高さ：850mmの場合》

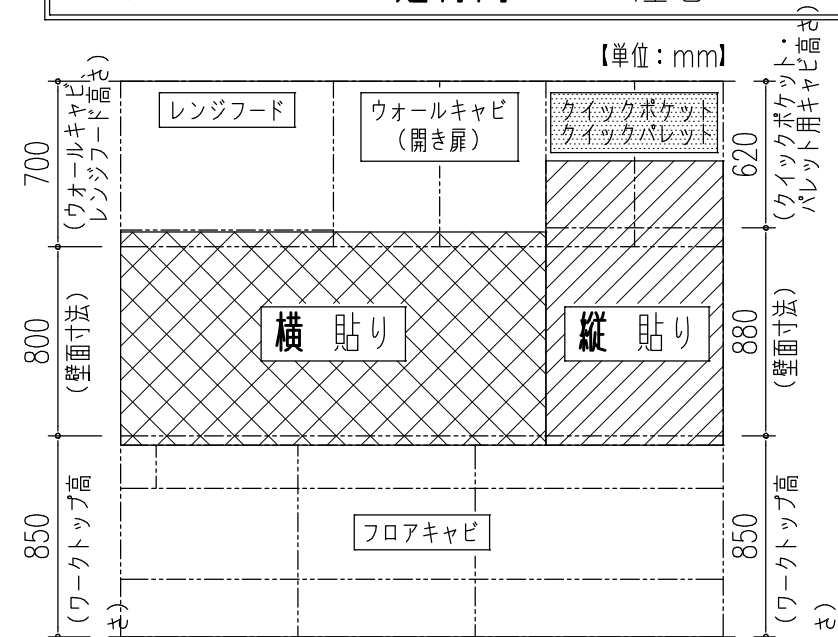


《キッチンパネル 貼付方向》
総高さ：2350mmの場合

	ウォールキャビ		
	開き扉		クイックボックet クイックバレット
	H700	H600 H500	H700 (620) H600 (520)
キッチンパネル 貼付方向	横	縦	

【ご注意】
リシエル以外のクイックパレットは、
キャビネットの背板高さがショート
(-80mm)してありませんので、
『開き扉』のキッチンパネル貼付方向
に合せてください。

《バックガード：なし、ワークトップ高さ：850mm、ウォールキャビ高さ：700mmの場合》


■レンジフード取付注意事項（壁面取付時）

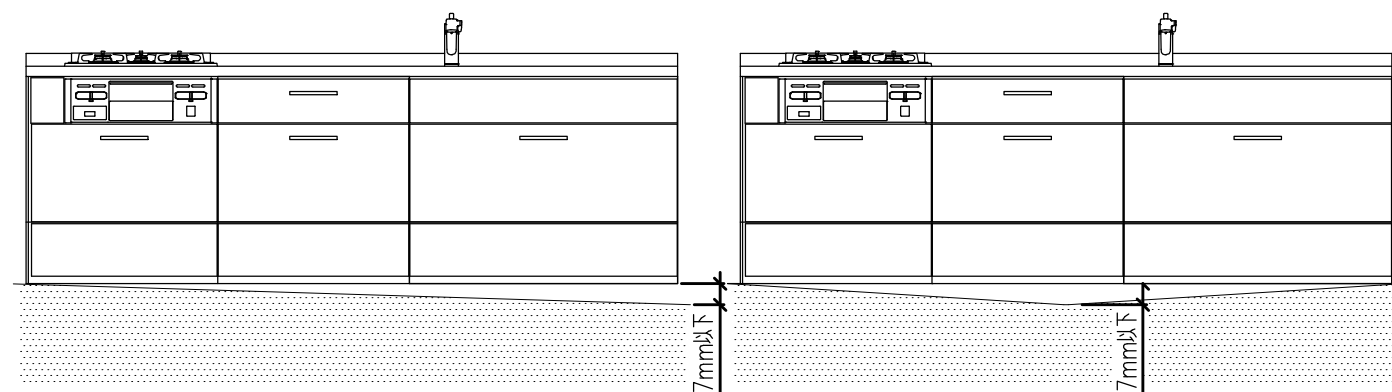


床の不陸は、7mm以下に抑えるようにしてください。不陸が大きい場合は、現場責任者に床の修正を依頼してください。
※キャビネット取付時には不陸調整スペーサー等で水平になるように設置してください。

レンジフードを取付ける場合は下地の桟が厚み30 mm以上、幅100 mm以上、ビス固定位置が桟の端部から25 mm以上であることを確認してください。
また、壁強度などの詳細は「レンジフード設置説明書」を必ず事前に確認してください。


取付位置については、取付設置図を確認してください。

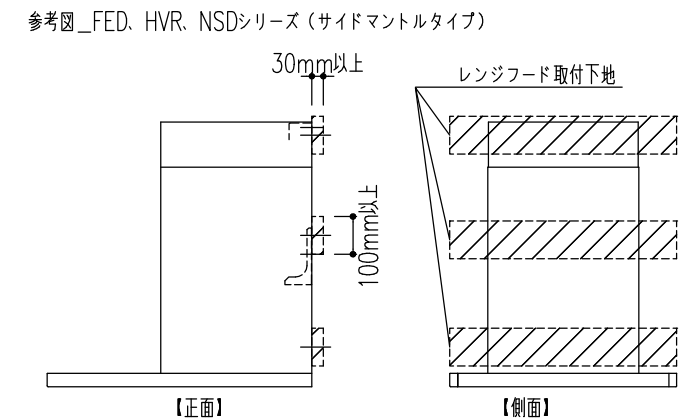

参考図_CLS、SER、NST、ASR、ADR、RVJ、GSR、BFRS、TARシリーズ
(※RVJ、GSRシリーズの場合はレンジフードパネルの取付下地は不要です。)

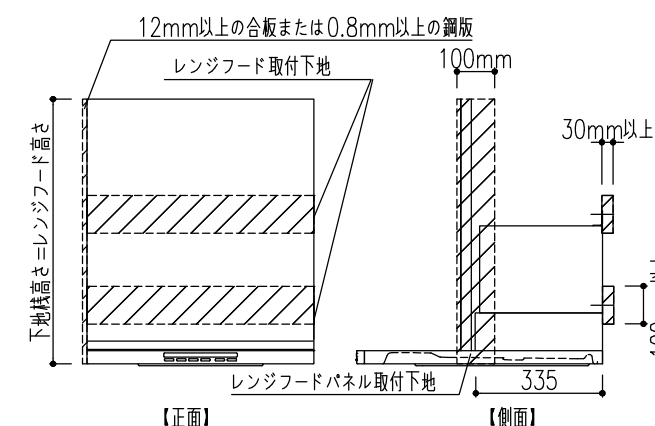


参考図_NBHシリーズ

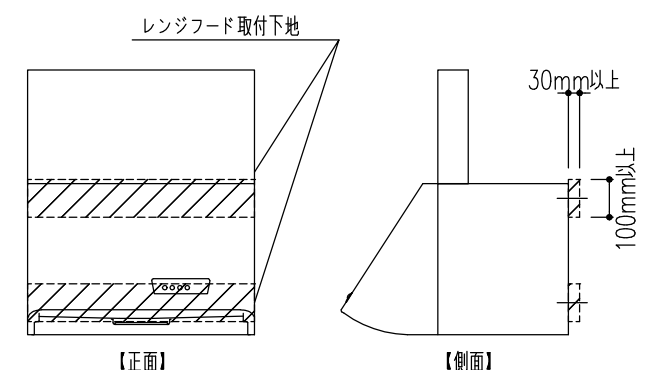


特記事項 扉色 VK5:グレージュスタック 取手 [R]スリム取手（シャインニッケル） ワークトップカラー 【DW】ソルティホワイト	物件名	山寄 梧 様邸	案件No.	図面名	担当	図面	図番：
			A2503DDDOEGDPJ	機能図	栗野 友仁		
	仕様	ES21	見積No.	縮尺	日付		株式会社 LIXIL
			M25047301367-009-2		2025.06.03		

■天井フィラーの取付（レンジフード上部）

レンジフード横に壁がくるレイアウト時は、横壁にも取付桝が必要になります。

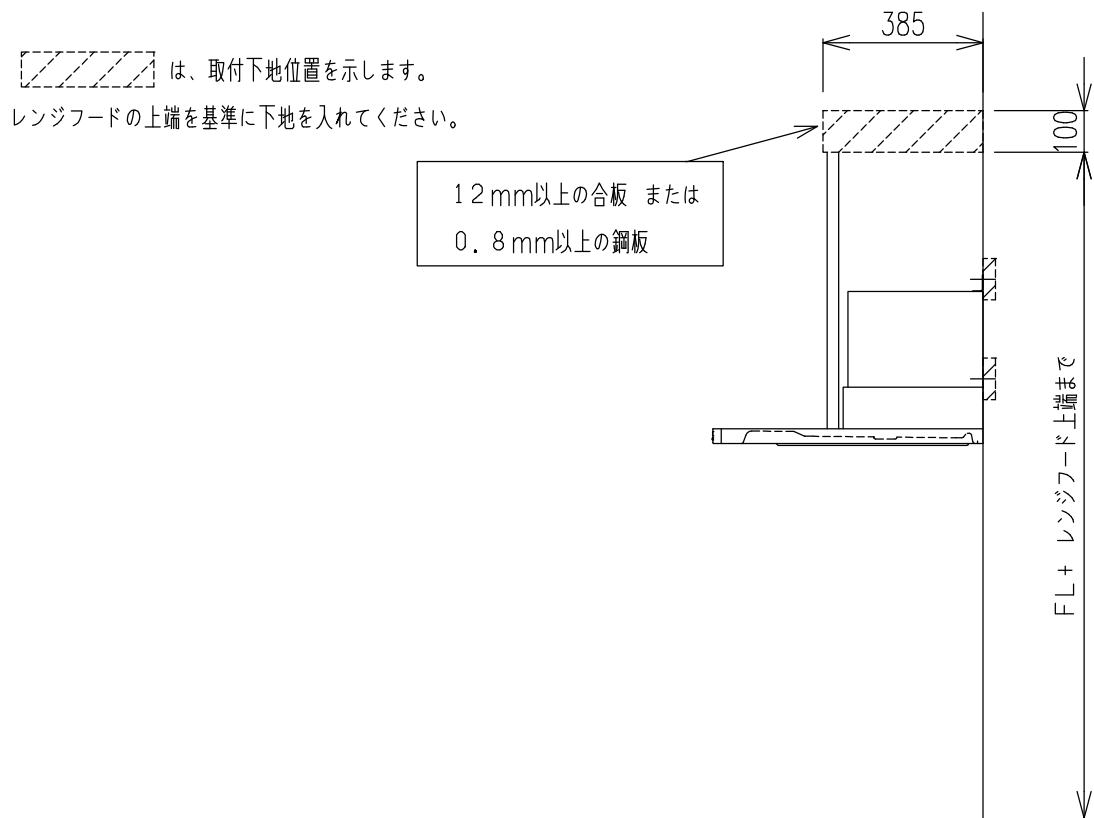

■ ASRフード

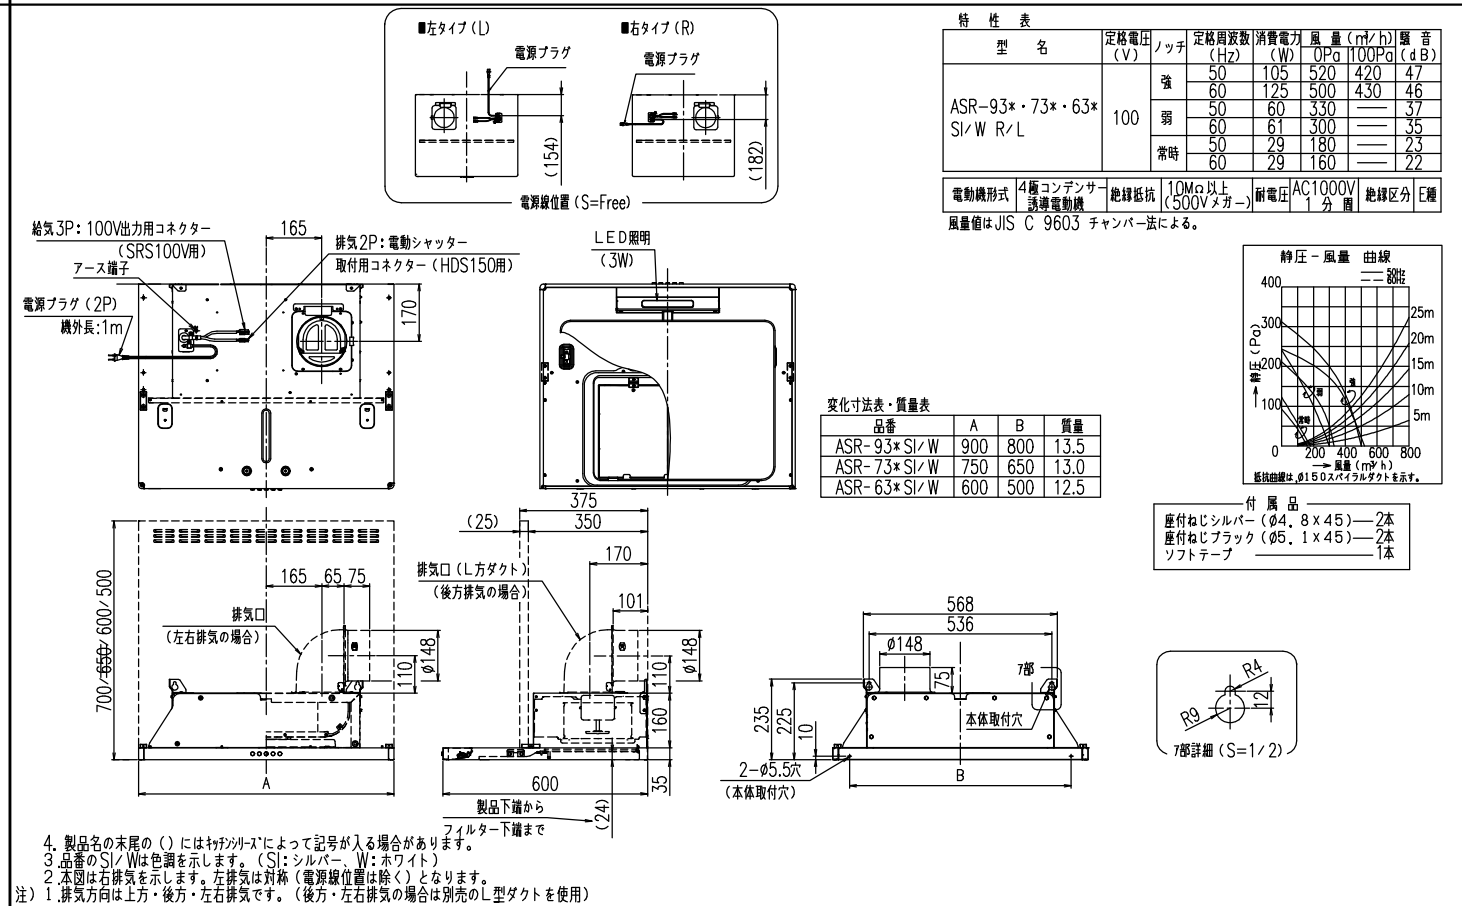


■ IHヒーター用コンセント推奨位置図 / 壁付設置の場合

※コンセントや電源プラグが、引き出しおよびIHヒーター用仕切板（オプション）に接触しないように注意してください。


※木製キャビネットの配管スペース付キャビネットを使用する場合は点検口裏の配管スペース内にコンセントを設置してください。

キッチン高さ	電源線高さ
800	400
850	450
900	500

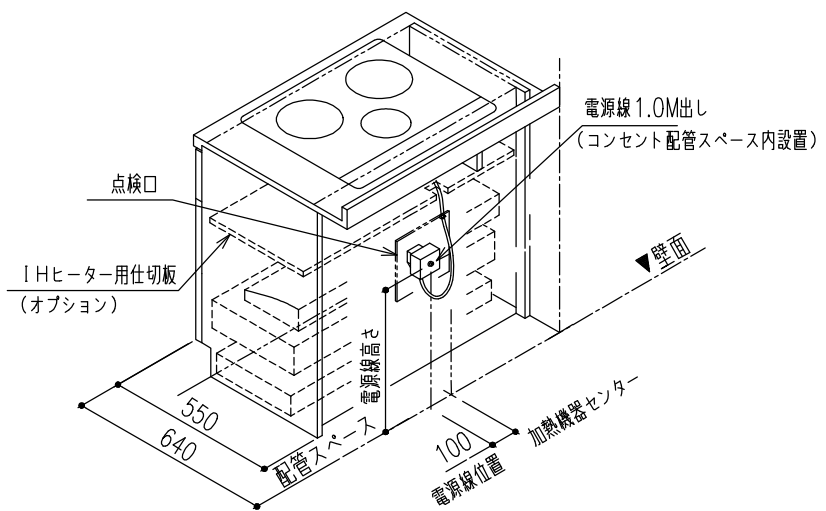

注意：引き出しおよびIHヒーター用仕切板（オプション）に接触しないように上記寸法を参照してください。

■食器洗い乾燥機内配管図 床立上げ配管例

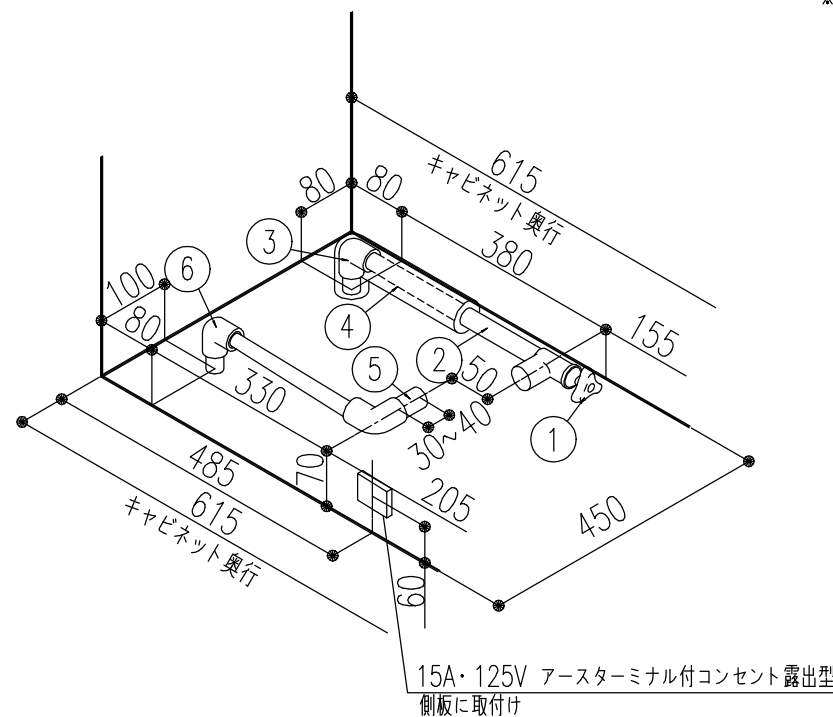

注意：配管立ち上げ位置は必ず本図の位置に立ち上げて下さい。

※給水接続か給湯接続かお客様に確認したうえで施工願います。

給水（給湯の場合は耐熱配管）

①アンゲル型止水栓（ハンドル式・固定ゴマタイプ）

※必ず固定ゴマタイプをご使用ください。

落としゴマタイプを使用すると、水栓内でコマが移動し、ゴトゴト音を生じる恐れがあります。

②硬質塩化ビニルライニング鋼管（相当品）

③RC1/2ソケット

④断熱材 (Φ48)

排水（耐熱塩ビ使用のこと）

⑤排水パイプHT20

⑥HTエルボ

※配水管先端のエルボを上向きにしないでください。


キャビネットに当たるため、排水ホース折れの原因になります。

特記事項 扉色 VK5:グレイジュスタコ 取手 [R]スリム取手 (シャインニッケル) ワークトップカラー 【DW】ソルティホワイト	物件名	山 寄 梧 様 邸	案件No.	図面名	担当	図面	図番 : 株式会社 LIXIL
			A2503DDD0EGDPJ	機能図	栗野 友仁		
	仕 様	ES21	見積No.	縮尺	日付		
			M25047301367-009-2		2025.06.03		

■ 止水栓図（床立上げ）

床立上げ配管

配管立ち上げ寸法は、止水栓芯までの高さを示しています。

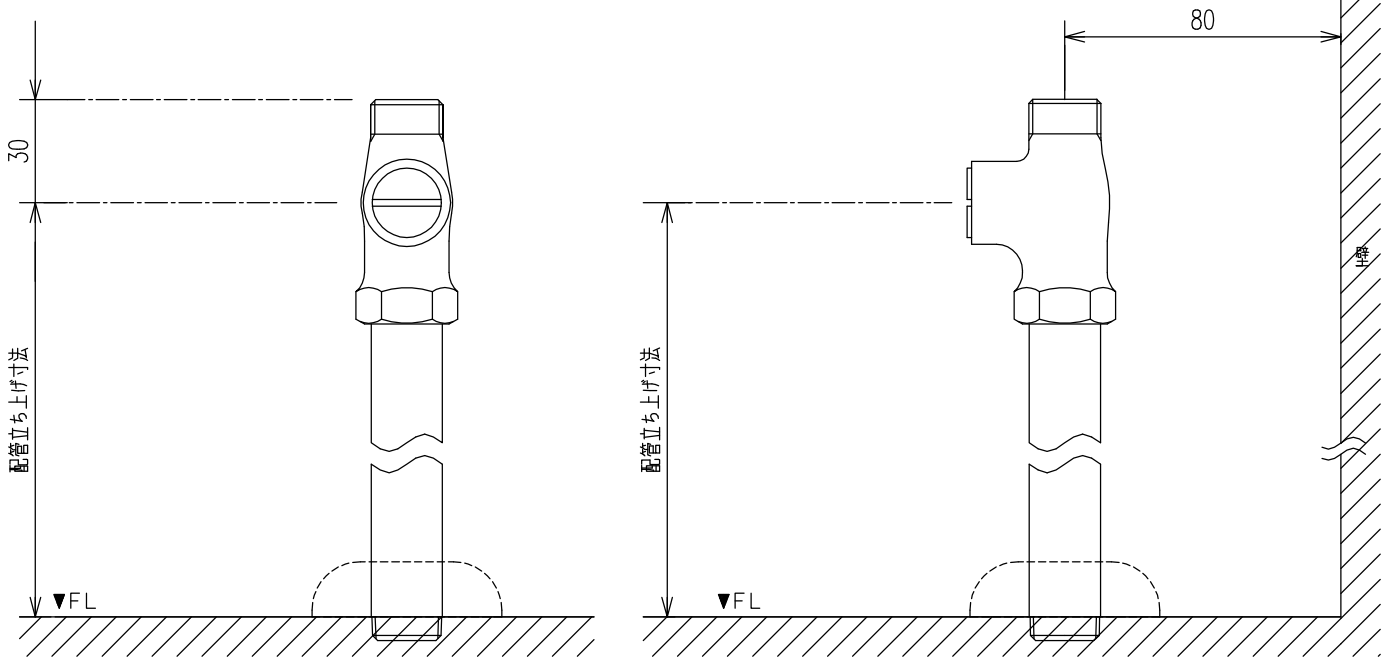

	特記事項 扉色 VK5:グレージュスタック 取手 [R]スリム取手（シャインニッケル） ワークトップカラー 【DW】ソルティホワイト	物件名 仕様	山寄悟 様邸 ES 2 1	案件No.	図面名	担当	図面	図番
				A2503DDD0EGDPJ	機能図	栗野 友仁		株式会社 LIXIL
				見積No.	縮尺	日付		
				M25047301367-009-2		2025.06.03		

■ キッチン取付者さま向け 動画コンテンツ ■
商品取付けの注意点を2次元コードでご視聴いただけます。
取付日より前に、是非ご確認ください。

1 ページ目

■ キッチン取付者さま向け 動画コンテンツ ■
商品取付けの注意点を2次元コードでご視聴いただけます。
取付日より前に、是非ご確認ください。


1 ページ目

■ キッチン取付者さま向け 動画コンテンツ ■
商品取付けの注意点を2次元コードでご視聴いただけます。
取付日より前に、是非ご確認ください。

1 ページ目

荷扱い・搬入

荷扱い・搬入

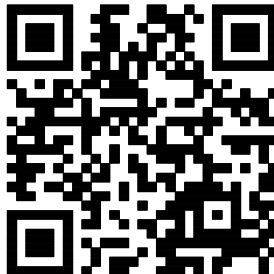

作成日：2024年10月01日

荷扱い・搬入

荷扱い・搬入




作成日：2024年10月01日



荷扱い・搬入

荷扱い・搬入

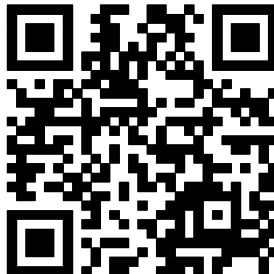

作成日：2024年10月01日

カウンター開梱搬入「養生ツール」

カウンター開梱搬入 「養生ツール」のご紹介



作成日：2024年10月01日

カウンター開梱搬入「養生ツール」

カウンター開梱搬入 「養生ツール」のご紹介



作成日：2024年10月01日




カウンター開梱搬入「養生ツール」

カウンター開梱搬入 「養生ツール」のご紹介






作成日：2024年10月01日


不陸の確認と調整

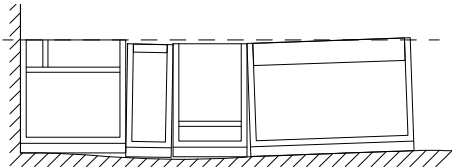

作成日：2024年02月07日

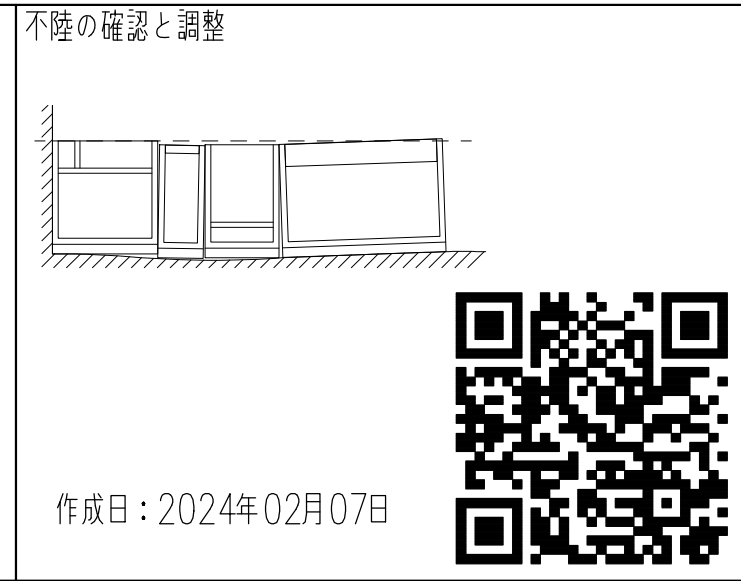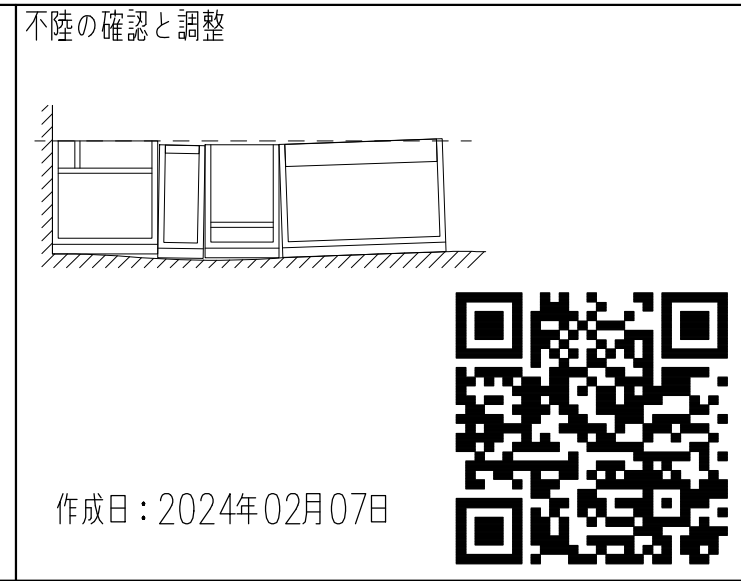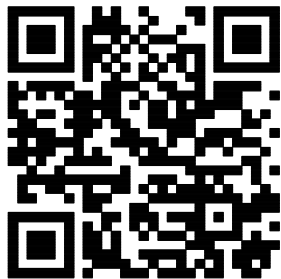

不陸の確認と調整

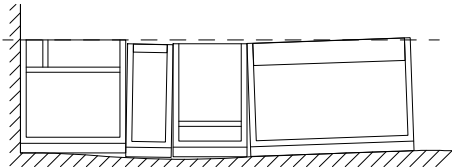

作成日：2024年02月07日



マグネット キッチンパネル

マグネット キッチンパネル 「取付・設置」ポイント



作成日：2024年03月06日

マグネット キッチンパネル

マグネット キッチンパネル 「取付・設置」ポイント



作成日：2024年03月06日




マグネット キッチンパネル

マグネット キッチンパネル 「取付・設置」ポイント



作成日：2024年03月06日


人造大理石カウンターL型キッチン

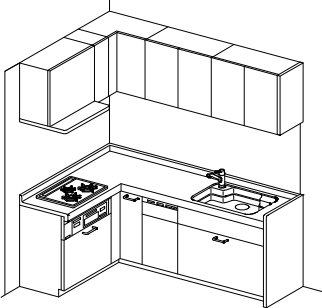

作成日：2024年02月07日




人造大理石カウンターL型キッチン

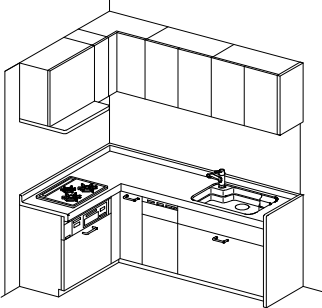



作成日：2024年02月07日




センターキッチン（ペニンシュラ型）

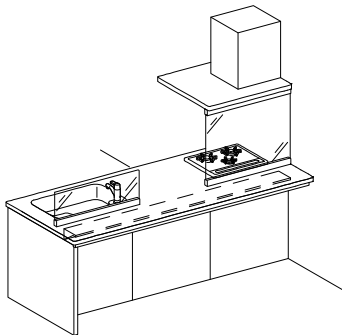

作成日：2024年02月07日

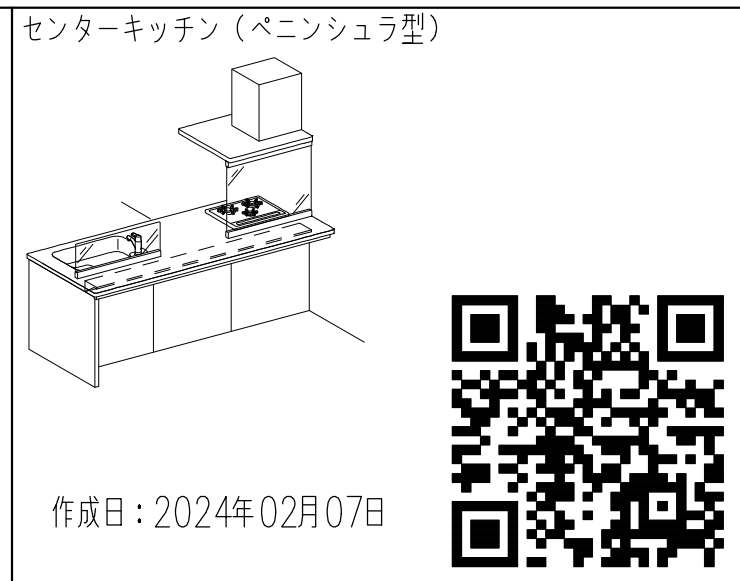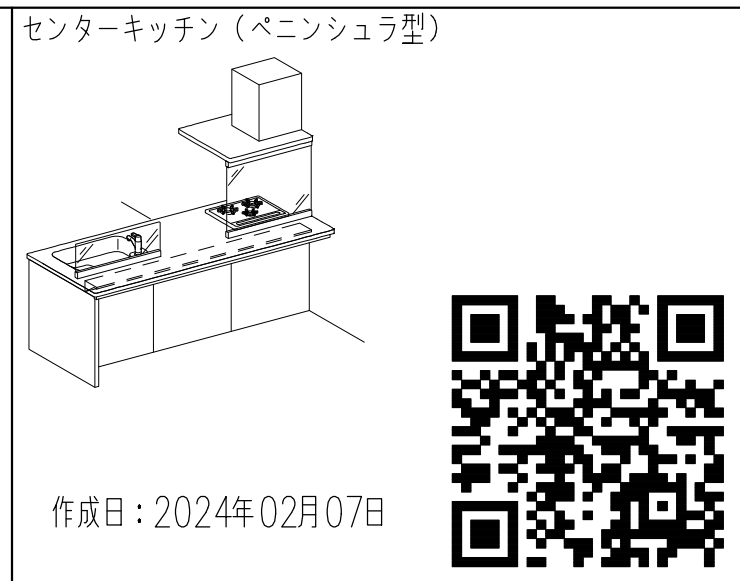




センターキッチン（ペニンシュラ型）

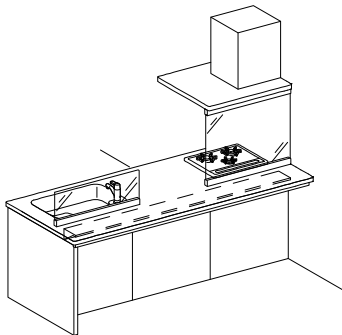

作成日：2024年02月07日

[illegible]




■ キッチン取付者さま向け 動画コンテンツ ■
商品取付けの注意点を2次元コードでご視聴いただけます。
取付日より前に、是非ご確認ください。

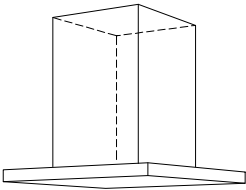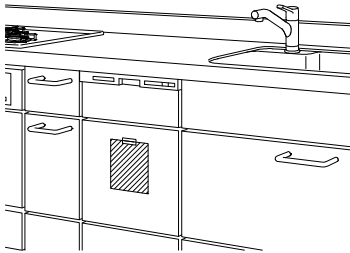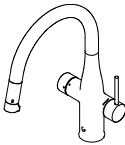センターフード型レンジフード (天吊りフード)  作成日：2024年06月03日 	I H加熱機器関連 I H加熱機器 仕切り板 作成日：2024年02月07日 	食器洗い乾燥機  作成日：2024年02月07日 	ミネラル浄水栓 Greentap  作成日：2024年06月03日 
---	--	--	---

--	--	--	--

--	--	--	--

特記事項 扉色 VK5:グレージュスタック 取手 [R]スリム取手 (シャインニッケル) ワークトップカラー 【DW】ソルティホワイト	物件名	山寄 悟 様邸	案件No.	図面名	担当	図面	図番
	仕様	ES 2 1	A2503DDD0EGDPJ	機能図	栗野 友仁		株式会社 LIXIL
			見積No.	縮尺	日付		
			M25047301367-009-2		2025.06.03		

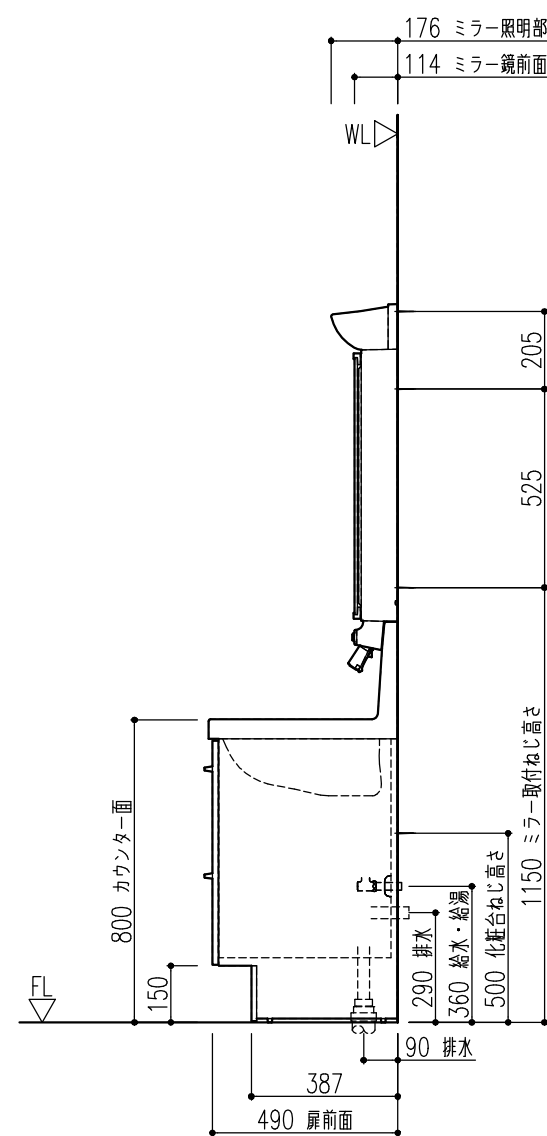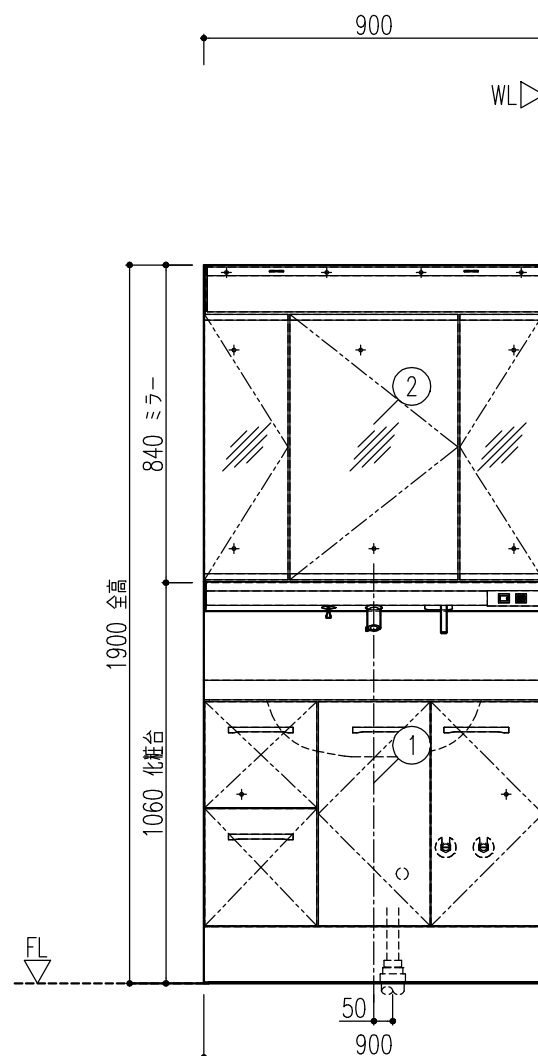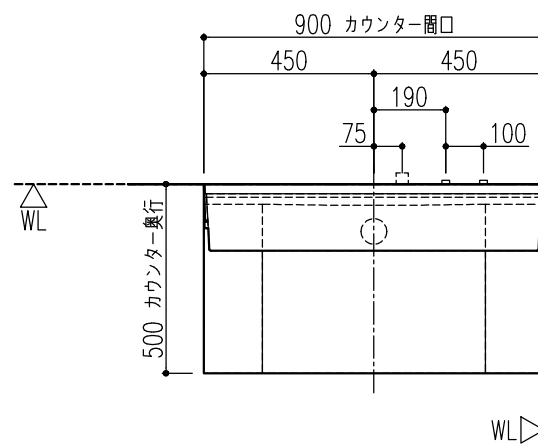[illegible]

- ※ 部品表の「図面」列に○がないものは図面表示されません。
- ・ 止水栓は左側が給湯位置、右側が給水位置を示します。
- ・ 排水管VP・VU50管の立上り法は、F.L.より、
20mm～30mmの範囲内で立ち上げてください。
- ・ 排水管VP・VU40管の立上り法は、F.L.より、
35mm～45mmの範囲内で立ち上げてください。
- ・ 給水、給湯接続はR1/2
- ※ 「ねじ固定位置」には必ず補強木（幅90mm×厚み30mm以上）または、
取付壁全面に厚み12mm以上のJAS規格品合板を強固に取り付けてください。
- ※ 止水栓は別途手配してください。
- ※ 壁排水のときは、市販の排水アダプターをご使用ください。
- ※ ミラーキャビネットはシリコンシーリングが出来ません。（シリコンが付きません。）

■化粧台本体仕様

扉カラー：YS2 グロスホワイト 材質：DAP化粧板

カウンターカラー：H プレーンネオホワイト 人造大理石（ポリエステル系樹脂）

洗面器容量：16L

水栓金具：シングルレバーシャワー水栓（ホース収納式／吐水切替付）エコハンドル

排水器具：ポップアップ排水栓（てまなし排水口）・ヘアキャッチャー付・フタ着脱式

排水トラップ：床排水・壁排水兼用ボルトトラップ（フレキホース・呼び径32mm）

■ミラーキャビネット仕様

照明（定格消費電力）：LED照明（9.8W）

くもり止めコート仕様（中央鏡）・トレイ12個付

コンセント2個（外付1個・内部1個） コンセント許容電力合計1300W以下（内部コンセント含む）

プラグ式電源仕様 電源コード長さ：2.1m ※取出可能長さは機能図参照の事

物件名	山寄 悟 様邸	案件No.	図面名	担当	図面	図番 : 株式会社 LIXIL
		A2503DDD0EGDPJ	簡易取付設置図	栗野 友仁		
仕様	EVノ奥行500タイプノ23モデルノ引出タイプノシングルレバーシャワー水栓 LED照明（スタンダードLED）ノ3面鏡（全収納）	見積No.	縮尺	日付		
		M25047301367-009-3	1/20	2025.06.03		


■参考取付図【排水金具】

＜壁床排水兼用のマルチボルトトラップ仕様について＞

マルチボルトトラップは、フレキホース仕様のため壁、床排水の両方に対応できるトラップです。


※マルチボルトトラップ（床排水）は、住宅品質確保促進法「維持管理対策等級」2または3に対応しています。

＜マルチボルトトラップの接続＞

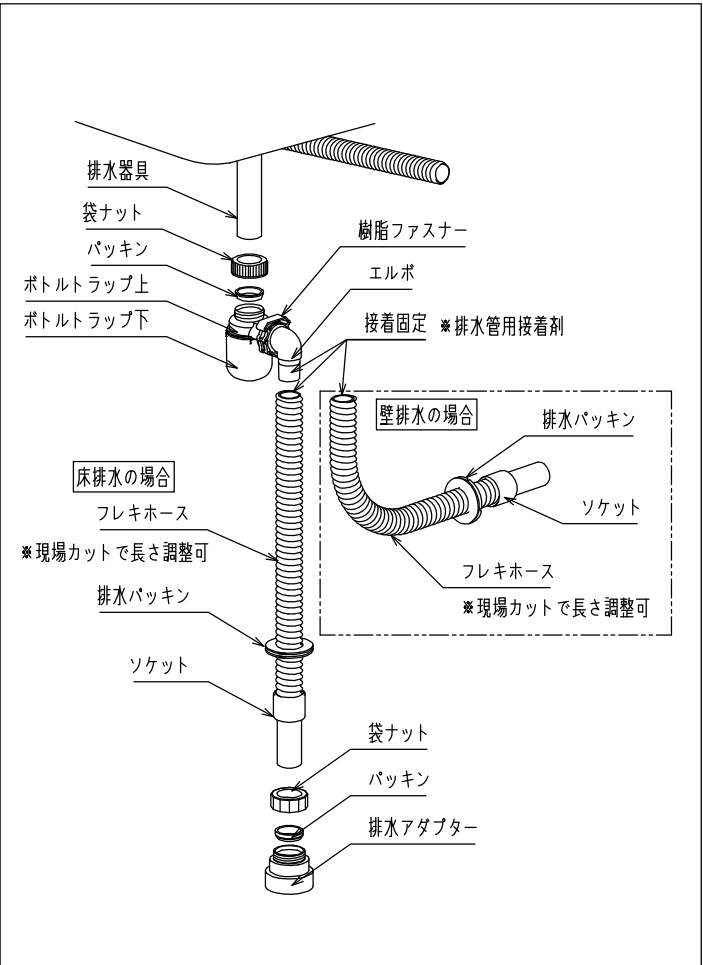

＜フレキホースの接続可能範囲＞


ハッチング範囲内の建築側排水管であれば接続可能です。
フレキホースは建築側排水管の真上から接続してください。

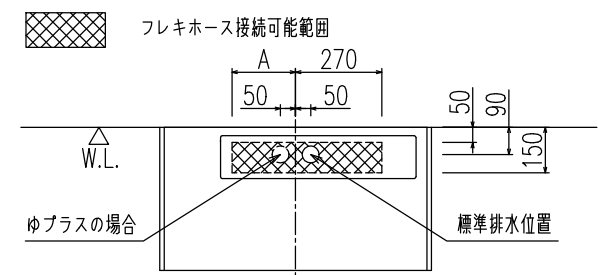

引出しタイプ		フルスライドタイプ		扉タイプ	
間口	A	間口	A	間口	A
750	24	750	130	750	210
900	99	900	130	900	210
1000	149	1000	130		
1200	210	1200	130		

注意

フレキホース取り回しの際は最小曲げR120以下にならないこと。
※ホースの折れ、つぶれ等が発生する恐れがあります

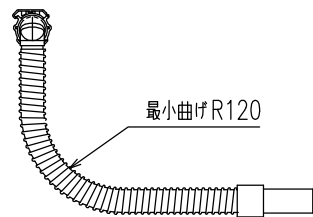


△ 注意

- ・建築側排水管VP・VU50管の立上寸法は、F.L.より20～30mmの範囲内で、VP・VU40管の立上寸法は、F.L.より35～45mmの範囲で立ち上げてください。（右図参照）
※立上寸法が足りないと接着できなくなります。
- ・配管の接着は接着面全面に塩ビ管用接着剤を十分に塗り、奥まで十分に押し込み接着してください。
- ・接着には耐熱塩ビ管（HT管）用接着剤を使用しないでください。
※漏水し、家財などを濡らす拡大損害発生 の恐れがあります。
- ・壁排水の場合は、市販の排水アダプターをご使用ください。
- ・建築側排水管と化粧台開口部に隙間がある場合、シリコンでシーリングしてください。


VP・VU50の場合

VP・VU40の場合

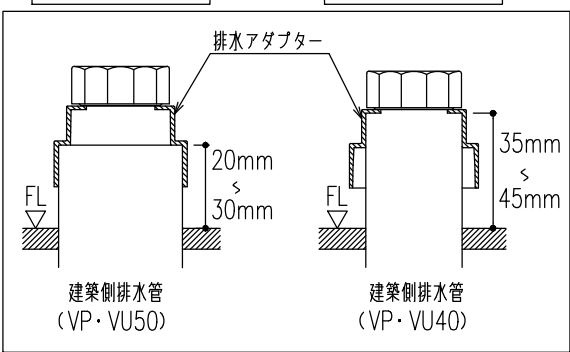


△ 注意

- ・パッキンの向きに注意してください。
- ・管は奥に当たるまで差し込んでください。
- ・袋ナットはしっかり締めてください。
※漏水し、家財などを濡らす拡大損害発生 の恐れがあります。

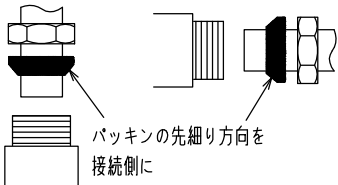

■カウンター・キャビネットを取付可能な壁面


【乾式壁の場合】

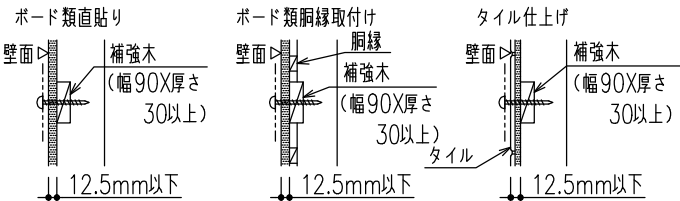


- 「ねじ固定位置」には必ず補強木（幅90mm X 厚み30mm以上）を設けてください。
- 補強木は必ず柱・間柱・縦杭木などの建築躯体に固定してください。
※補強木の固定は、キャビネットの固定強度と同等以上になるよう、種類・数を選定してください。
- 壁固定ねじを補強木に届かせるため、壁仕上の総厚さは12.5mm以下にしてください。

【壁面に補強木が取り付けられない場合】

- 取付壁全面に厚み12mm以上のJAS規格品合板を強固に取り付けてください。【建築工事】

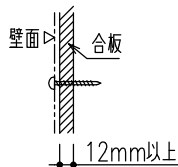

【湿式壁の場合】

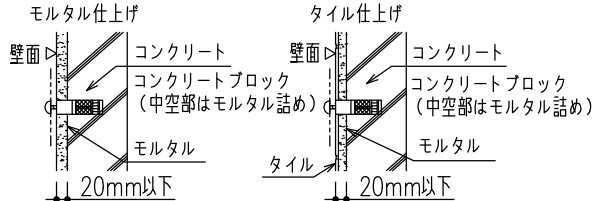

- ※AYボルト取付穴：φ7.5mm深さ60mm以上
- ※プラグ取付穴：φ6mm以上深さ50mm以上

【AYボルト・プラグセット品番】※別途手配品


標準の壁固定ねじの種類	対応AYボルト・プラグセット品番	セット内容
タッピンねじトラス	#KB-4X60T (AY)	M4X60mmトラス2本入り
平頭タッピンねじ	#KB-4X60WT (AY)	M4X60mmなべ2本入り、ワッシャー2個入り
平頭タッピンねじ化粧キャップ付	#KB-4X60SC (AY)	化粧キャップ（白）、皿ワッシャー、M4X60mm皿各2個入り
製品同梱ねじ使用	#MIL-T8	樹脂性プラグ2個入り
タッピンねじトラス	AY-24 (1P)	M6X65mmトラス1本

- 壁固定ねじに合ったAYボルトを使用してください。
※AYボルトを壁本体に届かせるため、壁仕上の総厚さは20mm以下にしてください。
※AYボルト・プラグの種類、必要数はキャビネットにより異なります。
詳しくは取付説明書または洗面化粧台特注マニュアルでご確認ください。

【コンクリートブロック壁の場合】

- ブロック中空部はモルタル詰めする。

■底板詳細図

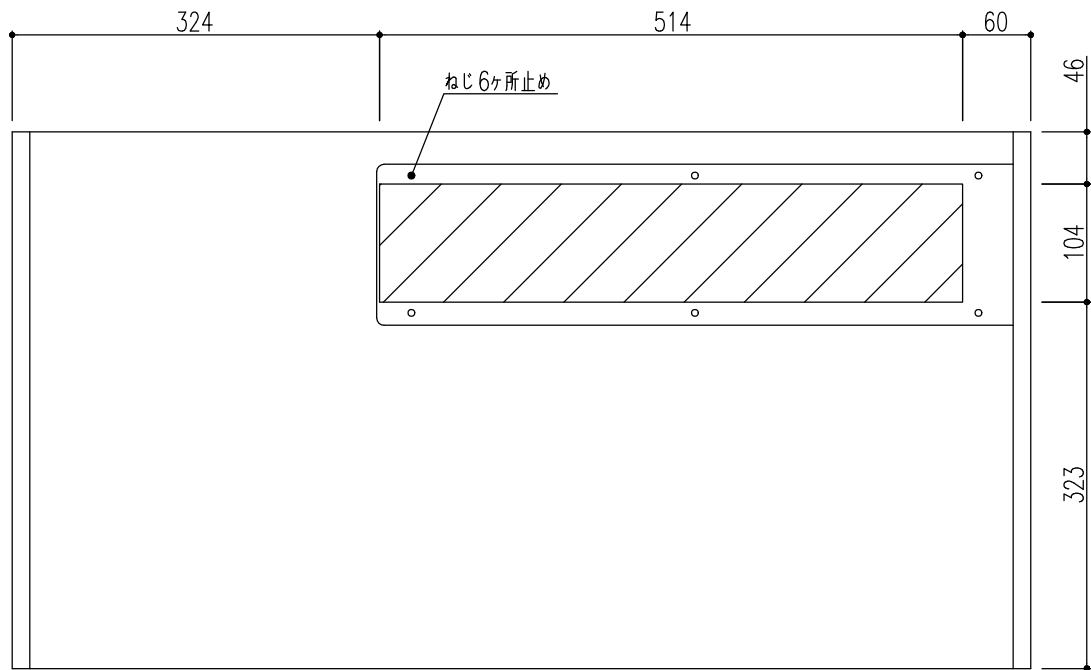

斜線部 底板開口範囲
着脱底板 560x141x2.5t

特記事項

取り付けに関わる情報は機能図に記載しています。
必ず機能図を出力の上ご確認ください。

物件名
仕様

山寄 悟 様邸

EV/奥行500タイプ/23モデル/引出タイプ/シングルレバーシャワー水栓
LED照明（スタンダードLED）/3面鏡（全収納）

案件No.

A2503DDDOEGDPJ

見積No.

M25047301367-009-3

図面名

機能図

縮尺

担当

栗野 友仁

目付

2025.06.03

図面

株式会社 LIXIL

■電源コード取出位置 【3面鏡】

- ※ 1.コード有効長さ：ミラーキャビネット 取出口からの実際のコード寸法です。
- ※ 2.右図は参考図のため、実際のプランとは異なります。
- ※ 3.W キャビネット本体間口は、ミラーキャビネットの間口調整材を含まない寸法です。

【コンセント仕様について】

- 電源は過電流遮断器（110V、15Aまたは20A）の設置された専用の回路からとってください。

【全収納タイプ】LED照明


※ 3キャビネット本体間口	※ 1キャビネット外 （コード有効長さ）			コード取出位置	
W	A	B	C	D	E
750	1400	950	800	150	1110
900	1400	900	800	225	1110
1000	1250	750	700	225	1110
1200	1150	650	700	225	1110

【全収納タイプ】スタンダードLED

※ 3キャビネット本体間口	※ 1キャビネット外 （コード有効長さ）			コード取出位置	
W	A	B	C	D	E
750	1400	950	800	150	1110
900	1400	900	800	225	1110
1000	1350	850	800	225	1110
1200	1250	750	800	225	1110

【スマートポケット付き全収納タイプ】LED照明

※ 3キャビネット本体間口	※ 1キャビネット外 （コード有効長さ）			コード取出位置	
W	A	B	C	D	E
750	1400	950	900	150	1210
900	1400	900	900	225	1210
1000	1350	850	900	225	1210
1200	1250	750	900	225	1210

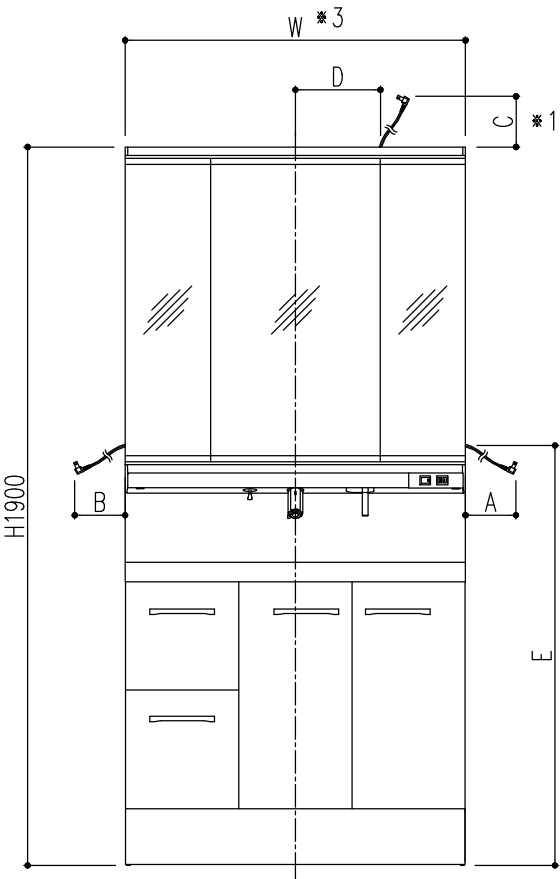

特記事項
取り付けに関わる情報は機能図に記載しています。
必ず機能図を出力の上ご確認ください。

物件名

仕様

山寄 悟 様邸
EVノ奥行500タイプノ23モデルノ引出タイプノシングルレバーシャワー水栓
LED照明（スタンダードLED）ノ3面鏡（全収納）




案件No.
A2503DDD0EGDPJ
見積No.
M25047301367-009-3

図面名
機能図
縮尺

担当
栗野 友仁
日付
2025.06.03

図番
：
株式会社 LIXIL

	図面	品名	品番	色板	数
1	○	ベーシア便器部（床排水）	BC-B30S/BW1		1
2	○	ベーシアシャワートイレ機能部（ECO5・手洗付・B3グレード）	DT-B383/BW1		1
3	○	ワンタッチ式紙巻器	CF-AA22H/WA		1
4	○	タオルリング	KF-AA70D		1

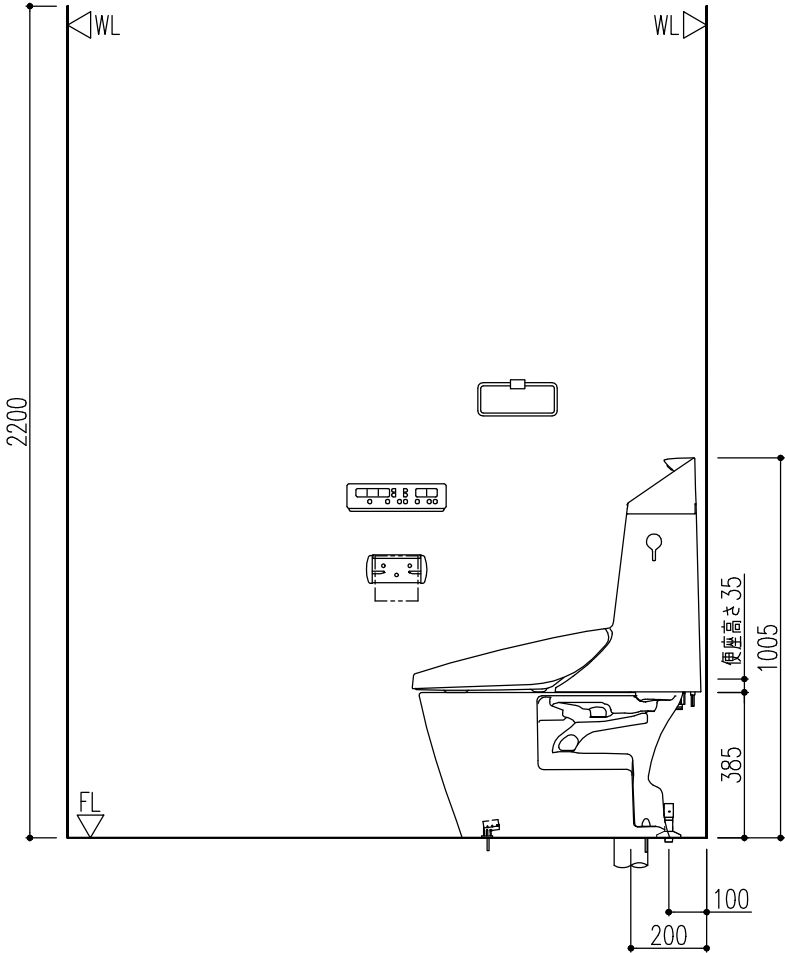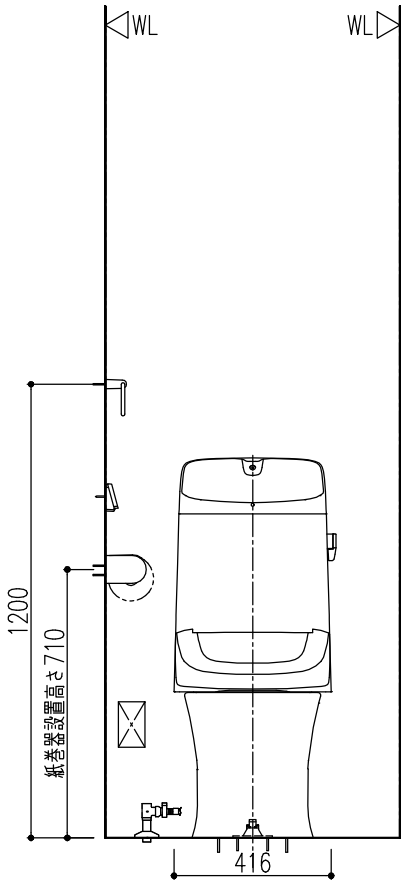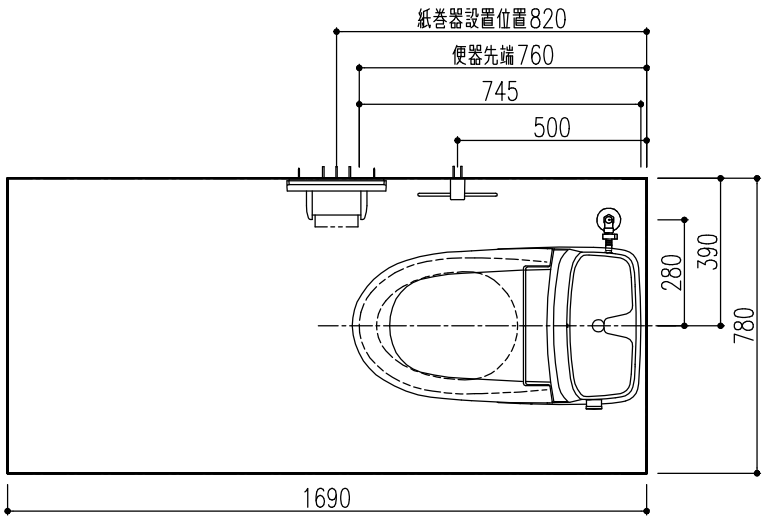

【共通】

※ 部品表の「図面」列に○がないものは図面表示されません。

・このプランの施工情報については事前に商品の施工説明書や工事用図面集にてご確認ください。

2枚目以降の機能図にも商品情報の記載があります。

・商品仕様・図面の改良や仕様変更等は、予告なく行う場合があります。

・壁面に取り付ける商品にはあらかじめ壁補強が必要です。必要な壁面工事は2枚目以降の機能図にてご確認ください。

・壁埋込みの必要な商品にはあらかじめ商品に合わせた開口を行ってください。

・電源が必要な商品には、商品の仕様に合わせてコンセント設置等の電気工事（別途工事）をあらかじめ行ってください。商品の施工説明書にて工事内容をご確認ください。

・コンセントは、電源コードの届く範囲で床面より高く水のかからない位置に設置してください。

また、コンセントの壁給水真下部設置や給水ホースとの接触は感電・火災の原因になりますので避けてください。

・扉等の建築物による干渉をご確認ください。

・アクセサリ類・手洗器の設置位置は参考寸法です。使いやすさに合わせて取付位置を決定ください。

・（ ）内寸法は、参考寸法です。

・陶器寸法許容差はJIS A5207に準じています。

・結露水・小水によるシミの発生を防ぐため、トイレ床材には防水加工が施された床材をご使用ください。

【便器】

・洗浄水量：大5L、小3.8L

・製品両側面から70mm以上の空間を確保してください。

・タンク上部に棚等を設置する場合は、床から1150mm以上の空間が必要です。

・一般地用、寒冷地用流動式兼用品です。

・トイレ内使用限界：－10℃以上、流動水量60L/h。

0℃を下回る場合は器具内の水を流動させてください。

・凍結防止には器具への通電が必要です。

・D種接地工事が必要です。アースターミナル付接地極付コンセントを使用してください。

・定格消費電力330W（タンク部）

・機能部電源コード長さ1000mm

・インバータ照明により誤作動する場合があります。














（重要）

排水管の立ち上げ高さは床仕上り面から60±5mmにしてください。排水管が床仕上り面と同じ高さの場合は市販の60mm立ち上げ用部材（持ち出しニップル）を別途手配ください。

	特記事項	物件名	山寄 悟 様邸	案件No.	図面名	担当	図面	図番
				A2503DDD0EGDPJ	簡易取付設置図	栗野 友仁		株式会社 LIXIL
		仕様	ベアシアシャワートイレ／EC05 床排水 一般地	見積No.	縮尺	日付		
				M25047301367-009-4	1/20	2025.06.03		

●アクセサリー 施工要領図




壁取付アクセサリーの落下事故防止のため、取付部材（木ねじ、AYボルト等）の固定強度（種類・数）については十分配慮を行っておりますが、壁面の構造についても配慮いただくことが不可欠です。

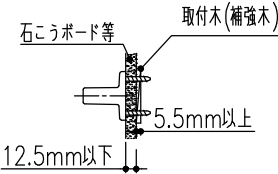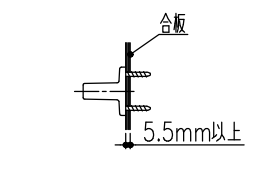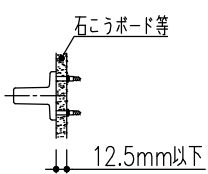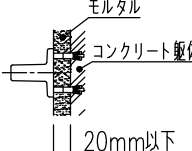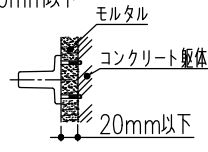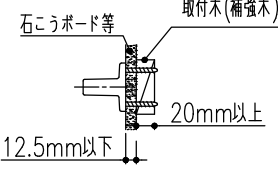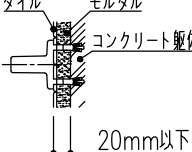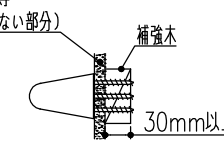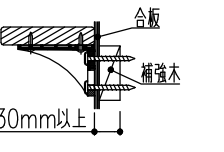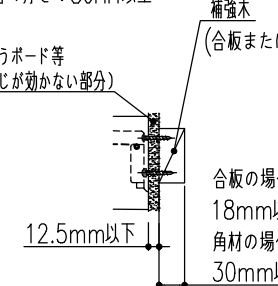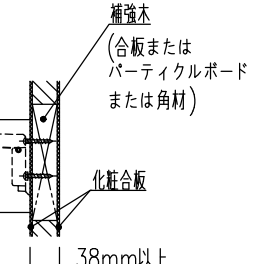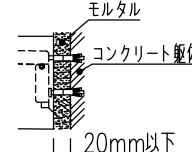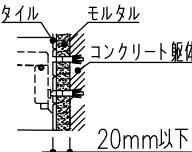アクセサリー種類	乾 式 壁			湿 式 壁	
	木 ね じ	木ねじ+プラスチックプラグ	パ ー テ ー シ ョ ン 壁	A Y ボ ル ト	木ねじ+プラスチックプラグ
紙巻器 化粧鏡 石けん入れ	ねじ込み深さ：5.5mm以上 	取付不可	取付不可	壁仕上材厚さ：20mm以下	取付不可
化粧鏡	12.5mm以下 	石こうボード壁厚：9.5mm以上 12.5mm以下 			
紙巻器 石けん入れ	5.5mm以上	12.5mm以下		20mm以下	壁仕上材厚さ：20mm以下 
紙巻器	ねじ込み深さ：20mm以上 	取付不可			壁仕上材厚さ：20mm以下 
フック タオル掛 化粧棚 紙巻器 タオルリング 化粧鏡 スベアペーパーホルダー サニタリーボックス	合板 取付木（補強木） 20mm以上			20mm以下	取付不可
アクセサリーパー 棚手すり 紙巻器 タオル棚 手すり 照明付鏡	ねじ込み深さ：30mm以上 石こうボード等 （ねじが効かない部分） 補強木 30mm以上  				
棚付二連紙巻器 横2連ストック付紙巻器 横4連ストック付紙巻器	合板の場合の厚さ：18mm以上 角材の場合の厚さ：30mm以上 		パーテーション （化粧合板+補強木）の厚さ：38mm以上 	壁仕上材厚さ：20mm以下  	

待記事項	物件名	山寄悟 様邸	案件No.	図面名	担当	図面	図番	
			A2503DDD0EGDPJ	機能図	栗野 友仁		株式会社 LIXIL	
		仕様	ベーシアシャワートイレ／ECO5 床排水 一般地	見積No.	縮尺	日付		
				M25047301367-009-4		2025.06.03		

●便器床設置面寸法・固定穴寸法				●給排水の位置決めと取出し				●排水塩ビ管の接続			
				給水管、排水管を取り出します。 ※ 給水管、排水管を施工寸法通りに取り出します。 誤って排水管を壁寄りに取り出した場合は、タンクと壁が干渉して施工できない恐れがあります。				※ 接続は、塩ビ接着剤にて確実に行なって下さい。 ※ 排水管の立ち上げ高さは、必ず60±5mmの位置で切断してください。 施工方法詳細の動画を以下から読み取ることができます。 ・ 通信料はお客様のご負担となります。 ・ お使いの環境・端末によっては、閲覧できない場合があります。 ・ 実物と動画のデザインが異なる場合があります。 ・ 動画内に表示される商品名と品番・デザインが異なる場合がありますが、施工手順に影響ありません。 ※注…立ち上げ寸法が60mm以下の場合は 既設配管に合った、市販の60mm立ち上げ用部材(持ち出しニップル)を別途手配ください。 ※注…防振シートを組み合わせる場合は5mm高くしてください。			
●取付最小スペース		●便フタ開時寸法									
※ 最小スペースはA寸法(前出寸法) + 400となり、便器排水方向や既設配管により、異なります。 A寸法は、床排水・床上排水(後抜き)の場合760mm、床上排水(横抜き)の場合860mmとなります。 ご確認ください。 ※ 右図の空間寸法は、衣服の着脱などの行為に必要な最低寸法です。 手すりや紙巻器などの機器を併設する場合は、必要に応じた広い空間が必要になります。 ※ 便器に向かって左右共に70mm以上の空間を確保してください。		※ 上図は代表商品のイメージ図です。 ※ 防振シートを組み合わせる場合は、全体が5mm高くなります。									
特記事項		物件名	山寄 悟 様邸		案件No.	図面名	担当	図面	図番		
		仕様	ベージャシャワートイレノECO5 床排水 一般地		A2503DDD0EGDPJ	機能図	栗野 友仁		株式会社 LIXIL		
					見積No.	縮尺	日付				
					M25047301367-009-4		2025.06.03				

	図面	品名	品番	色板	数
1	○	ベシア便器部（床排水）	BC-B30S/BW1		1
2	○	ベシアシャワートイレ機能部（ECO5・手洗付・B3グレード）	DT-B383/BW1		1
3	○	ワンタッチ式紙巻器	CF-AA22H/WA		1
4	○	タオルリング	KF-AA70D		1

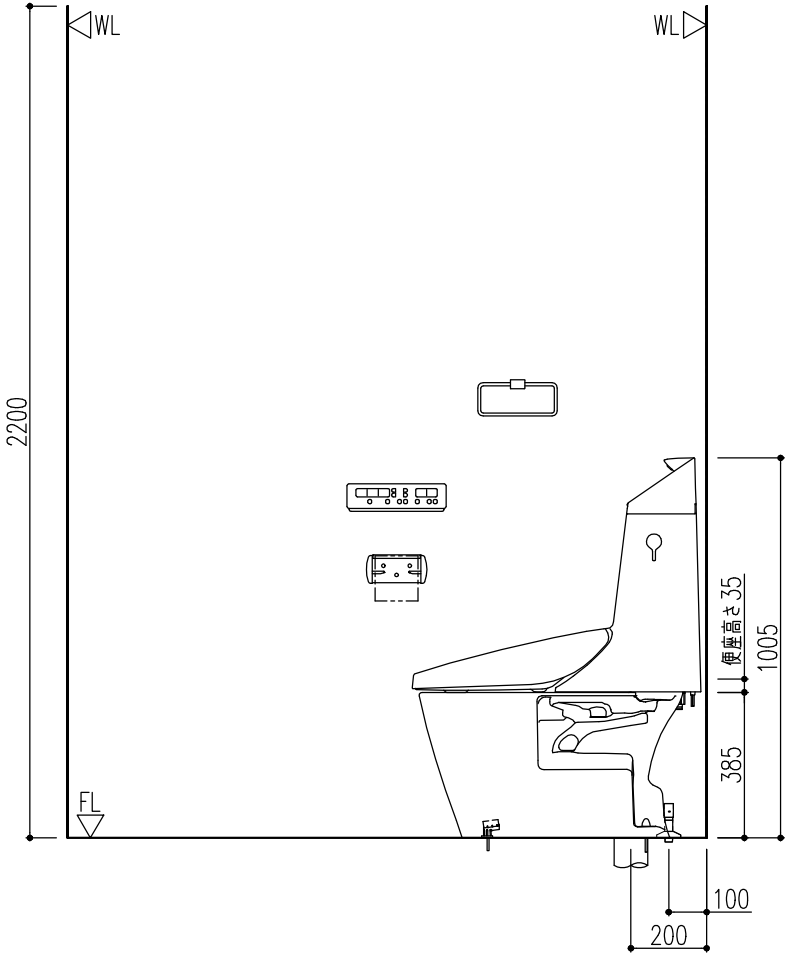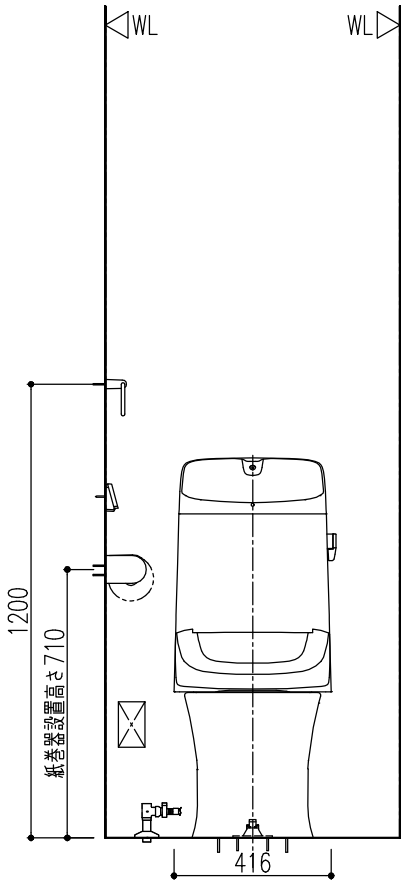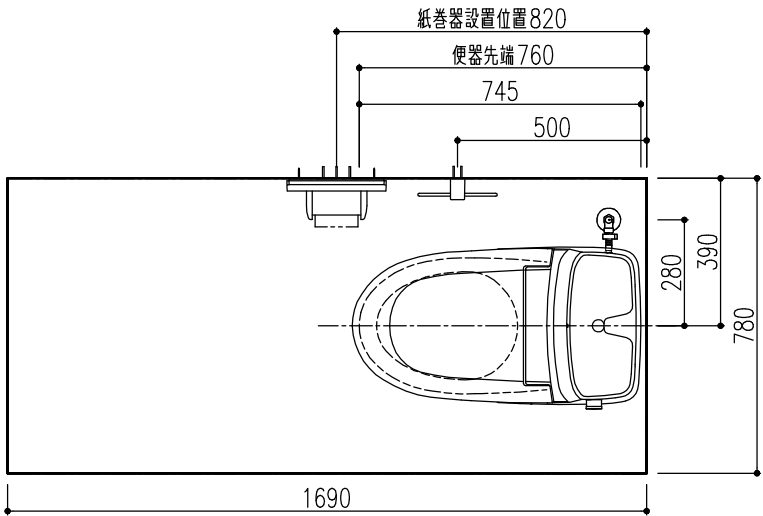

【共通】

- ※ 部品表の「図面」列に○がないものは図面表示されません。
- ・このプランの施工情報については事前に商品の施工説明書や工事用図面集にてご確認ください。
2枚目以降の機能図にも商品情報の記載があります。
- ・商品仕様・図面の改良や仕様変更等は、予告なく行う場合があります。
- ・壁面に取り付ける商品にはあらかじめ壁補強が必要です。必要な壁面工事は2枚目以降の機能図にてご確認ください。
- ・壁埋込みの必要な商品にはあらかじめ商品に合わせた開口を行ってください。
- ・電源が必要な商品には、商品の仕様に合わせたコンセント設置等の電気工事（別途工事）をあらかじめ行ってください。商品の施工説明書にて工事内容をご確認ください。
- ・コンセントは、電源コードの届く範囲で床面より高く水のかからない位置に設置してください。
また、コンセントの壁給水真下部設置や給水ホースとの接触は感電・火災の原因になりますので避けてください。
- ・扉等の建築物による干渉をご確認ください。
- ・アクセサリ類・手洗器の設置位置は参考寸法です。使いやすさに合わせて取付位置を決定ください。
- ・（ ）内寸法は、参考寸法です。
- ・陶器寸法許容差はJIS A5207に準じています。
- ・結露水・小水によるシミの発生を防ぐため、トイレ床材には防水加工が施された床材をご使用ください。

【便器】

- ・洗浄水量：大5L、小3.8L
- ・製品両側面から70mm以上の空間を確保してください。
- ・タンク上部に棚等を設置する場合は、床から1150mm以上の空間が必要です。
- ・一般地用、寒冷地用流動式兼用品です。
- ・トイレ内使用限界：－10℃以上、流動水量60L/h。
0℃を下回る場合は器具内の水を流動させてください。
- ・凍結防止には器具への通電が必要です。
- ・D種接地工事が必要です。アースターミナル付接地極付コンセントを使用してください。
- ・定格消費電力330W（タンク部）
- ・機能部電源コード長さ1000mm
- ・インバータ照明により誤作動する場合があります。















【重要】

排水管の立ち上げ高さは床仕上り面から60±5mmにしてください。排水管が床仕上り面と同じ高さの場合は市販の60mm立ち上げ用部材（持ち出しニップル）を別途手配ください。

	特記事項	物件名	山寄 悟 様邸	案件No.	図面名	担当	図面	図番
				A2503DDD0EGDPJ	簡易取付設置図	栗野 友仁		株式会社 LIXIL
		仕様	ベアシアシャワートイレ／EC05 床排水 一般地	見積No.	縮尺	日付		
				M25047301367-009-5	1/20	2025.06.03		

●アクセサリー 施工要領図

壁取付アクセサリーの落下事故防止のため、取付部材（木ねじ、AYボルト等）の固定強度（種類・数）については十分配慮を行っておりますが、壁面の構造についても配慮いただくことが不可欠です。

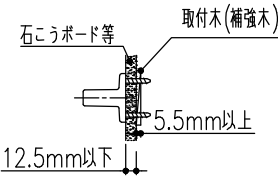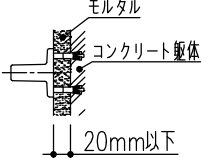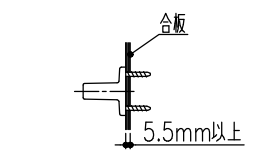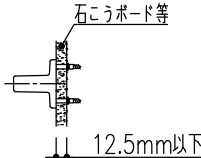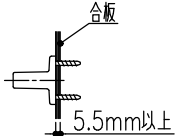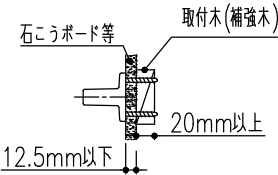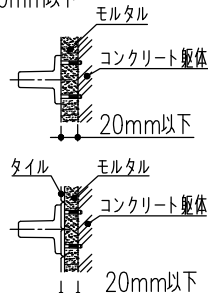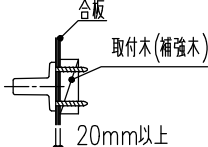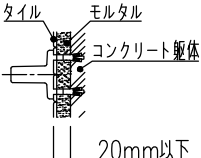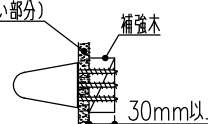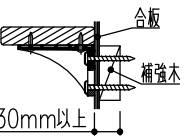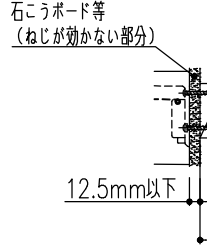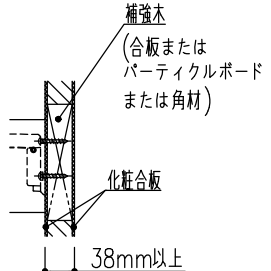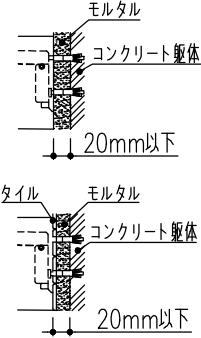アクセサリー種類	乾 式 壁			湿 式 壁	
	木 ね じ	木ねじ+プラスチックプラグ	パ ー テ ー シ ョ ン 壁	A Y ボ ル ト	木ねじ+プラスチックプラグ
紙巻器 化粧鏡 石けん入れ	ねじ込み深さ：5.5mm以上 	取付不可	取付不可	壁仕上材厚さ：20mm以下 	取付不可
化粧鏡	12.5mm以下 	石こうボード壁厚：9.5mm以上 12.5mm以下 			
紙巻器 石けん入れ	5.5mm以上 				
紙巻器	ねじ込み深さ：20mm以上 	取付不可			壁仕上材厚さ：20mm以下 
フック タオル掛 化粧棚 紙巻器 タオルリング 化粧鏡 スベアペーパーホルダー サニタリーボックス	20mm以上 				取付不可
アクセサリーパー 棚手すり 紙巻器 タオル棚 手すり 照明付鏡	ねじ込み深さ：30mm以上 石こうボード等 （ねじが効かない部分）   合板含め30mm以上				
棚付二連紙巻器 横2連ストック付紙巻器 横4連ストック付紙巻器	合板の場合の厚さ：18mm以上 角材の場合の厚さ：30mm以上  12.5mm以下	補強木 （合板または角材） 合板の場合：18mm以上 角材の場合：30mm以上	パーティション （化粧合板+補強木）の厚さ：38mm以上  38mm以上	壁仕上材厚さ：20mm以下  20mm以下	

特記事項	物件名	山寄 悟 様邸	案件No.	図面名	担当	図面	図番
			A2503DDD0EGDPJ	機能図	栗野 友仁		株式会社 LIXIL
		仕様	ベ－シアシャワ－トイレノEC05 床排水 一般地	見積No.	縮尺	日付	
				M25047301367-009-5		2025.06.03	

●便器床設置面寸法・固定穴寸法		●給排水の位置決めと取出し		●排水塩ビ管の接続					
		給水管、排水管を取り出します。 ※ 給水管、排水管を施工寸法通りに取り出します。 誤って排水管を壁寄りに取り出した場合は、タンクと壁が干渉して施工できない恐れがあります。		※ 接続は、塩ビ接着剤にて確実に行なって下さい。 ※ 排水管の立ち上げ高さは、必ず60±5mmの位置で切断してください。 施工方法詳細の動画を以下から読み取ることができます。 ・ 通信料はお客様のご負担となります。 ・ お使いの環境・端末によっては、閲覧できない場合があります。 ・ 実物と動画のデザインが異なる場合があります。 ・ 動画内に表示される商品名と品番・デザインが異なる場合がありますが、施工手順に影響ありません。 ※注…立ち上げ寸法が60mm以下の場合は 既設配管に合った、市販の60mm立ち上げ用部材(持ち出しニップル)を別途手配ください。 ※注…防振シートを組み合わせる場合は5mm高くしてください。					
●取付最小スペース		●便フタ開時寸法							
※ 最小スペースはA寸法(前出寸法) + 400となり、便器排水方向や既設配管により、異なります。 A寸法は、床排水・床上排水(後抜き)の場合760mm、床上排水(横抜き)の場合860mmとなります。 ご確認ください。 ※ 右図の空間寸法は、衣服の着脱などの行為に必要な最低寸法です。 手すりや紙巻器などの機器を併設する場合は、必要に応じた広い空間が必要になります。 ※ 便器に向かって左右共に70mm以上の空間を確保してください。		※ 上図は代表商品のイメージ図です。 ※ 防振シートを組み合わせる場合は、全体が5mm高くなります。							
特記事項		物件名	山寄 悟 様邸		案件No.	図面名	担当	図面	図番
		仕様	ベージャシャワートイレノECO5 床排水 一般地		A2503DDD0EGDPJ	機能図	栗野 友仁		株式会社 LIXIL
					見積No.	縮尺	日付		
					M25047301367-009-5		2025.06.03		