

G2

壁付付		住宅用火災報知器	数量
H 熱感知	熱感知器	電池式(単独型)	1
		露出型	

壁付付		住宅用火災報知器	数量
S 煙感知	煙感知器	電池式(単独型)	
		露出型	


※ 煙感知器は壁・梁より600mm以上離す
壁に取付ける場合、
天井から150mm以上500mm以内離す
換気扇・エアコン吹出口から1500mm以上離す
※ 全室LED照明とし、居室においては調光
制御、非居室においては人感センサーを
採用する。
※ 標準天井高さ2,400
※ 特記無きガラスは型ガラス

- * 凡例
- 管柱 (105×105)
 - K9' ムー (3.30倍 FRM-0641)
 - 片筋違い (2.00倍 45×90)
(例 左: 柱脚 右: 柱頭)
 - たすき掛筋違い (4.00倍 45×90)
 - 構造用合板 (2.70倍)
(t=9 タイガ EXH(ハバ))
 - 床点検口
 - 天井点検口
 - 換気扇
 - 熱交換換気扇VLR-70

アドバンスシリーズ	
スマートデザイン (外部)	
凡例	
①	コンセント 1ヶ所
②	コンセント 2ヶ所
③	コンセント 3ヶ所
①ET	コンセント1ヶ所接地ターミナル付
②ET	コンセント2ヶ所接地ターミナル付
①WP	コンセント 防水型
②WP	エアコン用コンセント
③WP	200V用コンセント
④WP	防雨入線プレート
⑤	スイッチ
③	3路スイッチ
④	4路スイッチ
⑥	直結電源
⑦TV	テレビ取出口
⑧TEL	電話取出口 (テレホンガイド)
⑨LAN	LAN取出口 (テレホンガイド)
⑩	壁照明
⑪	リモコン (給湯関係・ルフロ)
⑫	メーター
⑬	分電盤
⑭	チャイム

※ACコンセント天井付け
※TVアンテナ工事
※スイッチはFL+1100、コンセントはFL+200

決定図

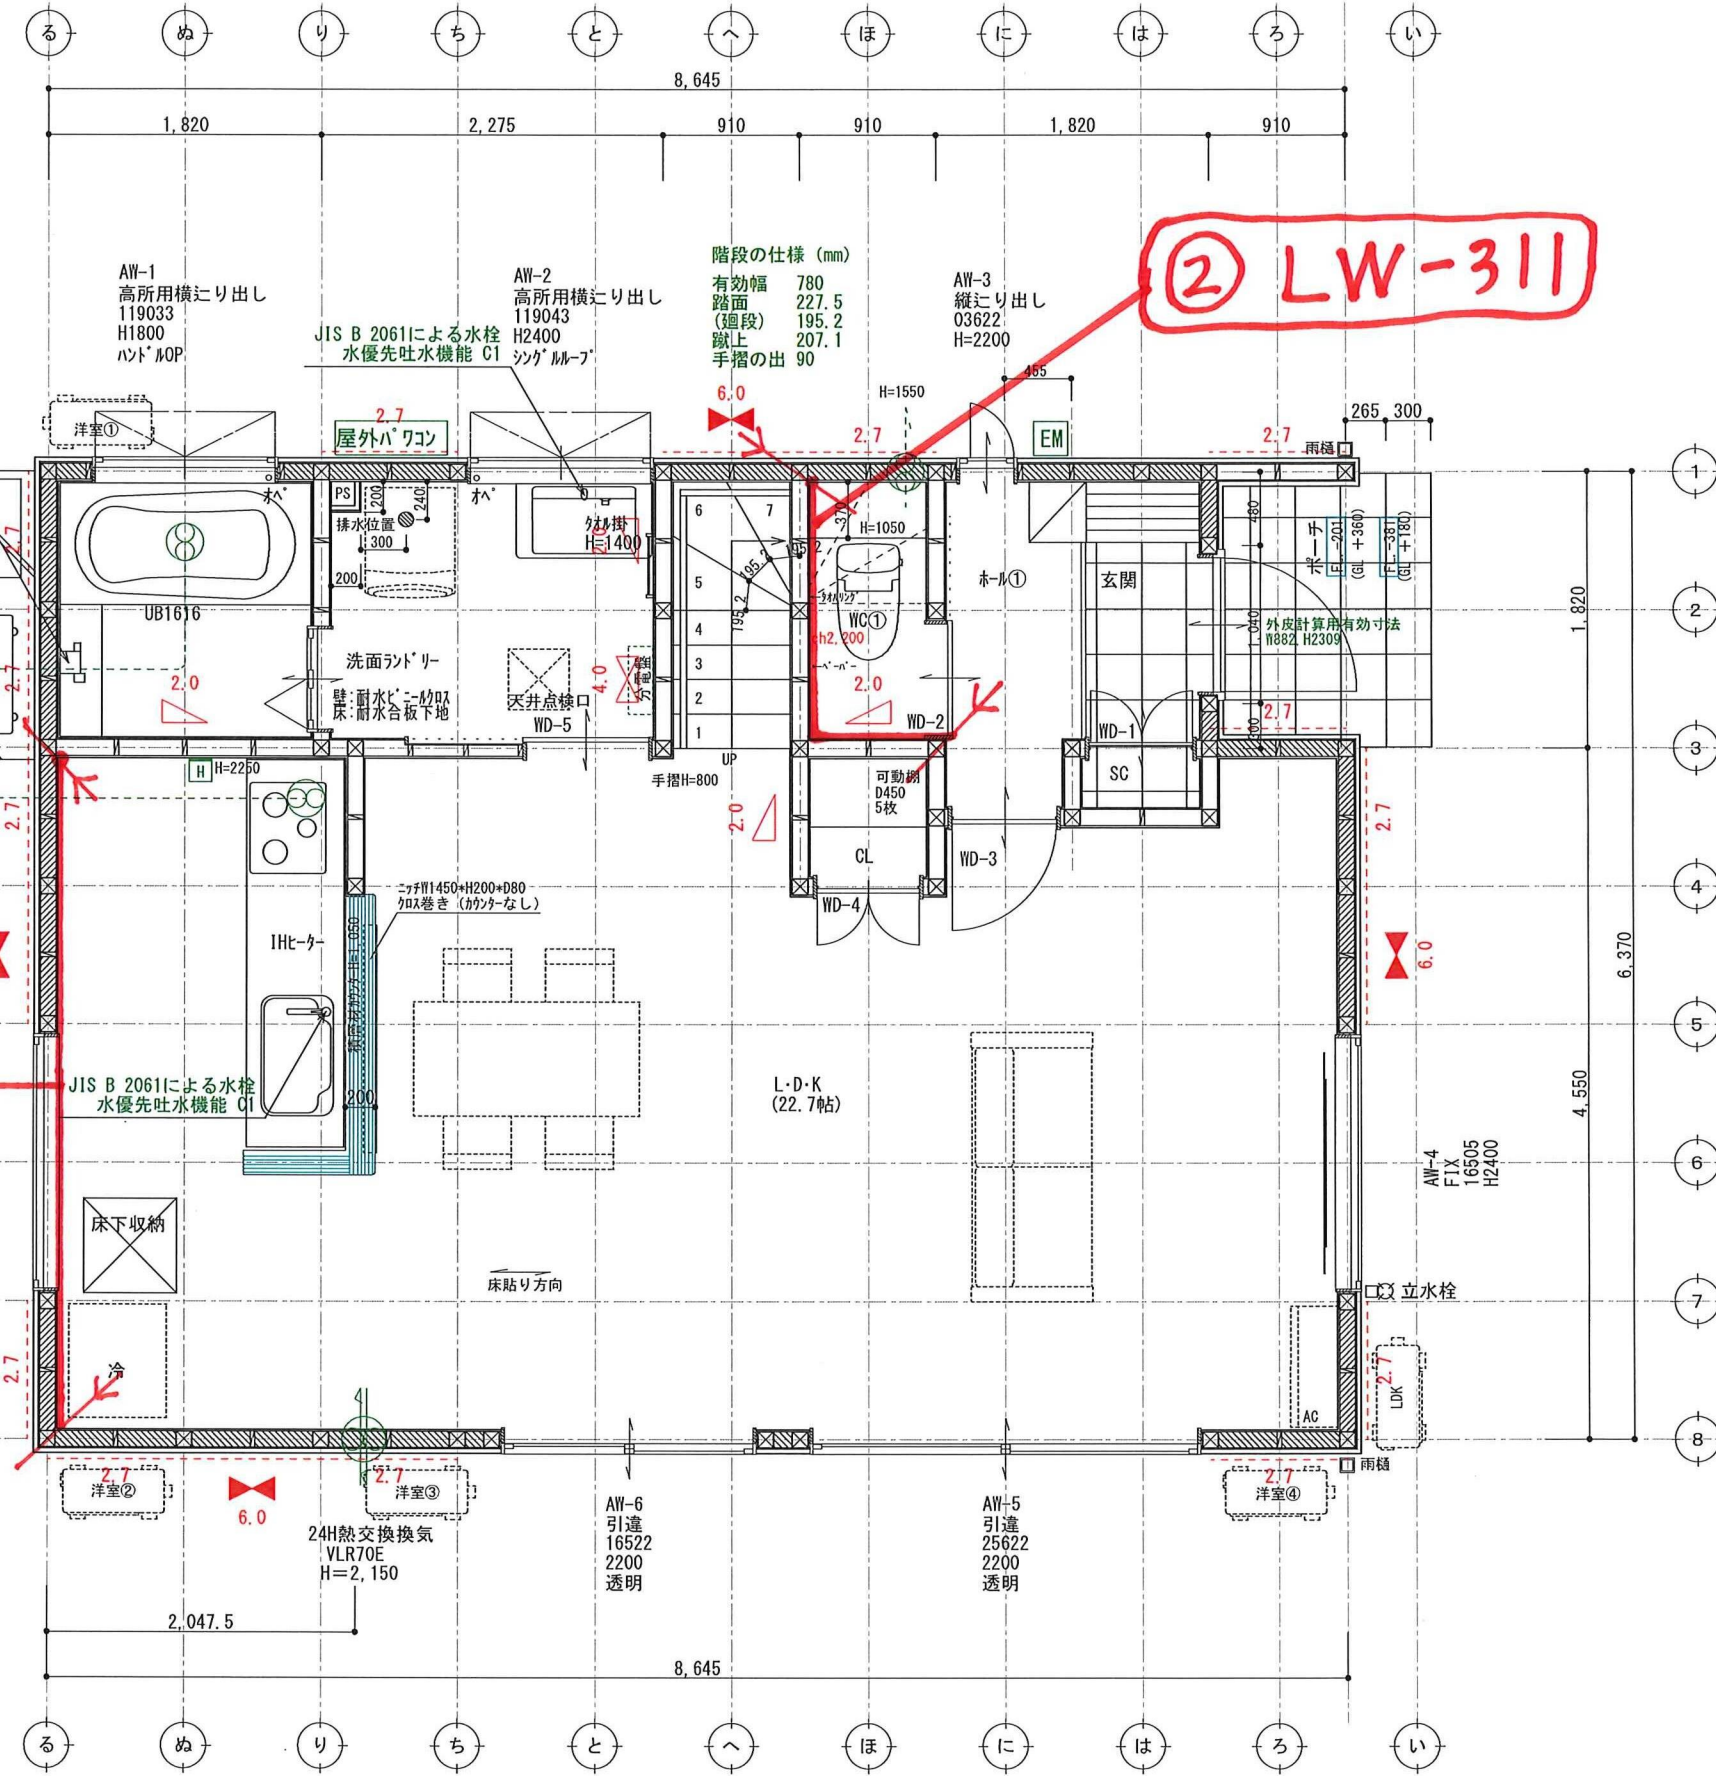

DBA7094

② LW-311

G2

壁付け 住宅用火災報知器			数量
H 熱感知	電池式(単独型)		
	露出型		
壁付け 住宅用火災報知器			数量
S 煙感知	電池式(単独型)		8
	露出型		

- ※ 煙感知器は壁・梁より600mm以上離す
壁に取付ける場合、
天井から150mm以上500mm以内離す
換気扇・エアコン吹出口から1500mm以上離す
- ※ 全室LED照明とし、居室においては調光
制御、非居室においては人感センサーを
採用する。
- ※ 標準天井高さ2,400
- ※ 特記無きガラスは型ガラス

- * 凡例
- ☒ 管柱 (105×105)
- ≡ Kダクト (3.30倍 FRM-0641)
- △ 片筋違い (2.00倍 45×90)
(例 左:柱脚 右:柱頭)
- ⊠ たすき掛筋違い (4.00倍 45×90)
- 構造用合板 (2.70倍)
(t=9 タガ-EXハイパー)
- △ 床点検口
- ⊠ 天井点検口
- ⊗ 換気扇
- ⊗ 熱交換換気扇VLR-70

アドバンスシリーズ	
スマートデザイン (外部)	
凡例	
①	コンセント 1ヶ所
②	コンセント 2ヶ所
③	コンセント 3ヶ所
①ET	コンセント1ヶ所接地ターミナル付
②ET	コンセント2ヶ所接地ターミナル付
WP	コンセント 防水型
WP	エアコン用コンセント
WP	200V用コンセント
WP	防雨入線プレート
●	スイッチ
●3	3路スイッチ
●4	4路スイッチ
⊗	直結電源
⊗TV	テレビ取出口
⊗TEL	電話取出口 (テレホンガイド)
⊗LAN	LAN取出口 (テレホンガイド)
⊗	壁照明
⊗	リモコン (給湯関係・ルフロ)
⊗	メーター
⊗	分電盤
⊗	チャイム

- ※ACコンセント天井付け
- ※TVアンテナ工事
- ※スイッチはFL+1100、コンセントはFL+200

決定図

