

■ 仕 様			■ HEAT20 G2
断熱工事	■ 床:ネオマフォーム t90 ■ 土間床等の外周:スタイロフォームAT t50 ■ 壁:アクアフォームLITE吹付 t90 ■ 天井:アクファフォームLITE吹付 t220		
床下換気	■ 基礎パッキン JOTO (玄関・UB周り:気密基礎パッキン)		
防虫防蟻	■ 土壌処理・木部 ガントナーMC		
■ 外 部 仕 上 表			■ 22条地域
部位	仕上・仕様・メーカー	色番・品番	
屋根	■ ガルバリウム鋼板(t0.35)UK立平 ニスクカラーPro GH 軒先通気金物 日本住環境株式会社【REV-15】	GHK01 Sブラック	
パラペット笠木	■ なし		
破風・鼻隠	■ なし		
雨樋	(軒樋) ■ Panasonic サーフeskエアFS-I型	ブラック	
	(縦樋) ■ Panasonic S30角樋	ブラック	
軒天	屋根軒 ■		
	ポーチ軒 ■ 神島化学 t= 6mm 軒天ボード エンボス	WEボニーブラウン	
	バルコニー軒 ■		
オーバーハング水切り	■ ガルバリウム鋼板 ※外壁合わせ JOTO:HF-A3550	ブラック	
外壁 通気金物(15mm) ※下地面材:タイガーEXハイパー 防火認定 PC030BE-4028	■メイン Kmewエクセラージ・ピエトラレリーフ	エピックブラック	
	■アクセントA なし		
	■アクセントB なし		
玄関ポーチ	■ 床 玄関に同じ	-	
基礎	■ 立上り巾木: モルタル刷毛引き	-	
基礎水切り金物	■ JOTO鋼板製 防鼠材付き水切り JOTO:WMF-N35	ブラック	
バルコニー	床・内壁 ■ なし	-	
	笠木 ■ なし		
外部建具	■ LIXIL EW(アルゴンガス高遮熱仕様LowEトリプルガラス クリア) ・SD、TSは、メーカー設定によるが、オペレーターハンドル優先とする ・オペレーター付サッシの場合は固定網戸とする ・グレモンハンドル式サッシの場合は可動網戸とする	外観 ブラック 内観 ホワイト ※樹脂パッキン・網戸付	
シャッター	■ なし		
軒天通気金物			
玄関扉	■ LIXIL ジエスタ2 K2仕様 LIXILファミロック タグキー×3 (電池式)	ドア型: M14 型 ドア色: クリアダーク ハンドル: S型ハンドル 色 ブラック	
外部物干し金物	■		
換気フード	■ 局所換気扇(トイレ 浴室 キッチンフード) 防火ダンパー無 ■ ダクトレス熱交換換気システム (日本スティーベル株式会社) VLR-70E 防火ダンパー無	外気フード: ブラック 外気フード: B ブラック 室内パネル ホワイト	

■ 構 造 概 要					
基礎	■ RCベタ基礎コンクリート				
通し柱・管柱	■ 構造用集成材 105×105		間柱	■ 集成材	
土台	■ 桧 105×105	大引き	■ 桧 90*90	筋交い	■ 構造用製材 火打梁 ■ 鋼製火打(当社基準により米松あり)
桁・梁	■ 構造用製材及び集成材			制震装置	■ Kダンパー (株)アイ・エム・エー
■ 設 備 装 着 品					
住宅設備	部位	メーカー	商品名 ※ 詳細は見積り、プレゼン参照	見積りNo.	(日付)
	キッチン	LIXIL	■ ES I型 扉グレー・ジュスタッコ 天板ソルティホワイト キッチンパネル:ラフサントホワイト 標準食洗器 標準IH、壁付レンジフードASR(ホワイト) スリム取手シャインニッケル	見積り番号 : M25047301367-010-2	(日付) 2025.6.6
	浴室	LIXIL	■ AX1616 PGハウス標準仕様 アクセント壁:モルティオダーク 浴槽:ミナモ ホワイト 床:グレー マグネットシェフ:ブラック	見積り番号 : M25047301367-010-1	(日付) 2025.6.6
	1Fトイレ	LIXIL	■ ベーシアシャワートイレ 白 ● タオル掛け: KF-AA70D(リング) タンク手洗 有り ● 紙巻き器: CF-AA22H /WA	見積り番号 : M25047301367-010-4	(日付) 2025.6.6
	2Fトイレ	LIXIL	■ ベーシアシャワートイレ 白 ● タオル掛け: KF-AA70D(リング) タンク手洗 有り ● 紙巻き器: CF-AA22H /WA	見積り番号 : M25047301367-010-5	(日付) 2025.6.6
	洗面台	LIXIL	■ EV W900(D500タイプ) 扉:グロスホワイト [引出しタイプ シングルハンドシャワー スタンダードLED三面鏡 その他 ● タオル掛け:KF-AA71D(バー)	見積り番号 : M25047301367-010-3	(日付) 2025.6.6
給排水設備	給湯器	■ エコキュート370L Panasonic Sシリーズ スタンダードモデル 追い焚きフルオート			
	排水	■ 下水			
	外水栓	■ 1 カ所 (平面図参照)		■ 外部立栓柱: PVC製 水栓柱12型【前澤化成工業】	
	外部ガーデンパン	■ 無し			
	その他	■ 洗濯機用単水栓: 緊急止水弁付 ■ 洗濯機用排水:トラップ金物(標準) ■ 排水さや管(長期優良住宅仕様)			
ガス配管設備		■ なし (配置図・平面図参照)		■ ガス使用器具	
電気設備	インターホン	■ パナソニック VL-SZ30KL			
	TVアンテナ	■ UHF + BS・110度CS／CSアンテナ [2K・4K・8K対応] ■ホワイト			
	エアコン	■ 設置場所:			
	ソーラー	■ あり(Qセルズ) 12 枚 5.28 KW Re.RISE-G3 440 (1722×1134×30)			
	※標準搭載	※メーカーのモデルチェンジ等で後継品に変更される可能性あり ■ 屋外パワコン エネルギーマネジメントシステム CubeJ			
その他					
決定図					

決定図



内 部 仕 上 表 （壁下地:石膏ボード12.5mm/天井下地:9.5mm）※脱衣室:床合板特類 下地									
階		床	巾木	壁	品番	廻 縁	天 井	品番	特記事項
1F	ポーチ	LIXILパセオ300/PSO-FIO 4							
	玄関	LIXILパセオ300/PSO-FIO 4		ビニルクロス	SLP-252	突付	ビニルクロス	SLP-252	付框
	ホール①	イタ銘木フロアーラステックt12 ハードメイプル3P	ライン巾木(W)	ビニルクロス	SLP-252	突付	ビニルクロス	SLP-252	
	LDK	イタ銘木フロアーラステックt12 ハードメイプル3P	ライン巾木(W)	ビニルクロス	SLP-252	突付	ビニルクロス	SLP-252	アクセントクロス キッチン西側 BA7094
	脱衣ランドリー	フロアタイルt2.3 サンゲツIS-2071	H40ソフト巾木W97	ビニルクロス	SLP-252	突付	ビニルクロス	SLP-252	
	WC①	フロアタイルt2.3 サンゲツIS-2070	H40ソフト巾木W97	ビニルクロス	SLP-252	突付	ビニルクロス	SLP-252	アクセントクロス LW-311
2F									
	ホール②	イタ銘木フロアーラステックt12 ハードメイプル3P	ライン巾木(W)	ビニルクロス	SLP-252	突付	ビニルクロス	SLP-252	
	洋室①	イタ銘木フロアーラステックt12 ハードメイプル4P	ライン巾木(W)	ビニルクロス	SLP-252	突付	ビニルクロス	SLP-252	
	洋室②	イタ銘木フロアーラステックt12 ハードメイプル5P	ライン巾木(W)	ビニルクロス	SLP-252	突付	ビニルクロス	SLP-252	
	洋室③	イタ銘木フロアーラステックt12 ハードメイプル6P	ライン巾木(W)	ビニルクロス	SLP-252	突付	ビニルクロス	SLP-252	アクセントクロス LL-6455
	洋室④	イタ銘木フロアーラステックt12 ハードメイプル7P	ライン巾木(W)	ビニルクロス	SLP-252	突付	ビニルクロス	SLP-252	
	WIC	イタ銘木フロアーラステックt12 ハードメイプル8P	ライン巾木(W)	ビニルクロス	SLP-252	突付	ビニルクロス	SLP-252	
	WC②	フロアタイルt2.3 サンゲツIS-2071	H40ソフト巾木W97	ビニルクロス	SLP-252	突付	ビニルクロス	SLP-252	
物入・収納・CL etc		※接続する部屋と同仕様とする							

上 框 ※	■ LIXILラシッサS 上框のみ30×150 色: クリエペール		
階 段	■ LIXIL KA 階段	ササラ:	クリエアイボリー
KA階段で対応できない場合、オプション	段 板 :	クリエアイボリー	蹴込板: プレシャスホワイト
にてラシッサS階段	ラウンド手摺:	プレシャスホワイト	手摺金物 プレシャスホワイト
	上段框:	クリエアイボリー	長尺笠木156: LIXIL クリエアイボリー
窓 枠	■ LIXIL スマート10	色	プレシャスホワイト
	※浴室ドア枠 フクビ3方枠 [ホワイト]		
キッチン笠木	■ ゴム集成カウンター(オスモカラー) 色	3062フロアークリアmatt	
カウンター	形状 L型(ジョイント加工)	t=30	
天井点検口	■ 天井アルミ点検口枠 450角 TAN45BW	フクビ化学工業 ミルキーホワイト	
床下収納庫	■ 高気密型床下点検口断熱型 SPF-R6060 城東テクノ	収納付 (キッチン) ナチュラル(NL)	
トイレ棚	■ 1,2階トイレ D250	アートランバー棚(シェルホワイト)	
室内物干し金物	■		
LDK-カウンター	■ なし	色	
下足入	■ LIXILラシッサS	色	クリエアイボリー
プッシュタイプ	サイズ: W1200 D400	形状:	コの字型ミラー付

支給品	■ 無し
備考	※付框は(30×150)プレシャスホワイト 可動棚アートランバー色 アッシュウォールナット 棚受金物類は全てシルバー

内 部 建 具 表							
LIXIL		建具色：クリエイイボリー		枠色 ： 扉同色		※その他、下記特記による	
ラシッサS(標準)		把手 ： スクエアL (シャインニッケル) 丁番 固定枠(156) 外付戸当り ガイドピン床色合せ 引戸のみ上吊Wソフトモーション					
階	No	室名	形式	枠外W サイズ	デザイン	枠色	特記事項
				枠外H サイズ	建具色	把手	
1	1	SC	観音開	—	LAA	—	角型Lタテ取付
	WD			2000	—	—	
	2	WC①	片引き戸	—	LAA	—	明り窓・表示錠
	WD			2000	—	—	
	3	LDK	片開き戸	—	LGK 格子無	—	
	WD			2000	—	—	
	4	LDK	観音開	—	LAA	—	角型Lタテ取付
	WD			2000	—	—	
	5	脱衣ラントリー	片引き戸	—	LAA	—	明り窓・表示錠
	WD			2000	—	—	
2	6	洋室④	片開き戸	—	LAA	—	
	WD			2000	—	—	
	7	洋室③	片開き戸	—	LAA	—	
	WD			2000	—	—	
	8	洋室②	片開き戸	—	LAA	—	
	WD			2000	—	—	
	9	洋室①	片開き戸	—	LAA	—	
	WD			2000	—	—	
	10	WC②	片開き戸	—	LAA	—	明り窓・表示錠
	WD			1700	—	—	

	浜 岡 一 級 総 合 設 計 事 務 所		株式会社 LIFEFUND InDesign office 一級建築士事務所		年 月 日	件名			設計	IC	工務	図 番
	一級建築士事務所 静岡県知事登録第 (10)2441 号		〒432-8023 静岡県浜松市中央区鴨江3丁目70番23号		2025.6.14	山崎悟様 邸新築工事			酒井	0	青島	1-2
	一級建築士 大臣登録第 365879 号 西原利昌		事務所登録 (2) 第7595号 一級建築士登録 第179770号 鈴木 達男		縮尺	図面	仕上表 2					

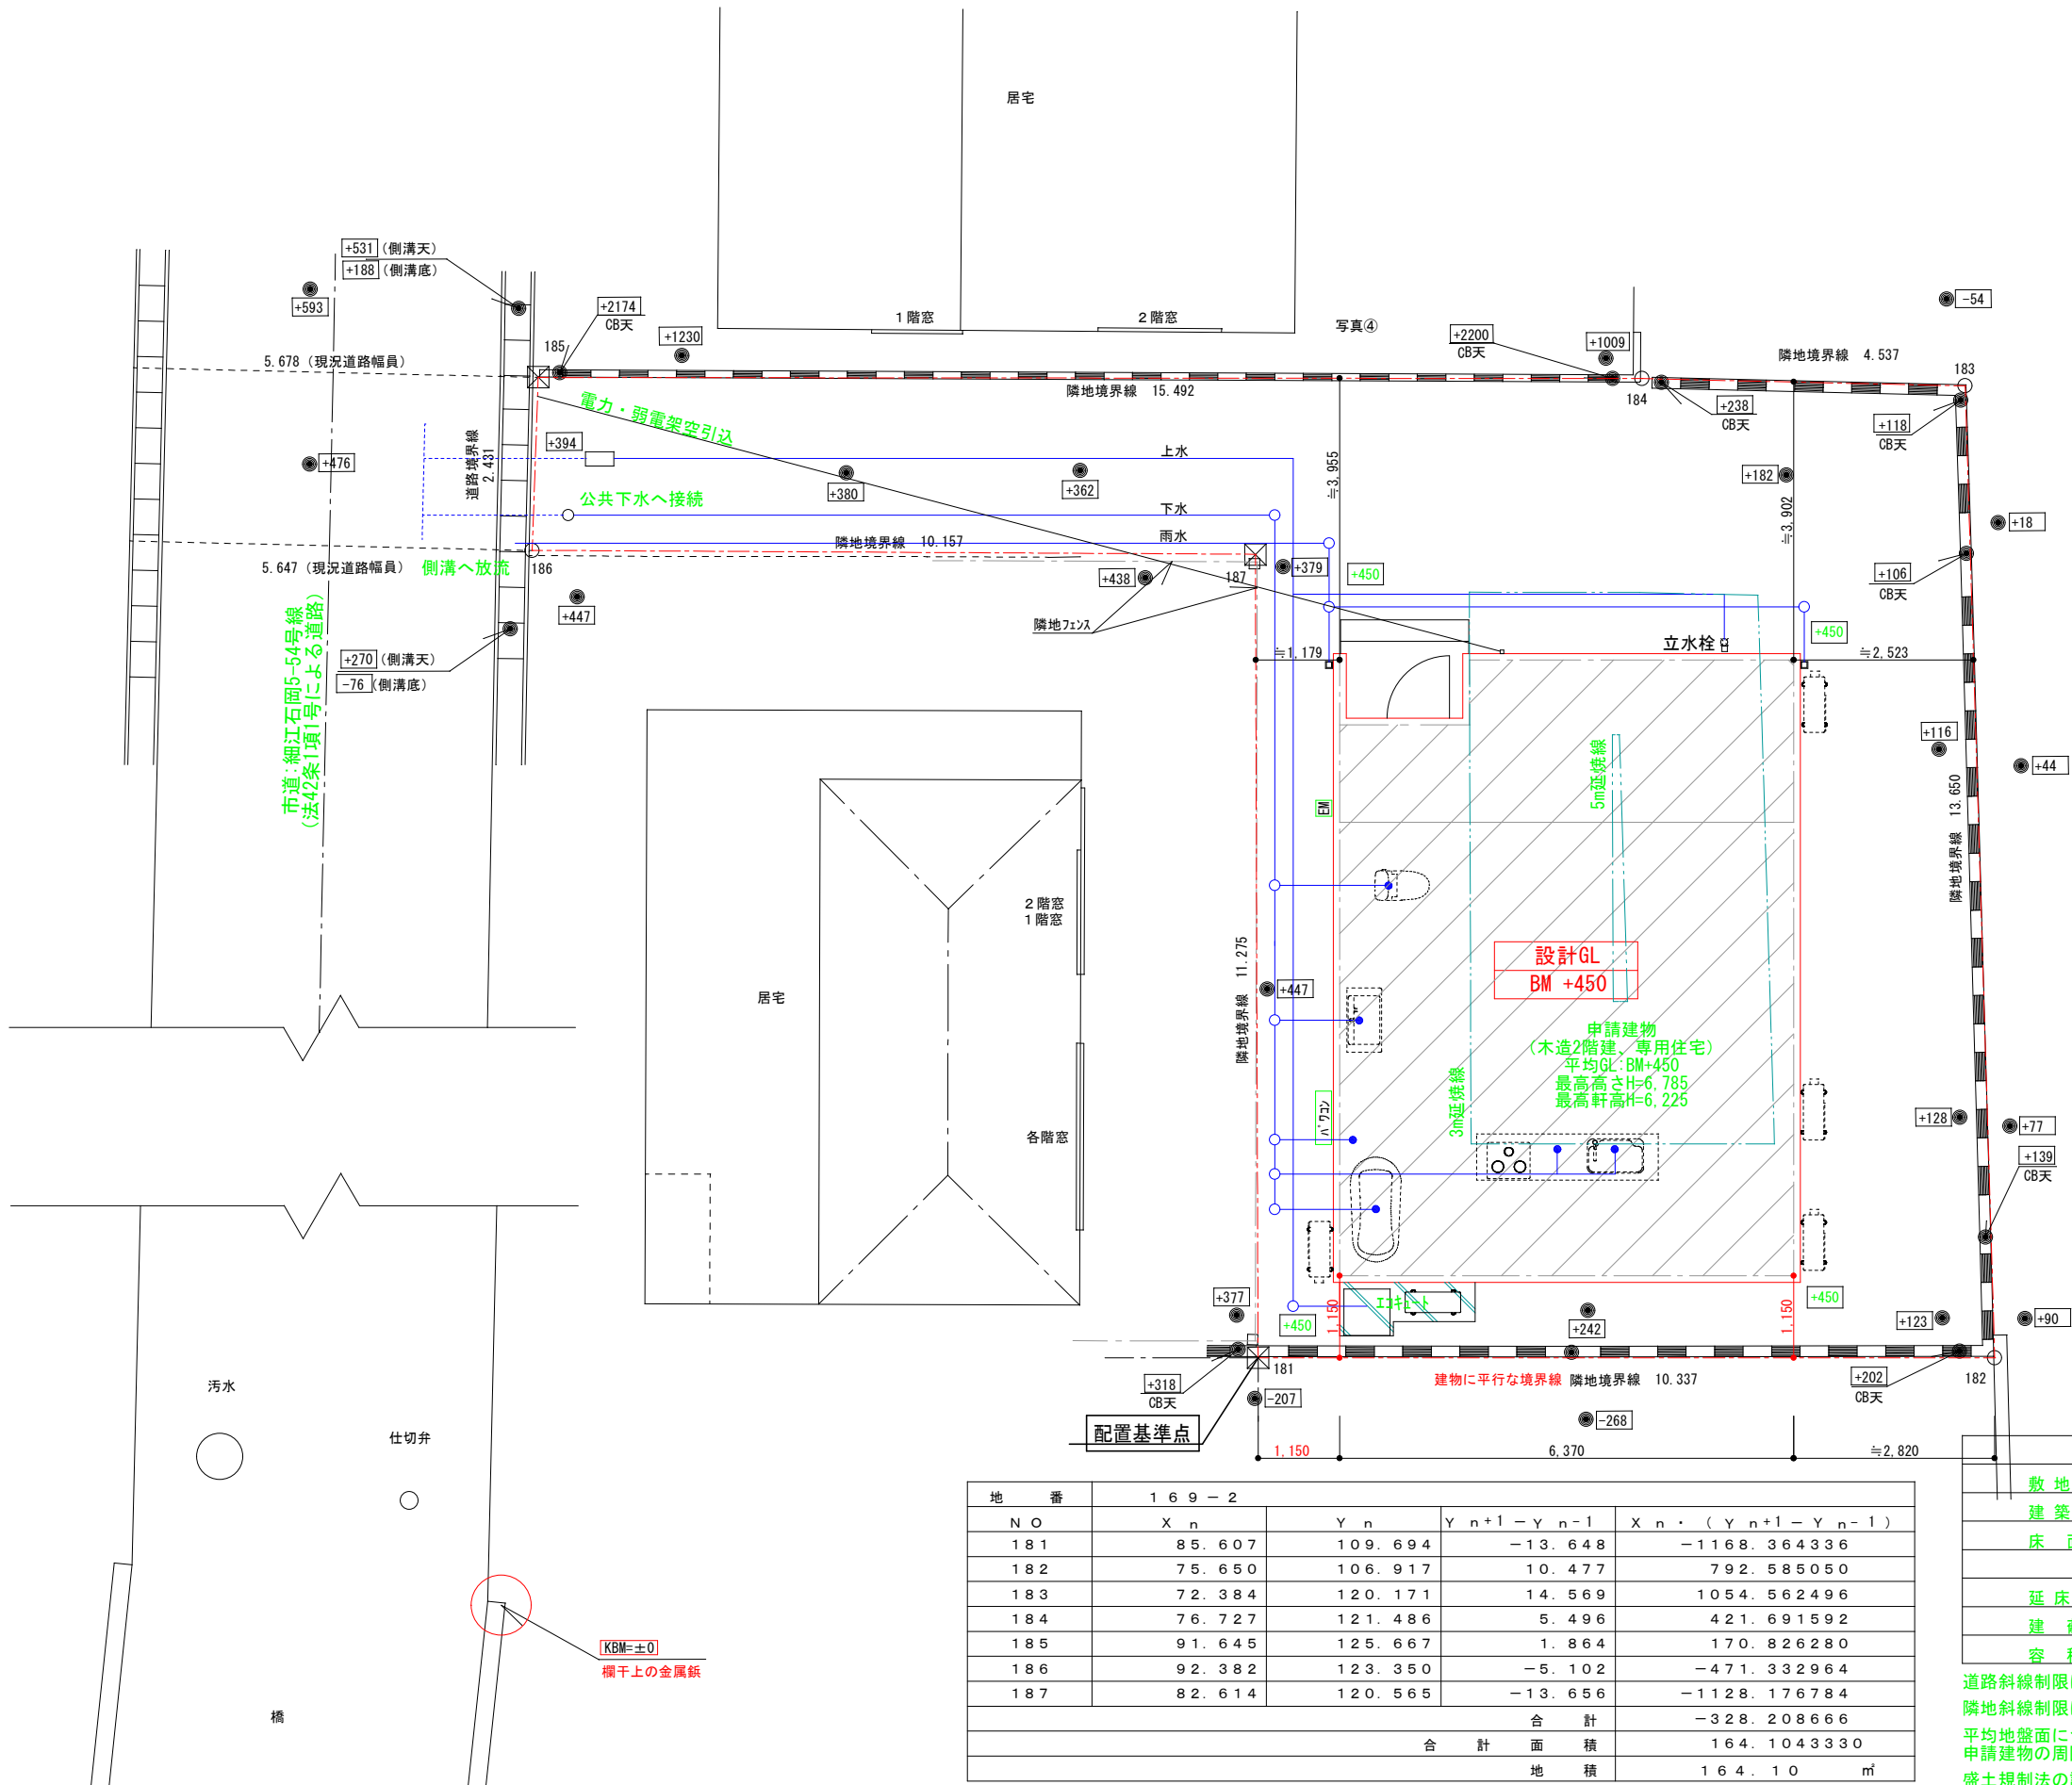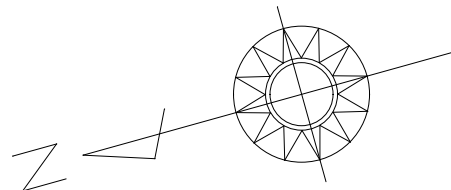


決定図

地番	1 6 9 - 2				
N O	X _n	Y _n	Y _{n+1} - Y _{n-1}	X _n × (Y _{n+1} - Y _{n-1})	
1 8 1	8 5 . 6 0 7	1 0 9 . 6 9 4	- 1 3 . 6 4 8	- 1 1 6 8 . 3 6 4 3 3 6	
1 8 2	7 5 . 6 5 0	1 0 6 . 9 1 7	1 0 . 4 7 7	7 9 2 . 5 8 5 0 5 0	
1 8 3	7 2 . 3 8 4	1 2 0 . 1 7 1	1 4 . 5 6 9	1 0 5 4 . 5 6 2 4 9 6	
1 8 4	7 6 . 7 2 7	1 2 1 . 4 8 6	5 . 4 9 6	4 2 1 . 6 9 1 5 9 2	
1 8 5	9 1 . 6 4 5	1 2 5 . 6 6 7	1 . 8 6 4	1 7 0 . 8 2 6 2 8 0	
1 8 6	9 2 . 3 8 2	1 2 3 . 3 5 0	- 5 . 1 0 2	- 4 7 1 . 3 3 2 9 6 4	
1 8 7	8 2 . 6 1 4	1 2 0 . 5 6 5	- 1 3 . 6 5 6	- 1 1 2 8 . 1 7 6 7 8 4	
合 計				- 3 2 8 . 2 0 8 6 6 6	
合 計 面 積				1 6 4 . 1 0 4 3 3 3 0	
地 積				1 6 4 . 1 0 m ²	

トータル面積表 (㎡)	
敷地面積	164.10
建築面積	55.06
床面積 1階	53.41
2階	55.06
延床面積	108.47
建蔽率	(55.06/164.10) × 100 33.56%
容積率	(108.47/164.10) × 100 66.10%


道路斜線制限については、明らかに適合する。
隣地斜線制限については、明らかに適合する。
平均地盤面について
申請建物の周囲の平均地盤面高さをBM+450とする。
盛土規制法の許可対象となる工事なし。

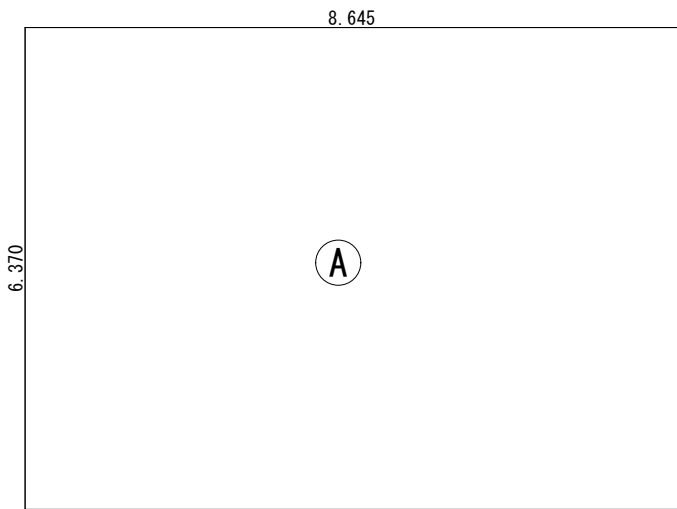

建築面積求積図 S=1/100

建築面積求積表


番号	計算式	(m)	面積 (㎡)
Ⓐ	8.645 × 6.370		55.0687
合計			55.0687 55.06 (16.6坪)

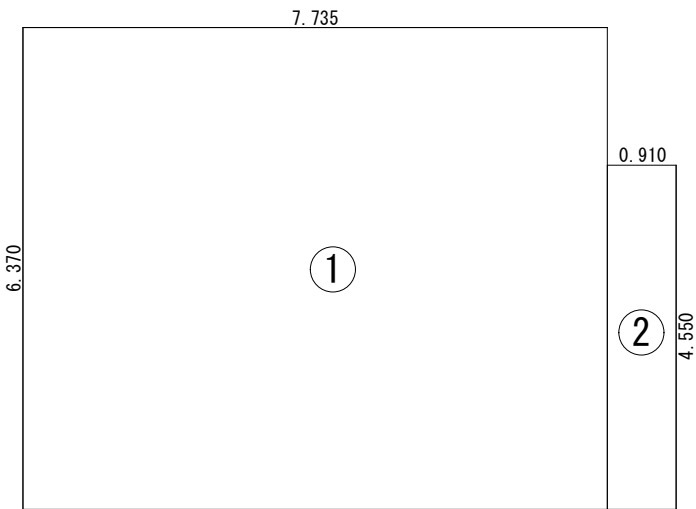

1階床面積図 S=1/100

1階床面積求積表

番号	計算式	(m)	面積 (㎡)
①	7.735 × 6.370		49.2720
②	0.91 × 4.550		4.1405
合計			53.4125 53.41 (16.1坪)

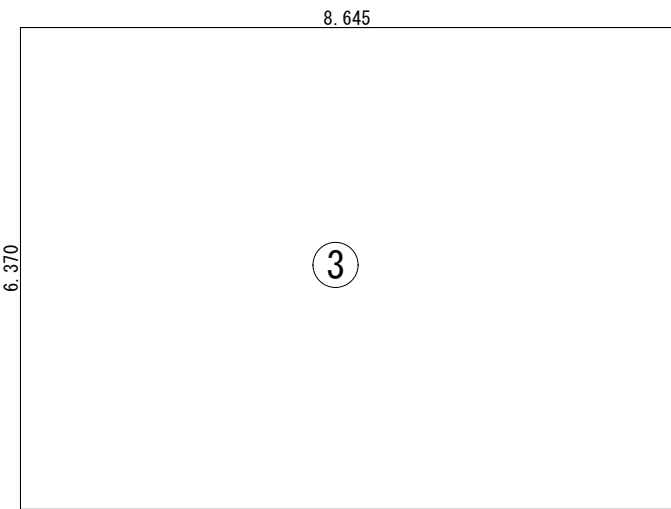

2階床面積図 S=1/100

2階床面積求積表

番号	計算式	(m)	面積 (㎡)
③	8.645 × 6.370		55.0687
合計			55.0687 55.06 (16.6坪)

延べ床面積表

	番号	(m)	面積 (㎡)
1階床面積	① ②		53.41
2階床面積	③		55.06
合計			108.47 (32.8坪)

決定図



G2

壁付け 住宅用火災報知器			数量
H	熱感知器	電池式(単独型)	1
	熱感知器	露出型	
壁付け 住宅用火災報知器			数量
S	煙感知器	電池式(単独型)	
	煙感知器	露出型	

- ※ 煙感知器は壁・梁より600mm以上離す
壁に取付ける場合、
天井から150mm以上500mm以内離す
換気扇・エアコン吹出口から1500mm以上離す
- ※ 全室LED照明とし、居室においては調光
制御、非居室においては人感センサーを
採用する。
- ※ 標準天井高さ2,400
- ※ 特記無きガラスは型ガラス

* 凡例

- ☒ 管柱 (105×105)
- ◀▶ Kダクト (3.30倍 FRM-0641)
- △ 片筋違い (2.00倍 45×90)
(例 左:柱脚 右:柱頭)
- ⊠ たすき掛筋違い (4.00倍 45×90)
- 構造用合板 (2.70倍)
(t=9 材種-EXハイバ-)
- △ 床点検口
- ⊠ 天井点検口
- ⊙ 換気扇
- ⊙ 熱交換換気扇VLR-70

アドバンスシリーズ		
スマートデザイン (外部)		
凡例		
	1	コンセント 1ヶ所
	2	コンセント 2ヶ所
	3	コンセント 3ヶ所
	1ET	コンセント1ヶ所接地ターミナル付
	2ET	コンセント2ヶ所接地ターミナル付
	WP	コンセント 防水型
		エアコン用コンセント
		200V用コンセント
	WP	防雨入線プレート
		スイッチ
	3	3路スイッチ
	4	4路スイッチ
		直結電源
	TV	テレビ取出口
	TEL	電話取出口 (テレホンガイド)
	LAN	LAN取出口 (テレホンガイド)
		壁照明
		リモコン (給湯関係・ルフロ)
		メーター
		分電盤
		チャイム

- ※ACコンセント天井付け
- ※TVアンテナ工事
- ※スイッチはFL+1100、コンセントはFL+200

決定図



訂正

浜岡一級総合設計事務所
一級建築士事務所 静岡県知事登録第 (10)2441 号
一級建築士 大臣登録第 365879 号 西原利昌



株式会社 LIFEFUND InDesign office 一級建築士事務所
事務所登録 (2) 第7595号 一級建築士登録 第179770号 鈴木 達男
〒432-8023 静岡県浜松市中央区鴨江3丁目70番23号

年月日
2025. 6. 14
縮尺
1/50

件名
山崎悟様邸 新築工事
図名
1階平面図

設計	IC	工事	図番
酒井		青島	3-1

G2

壁付け 住宅用火災報知器			数量
H 熱感知	電池式(単独型)		
	露出型		
壁付け 住宅用火災報知器			数量
S 煙感知	電池式(単独型)		8
	露出型		

- ※ 煙感知器は壁・梁より600mm以上離す
壁に取付ける場合、
天井から150mm以上500mm以内離す
換気扇・エアコン吹出口から1500mm以上離す
- ※ 全室LED照明とし、居室においては調光
制御、非居室においては人感センサーを
採用する。
- ※ 標準天井高さ2,400
- ※ 特記無きガラスは型ガラス


* 凡例

- ☒ 管柱 (105×105)
- ◀▶ Kダクト (3.30倍 FRM-0641)
- △ 片筋違い (2.00倍 45×90)
(例 左:柱脚 右:柱頭)
- ⊠ たすき掛筋違い (4.00倍 45×90)
- 構造用合板 (2.70倍)
(t=9 材種-EXハイパ-)
- △ 床点検口
- ⊠ 天井点検口
- ⊙ 換気扇
- ⊙ 熱交換換気扇VLR-70

アドバンスシリーズ		
スマートデザイン (外部)		
凡例	1	コンセント 1ヶ所
①	2	コンセント 2ヶ所
②	3	コンセント 3ヶ所
①ET	コンセント1ヶ所接地ターミナル付	
②ET	コンセント2ヶ所接地ターミナル付	
WP	コンセント 防水型	
⊙	エアコン用コンセント	
⊙	200V用コンセント	
WP	防雨入線プレート	
●	スイッチ	
●	3路スイッチ	
●	4路スイッチ	
⊙	直結電源	
⊙TV	テレビ取出口	
⊙TEL	電話取出口 (テレホンガイド)	
⊙LAN	LAN取出口 (テレホンガイド)	
⊙	壁照明	
⊙	リモコン(給湯関係・ルフロ)	
⊙	メーター	
⊙	分電盤	
⊙	チャイム	


- ※ACコンセント天井付け
- ※TVアンテナ工事
- ※スイッチはFL+1100、コンセントはFL+200

決定図

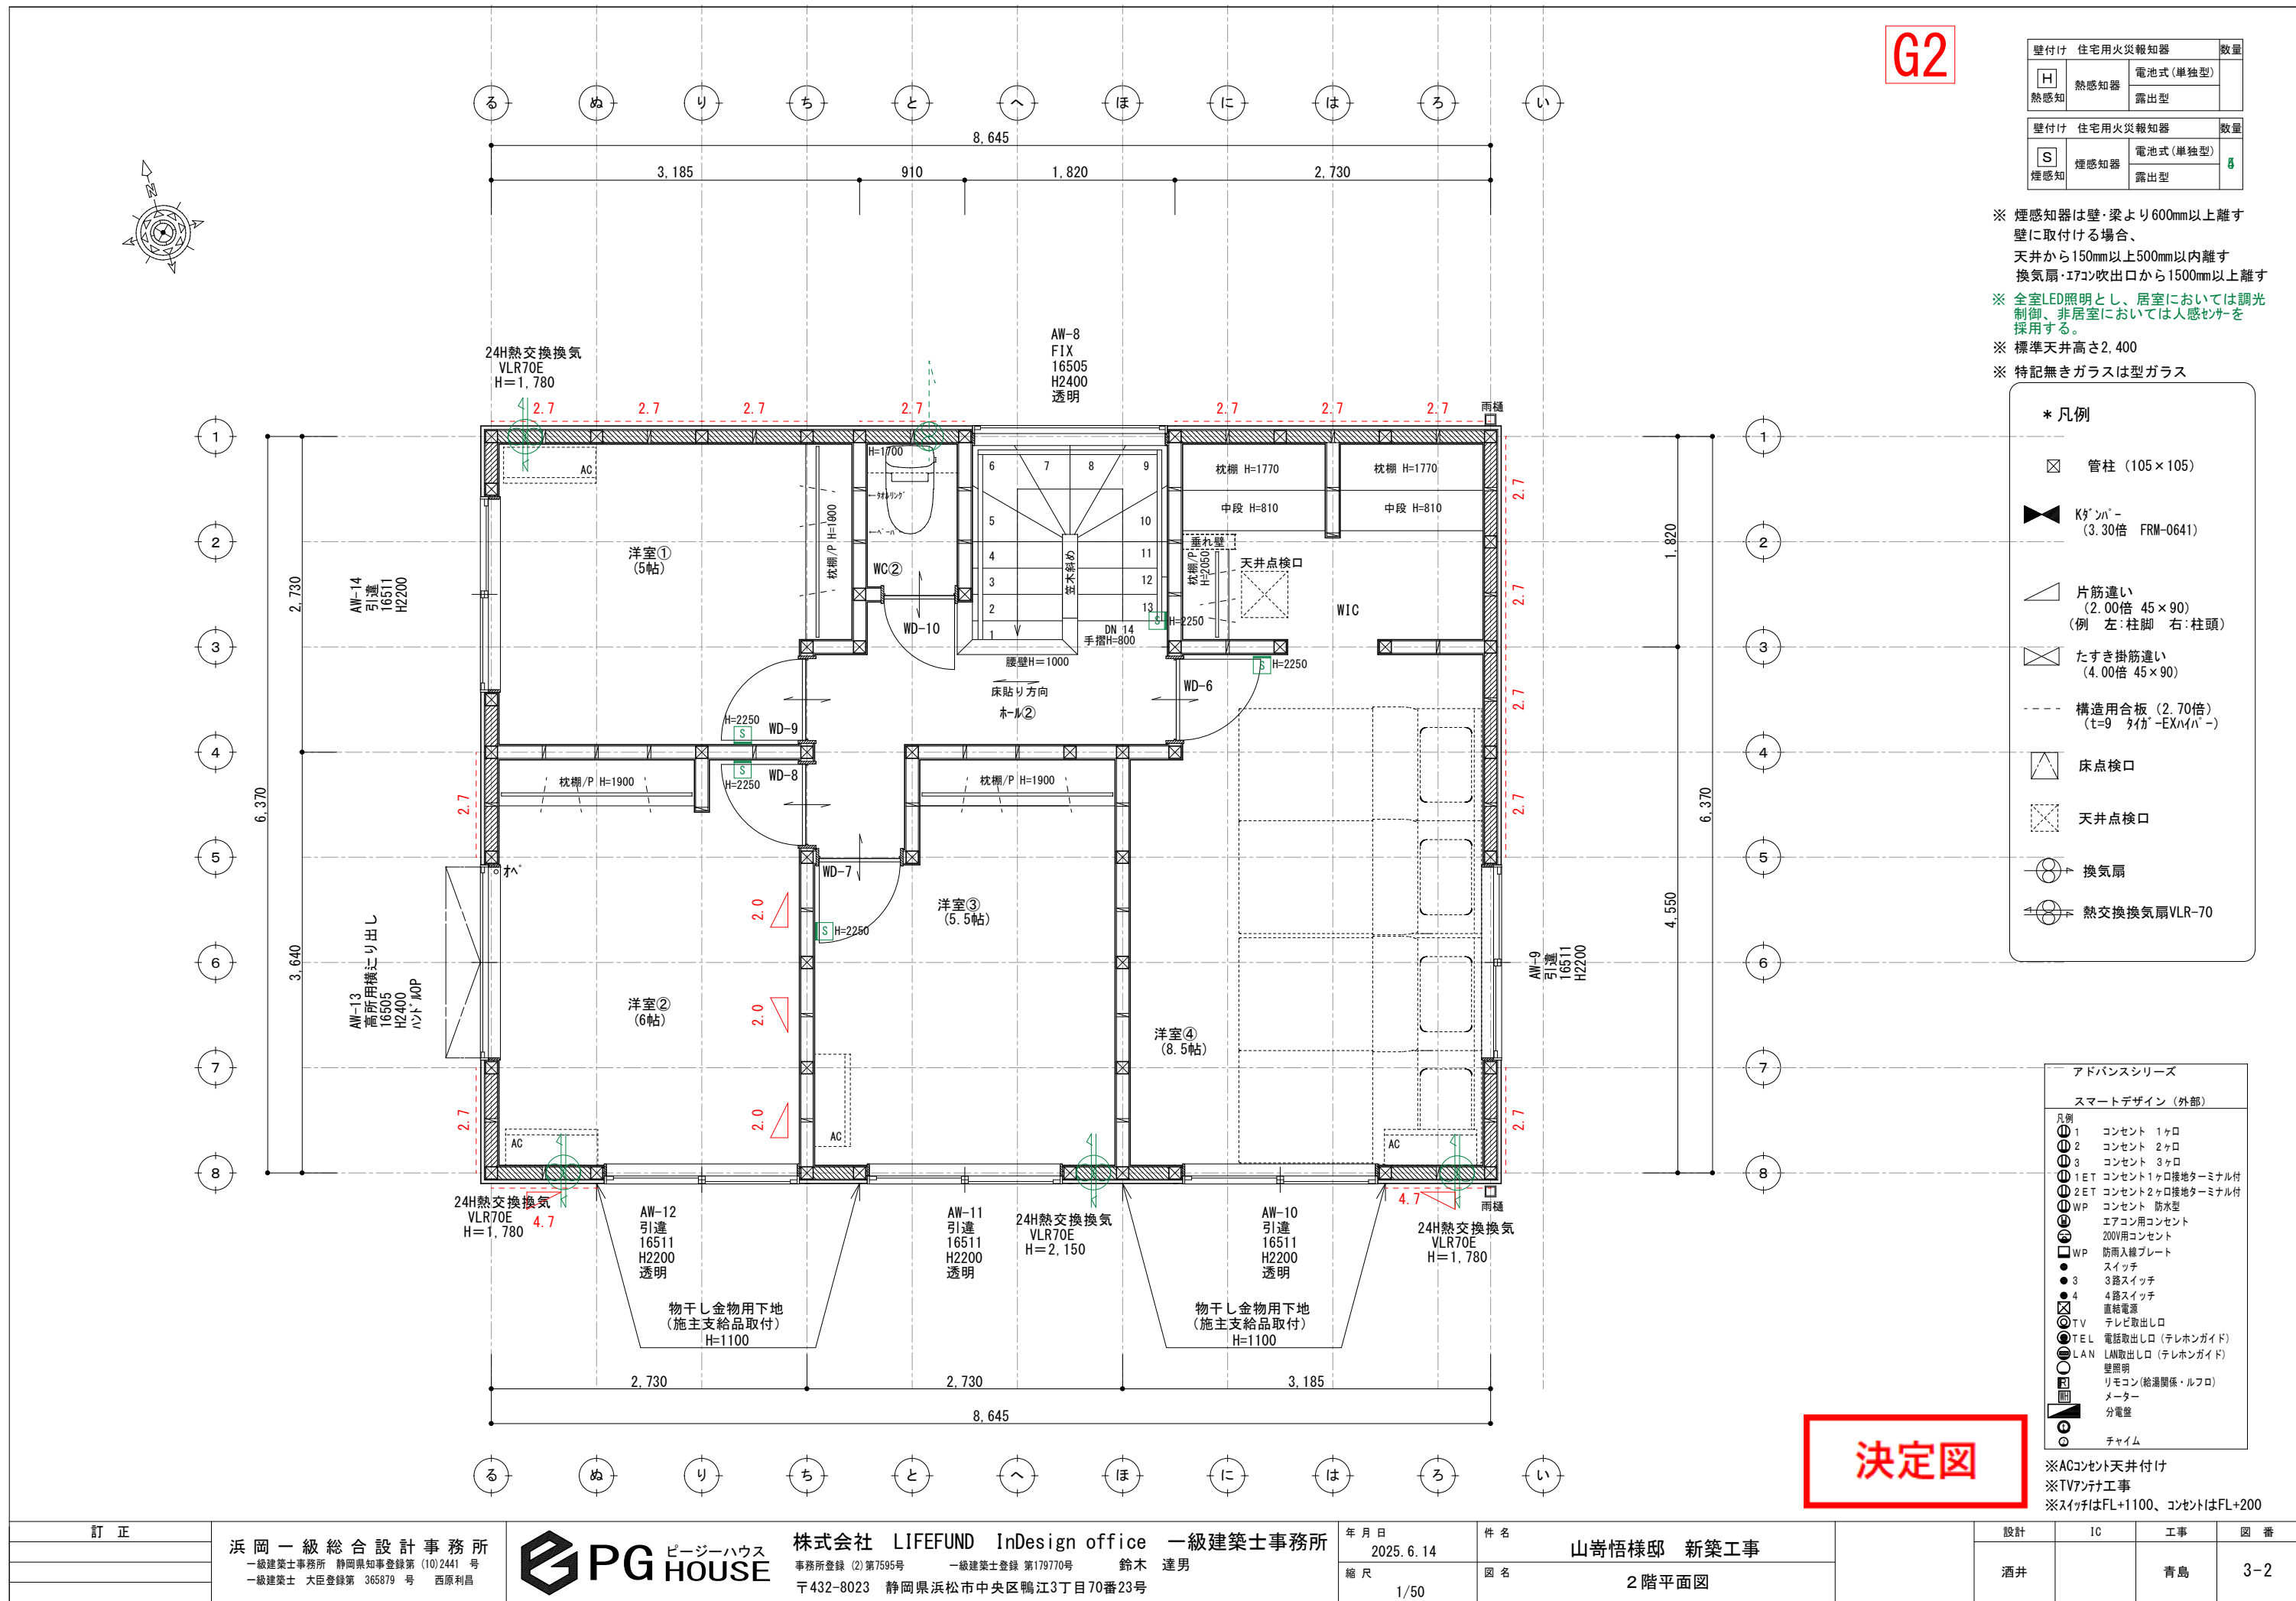



訂正	浜岡一級総合設計事務所 一級建築士事務所 静岡県知事登録第 (10)2441 号 一級建築士 大臣登録第 365879 号 西原利昌	PG HOUSE	株式会社 LIFEFUND InDesign office 一級建築士事務所 事務所登録 (2) 第7595号 一級建築士登録 第179770号 鈴木 達男 〒432-8023 静岡県浜松市中央区鴨江3丁目70番23号	年月日 2025.6.14 縮尺 1/50	件名 山崎悟様邸 新築工事 図名 2階平面図	設計 酒井	IC	工事 青島	図番 3-2
----	--	----------	---	--------------------------------	---------------------------------	----------	----	----------	-----------

GX住宅 (Cube J付)
太陽光あり

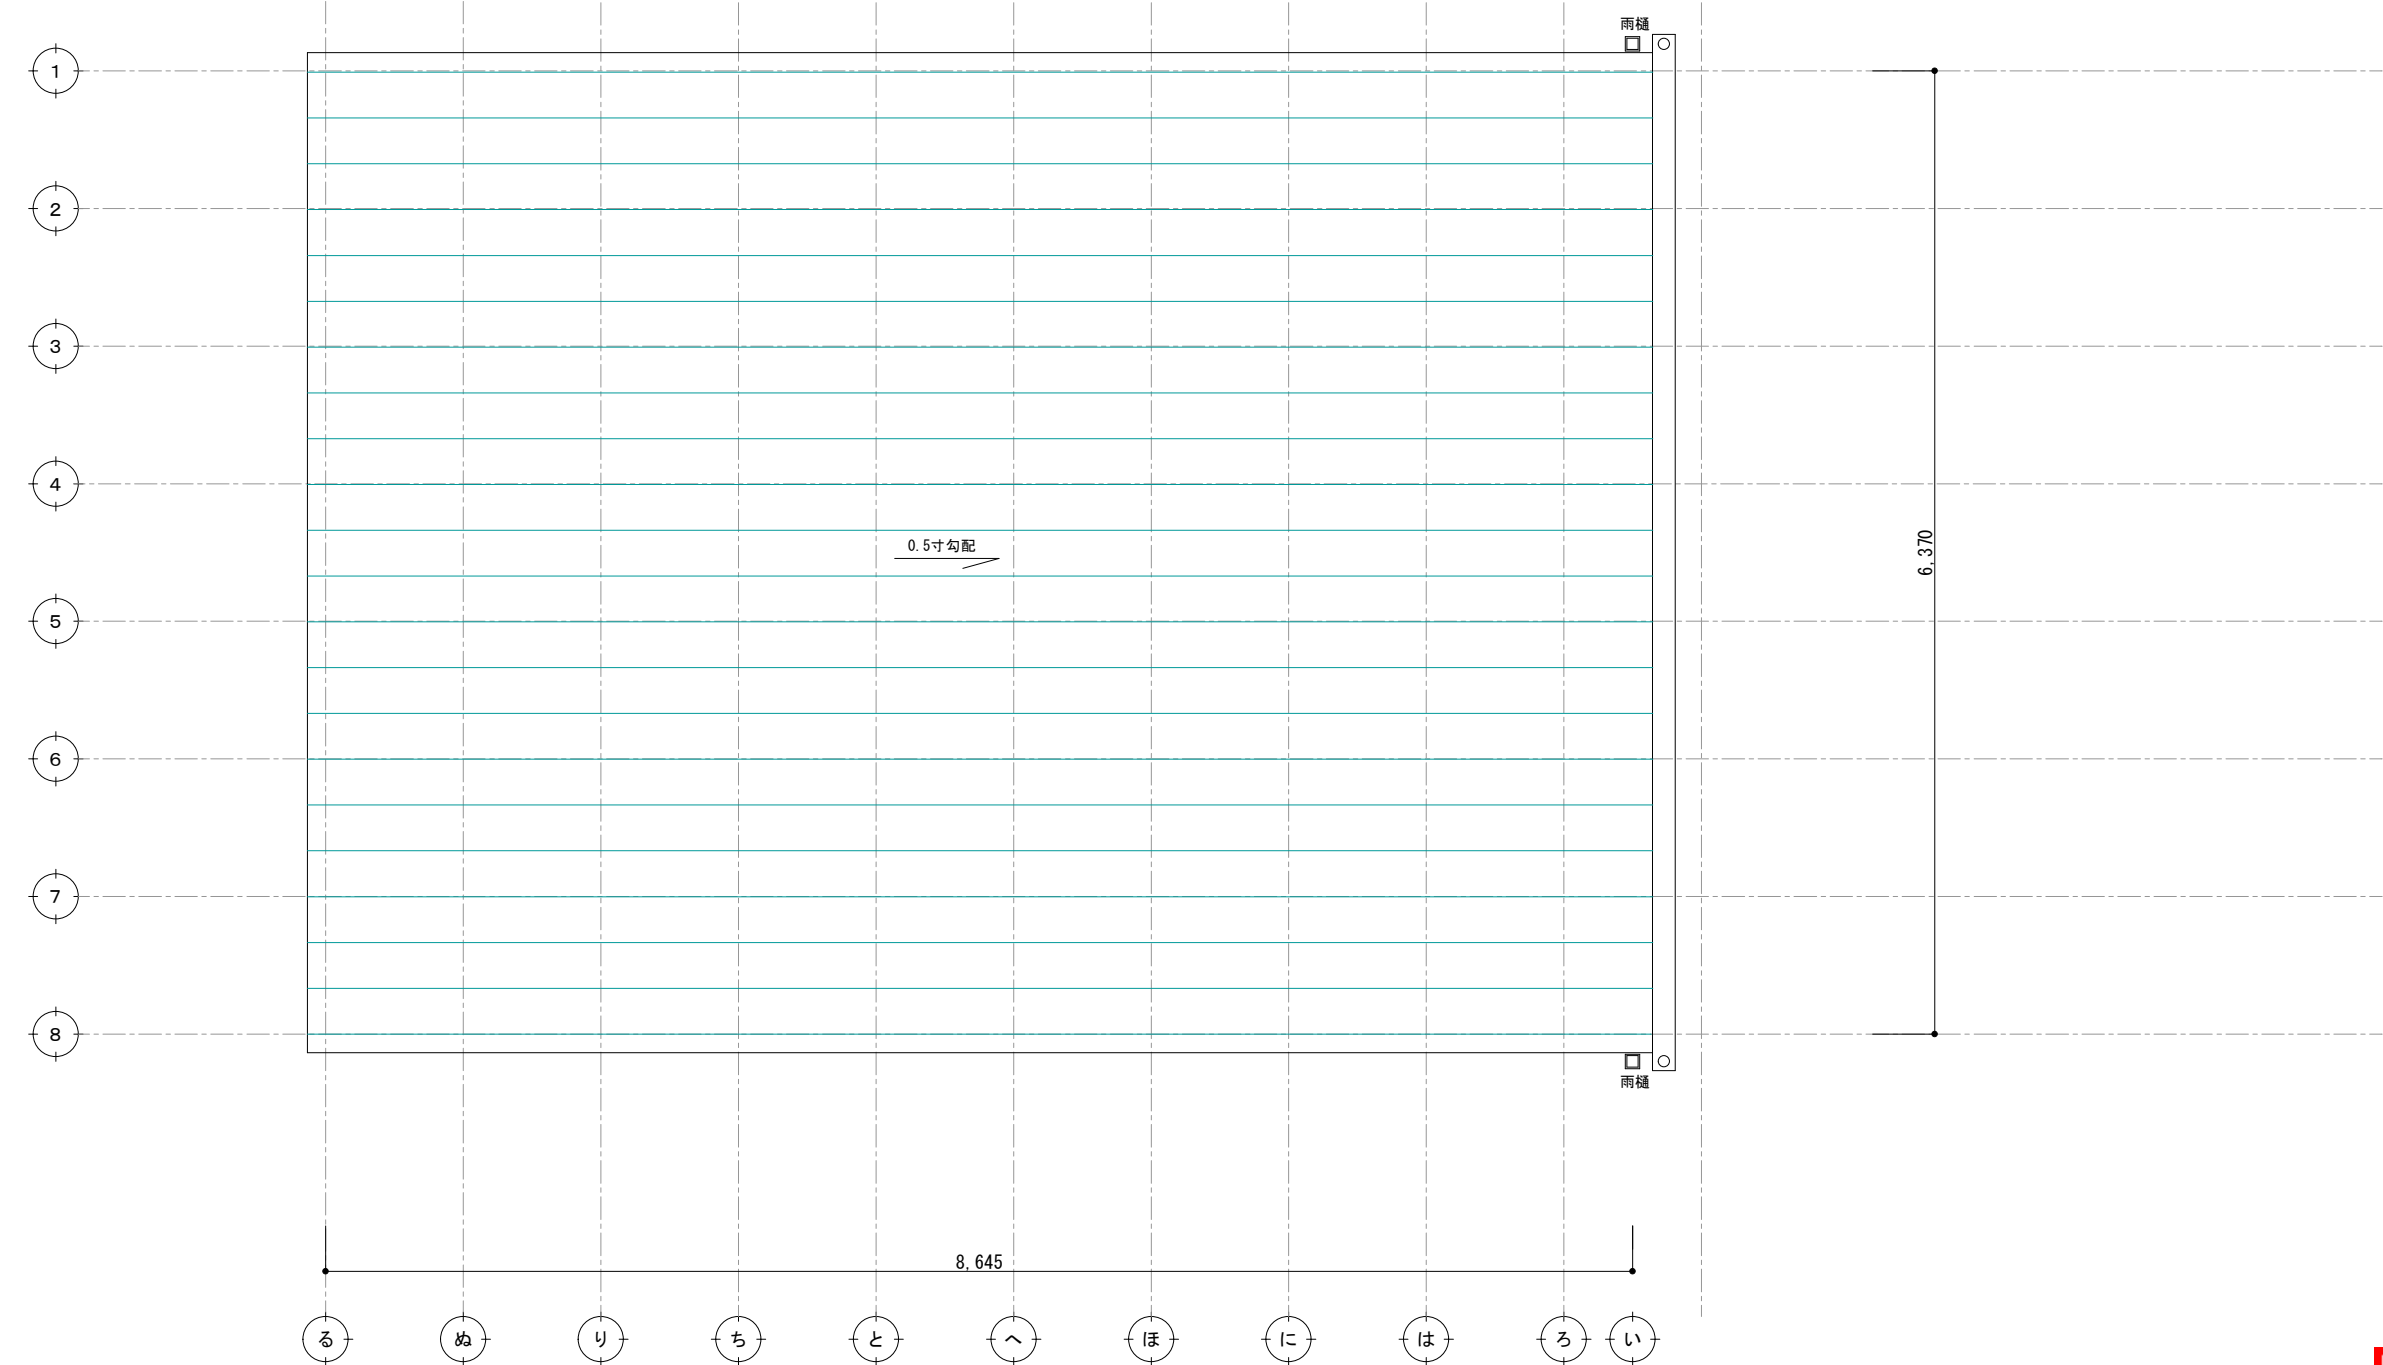


決定図

訂 正	浜 岡 一 級 総 合 設 計 事 務 所 一級建築士事務所 静岡県知事登録第 (10)2441 号 一級建築士 大臣登録第 365879 号 西原利昌		株式会社 LIFEFUND InDesign office 一級建築士事務所 事務所登録 (2) 第7595号 一級建築士登録 第179770号 鈴木 達男 〒432-8023 静岡県浜松市中央区鴨江3丁目70番23号	年 月 日	件 名		設計	IC	工事	図 番
				2025. 6. 14	山崎悟様邸 新築工事					
				縮 尺	図 名					
				1/100	屋根伏図		酒井		青島	3-3

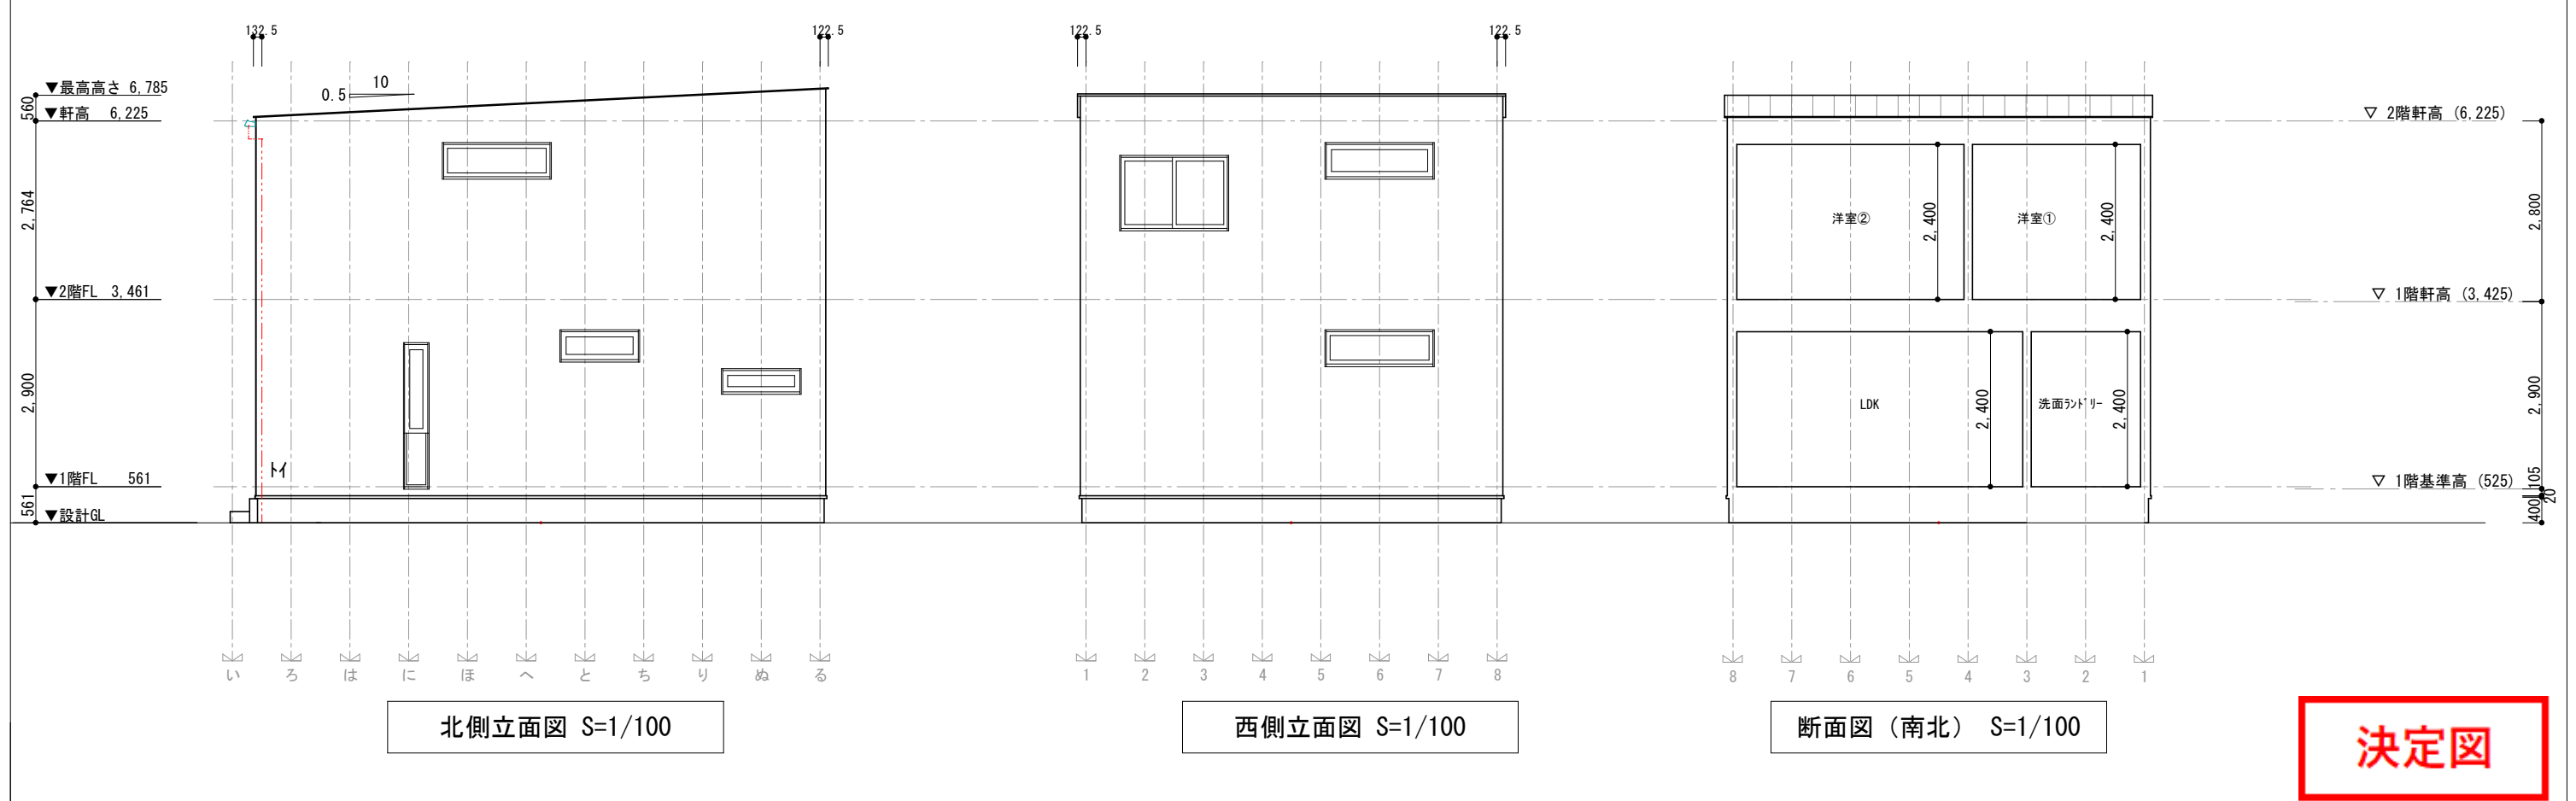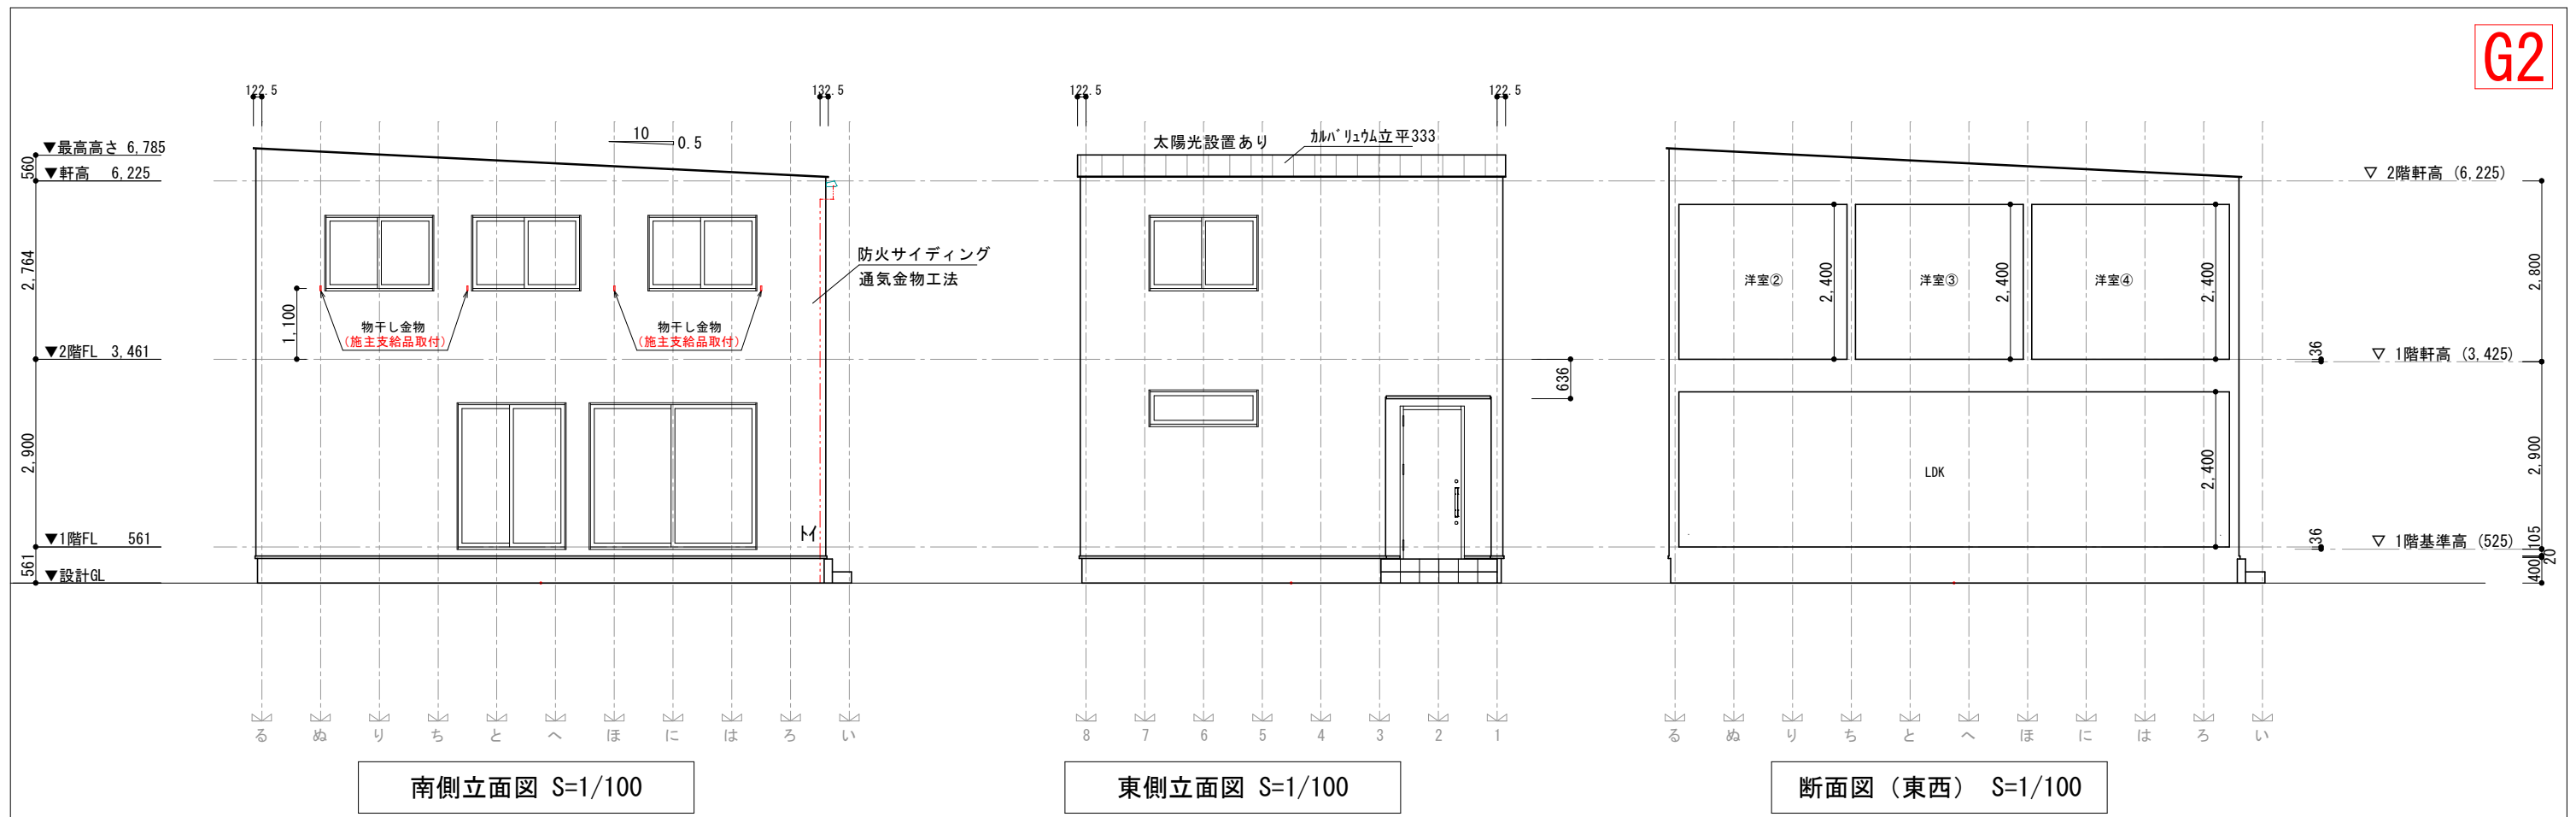


決定図


訂 正	浜 岡 一 級 総 合 設 計 事 務 所 一級建築士事務所 静岡県知事登録第 (10)2441 号 一級建築士 大臣登録第 365879 号 西原利昌		株式会社 LIFEFUND InDesign office 一級建築士事務所 事務所登録 (2) 第7595号 一級建築士登録 第179770号 鈴木 達男 〒432-8023 静岡県浜松市中央区鴨江3丁目70番23号	年 月 日	件 名		設計	IC	工事	図 番
				2025. 6. 14	山嵯悟様邸 新築工事					
				縮 尺	図 名					
				1/100	立面図		酒井		青島	4

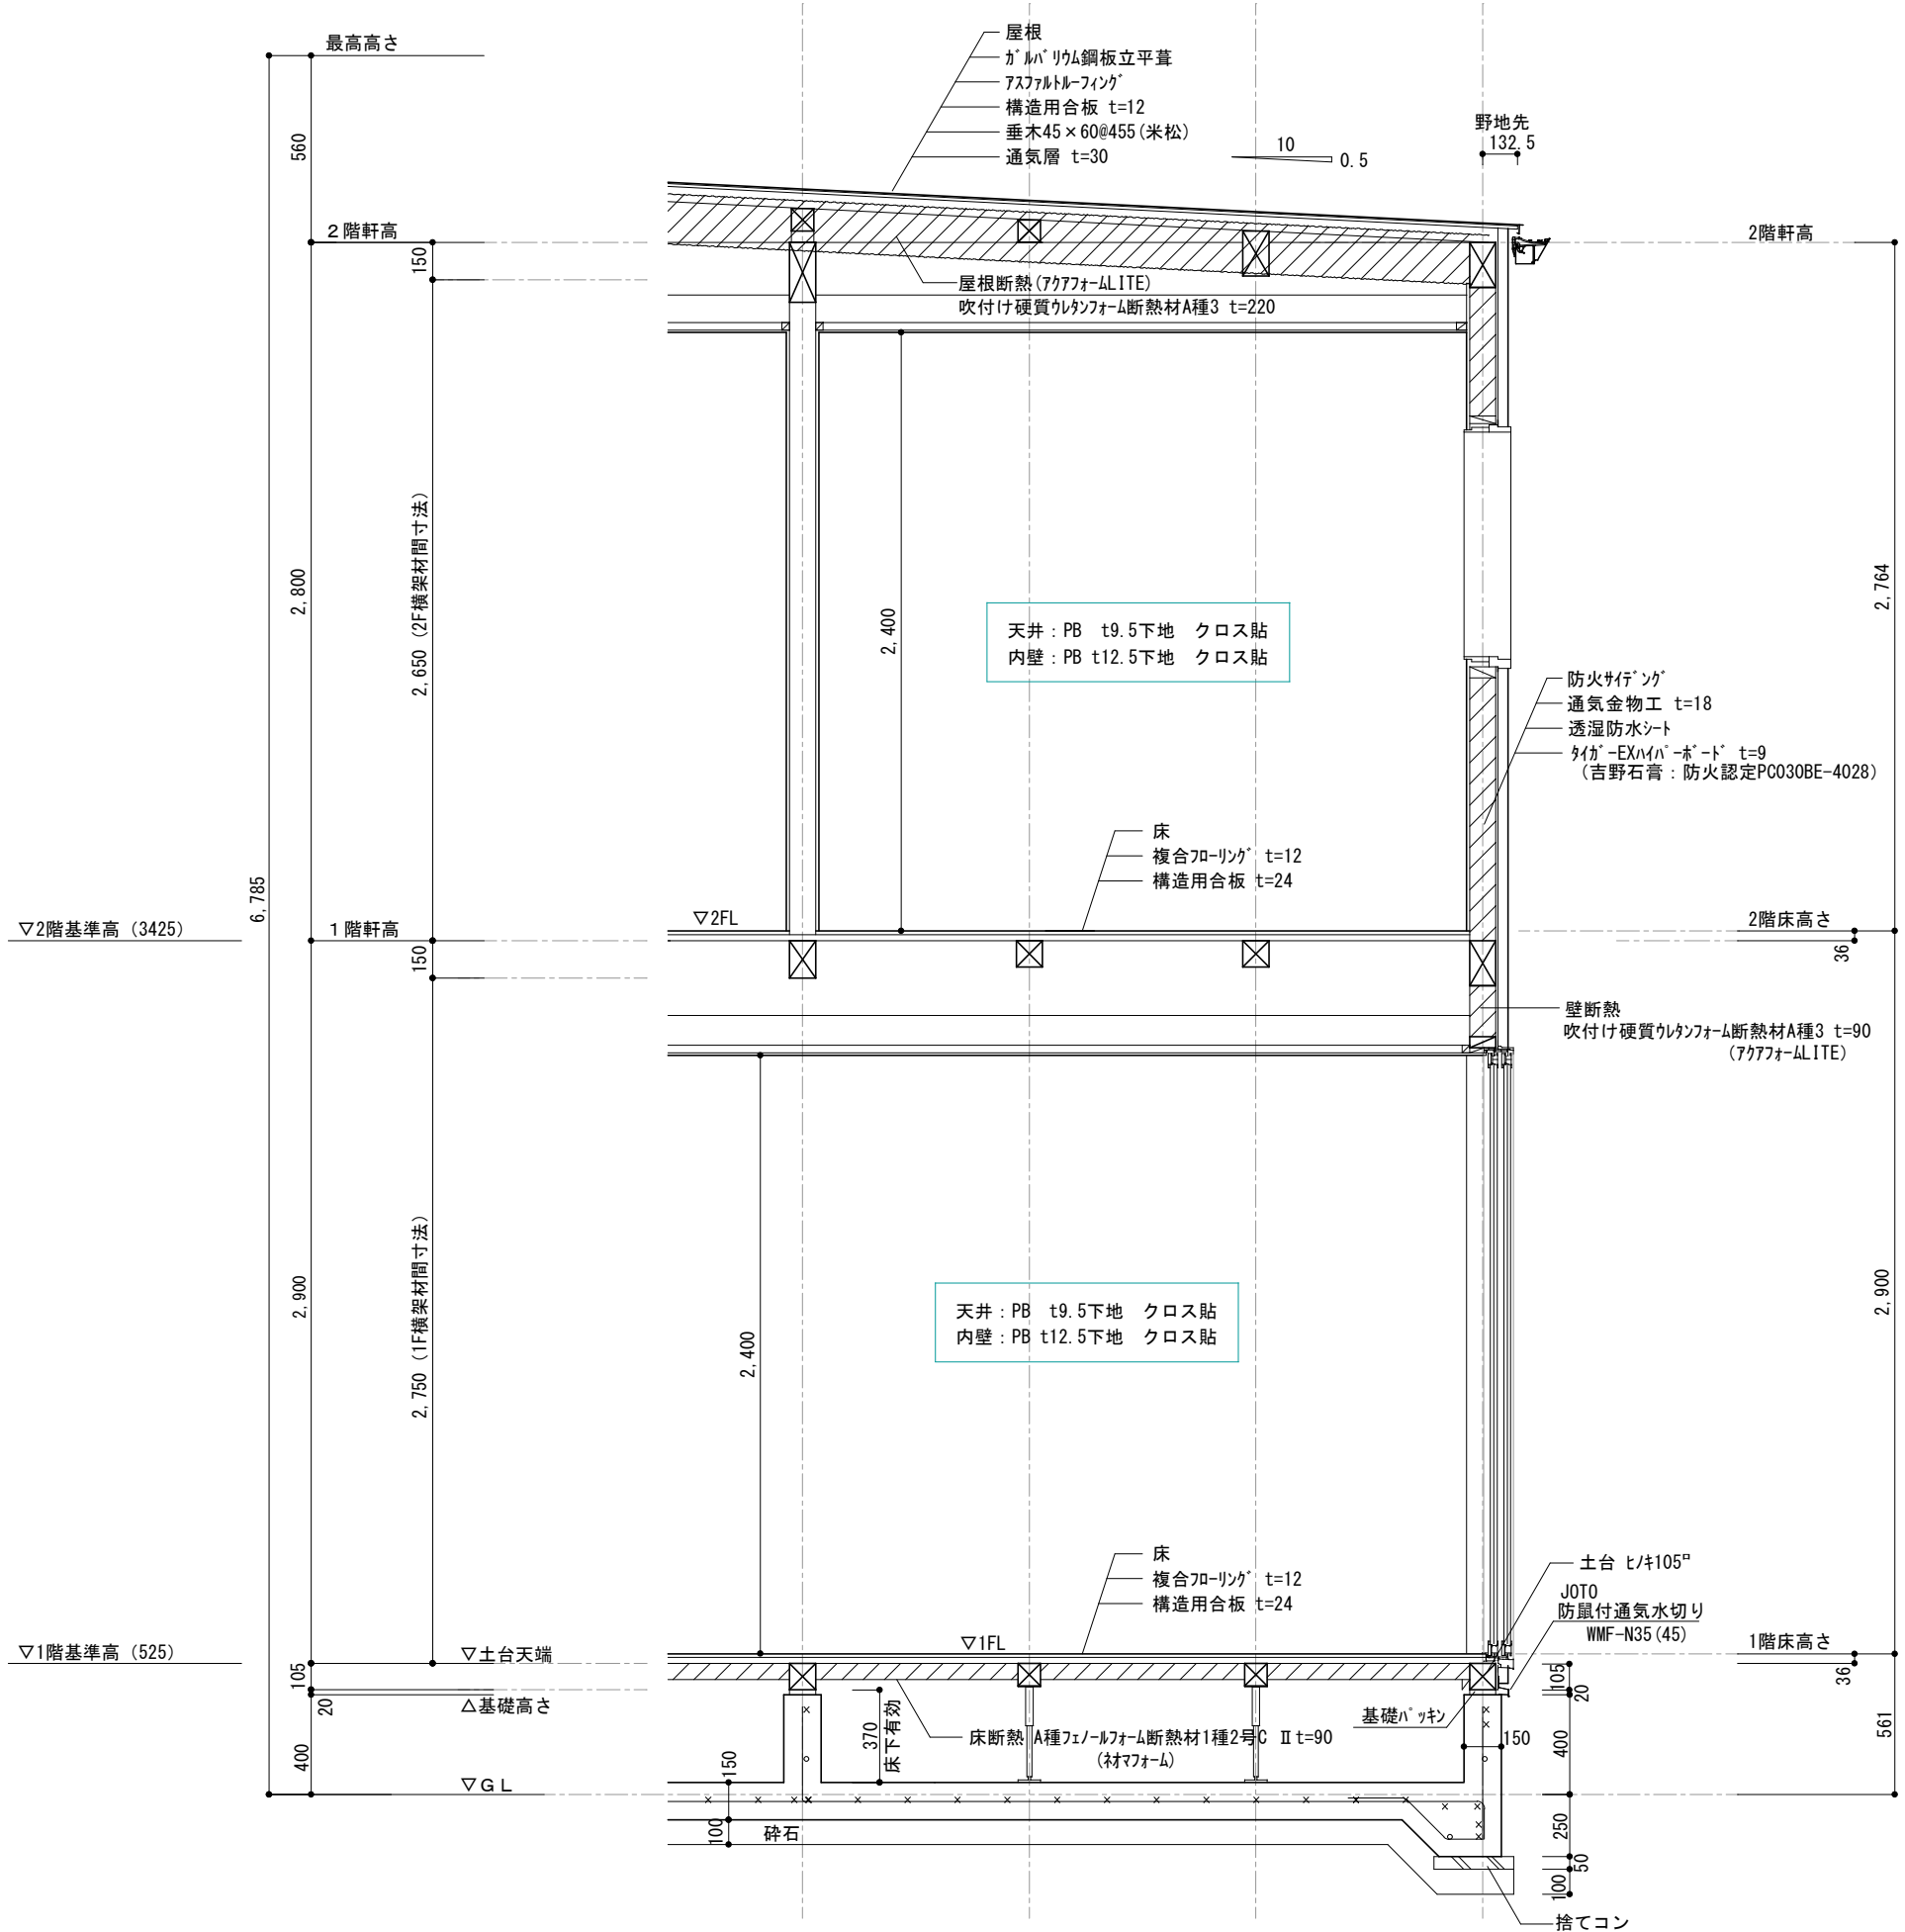


決定図

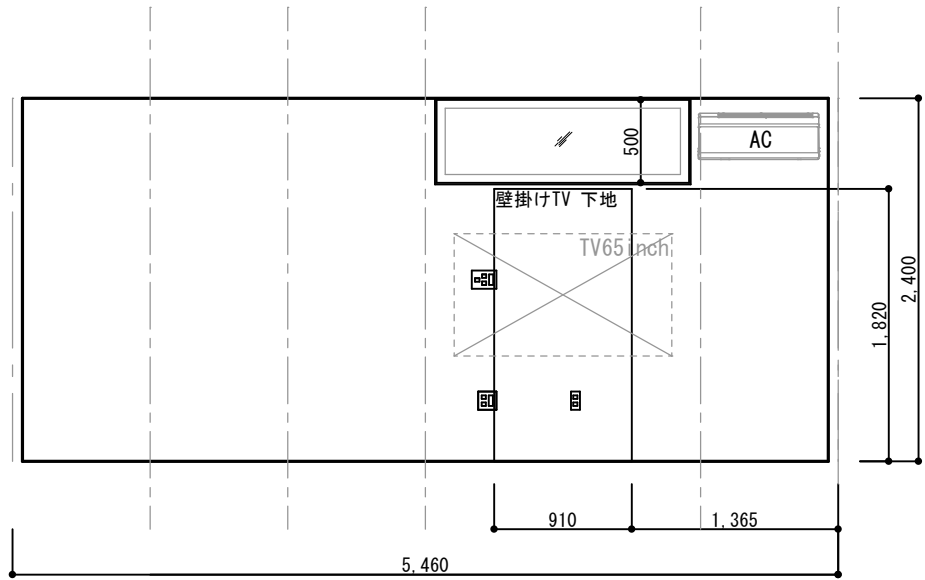



LDK① 東面

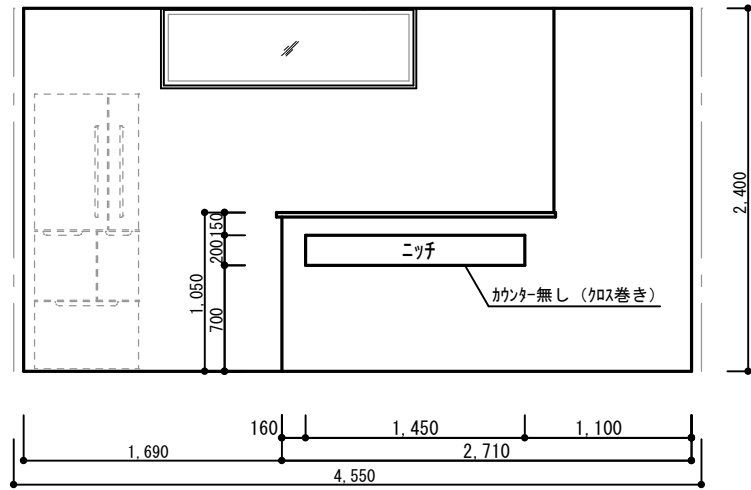

LDK① 西面

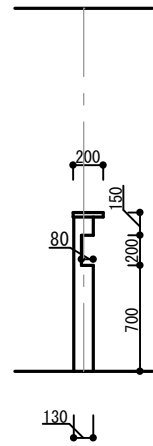

キッチン腰壁 断面

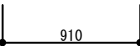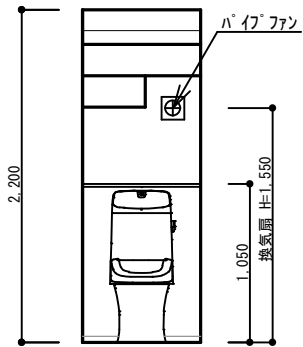

WC① 南面

決定図

訂正	浜岡一級総合設計事務所	LIFEFUND PG HOUSE	株式会社 LIFEFUND InDesign office 一級建築士事務所 事務所登録 (2) 第7595号 一級建築士登録 第179770号 鈴木 達男 〒432-8023 静岡県浜松市中央区鴨江3丁目70番23号	年月日 2025. 6. 14	件名 山崎悟様 新築工事		設計	IC	工事	図番
	一級建築士事務所 静岡県知事登録第 (10) 2441 号			縮尺 1/50	図名 展開図-1		酒井		青島	6-1
	一級建築士 大臣登録第 365879 号 西原利昌									

G2

壁付け 住宅用火災報知器			数量
H	熱感知器	電池式(単独型)	1
	熱感知器	露出型	
壁付け 住宅用火災報知器			数量
S	煙感知器	電池式(単独型)	
	煙感知器	露出型	

※ 煙感知器は壁・梁より600mm以上離す
壁に取付ける場合、
天井から150mm以上500mm以内離す
換気扇・エアコン吹出口から1500mm以上離す

※ 全室LED照明とし、居室においては調光
制御、非居室においては人感センサーを
採用する。

※ 標準天井高さ2,400

※ 特記無きガラスは型ガラス


* 凡例

- ☒ 管柱 (105×105)
- ▶ Kダクト (3.30倍 FRM-0641)
- △ 片筋違い (2.00倍 45×90)
(例 左:柱脚 右:柱頭)
- ⊠ たすき掛筋違い (4.00倍 45×90)
- 構造用合板 (2.70倍)
(t=9 3枚付 EXハイパー)
- △ 床点検口
- ⊠ 天井点検口
- ⊗ 換気扇
- ⊗ 熱交換換気扇VLR-70

アドバンスシリーズ			
スマートデザイン (外部)			
凡例	1	コンセント	1ヶ所
①	2	コンセント	2ヶ所
②	3	コンセント	3ヶ所
③	1ET	コンセント1ヶ所接地ターミナル付	
④	2ET	コンセント2ヶ所接地ターミナル付	
⑤	WP	コンセント 防水型	
⑥	⑦	エアコン用コンセント	
⑧	⑨	200V用コンセント	
⑩	WP	防雨入線プレート	
⑪	⑫	スイッチ	
⑬	⑭	3路スイッチ	
⑮	⑯	4路スイッチ	
⑰	⑱	直結電源	
⑲	⑳	テレビ取出口	
㉑	TEL	電話取出口 (テレホンガイド)	
㉒	LAN	LAN取出口 (テレホンガイド)	
㉓	①	壁照明	
㉔	②	リモコン (給湯関係・ルフロ)	
㉕	③	メーター	
㉖	④	分電盤	
㉗	⑤	チャイム	

※ACコンセント天井付け
※TVアンテナ工事
※スイッチはFL+1100、コンセントはFL+200

決定図

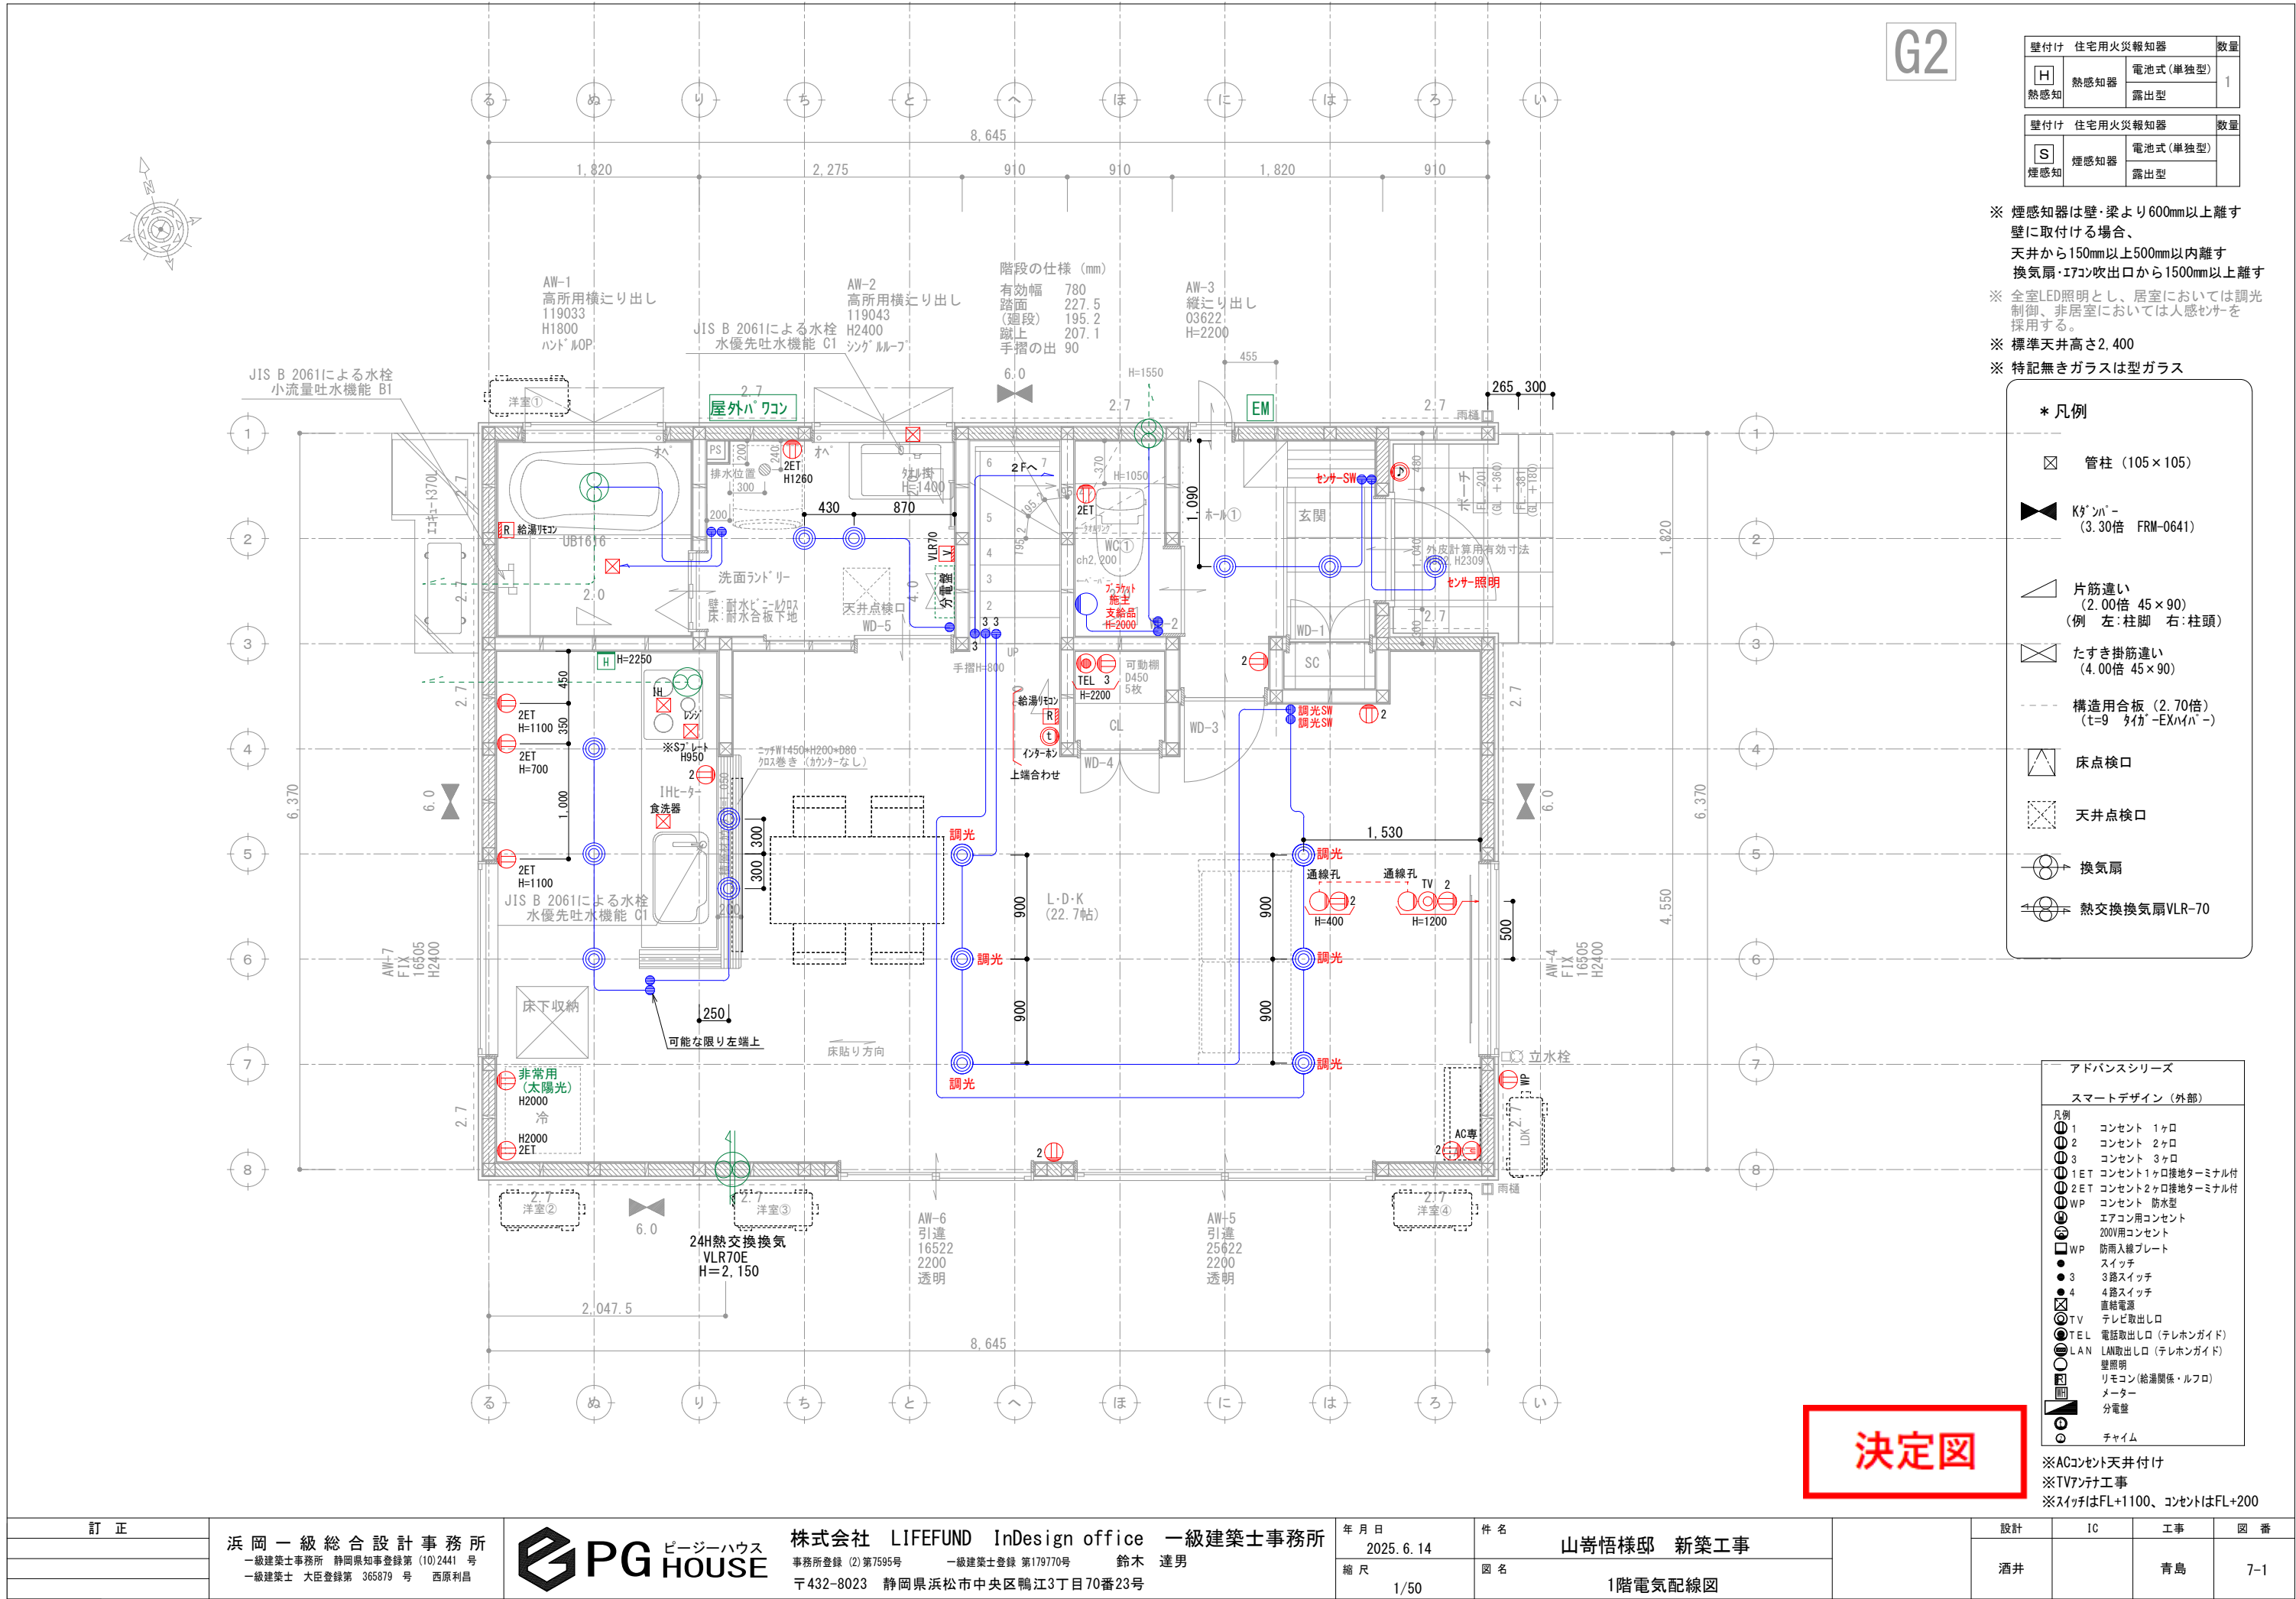

訂正	浜岡一級総合設計事務所 一級建築士事務所 静岡県知事登録第 (10)2441 号 一級建築士 大臣登録第 365879 号 西原利昌	PG HOUSE ピージーハウス	株式会社 LIFEFUND InDesign office 一級建築士事務所 事務所登録 (2) 第7595号 一級建築士登録 第179770号 鈴木 達男 〒432-8023 静岡県浜松市中央区鴨江3丁目70番23号	年月日	2025. 6. 14	件名	山崎悟様邸 新築工事	設計	IC	工事	図番
				縮尺	1/50	図名	1階電気配線図				
								酒井		青島	7-1

G2

壁付け 住宅用火災報知器			数量
H 熱感知	熱感知器	電池式(単独型)	
		露出型	
壁付け 住宅用火災報知器			数量
S 煙感知	煙感知器	電池式(単独型)	5
		露出型	

- ※ 煙感知器は壁・梁より600mm以上離す
壁に取付ける場合、
天井から150mm以上500mm以内離す
換気扇・エアコン吹出口から1500mm以上離す
- ※ 全室LED照明とし、居室においては調光
制御、非居室においては人感センサーを
採用する。
- ※ 標準天井高さ2,400
- ※ 特記無きガラスは型ガラス

* 凡例


- ☒ 管柱 (105×105)
- ◀▶ Kダクト (3.30倍 FRM-0641)
- △ 片筋違い (2.00倍 45×90)
(例 左:柱脚 右:柱頭)
- ⊠ たすき掛筋違い (4.00倍 45×90)
- 構造用合板 (2.70倍)
(t=9 3枚入-EKハイパー)
- △ 床点検口
- ⊠ 天井点検口
- ⊗ 換気扇
- ⊗ 熱交換換気扇VLR-70

アドバンスシリーズ			
スマートデザイン (外部)			
凡例	1	コンセント	1ヶ所
2	コンセント	2ヶ所	
3	コンセント	3ヶ所	
1ET	コンセント1ヶ所接地ターミナル付		
2ET	コンセント2ヶ所接地ターミナル付		
WP	コンセント 防水型		
⊗	エアコン用コンセント		
⊗	200V用コンセント		
WP	防雨入線プレート		
●	スイッチ		
●	3路スイッチ		
●	4路スイッチ		
⊗	直結電源		
TV	テレビ取出口		
TEL	電話取出口 (テレホンガイド)		
LAN	LAN取出口 (テレホンガイド)		
⊗	壁照明		
⊗	リモコン (給湯関係・ルフロ)		
⊗	メーター		
⊗	分電盤		
⊗	チャイム		


- ※ACコンセント天井付け
- ※TVアンテナ工事
- ※スイッチはFL+1100、コンセントはFL+200

決定図

訂正	浜岡一級総合設計事務所 一級建築士事務所 静岡県知事登録第 (10)2441 号 一級建築士 大臣登録第 365879 号 西原利昌	PG HOUSE ピージーハウス	株式会社 LIFEFUND InDesign office 一級建築士事務所 事務所登録 (2) 第7595号 一級建築士登録 第179770号 鈴木 達男 〒432-8023 静岡県浜松市中央区鴨江3丁目70番23号	年月日 2025. 6. 14	件名 山崎悟様邸 新築工事	設計 酒井	IC	工事 青島	図番 7-2
				縮尺 1/50	図名 2階電気配線図				

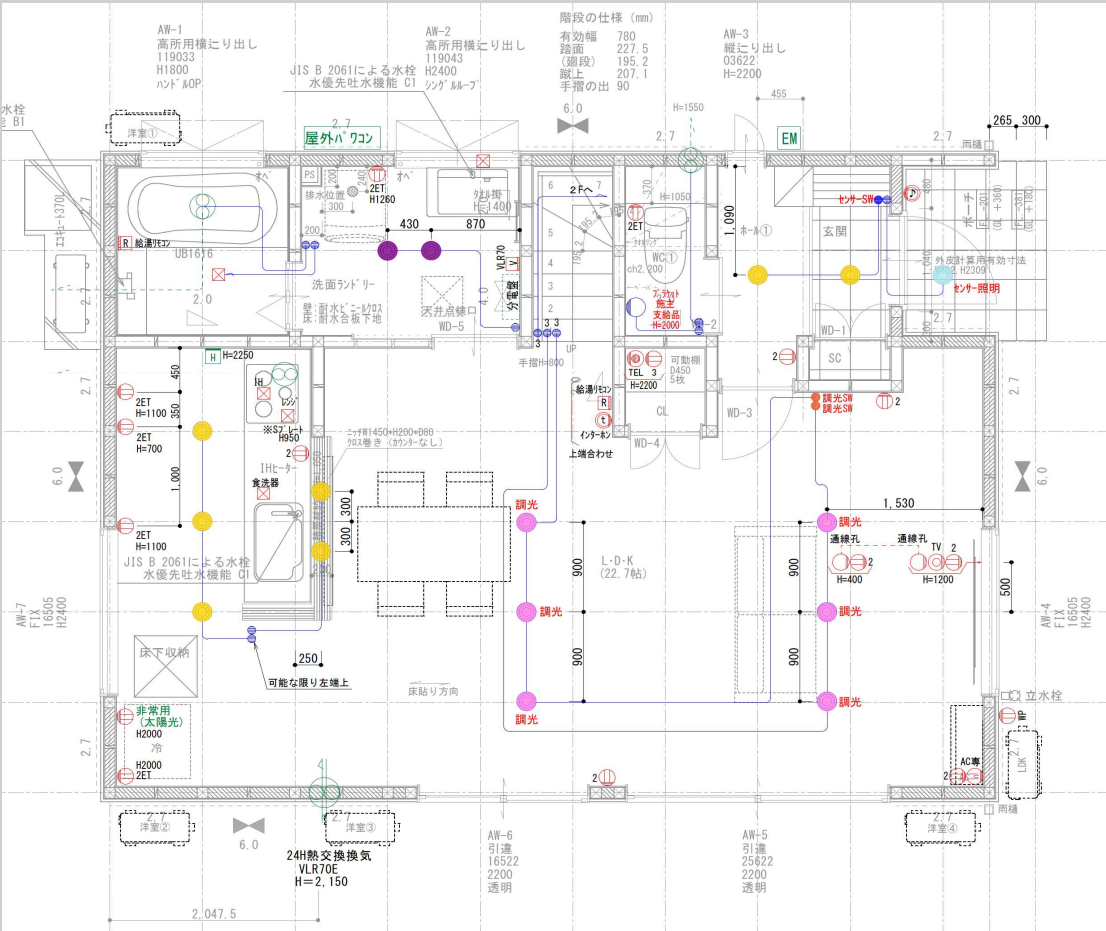

1階

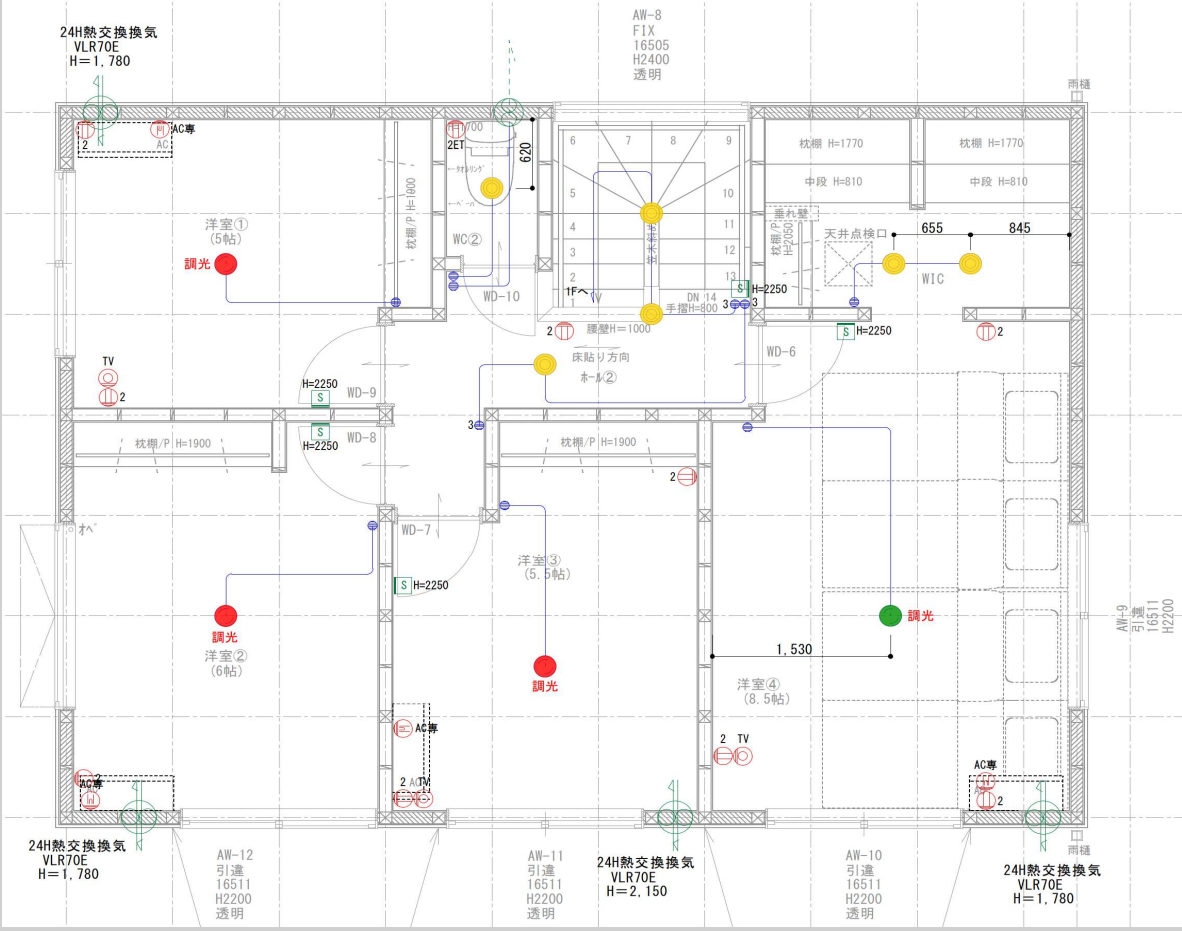

2階

ドアホン：VL-SZ30KL
(Panasonic)



内部SW：アドバンス
マットホワイト



ポーチ灯

×1

センサー付きダウナイト

DDL_4496YW

基本照明ダウナイト

×13

DDL_6102YW

洗面ランドリ

×2

ダウナイト

DDL_6102AW

LDK

×6

調光ダウナイト

DDL_6002YWG

洋室①、洋室②、洋室③

×3

シーリングライト

DCL_40507

洋室④

×1

シーリングライト

DCL_40508

LDK

×2

調光SW

WTA_57583WK

ホール

×1

センサーSW

WTA_14119W

高気密Se形
人感センサー

連動マルチタイプ

電球色 2700K・Ra83

DDL-4496 YW

¥16,800(税抜) (LED内蔵)

定格光束 420lm 消費電力 7.7W

LED LED 7.7W
白熱灯60W相当

- アルミダイカスト 白塗装
- アクリル 乳白(マット)
- 径φ111 埋込穴φ100 埋込深80mm 0.5kg
- 14VA
- 点灯角度調節機能付(暗・明切)
- 点灯保持時間(1分)
- 拡散パネル付 ■AC100V
- 送りの点灯可能 LED調光タイプ60VAまで
- LED非調光タイプ不可
- 蛍光灯不可 白熱灯60Wまで
- 光源寿命50,000時間
- 取付可能天井厚5~25mm
- 調光器併用不可

防雨形 温度保護機能付

COBタイプ | 高気密Se形

電球色 / 2700K・Ra83

DDL-6102 YW

¥3,600-(税抜) (LED内蔵)

LED LED 4.6W
白熱灯60W相当

- 鏡板 白塗装
- アクリル 乳白(マット)
- 径φ116 埋込穴φ100 埋込深70mm 0.3kg
- 5VA
- 拡散パネル付
- AC100V
- 光源寿命60,000時間
- 取付可能天井厚5~25mm
- 調光器併用不可

防雨形 温度保護機能付

COBタイプ | 高気密Se形

電球色 / 2700K・Ra83

DDL-6102 AW

¥3,600-(税抜) (LED内蔵)

LED LED 4.6W
白熱灯60W相当

- 鏡板 白塗装
- アクリル 乳白(マット)
- 径φ116 埋込穴φ100 埋込深70mm 0.3kg
- 5VA
- 拡散パネル付
- AC100V
- 光源寿命60,000時間
- 取付可能天井厚5~25mm
- 調光器併用不可

防雨形 温度保護機能付

COBタイプ | 高気密Se形

電球色 / 2700K・Ra83

DDL-6002 YWG

¥4,600-(税抜) (LED内蔵)

LED LED 5.8W
白熱灯60W相当

- 鏡板 白塗装
- アクリル 乳白(マット)
- 径φ116 埋込穴φ100 埋込深71mm 0.3kg
- 7VA
- 拡散パネル付
- AC100V
- 調光可能(1%~100%)
- 調光器併用不可
- 光源寿命60,000時間
- 取付可能天井厚5~25mm

防雨形 温度保護機能付

タイマー付リモコンブルース | 調色調光タイプ

電球色 / 6500K・Ra83 ~ 電球色 / 2700K・Ra83

DCL-40507

LED LED 29.5W 定格光束 3690lm 消費電力 29.5W 125.3lm/W

¥22,000-(税抜) (LED内蔵)

- アクリル 乳白(マット)
- 径φ110 高128mm 1.6kg
- フルスイング付(昼・夜・常夜灯)
- ※調光器の接続は別途要
- 調光機能付(6500K~2700K)
- 調光範囲付(5%~100%)
- 常夜灯60時間
- AC100V
- 光源寿命40,000時間
- 消費効率白色時
- 調光器併用不可
- シーンコントロールは使用できません。

タイプ別取付式
カバー別取付式

タイマー付リモコンブルース | 調色調光タイプ

電球色 / 6500K・Ra83 ~ 電球色 / 2700K・Ra83

DCL-40508

LED LED 34W 定格光束 4299lm 消費電力 34W 126.4lm/W

¥26,000-(税抜) (LED内蔵)

- アクリル 乳白(マット)
- 径φ110 高128mm 1.6kg
- フルスイング付(昼・夜・常夜灯)
- ※調光器の接続は別途要
- 調光機能付(6500K~2700K)
- 調光範囲付(5%~100%)
- 常夜灯60時間
- AC100V
- 光源寿命40,000時間
- 消費効率白色時
- 調光器併用不可
- シーンコントロールは使用できません。

タイプ別取付式
カバー別取付式

3H・HN(3.2A)
(ロータリー式)

WTA57583WK

希望小売価格 11,900円(税抜)

※掲載の価格には消費税は含まれていません。

[LED]埋込逆位相調光スイッチC(ほたるスイッチC)
(適合LED専用3.2A) (ロータリー式)

(下照照度設定機能付) (マットホワイト)

プレート別売

WTA7101WK

希望小売価格 320円(税抜)

※掲載の価格には消費税は含まれていません。

◆RAS(3A) (鏡器)

3線 / 4線式

WTA14119W


壁取付 熱線センサー付自動スイッチ(鏡器)
(検知後連続動作時間 約10秒~30分可変形)

(明るさセンサー・手動スイッチ付) (マットホワイト)

3A 100V AC

プレート別売

外部：スマートデザインシリーズ
ブラック

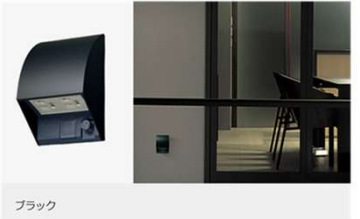

決定図


PG House

山崎 悟様 邸新築工事

Lighting Plan

2025.6.14

(図面 7-3)

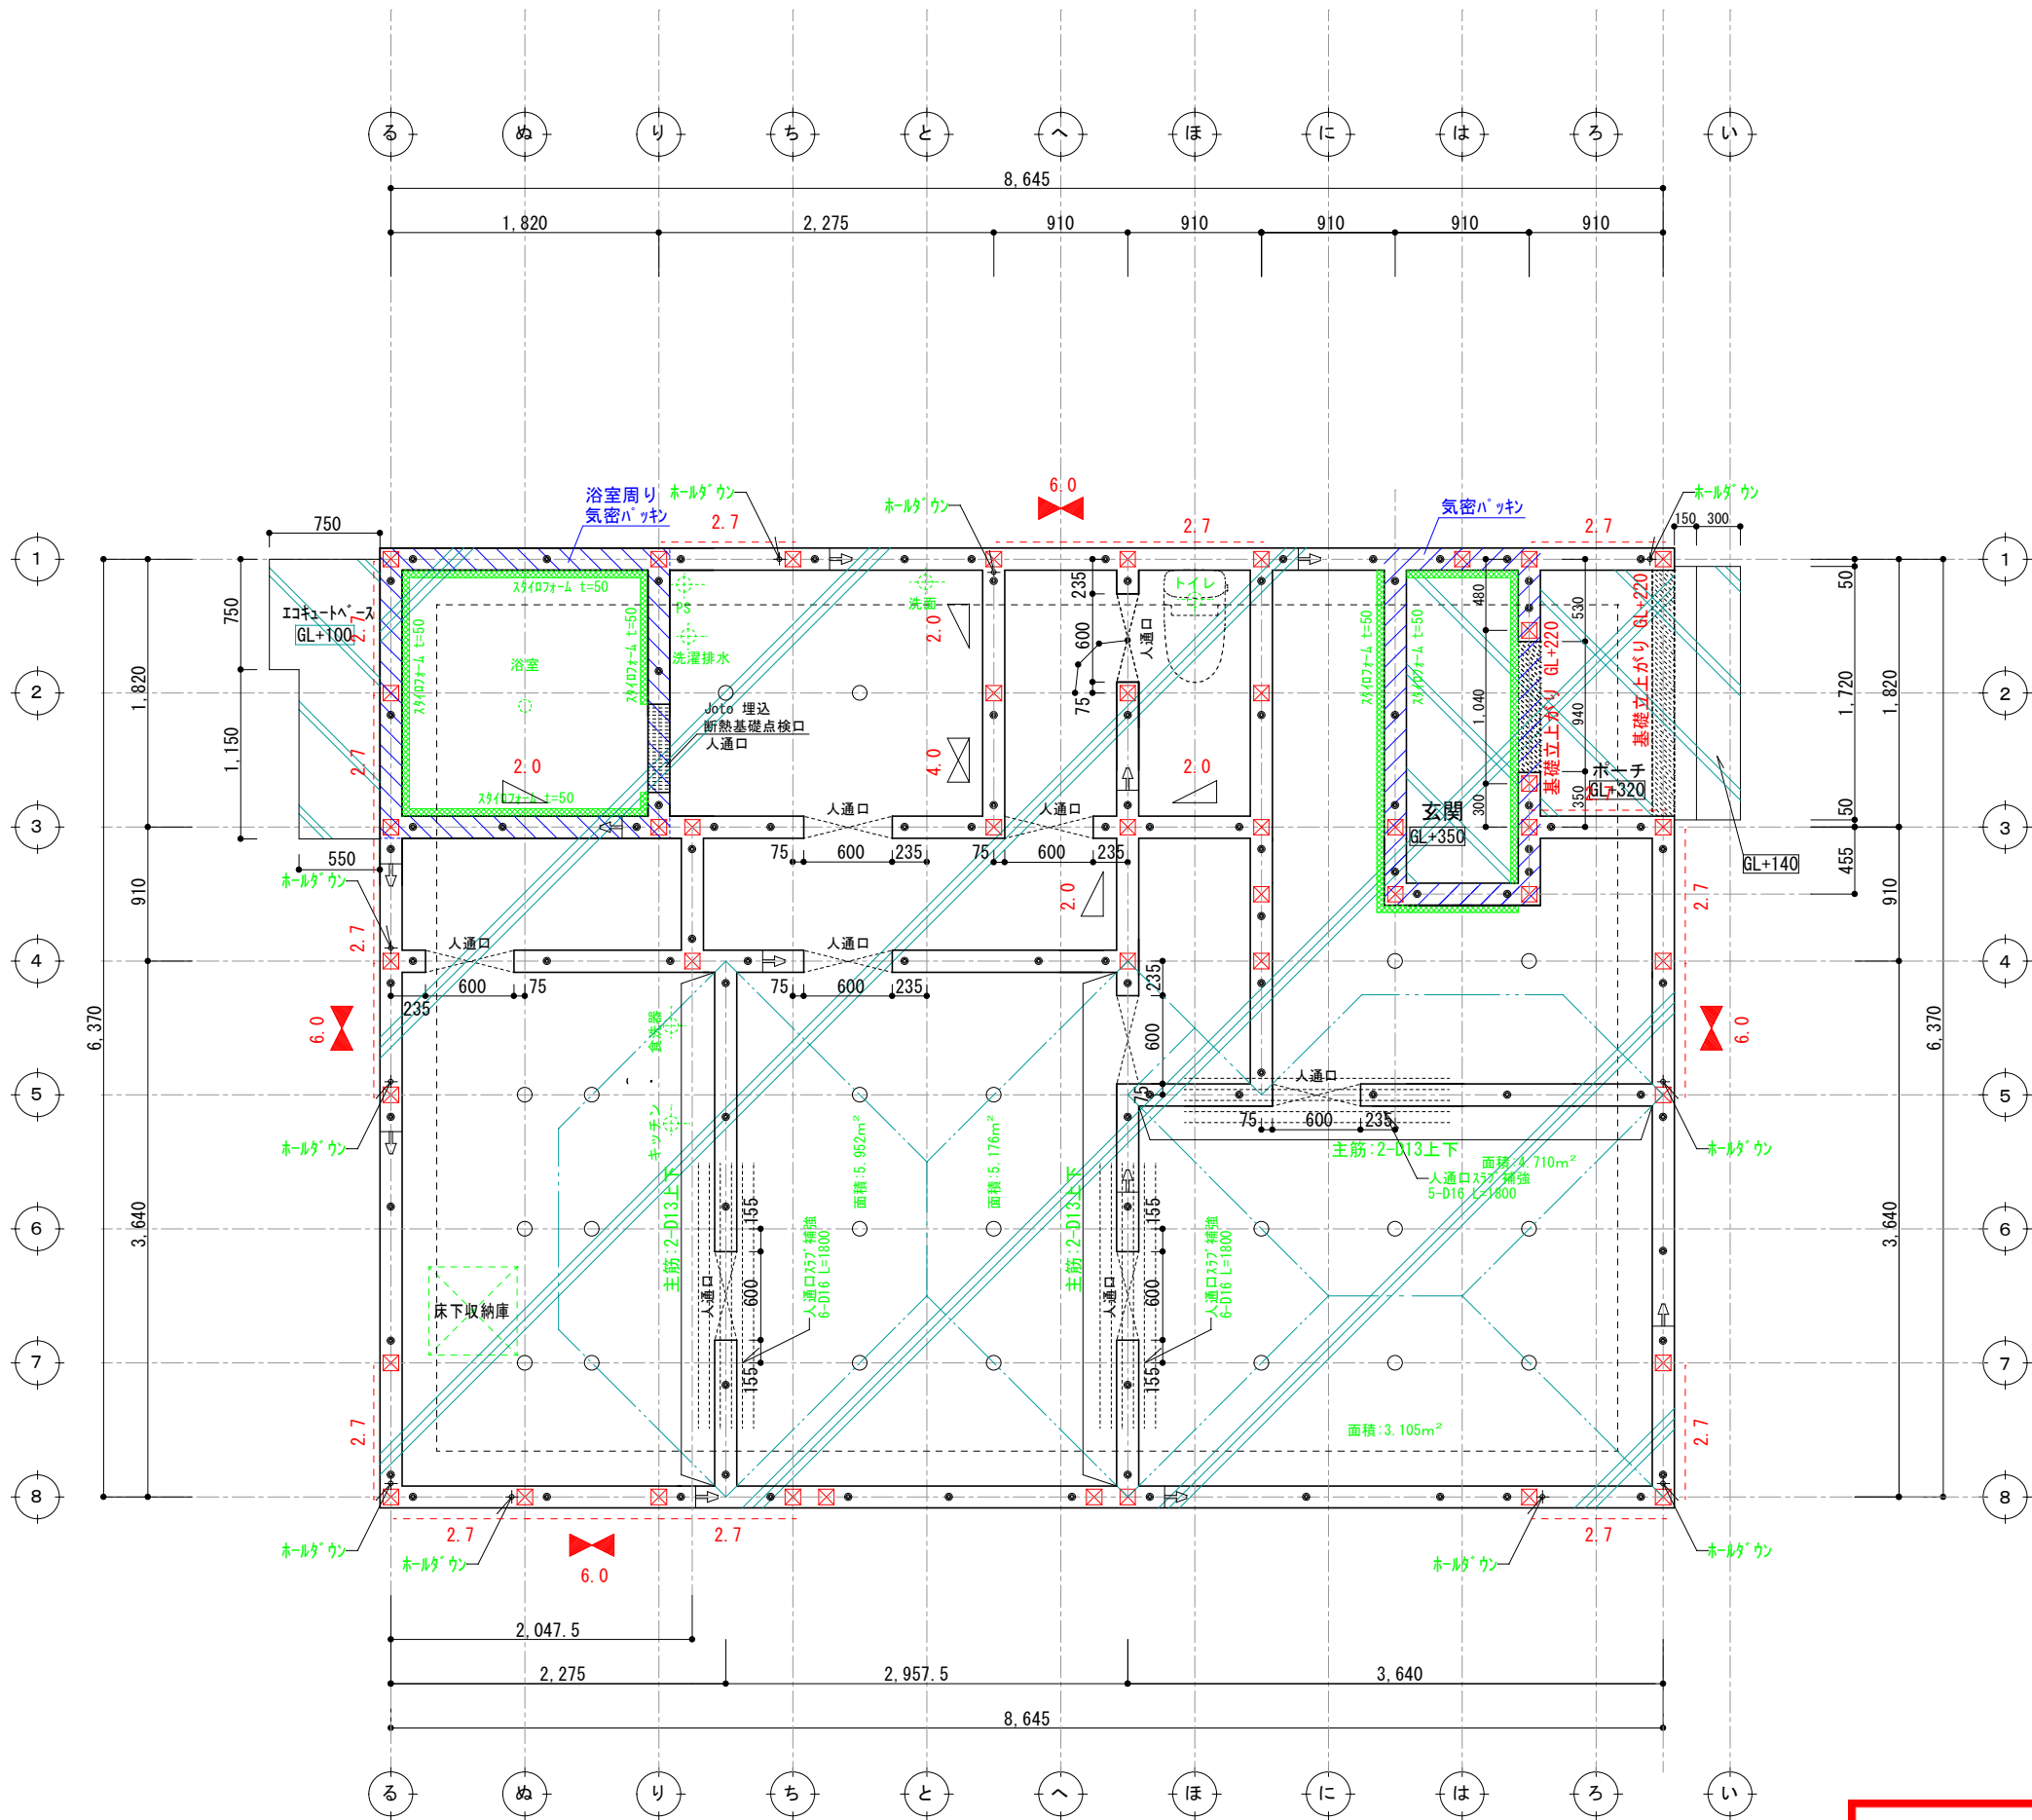

構造体ベースコンクリート t=150



後打ち土間コン




アンカーボルトの配置

- 土台切れの箇所より150mm
- 土台の継手及び仕口の端部より150mm
- 耐力壁の端部、筋交いの脚部より150mm
- 1.82m以下の間隔
- 250mm以上埋込み
- 基礎天端より120mm

筋かい凡例

- 柱脚 柱頭 片筋かい
- たすき掛け筋かい
- 構造用合板

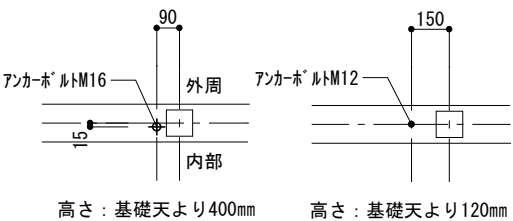

ホルダウン用アンカーボルト配置

アンカーボルト配置


凡例


- 通し柱 (105*105) 管柱 (105*105)
- アンカーボルトM12 L=400
- + ホルダーアンカーM16 L=800
- 柱芯より90mm 280mm以上埋め込み (カナイフリストアンカーボルトM16)
- ⊕ 鋼製束
- ≡ 土台ジョイント
- ▨ ベースコンクリート (t=150)
- ▨ 後打ちコンクリート

基礎伏図について特記なき場合に限り下記による。


1. コンクリート：呼び強度 21N/mm²
2. 鉄筋：SD295A
3. 設計地耐力：fe=20kN/m²
地耐力計測後、不足の場合は相当の改良を行い、満たすものとする。
4. 基礎の位置は、芯振分けとする。
5. 玄関・S/C・UB周囲の基礎天端は気密パッキン施工 (網掛け部) とし、その他の基礎天端は基礎パッキン施工とする。
6. 設備配管の屋内への取り入れは基礎立上り部のスリーブによる。

決定図

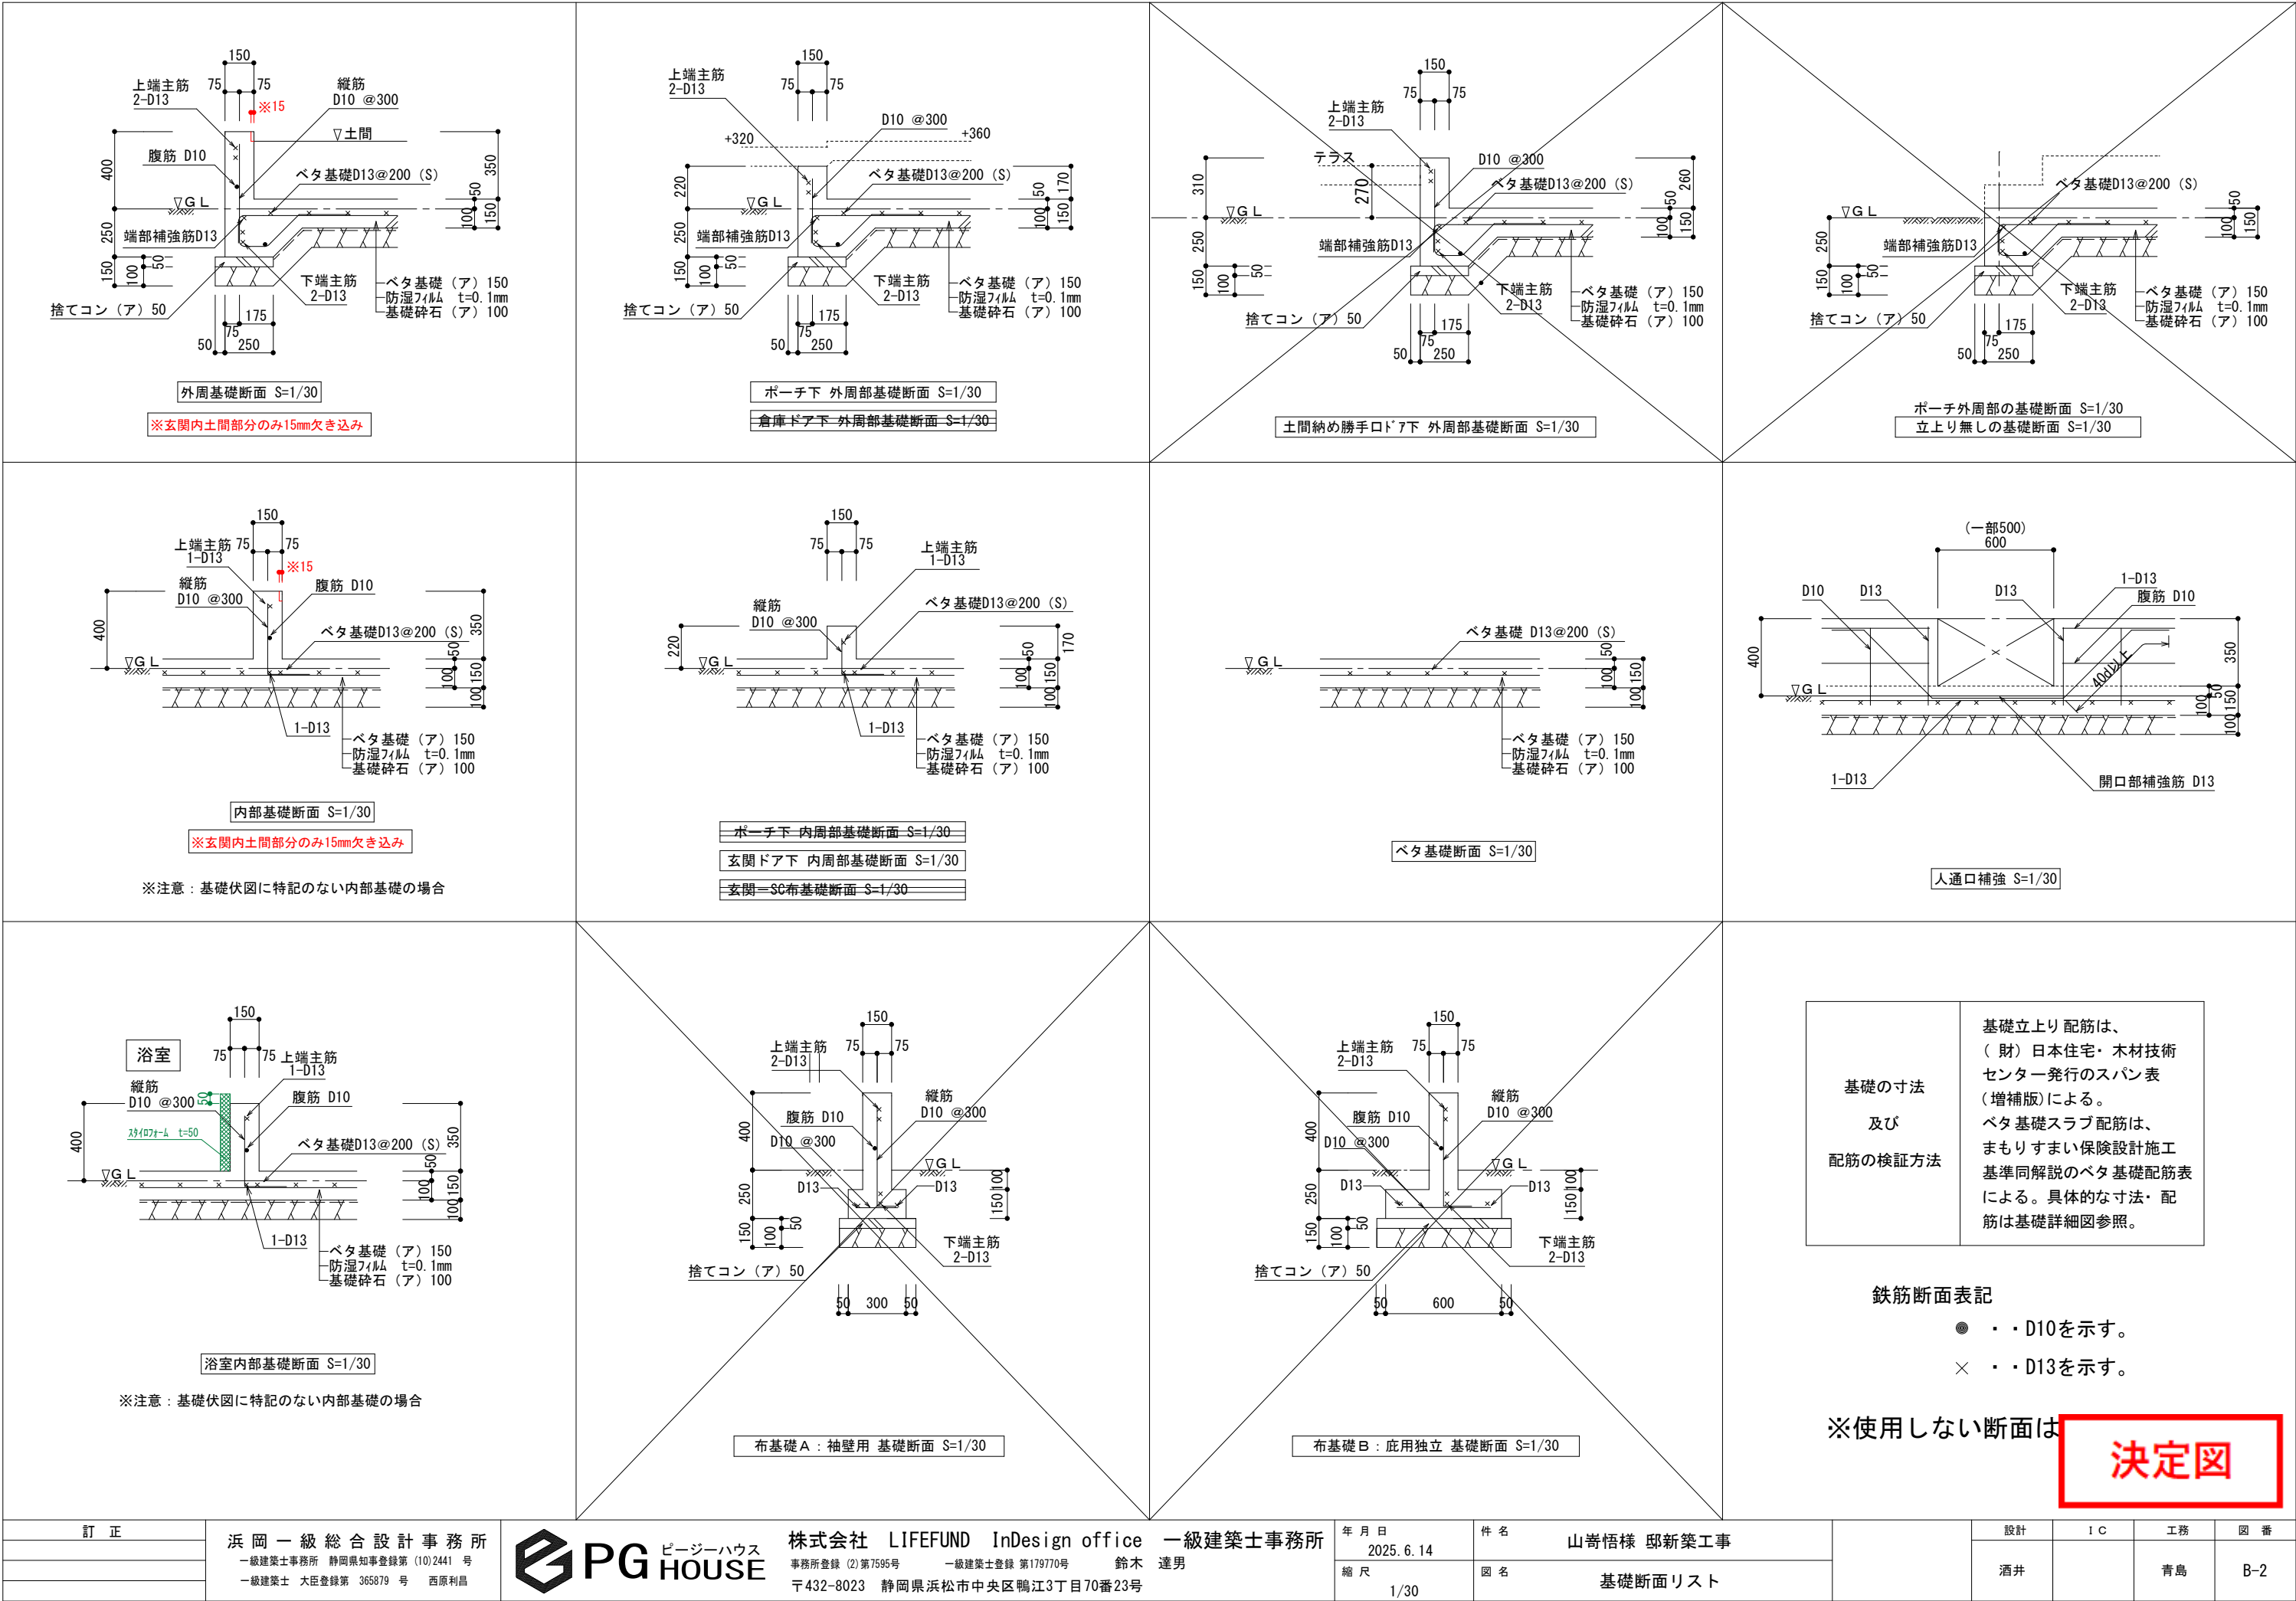

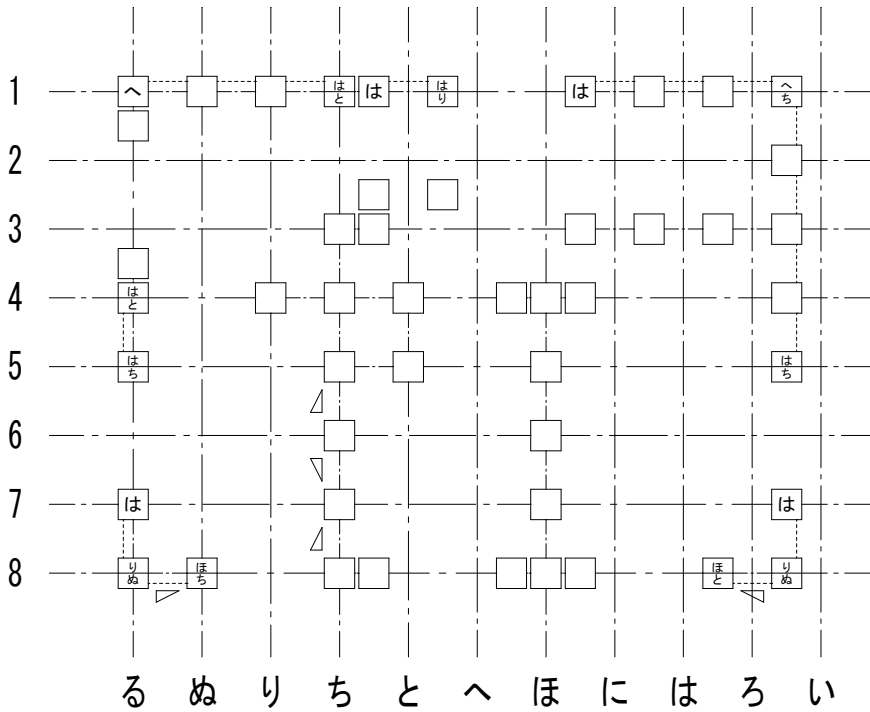

2 階柱壁伏図

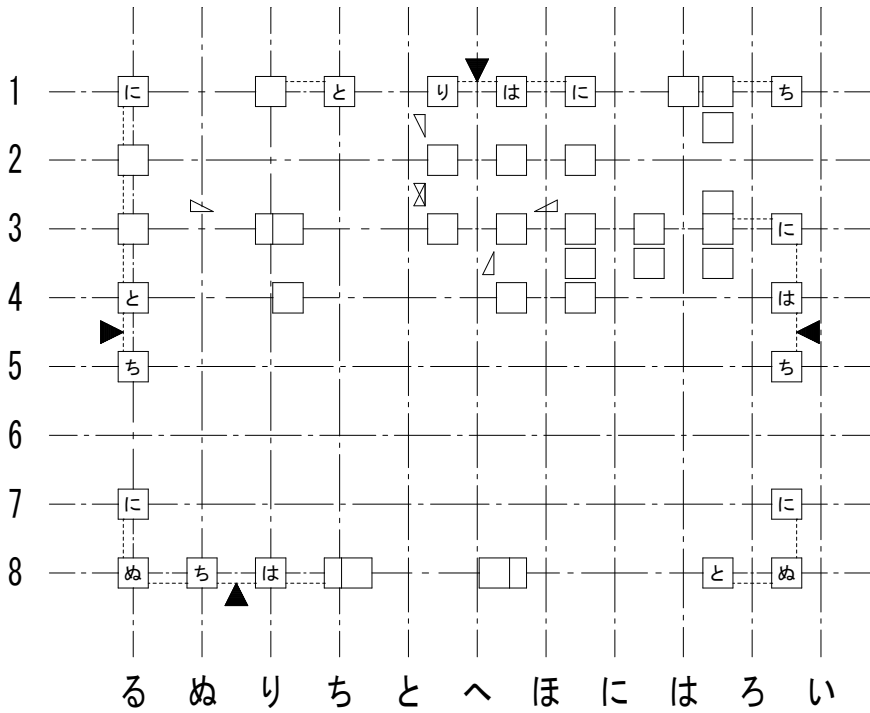

1 階柱壁伏図

接合部凡例				*接合部凡例はユーザ設定されたものです。	
記号	仕様（カナイ金物）		N	倍率	
SBCP	スリムビルドコーナー75, チビクリCK(化粧柱の場合)		0.00	1.00	
SBCP	スリムビルドコーナー75, チビクリCK(化粧柱の場合)		0.65	1.00	
SBCP	は	スリムビルドコーナー75	1.00	1.00	
ARCG	に	アレントコーナー合板用	1.40	2.20	
ARCG	ほ	アレントコーナー合板用	1.60	2.20	
ARCG	へ	アレントコーナー合板用	1.80	2.20	
HD15	と	ブレイブホールダウン B-HD15	2.80	3.60	
HD20	ち	ブレイブホールダウン B-HD20	3.70	4.70	
HD25	り	ブレイブホールダウン B-HD25	4.70	4.80	
HD30	ぬ	ブレイブホールダウン B-HD30	5.60	7.20	
J1	る	腰掛け蟻若しくは大入れ蟻掛け+羽子板ボルト、短冊金物		1.90	
J2	を	腰掛け蟻若しくは大入れ蟻掛け+羽子板ボルト、短冊金物×2		3.00	

※表示なき金物は「は」とする。

梁継手・仕口用

梁継手・仕口用

接合部凡例				*接合部凡例はユーザ設定されたものです。	
記号	仕様（タナカ金物）		N	倍率	
FCP	フックコーナー, チビクリCK(化粧柱の場合)		0.00	1.00	
FCP	フックコーナー, チビクリCK(化粧柱の場合)		0.65	1.00	
FCP	は	フックコーナー	1.00	1.00	
GCP	に	シナコーナー	1.40	2.20	
GCP	ほ	シナコーナー	1.60	2.20	
GCP	へ	シナコーナー	1.80	2.20	
HD15	と	ビス止めホールダウンU HD15	2.80	3.60	
HD20	ち	ビス止めホールダウンU HD20	3.70	4.70	
HD25	り	ビス止めホールダウンU HD25	4.70	4.80	
HD30	ぬ	ビス止めホールダウンU HD15×2 (HD35)	5.60	7.20	
J1	る	腰掛け蟻若しくは大入れ蟻掛け+羽子板ボルト、短冊金物		1.90	
J2	を	腰掛け蟻若しくは大入れ蟻掛け+羽子板ボルト、短冊金物×2		3.00	

※表示なき金物は「は」とする。

梁継手・仕口用

梁継手・仕口用

筋かいの種類に応じた筋かいの端部の接合部の仕様		
	筋かいの種類	接合部の仕様（構造方法）
イ	鉄筋φ9	柱又は横架材を貫通し、三角座金を介してナット締め、又は鋼板添え板を用い鋼板を柱及び横架材にCN90, 8本平打ち
ロ	筋かい:15×90	柱・横架材を欠き込み、柱・横架材双方に対してN65, 5本平打ち
ハ	筋かい:30×90	鋼板添え板t=1.6mmを筋かいに対してボルトφ12及びCN65, 3本平打ち、柱に対してCN65, 3本平打ち、横架材に対してCN65, 4本平打ち。筋かいプレートBP同等品
ニ	筋かい:45×90	鋼板添え板t=2.3mmを筋かいに対してボルトφ12及びスクリュー釘φ4.5L50, 7本平打ち、柱及び横架材に対してスクリュー釘φ4.5L50, 5本平打ち。筋かいプレートBP-2同等品
ホ	筋かい:90×90	柱又は横架材にボルトφ12mmを用いて一面剪断接合

胴差と通し柱の接合部の仕様		
	胴差と通し柱の条件	仕口
T1	通し柱の片側に胴差が来る場合	胴差を柱にかたぎ大入れ短ほぞ差しの上、羽子板ボルト、かね折り金物又は同等以上の仕口
T2	通し柱の両側に胴差が来る場合	胴差を柱にかたぎ大入れ短ほぞ差しの上、短冊金物又は、同等以上の仕口で胴差相互を緊結
T3	通し柱と胴差の接合部の近くに90×90以上の筋かいが来る場合(通し柱が建物の出隅にあるか、筋かい壁が外壁と直交して接する場合)	胴差を通し柱に、15KN用引き寄せ金物を水平に用いて緊結

決定図

G2

壁付付 住宅用火災報知器			数量
H 熱感知	熱感知器	電池式(单独型)	1
		露出型	
壁付付 住宅用火災報知器			数量
S 煙感知	煙感知器	電池式(单独型)	
		露出型	

※ 煙感知器は壁・梁より600mm以上離す
壁に取付ける場合、
天井から150mm以上500mm以内離す
換気扇・エアコン吹出口から1500mm以上離す
※ 全室LED照明とし、居室においては調光
制御、非居室においては人感センサーを
採用する。
※ 標準天井高さ2,400
※ 特記無きガラスは型ガラス


* 凡例

- ☒ 管柱 (105×105)
- ☒ K9ノック (3.30倍 FRM-0641)
- △ 片筋違い (2.00倍 45×90)
(例 左:柱脚 右:柱頭)
- ☒ たすき掛筋違い (4.00倍 45×90)
- 構造用合板 (2.70倍)
(t=9 タイガ EXH(ハナ))
- △ 床点検口
- ☒ 天井点検口
- ☒ 換気扇
- ☒ 熱交換換気扇VLR-70

アドバンスシリーズ	
スマートデザイン (外部)	
凡例	
①	コンセント 1ヶ所
②	コンセント 2ヶ所
③	コンセント 3ヶ所
①ET	コンセント1ヶ所接地ターミナル付
②ET	コンセント2ヶ所接地ターミナル付
①WP	コンセント 防水型
②WP	エアコン用コンセント
③WP	200V用コンセント
④WP	防雨入線プレート
⑤	スイッチ
③	3路スイッチ
④	4路スイッチ
⑥	直結電源
⑦TV	テレビ取出口
⑧TEL	電話取出口 (テレホンガイド)
⑨LAN	LAN取出口 (テレホンガイド)
⑩	壁照明
⑪	リモコン (給湯関係・ルフロ)
⑫	メーター
⑬	分電盤
⑭	チャイム

※ACコンセント天井付け
※TVアンテナ工事
※スイッチはFL+1100、コンセントはFL+200

決定図

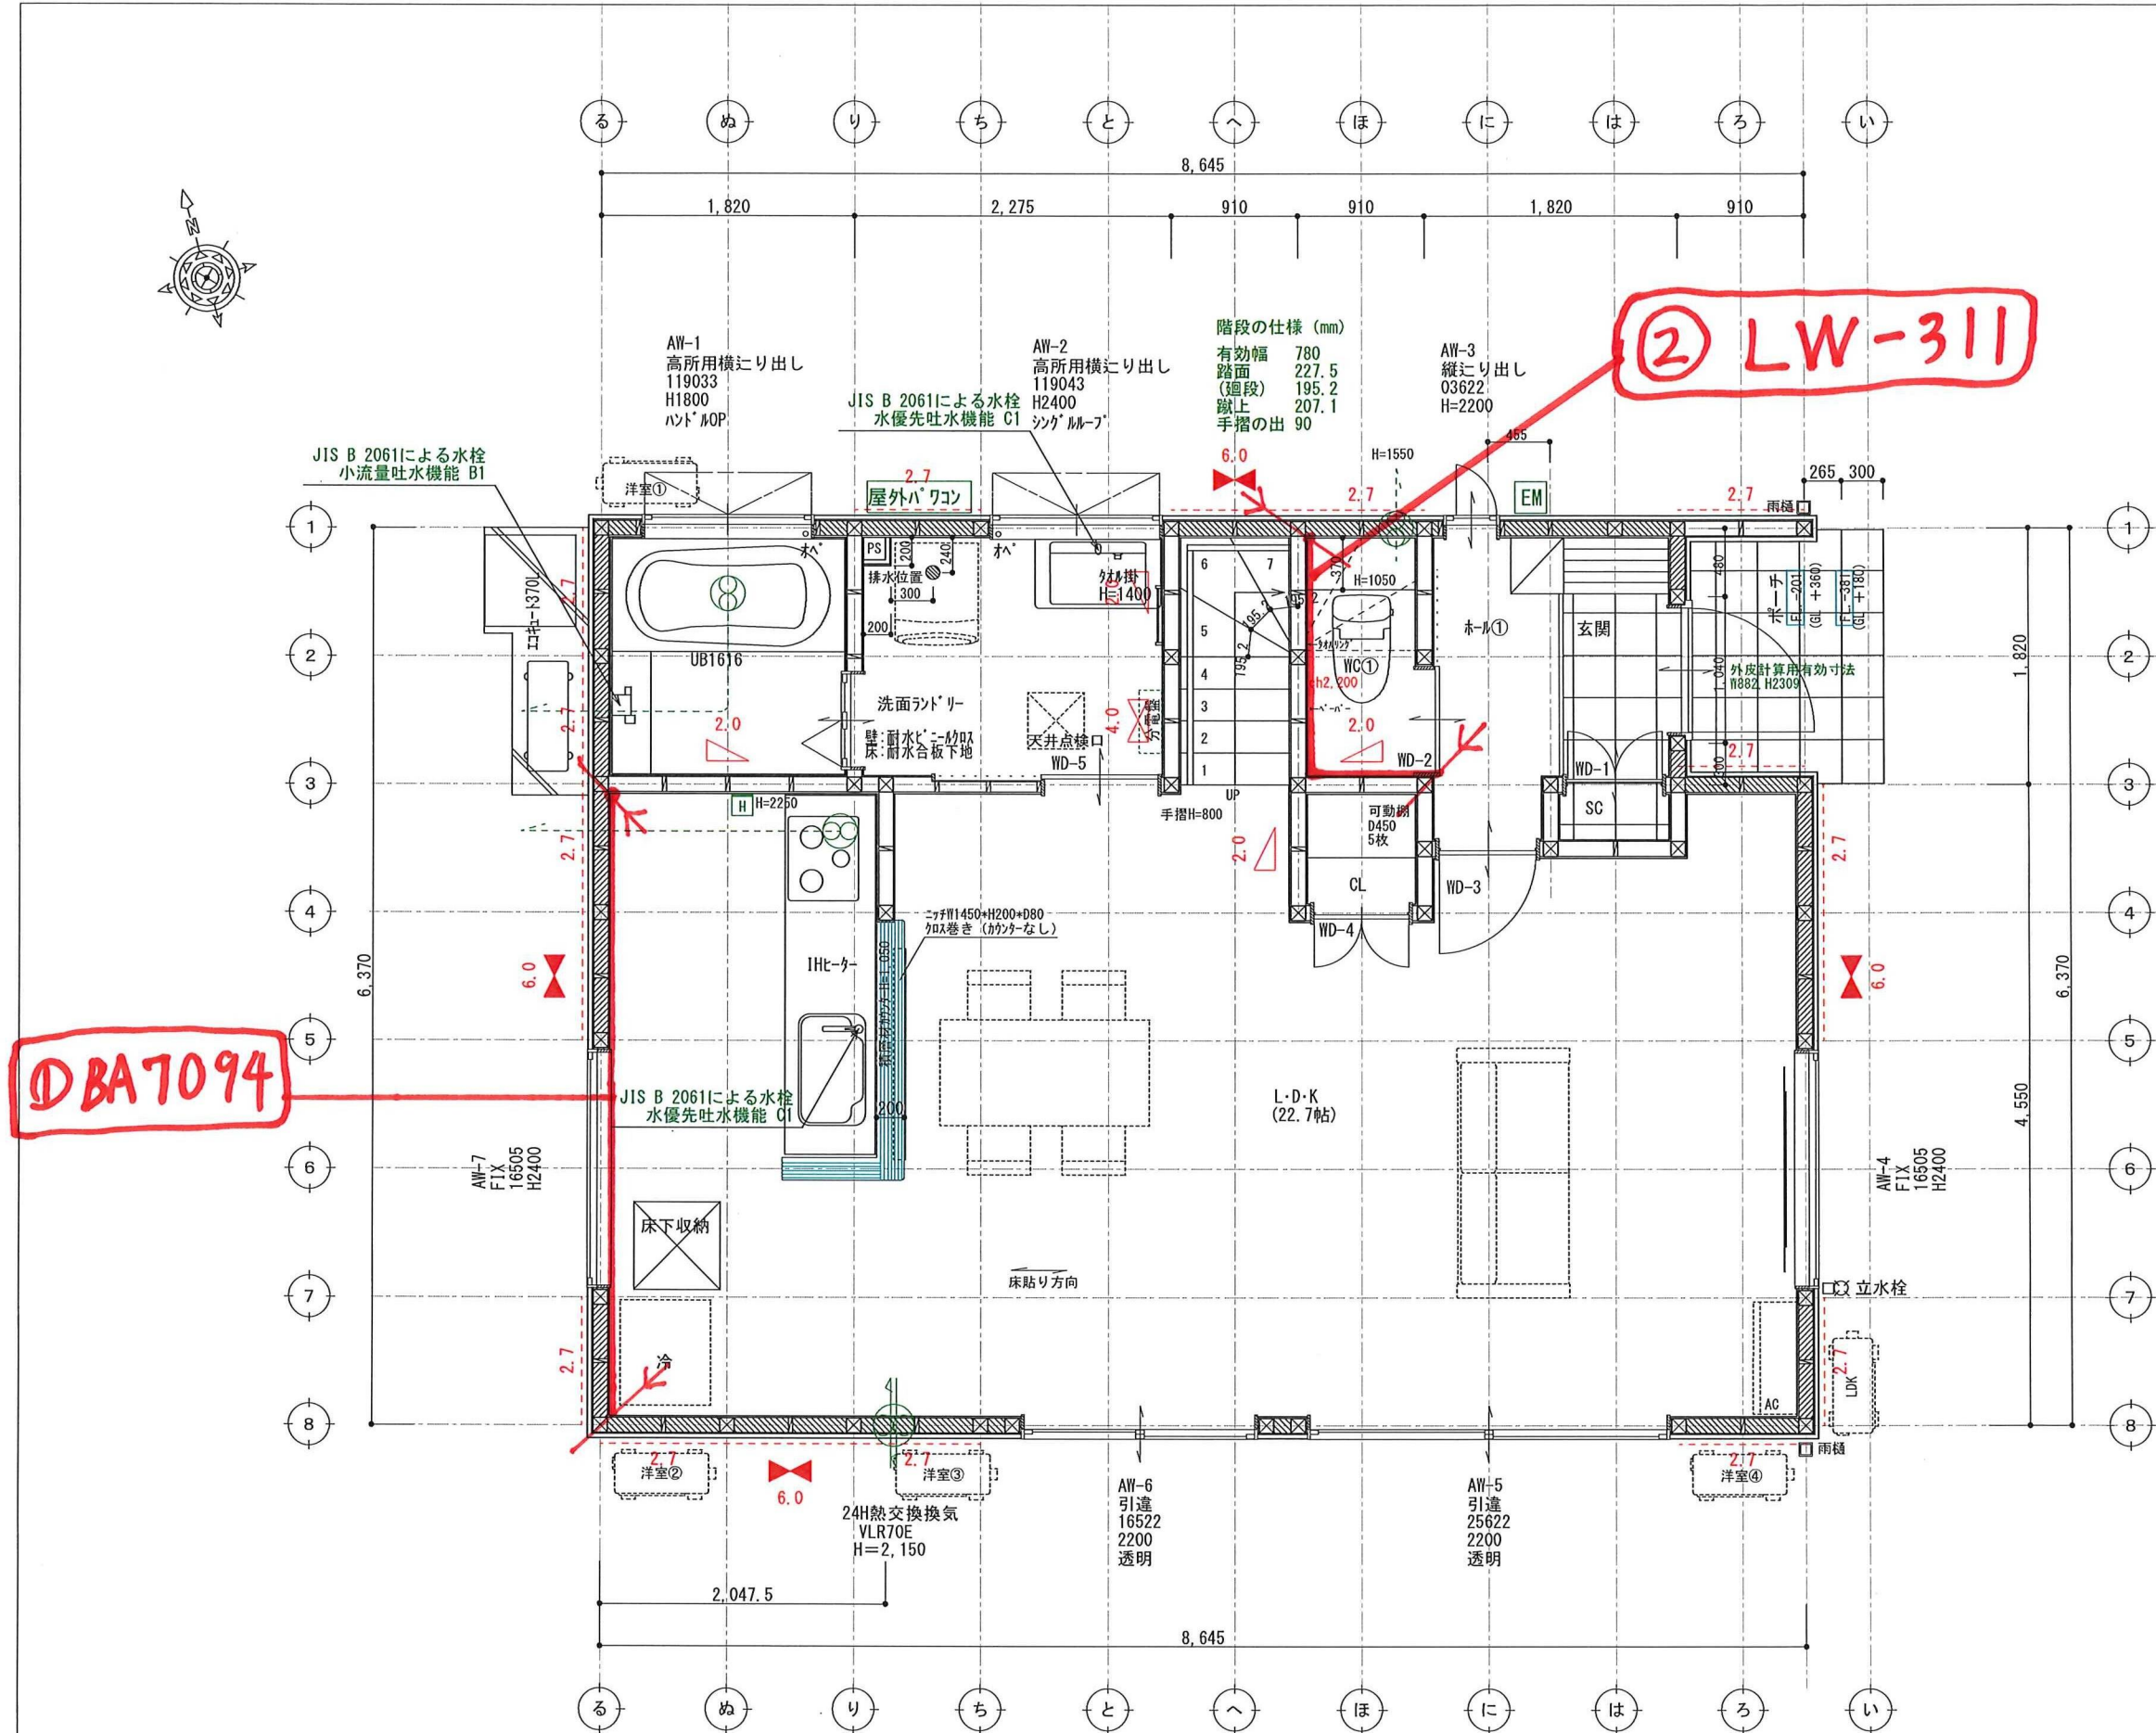

DBA7094

G2

壁付け 住宅用火災報知器			数量
H 熱感知	電池式(単独型)		8
	露出型		
壁付け 住宅用火災報知器			数量
S 煙感知	電池式(単独型)		8
	露出型		

- ※ 煙感知器は壁・梁より600mm以上離す
壁に取付ける場合、
天井から150mm以上500mm以内離す
換気扇・エアコン吹出口から1500mm以上離す
- ※ 全室LED照明とし、居室においては調光
制御、非居室においては人感センサーを
採用する。
- ※ 標準天井高さ2,400
- ※ 特記無きガラスは型ガラス

* 凡例

- ☒ 管柱 (105×105)
- ◀▶ Kダクト (3.30倍 FRM-0641)
- △ 片筋違い (2.00倍 45×90)
(例 左:柱脚 右:柱頭)
- ⊠ たすき掛筋違い (4.00倍 45×90)
- 構造用合板 (2.70倍)
(t=9 タガ-EXハイパー)
- ⬆ 床点検口
- ⬆ 天井点検口
- ⊗ 換気扇
- ⊗ 熱交換換気扇VLR-70

アドバンスシリーズ	
スマートデザイン (外部)	
凡例	
①	コンセント 1ヶ所
②	コンセント 2ヶ所
③	コンセント 3ヶ所
①ET	コンセント1ヶ所接地ターミナル付
②ET	コンセント2ヶ所接地ターミナル付
WP	コンセント 防水型
WP	エアコン用コンセント
WP	200V用コンセント
WP	防雨入線プレート
●	スイッチ
●3	3路スイッチ
●4	4路スイッチ
⊗	直結電器
⊗TV	テレビ取出口
⊗TEL	電話取出口 (テレホンガイド)
⊗LAN	LAN取出口 (テレホンガイド)
⊗	壁照明
⊗	リモコン (給湯関係・ルフロ)
⊗	メーター
⊗	分電盤
⊗	チャイム

- ※ACコンセント天井付け
- ※TVアンテナ工事
- ※スイッチはFL+1100、コンセントはFL+200

決定図

