



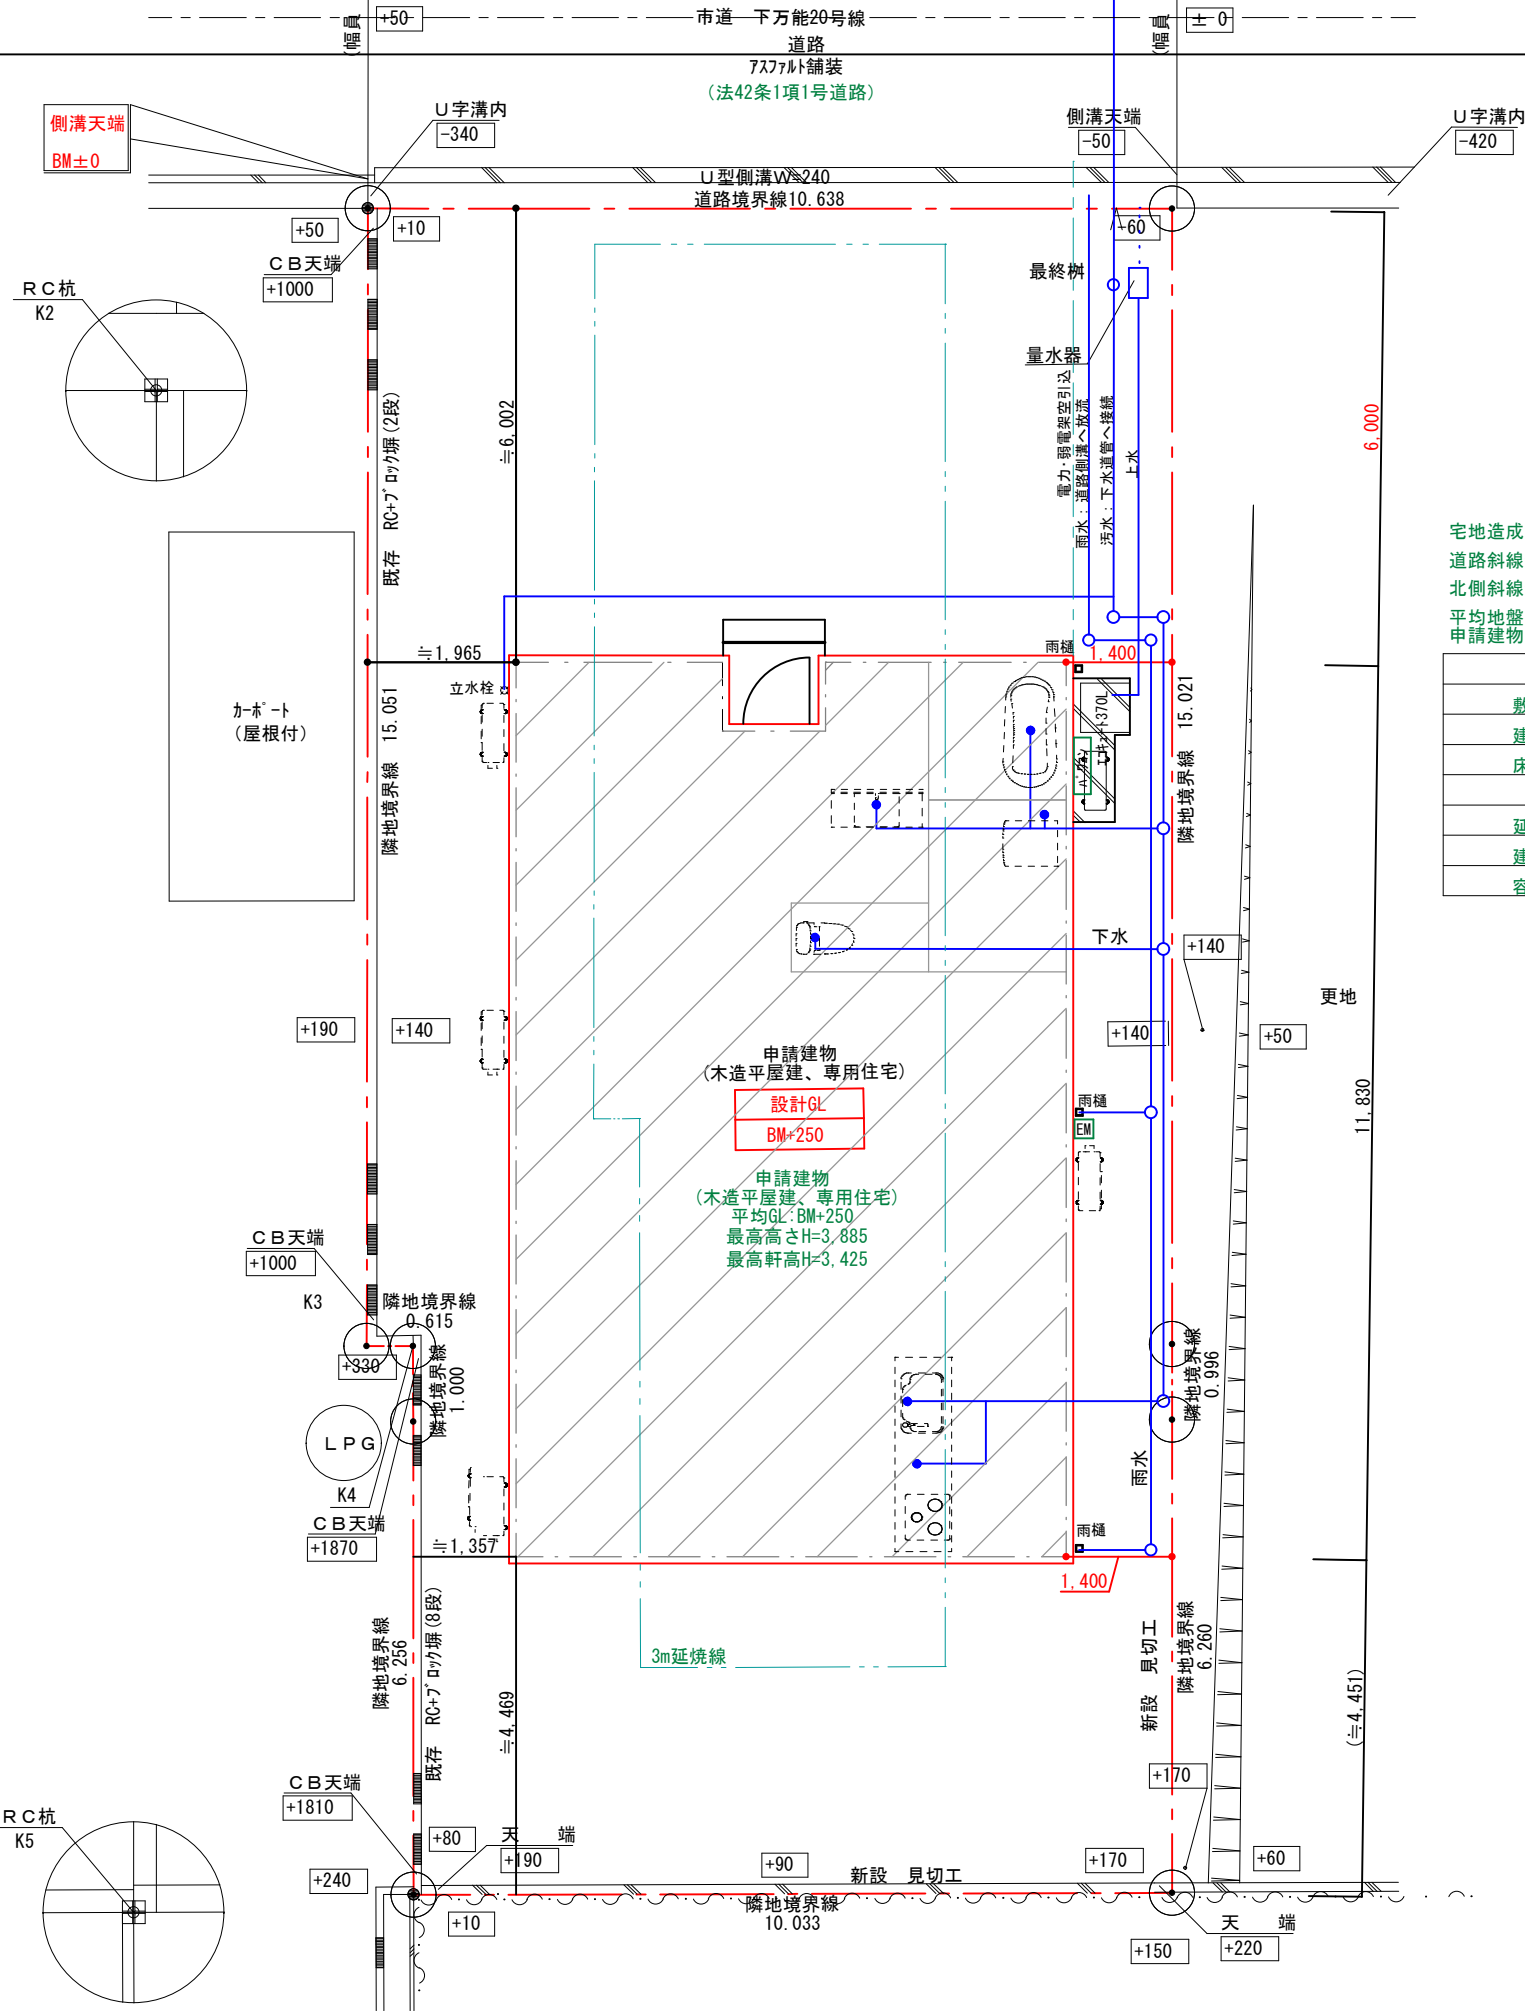

宅地造成等工事規制による盛土切土無し
道路斜線制限については、明らかに適合する。
北側斜線制限については、明らかに適合する。
平均地盤面について
申請建物の周囲の平均地盤面高さをBM+250とする。

トータル面積表 (㎡)	
敷地面積	232.90
建築面積	86.12
床面積 1階	85.19
延床面積	85.19
建築率	$(86.12/232.90) \times 100$ 36.98%
容積率	$(85.19/232.90) \times 100$ 36.58%

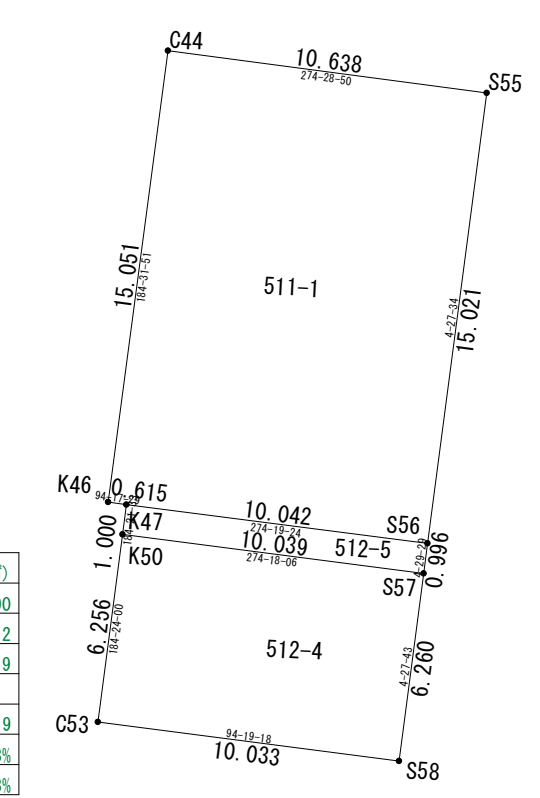

座 標 求 積 表

地 番	512-4			
測 点	Xn	Yn	(Xn+1 - Xn-1) Yn	距 離
K50	198.896	72.120	-395.578200	6.256
C53	192.658	71.640	-501.050160	10.033
S58	191.902	81.644	447.817340	6.260
S57	198.143	82.131	574.424214	10.039
		倍 面 積	125.613194	
		面 積	62.8065970	
		地 積	62.80 m ²	

地 番	512-5			
測 点	Xn	Yn	(Xn+1 - Xn-1) Yn	距 離
K47	199. 893	72. 196	-17. 327040	1. 000
K50	198. 896	72. 120	-126. 210000	10. 039
S57	198. 143	82. 131	19. 711440	0. 996
S56	199. 136	82. 209	143. 865750	10. 042
		倍 面 積	20. 040150	
		面 積	10. 0200750	
		地 積	10. 02 m ²	

地 番	511-1			
測 点	Xn	Yn	(Xn+1 - Xn-1)Yn	距 離
S55	214. 112	83. 377	1317. 940239	10. 638
C44	214. 943	72. 772	-1031. 397556	15. 051
K46	199. 939	71. 583	-1077. 324150	0. 615
K47	199. 893	72. 196	-57. 973388	10. 042
S56	199. 136	82. 209	1168. 929771	15. 021
		倍 面 積	320. 174916	
		面 積	160. 0874580	
		地 積	160. 08 m ²	

敷地合計面積
62.80+10.02+160.08=232.90㎡

決定図