
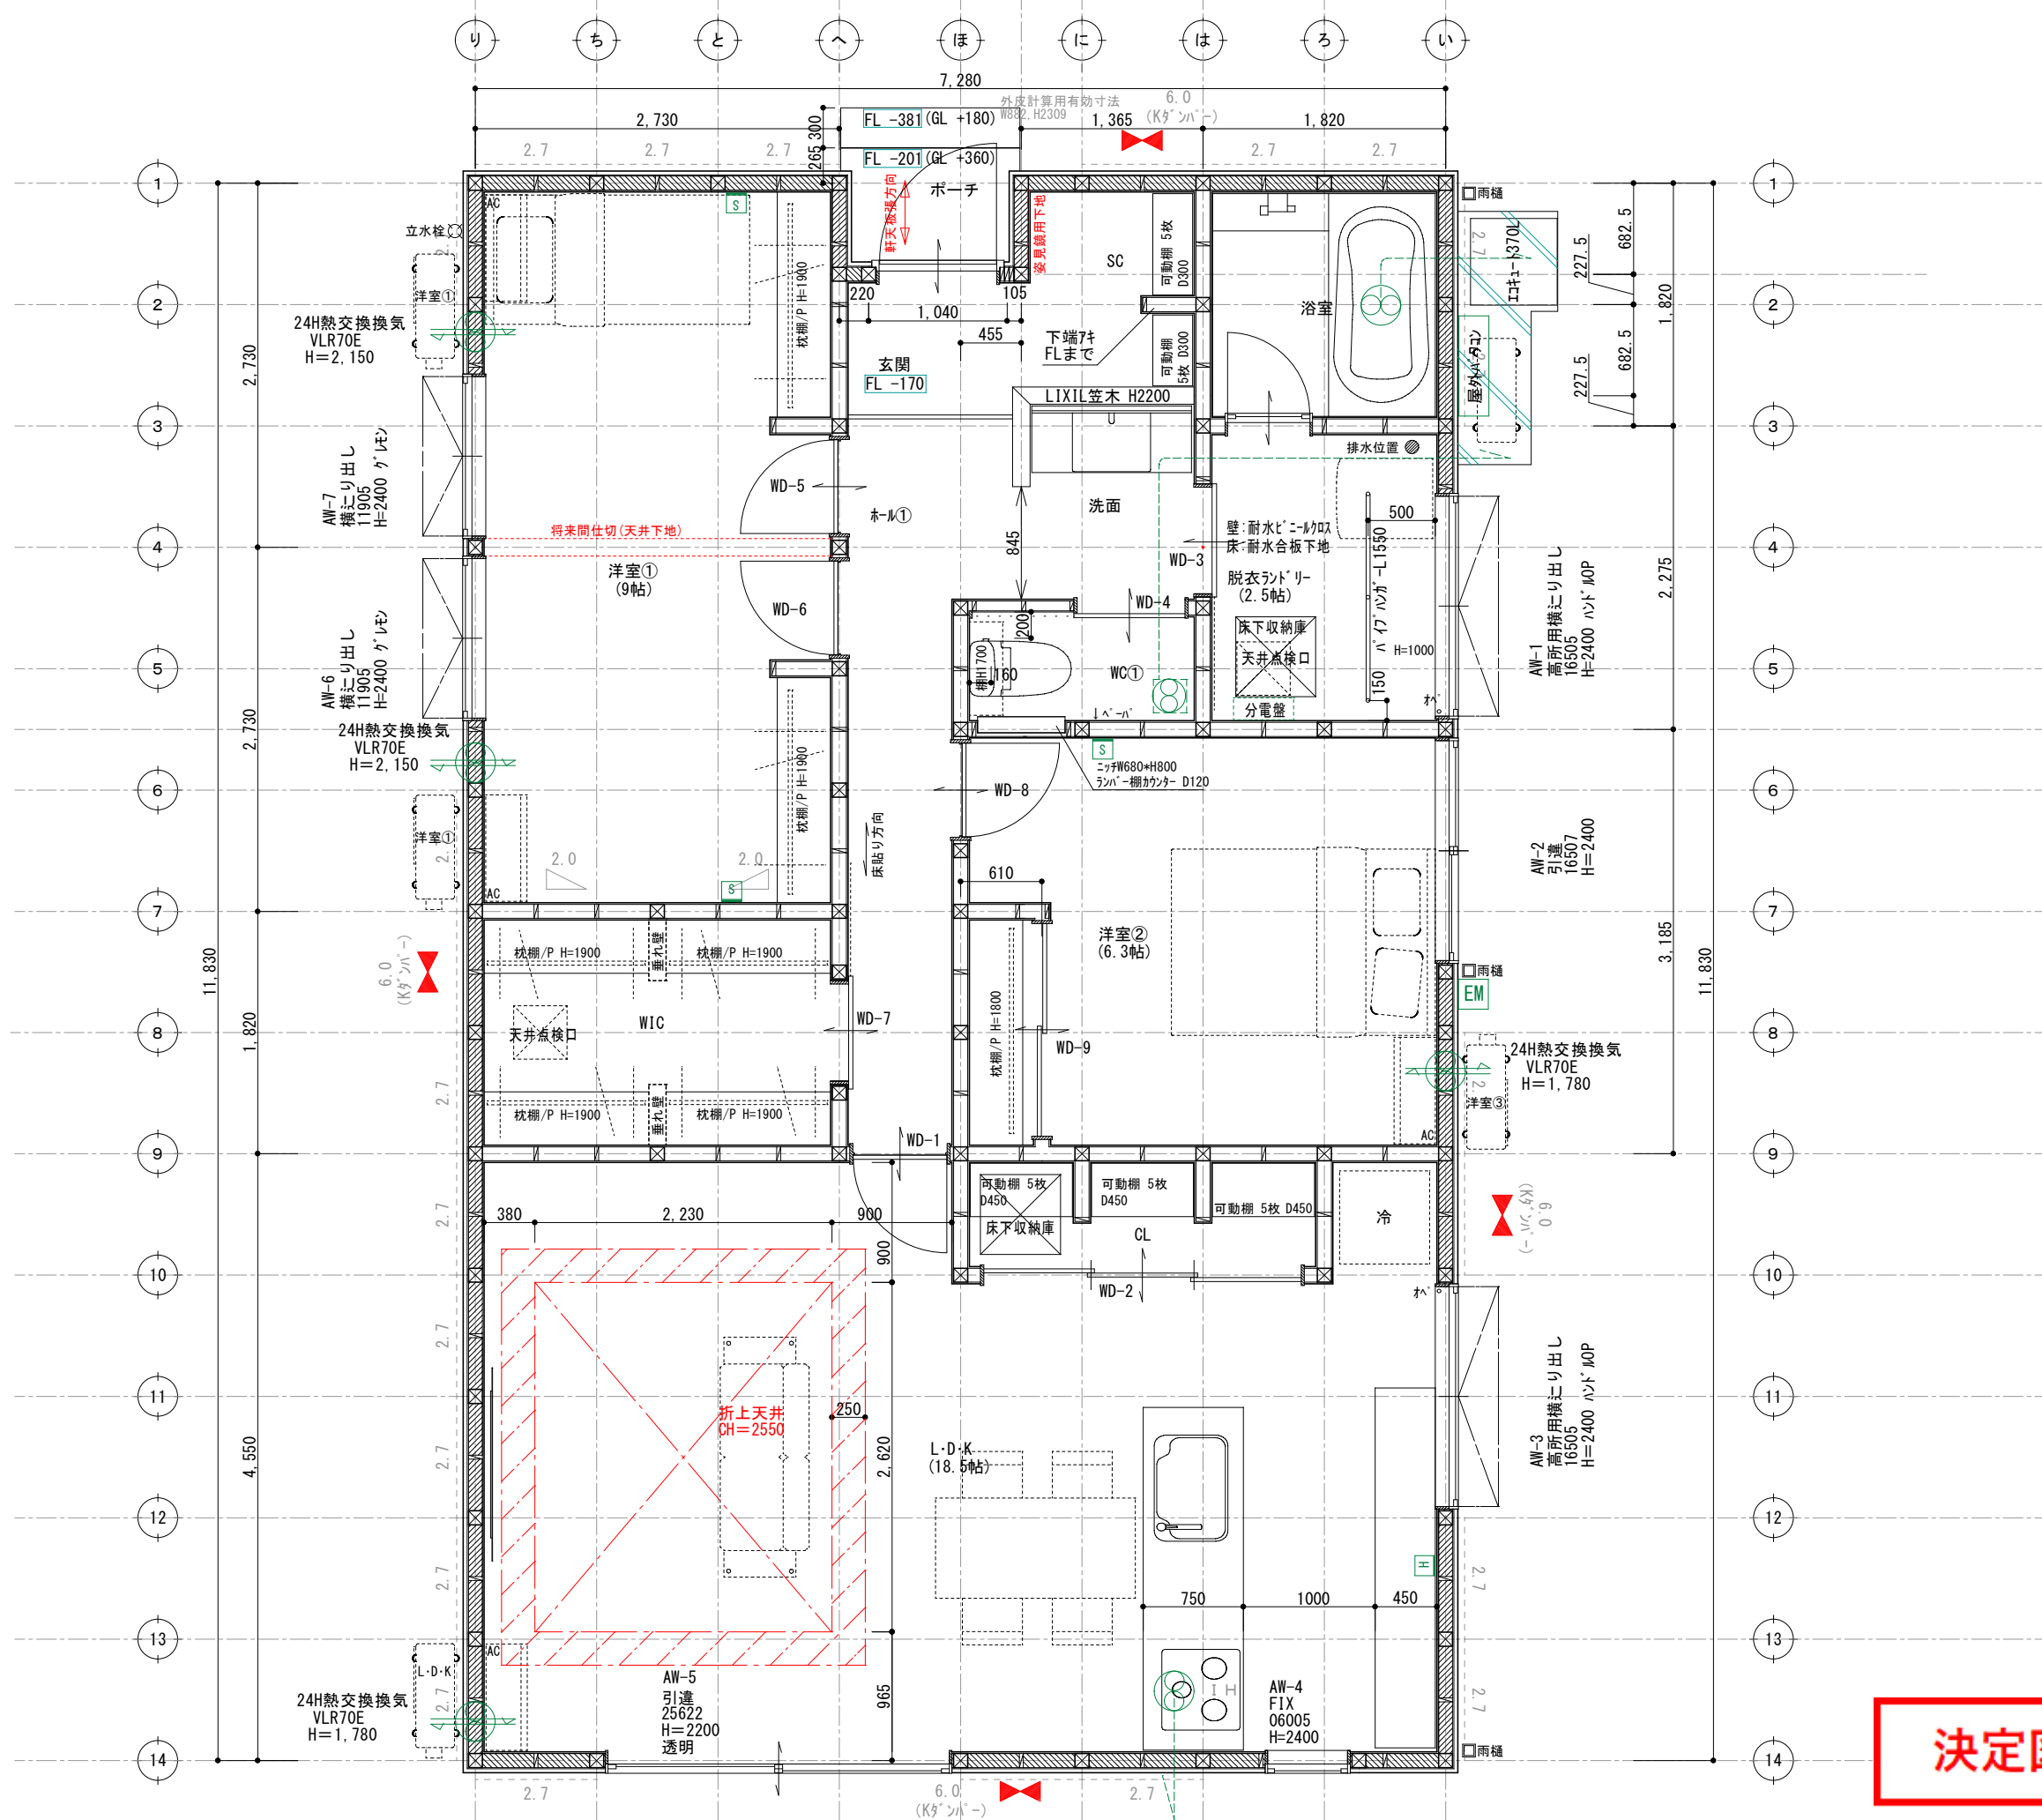


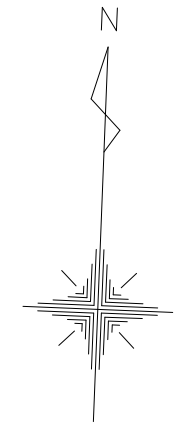

壁付け 住宅用火災報知器			数量
H	熱感知器	電池式(単独型)	1
	露出型		
壁付け 住宅用火災報知器			数量
S	煙感知器	電池式(単独型)	
	露出型		

※ 煙感知器は壁・梁より600mm以上離す
壁に取付ける場合、
天井から150mm以上500mm以内離す
換気扇・エアコン吹出口から1500mm以上離す

※ 全室LED照明とする。

※ 標準天井高さ2,400

※ 特記無きガラスは型ガラス

* 凡例

- 管柱 (105×105)
- Kダクト (3.30倍 FRM-0641)
- 片筋違い (2.00倍 45×90)
(例 左:柱脚 右:柱頭)
- たすき掛筋違い (4.00倍 45×90)
- 構造用合板 (2.70倍)
(t=9 9材 EXハイバ)
- 床点検口
- 天井点検口
- 換気扇
- 熱交換換気扇VLR-70

アドバンスシリーズ		
スマートデザイン (外部)		
凡例		
①	1	コンセント 1ヶ所
②	2	コンセント 2ヶ所
③	3	コンセント 3ヶ所
①ET	1 ET	コンセント1ヶ所接地ターミナル付
②ET	2 ET	コンセント2ヶ所接地ターミナル付
WP		コンセント 防水型
		エアコン用コンセント
		200V用コンセント
WP		防雨入線プレート
		スイッチ
●	3	3路スイッチ
●	4	4路スイッチ
⊗		直結電源
TV		テレビ取出口
TEL		電話取出口 (テレホンガイド)
LAN		LAN取出口 (テレホンガイド)
		壁照明
		リモコン (給湯関係・ルフロ)
		メーター
		分電盤
		チャイム

※ACコンセント天井付け
※TVアンテナ工事
※スイッチはFL+1100、コンセントはFL+200