



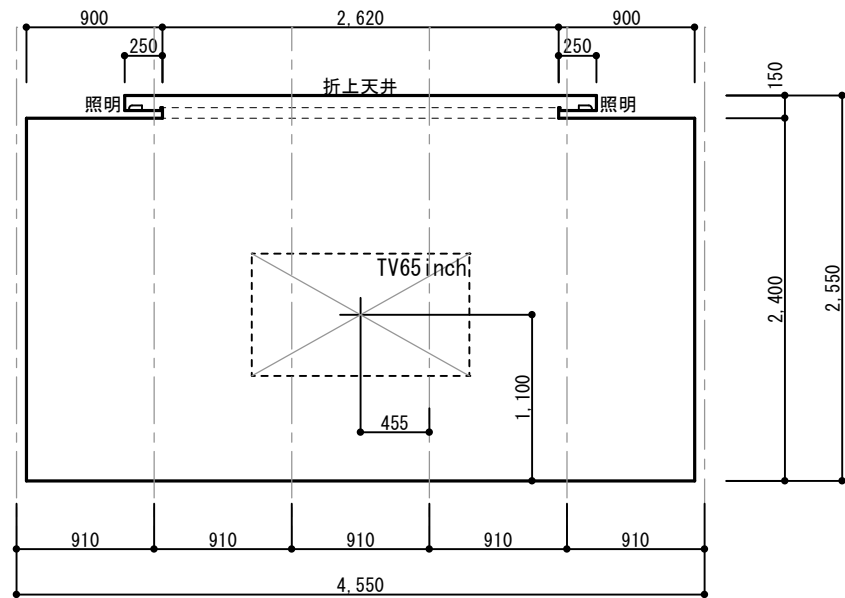


LDK① 西面

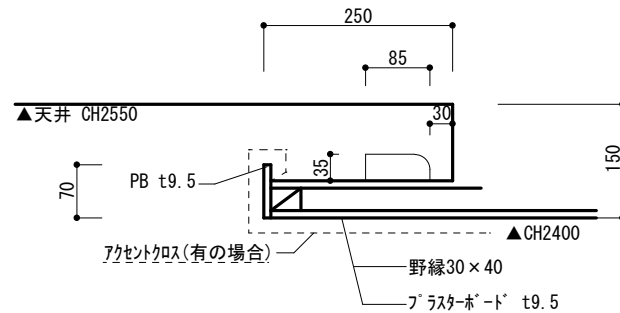


照明器具：まくちゃん (DAIKO)


LDK 折上天井 間接照明

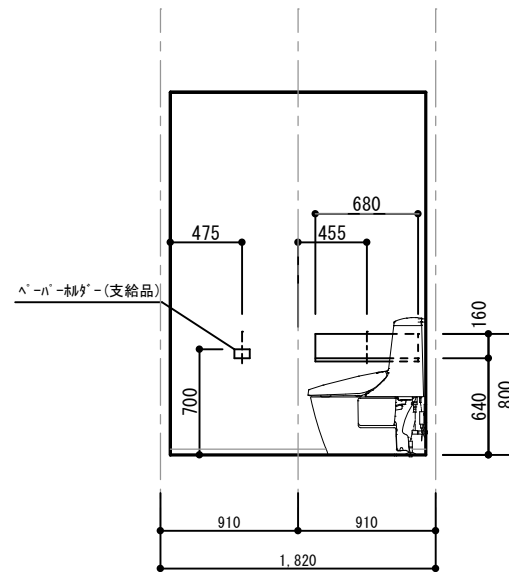


WC① 南面

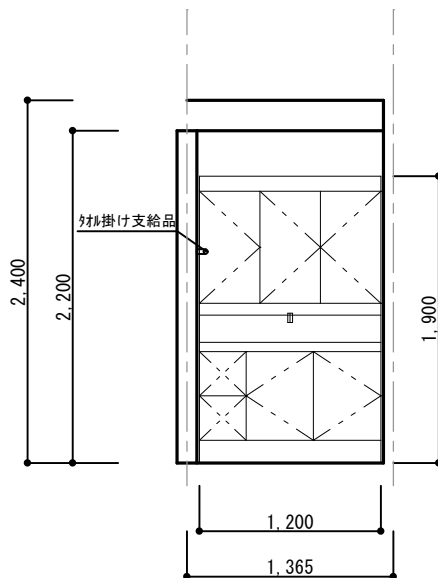

洗面 北面

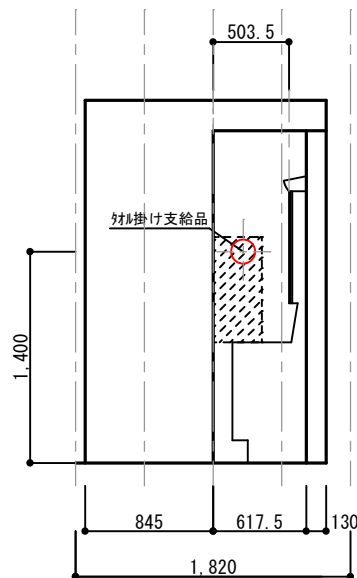

洗面 西面

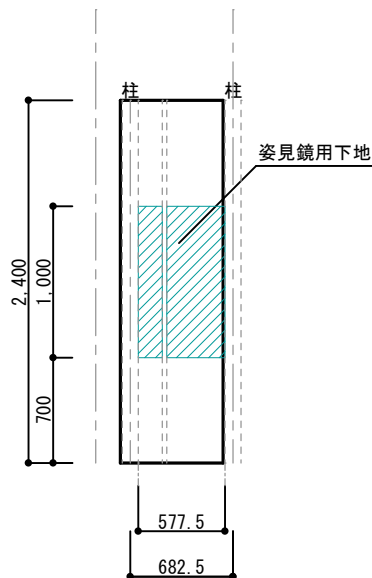

SC 西面

決定図

訂正	浜岡一級総合設計事務所	LIFEFUND PG HOUSE	株式会社 LIFEFUND InDesign office 一級建築士事務所 事務所登録 (2) 第7595号 一級建築士登録 第179770号 鈴木 達男 〒432-8023 静岡県浜松市中央区鴨江3丁目70番23号	年月日 2025. 6. 13	件名 杉山翔海様・美雨様 邸新築工事		設計	IC	工事	図番
	一級建築士事務所 静岡県知事登録第 (10) 2441 号			縮尺 1/50	図名 展開図-1		酒井		青島	6-1
	一級建築士 大臣登録第 365879 号 西原利昌									