
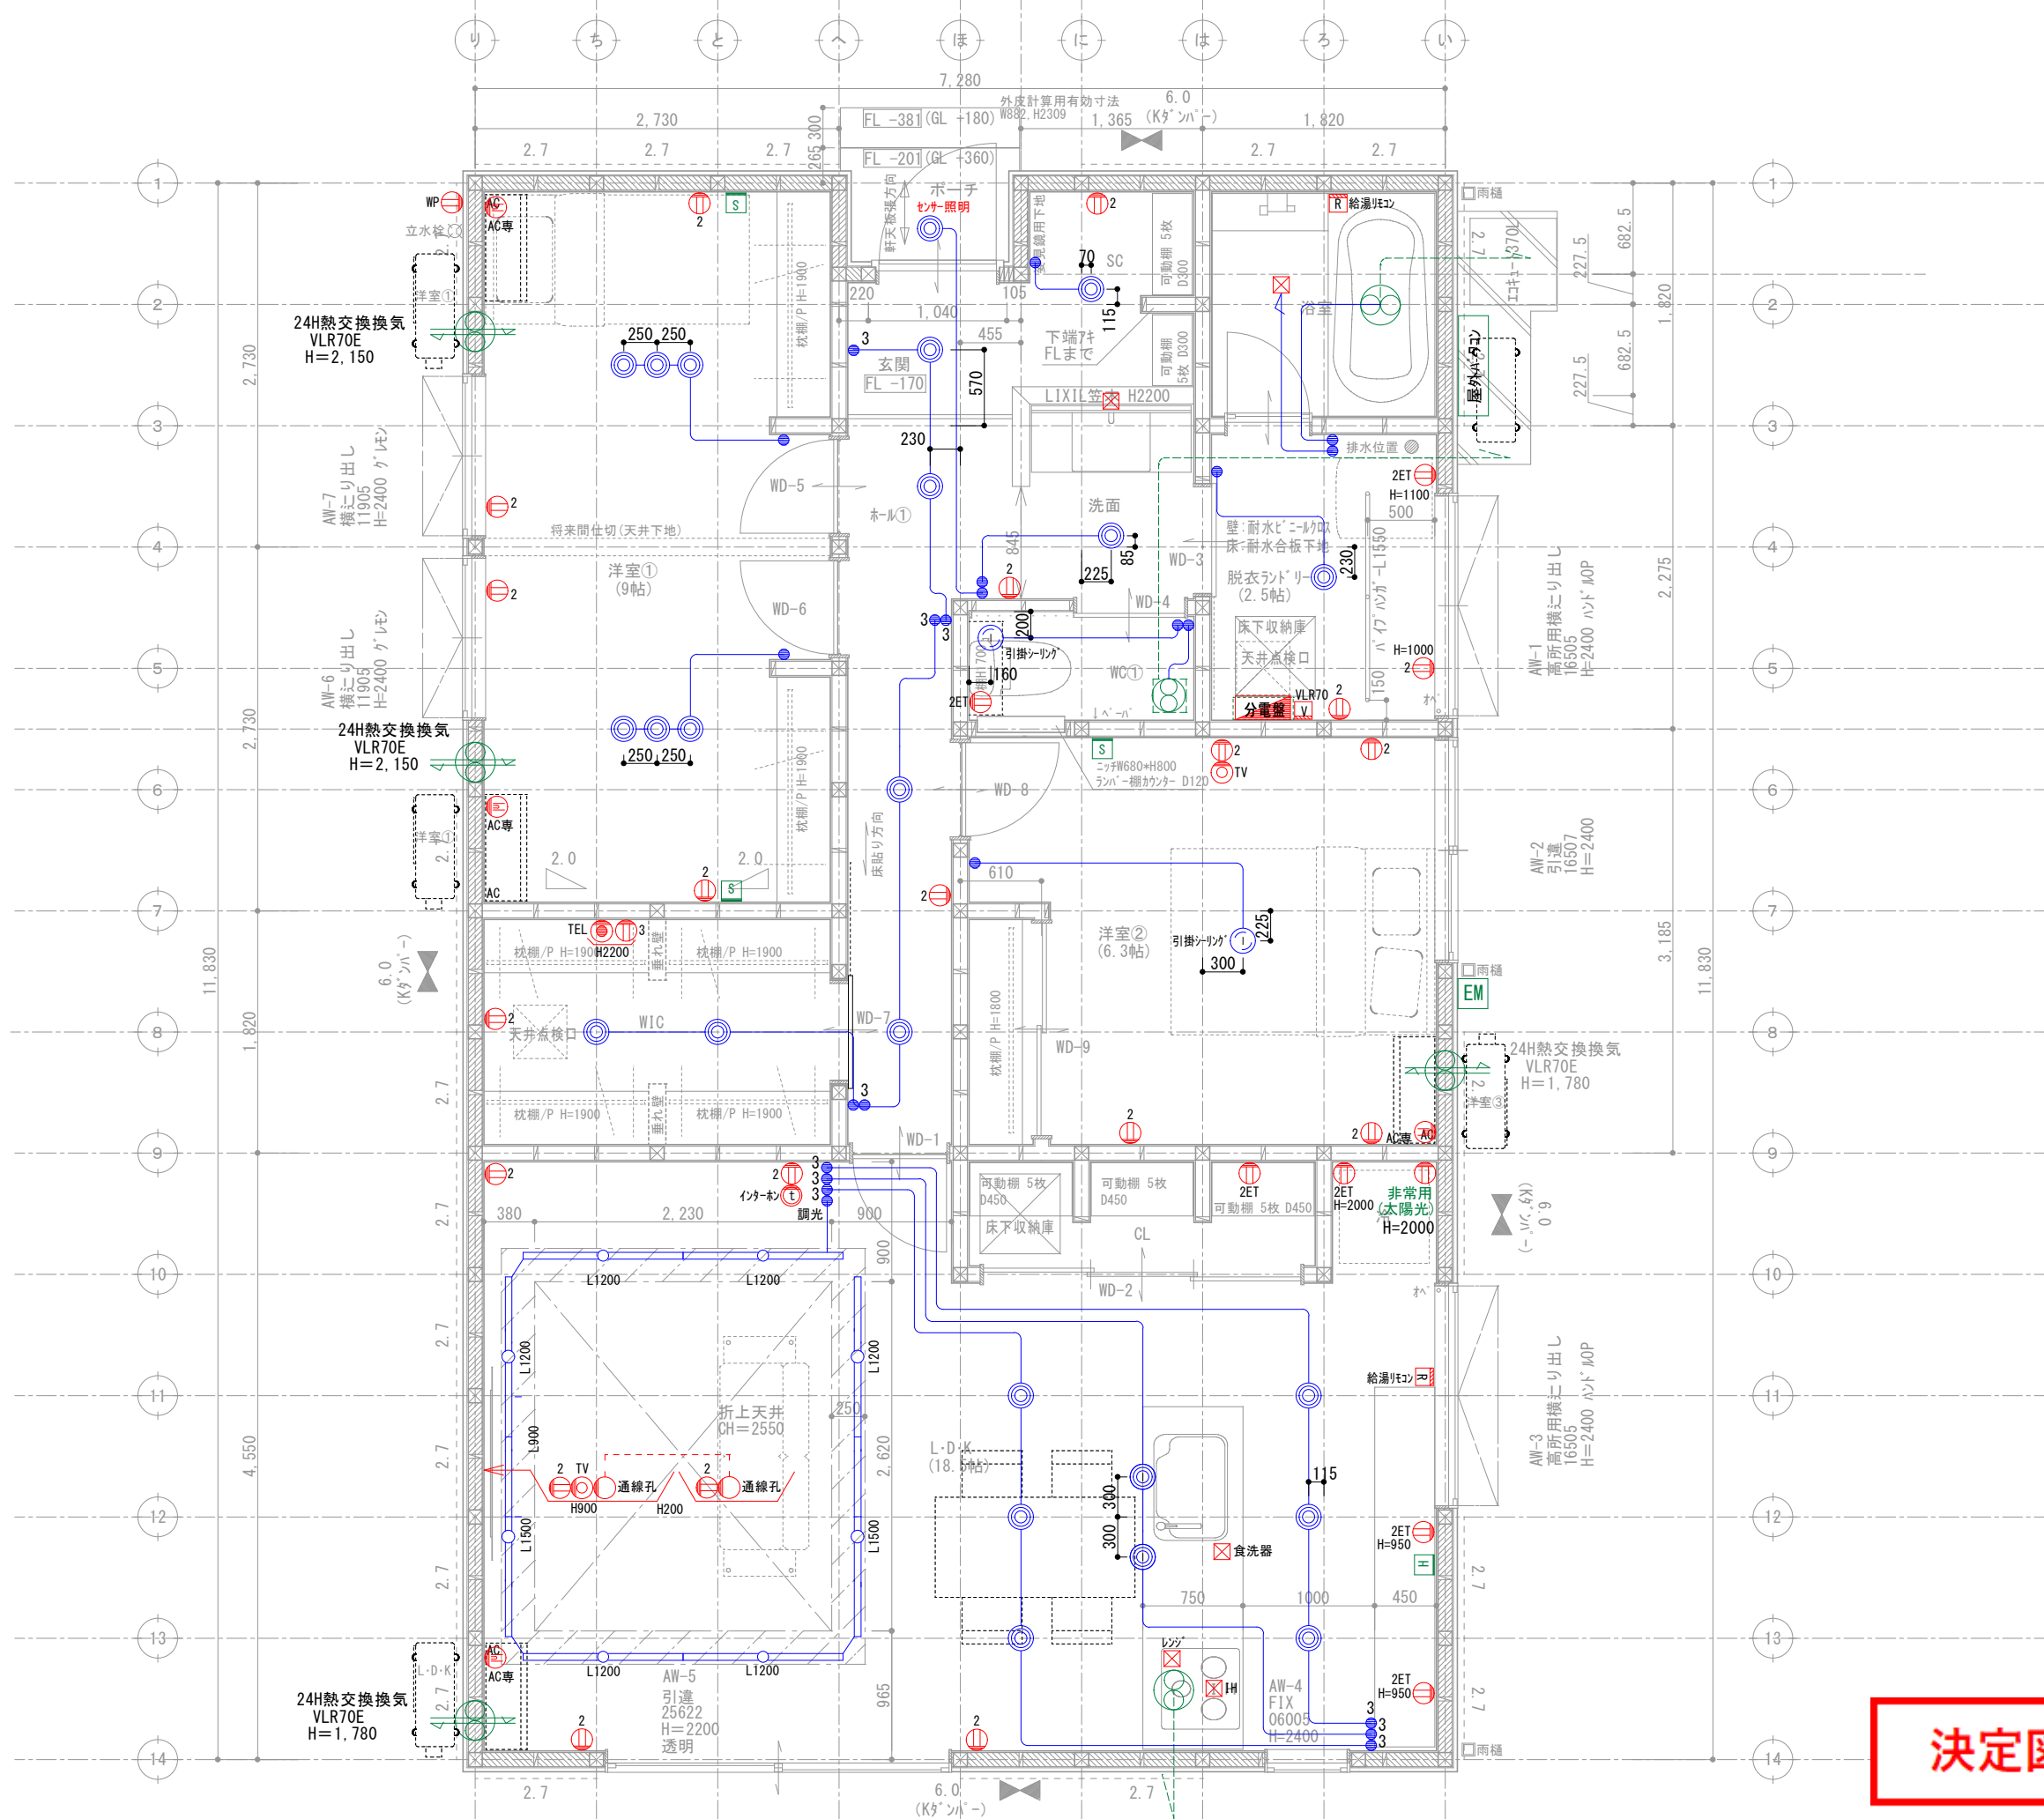


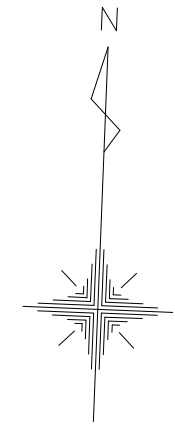

| 壁付け 住宅用火災報知器 |      |          | 数量 |
|--------------|------|----------|----|
| H<br>熱感知     | 熱感知器 | 電池式(単独型) | 1  |
|              |      | 露出型      |    |
| 壁付け 住宅用火災報知器 |      |          | 数量 |
| S<br>煙感知     | 煙感知器 | 電池式(単独型) |    |
|              |      | 露出型      |    |

※ 煙感知器は壁・梁より600mm以上離す  
壁に取付ける場合、  
天井から150mm以上500mm以内離す  
換気扇・エアコン吹出口から1500mm以上離す

※ 全室LED照明とする。

※ 標準天井高さ2,400

※ 特記無きガラスは型ガラス

**\* 凡例**

管柱 (105×105)

Kタンパー (3.30倍 FRM-0641)

片筋違い (2.00倍 45×90)  
(例 左:柱脚 右:柱頭)

たすき掛筋違い (4.00倍 45×90)

構造用合板 (2.70倍)  
(t=9 3枚-EXハイパー)

床点検口

天井点検口

換気扇

熱交換換気扇VLR-70

| アドバンスシリーズ     |                  |       |     |
|---------------|------------------|-------|-----|
| スマートデザイン (外部) |                  |       |     |
| 凡例            | 1                | コンセント | 1ヶロ |
| 2             | コンセント            | 2ヶロ   |     |
| 3             | コンセント            | 3ヶロ   |     |
| 1ET           | コンセント1ヶロ接地ターミナル付 |       |     |
| 2ET           | コンセント2ヶロ接地ターミナル付 |       |     |
| WP            | コンセント 防水型        |       |     |
| EA            | エアコン用コンセント       |       |     |
| 200V          | 200V用コンセント       |       |     |
| WP            | 防雨入線プレート         |       |     |
| スイッチ          |                  |       |     |
| 3             | 3路スイッチ           |       |     |
| 4             | 4路スイッチ           |       |     |
| 直結電源          |                  |       |     |
| TV            | テレビ取出口           |       |     |
| TEL           | 電話取出口 (テレホンガイド)  |       |     |
| LAN           | LAN取出口 (テレホンガイド) |       |     |
| 壁照明           |                  |       |     |
| リモコン          | リモコン(給湯関係・ルフロ)   |       |     |
| メーター          |                  |       |     |
| 分電盤           |                  |       |     |
| チャーム          |                  |       |     |

※ACコンセント天井付け  
※TVアンテナ工事  
※スイッチはFL+1100、コンセントはFL+200

決定図