


決定図

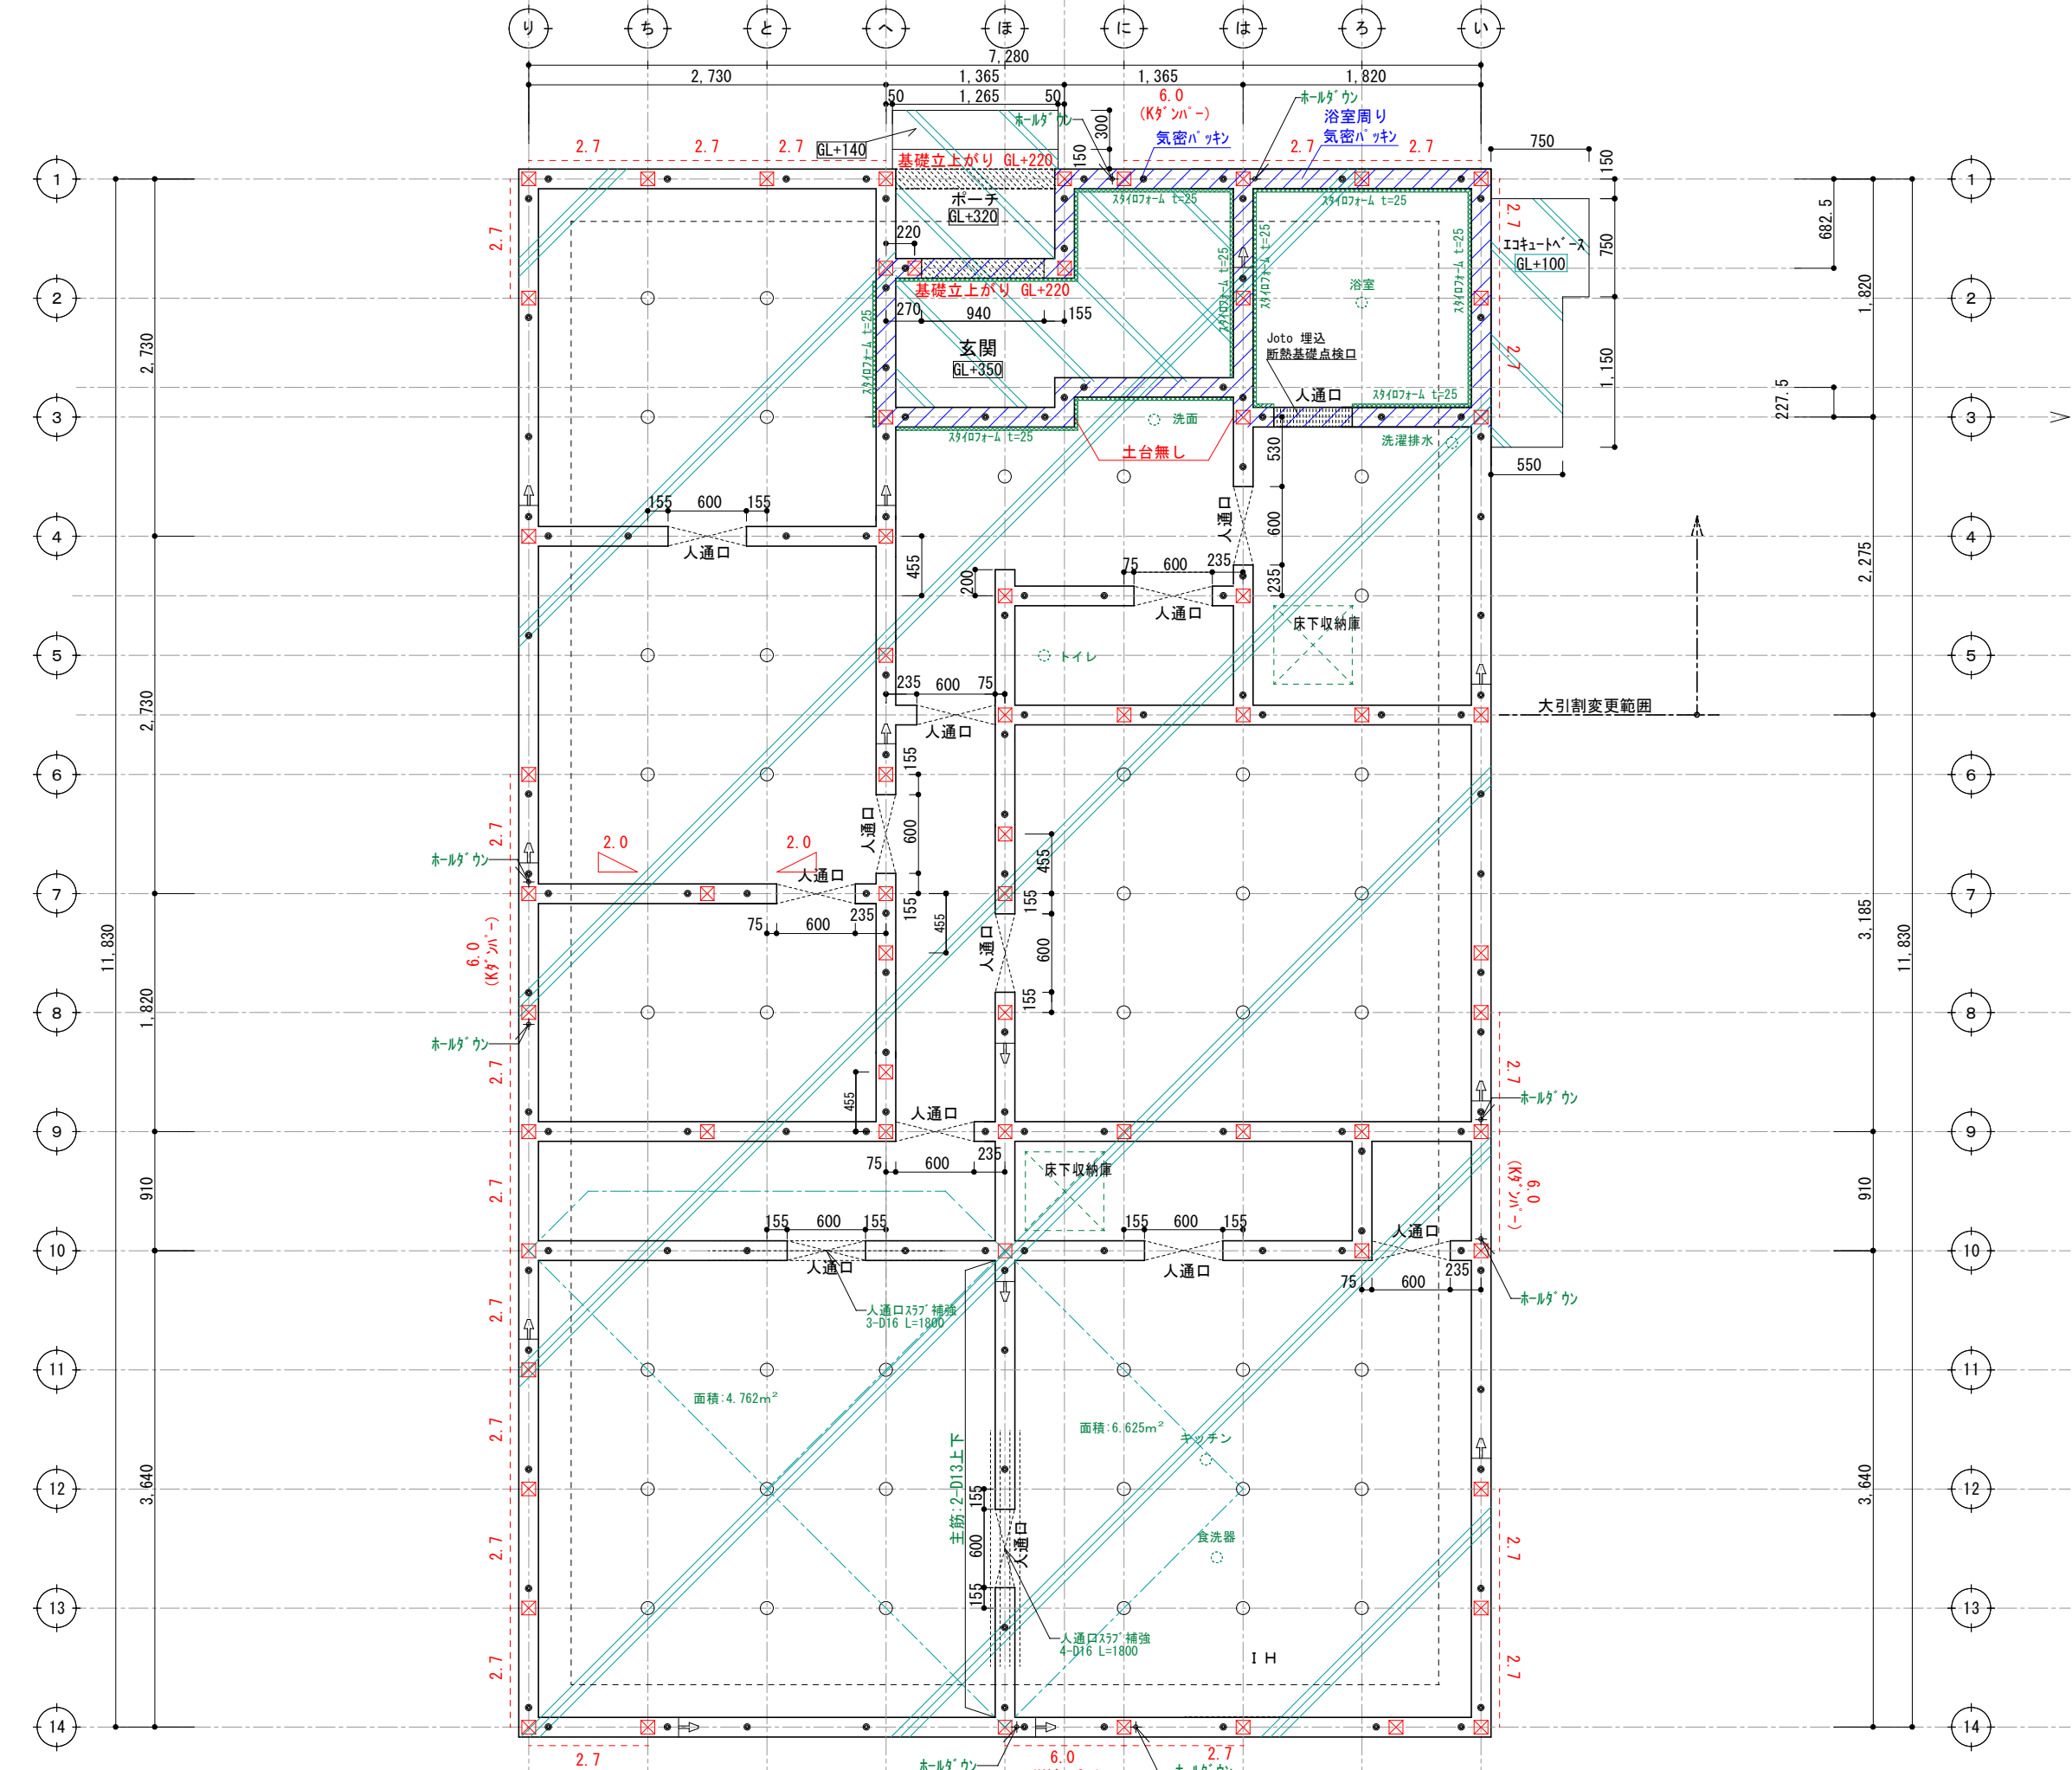

構造体ベースコンクリート t=150




後打ち土間コン



- アンカーボルトの配置
- 土台切れの箇所より150mm
 - 土台の継手及び仕口の端部より150mm
 - 耐力壁の端部、筋交いの脚部より150mm
 - 1.82m以下の間隔
 - 250mm以上埋込み
 - 基礎天端より120mm

- 筋かい凡例
- 柱脚 柱頭 片筋かい
 - たすき掛け筋かい
 - 構造用パネル

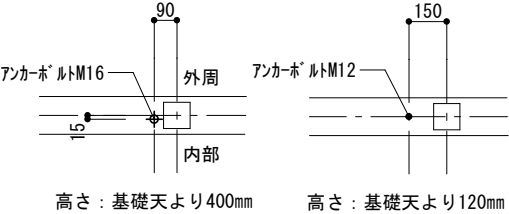

ホールダウン用アンカーボルト配置 アンカーボルト配置

- 凡例
- 通し柱 (105*105) 管柱 (105*105)
 - アンカーボルトM12 L=400
 - + ホールダウンアンカーM16 L=800
 - 柱芯より90mm 280mm以上埋め込み (カナダフィストアンカーボルトM16)
 - ⊕ 鋼製束
 - 土台ジョイント
 - ベースコンクリート (t=150)
 - 後打ちコンクリート

- 基礎伏図について特記なき場合に限り下記による。
- コンクリート：呼び強度 21N/mm2
 - 鉄筋：SD295A
 - 設計地耐力： $f_e=20\text{kN/m}^2$
地耐力計測後、不足の場合は相当の改良を行い、満たすものとする。
 - 基礎の位置は、芯振分けとする。
 - 玄関・S/C・UB周囲の基礎天端は気密パッキン施工（網掛け部）とし、その他の基礎天端は基礎パッキン施工とする。
 - 設備配管の屋内への取り入れは基礎立上り部のスリーブによる。