


■ 仕 様		■ HEAT20 G1
断熱工事	■ 床:カネライトフォーム t65 ■ 壁:アクアフォームLITE吹付 t85	■ 土間床等の外周:スタイロフォームAT t25 ■ 天井:アクファフォームLITE吹付 t170
床下換気	■ 基礎パッキン JOTO (玄関・UB周り:気密基礎パッキン)	
防虫防蟻	■ 土壌処理・木部 ガントナーMC	

■ 外 部 仕 上 表			■ 22条地域
部位		仕上・仕様・メーカー	色番・品番
屋根		■ ガルバリウム鋼板 (t0.35) UK立平 ニスカカラーPro GH 軒先通気金物 日本住環境株式会社【REV-15】	GHK01 Sブラック
パラペット笠木		■ なし	
破風・鼻隠		■ なし	
雨樋 (軒樋)		■ Panasonic サーフェスケアFS-I型	ブラック
(縦樋)		■ Panasonic S30角樋	ブラック
軒天	屋根軒	■	
	ポーチ軒	■ 神島化学 t= 6mm 軒天ボード エンボス	Wファインステン
	バルコニー軒	■	
オーバーハング水切り		■ ガルバリウム鋼板 ※外壁合わせ JOTO:HF-A3550	ブラック
外壁 通気金物(15mm) ※下地面材:タイガーEXハイパー 防火認定 PC030BE-4028	■メイン	ニチハ エモンエクセラード [®] 16 Vシリーズ しぶきV	シェルトグレー
	■アクセントA	なし	
	■アクセントB	なし	
玄関ポーチ		■ 床 玄関に同じ	-
基礎		■ 立上り巾木: モルタル刷毛引き	-
基礎水切り金物		■ JOTO鋼板製 防鼠材付き水切り JOTO:WMF-N35	ブラック
バルコニー	床・内壁	■ なし	-
	笠木	■ なし	
外部建具		■ LIXIL EW(アルゴン [®] ガス高遮熱仕様LowE複層ガラスグリーン) ・SD、TSは、メーカー設定によるが、オペレーターハンドル優先とする ・オペレーター付サッシの場合は固定網戸とする ・グレモンハンドル式サッシの場合は可動網戸とする	外観 ブラック 内観 ホワイト ※樹脂パッキン・網戸付
シャッター		■ なし	
軒天通気金物			
玄関扉		■ LIXIL ジェスタ2 K2仕様 LIXILファミロック タグキー×3 (電池式)	ドア型: M17 型 ドア色: マットブラック ハンドル: S型ハンドル 色: ブラック
外部物干し金物		■	
換気フード		■ 局所換気扇(トイレ 浴室 キッチンフード) 防火ダンパー無 ■ ダクトレス熱交換換気システム (日本スティーベル株式会社) VLR-70E 防火ダンパー無	外気フード: ブラック 外気フード: B ブラック 室内パネル ホワイト

■ 構 造 概 要				
基礎	■ RCベタ基礎コンクリート			
通し柱・管柱	■ 構造用集成材 105×105		間柱	■ 集成材
土台	■ 桧 105×105	大引き ■ 桧 90×90	筋交い	■ 構造用製材 火打梁 ■ 鋼製火打(当社基準により米松あり)
桁・梁	■ 構造用製材及び集成材		制震装置	■ Kダンパー (株)アイ・エム・エー


■ 設 備 装 着 品				
住宅設備	部位	メーカー	商品名 ※ 詳細は見積り、プレゼン参照	見積りNo. (日付)
	キッチン	LIXIL	■ ES I 型 扉 グレー ジュスタック 天板 ルティホワイト キッチンパネル: フレッシュホワイト 見積り番号 : M25026565124-007-2 標準食洗器 標準IH, 壁付レンジフードHVR(シルバー) スリム取手シルバー (日付) 2025.5.16	
	バックカウンタ ※オプション	LIXIL	■ L2700 下台のみ 見積り番号 : M25026565124-007-3 (日付) 2025.5.16	
	浴室	LIXIL	■ AX1616 PGハウス標準仕様 見積り番号 : M25026565124-007-1 アクセント壁: シルバーグレー 浴槽: ミナモ ホワイト 床: グレー マグネットシェフ: ホワイト (日付) 2025.5.16	
	1Fトイレ	LIXIL	■ ペーシアシャワートイレ 白 ● タオル掛け: 見積り番号 : M25026565124-007-5 タンク手洗 無し ● 紙巻き器: なし(支給品取付) (日付) 2025.5.16	
	洗面台	LIXIL	■ EV W1200(D500タイプ) 扉: 見積り番号 : M25026565124-007-4 [引出しタイプ シングルハンドシャワー スタンダードLED三面鏡 (日付) 2025.5.16 その他 ● タオル掛け: なし(支給品取付)	
給排水設備	給湯器		■ エコキュート370L Panasonic Sシリーズ スタンダードモデル 追い焚きフルオート	
	排水		■ 下水	
	外水栓		■ 1 カ所 (平面図参照) ■ 外部立栓柱: PVC製 水栓柱12型【前澤化成工業】	
	外部ガーデンパン		■ 無し	
	その他		■ 洗濯機用単水栓: 緊急止水弁付 ■ 洗濯機用排水: トラップ金物(標準) ■ 排水さや管(長期優良住宅仕様)	
ガス配管設備			■ なし (配置図・平面図参照) ■ ガス使用器具	
電気設備	インターホン		■ パナソニック VL-SZ30KL	
	TVアンテナ		■ UHF + BS・110度CS/CSアンテナ [2K・4K・8K対応] ■ ブラック ※電波状況によりホワイトになる可能性あり	
	エアコン		■ 設置場所:	
	ソーラー ※標準搭載		■ あり(Qセルズ) 12 枚 5.28 KW Re.RISE-G3 440 (1722 × 1134 × 30) ※メーカーのモデルチェンジ等で後継品に変更される可能性あり ■ 屋外パワコン	
その他				

	浜岡一級総合設計事務所	 株式会社 LIFEFUND InDesign office 一級建築士事務所 事務所登録 (2) 第7595号 一級建築士登録 第179770号 鈴木 達男 〒432-8023 静岡県浜松市中央区鴨江3丁目70番23号	年 月 日 2025.6.13	件名 杉山翔海様美雨様 邸新築工事	設計 IC 工務 図 番	酒井 青島 1-1
	一級建築士事務所 静岡県知事登録第 (10)2441 号		縮尺	図面 仕上表 1		
	一級建築士 大臣登録第 365879 号 西原利昌					

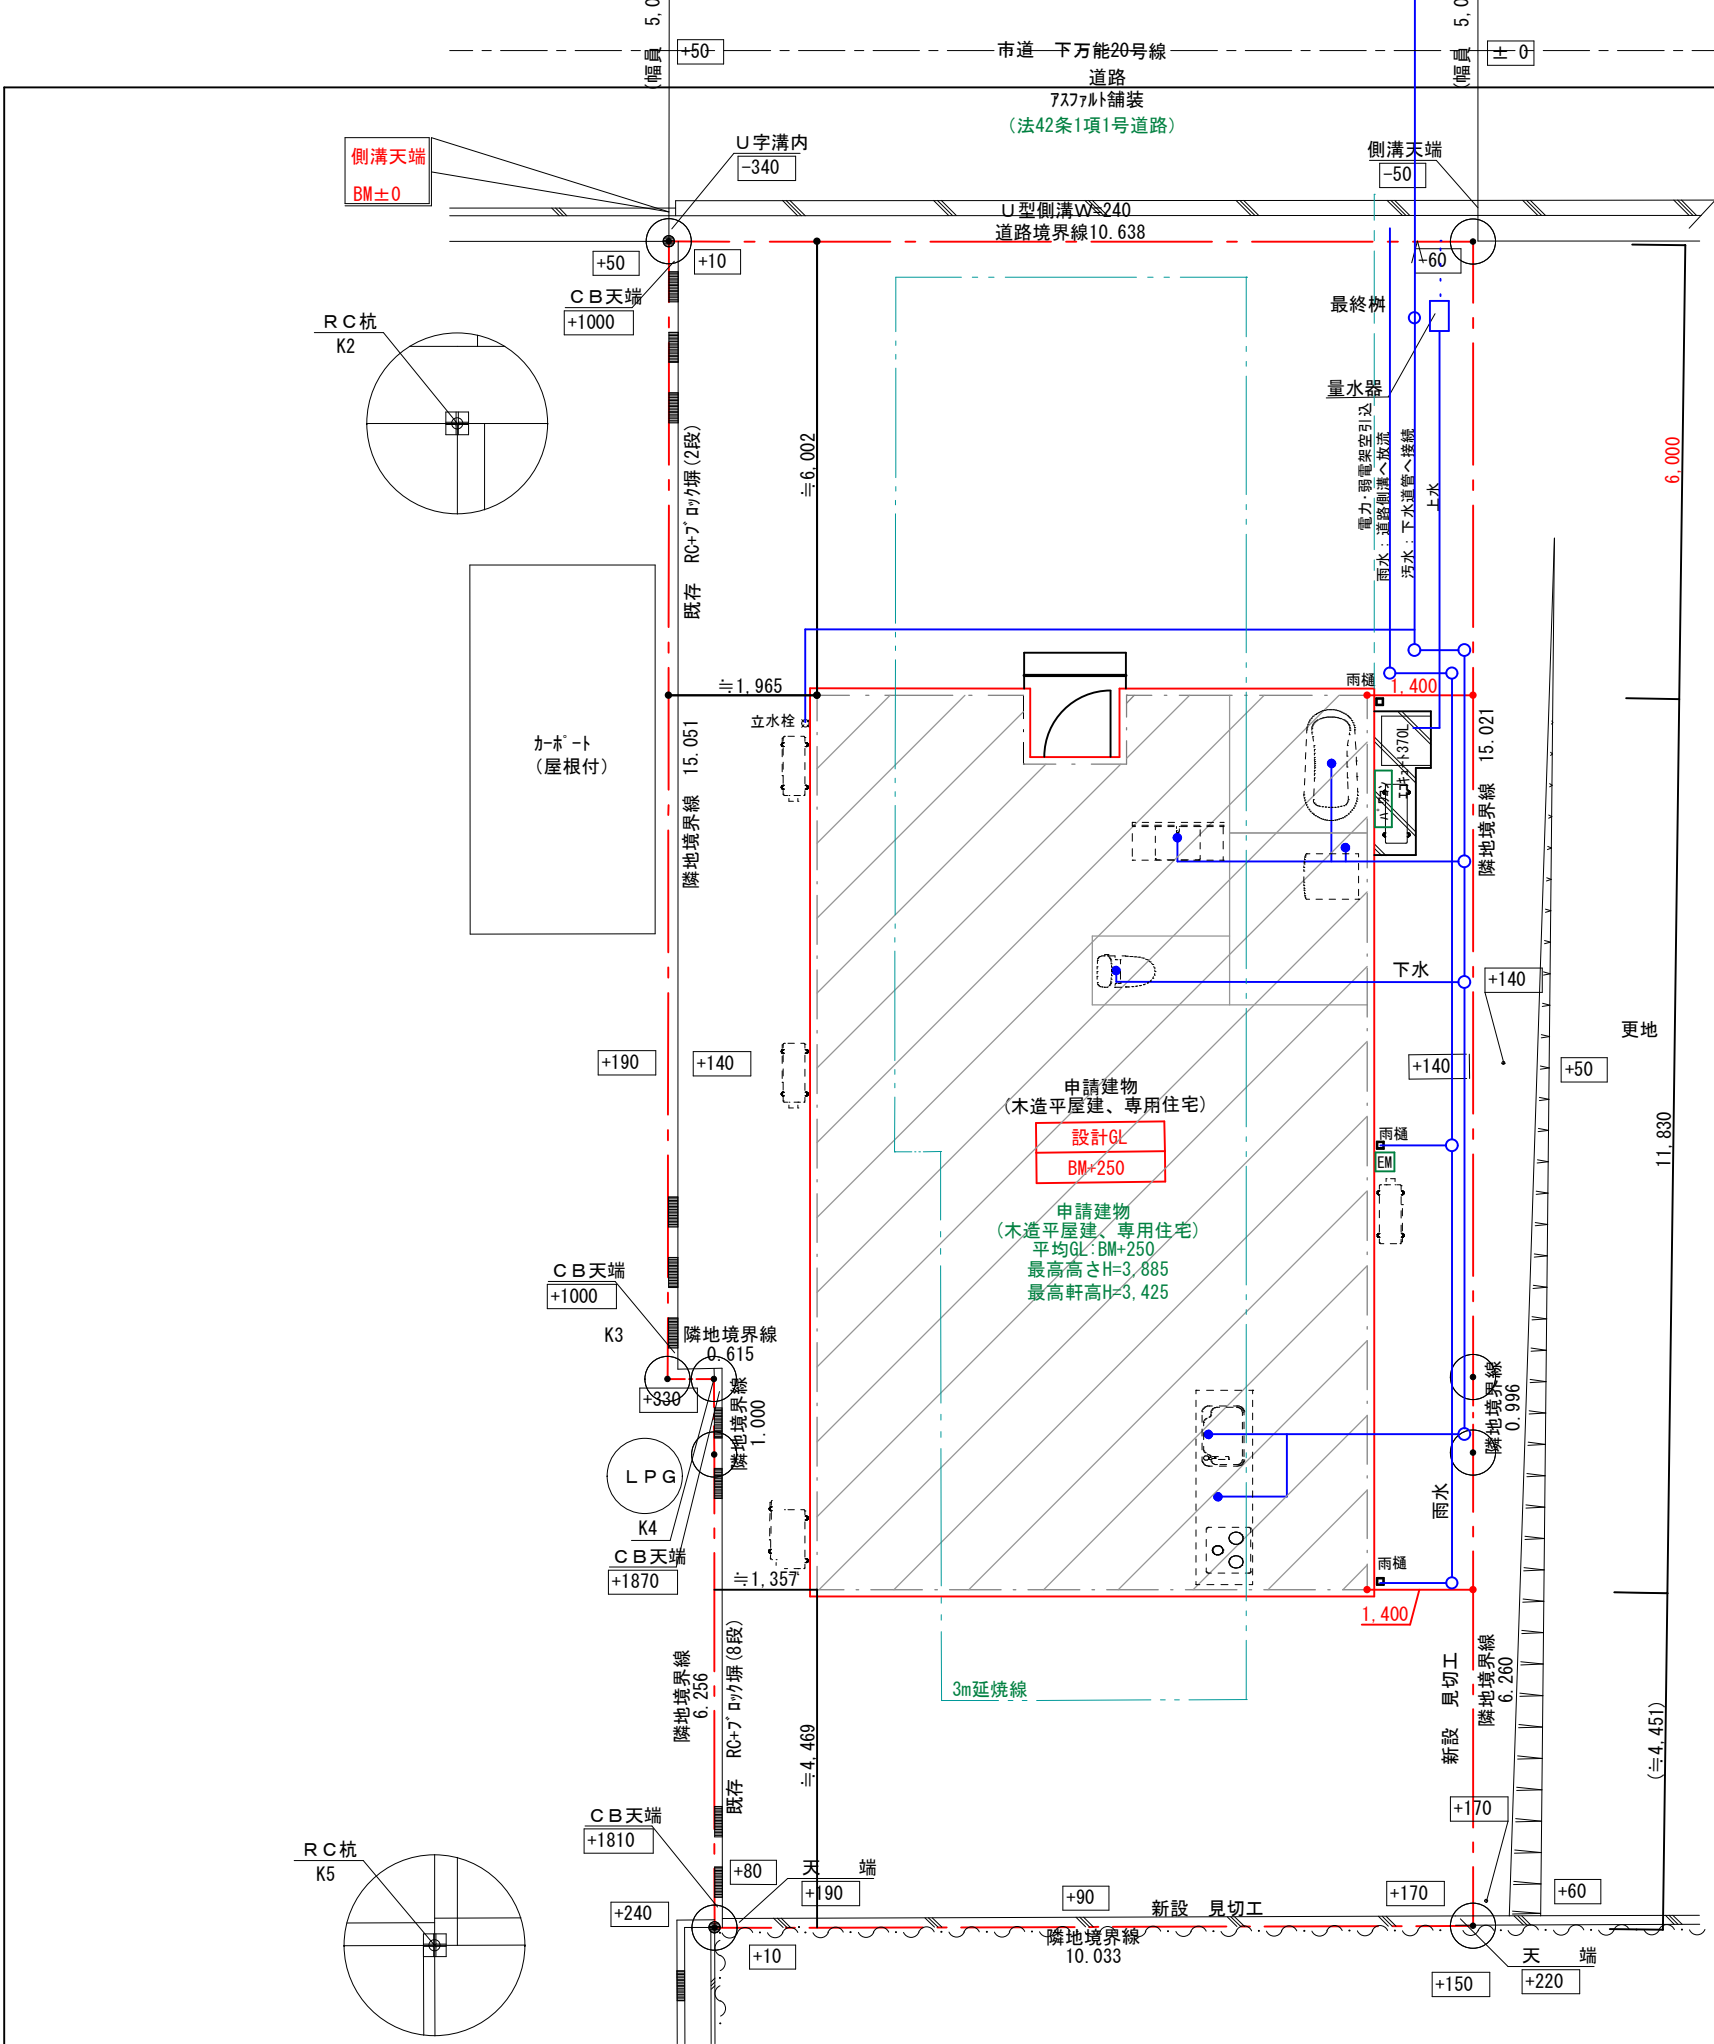

宅地造成等工事規制による盛土切土無し
道路斜線制限については、明らかに適合する。
北側斜線制限については、明らかに適合する。
平均地盤面について
申請建物の周囲の平均地盤面高さをBM+250とする。

トータル面積表 (㎡)	
敷地面積	232.90
建築面積	86.12
床面積 1階	85.19
延床面積	85.19
建築率	$(86.12/232.90) \times 100$ 36.98%
容積率	$(85.19/232.90) \times 100$ 36.58%

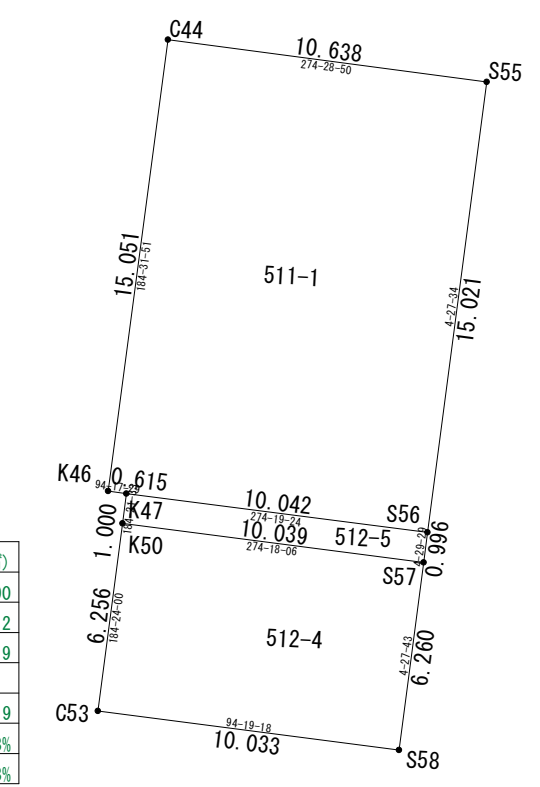

座 標 求 積 表


地 番	512-4			
測 点	Xn	Yn	(Xn+1 - Xn-1) Yn	距 離
K50	198.896	72.120	-395.578200	6.256
C53	192.658	71.640	-501.050160	10.033
S58	191.902	81.644	447.817340	6.260
S57	198.143	82.131	574.424214	10.039
		倍 面 積	125.613194	
		面 積	62.8065970	
		地 積	62.80 m ²	

地 番	512-5			
測 点	Xn	Yn	(Xn+1 - Xn-1) Yn	距 離
K47	199. 893	72. 196	-17. 327040	1. 000
K50	198. 896	72. 120	-126. 210000	10. 039
S57	198. 143	82. 131	19. 711440	0. 996
S56	199. 136	82. 209	143. 865750	10. 042
		倍 面 積	20. 040150	
		面 積	10. 0200750	
		地 積	10. 02 m ²	

地 番	511-1			
測 点	Xn	Yn	(Xn+1 - Xn-1)Yn	距 離
S55	214.112	83.377	1317.940239	10.638
C44	214.943	72.772	-1031.397556	15.051
K46	199.939	71.583	-1077.324150	0.615
K47	199.893	72.196	-57.973388	10.042
S56	199.136	82.209	1168.929771	15.021
		倍 面 積	320.174916	
		面 積	160.0874580	
		地 積	160.08 m ²	

敷地合計面積
62.80+10.02+160.08=232.90㎡

決定図

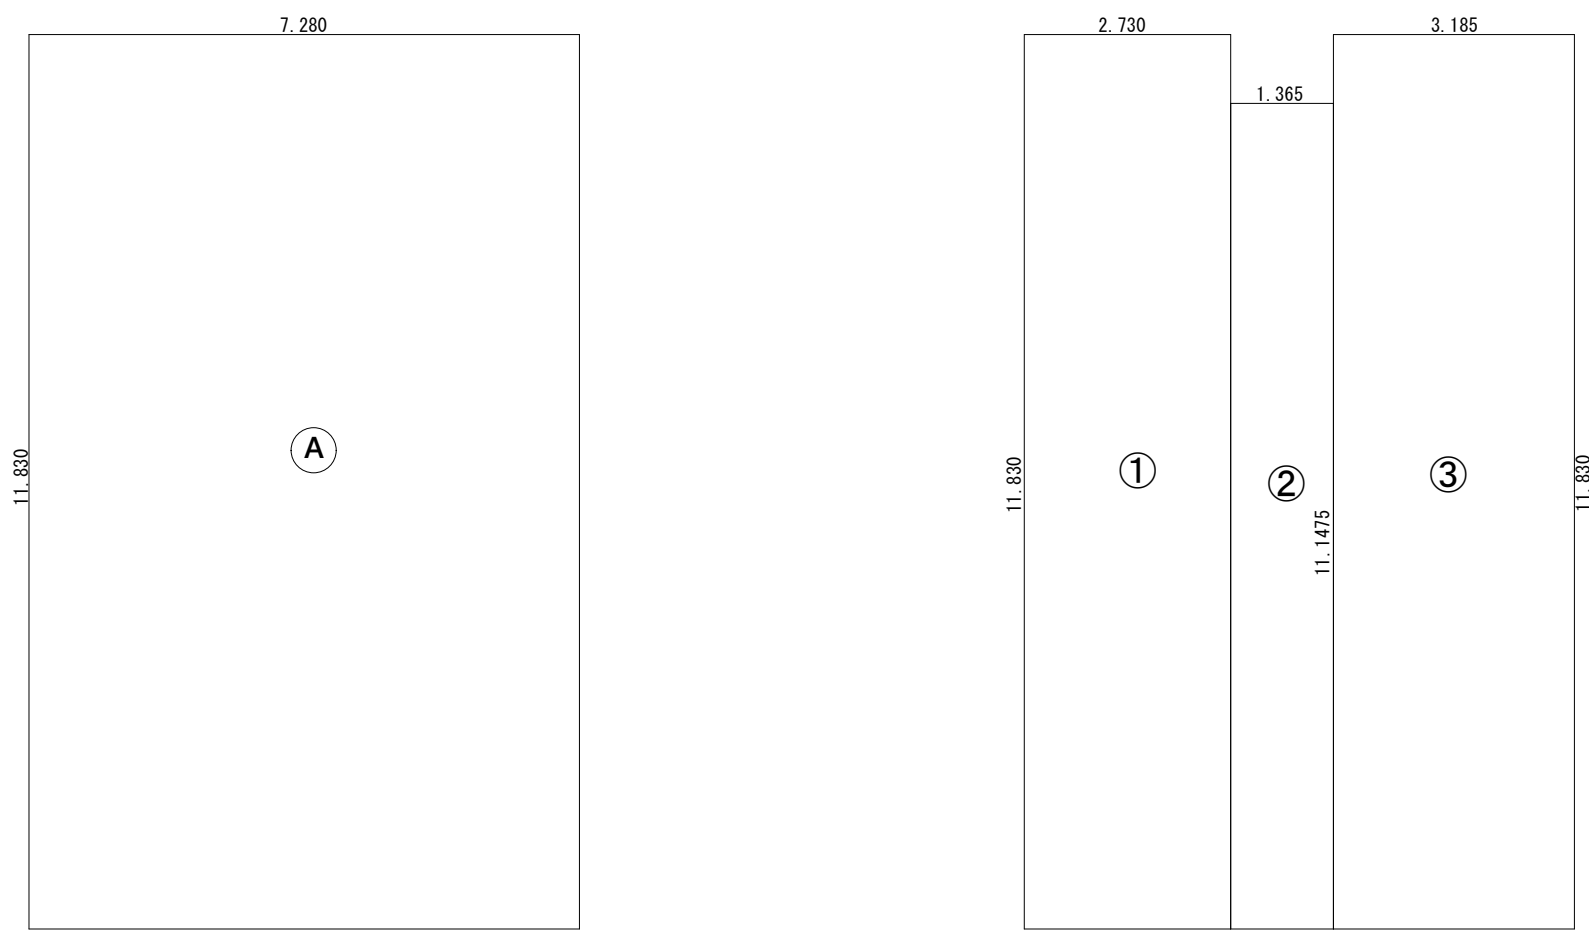

建築面積求積図 S=1/100

建築面積求積表

番号	計算式 (m)	面積 (㎡)
Ⓐ	7.280 × 11.830	86.1224
合計		86.1224 86.12 (26.0坪)

1階床面積図 S=1/100



1階床面積求積表

番号	計算式 (m)	面積 (㎡)
①	2.730 × 11.830	32.2959
②	1.365 × 11.1475	15.2163
③	3.185 × 11.830	37.6786
合計		85.1908 85.19 (25.7坪)

延べ床面積表

	番号 (m)	面積 (㎡)
1階床面積	① ② ③	85.19
合計		85.19 (25.7坪)

決定図

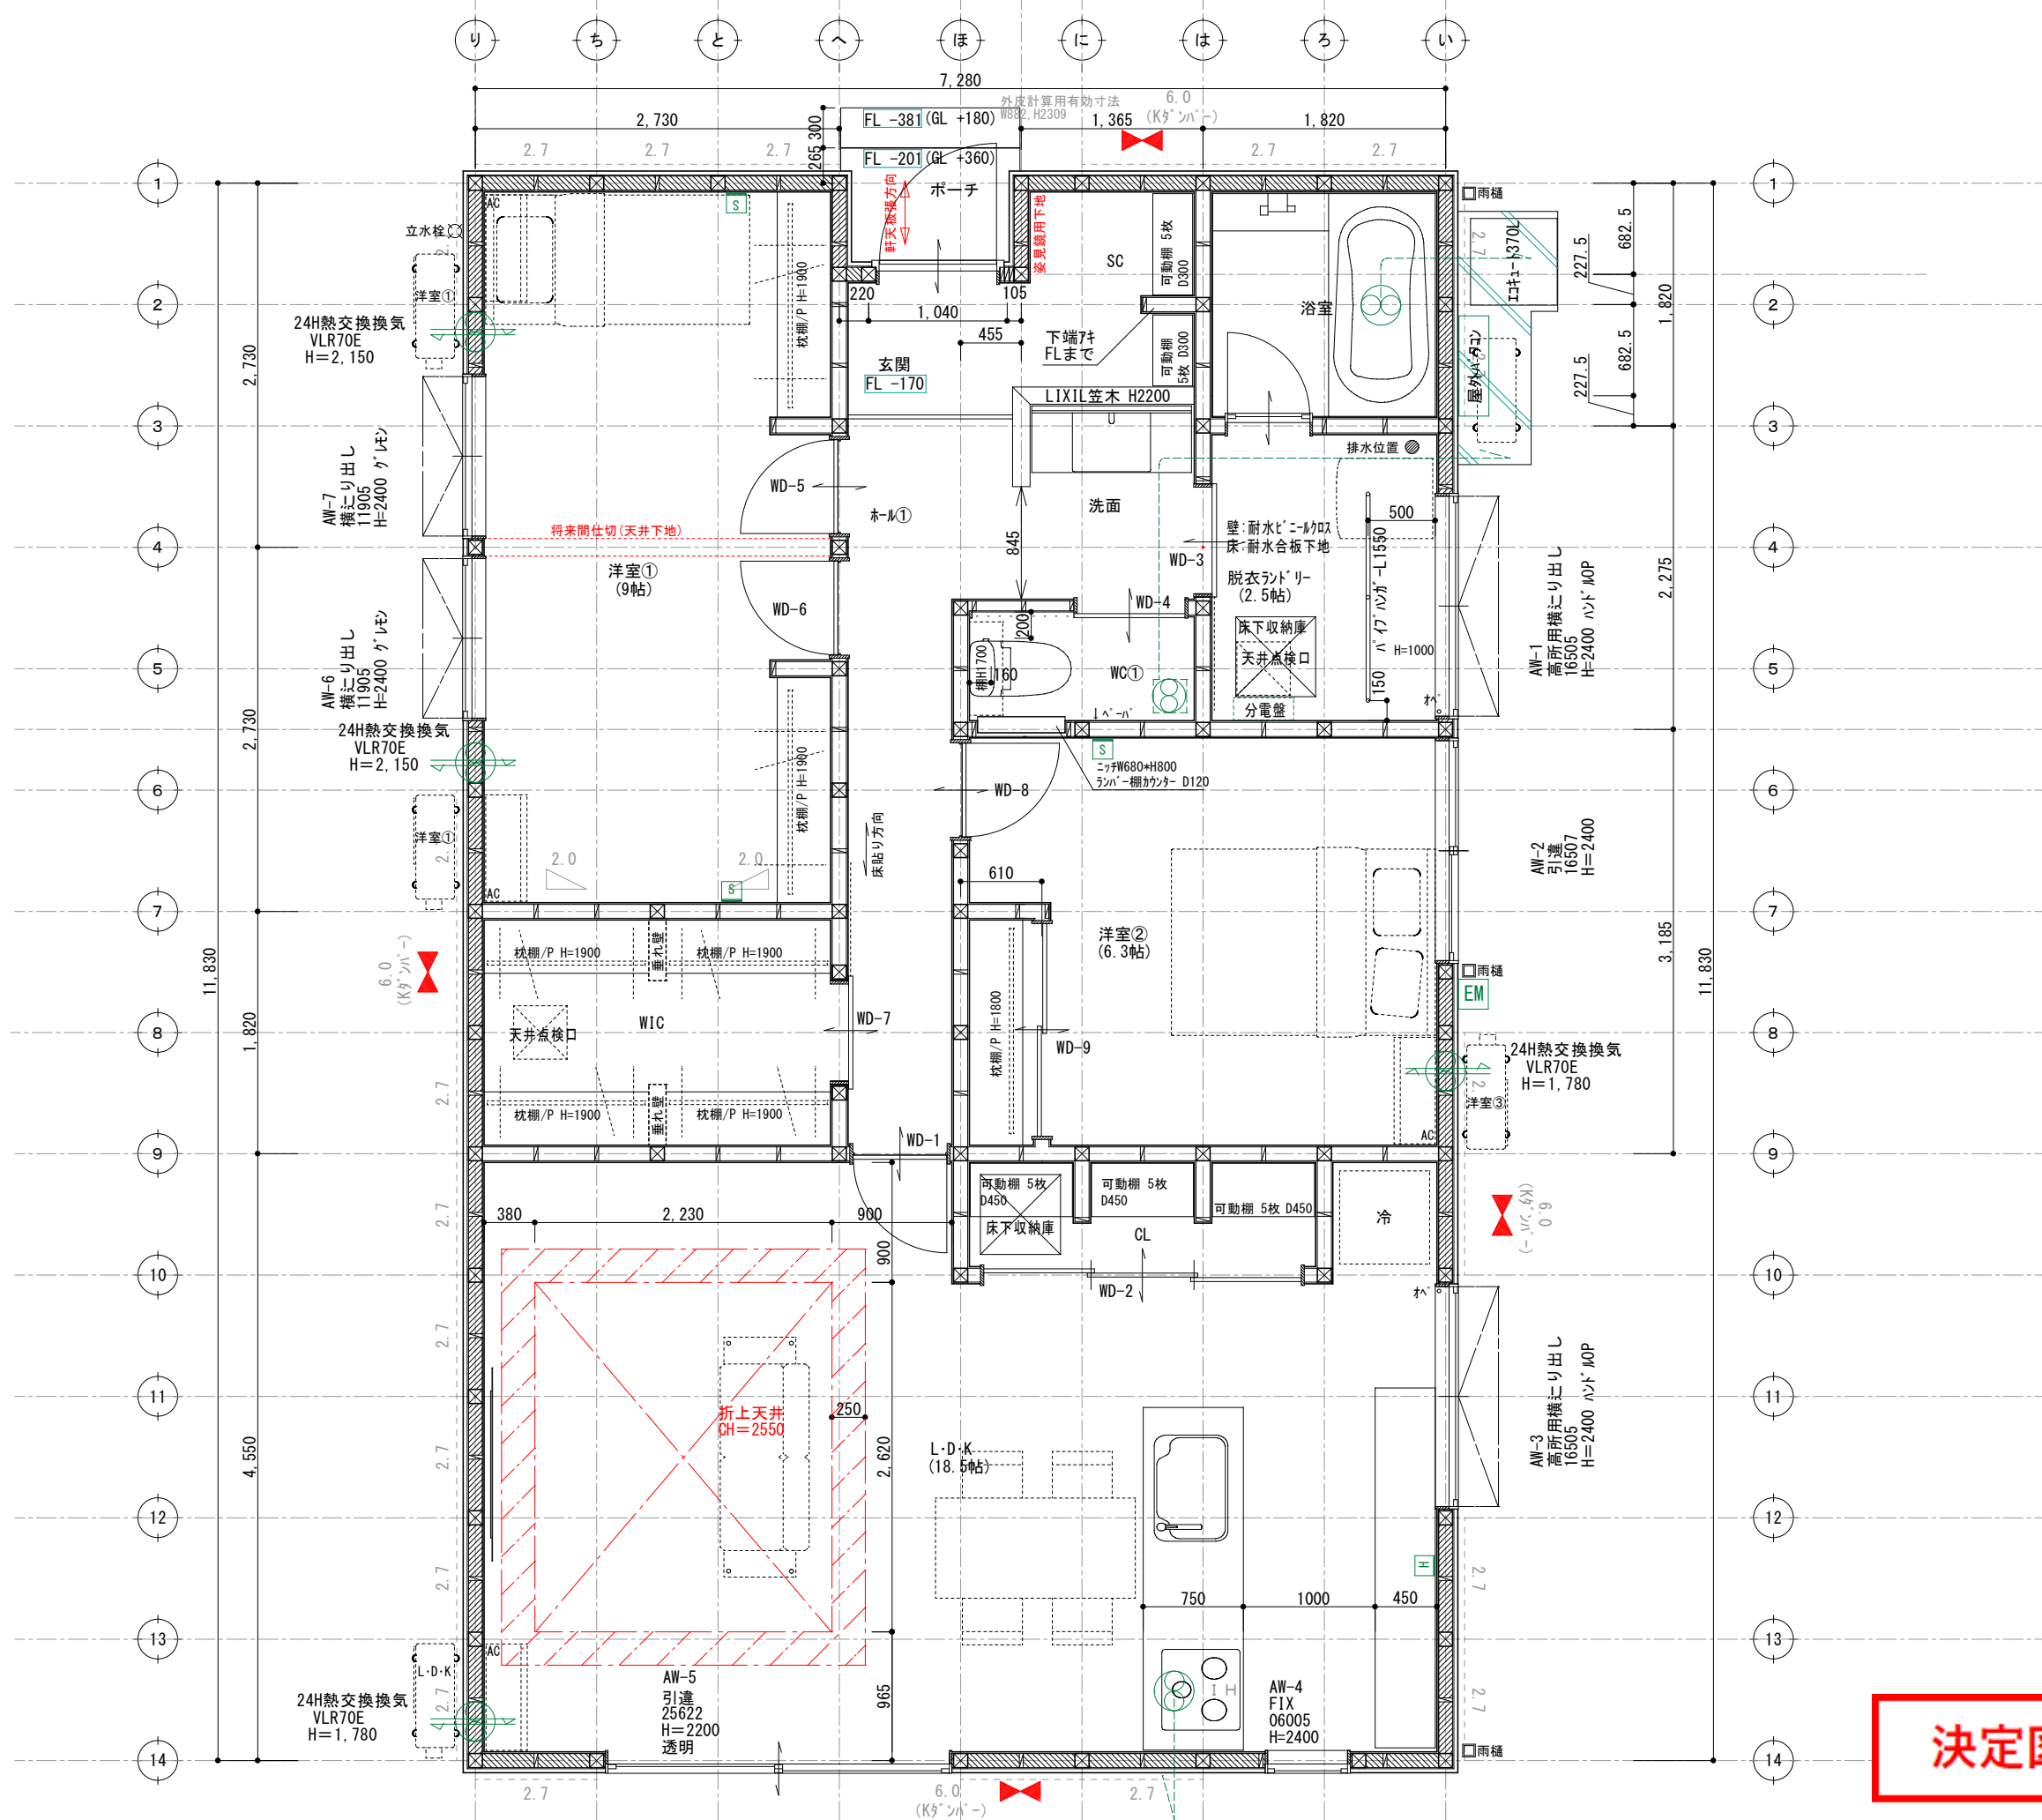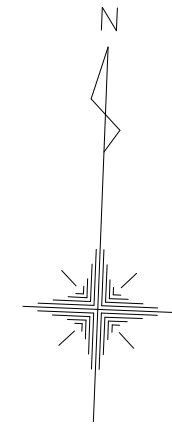

壁付け 住宅用火災報知器			数量
H 熱感知	熱感知器	電池式(単独型)	1
		露出型	

壁付け 住宅用火災報知器			数量
S 煙感知	煙感知器	電池式(単独型)	
		露出型	

※ 煙感知器は壁・梁より600mm以上離す
壁に取付ける場合、
天井から150mm以上500mm以内離す
換気扇・エアコン吹出口から1500mm以上離す

※ 全室LED照明とする。

※ 標準天井高さ2,400


※ 特記無きガラスは型ガラス

* 凡例


- 管柱 (105×105)
- Kダクト (3.30倍 FRM-0641)
- 片筋違い (2.00倍 45×90)
(例 左:柱脚 右:柱頭)
- たすき掛筋違い (4.00倍 45×90)
- 構造用合板 (2.70倍)
(t=9 9材 EXハイバ)
- 床点検口
- 天井点検口
- 換気扇
- 熱交換換気扇VLR-70

アドバンスシリーズ		
スマートデザイン (外部)		
凡例		
①	1	コンセント 1ヶ所
②	2	コンセント 2ヶ所
③	3	コンセント 3ヶ所
①ET	1 ET	コンセント1ヶ所接地ターミナル付
②ET	2 ET	コンセント2ヶ所接地ターミナル付
WP		コンセント 防水型
		エアコン用コンセント
		200V用コンセント
WP		防雨入線プレート
		スイッチ
●	3	3路スイッチ
●	4	4路スイッチ
⊗		直結電源
TV		テレビ取出口
TEL		電話取出口 (テレホンガイド)
LAN		LAN取出口 (テレホンガイド)
		壁照明
		リモコン (給湯関係・ルフロ)
		メーター
		分電盤
		チャイム

※ACコンセント天井付け
※TVアンテナ工事
※スイッチはFL+1100、コンセントはFL+200

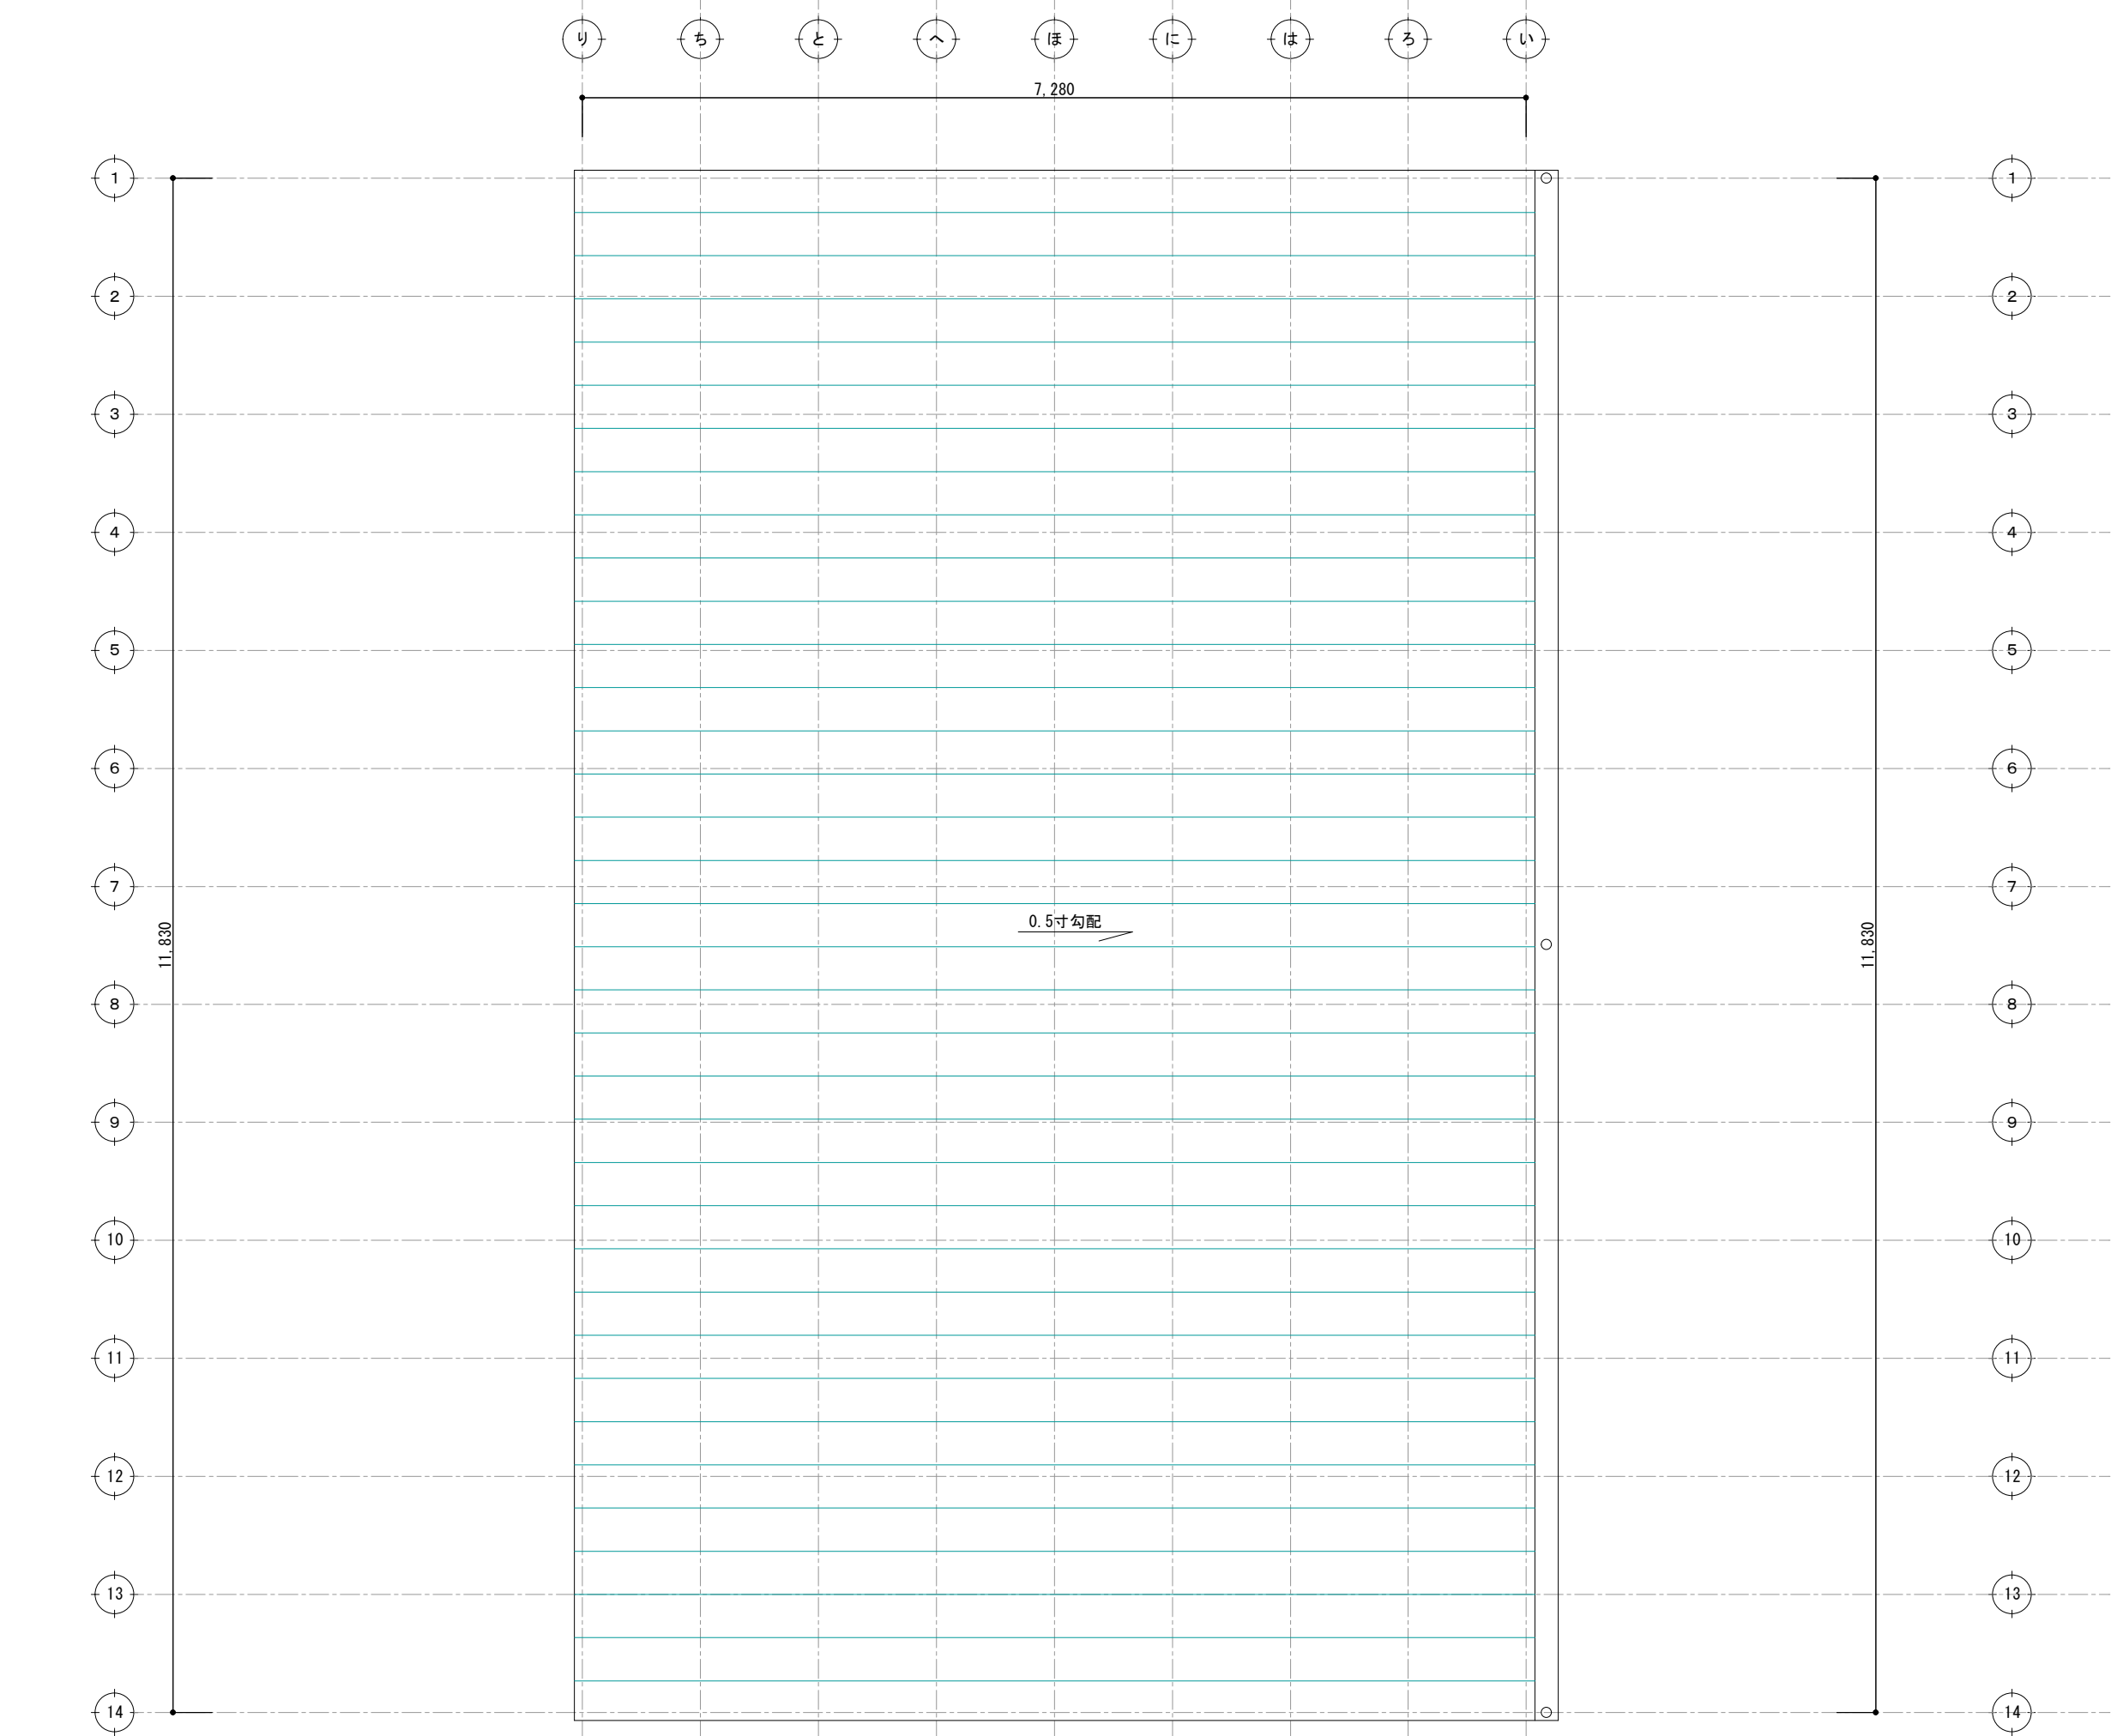


太陽光あり

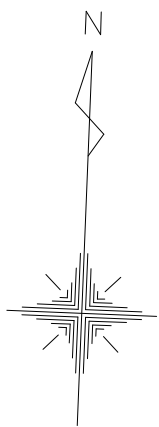


決定図

訂正	浜岡一級総合設計事務所		株式会社 LIFEFUND InDesign office 一級建築士事務所	年月日	件名		設計	IC	工事	図番
	一級建築士事務所 静岡県知事登録第 (10)2441 号			2025. 6. 13	杉山翔海様・美雨様 邸新築工事		酒井		青島	3-3
	一級建築士 大臣登録第 365879 号 西原利昌			縮尺	図名					
			事務所登録 (2) 第7595号 一級建築士登録 第179770号 鈴木 達男	1/100	屋根伏図					
			〒432-8023 静岡県浜松市中央区鴨江3丁目70番23号							

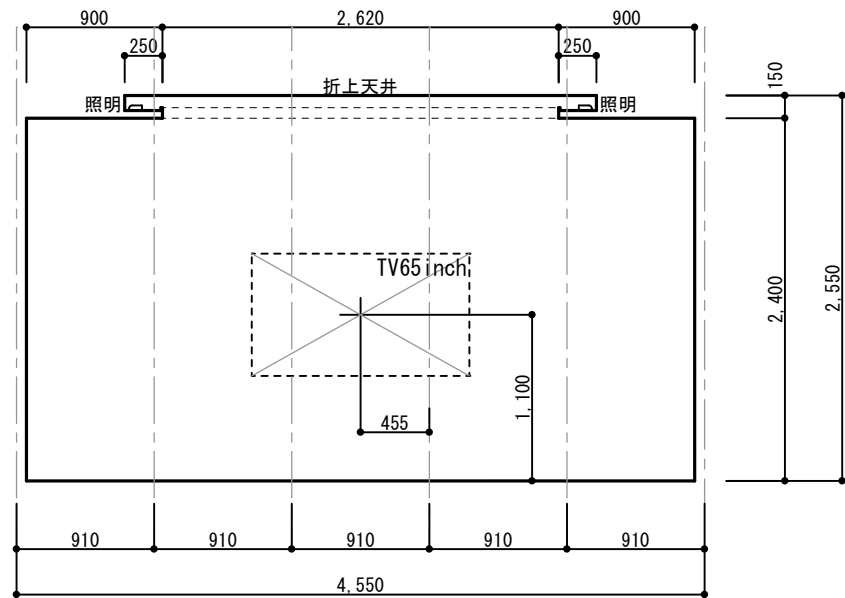


LDK① 西面

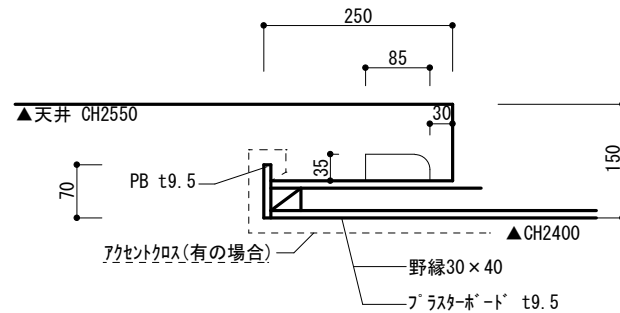


照明器具：まくちゃん(DAIKO)


LDK 折上天井 間接照明

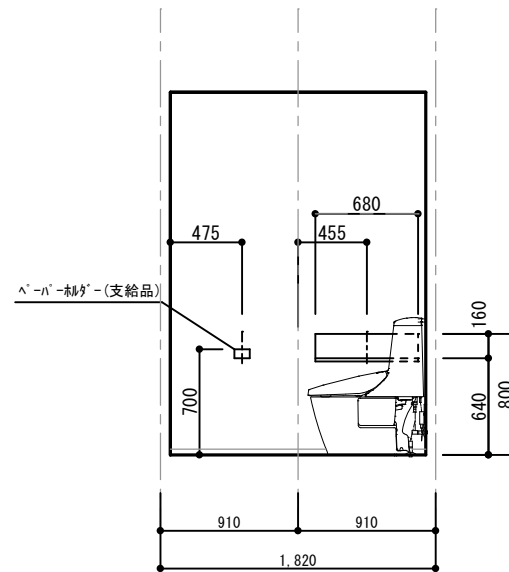


WC① 南面

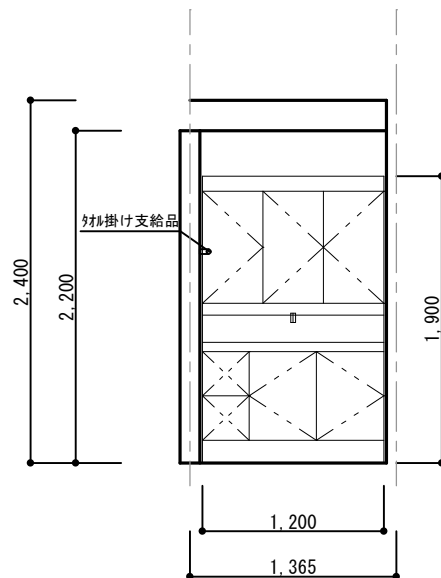

洗面 北面

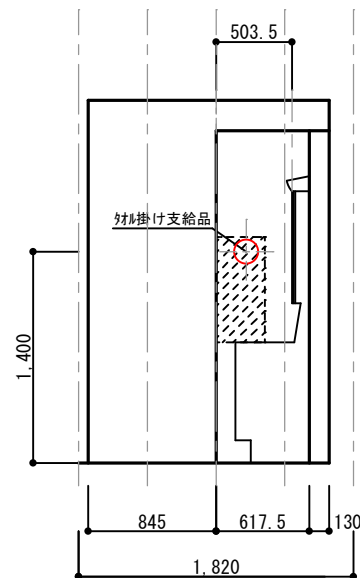


洗面 西面

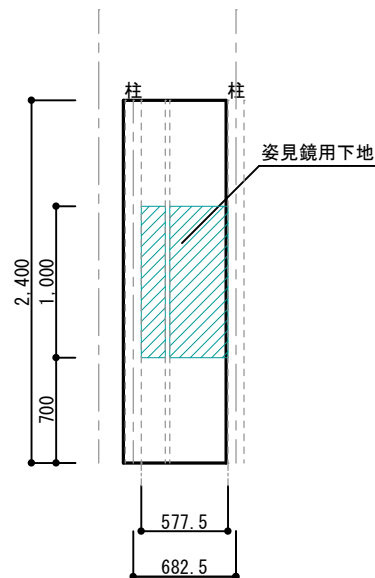

SC 西面

決定図

訂正	浜岡一級総合設計事務所 一級建築士事務所 静岡県知事登録第 (10)2441 号 一級建築士 大臣登録第 365879 号 西原利昌	LIFEFUND PG HOUSE	株式会社 LIFEFUND InDesign office 一級建築士事務所 事務所登録 (2) 第7595号 一級建築士登録 第179770号 鈴木 達男 〒432-8023 静岡県浜松市中央区鴨江3丁目70番23号	年月日 2025. 6. 13 縮尺 1/50	件名 杉山翔海様・美雨様 邸新築工事 図名 展開図-1		設計 酒井	IC	工事 青島	図番 6-1
----	--	----------------------	---	----------------------------------	--------------------------------------	--	----------	----	----------	-----------

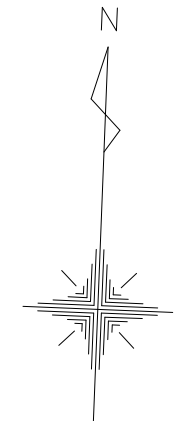

壁付け 住宅用火災報知器			数量
H 熱感知	熱感知器	電池式(単独型)	1
		露出型	

壁付け 住宅用火災報知器			数量
S 煙感知	煙感知器	電池式(単独型)	
		露出型	

※ 煙感知器は壁・梁より600mm以上離す
壁に取付ける場合、
天井から150mm以上500mm以内離す
換気扇・エアコン吹出口から1500mm以上離す

※ 全室LED照明とする。

※ 標準天井高さ2,400

※ 特記無きガラスは型ガラス


* 凡例

- 管柱 (105×105)
- Kタンパー (3.30倍 FRM-0641)
- 片筋違い (2.00倍 45×90)
(例 左:柱脚 右:柱頭)
- たすき掛筋違い (4.00倍 45×90)
- 構造用合板 (2.70倍)
(t=9 3枚 -EXハイパー)
- 床点検口
- 天井点検口
- 換気扇
- 熱交換換気扇VLR-70

アドバンスシリーズ		
スマートデザイン (外部)		
凡例	1	コンセント 1ヶロ
2	コンセント 2ヶロ	
3	コンセント 3ヶロ	
1ET	コンセント1ヶロ接地ターミナル付	
2ET	コンセント2ヶロ接地ターミナル付	
WP	コンセント 防水型	
WP	エアコン用コンセント	
WP	200V用コンセント	
WP	防雨入線プレート	
スイッチ	スイッチ	
3	3路スイッチ	
4	4路スイッチ	
直結電源	直結電源	
TV	テレビ取出口	
TEL	電話取出口 (テレホンガイド)	
LAN	LAN取出口 (テレホンガイド)	
壁照明	壁照明	
リモコン	リモコン (給湯関係・ルフロ)	
メーター	メーター	
分電盤	分電盤	
チャーム	チャーム	

※ACコンセント天井付け
※TVアンテナ工事
※スイッチはFL+1100、コンセントはFL+200

決定図

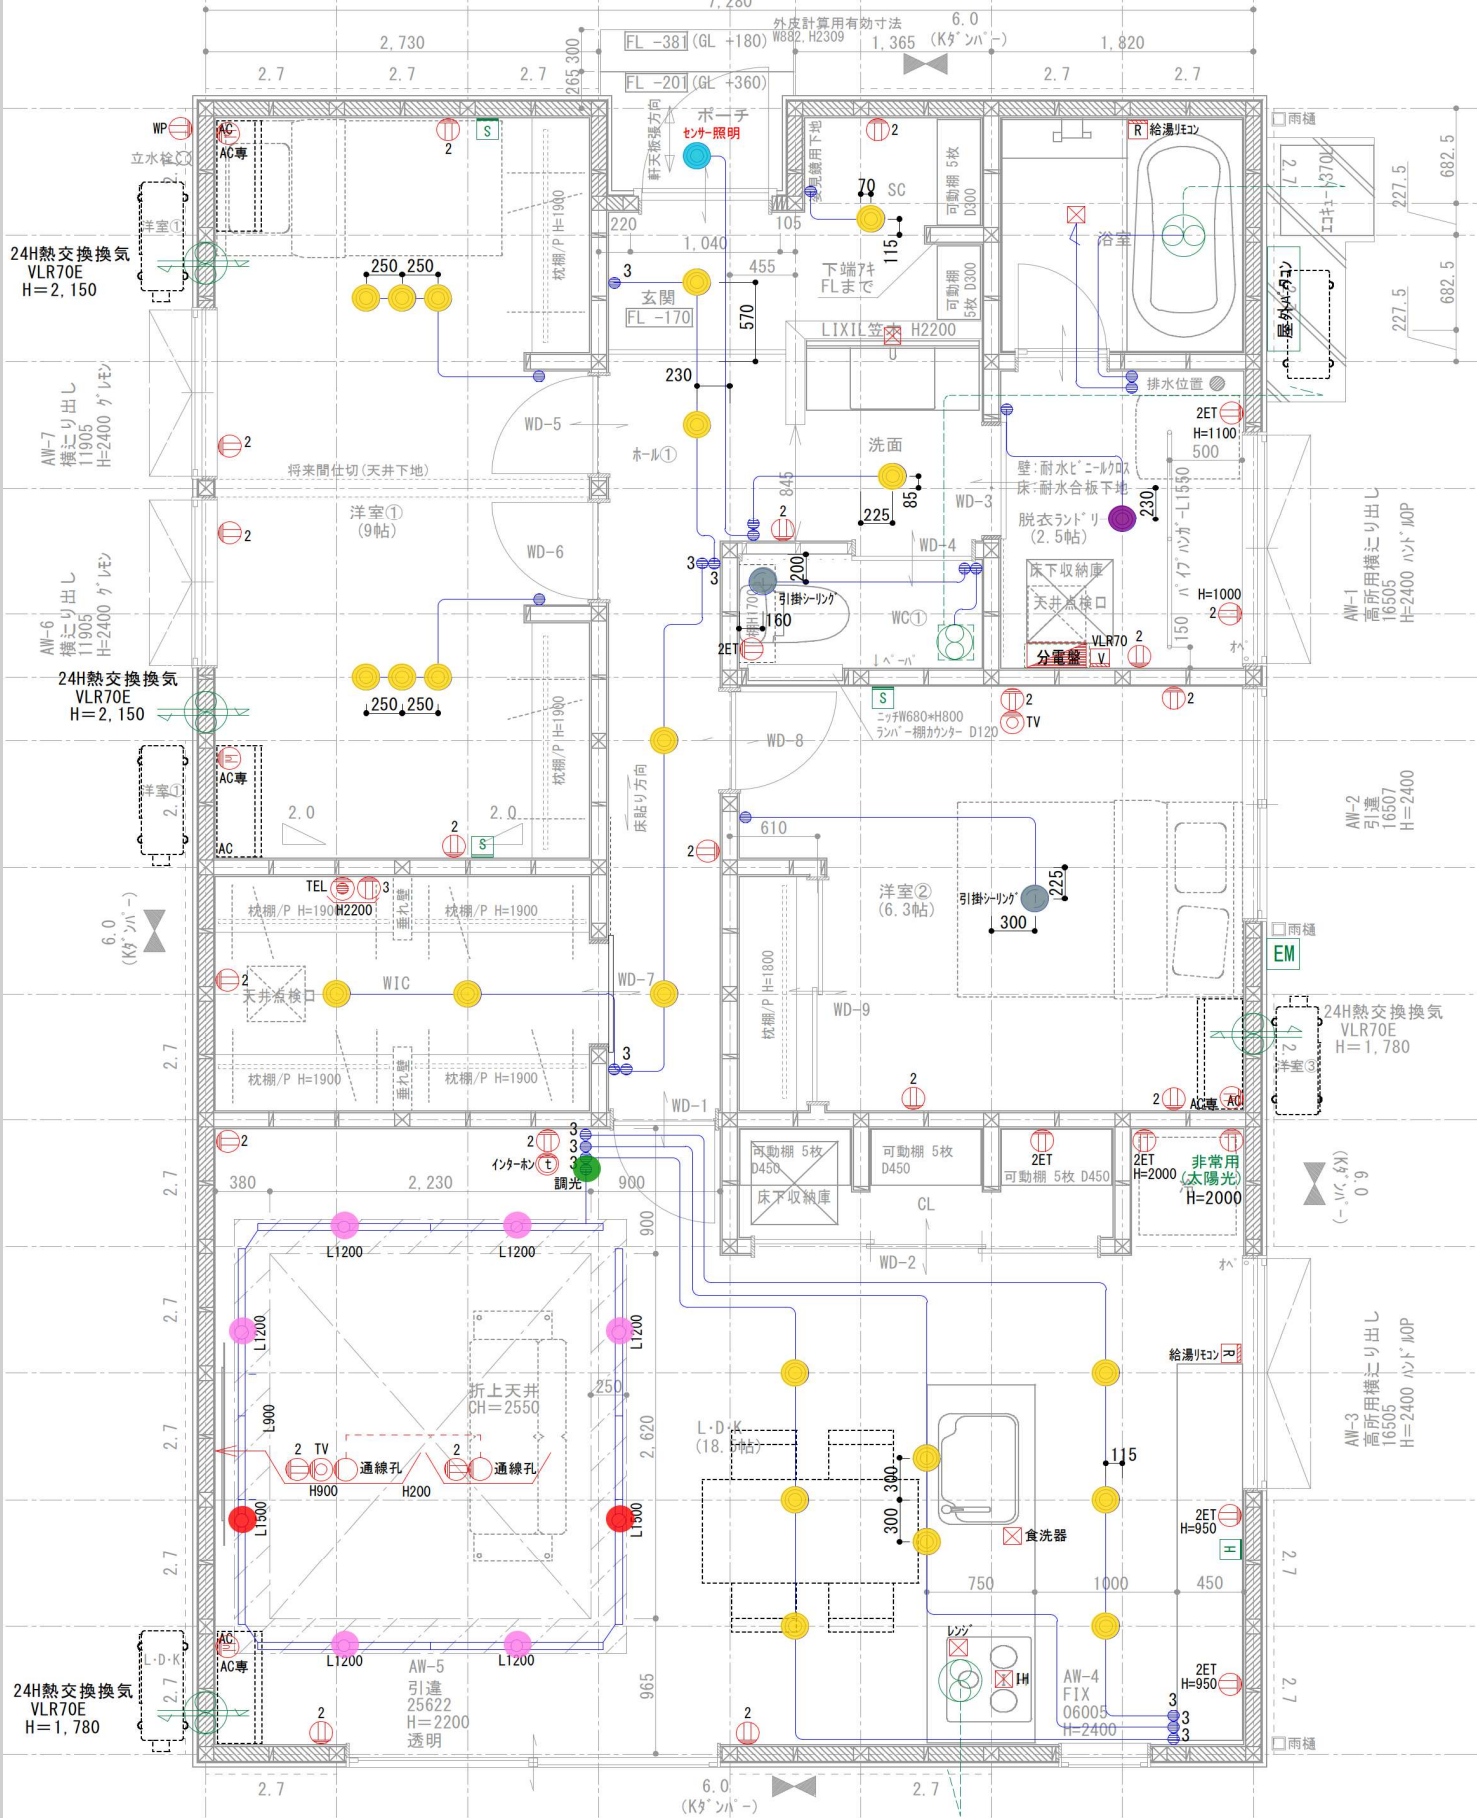

ドアホン：VL-SZ30KL
(Panasonic)

内部SW：アドバンス
マットホワイト

引っ掛けシーリング
● × 2

外部：スマートデザインシリーズ
ホワイトシルバー

ポーチ灯
● × 1
センサー付きダウンライト
DDL_4496YW

基本照明ダウンライト
● × 22
DDL_6102YW

脱衣ランドリ
● × 1
ダウンライト
DDL_6102AW


LDK
● × 6
間接照明
DSY_4393YWG

LDK
● × 2
間接照明
DSY_4394YWG

LDK 間接照明スイッチ
● × 1
調光SW
WTA_57583WK

決定図

決定図

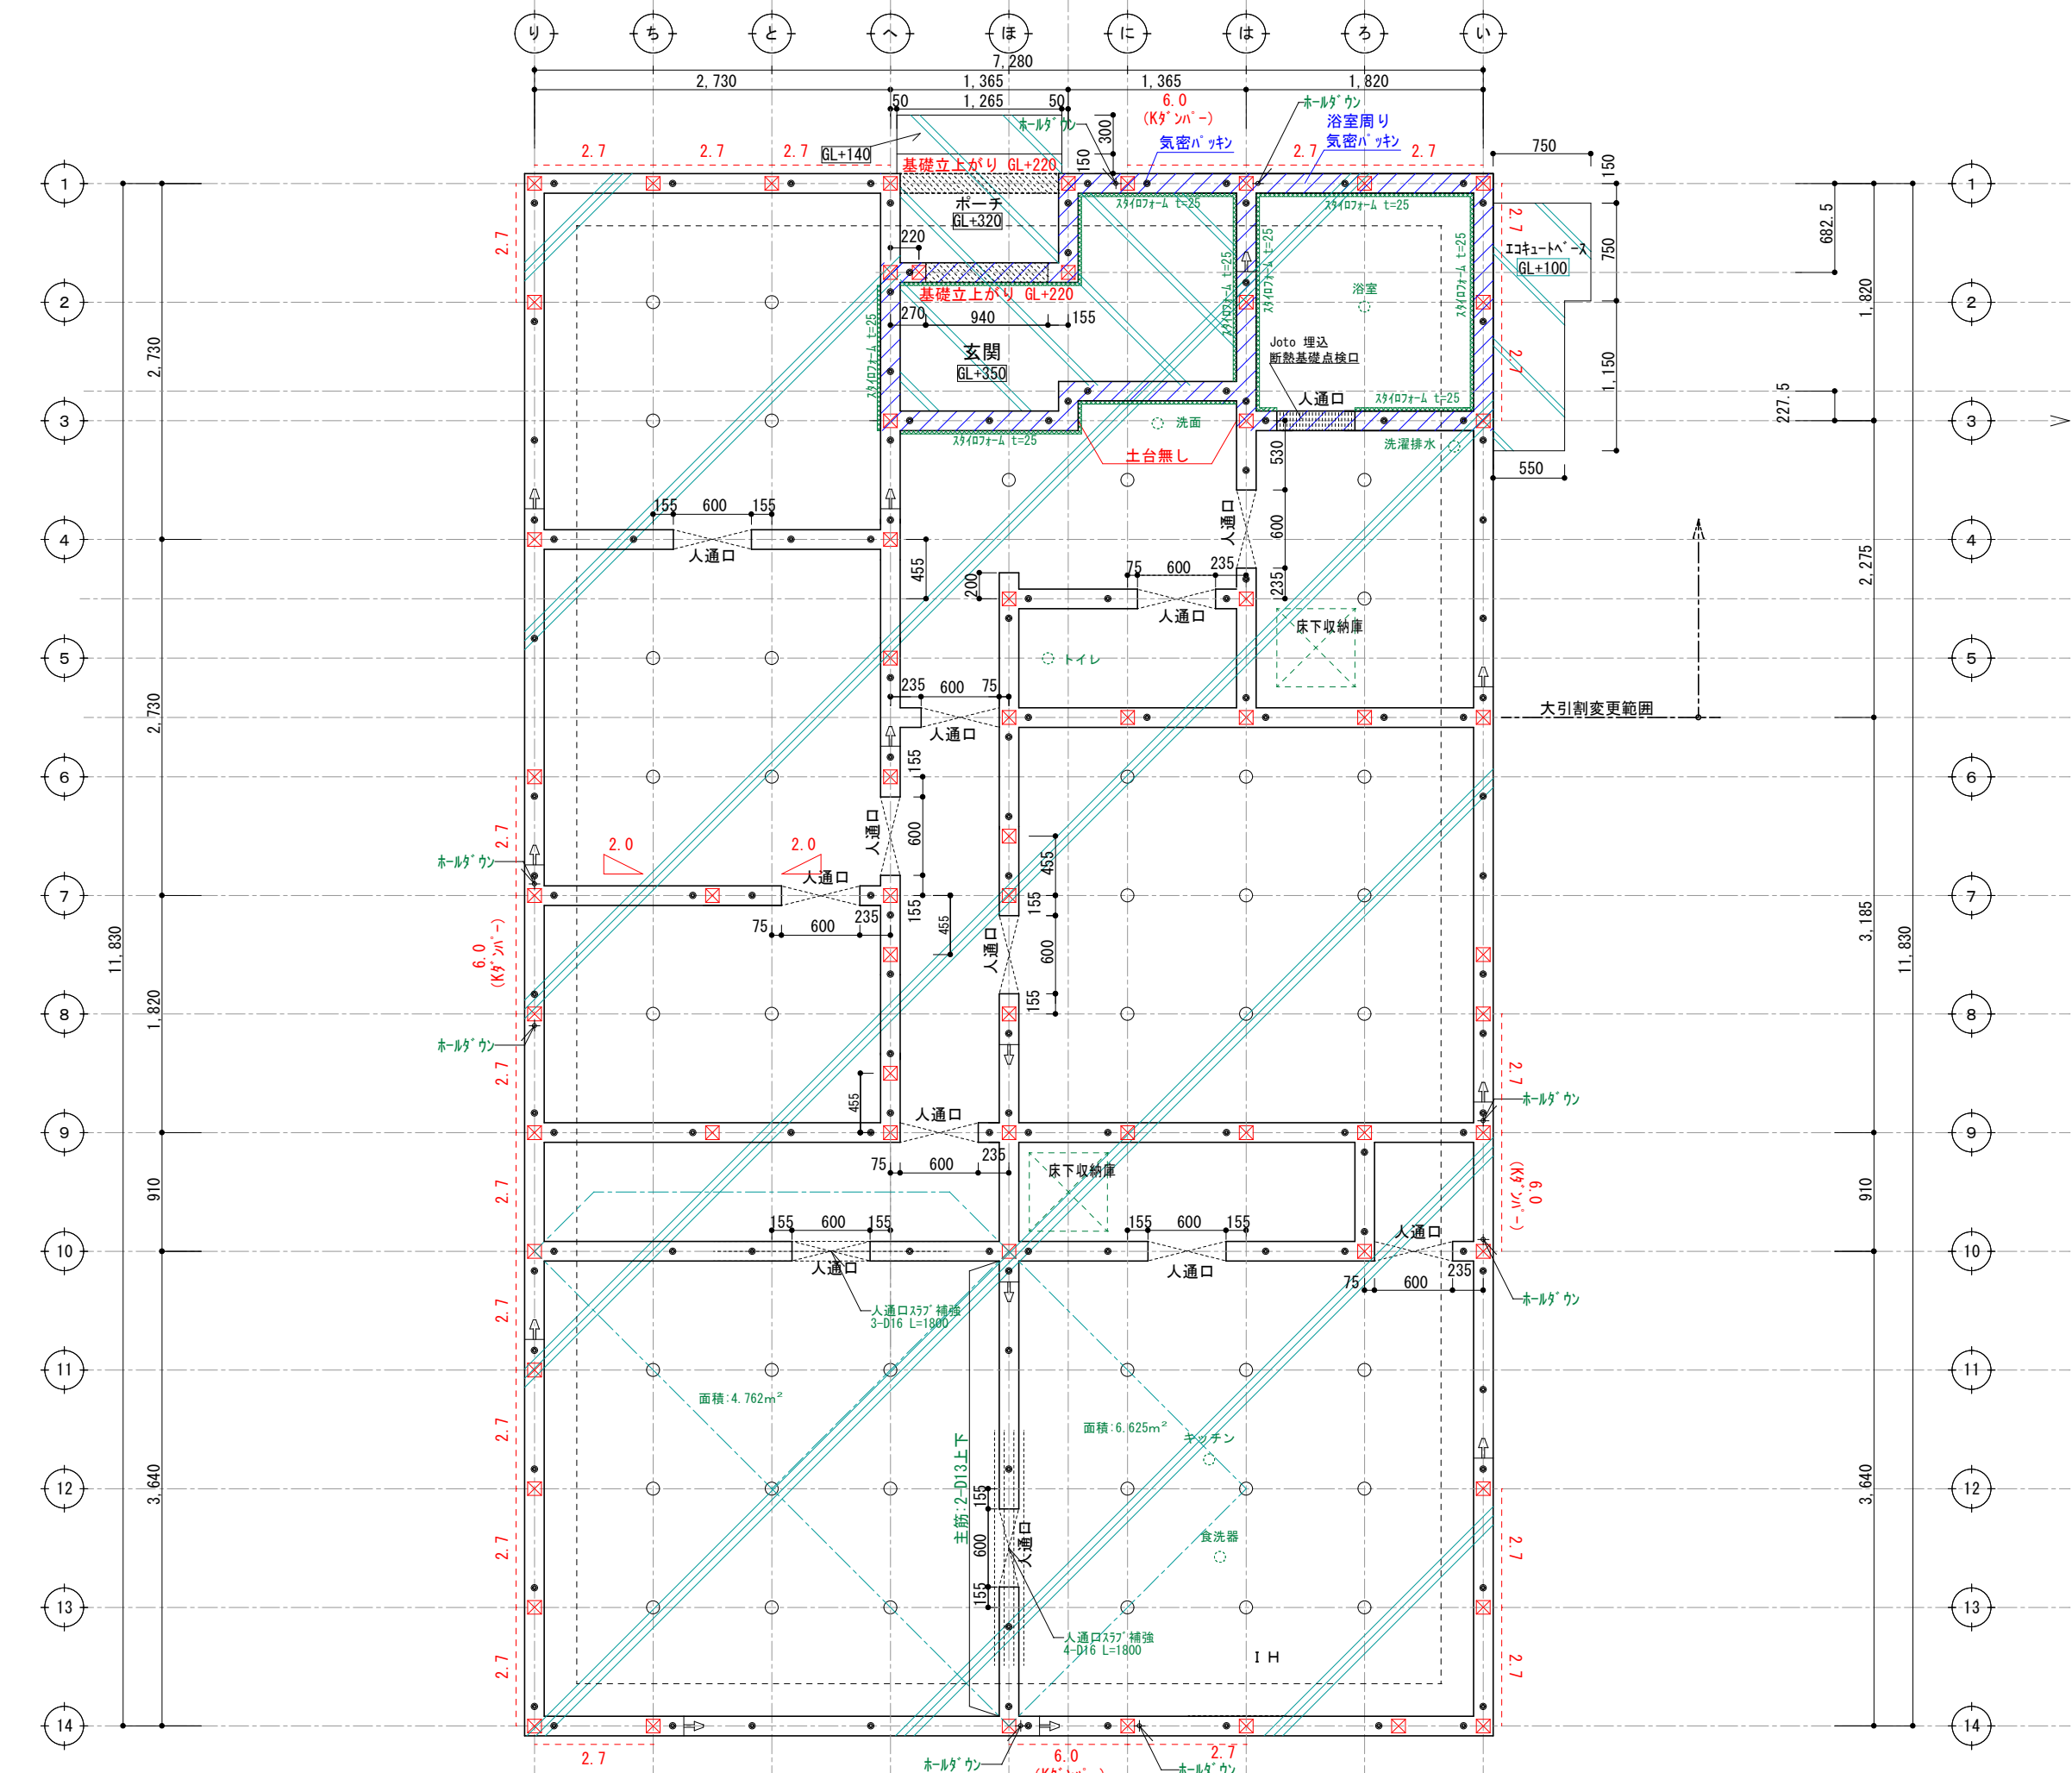


構造体ベースコンクリート t=150

後打ち土間コン

アンカーボルトの配置
土台切れの箇所より150mm
土台の継手及び仕口の端部より150mm
耐力壁の端部、筋交いの脚部より150mm
1.82m以下の間隔
250mm以上埋込み
基礎天端より120mm

筋かい凡例
柱脚 柱頭 片筋かい
たすき掛け筋かい
構造用パネル

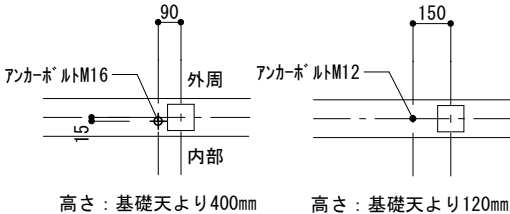







ホールダウン用アンカーボルト配置 アンカーボルト配置

凡例
通し柱 (105*105) 管柱 (105*105)
● アンカーボルトM12 L=400
+ ホールダウンアンカーM16 L=800
柱芯より90mm 280mm以上埋め込み
(カナダフィストアンカーボルトM16)
⊕ 鋼製束
土台ジョイント
ベースコンクリート (t=150)
後打ちコンクリート

基礎伏図について特記なき場合に限り下記による。

1. コンクリート：呼び強度 21N/mm²
2. 鉄筋：SD295A
3. 設計地耐力： $f_e=20\text{kN/m}^2$
地耐力計測後、不足の場合は相当の改良を行い、満たすものとする。
4. 基礎の位置は、芯振分けとする。
5. 玄関・S/C・UB周囲の基礎天端は気密パッキン施工（網掛け部）とし、その他の基礎天端は基礎パッキン施工とする。
6. 設備配管の屋内への取り入れは基礎立上り部のスリーブによる。

訂正	浜岡一級総合設計事務所 一級建築士事務所 静岡県知事登録第 (10)2441 号 一級建築士 大臣登録第 365879 号 西原利昌	LIFEFUND PG HOUSE	株式会社 LIFEFUND InDesign office 一級建築士事務所 事務所登録 (2)第7595号 一級建築士登録 第179770号 鈴木 達男 〒432-8023 静岡県浜松市中央区鴨江3丁目70番23号	年月日 2024.6.13 縮尺 1/50	件名 杉山翔海様・美雨様 邸新築工事 図名 基礎伏図	設計 酒井	IC	工事 青島	図番 B-1
----	--	----------------------	--	--------------------------------	-------------------------------------	----------	----	----------	-----------

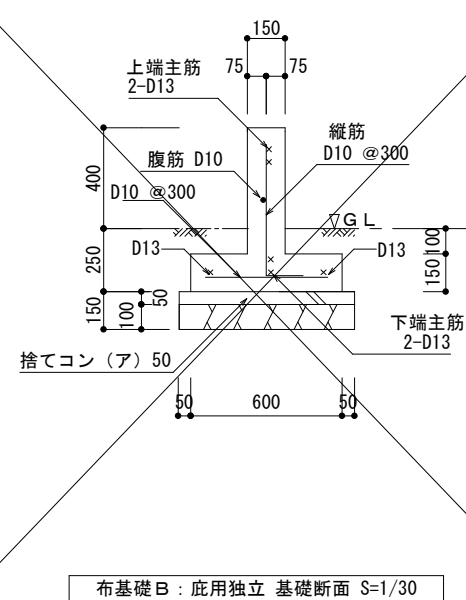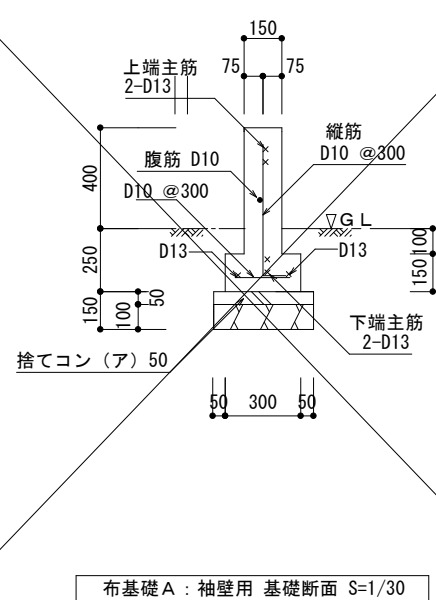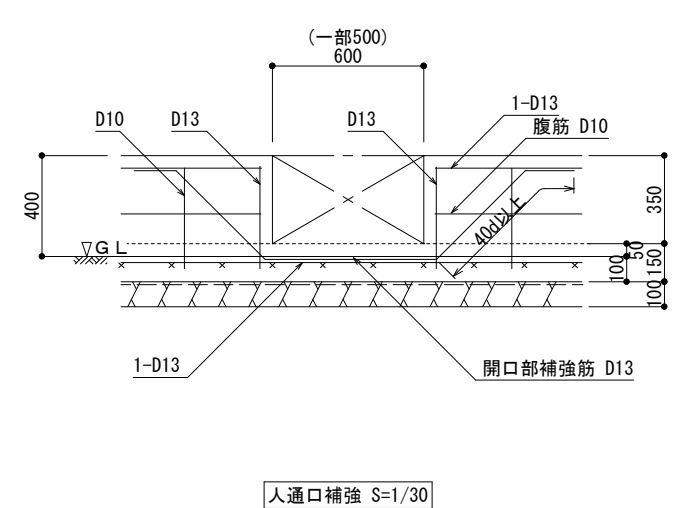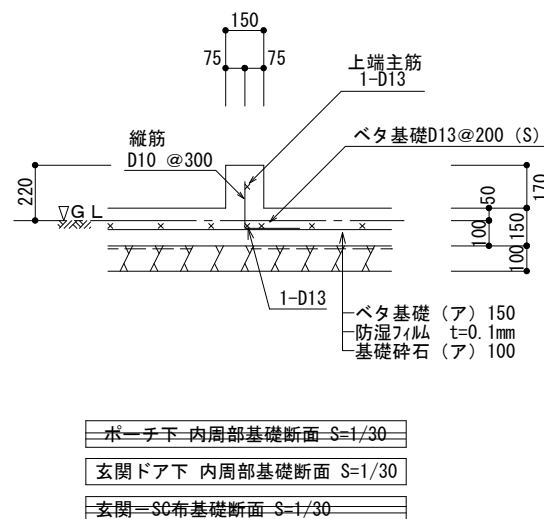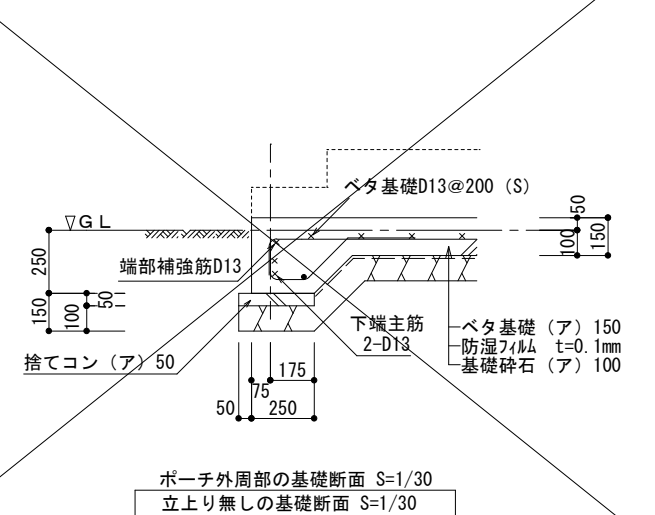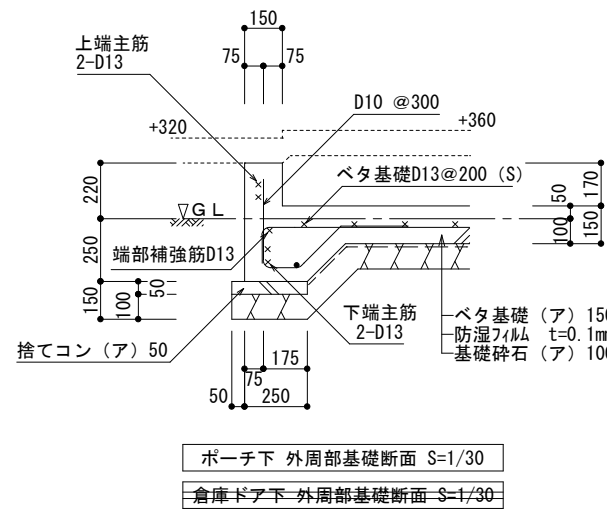


基礎の寸法 及び 配筋の検証方法	基礎立上り配筋は、 (財)日本住宅・木材技術 センター発行のスパン表 (増補版)による。 ベタ基礎スラブ配筋は、 まもりすまい保険設計施工 基準同解説のベタ基礎配筋表 による。具体的な寸法・配 筋は基礎詳細図参照。
------------------------	---

鉄筋断面表記

● ・ ・ D10を示す。

× ・ ・ D13を示す。

※使用しない断面は **決定図**

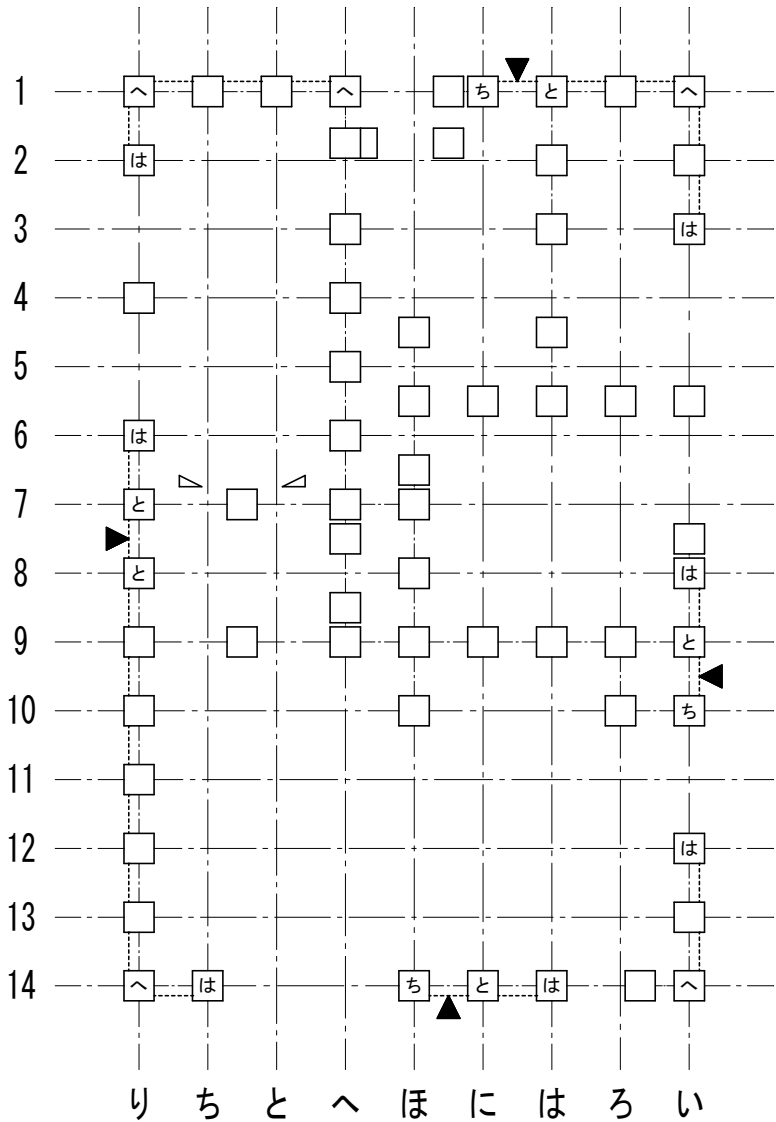

1 階柱壁伏図

接合部凡例				*接合部凡例はユーザ設定されたものです。	
記号	仕様（カナイ金物）		N	倍率	
SBCP	スリムビルドコーナー75, チビクリCK (化粧柱の場合)		0.00	1.00	
SBCP	スリムビルドコーナー75, チビクリCK (化粧柱の場合)		0.65	1.00	
SBCP	は	スリムビルドコーナー75	1.00	1.00	
ARCG	に	アレントコーナー合板用	1.40	2.20	
ARCG	ほ	アレントコーナー合板用	1.60	2.20	
ARCG	へ	アレントコーナー合板用	1.80	2.20	
HD15	と	ブレイブホールダウン B-HD15	2.80	3.60	
HD20	ち	ブレイブホールダウン B-HD20	3.70	4.70	
HD25	り	ブレイブホールダウン B-HD25	4.70	4.80	
HD30	ぬ	ブレイブホールダウン B-HD30	5.60	7.20	
J1	る	腰掛け蟻若しくは大入れ蟻掛け+羽子板ボルト、短冊金物		1.90	
J2	を	腰掛け蟻若しくは大入れ蟻掛け+羽子板ボルト、短冊金物×2		3.00	

※表示なき金物は「は」とする。

梁継手・仕口用

梁継手・仕口用

接合部凡例				*接合部凡例はユーザ設定されたものです。	
記号	仕様（タナカ金物）		N	倍率	
FCP	フックコーナー, チビクリCK (化粧柱の場合)		0.00	1.00	
FCP	フックコーナー, チビクリCK (化粧柱の場合)		0.65	1.00	
FCP	は	フックコーナー	1.00	1.00	
GCP	に	シナコーナー	1.40	2.20	
GCP	ほ	シナコーナー	1.60	2.20	
GCP	へ	シナコーナー	1.80	2.20	
HD15	と	ビス止めホールダウンU HD15	2.80	3.60	
HD20	ち	ビス止めホールダウンU HD20	3.70	4.70	
HD25	り	ビス止めホールダウンU HD25	4.70	4.80	
HD30	ぬ	ビス止めホールダウンU HD15×2 (HD35)	5.60	7.20	
J1	る	腰掛け蟻若しくは大入れ蟻掛け+羽子板ボルト、短冊金物		1.90	
J2	を	腰掛け蟻若しくは大入れ蟻掛け+羽子板ボルト、短冊金物×2		3.00	

※表示なき金物は「は」とする。

梁継手・仕口用

梁継手・仕口用

筋かいの種類に応じた筋かいの端部の接合部の仕様		
	筋かいの種類	接合部の仕様（構造方法）
イ	鉄筋φ9	柱又は横架材を貫通し、三角座金を介してナット締め、又は鋼板添え板を用い鋼板を柱及び横架材にCN90, 8本平打ち
ロ	筋かい:15×90	柱・横架材を欠き込み、柱・横架材双方に対してN65, 5本平打ち
ハ	筋かい:30×90	鋼板添え板t=1.6mmを筋かいに対してボルトφ12及びCN65, 3本平打ち、柱に対してCN65, 3本平打ち、横架材に対してCN65, 4本平打ち。筋かいプレートBP同等品
ニ	筋かい:45×90	鋼板添え板t=2.3mmを筋かいに対してボルトφ12及びスクリュー釘φ4.5L50, 7本平打ち、柱及び横架材に対してスクリュー釘φ4.5L50, 5本平打ち。筋かいプレートBP-2同等品
ホ	筋かい:90×90	柱又は横架材にボルトφ12mmを用いて一面剪断接合

胴差と通し柱の接合部の仕様		
	胴差と通し柱の条件	仕口
T1	通し柱の片側に胴差が来る場合	胴差を柱にかたぎ大入れ短ほぞ差しの上、羽子板ボルト、かね折り金物又は同等以上の仕口
T2	通し柱の両側に胴差が来る場合	胴差を柱にかたぎ大入れ短ほぞ差しの上、短冊金物又は、同等以上の仕口で胴差相互を緊結
T3	通し柱と胴差の接合部の近くに90×90以上の筋かいが来る場合 (通し柱が建物の出隅にあるか、筋かい壁が外壁と直交して接する場合)	胴差を通し柱に、15KN用引き寄せ金物を水平に用いて緊結

決定図