
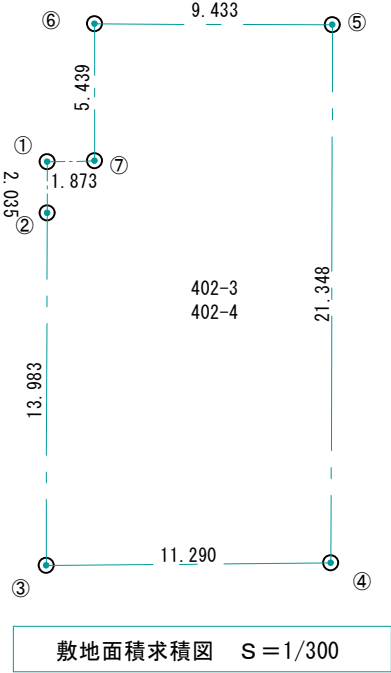


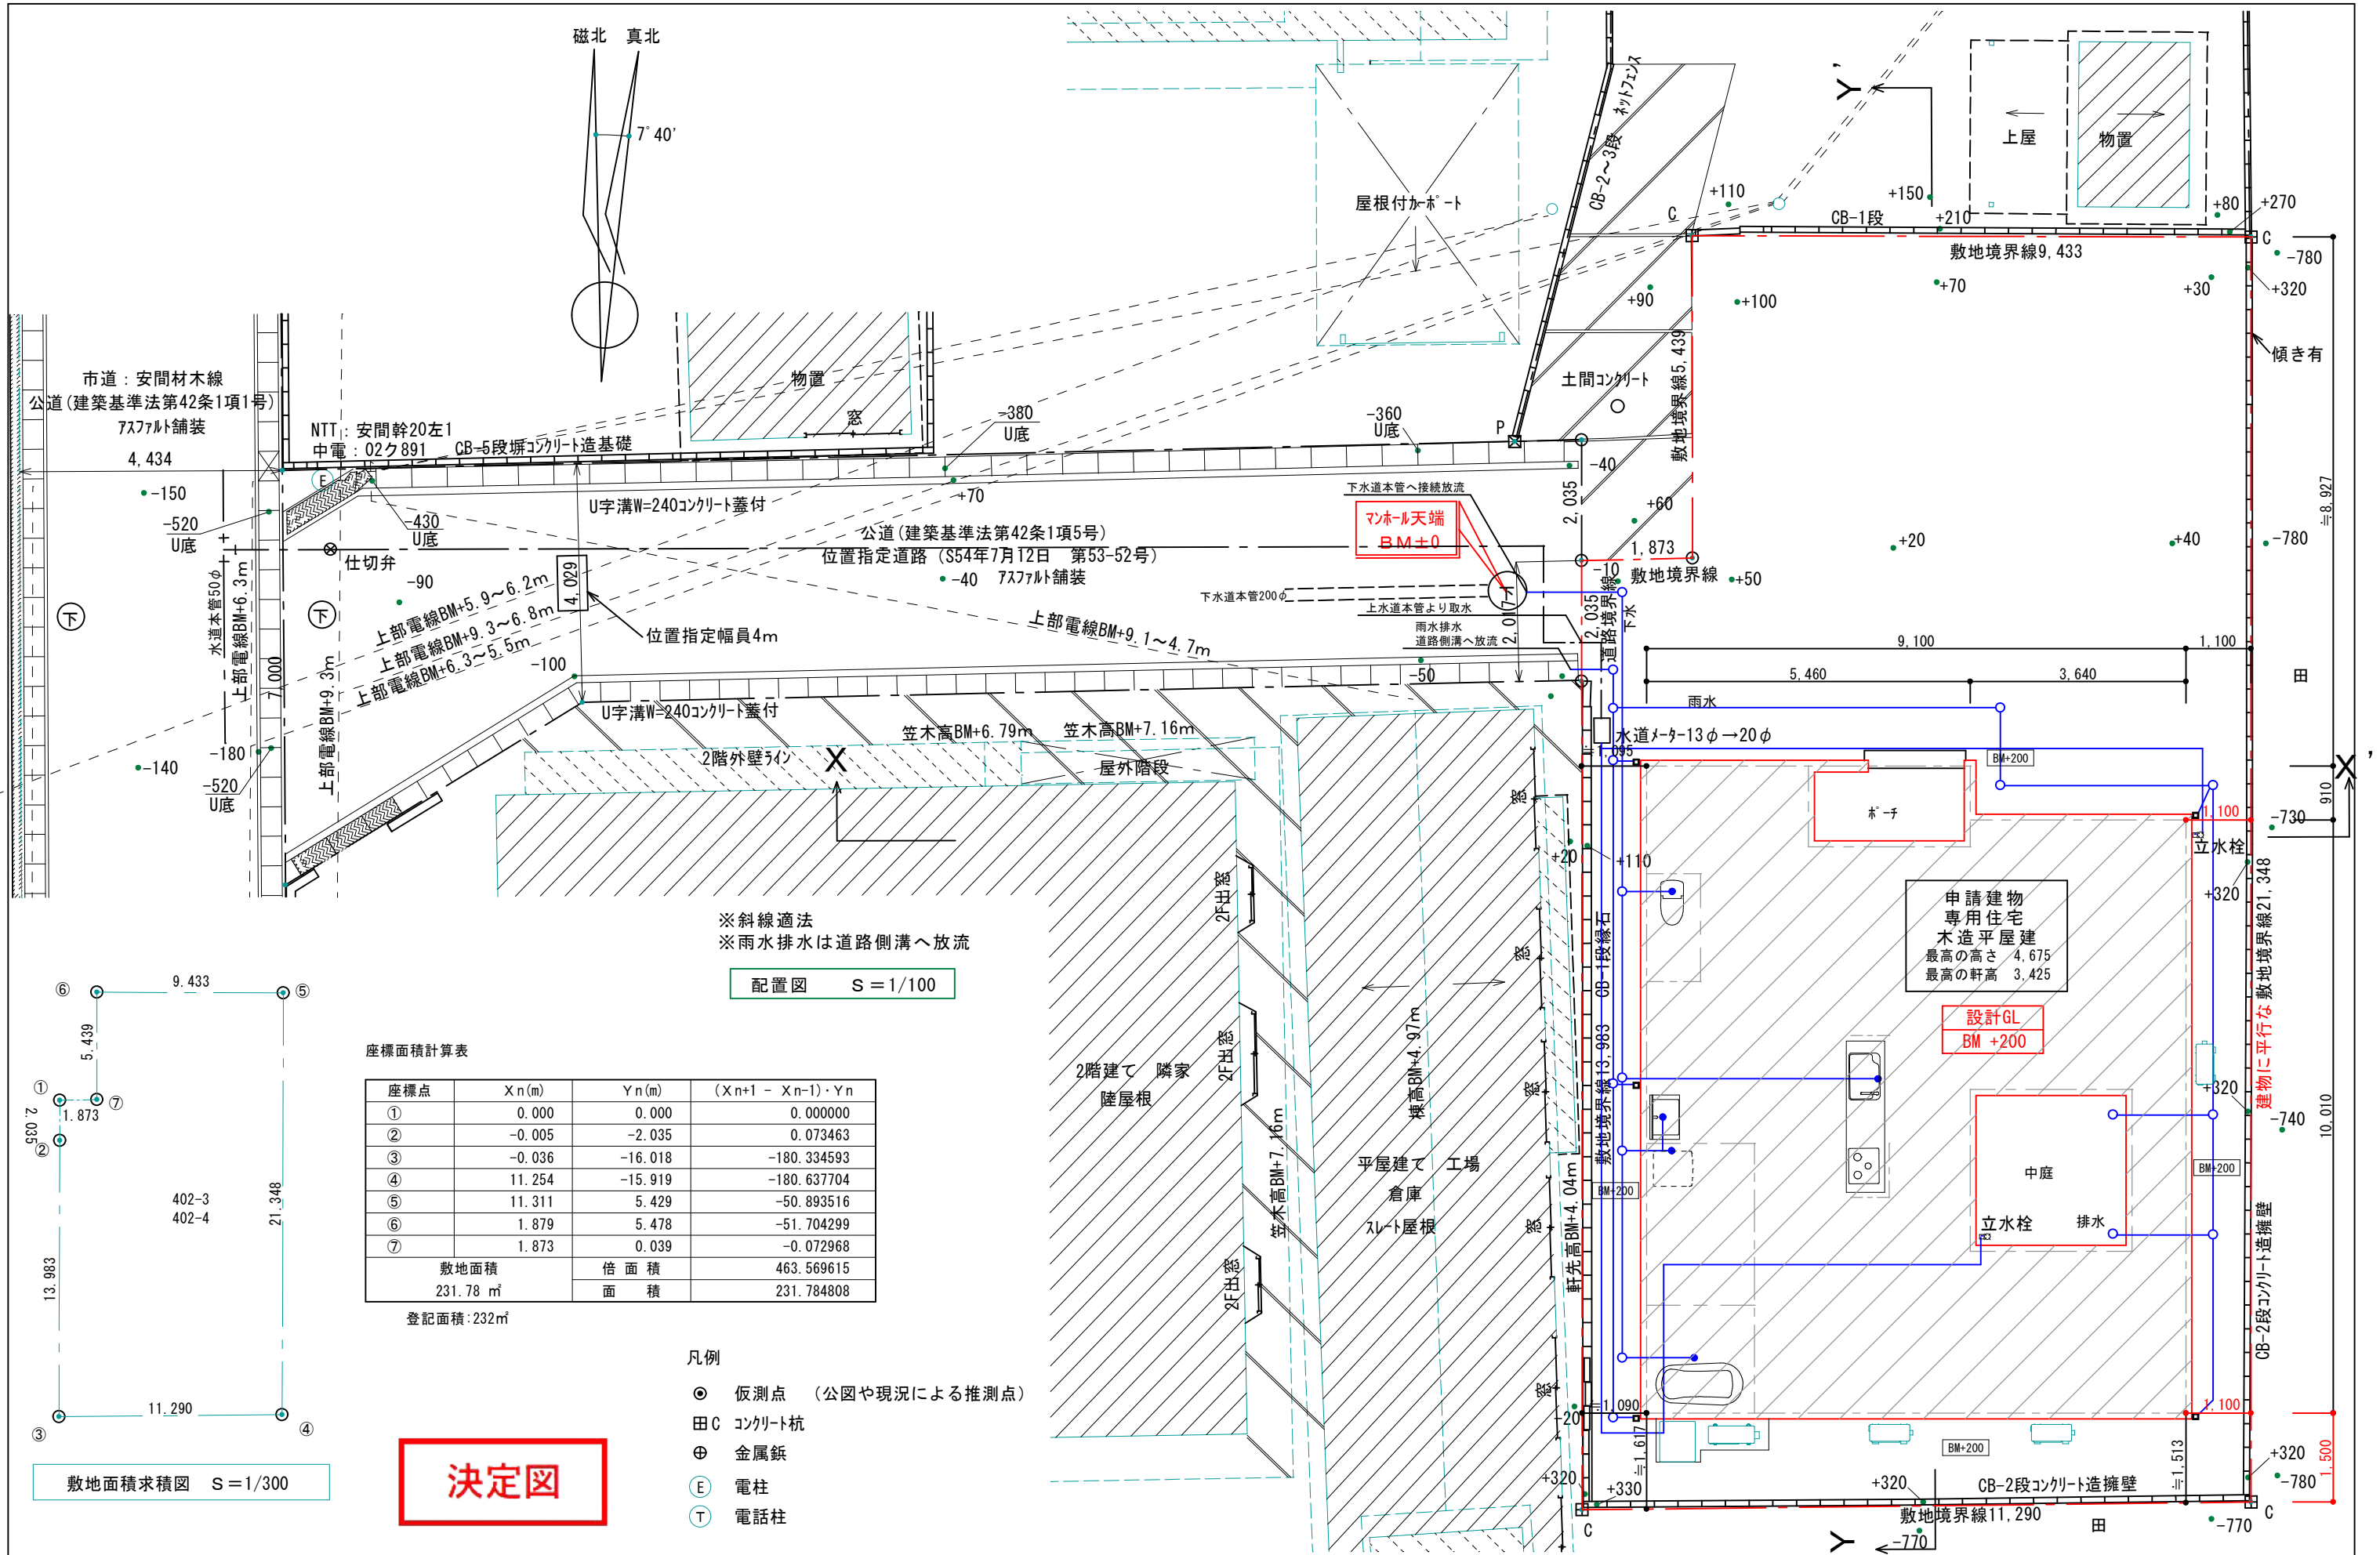

座標面積計算表

座標点	X n (m)	Y n (m)	(X n+1 - X n-1)・Y n
①	0.000	0.000	0.000000
②	-0.005	-2.035	0.073463
③	-0.036	-16.018	-180.334593
④	11.254	-15.919	-180.637704
⑤	11.311	5.429	-50.893516
⑥	1.879	5.478	-51.704299
⑦	1.873	0.039	-0.072968
敷地面積		倍面積	463.569615
231.78 m ²		面積	231.784808

登記面積：232m²

※斜線適法
※雨水排水は道路側溝へ放流

配置図 S = 1/100

凡例

- 仮測点 (公図や現況による推測点)
- 田C コンクリート杭
- ⊕ 金属鈑
- ⓔ 電柱
- Ⓣ 電話柱

決定図