


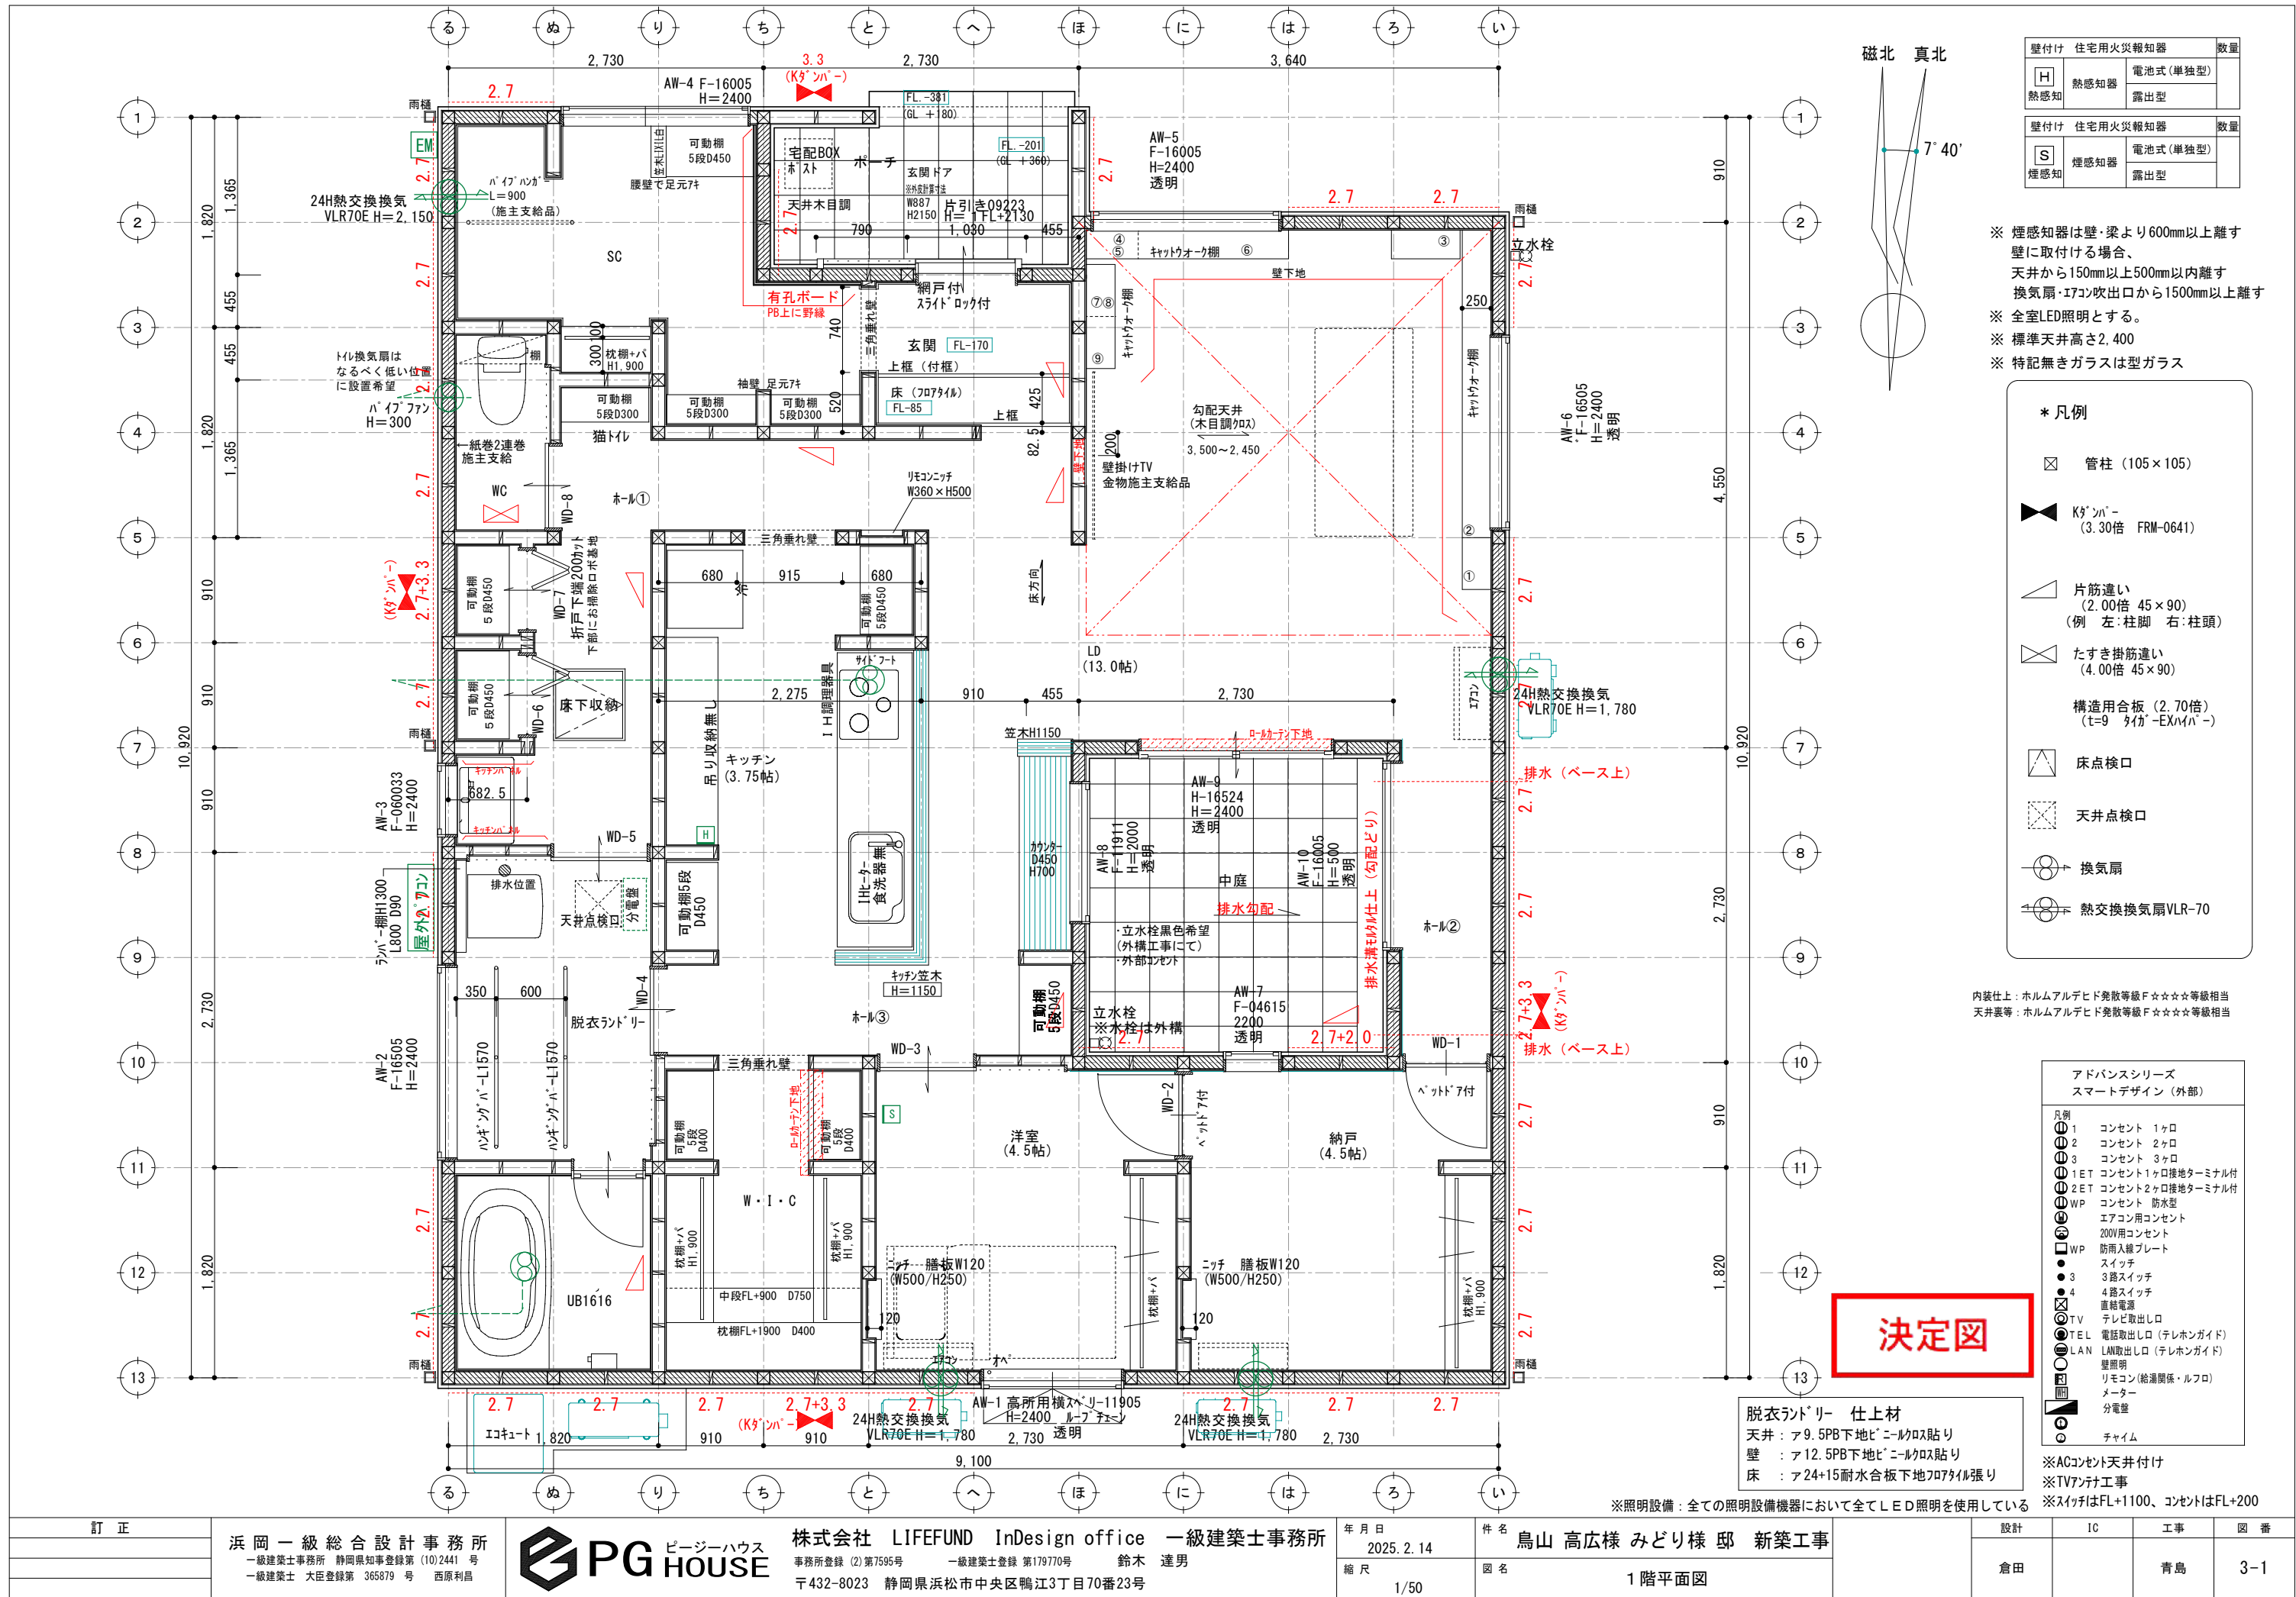

| 壁付け 住宅用火災報知器 |      |          | 数量 |
|--------------|------|----------|----|
| H            | 熱感知器 | 電池式(単独型) |    |
|              | 露出型  |          |    |
| 壁付け 住宅用火災報知器 |      |          | 数量 |
| S            | 煙感知器 | 電池式(単独型) |    |
|              | 露出型  |          |    |

※ 煙感知器は壁・梁より600mm以上離す  
壁に取付ける場合、  
天井から150mm以上500mm以内離す  
換気扇・エアコン吹出口から1500mm以上離す  
※ 全室LED照明とする。  
※ 標準天井高さ2,400  
※ 特記無きガラスは型ガラス

\* 凡例

- 管柱 (105×105)
- Kダクト (3.30倍 FRM-0641)
- 片筋違い (2.00倍 45×90)  
(例 左:柱脚 右:柱頭)
- たすき掛筋違い (4.00倍 45×90)
- 構造用合板 (2.70倍)  
(t=9 90°付 EXハイパー)
- 床点検口
- 天井点検口
- 換気扇
- 熱交換換気扇VLR-70

内装仕上：ホルムアルデヒド発散等級F☆☆☆☆等級相当  
天井裏等：ホルムアルデヒド発散等級F☆☆☆☆等級相当

| アドバンスシリーズ<br>スマートデザイン (外部) |   |                  |
|----------------------------|---|------------------|
| 凡例                         |   |                  |
| ①                          | 1 | コンセント 1ヶ所        |
| ②                          | 2 | コンセント 2ヶ所        |
| ③                          | 3 | コンセント 3ヶ所        |
| ①ET                        |   | コンセント1ヶ所接地ターミナル付 |
| ②ET                        |   | コンセント2ヶ所接地ターミナル付 |
| WP                         |   | コンセント 防水型        |
|                            |   | エアコン用コンセント       |
|                            |   | 200V用コンセント       |
| WP                         |   | 防雨入線プレート         |
| ●                          |   | スイッチ             |
| ●                          | 3 | 3路スイッチ           |
| ●                          | 4 | 4路スイッチ           |
| ⊗                          |   | 直結電源             |
| TV                         |   | テレビ取出口           |
| TEL                        |   | 電話取出口 (テレホンガイド)  |
| LAN                        |   | LAN取出口 (テレホンガイド) |
| 壁                          |   | 壁照明              |
| リモ                         |   | リモコン (給湯関係・ルフロ)  |
| メ                          |   | メーター             |
| 分                          |   | 分電盤              |
| チャ                         |   | チャイム             |

※ACコンセント天井付け  
※TVアンテナ工事  
※スイッチはFL+1100、コンセントはFL+200