


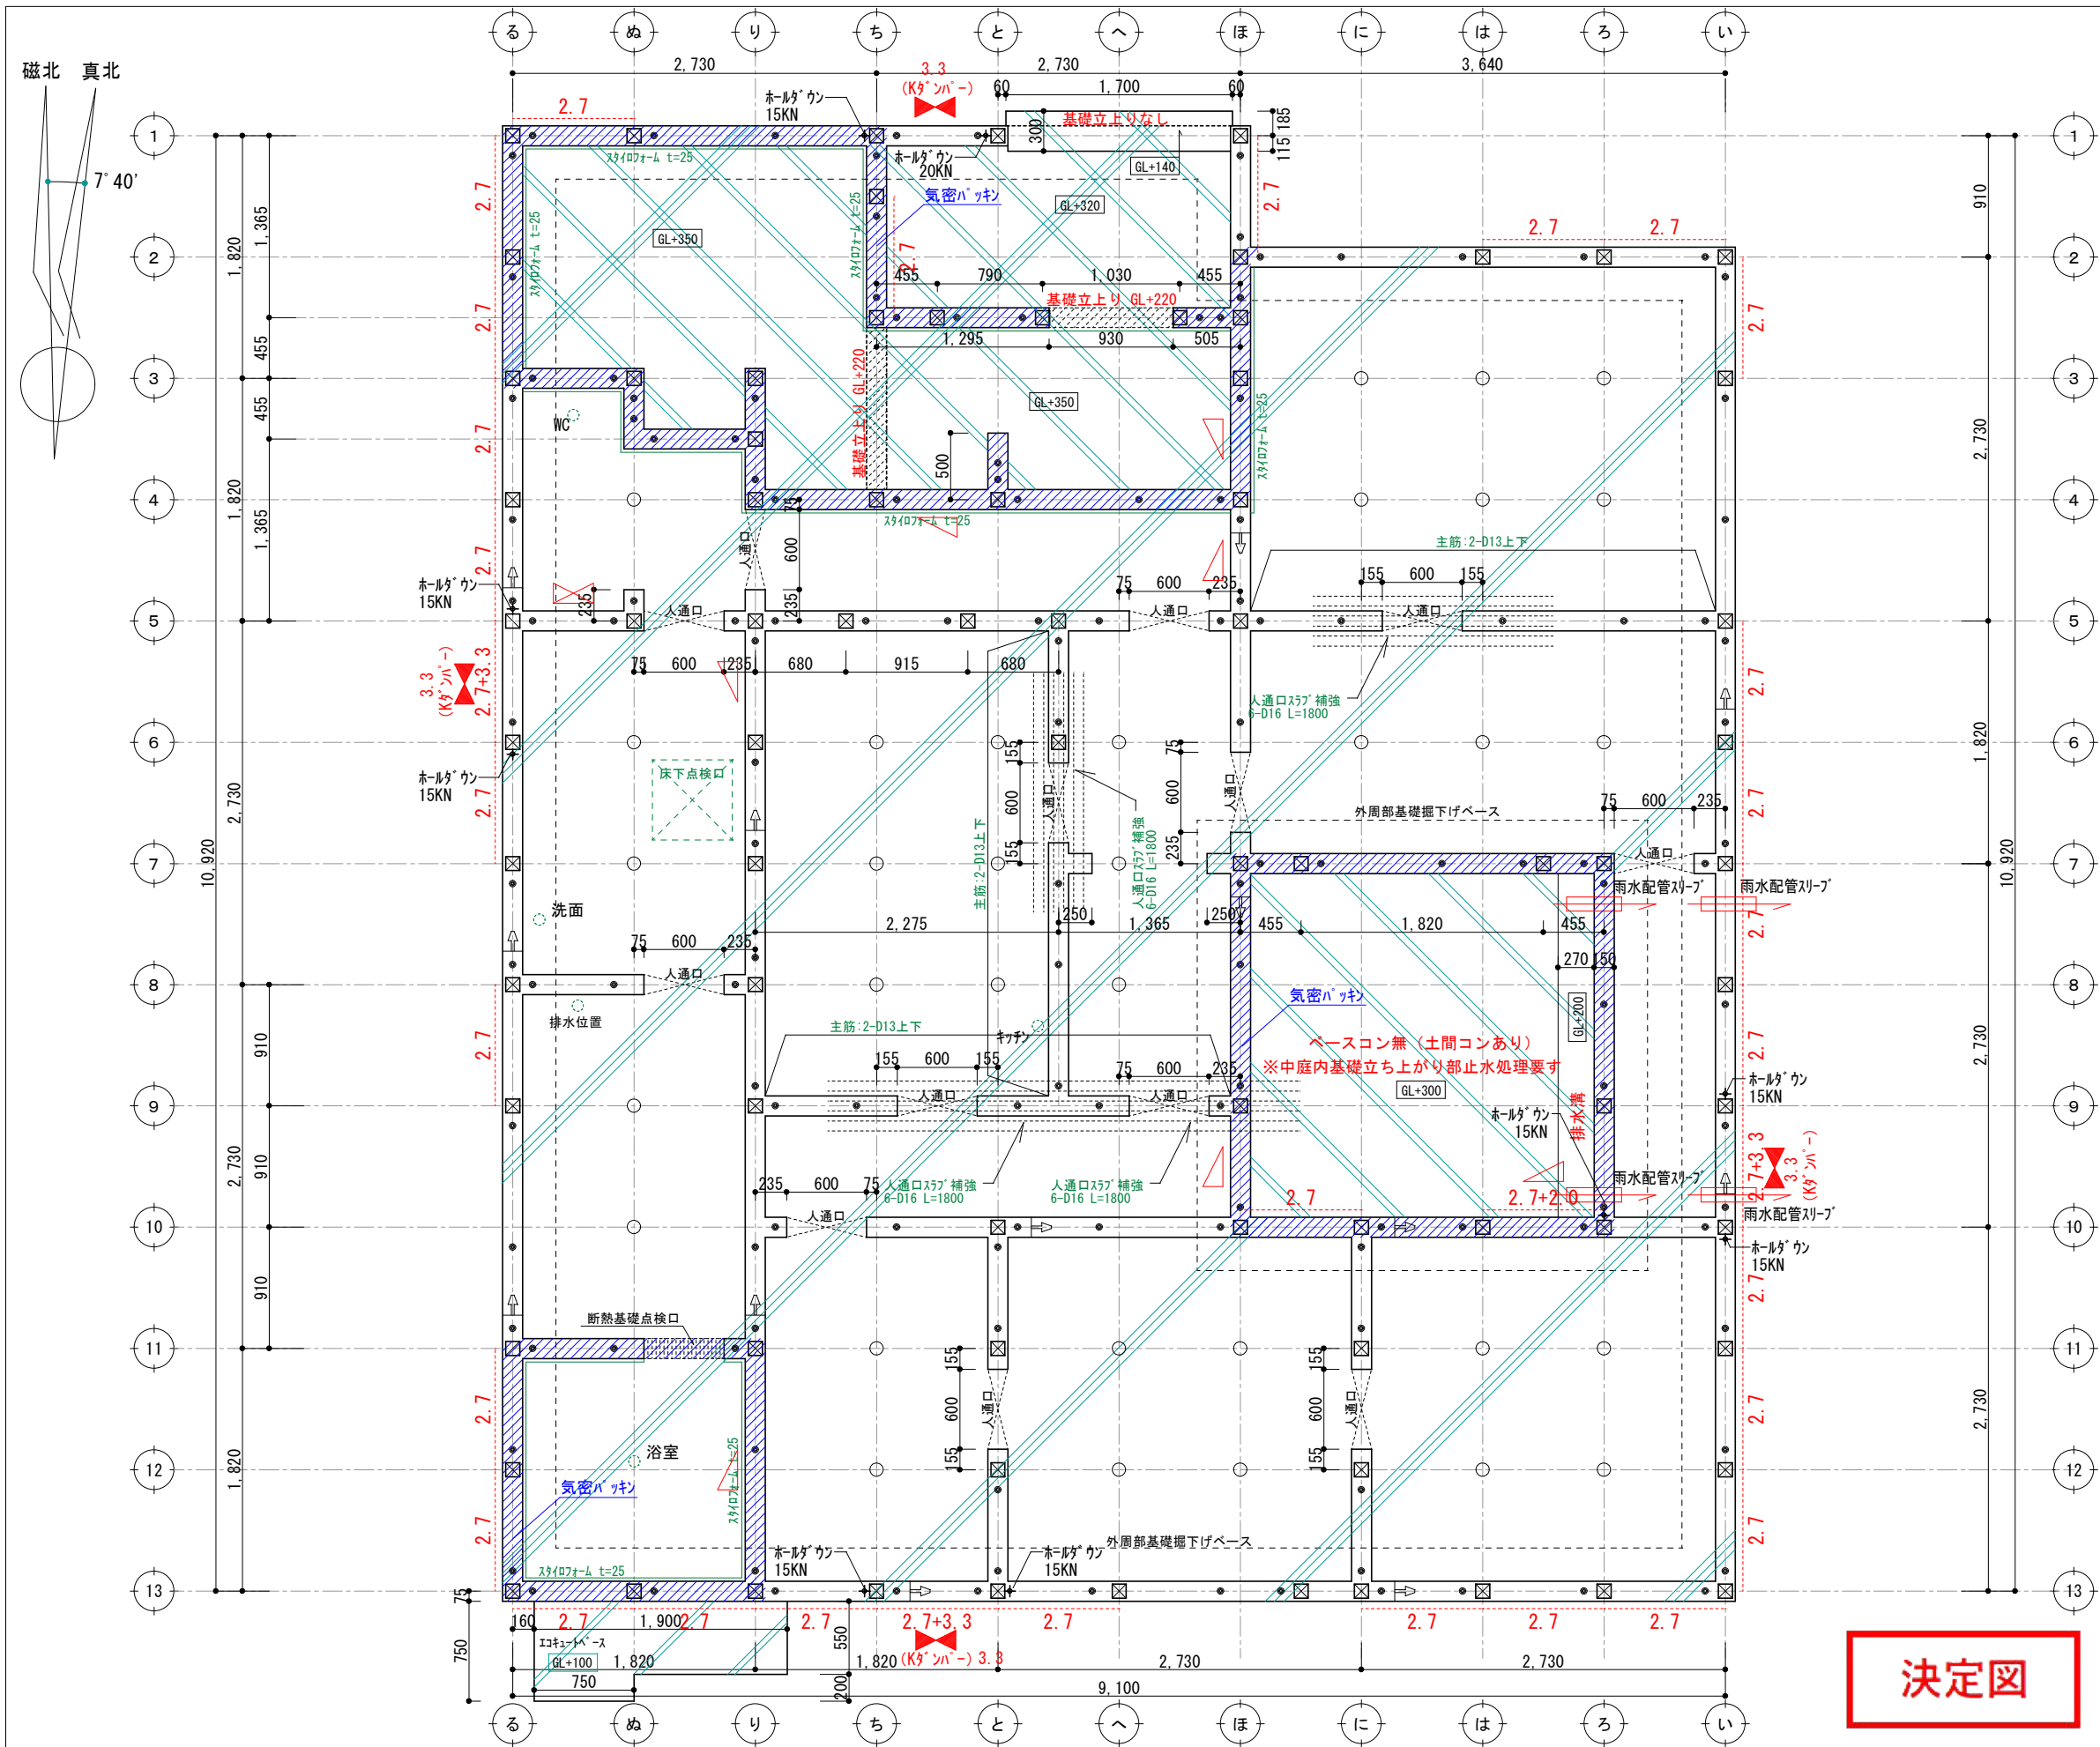


構造体ベースコンクリート t=150

後打ち土間コン

アンカーボルトの配置
土台切れの箇所より150mm
土台の継手及び仕口の端部より150mm
耐力壁の端部、筋交いの脚部より150mm
1.82m以下の間隔
250mm以上埋込み
基礎天端より120mm

筋かい凡例
柱脚 柱頭 片筋かい
たすき掛け筋かい
構造用合板

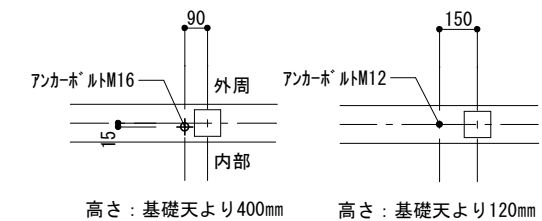

ホールダウンアンカーボルト配置

アンカーボルト配置

凡例	
通し柱 (105*105)	管柱 (105*105)
● アンカーボルトM12 L=400	
+ ホールダウンアンカーM16 L=800	
柱芯より90mm 280mm以上埋め込み (カナフィストアンカーボルトM16)	
⊕ 鋼製束	
└ 土台ジョイント	
▨ ベースコンクリート (t=150)	
▨ 後打ちコンクリート	

基礎伏図について特記なき場合に限り下記による。

1. コンクリート：呼び強度 21N/mm²
2. 鉄筋：SD295A
3. 設計地耐力：fe=30kN/m²
地耐力計測後、不足の場合は相当の改良を行い、満たすものとする。
4. 基礎の位置は、芯振分けとする。
5. 玄関・S/C・UB周囲の基礎天端は気密パッキン施工（網掛け部）とし、その他の基礎天端は基礎パッキン施工とする。
6. 設備配管の屋内への取り入れは基礎立上り部のスリーブによる。