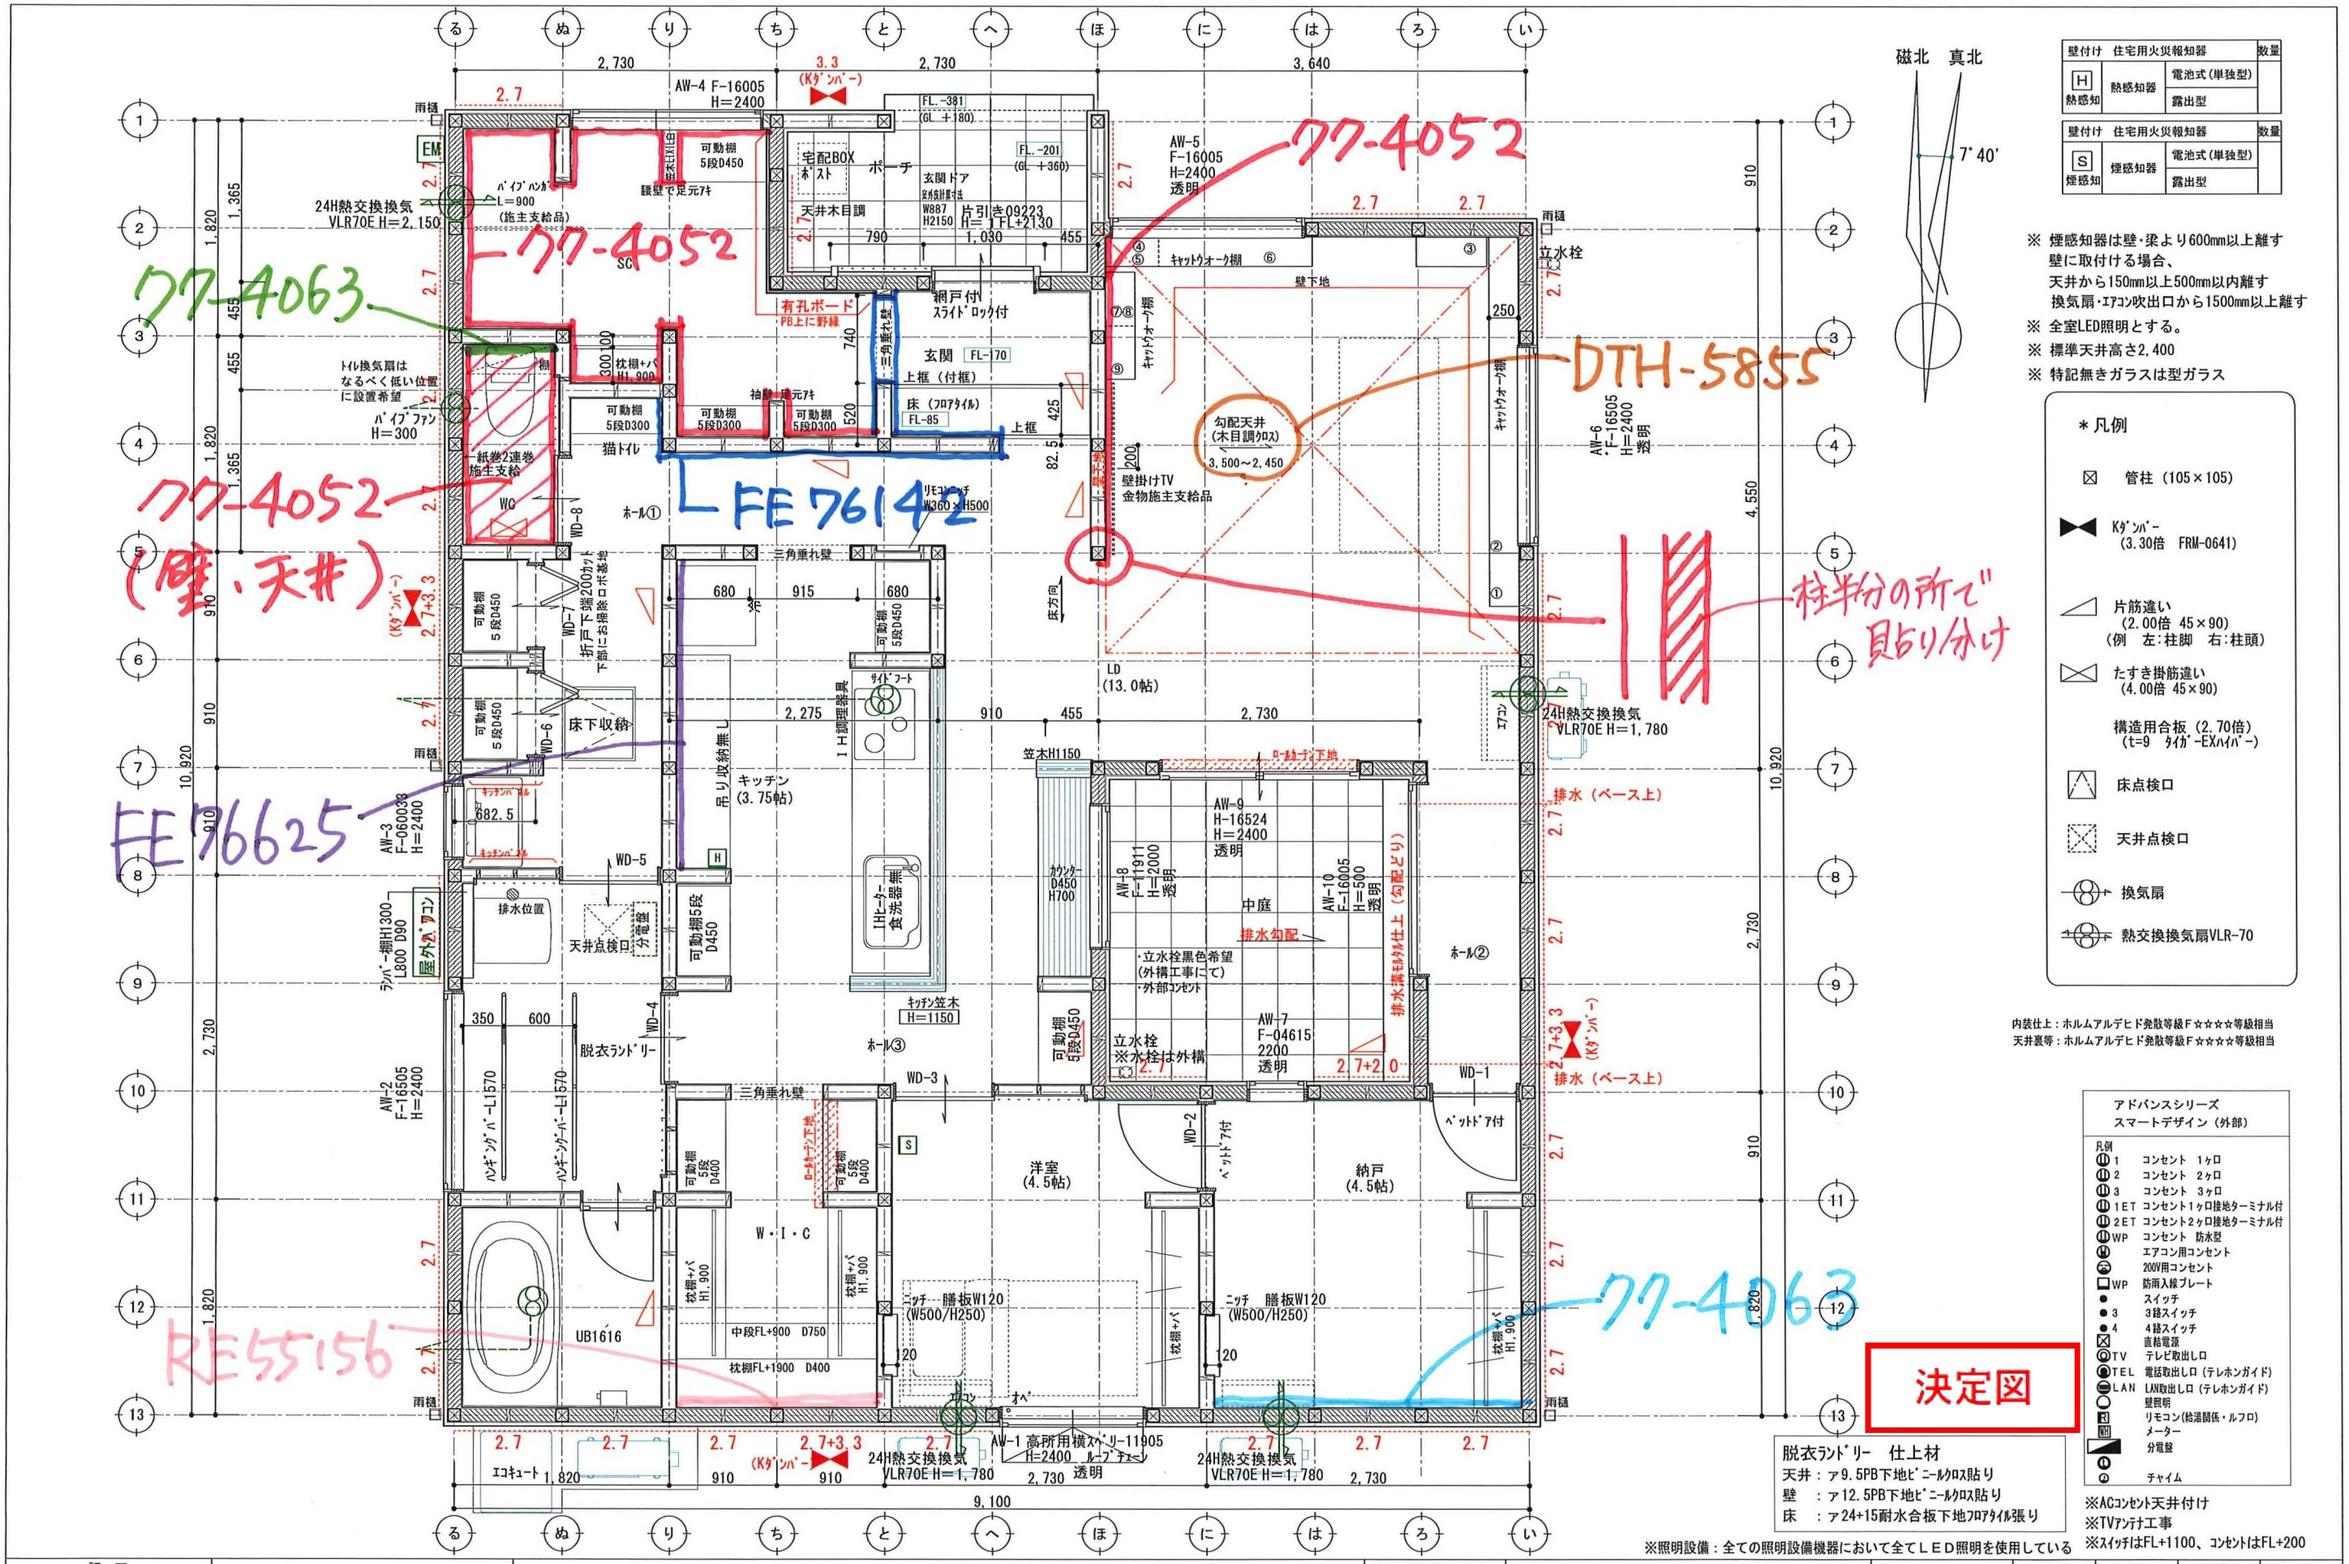


訂正	浜岡一級総合設計事務所 一級建築士事務所 静岡県知事登録第(10)2441号 一級建築士 大臣登録第 365879 号 西原利昌	PG HOUSE ピージーハウス	株式会社 LIFEFUND InDesign office 一級建築士事務所 事務所登録(2)第7595号 一級建築士登録 第179770号 鈴木 達男 〒432-8023 静岡県浜松市中央区鴨江3丁目70番23号	年月日 2025.2.10	件名 鳥山 高広様 みどり様 邸 新築工事	設計	IC	工事	図番
				縮尺 1/50	図名 1階平面図	倉田		青島	3-1