



■ 仕 様			■ HEAT20 G1		
断熱工事		■ 床:カネライトフォーム t65 ■ 土間床等の外周:スタイロフォームAT t25 ■ 壁:アクアフォームLITE吹付 t85 ■ 天井:アクファフォームLITE吹付 t170			
床下換気		■ 基礎パッキン JOTO (玄関・UB周り:気密基礎パッキン)			
防虫防蟻		■ 土壌処理・木部 ガントナーMC			
■ 外 部 仕 上 表			■ 22条地域		
部位		仕上・仕様・メーカー		色番・品番	
屋根		■ ガルバリウム鋼板(t0.35)UK立平 ニスクカラーPro GH 軒先通気金物 日本住環境株式会社【REV-15】		GHK01 Sブラック	
パラペット笠木		■			
破風・鼻隠		■ なし			
雨樋	(軒樋)	■ Panasonic サーフeskエアFS-I型		ブラック	
	(縦樋)	■ Panasonic S30角樋		ブラック	
軒天	屋根軒天	■			
	ポーチ軒	■ ニチハ軒天5 木目調 910×1820×5		ミディアム	
	バルコニー軒	■			
オーバーハング水切り		■ ガルバリウム鋼板 ※外壁合わせ JOTO:HF-A3550		ブラック	
外壁 通気金物(15mm) ※下地面材:タイガーEXハイパー 防火認定 PC030BE-4028	■メイン	ケイミュー エクセレージ光セラ15 シマンフラット		ラントチタン モスグレー	
	■中庭外壁	ケイミュー エクセレージ光セラ15 シマンフラット		ラントチタン ライトグレー	
	■アクセントB	なし			
玄関ポーチ 中庭テラス		■ 床 LIXILパセオ300/PSO-BR 2		-	
基礎		■ 立上り巾木: モルタル刷毛引き		-	
基礎水切り金物		■ JOTO鋼板製 防鼠材付き水切り JOTO:WMF-N35		ブラック	
バルコニー	床・内壁				
	笠木				
外部建具		■ LIXIL EW(アルゴンガス高遮熱仕様LowE複層ガラス クリーン) ・SD、TSで記載がないものは、オペレーターハンドルとする ・オペレーター付サッシは固定網戸とする ・グレモンハンドル式サッシの選択箇所は可動網戸とする		外観 ブラック 内観 シャドーオーク ※網戸付	
シャッター		■ なし			
軒天通気金物		日本住環境株式会社 SEV-15			
玄関扉		■ LIXIL エルムーブ2(引き戸) LIXILファミロック タグキー×3 (電池式) スライドロック付仕様		ドア型: L16型 ドア色: チーク浮造 ハンドル: 色 ブラック	
外部物干し金物		■			
換気フード	■ 局所換気扇(トイレ 浴室 キッチンフード) 防火ダンパー無		外気フード: ブラック		
	■ ダクトレス熱交換換気システム (日本スティーベル株式会社) VLR-70E 防火ダンパー無		外気フード: B ブラック 室内パネル ホワイト		

■ 構 造 概 要					
基礎	■ RCベタ基礎コンクリート				
通し柱・管柱	■ 構造用集成材 105×105		間柱	■ 集成材	
土台	■ 桧 105×105	大引き	■ 桧 90*90	筋交い	■ 構造用製材 火打梁 ■ 鋼製火打(当社基準により米松あり)
桁・梁	■ 構造用製材及び集成材		制震装置	■ Kダンパー (株)アイ・エム・エー	
■ 設 備 装 着 品					
住宅設備	部位	メーカー	商品名 ※ 詳細は見積り、プレゼン参照	見積りNo.	(日付)
	キッチン	LIXIL	■ ES I型D650	見積り番号 : M24125865946-006-2 (日付) 2024.12.23	
	バックカウンタ ※オプション	LIXIL	■ ES L1800(W900スライドストッカー+マルチスペース)	見積り番号 : M24125865946-006-3 (日付) 2024.12.23	
	浴室	LIXIL	■ AX1616 ●扉 開き戸タイプ	見積り番号 : M24125865946-006-1 (日付) 2024.12.23	
	1Fトイレ	LIXIL	■ ベーシアシャワートイレ 白 ● タオル掛け:なし タンク手洗 無し ● 紙巻き器: なし(支給品取付)	見積り番号 : M24125865946-006-6 (日付) 2024.12.23	
	2Fトイレ	LIXIL			
	洗面台	LIXIL	■ EV W750(D500タイプ) 扉:ディープグレイ [引出しタイプ シングルハンドシャワー スタンドLED三面鏡 ● タオル掛け:なし	見積り番号 : M24125865946-006-4 (日付) 2024.12.23	
		LIXIL	■ 洗面化粧台 両サイド キッチンパネル	M24125865946-006-5 2024.12.23	
給排水設備	給湯器	■ エコキュート370L Panasonic NSシリーズ スタンダードモデル 追い焚きフルオート			
	排水	■ 下水			
	外水栓	■ 2 カ所 (平面図参照)		■ 外部立栓柱: マエザワ12型・中庭は外構工事にて	
	外部ガーデンパン	■ 無し			
	その他	■ 洗濯機用単水栓: 緊急止水弁付 ■ 洗濯機用排水:トラップ金物(標準) ■ 排水さや管(長期優良住宅仕様)			
ガス配管設備	■ なし (平面図参照)				
電気設備	インターホン	■ パナソニック VL-SZ30KL			
	TVアンテナ	■ UHF + BS・110度CS/CSアンテナ [2K・4K・8K対応] ■ホワイト			
	エアコン	■ なし 設置場所:			
	ソーラー	■ あり(Qセルズ) 12 枚 5.28 KW Re.RISE-G3 440 (1722×1134×30)			
	※標準搭載	屋外パワコン ■ 蓄電池:無			
その他					

決定図

決定図

	浜 岡 一 級 総 合 設 計 事 務 所 一級建築士事務所 静岡県知事登録第 (10)2441 号 一級建築士 大臣登録第 365879 号 西原利昌	 PG HOUSE 株式会社 LIFEFUND InDesign office 一級建築士事務所 事務所登録 (2)第7595号 一級建築士登録 第179770号 鈴木 達男 〒432-8023 静岡県浜松市中央区鴨江3丁目70番23号	年 月 日	2025.2.14	件名	鳥山高広様みどり様 邸新築工事		設計	IC	工務	図 番
			縮尺		図面	仕上表 1		倉田		青島	1-1

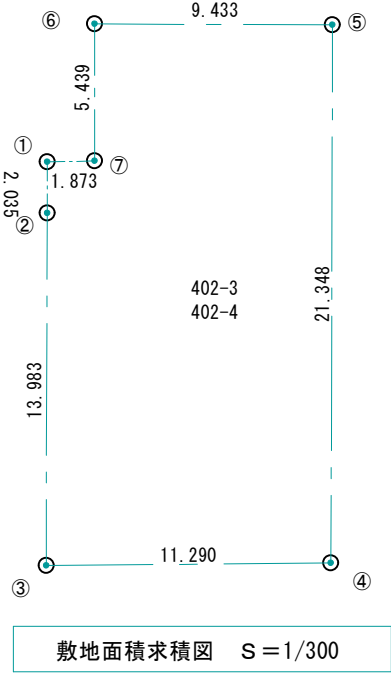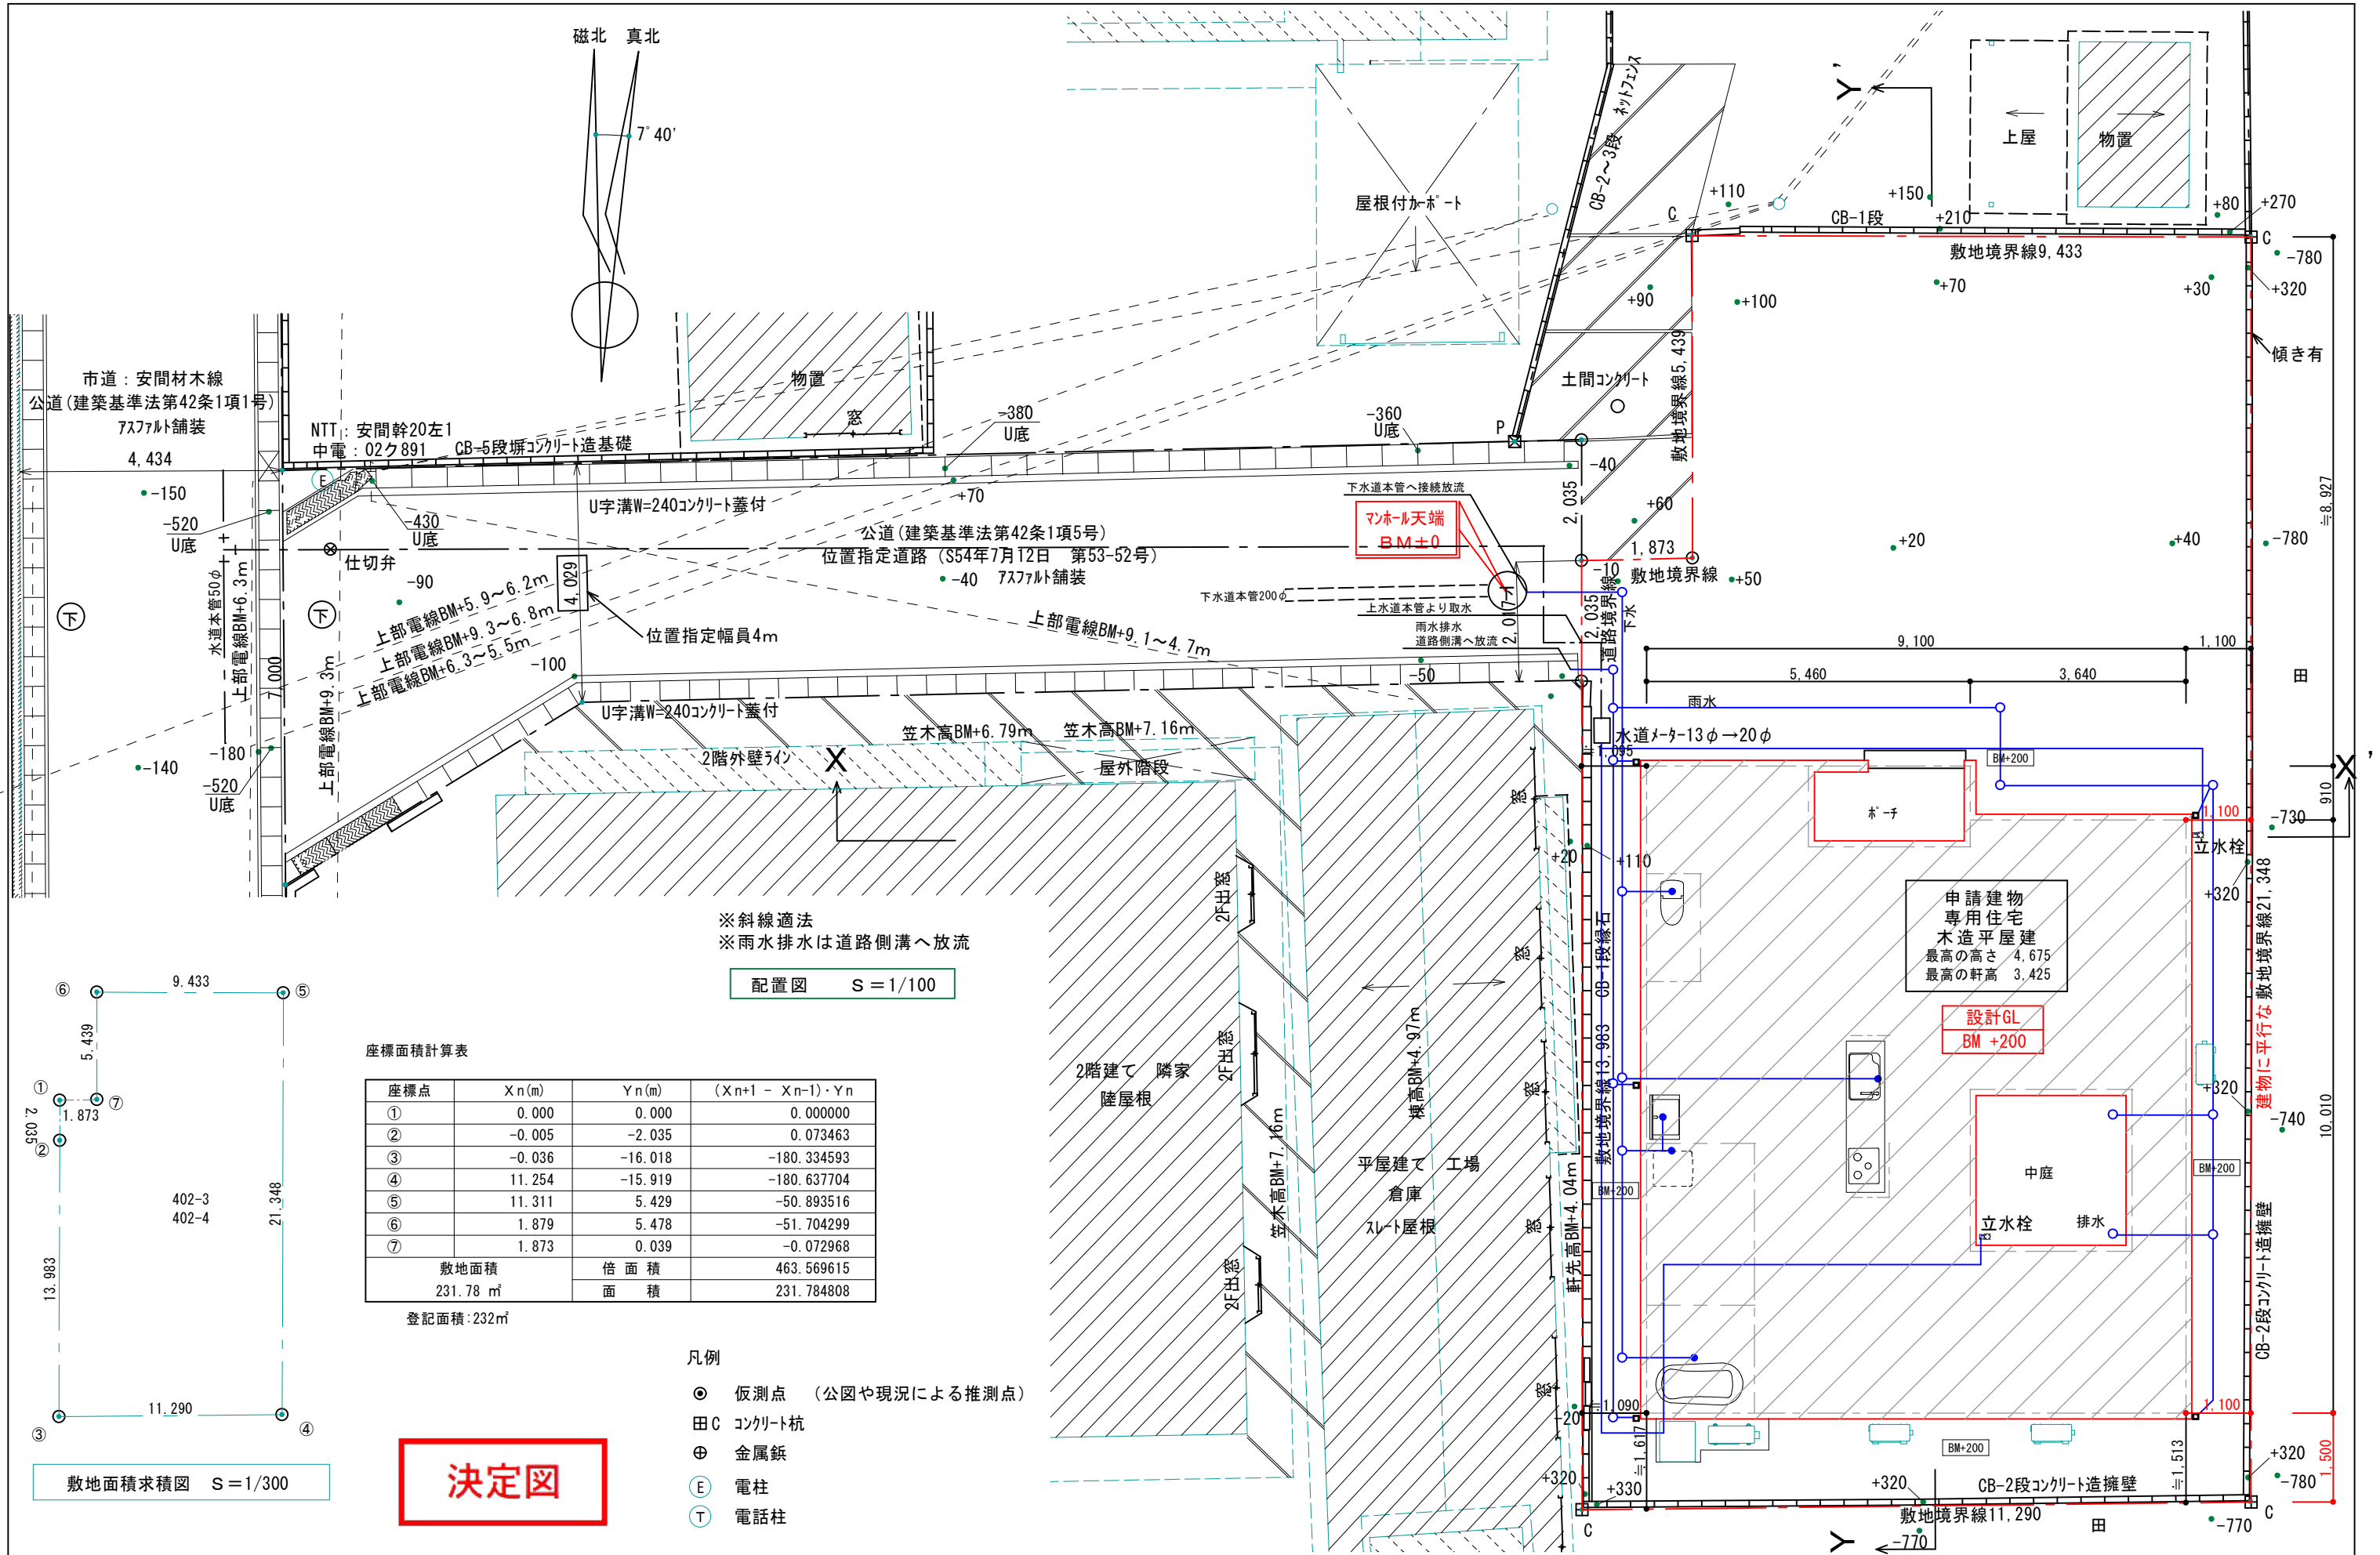


座標面積計算表

座標点	X n (m)	Y n (m)	(X n+1 - X n-1)・Y n
①	0.000	0.000	0.000000
②	-0.005	-2.035	0.073463
③	-0.036	-16.018	-180.334593
④	11.254	-15.919	-180.637704
⑤	11.311	5.429	-50.893516
⑥	1.879	5.478	-51.704299
⑦	1.873	0.039	-0.072968
敷地面積		倍面積	463.569615
231.78 m ²		面積	231.784808

登記面積：232m²

決定図


- 凡例
- 仮測点 (公図や現況による推測点)
 - 田C コンクリート杭
 - ⊕ 金属鈑
 - ⓔ 電柱
 - Ⓣ 電話柱

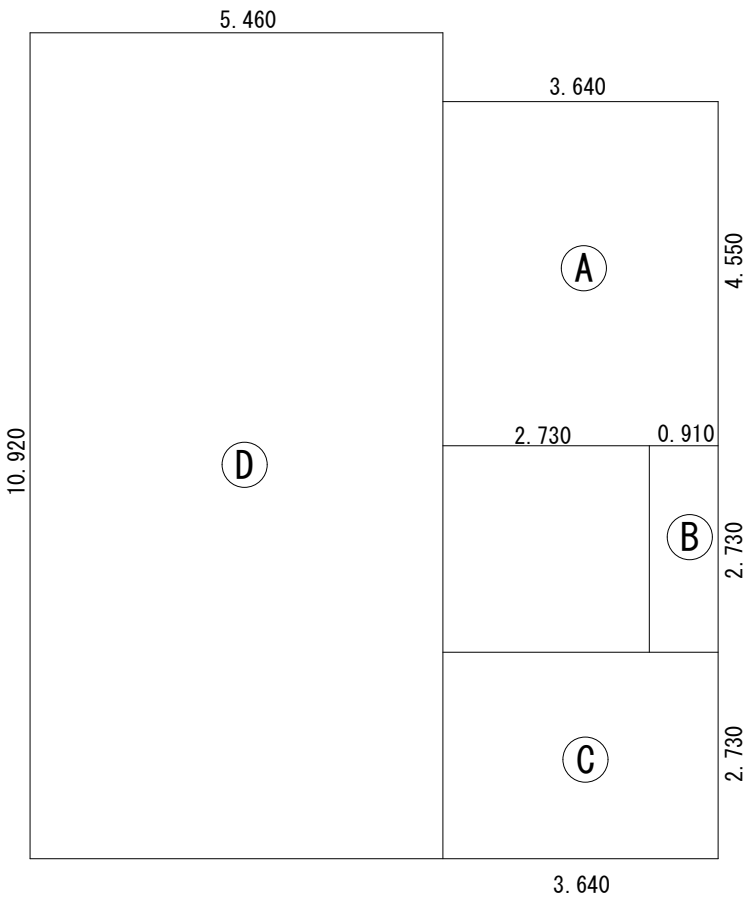

建築面積求積図 S=1/100

建築面積求積表

番号	計算式 (m)	面積 (㎡)
Ⓐ	3.640 × 4.550	16.562
Ⓑ	0.910 × 2.730	2.4843
Ⓒ	3.640 × 2.730	9.9372
Ⓓ	5.460 × 10.920	59.6232
合計 ≡		88.6067 86.60 (26.8坪)

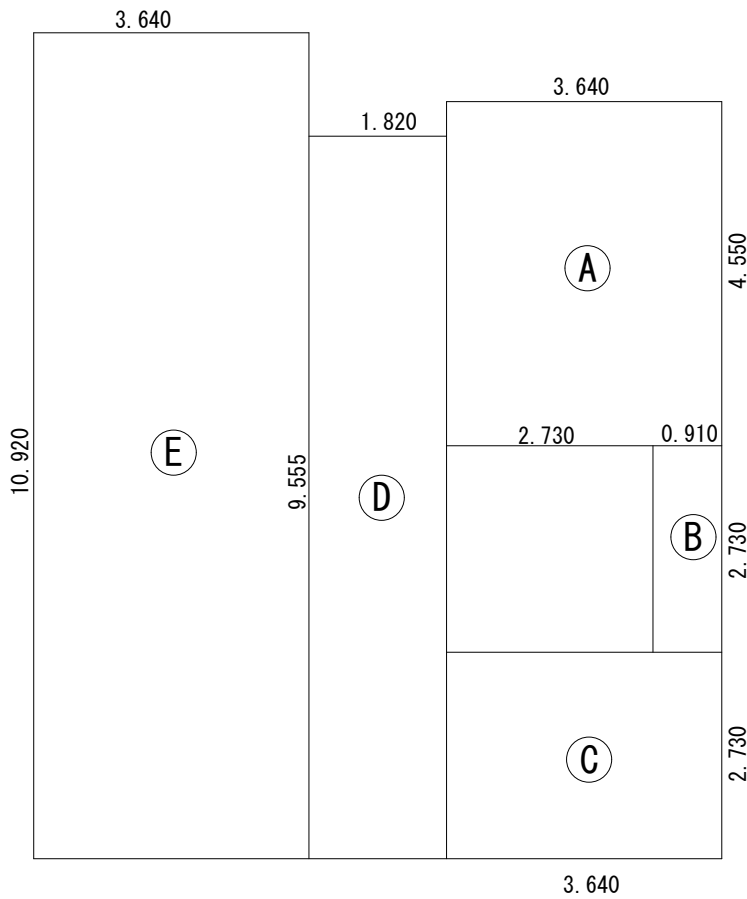


1階床面積図 S=1/100

1階床面積求積表

番号	計算式 (m)	面積 (㎡)
Ⓐ	3.640 × 4.550	16.562
Ⓑ	0.910 × 2.730	2.4843
Ⓒ	3.640 × 2.730	9.9372
Ⓓ	1.820 × 9.555	17.3901
Ⓔ	3.640 × 10.920	39.7488
合計 ≡		86.1224 86.12 (26.0坪)

決定図

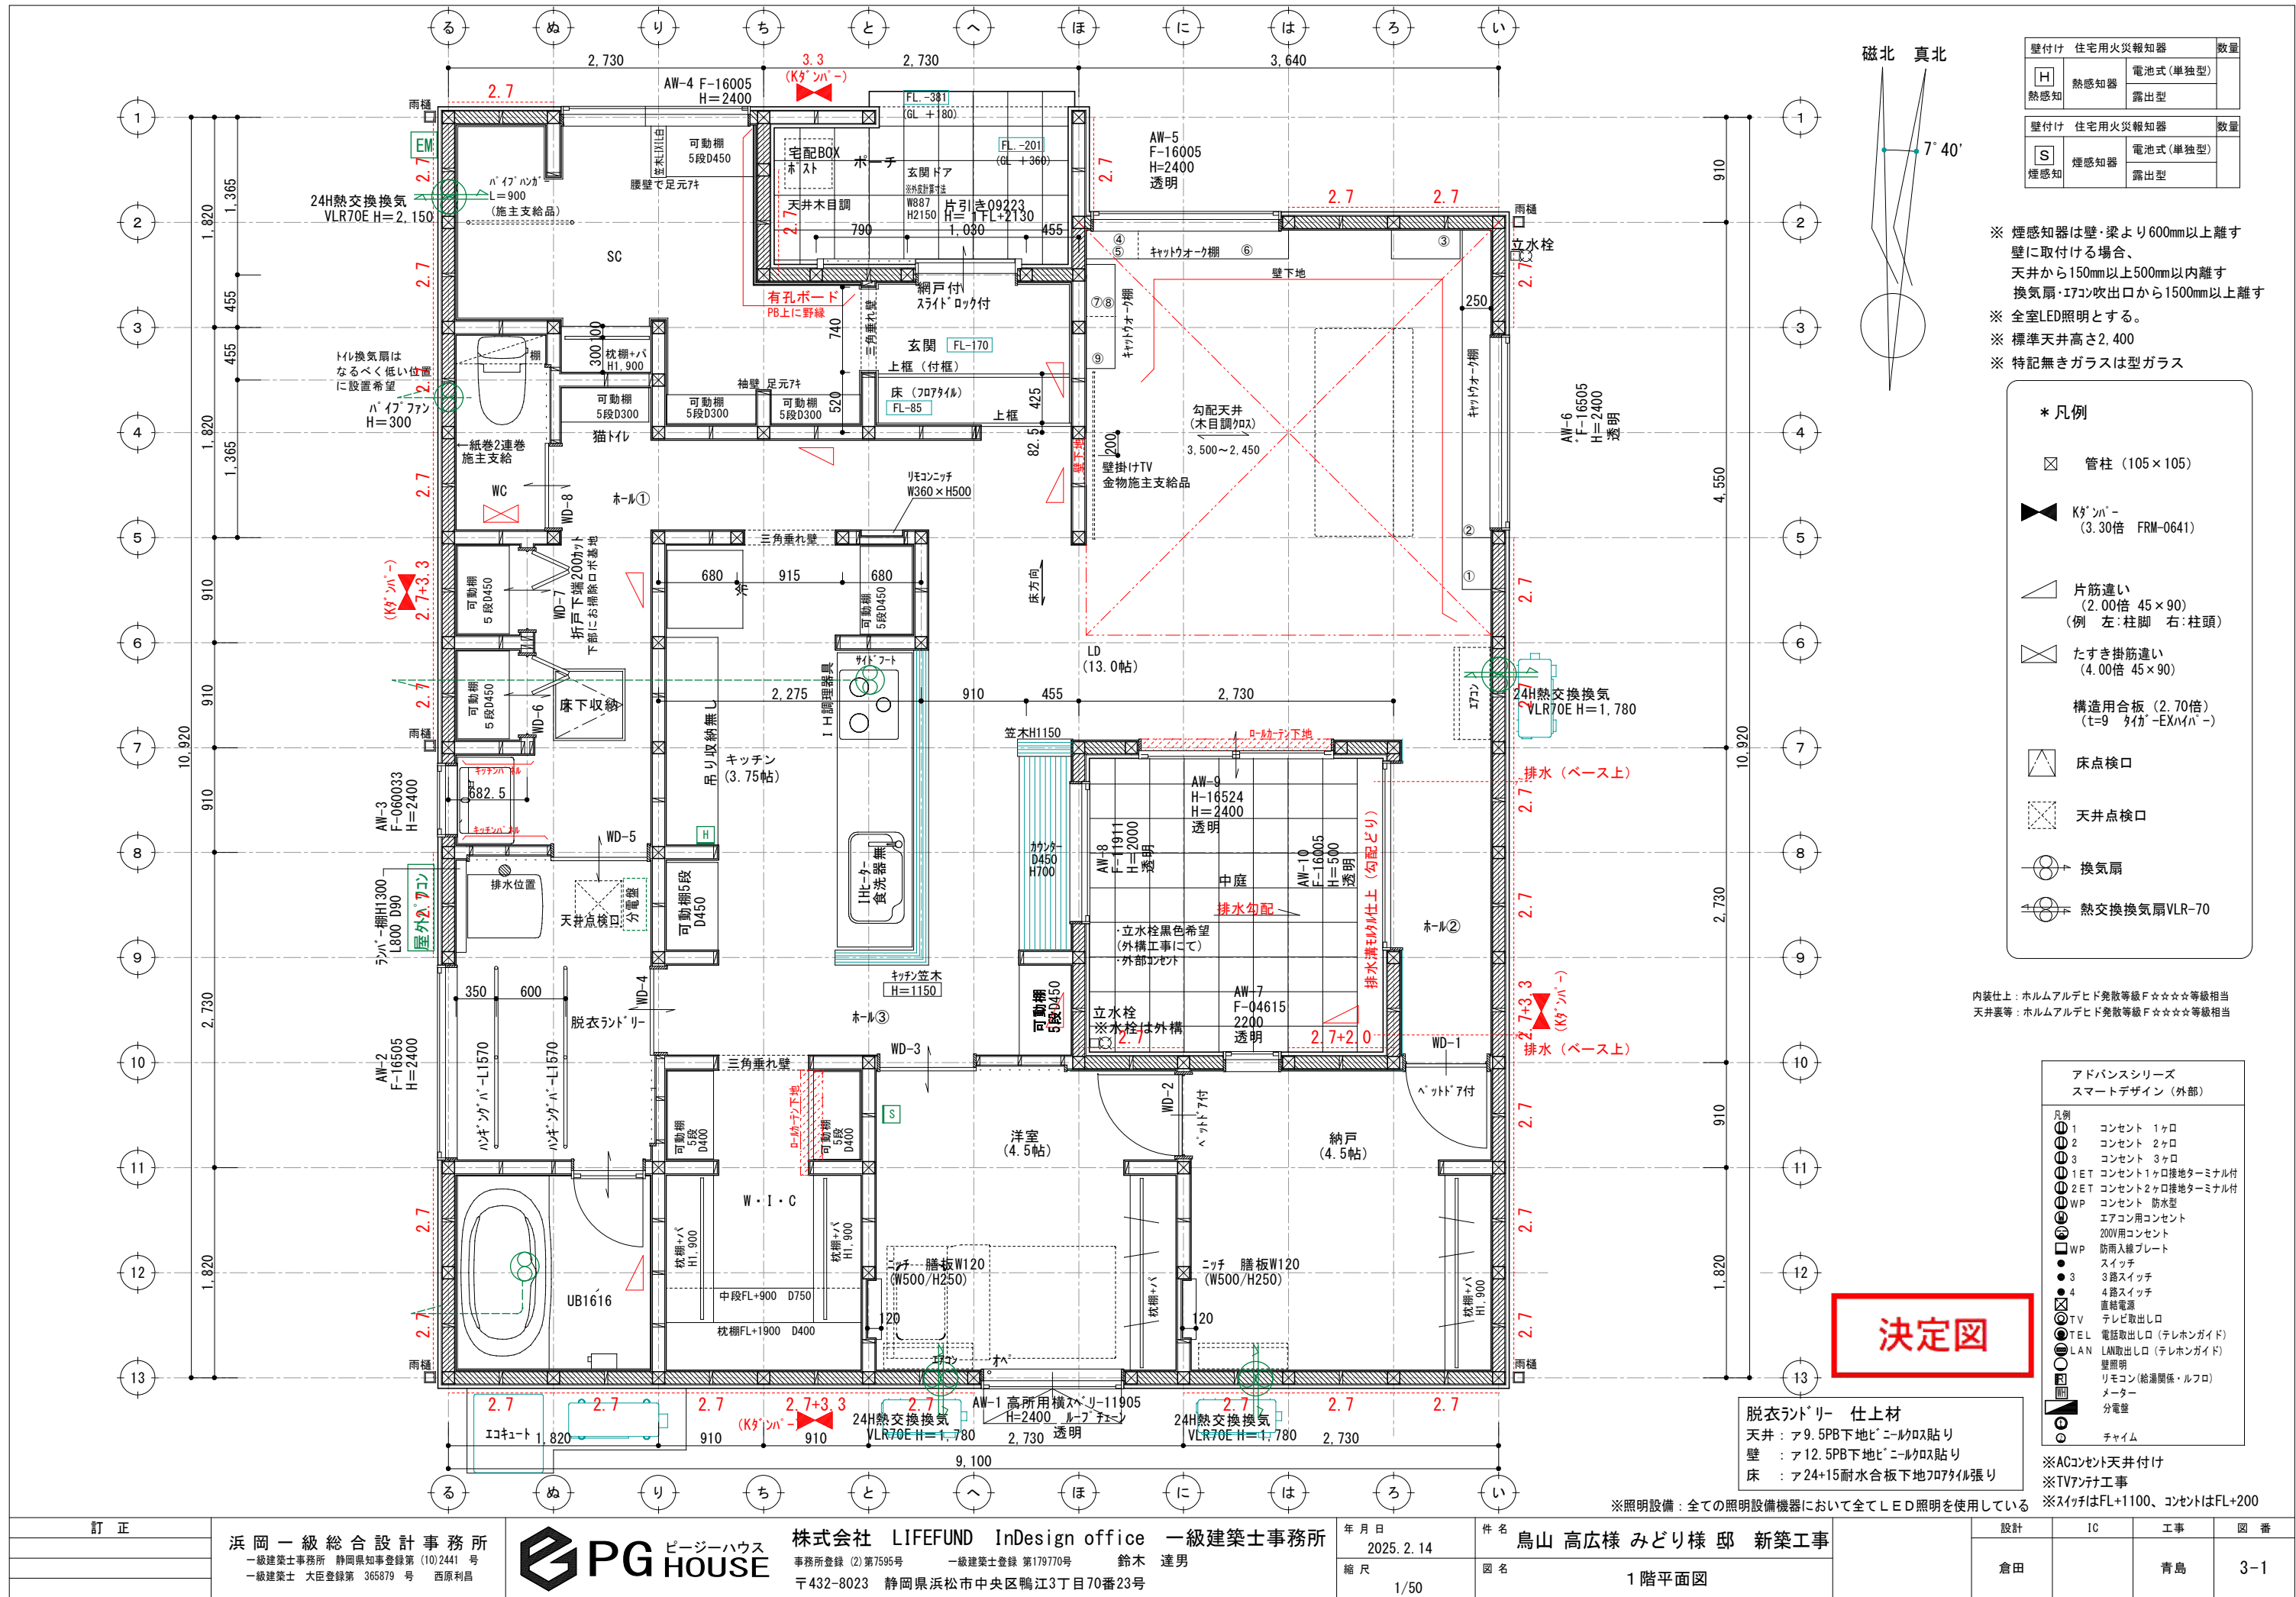

壁付け 住宅用火災報知器			数量
H	熱感知器	電池式(単独型)	
	熱感知器	露出型	
壁付け 住宅用火災報知器			数量
S	煙感知器	電池式(単独型)	
	煙感知器	露出型	

※ 煙感知器は壁・梁より600mm以上離す
壁に取付ける場合、
天井から150mm以上500mm以内離す
換気扇・エアコン吹出口から1500mm以上離す
※ 全室LED照明とする。
※ 標準天井高さ2,400
※ 特記無きガラスは型ガラス

* 凡例

- 管柱 (105×105)
- Kダクト (3.30倍 FRM-0641)
- 片筋違い (2.00倍 45×90)
(例 左:柱脚 右:柱頭)
- たすき掛筋違い (4.00倍 45×90)
- 構造用合板 (2.70倍)
(t=9 9割-EKハイパー)
- 床点検口
- 天井点検口
- 換気扇
- 熱交換換気扇VLR-70

内装仕上：ホルムアルデヒド発散等級F☆☆☆☆等級相当
天井裏等：ホルムアルデヒド発散等級F☆☆☆☆等級相当


アドバンスシリーズ スマートデザイン (外部)

凡例

-  1 コンセント 1ヶ所
-  2 コンセント 2ヶ所
-  3 コンセント 3ヶ所
-  1 ET コンセント1ヶ所接地ターミナル付
-  2 ET コンセント2ヶ所接地ターミナル付
-  WP コンセント 防水型
-  WP エアコン用コンセント
-  WP 200V用コンセント
-  WP 防雨入線プレート
-  スイッチ
-  ● 3路スイッチ
-  ● 4路スイッチ
-  ● 直結電源
-  ● TV テレビ取出口
-  ● TEL 電話取出口 (テレホンガイド)
-  ● LAN LAN取出口 (テレホンガイド)
-  ● 壁照明
-  ● リモコン (給湯関係・ルフロ)
-  ● メーター
-  ● 分電盤
-  ● チャイム

※ACコンセント天井付け
※TVアンテナ工事
※スイッチはFL+1100、コンセントはFL+200


太陽光あり

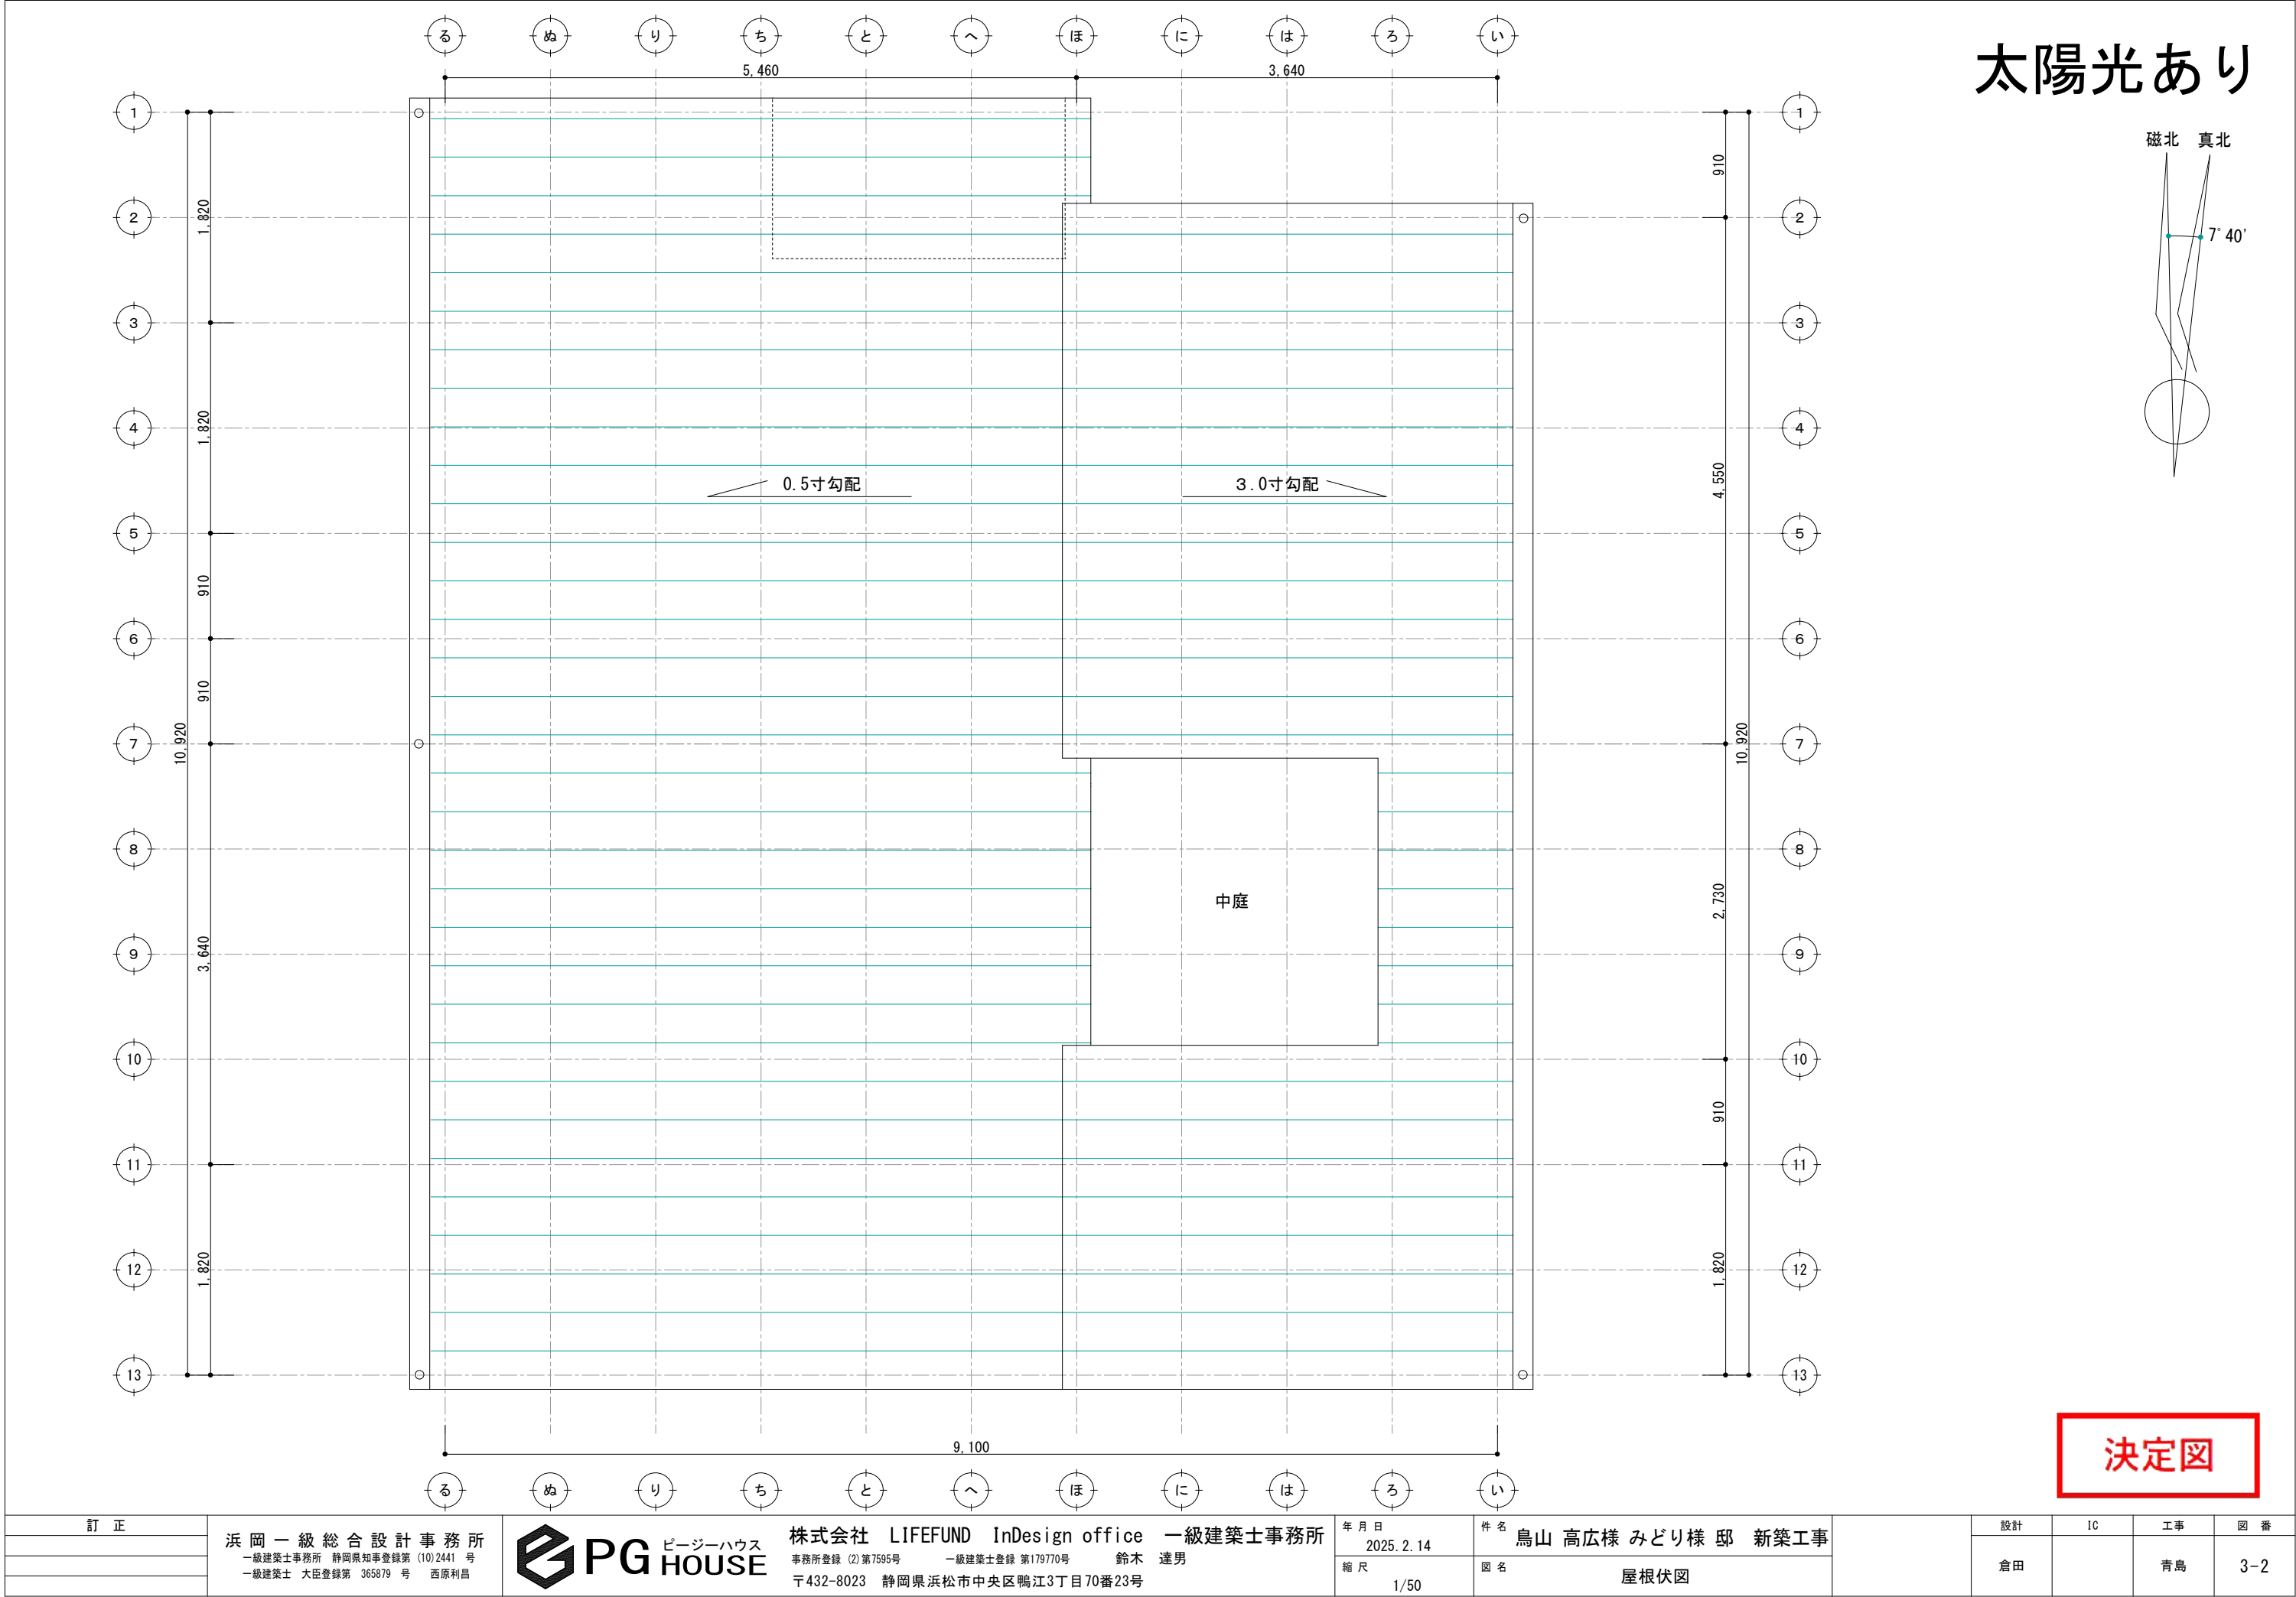

決定図


訂 正	浜 岡 一 級 総 合 設 計 事 務 所 一級建築士事務所 静岡県知事登録第 (10)2441 号 一級建築士 大臣登録第 365879 号 西原利昌		株式会社 LIFEFUND InDesign office 一級建築士事務所 事務所登録 (2) 第7595号 一級建築士登録 第179770号 鈴木 達男 〒432-8023 静岡県浜松市中央区鴨江3丁目70番23号	年 月 日 2025. 2. 14	件 名 鳥山 高広様 みどり様 邸 新築工事	設計	IC	工事	図 番			
				縮 尺 1/50	図 名 屋根伏図					倉田	青島	3-2

太陽光搭載あり

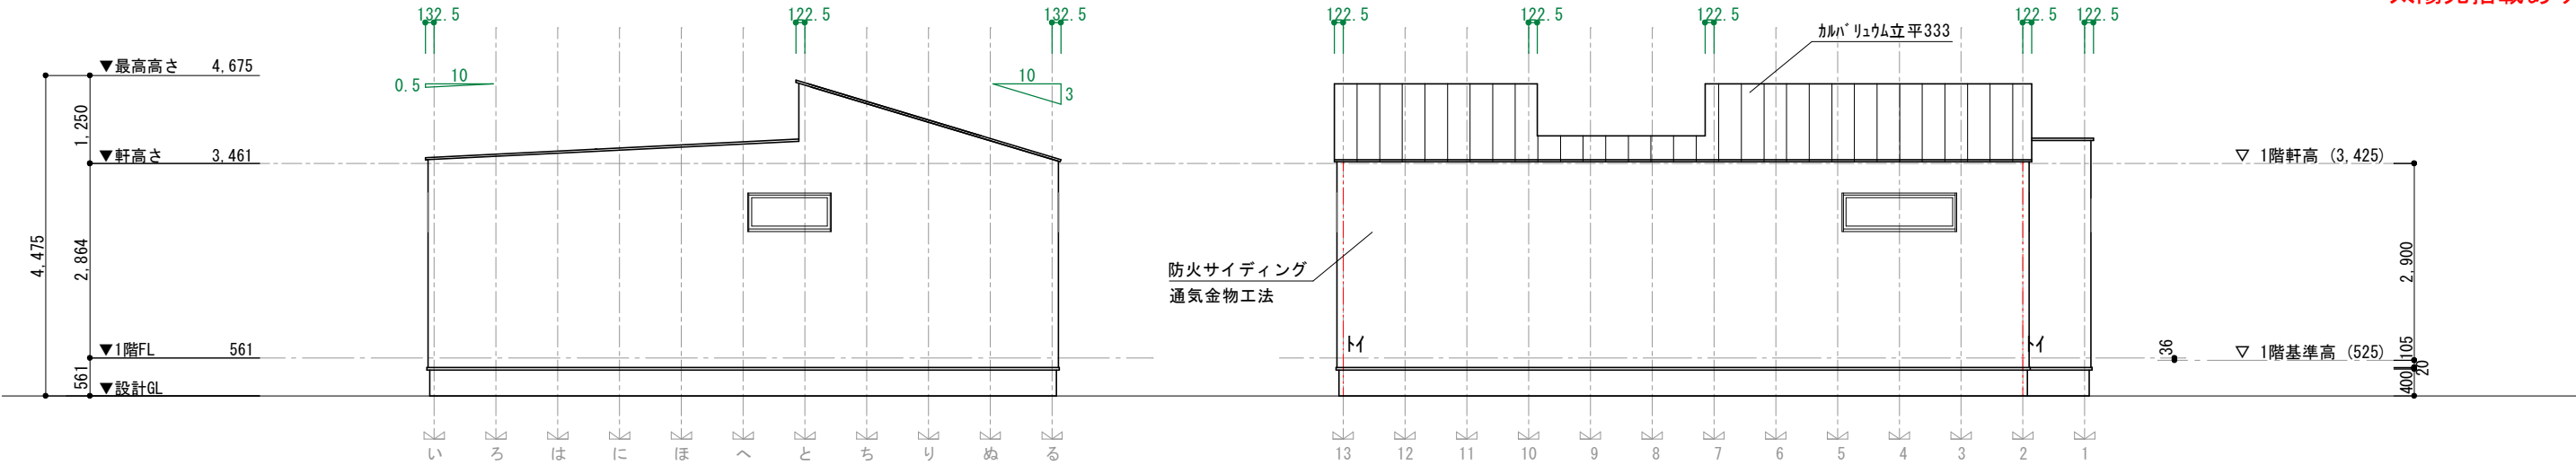


南側立面図 S=1/100

東側立面図 S=1/100

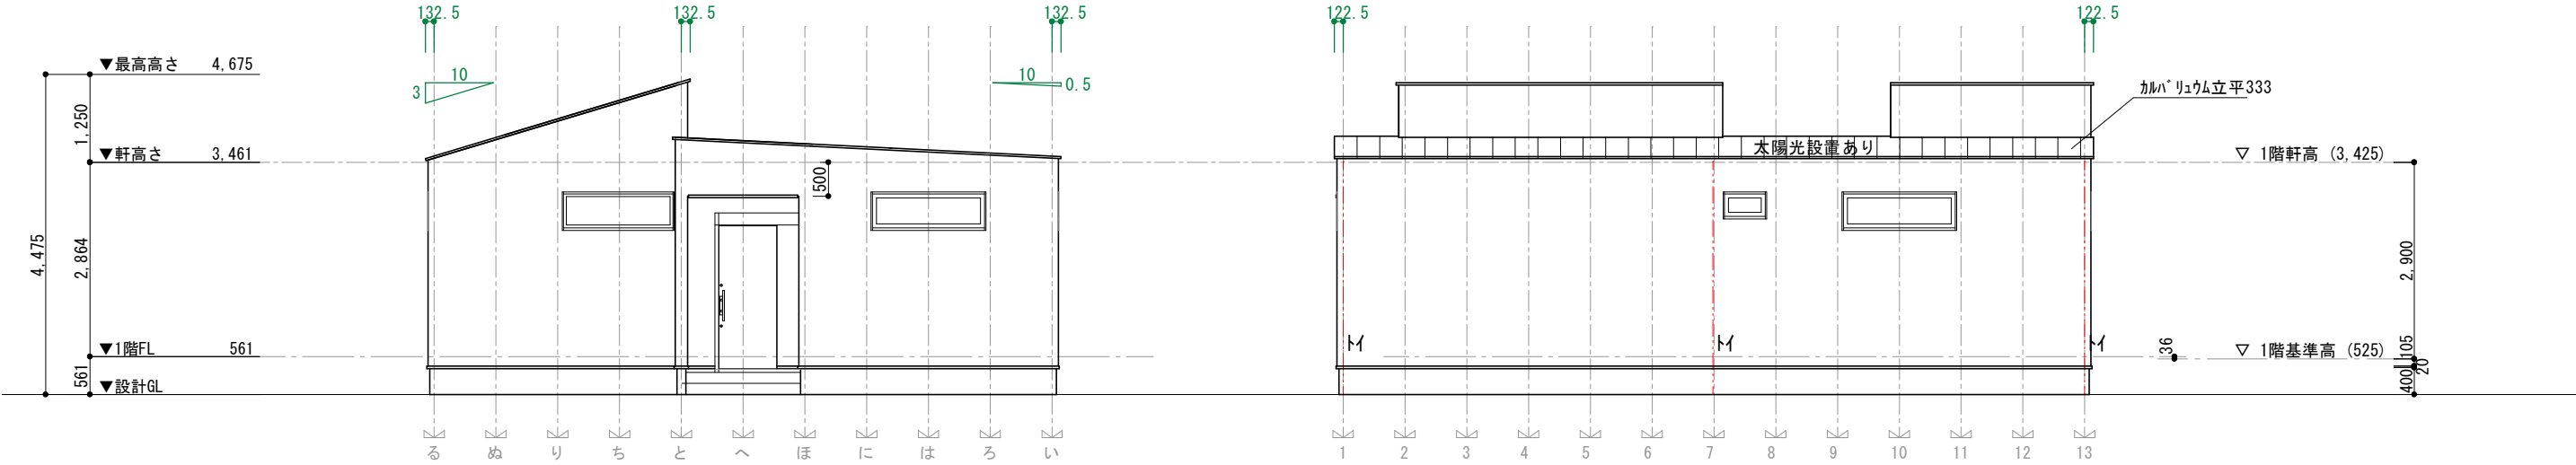

北側立面図 S=1/100

西側立面図 S=1/100

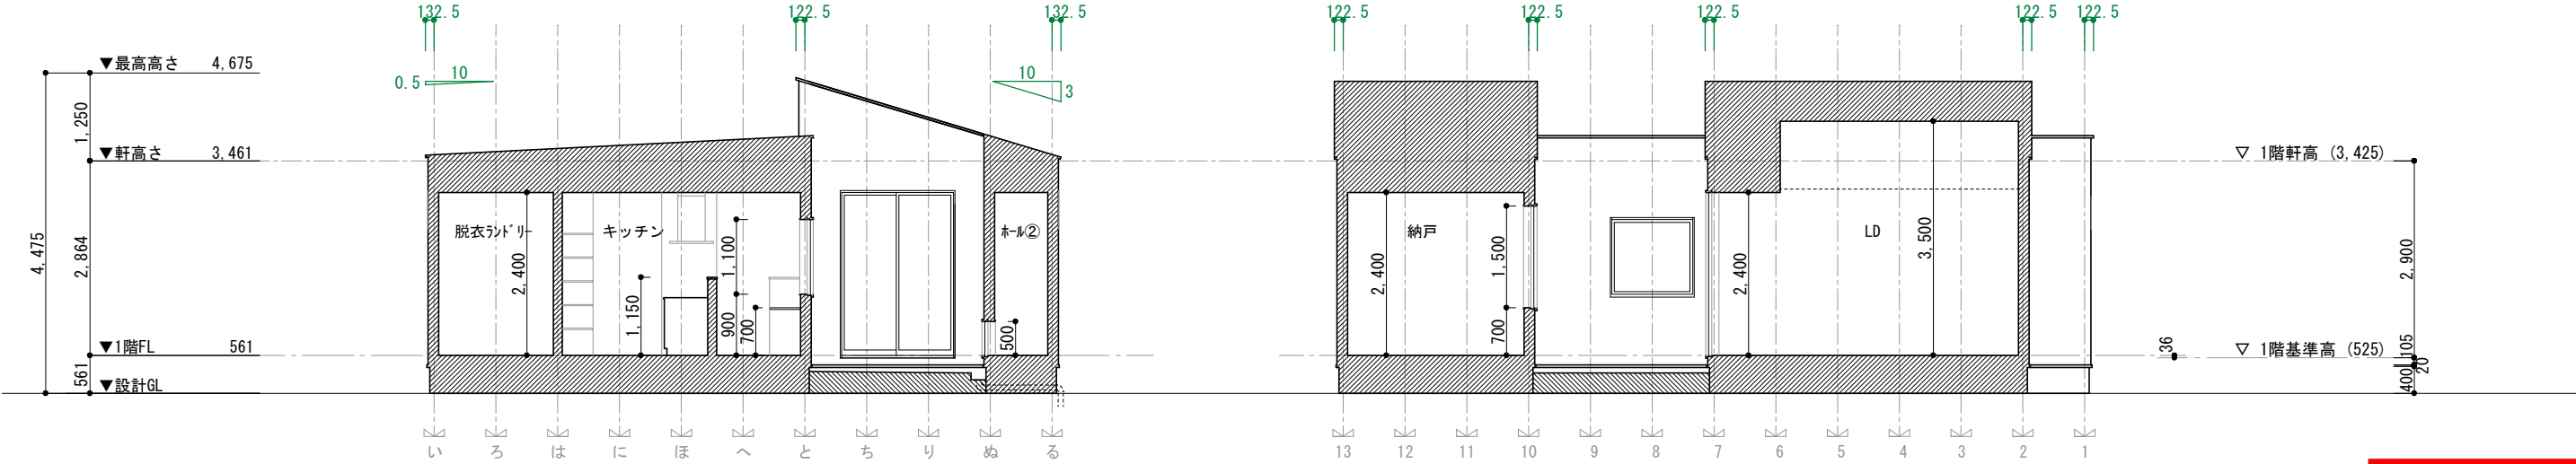


南側断面図 S=1/100 (中庭南立面)

東側断面図 S=1/100 (中庭東立面)


決定図

訂 正	浜 岡 一 級 総 合 設 計 事 務 所 一級建築士事務所 静岡県知事登録第 (10)2441 号 一級建築士 大臣登録第 365879 号 西原利昌		 PG HOUSE	株式会社 LIFEFUND InDesign office 一級建築士事務所 事務所登録 (2) 第7595号 一級建築士登録 第179770号 鈴木 達男 〒432-8023 静岡県浜松市中央区鴨江3丁目70番23号		年 月 日 2025. 2. 14	件 名 鳥山 高広様 みどり様 邸 新築工事	設計	IC	工事	図 番	
				縮 尺 1/100	図 名 立面図	倉田	青島					4

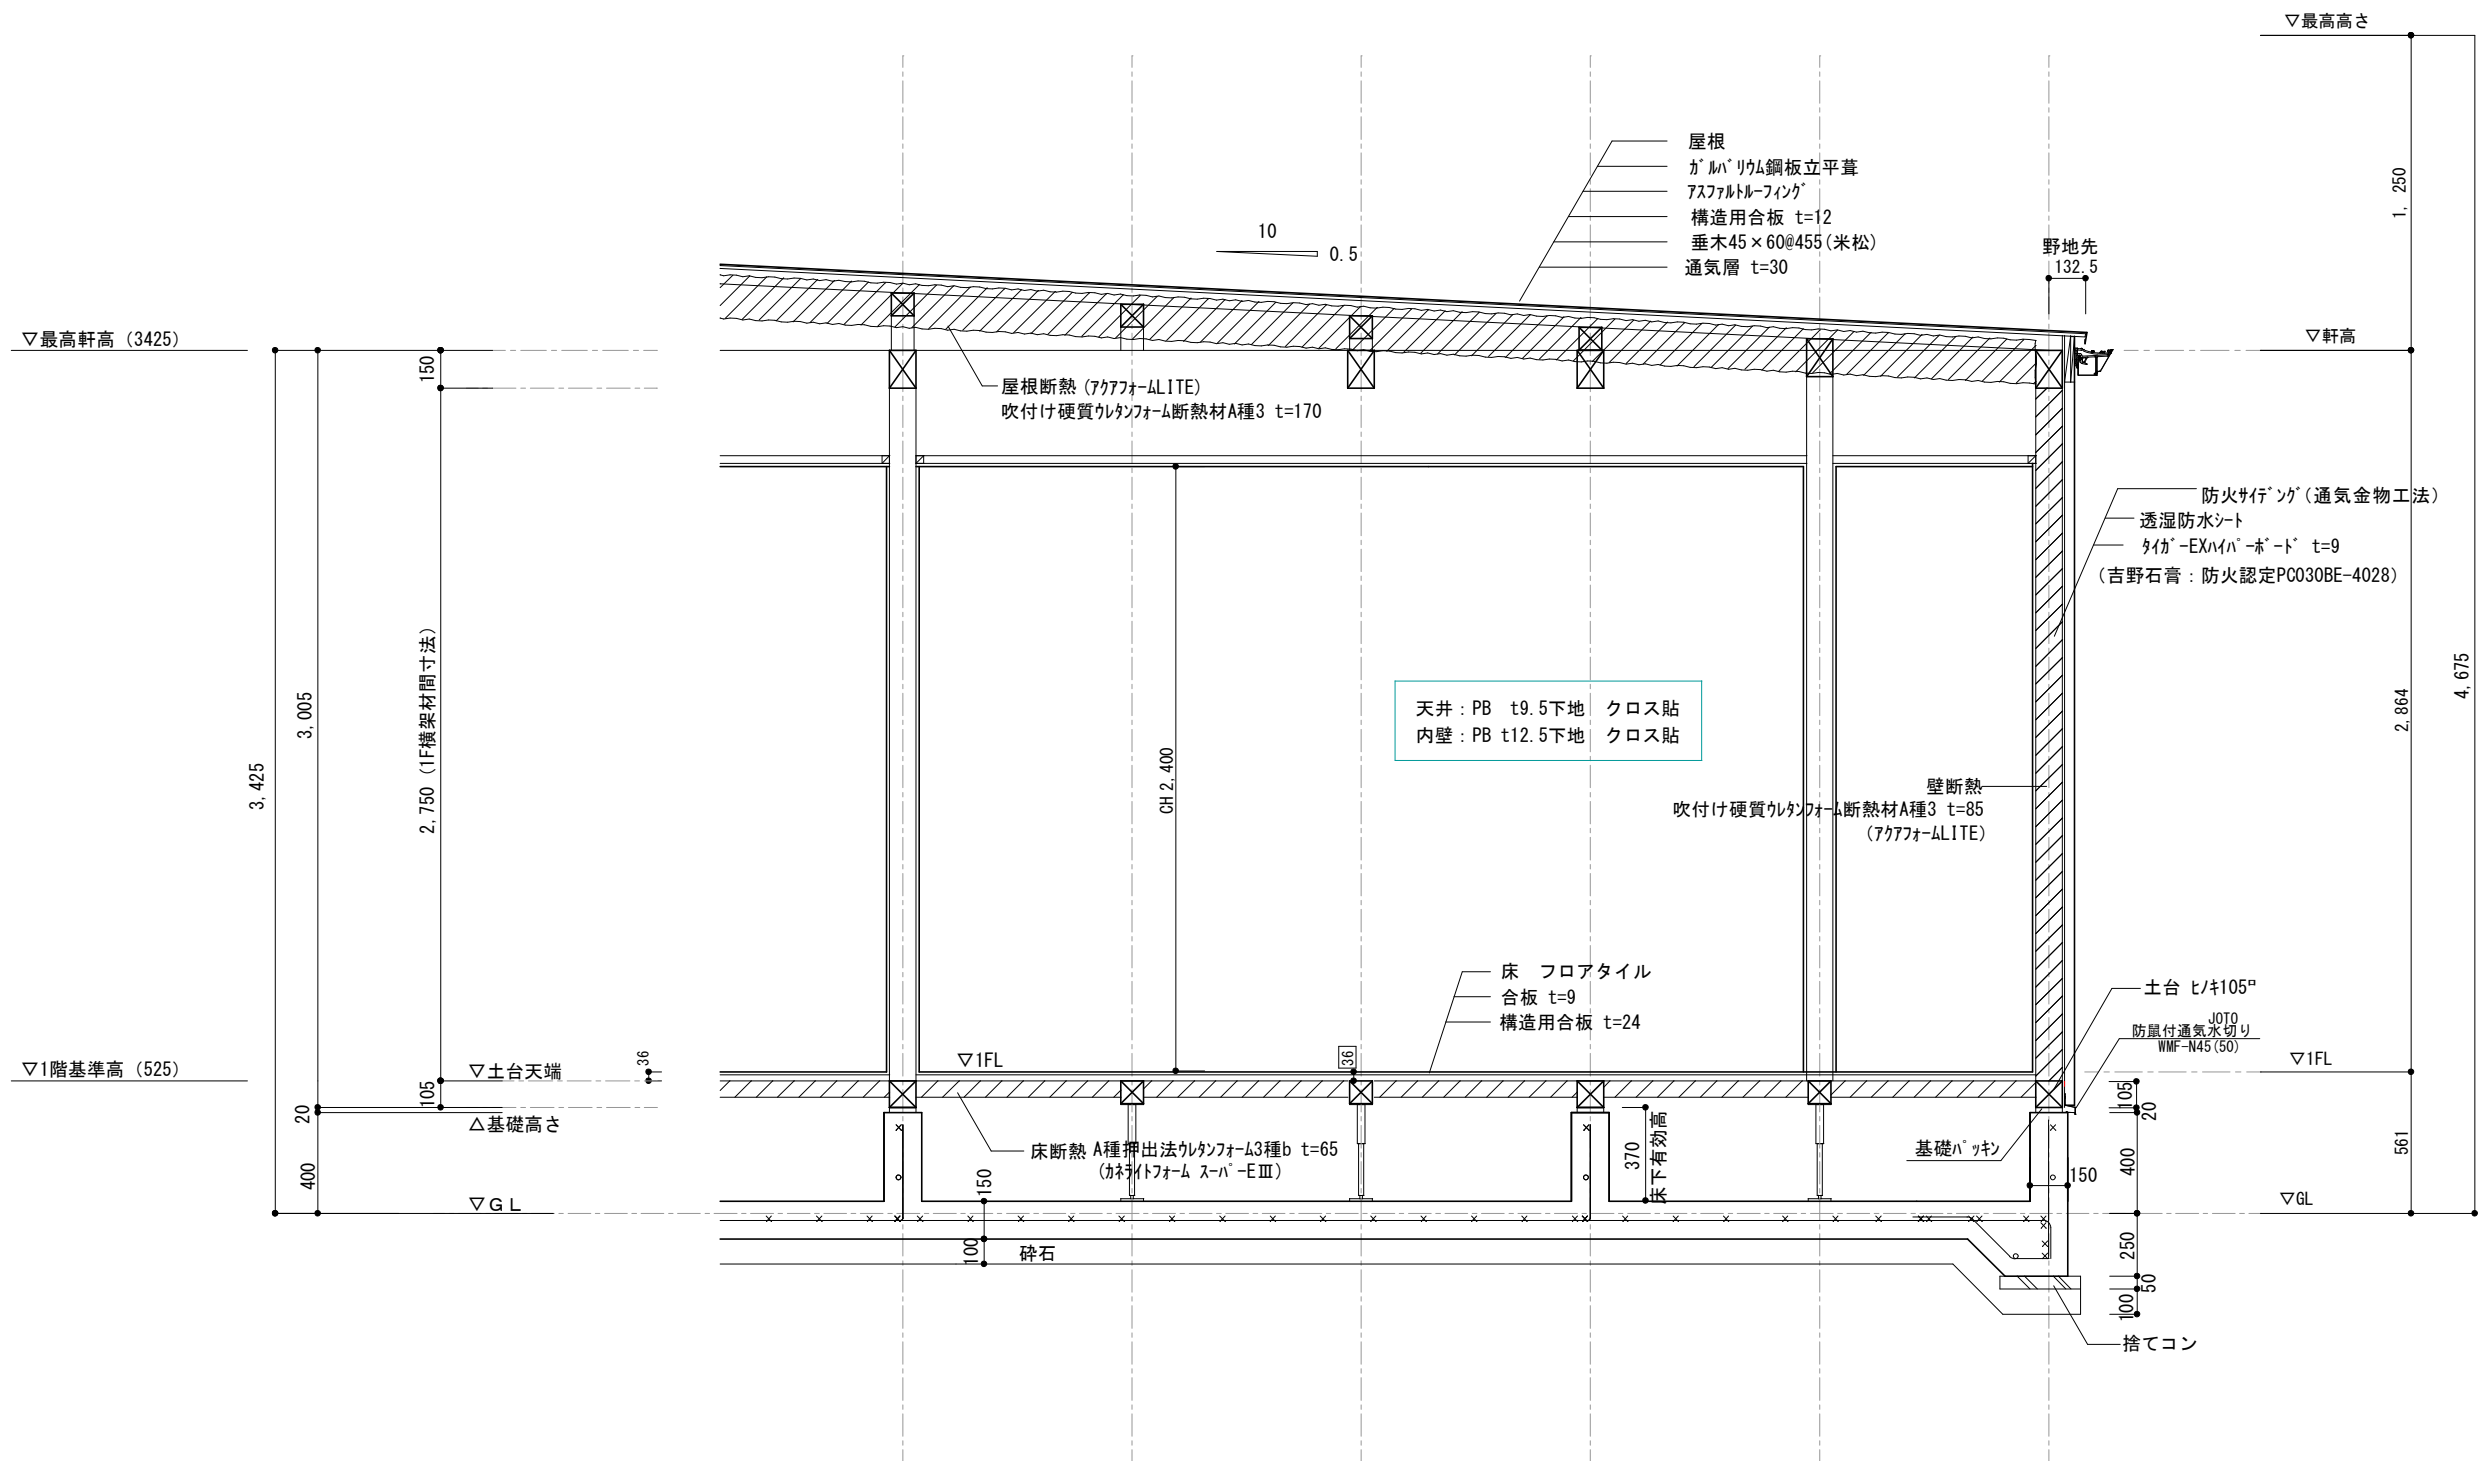


決定図

訂正	浜岡一級総合設計事務所 一級建築士事務所 静岡県知事登録第 (10)2441 号 一級建築士 大臣登録第 365879 号 西原利昌	PG HOUSE ピージーハウス	株式会社 LIFEFUND InDesign office 一級建築士事務所 事務所登録 (2) 第7595号 一級建築士登録 第179770号 鈴木 達男 〒432-8023 静岡県浜松市中央区鴨江3丁目70番23号	年月日 2025. 2. 14 縮尺 1/30	件名 鳥山 高広様 みどり様 邸新築工事 図名 矩計図	設計 倉田	IC	工事 青島	図番 5
----	--	---------------------	---	----------------------------------	--------------------------------------	----------	----	----------	---------

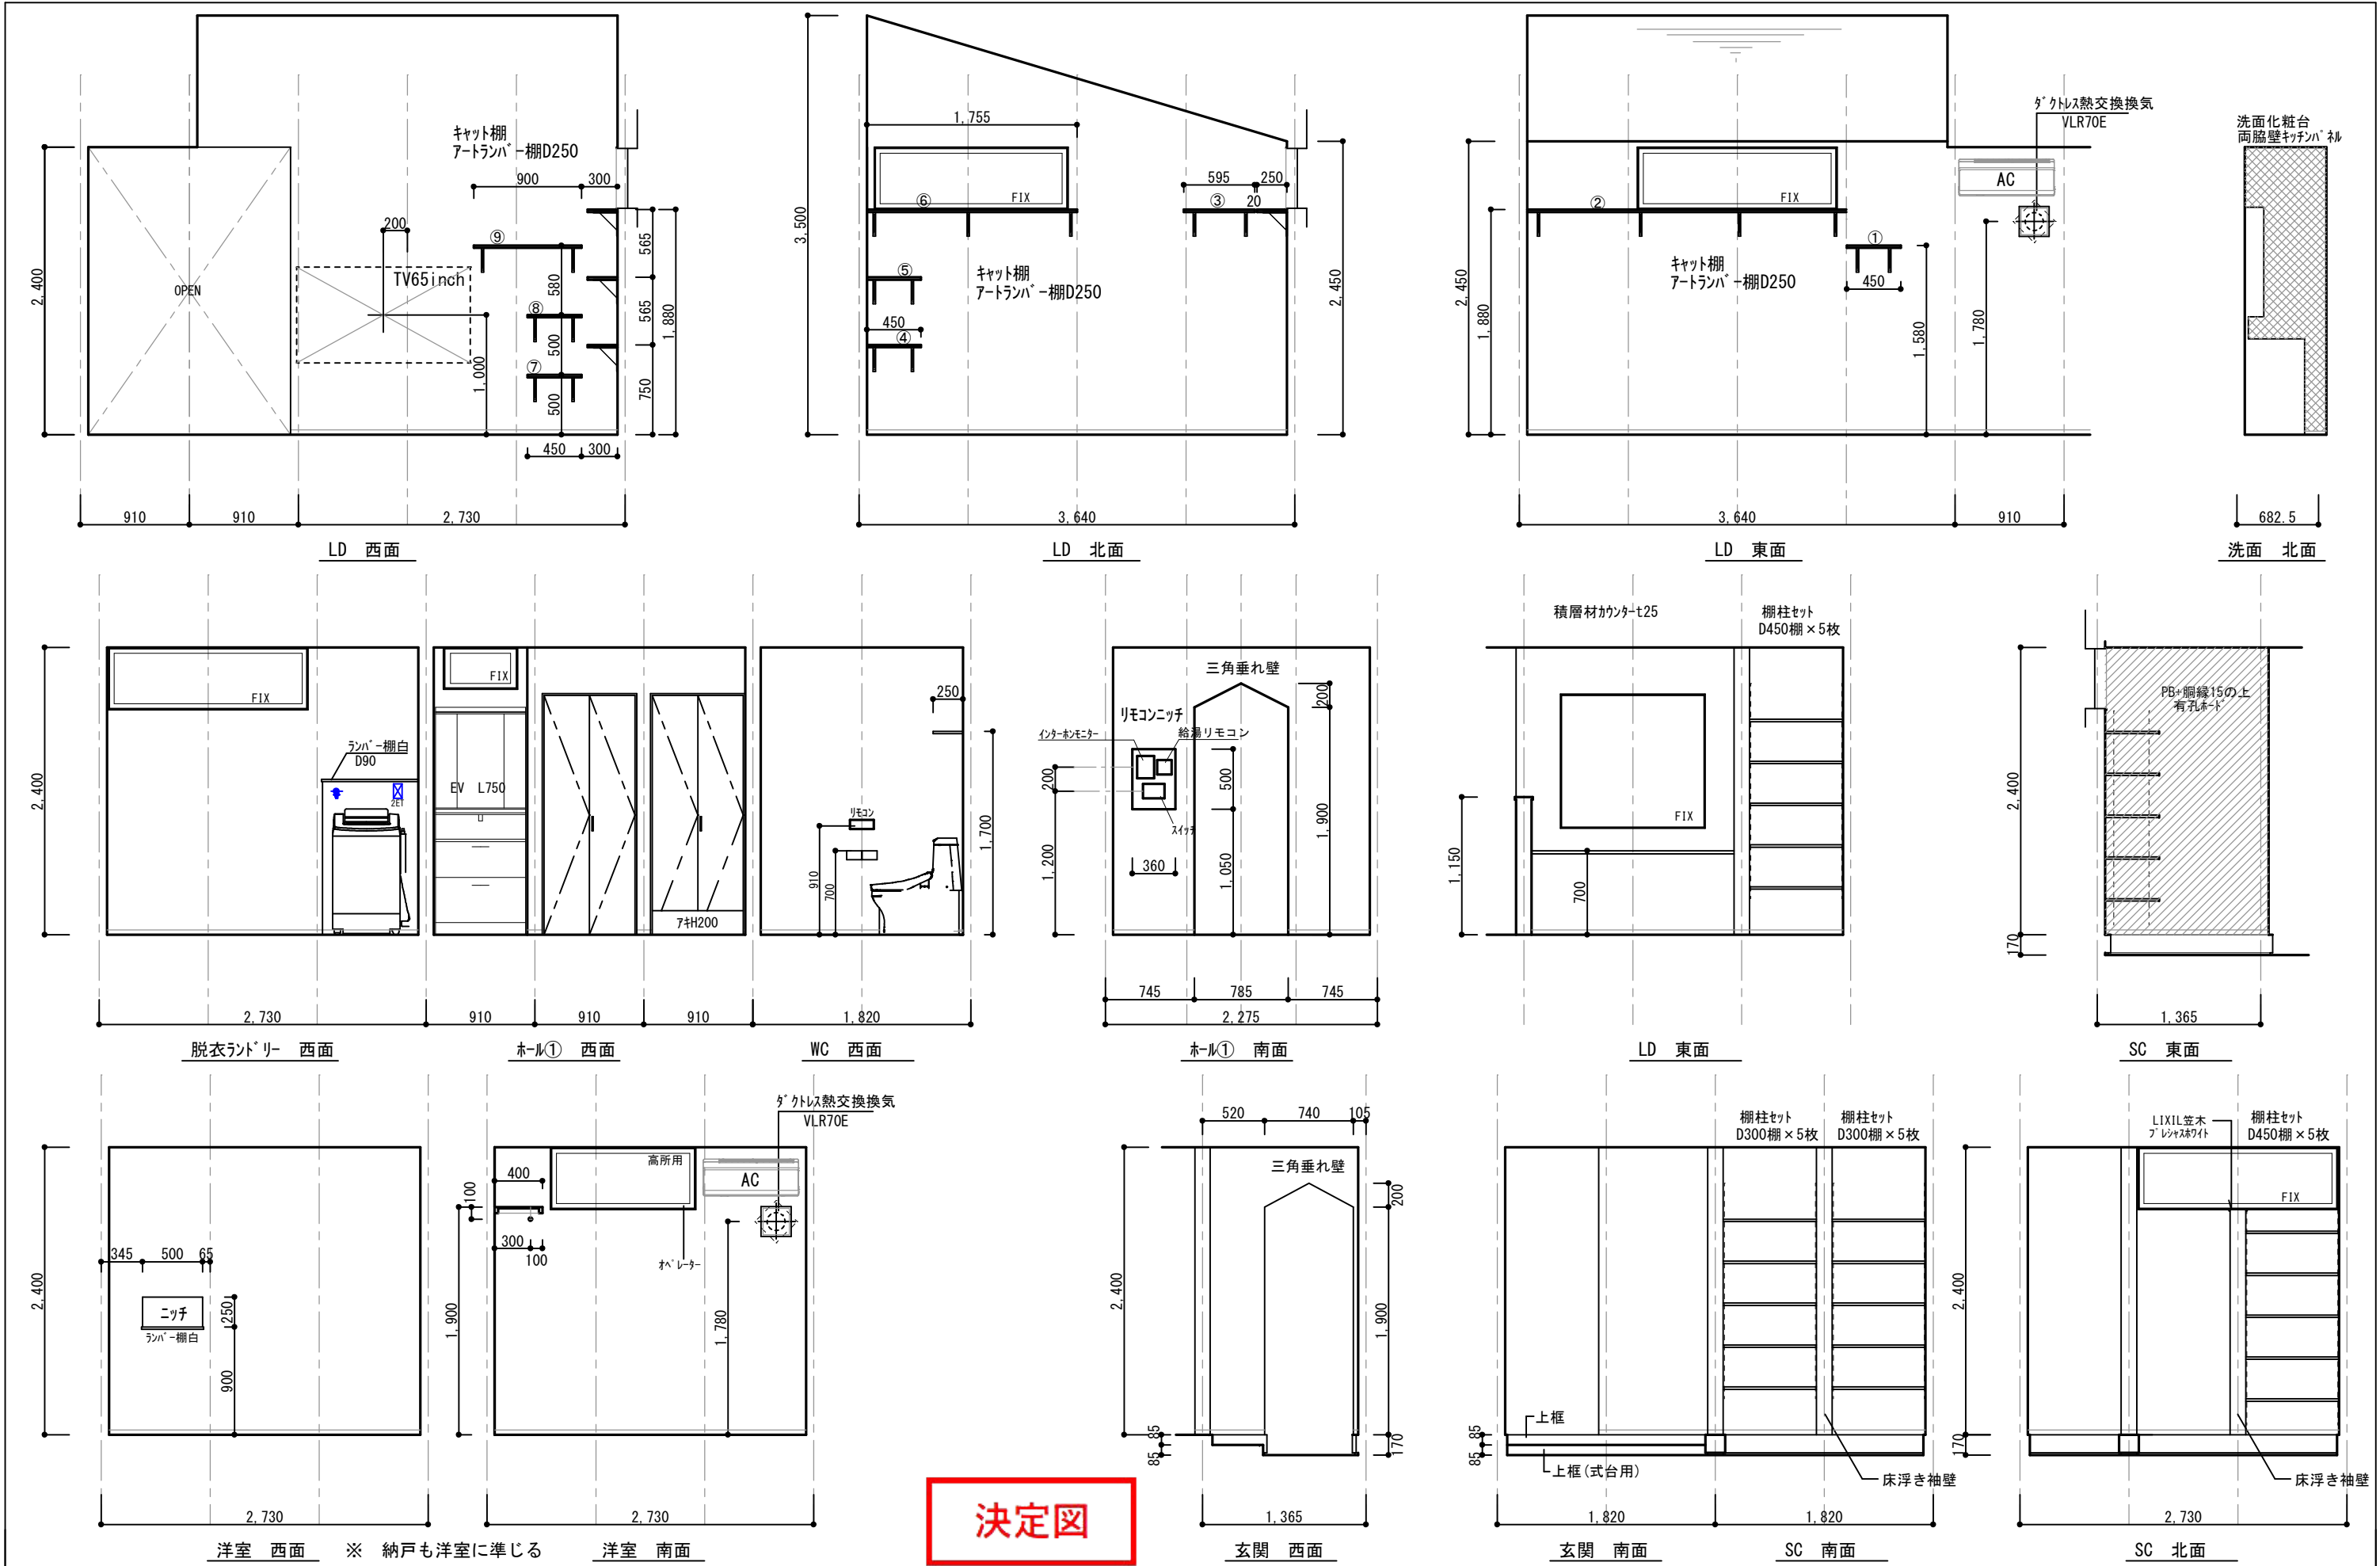

訂 正	浜 岡 一 級 総 合 設 計 事 務 所 一級建築士事務所 静岡県知事登録第 (10)2441 号 一級建築士 大臣登録第 365879 号 西原利昌	LIFEFUND PG HOUSE	株式会社 LIFEFUND InDesign office 一級建築士事務所 事務所登録 (2) 第7595号 一級建築士登録 第179770号 鈴木 達男 〒432-8023 静岡県浜松市中央区鴨江3丁目70番23号	年 月 日	件 名		設計	IC	工事	図 番
				2025. 2. 14	鳥山 高広様 みどり様 邸新築工事					
				縮 尺	図 名					
				1/50	展開図					

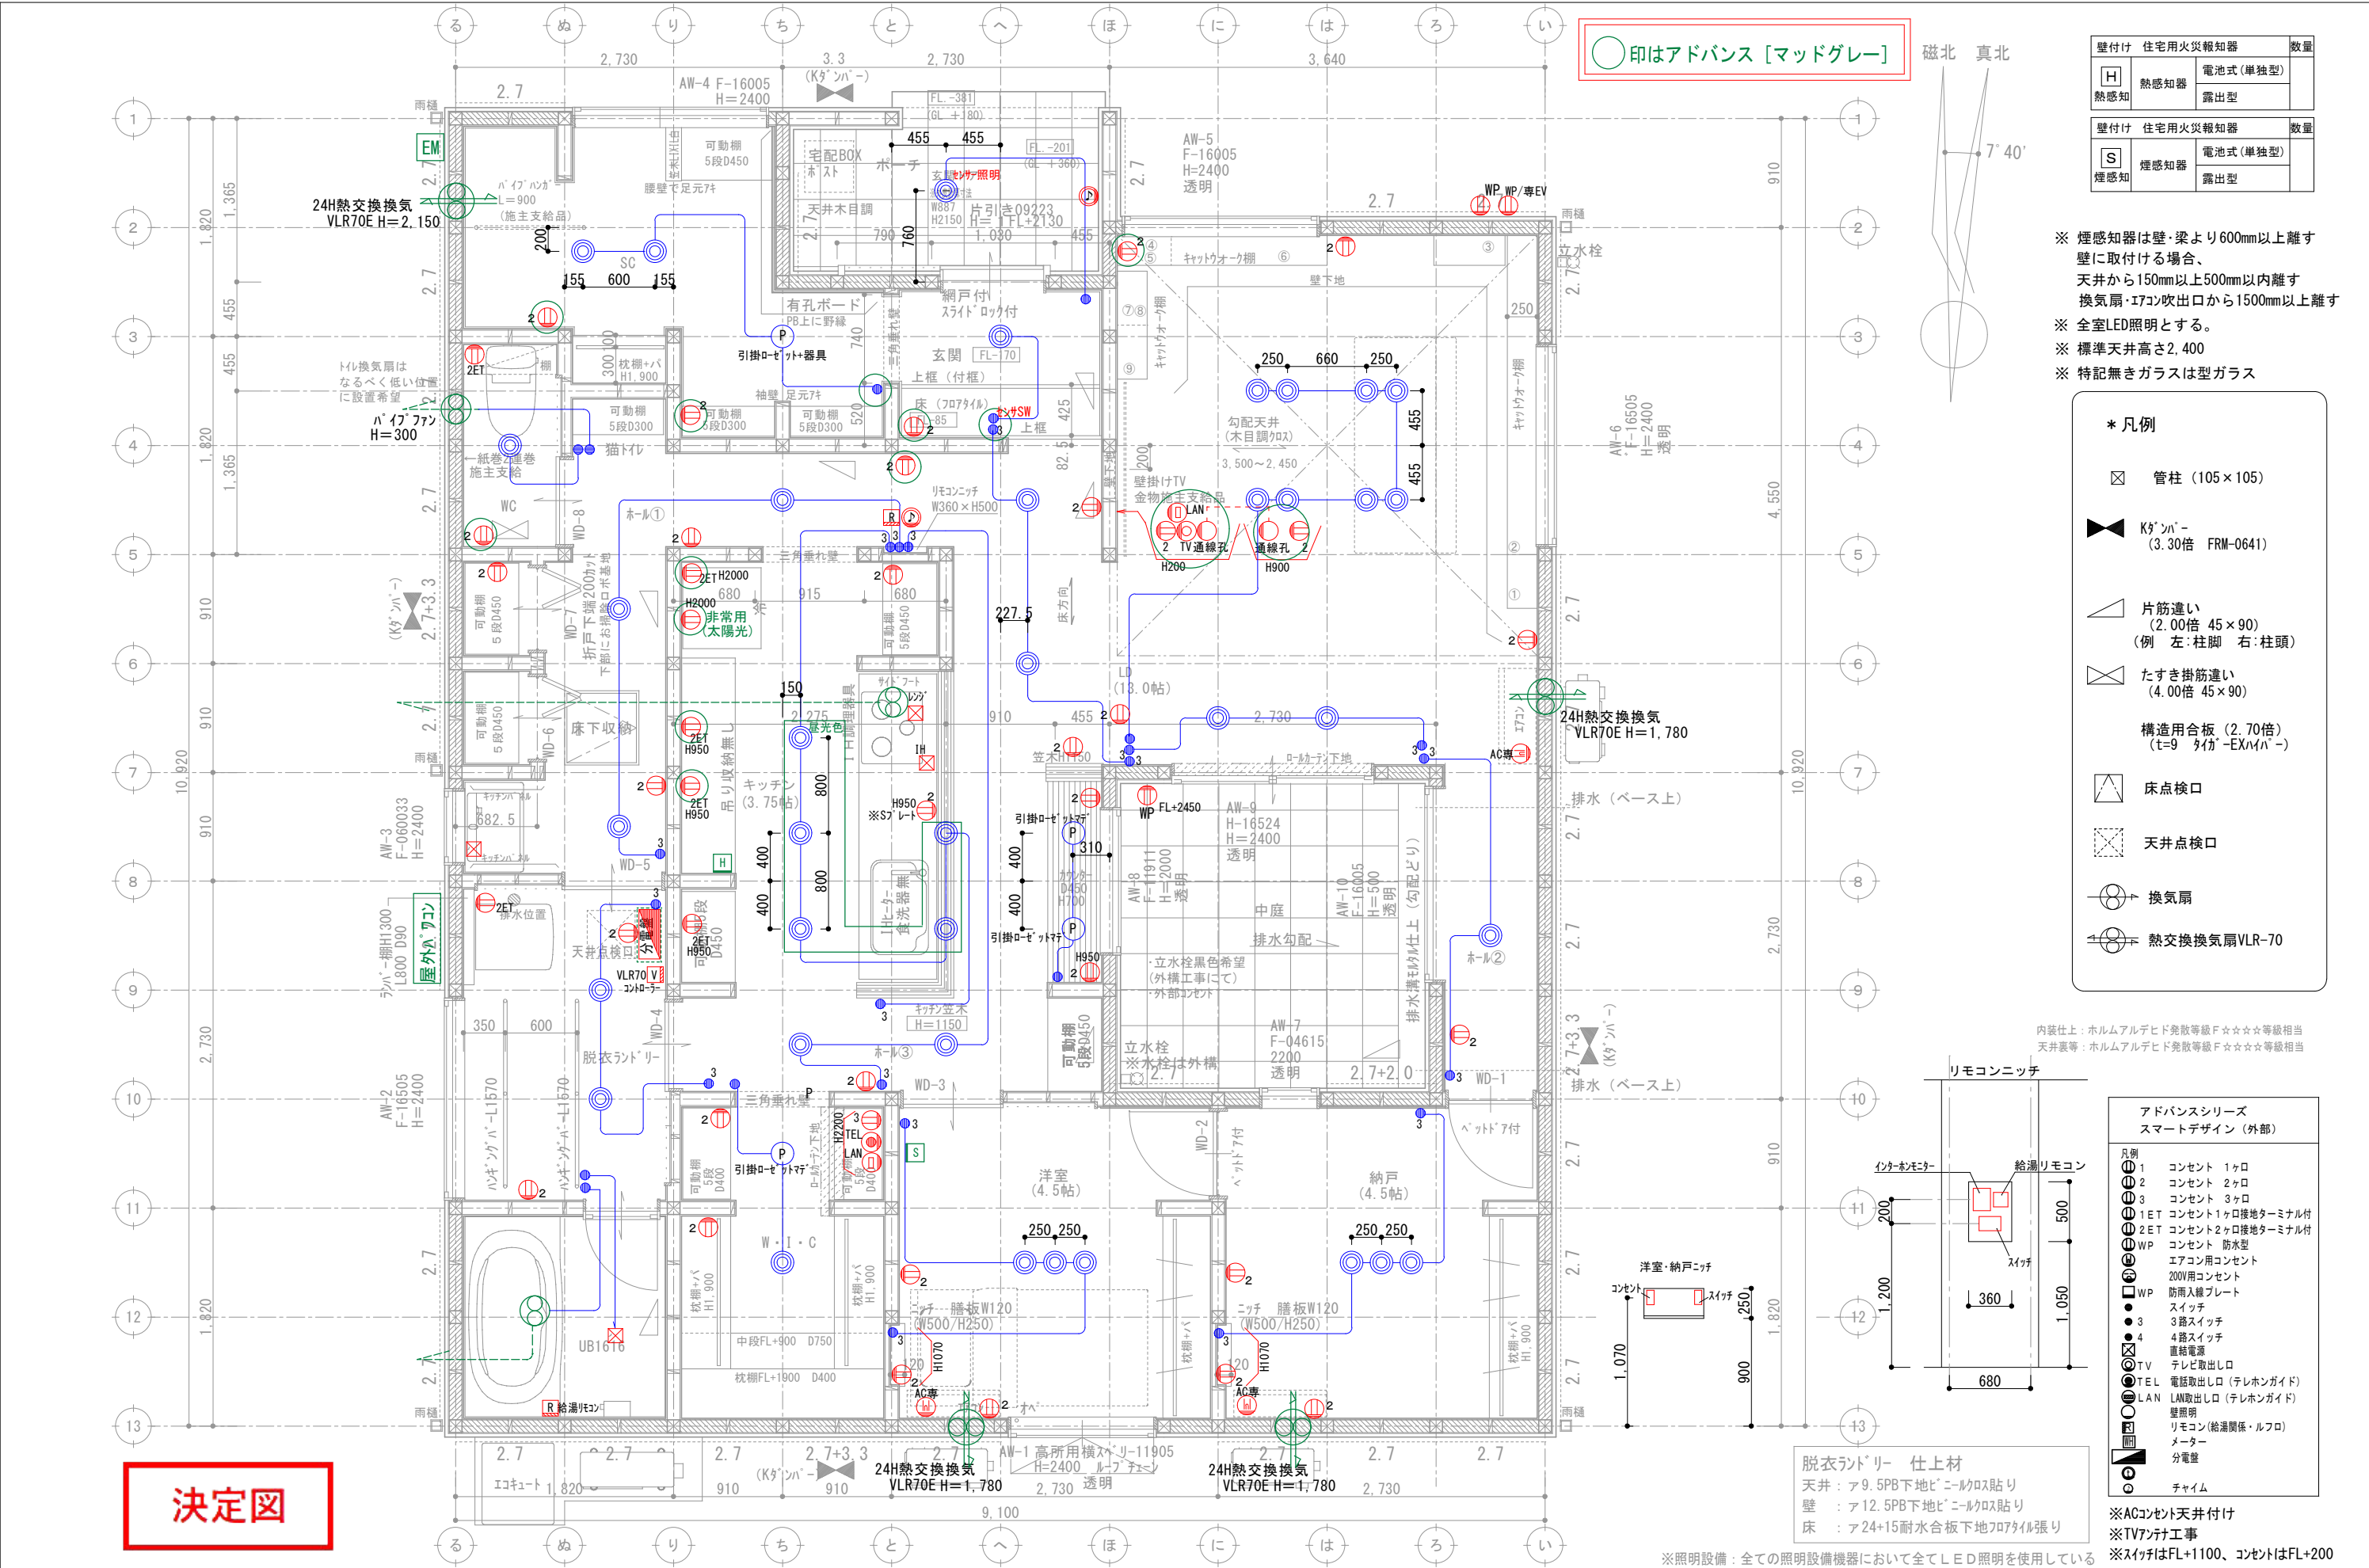

壁付け 住宅用火災報知器			数量
H	熱感知器	電池式(単独型)	
	露出型		
壁付け 住宅用火災報知器			数量
S	煙感知器	電池式(単独型)	
	露出型		


※ 煙感知器は壁・梁より600mm以上離す
壁に取付ける場合、
天井から150mm以上500mm以内離す
換気扇・エアコン吹出口から1500mm以上離す
※ 全室LED照明とする。
※ 標準天井高さ2,400
※ 特記無きガラスは型ガラス

- * 凡例**
- 管柱 (105×105)
 - Kダクト (3.30倍 FRM-0641)
 - 片筋違い (2.00倍 45×90)
(例 左:柱脚 右:柱頭)
 - たすき掛筋違い (4.00倍 45×90)
 - 構造用合板 (2.70倍)
(t=9 9材 EXハイパー)
 - 床点検口
 - 天井点検口
 - 換気扇
 - 熱交換換気扇VLR-70

内装仕上: ホルムアルデヒド発散等級F☆☆☆☆等級相当
天井裏等: ホルムアルデヒド発散等級F☆☆☆☆等級相当

アドバンスシリーズ スマートデザイン (外部)	
凡例	
1	コンセント 1ヶロ
2	コンセント 2ヶロ
3	コンセント 3ヶロ
1ET	コンセント1ヶロ接地ターミナル付
2ET	コンセント2ヶロ接地ターミナル付
WP	コンセント 防水型
	エアコン用コンセント
	200V用コンセント
WP	防雨入線プレート
	スイッチ
●	3路スイッチ
●	4路スイッチ
●	直結電源
●	テレビ取出口
●	TEL 電話取出口 (テレホンガイド)
●	LAN LAN取出口 (テレホンガイド)
●	壁照明
●	リモコン (給湯関係・ルフロ)
●	メーター
●	分電盤
●	チャイム

※ACコンセント天井付け
※TVアンテナ工事
※スイッチはFL+1100、コンセントはFL+200

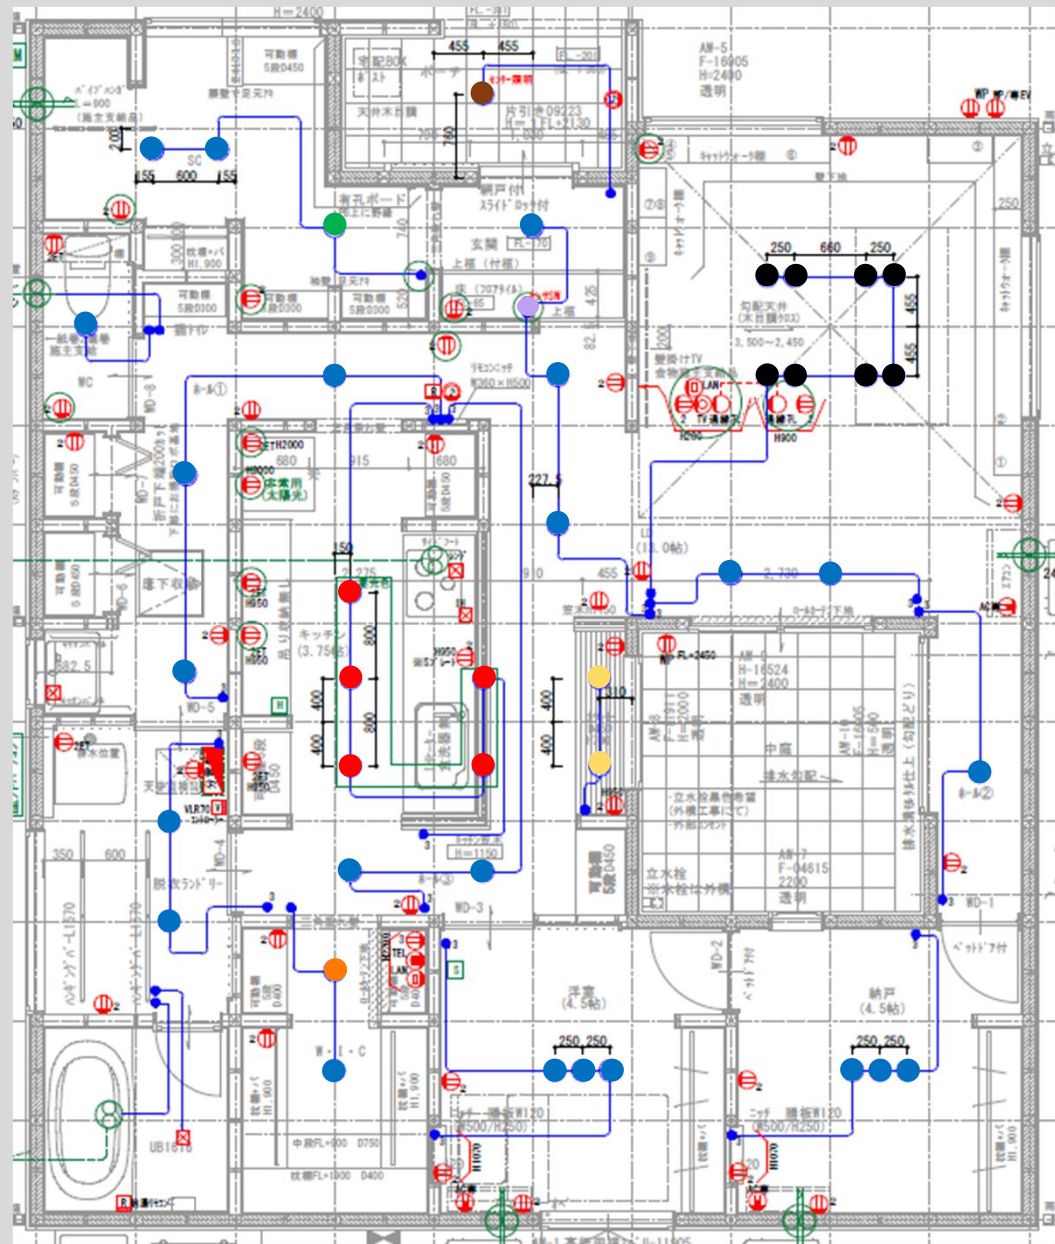

基本照明ダウライト

● × 23
DDL6102YW



COBタイプ | 高気密Se形

DDL-6102 YW
電球色 / 2700K・Ra83
定格光束 消費電力 固有エネルギー消費効率
440lm 4.6W 95.6lm/W
¥3,600-(税抜) (LED内蔵)
LED LED 4.6W 白熱灯60W相当
●銅板 白塗装
●アクリル 乳白(マット)
●径φ116 埋込穴φ100 埋込深70mm 0.3kg
●8VA
●拡散バネル付
●AC100V
●光源寿命60,000時間
●取付可能天井厚5~25mm
●調光器併用不可

● × 8
DDL6102YB



COBタイプ | 高気密Se形

DDL-6102 YB
電球色 / 2700K・Ra83
定格光束 消費電力 固有エネルギー消費効率
370lm 4.6W 80.4lm/W
¥3,600-(税抜) (LED内蔵)
LED LED 4.6W 白熱灯60W相当
●銅板 黒塗装
●アクリル 乳白(マット)
●径φ116 埋込穴φ100 埋込深70mm 0.3kg
●8VA
●拡散バネル付
●AC100V
●光源寿命60,000時間
●取付可能天井厚5~25mm
●調光器併用不可

● × 5
DDL6102WW



COBタイプ | 高気密Se形

DDL-6102 WW
昼白色 / 5000K・Ra83
定格光束 消費電力 固有エネルギー消費効率
480lm 4.6W 104.3lm/W
¥3,600-(税抜) (LED内蔵)
LED LED 4.6W 白熱灯60W相当
●銅板 白塗装
●アクリル 乳白(マット)
●径φ116 埋込穴φ100 埋込深70mm 0.3kg
●8VA
●拡散バネル付
●AC100V
●光源寿命60,000時間
●取付可能天井厚5~25mm
●調光器併用不可

WIC ペンダント
ダイング ペンダント

● × 3

引掛ローゼット
器具は別途

センサー-SW ● × 1



WTA1811HK
希望小売価格 12,400円 (税抜)
※掲載の価格には消費税は含まれていません。
壁取付 熱線センサー付自動スイッチ
(2線式・3路配線対応形) (LED専用)
(検知後連続動作時間 約10秒~30分可変形)
(明るさセンサー・手動スイッチ付) (マットグレー)
1.2A 100V AC
プレート別売
WTA7101HK
希望小売価格 330円 (税抜)
※掲載の価格には消費税は含まれていません。
スイッチプレート・1連用 (マットグレー)

コードペンダント

● × 1
DPN-41421Y



DPN-41421 Y
電球色 / 2700K・Ra83
定格光束 消費電力 固有エネルギー消費効率
550lm 4.5W 122.2lm/W
¥15,000-(税抜) (ランプ付)
LEDユニットフラット形(径90mm) 4.5W(GX53-1a) 広角形
白熱灯60W相当
●陶器(信楽焼) 白
●径φ177 高さ 全長700~1200mm 1.0kg
●9VA
●吊高さ調節可能
●AC100V
●光源寿命40,000時間
●調光器併用不可
直付専用

ポーチ灯

● × 1
DDL-4496YB



高気密Se形 | 人感センサー | 連動マルチタイプ

DDL-4496 YB
電球色 / 2700K・Ra83
定格光束 消費電力 固有エネルギー消費効率
425lm 7.7W 55.1lm/W
¥18,800-(税抜) (LED内蔵)
LED LED 7.7W 白熱灯60W相当
●アルミダイカスト 黒塗装
●アクリル 乳白(マット)
●径φ111 埋込穴φ100
埋込深80mm 0.5kg
●14VA
●点灯照度調節機能付(暗・明・切)
●点灯保持時間(1分)
●拡散バネル付
●AC100V
●光源寿命50,000時間
●取付可能天井厚5~25mm
●調光器併用不可
【連動器具について】
LED調光タイプ60VAまで
LED非調光タイプ不可 蛍光灯不可
白熱灯60Wまで

外部：スマートデザインシリーズ (Panasonic)

表情豊かな住まいをつくり出すスマートデザインシリーズ。



ドアホン：VL-SZ30KL
(Panasonic)



内部SW：アドバンス
電気図に特記無き限りマッドホワイト




特記ある箇所 [マッドグレー]



決定図

2025.2.14

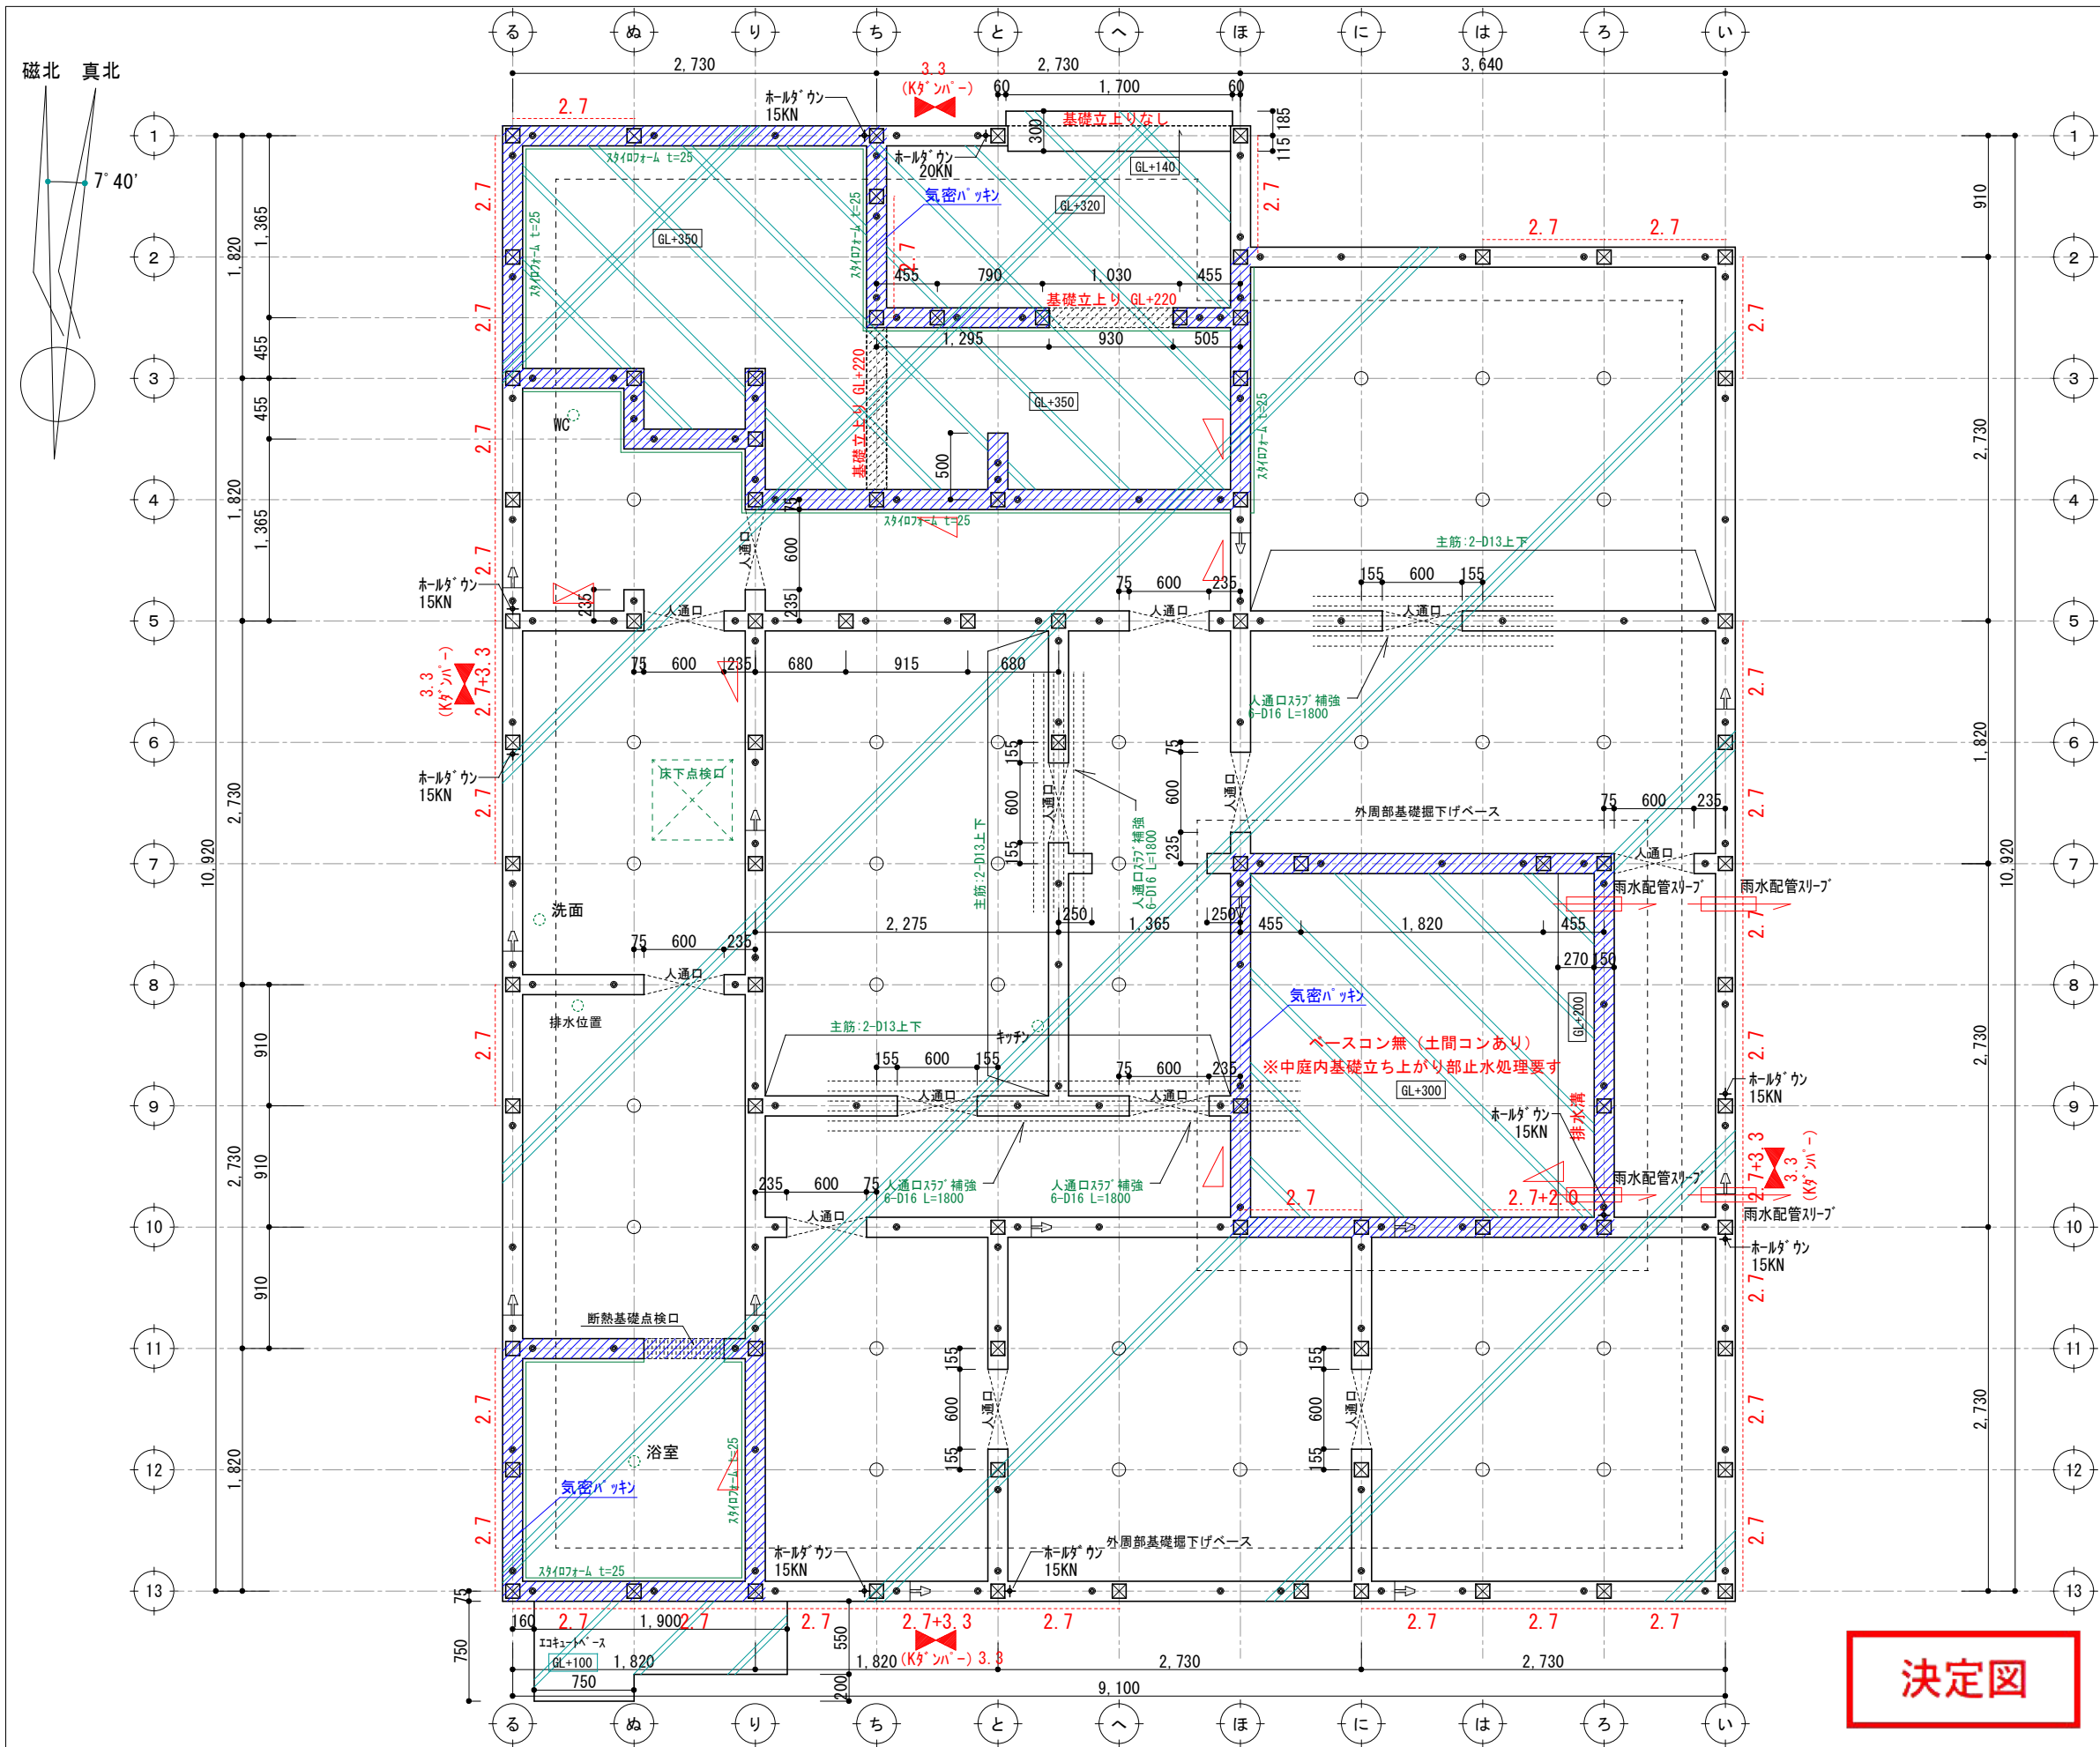


構造体ベースコンクリート t=150

後打ち土間コン

アンカーボルトの配置
土台切れの箇所より150mm
土台の継手及び仕口の端部より150mm
耐力壁の端部、筋交いの脚部より150mm
1.82m以下の間隔
250mm以上埋込み
基礎天端より120mm

筋かい凡例
柱脚 柱頭 片筋かい
たすき掛け筋かい
構造用合板

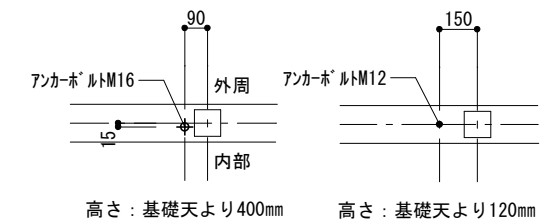


ホールダウン用アンカーボルト配置

アンカーボルト配置

凡例	
通し柱 (105*105)	管柱 (105*105)
● アンカーボルトM12 L=400	
+ ホールダウンアンカーM16 L=800	
柱芯より90mm 280mm以上埋め込み (カナフィストアンカーボルトM16)	
⊕ 鋼製束	
└ 土台ジョイント	
▨ ベースコンクリート (t=150)	
▨ 後打ちコンクリート	

- 基礎伏図について特記なき場合に限り下記による。
1. コンクリート：呼び強度 21N/mm²
 2. 鉄筋：SD295A
 3. 設計地耐力：fe=30kN/m²
地耐力計測後、不足の場合は相当の改良を行い、満たすものとする。
 4. 基礎の位置は、芯振分けとする。
 5. 玄関・S/C・UB周囲の基礎天端は気密パッキン施工（網掛け部）とし、その他の基礎天端は基礎パッキン施工とする。
 6. 設備配管の屋内への取り入れは基礎立上り部のスリーブによる。

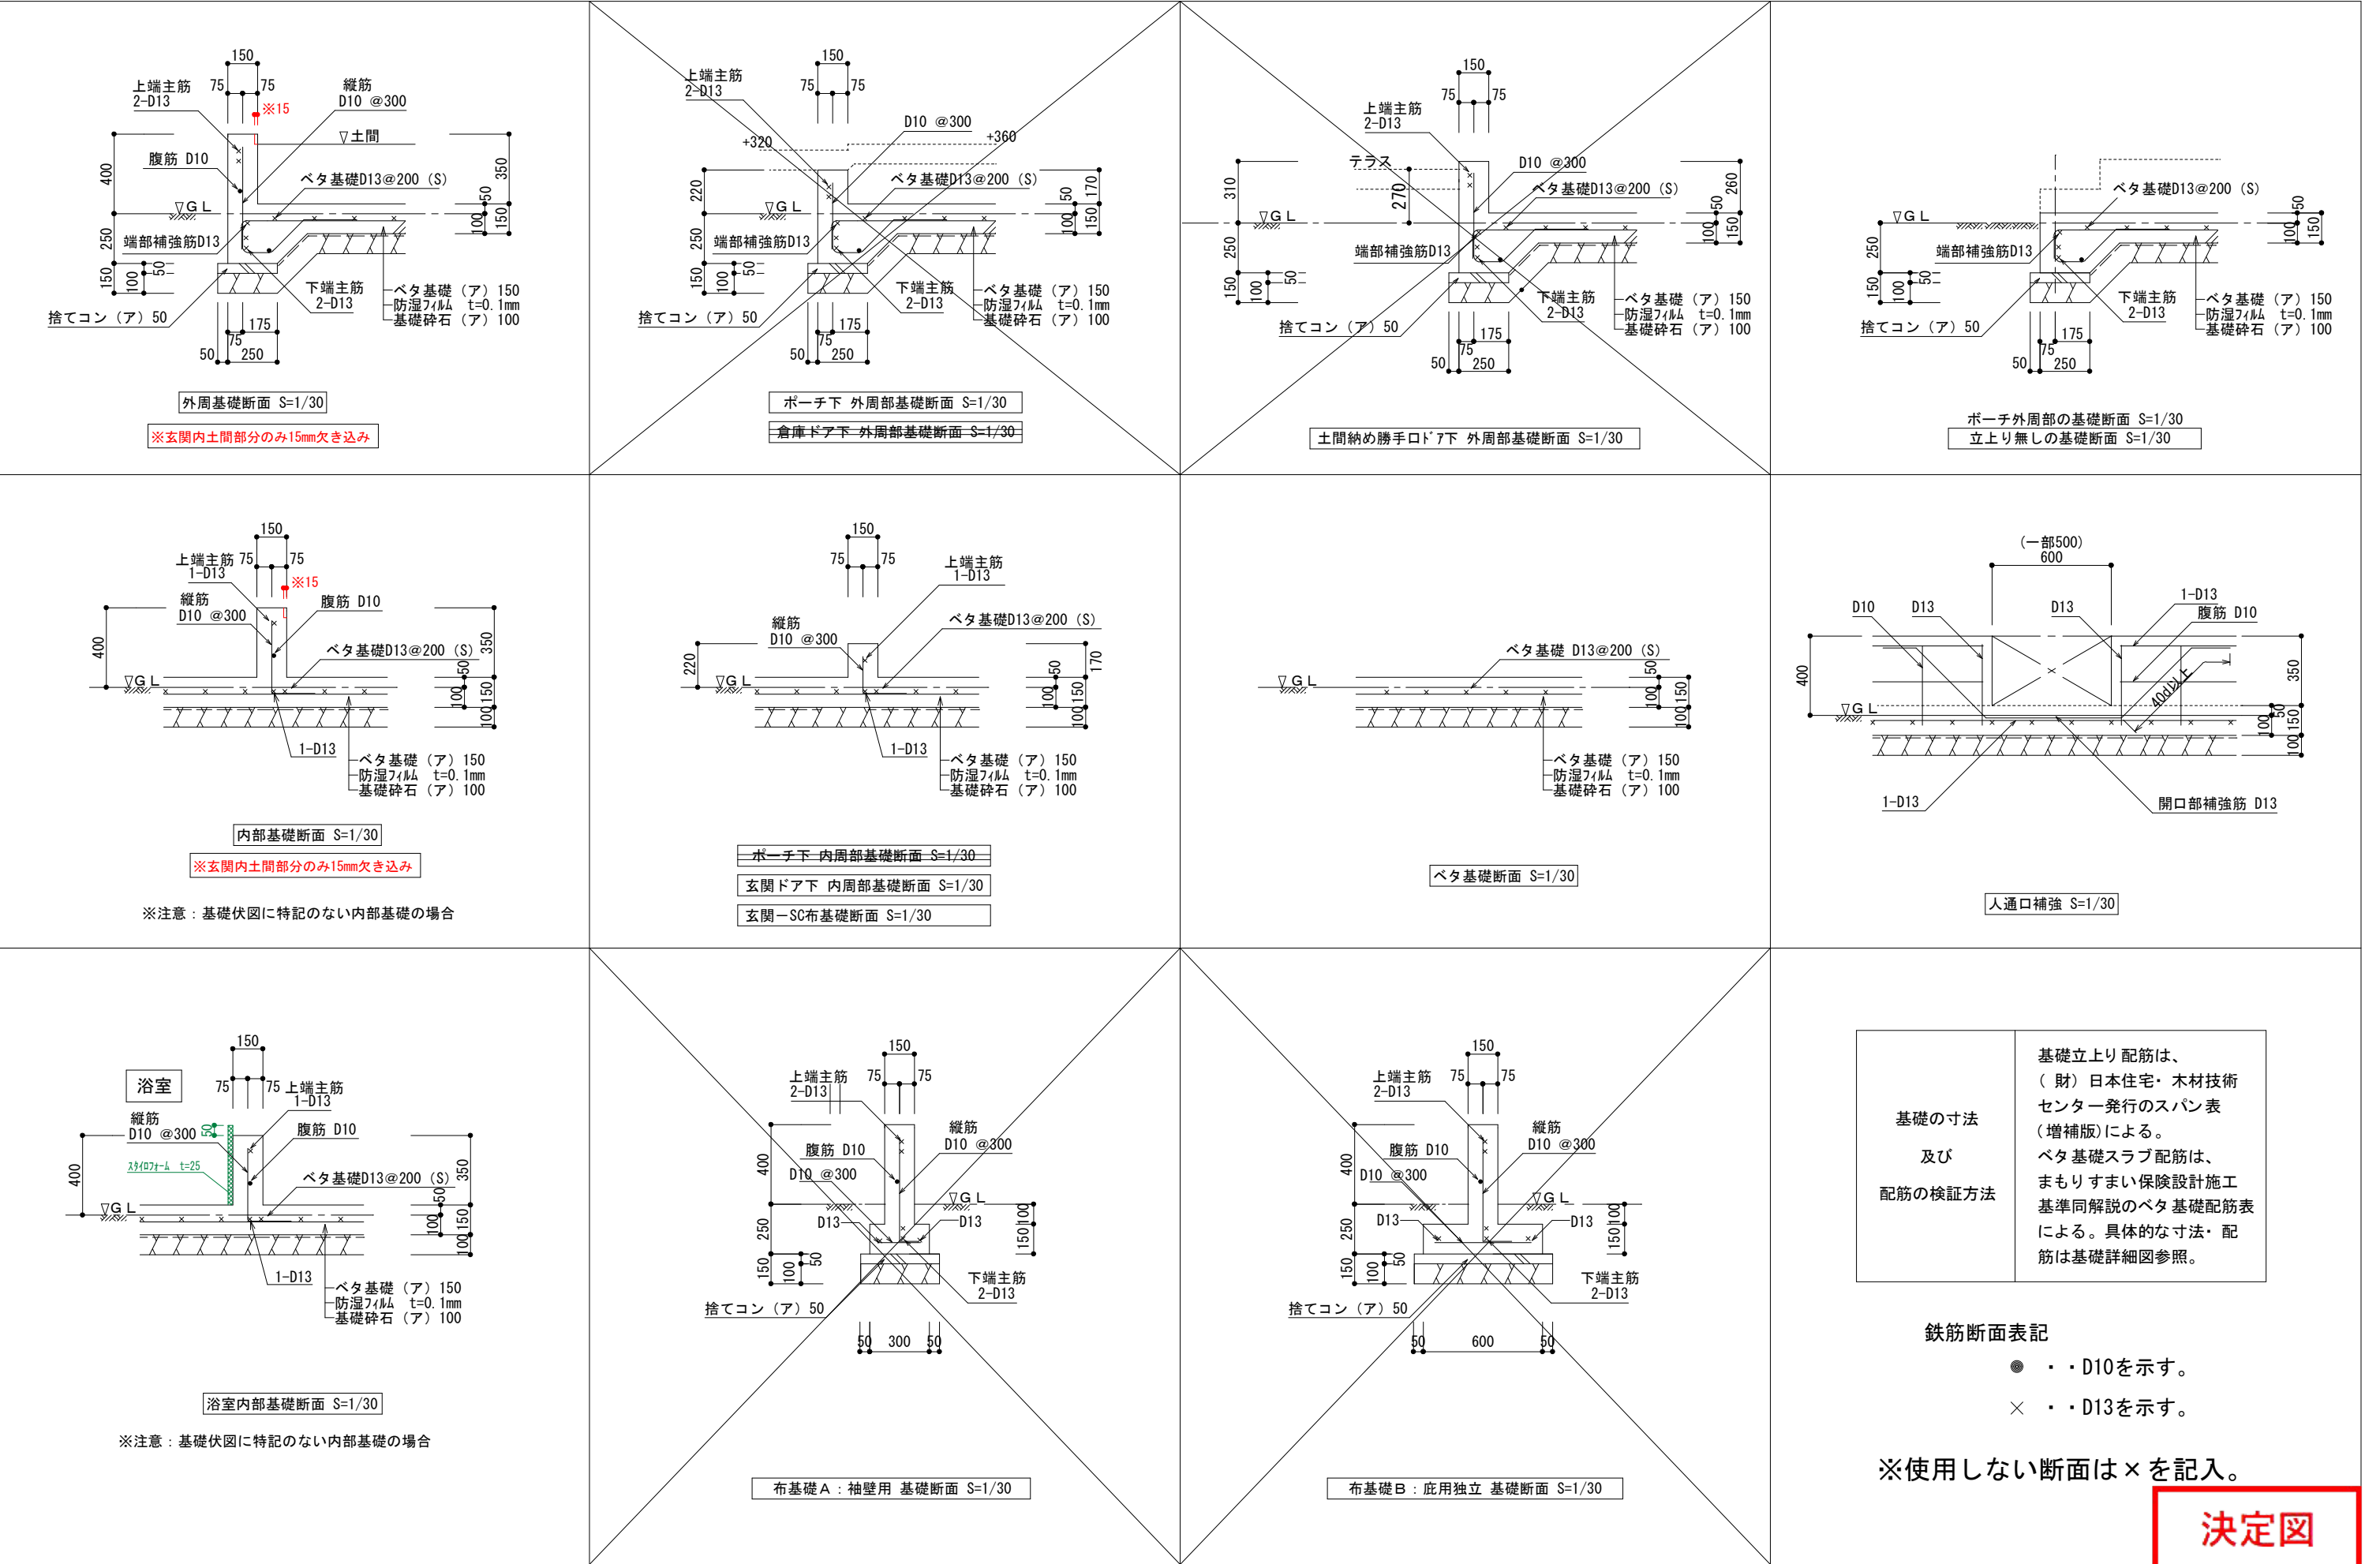

基礎の寸法
及び
配筋の検証方法


基礎立上り配筋は、
(財)日本住宅・木材技術
センター発行のスパン表
(増補版)による。
ベタ基礎スラブ配筋は、
まもりすまい保険設計施工
基準同解説のベタ基礎配筋表
による。具体的な寸法・配
筋は基礎詳細図参照。

鉄筋断面表記

●・・・D10を示す。
×・・・D13を示す。

※使用しない断面は×を記入。

決定図

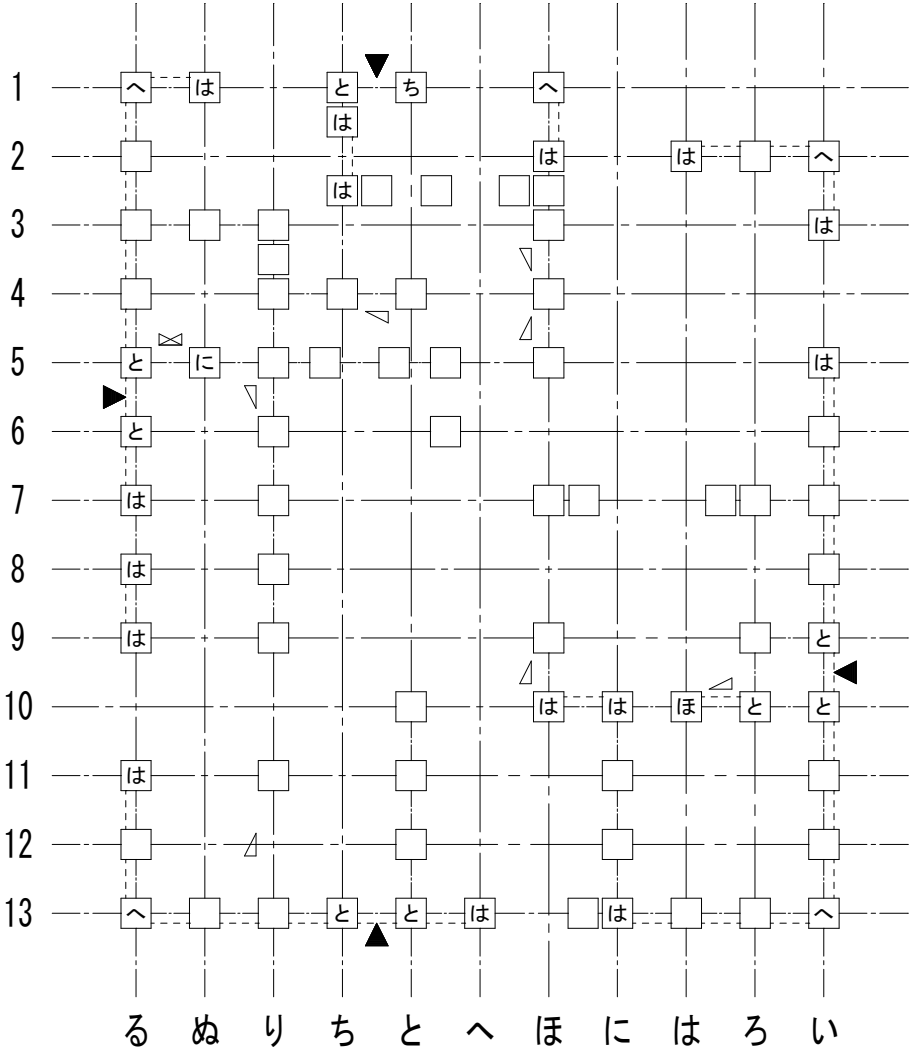

1 階柱壁伏図

接合部凡例				*接合部凡例はユーザ設定されたものです。	
記号	仕様（カナイ金物）		N	倍率	
SBCP		スリムビルドコーナー75	0.00	1.00	
SBCP		スリムビルドコーナー75	0.65	1.00	
SBCP	は	スリムビルドコーナー75	1.00	1.00	
ARCG	に	アレントコーナー合板用	1.40	2.20	
ARCG	ほ	アレントコーナー合板用	1.60	2.20	
ARCG	へ	アレントコーナー合板用	1.80	2.20	
HD15	と	ブレイブホールダウン B-HD15	2.80	3.60	
HD20	ち	ブレイブホールダウン B-HD20	3.70	4.70	
HD25	り	ブレイブホールダウン B-HD25	4.70	4.80	
HD30	ぬ	ブレイブホールダウン B-HD30	5.60	7.20	
J1	る	腰掛け蟻若しくは大入れ蟻掛け+羽子板ボルト、短冊金物		1.90	
J2	を	腰掛け蟻若しくは大入れ蟻掛け+羽子板ボルト、短冊金物×2		3.00	

※表示なき金物は「は」とする。

梁継手・仕口用
梁継手・仕口用

接合部凡例				*接合部凡例はユーザ設定されたものです。	
記号	仕様（タナカ金物）		N	倍率	
FCP		フックコーナー	0.00	1.00	
FCP		フックコーナー	0.65	1.00	
FCP	は	フックコーナー	1.00	1.00	
GCP	に	シナコーナー	1.40	2.20	
GCP	ほ	シナコーナー	1.60	2.20	
GCP	へ	シナコーナー	1.80	2.20	
HD15	と	ビス止めホールダウンU HD15	2.80	3.60	
HD20	ち	ビス止めホールダウンU HD20	3.70	4.70	
HD25	り	ビス止めホールダウンU HD25	4.70	4.80	
HD30	ぬ	ビス止めホールダウンU HD15×2（HD35）	5.60	7.20	
J1	る	腰掛け蟻若しくは大入れ蟻掛け+羽子板ボルト、短冊金物		1.90	
J2	を	腰掛け蟻若しくは大入れ蟻掛け+羽子板ボルト、短冊金物×2		3.00	


※表示なき金物は「は」とする。

梁継手・仕口用
梁継手・仕口用

筋かいの種類に応じた筋かいの端部の接合部の仕様		
	筋かいの種類	接合部の仕様（構造方法）
イ	鉄筋φ9	柱又は横架材を貫通し、三角座金を介してナット締め、又は鋼板添え板を用い鋼板を柱及び横架材にCN90, 8本平打ち
ロ	筋かい:15×90	柱・横架材を欠き込み、柱・横架材双方に対してN65, 5本平打ち
ハ	筋かい:30×90	鋼板添え板t=1.6mmを筋かいに対してボルトφ12及びCN65, 3本平打ち、柱に対してCN65, 3本平打ち、横架材に対してCN65, 4本平打ち。筋かいプレートBP同等品
ニ	筋かい:45×90	鋼板添え板t=2.3mmを筋かいに対してボルトφ12及びスクリュー釘φ4.5L50, 7本平打ち、柱及び横架材に対してスクリュー釘φ4.5L50, 5本平打ち。筋かいプレートBP-2同等品
ホ	筋かい:90×90	柱又は横架材にボルトφ12mmを用いて一面剪断接合

胴差と通し柱の接合部の仕様		
	胴差と通し柱の条件	仕口
T1	通し柱の片側に胴差が来る場合	胴差を柱にかたぎ大入れ短ほぞ差しの上、羽子板ボルト、かね折り金物又は同等以上の仕口
T2	通し柱の両側に胴差が来る場合	胴差を柱にかたぎ大入れ短ほぞ差しの上、短冊金物又は、同等以上の仕口で胴差相互を緊結
T3	通し柱と胴差の接合部の近くに90×90以上の筋かいが来る場合(通し柱が建物の出隅にあるか、筋かい壁が外壁と直交して接する場合)	胴差を通し柱に、15KN用引き寄せ金物を水平に用いて緊結

決定図

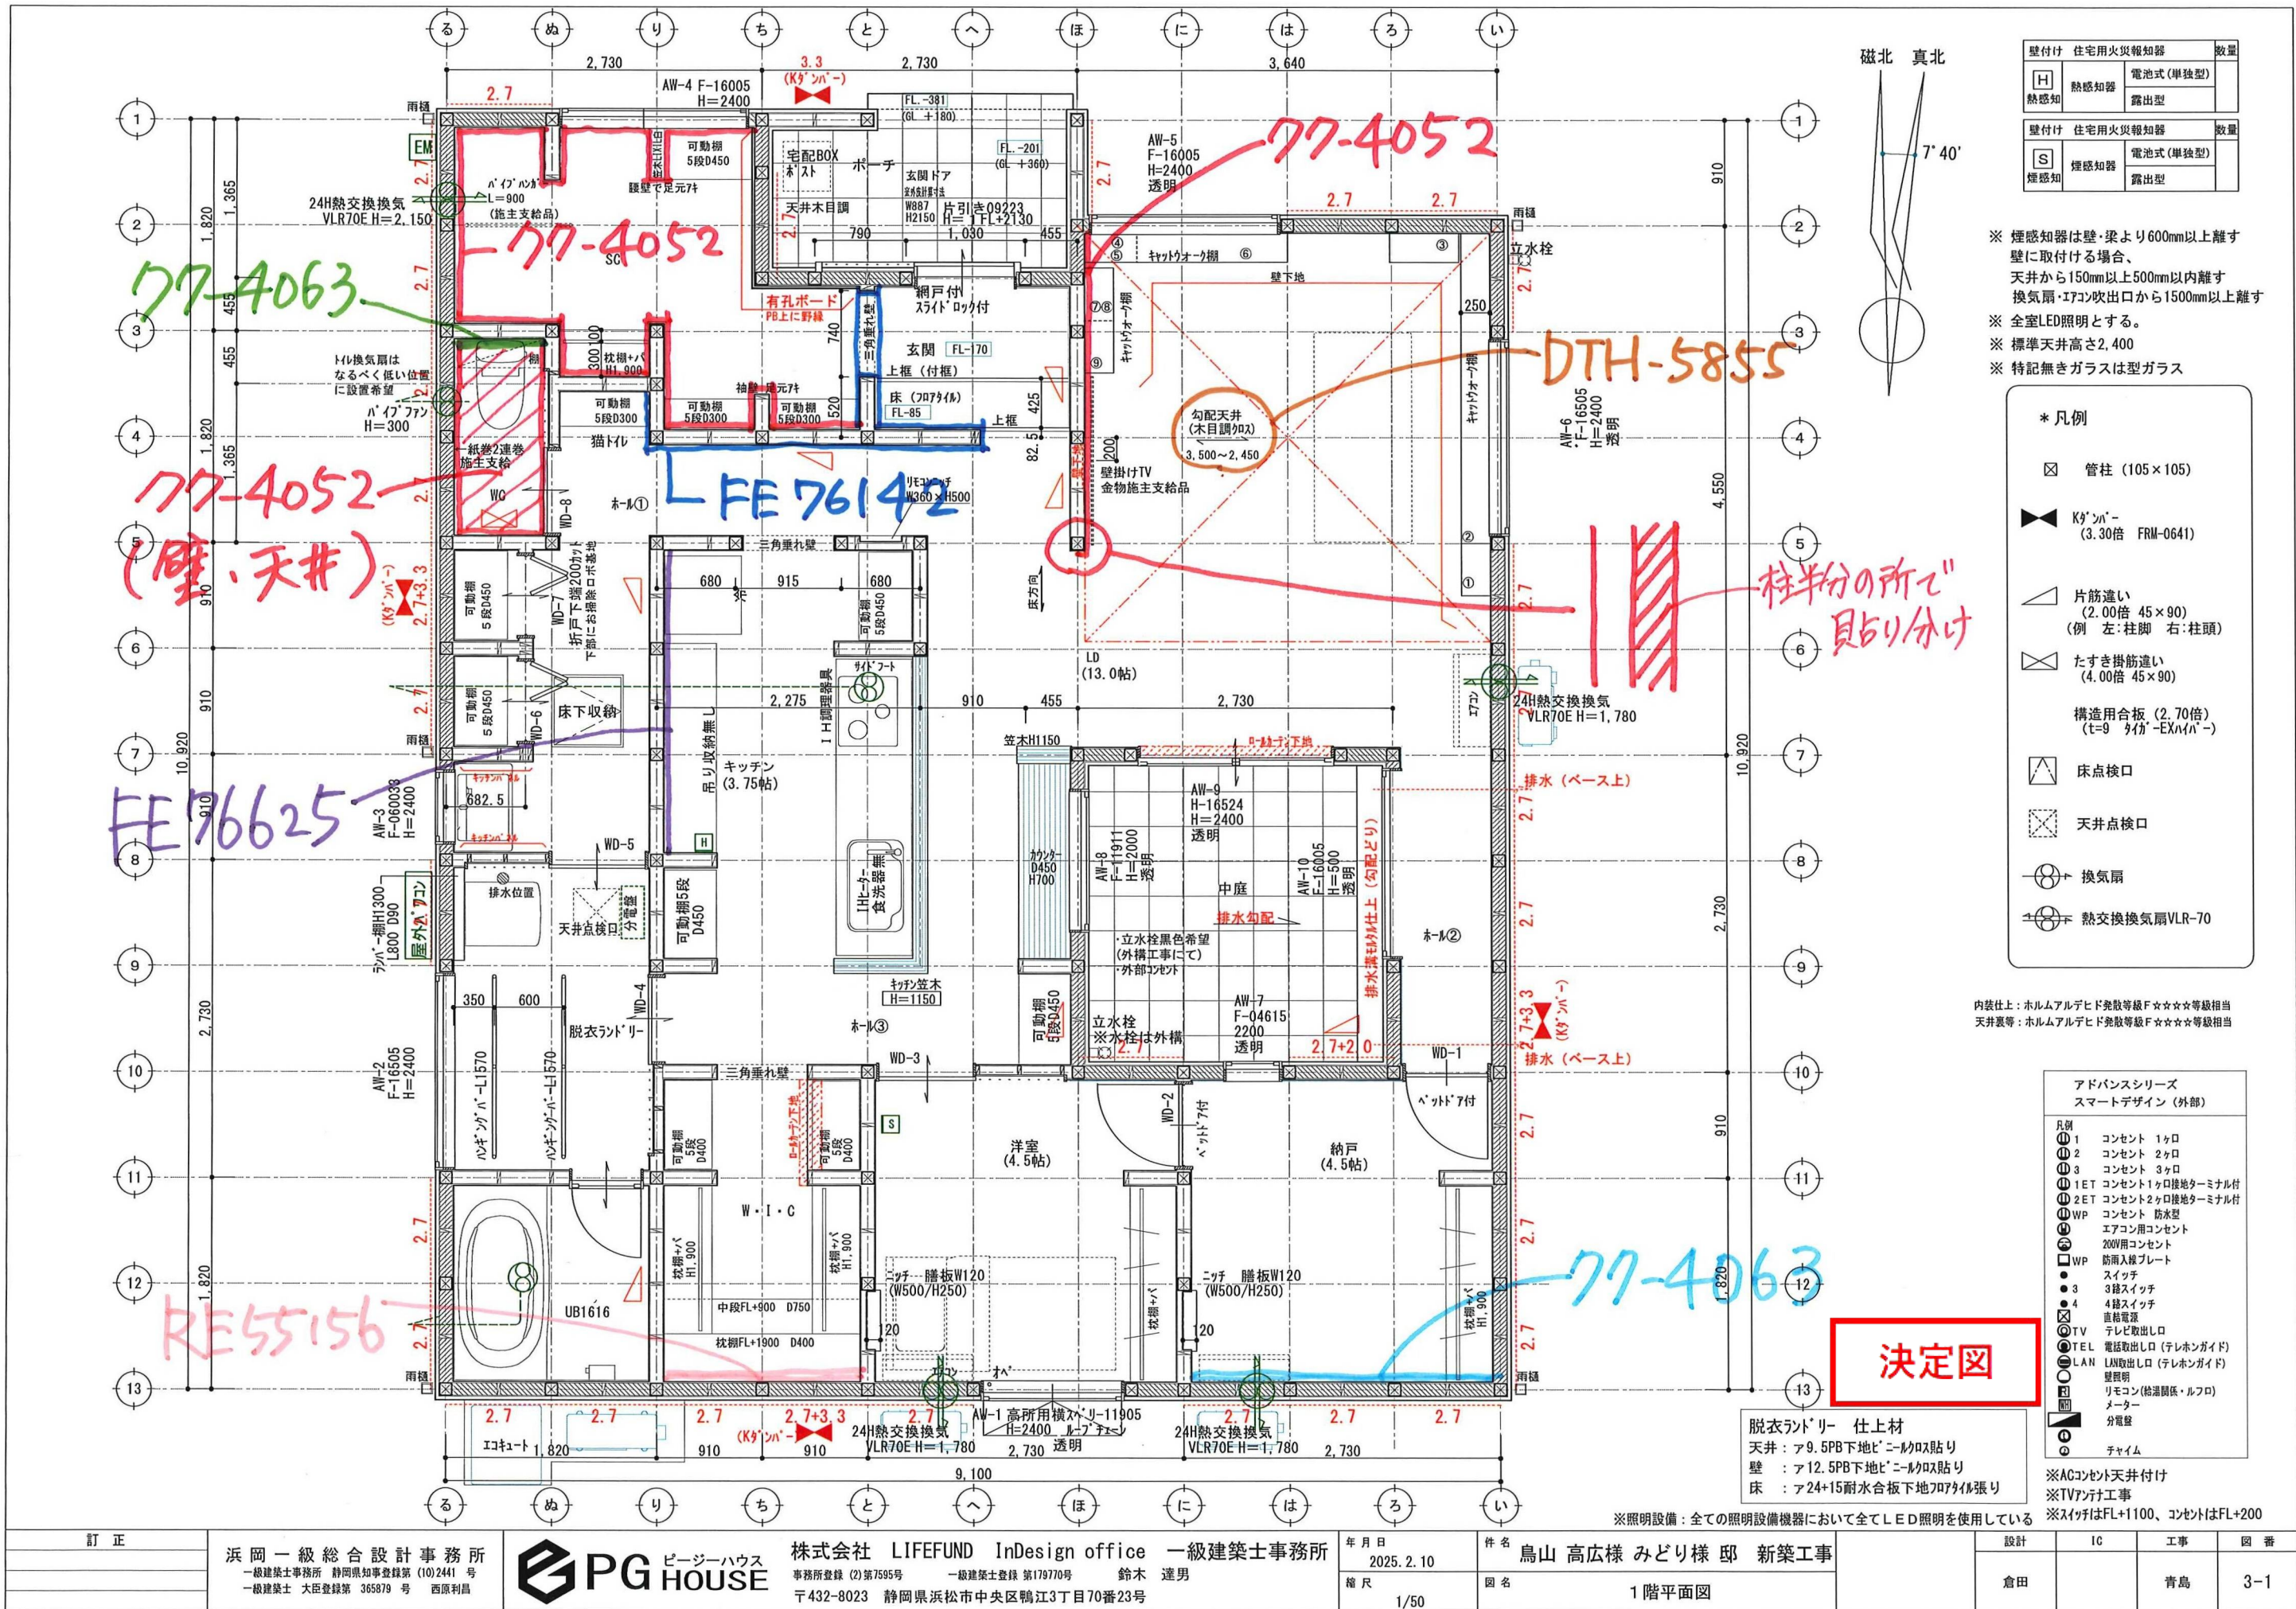

訂正

浜岡一級総合設計事務所
一級建築士事務所 静岡県知事登録第 (10)2441 号
一級建築士 大臣登録第 365879 号 西原利昌

PG HOUSE
ピージーハウス

株式会社 LIFEFUND InDesign office 一級建築士事務所
事務所登録 (2)第7595号 一級建築士登録 第179770号 鈴木 達男
〒432-8023 静岡県浜松市中央区鶴江3丁目70番23号

年月日
2025. 2. 10
縮尺
1/50

件名
鳥山 高広様 みどり様 邸 新築工事
図名
1階平面図

設計
倉田
IC
工事
青島
図番
3-1