

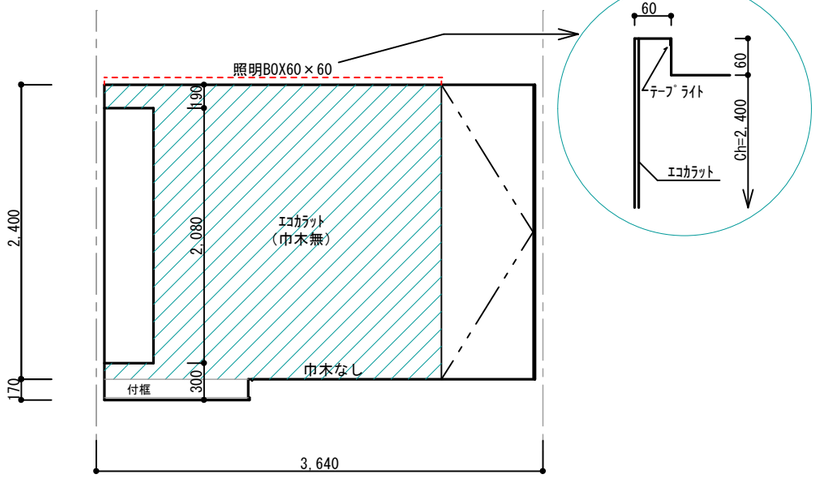



玄関　西面

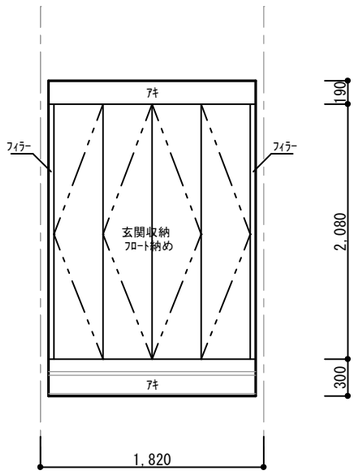


玄関　南面

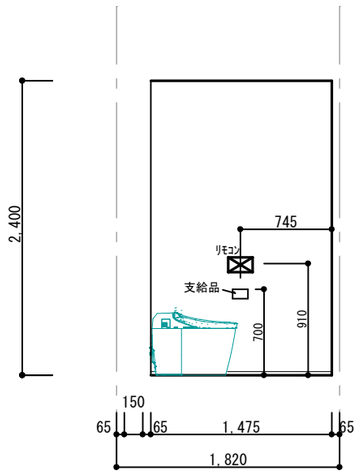


WC①　南面

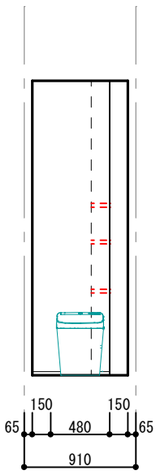


WC①　東面

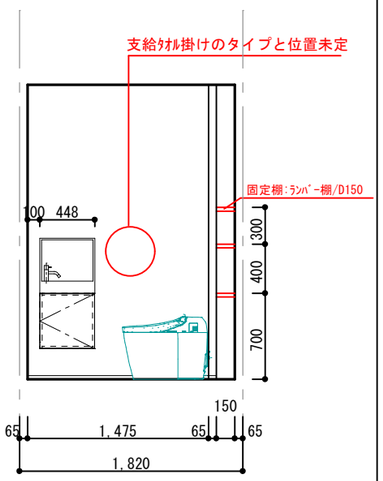


WC①　北面

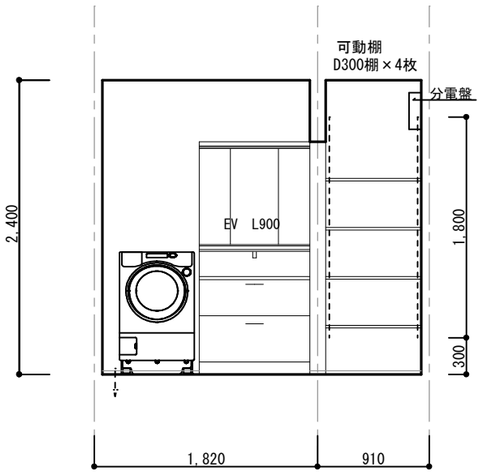


洗面所　東面

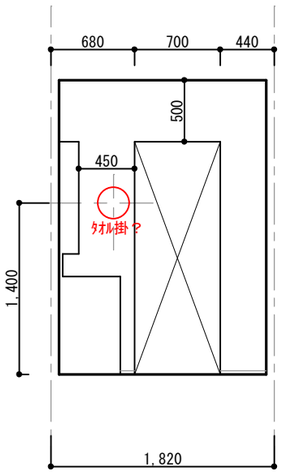


洗面所　南面

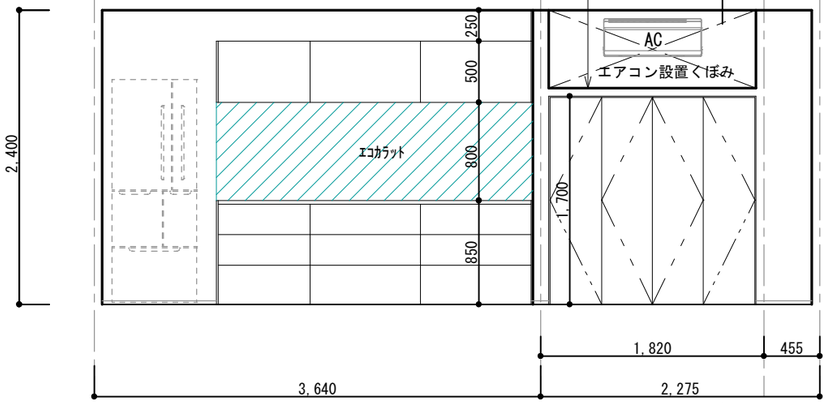

LDK　北面

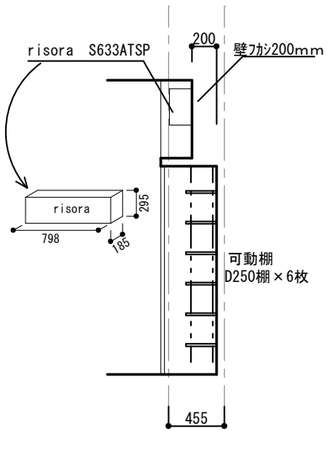

A-A 断面

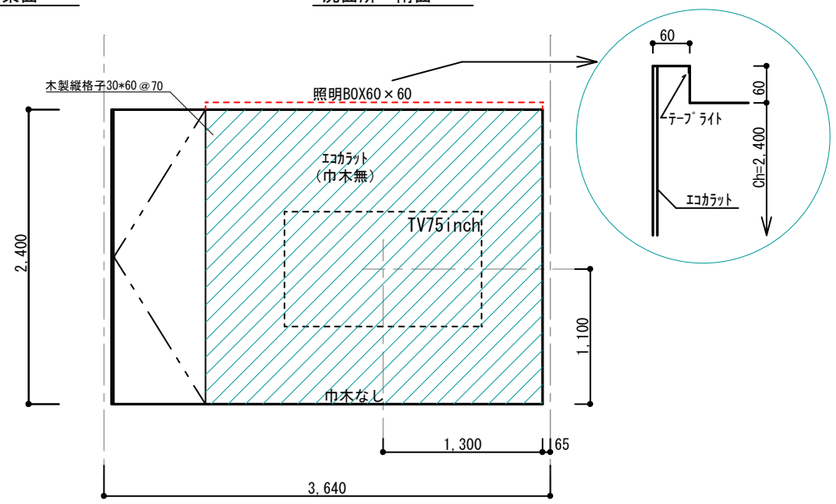

LDK　東面

決定図

訂正	浜岡一級総合設計事務所 一級建築士事務所　静岡県知事登録第（10)2441　号 一級建築士　大臣登録第　365879　号　西原利昌	LIFEFUND PG HOUSE	株式会社　LIFEFUND　InDesign office　一級建築士事務所 事務所登録（2)第7595号　一級建築士登録 第179770号　鈴木　達男 〒432-8023　静岡県浜松市中央区鴨江3丁目70番23号	年月日 2024.11.20 縮尺 1/50	件名 竹内優太郎様　新築工事 図名 展開図-1		設計 倉田	IC	工事 青島	図番 6-1