

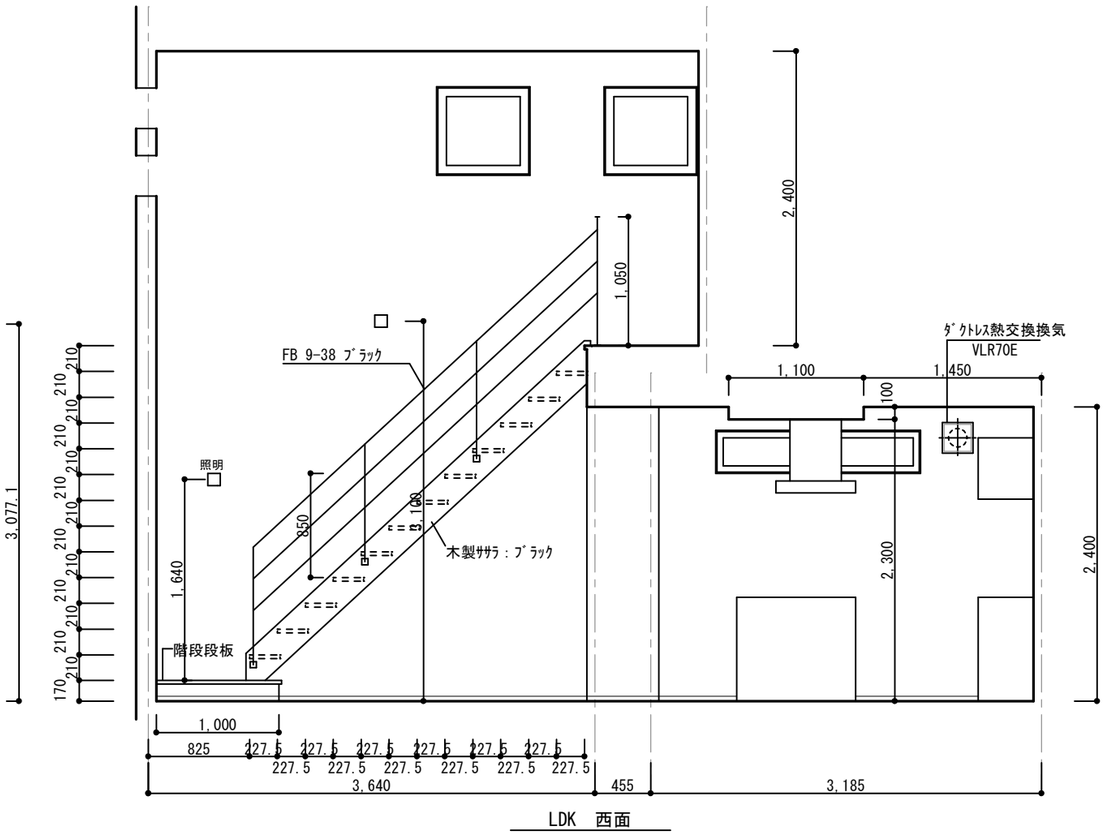



LDK　西面

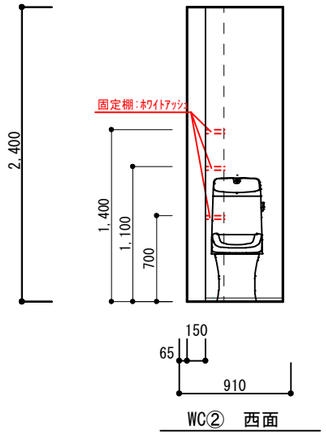


WC②　西面

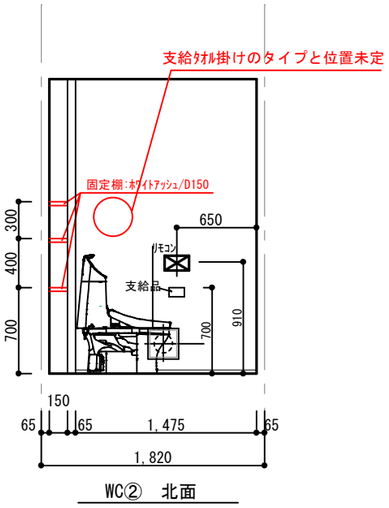


WC②　北面

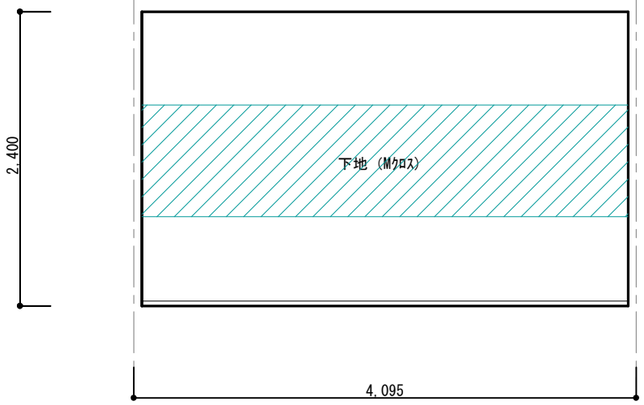


洋室　南面

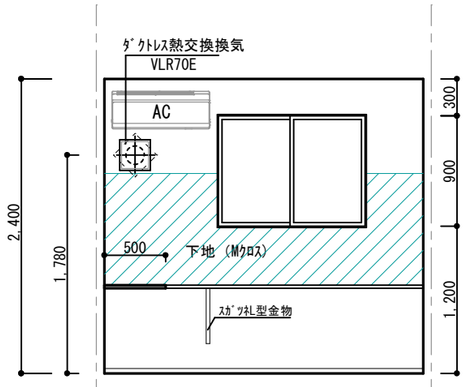


書斎　北面

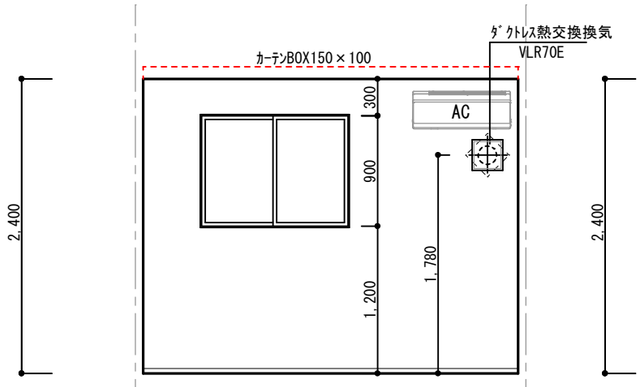

寝室　北面

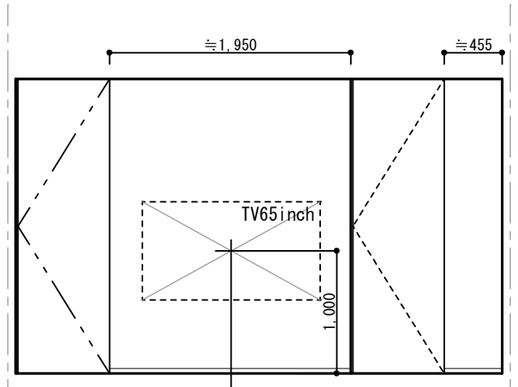

洋室　北面

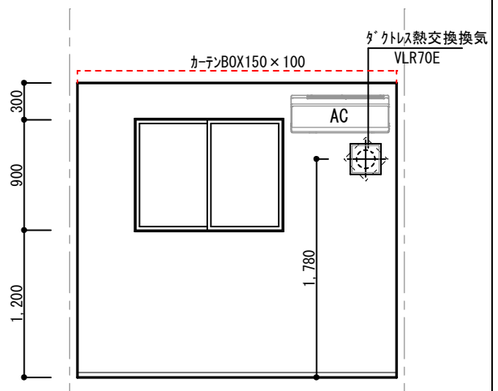

洋室　東面

決定図

訂　正	浜岡一級総合設計事務所 一級建築士事務所　静岡県知事登録第（10）2441　号 一級建築士　大臣登録第　365879　号　西原利昌	LIFEFUND PG HOUSE	株式会社　LIFEFUND　InDesign office　一級建築士事務所 事務所登録（2）第7595号　一級建築士登録 第179770号　鈴木　達男 〒432-8023　静岡県浜松市中央区鴨江3丁目70番23号	年月日 2024.12.11 縮尺 1/50	件名 竹内優太郎様　新築工事 図名 展開図-2	設計 倉田 / IC / 工事 青島 / 図番 6-2